

展開接続図

御注文主 久留米市企業局 上下水道部下水道施設課 様

納入場所 大善寺中継ポンプ場

用途 大善寺中継ポンプ場電気設備改築工事

プロジェクト番号 M013628701

項目	内 容	ペ ー ジ	項目	内 容	ペ ー ジ
1	目次	001	16	—	—
2	変更履歴一覧表	002	17	—	—
3	工事履歴一覧表	003	18	—	—
4	関連図番一覧表	004	19	—	—
5	取り合い図面一覧表	005	20	—	—
6	展開接続図の見方	011~012	21	—	—
7	図記号一覧表	014~016	22	—	—
8	制御器具番号表	017	23	—	—
9	配電盤接地構成	019	24	—	—
10	接地と端末処理	020	25	—	—
11	システム系統図	ソフトウェア共通仕様書参考 (図番、頁後報)	26	—	—
12	ネットワーク構成図	021	27	—	—
13	XH展開表	031	28	—	—
14	XH名称配置図	036	29	—	—
15	集合表示灯名称配置図	037	30	—	—

変更記号
変更記号及び 内容の詳細は 次ページに記載

作 成	調 査	検 認
丸小野/阿多	丹/淵邊	舟木
2024 - 09 - 20	2024 - 09 - 20	2024 - 09 - 20

図番 MWA402712

A		B		C		D		E		F		G		H					
項 目		内 容				ペ ー ジ		項 目		内 容				ペ ー ジ					
3 1		ミニUPS [UPS]				100		6 1		—				—					
3 2		—				—		6 2		—				—					
3 3		監視操作盤 [K01]				—		6 3		—				—					
3 4		電源回路				101,103		6 4		—				—					
3 5		盤内付属電源回路				106		6 5		—				—					
3 6		信号受信回路				111~129		6 6		—				—					
3 7		制御回路				141~196		6 7		—				—					
3 8		表示回路				211~232		6 8		—				—					
3 9		警報回路				241~246		6 9		—				—					
4 0		信号送出回路				261~281		7 0		—				—					
4 1		—				—		7 1		—				—					
4 2		—				—		7 2		—				—					
4 3		計装テレメータ盤 [KP]				—		7 3		—				—					
4 4		電源回路				301~302		7 4		—				—					
4 5		盤内付属電源回路				306		7 5		—				—					
4 6		ルータ・ONU接続図				311		7 6		—				—					
4 7		SAPPHIRUS CPU(マスター)接続図				313		7 7		—				—					
4 8		SAPPHIRUS CPU(スレーブ)接続図				314		7 8		—				—					
4 9		制御モジュール接続図				315		7 9		—				—					
5 0		I/Fモジュール接続図				316~317		8 0		—				—					
5 1		インターフェイス回路				321~336		8 1		—				—					
5 2		計装電源				351~353		8 2		—				—					
5 3		計装回路				361~376		8 3		—				—					
5 4		—				—		8 4		—				—					
5 5		—				—		8 5		—				—					
5 6		—				—		8 6		—				—					
5 7		—				—		8 7		—				—					
5 8		—				—		8 8		—				—					
5 9		—				—		8 9		—				—					
6 0		—				—		9 0		—				—					
Revisions	)				Date	Name	メタウォーター株式会社 METAWATER Co., Ltd.	Title	目 次				Dwg.No.	MWA402712		001			
	)																		
	)				Checked	2024-09-20							丹/淵邊						
	)												舟木						
A		B		C		D		E		F		G		H					

	A	B	C	D	E	F	G	H																									
1	変 更 履 歴 一 覧 表																																
	変更 記号	変 更 日 付	PROJECT番号	変 更 理 由 ま た は 内 容	変 更 頁	検 認	調 査	作 成																									
	a	2024-11-11	M013628701	・制御リレー追加、削除 ・信号項目追加、変更 ・接地構成変更 ・図面修正フォロー	変更頁：019,037,100,118,121,191,196,226,273,302,321~323, 325~327,332,333,361,363,366,371,375,376	舟木	丹／淵邊	丸小野 ／阿多																									
2	b	2025-02-04	M013628701	・制御リレー追加 ・配線変更 ・図面修正フォロー ・取合フォロー	変更頁：101,103,106,111,113,115,116,119,123,128,168,268, 306,313~317,352,353,363	舟木	丹／淵邊	丸小野 ／阿多																									
3																																	
4																																	
5																																	
<table><tr><td rowspan="4">Revisions</td><td>)</td><td rowspan="4"> </td><td>Date</td><td>Name</td><td rowspan="4">メタウォーター株式会社 METAWATER Co., Ltd.</td><td rowspan="4">Title</td><td rowspan="4">変更履歴一覧表</td><td rowspan="4">Dwg.No.</td><td rowspan="4">MWA402712</td><td rowspan="4">002</td><td rowspan="4"></td><td rowspan="4"></td></tr><tr><td>)</td><td>Drawn</td><td>2024-09-20</td><td>丸小野／阿多</td></tr><tr><td>)</td><td>Checked</td><td>2024-09-20</td><td>丹／淵邊</td></tr><tr><td>)</td><td></td><td></td><td>舟木</td></tr></table>									Revisions	)		Date	Name	メタウォーター株式会社 METAWATER Co., Ltd.	Title	変更履歴一覧表	Dwg.No.	MWA402712	002			)	Drawn	2024-09-20	丸小野／阿多	)	Checked	2024-09-20	丹／淵邊	)			舟木
Revisions	)		Date	Name	メタウォーター株式会社 METAWATER Co., Ltd.	Title	変更履歴一覧表	Dwg.No.		MWA402712		002																					
	)		Drawn	2024-09-20																			丸小野／阿多										
	)		Checked	2024-09-20																			丹／淵邊										
	)								舟木																								
	A	B	C	D	E	F	G	H																									

工 事 履 歴 一 覧 表

変更記号	PROJECT番号	年月日	工 事 名 称	備 考
オリジナル	M013628701	2024-09-20	大善寺中継ポンプ場電気設備改築工事	—

	A		B		C		D		E		F		G		H						
	(H：ハード，S：ソフト)																				
	No.	図 番	図 面 名 称	PROJECT番号	H／S	設 備 名 称	機 種	ステーション (STNo.)				備 考									
								FL-net			Pリンク (10進)										
1	01	MWD400262	システム機能仕様書	M013628701	－	－	－	－	－	－	－	－	－	－	－						
	02	MWA402687	展開接続図	M013628701	H	汚水ポンプ盤、補機盤、現場盤	－	－	－	－	－	－	－	－	－						
	03	MWA402712	展開接続図	M013628701	H	監視操作盤、計装テレメータ盤	－	－	－	－	－	－	－	(本図番)							
	04	MWA402847	ソフトウェア仕様書	M013628701	S	計装テレメータ盤シーケンサ	SAPPHIRUS	－	－	－	－	－	－	－	－						
2	05	MWN41924	展開接続図	M013628701	H	受変電設備	－	－	－	－	－	－	－	－	－						
	06																				
	07																				
	08																				
	09																				
	10																				
3	11																				
	12																				
	13																				
	14																				
	15																				
4	16																				
	17																				
	18																				
	19																				
	20																				
5	21																				
	22																				
Revisions	)				Date	Name	メタウォーター株式会社 METAWATER Co., Ltd.					Title	関連図番一覧表			Dwg.No.	MWA402712		004		
	)			Drawn	2024-09-20	丸小野/阿多															
	)			Checked	2024-09-20	丹/淵邊						Ref.				CW00_04					
	)					舟木															
	A		B		C		D		E		F		G		H						

A		B		C		D		E		F		G		H													
1	No.	本PJ 対象	本図番 変更 記号	取 り 合 い 先			取 り 合 い 先 情 報				備 考																
				図 面 名 称	図 番	変更 記号	工 場 ・ メ ー カ ー	未対応 (製作優先)	取合図面無	現地調査要			完了														
2	0 1	○	初版	展開接続図	331LN44724	1	日立殿	－	－	－	○	－															
	0 2	○	b	展開接続図	MWA402687	d	メタウォーター	－	－	－	○	(動力設備)															
	0 3	○	初版	展開接続図	3101S881－332	1	日立殿	－	－	－	○	(自家発設備)															
	0 4	○	初版	展開接続図	5PC－D24246	C	日立殿	－	－	－	○	(直流電源装置)															
	0 5	○	b	展開接続図	MWN41924	b	メタウォーター	－	－	－	○																
3	0 6																										
	0 7																										
	0 8																										
	0 9																										
	1 0																										
	1 1																										
	1 2																										
	1 3																										
	1 4																										
	1 5																										
4	1 6																										
	1 7																										
	1 8																										
	1 9																										
	2 0																										
	2 1																										
→ 本図番の変更がなくても取り合いを確認したら変更記号を記入・更新する。																											
Revisions	)			Date	Name	メタウォーター株式会社 METAWATER Co., Ltd.					Title	取り合い図面一覧表			Dwg.No.	MWA402712		005									
	)																										
	)			Drawn	2024-09-20	丸小野/阿多																					
	)			Checked	2024-09-20	丹/淵邊 舟木	Ref.		CW00_06a																		
A		B		C		D		E		F		G		H													

1

2

3

4

5

展開接続図の見方

1. 展開接続図は下記の規格を基準としてE, W, D (Elementary Wiring Diagram) 方式で記載されています。

(1) J I S C 0 6 1 7 - 1 ~ 1 3 電気用図記号

(2) J E M 1 0 9 0 ~ 1 0 9 4 制御器具番号

2. 展開接続図のシート番号は2～4桁を標準としています。

尚、変更により分割された場合前頁のシート番号－1，－2としています。

(例0 0 0 2－1，0 0 0 2－2)

3. 外線端子および線番号は下記により表しています。

(1) 一般

□□□□	○○
------	----

シート番号に対応した英文字・数字

同一シート内での追番号 (原則2桁)

[左より右へ、かつ上から下への順 (0 1～9 9)]

4. 使用器具型式の表示

(1)各機器のシンボルの近傍に項番 (弊社手配No.) 型式、仕様を記入しています。

(2)タイマーについては、整定範囲を記入しています。

(3)整定値を指定する場合は、コイル右下に記入しています。

(4)機器仕様一覧表とのリンク：展開接続図に記載した型式は、各盤図の機器一覧表でも確認下さい。

(5)購入品の仕様は、型式、定格、品名、メーカー名 等を表示します。

5. 接点の来先、行先表示

(1)来先はコイルが記入されたシート番号とコイル位置アドレス (横座標区分A～H) で示しています。

また同一シート内のものは位置アドレスのみ記入し、シート番号は省略します。

52C
X

52C
↑

1sec → 整定値

52CX
< 1235 >
[*****]

52CT
< 1236 >
[*****]

→ デバイスNo.
→ 項番 (手配番号)
→ PCMNo.
→ 形式
→ 定格等

a	5	3	
b	5	4	
a	6	2	
b	6	9	
a	7	10	
b	7	8	0002 A

T a	8	6	
T b	8	5	
T a	3	3	
T b	1	4	

行先シート番号

行先シート中の横座標区分
(同一シート内では省略します。)
(A～H)

6. 制御電源又は信号線が、前後のシート以外におよぶ場合は来先、行先を記入しています。

(例) ----- R 1 C ----- 線番記号
(0 0 2 8 B) ----- 行先シートNo. 域は、行先ユニットページNo.

7. ----- (空) -----

8. 回路図上でシンボル及び配線が点線表示の部分は、「将来回路」を示します。

A

B

C

D

E

F

G

H

1

2

3

4

5

Bの所有範囲

7

10

52CX
(0003 A)

来先シート番号

コイル位置
(横座標区分A～H)

シート番号
(ページ)

図番

0002

RY1

盤記号

(図枠右下部に表示)

注) 線上は左側アドレスに含まれます。

Revisions

)

)

)

)

Drawn

2024-09-20

丸小野/阿多

Checked

2024-09-20

丹/淵邊

舟木

メタウォーター株式会社

METAWATER Co., Ltd.

Title

展開接続図の見方 (1 / 2)

Dwg.No.

MWA402712

011

Ref.

CW01_01-01c

1



3

4

5

Revisions

	Date	Name
Drawn	2024-09-20	丸小野 / 阿多
Checked	2024-09-20	丹 / 淵邊
		舟木

Title

Ref	Dwa No
-----	--------

012 | F

A

B










C





D

--	--

F


G[illegible]

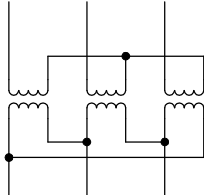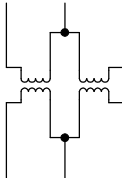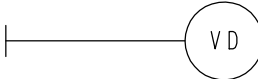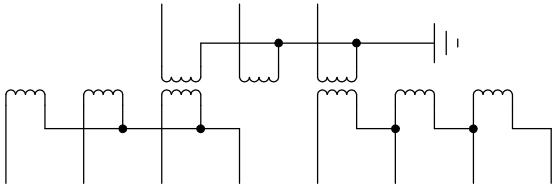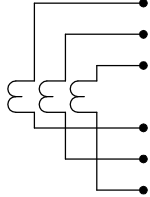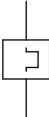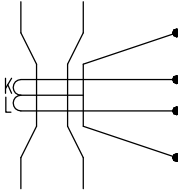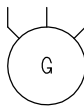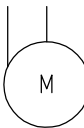A		B		C		D		E		F		G		H	
名称		図記号		名称		図記号		名称		図記号					
1	しゃ断器（一般）			変圧器（一般）				避雷器						1	
	断路器（一般）			計器用変圧器（2巻線） （PT）				検電器							
2	負荷開閉器			計器用変圧器（3巻線） （GPT）				ヒューズ（一般）						2	
	ACB			変流器 （CT）				サーマルリレー						3	
3	配電用しゃ断器			零相変流器 （ZCT）				コネクタ端子（一般）							
	発電機			コンデンサ（一般）				接地						4	
4	モータ			リアクトル				ケーブルヘッド							
														5	
Revisions				Date		Name		Title		Dwg.No.		MWA402712		014	
				Drawn		2024-09-20		丸小野/阿多							
				Checked		2024-09-20		丹/淵達							
						舟木		METAWATER Co., Ltd.							
								図記号一覧表（1／3）		Ref.		CW01_05			

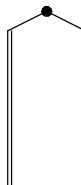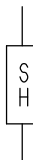 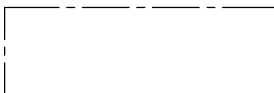A		B		C		D		E		F		G		H	
名称		図記号		名称		図記号		名称		図記号		名称		図記号	
1	計器用切換開閉器	 (電流計)		 (電圧計)		電流計用分流器				蛍光灯					
2	熱電対			熱電対		保護継電器				コンセント					
						端子（一般）				スペースヒーター					
3	計器（一般） V : 電圧計 A : 電流計 W : 電力計 Var : 無効電力計 Pf : 力率計 F : 周波数計 TI : 温度指示計 GV : ガイドベーン開度計 LL : 負荷制限位置指示計 RV : ランナベーン開度計 N : 回転計 WL : 水位計			電気配線（一般）											
				対より線 （ツイスト）											
				シールド線											
4	WH : 電力量計 VarH : 無効電力量計			盤境線											
5	変換器（一般） V TD : 電圧変換器 A TD : 電流変換器 W TD : 電力変換器 Var TD : 無効電力変換器 Pf TD : 力率変換器 F TD : 周波数変換器 ISO : 絶縁変換器 P CNV : パルス変換器														
Revisions)))) Date 2024-09-20 2024-09-20 Name 丸小野/阿多 丹/淵邊 舟木 METAWATER Co., Ltd. Title 図記号一覧表（2／3） Ref. Dwg.No. MWA402712 CW01_06 015															
A		B		C		D		E		F		G		H	


A		B		C	D	E	F	G	H
名称		図記号		名称	図記号	名称	図記号		
		a 接点	b 接点					備考	
1	継電器接点			継電器（一般）		可変抵抗器			
	手動復帰接点			キープリレー		切替スイッチ(COS) 操作スイッチ(CS)			
	電磁接触器接点					押しボタンスイッチ			
2	切替スイッチ接点			遅延動作継電器 (オンディレータイマー)		ランプ内蔵押しボタンスイッチ			
	操作スイッチ接点 (自動復帰)			遅延復旧形継電器 (オフディレータイマー)		ランプ内蔵押しボタンスイッチ			
	押しボタンスイッチ残留接点			機械式故障表示器		テストターミナル (引き出し型) ジャック・引き出し機構			
3	押しボタンスイッチ接点			電磁弁		テストターミナル (スタッド型)	: 電流回路用 : 電圧回路用 2重端子 1重端子		
	引きスイッチ接点			ランプ	RL: レッド WL: ホワイト GL: グリーン CL: 透明 OL: オレンジ	整流器（ダイオード）	本		
	限時動作接点			状態・故障表示器		サイリスタ			
4	限時復帰接点			ベル		ツェナダイオード			
	リミットスイッチ接点			ブザー		セレンアレスタ	本		
	機械接点 (圧カリレー・フローリレー等)			抵抗器（一般）		バリスタ			
Revisions				Date	Name	Title	Dwg.No.	MWA402712	016
				Drawn	2024-09-20 丸小野/阿多				
				Checked	2024-09-20 丹/淵邊				
					舟木				
メタウォーター株式会社 METAWATER Co., Ltd.						図記号一覧表（3 / 3）		Ref. CW01_07b	

[illegible]

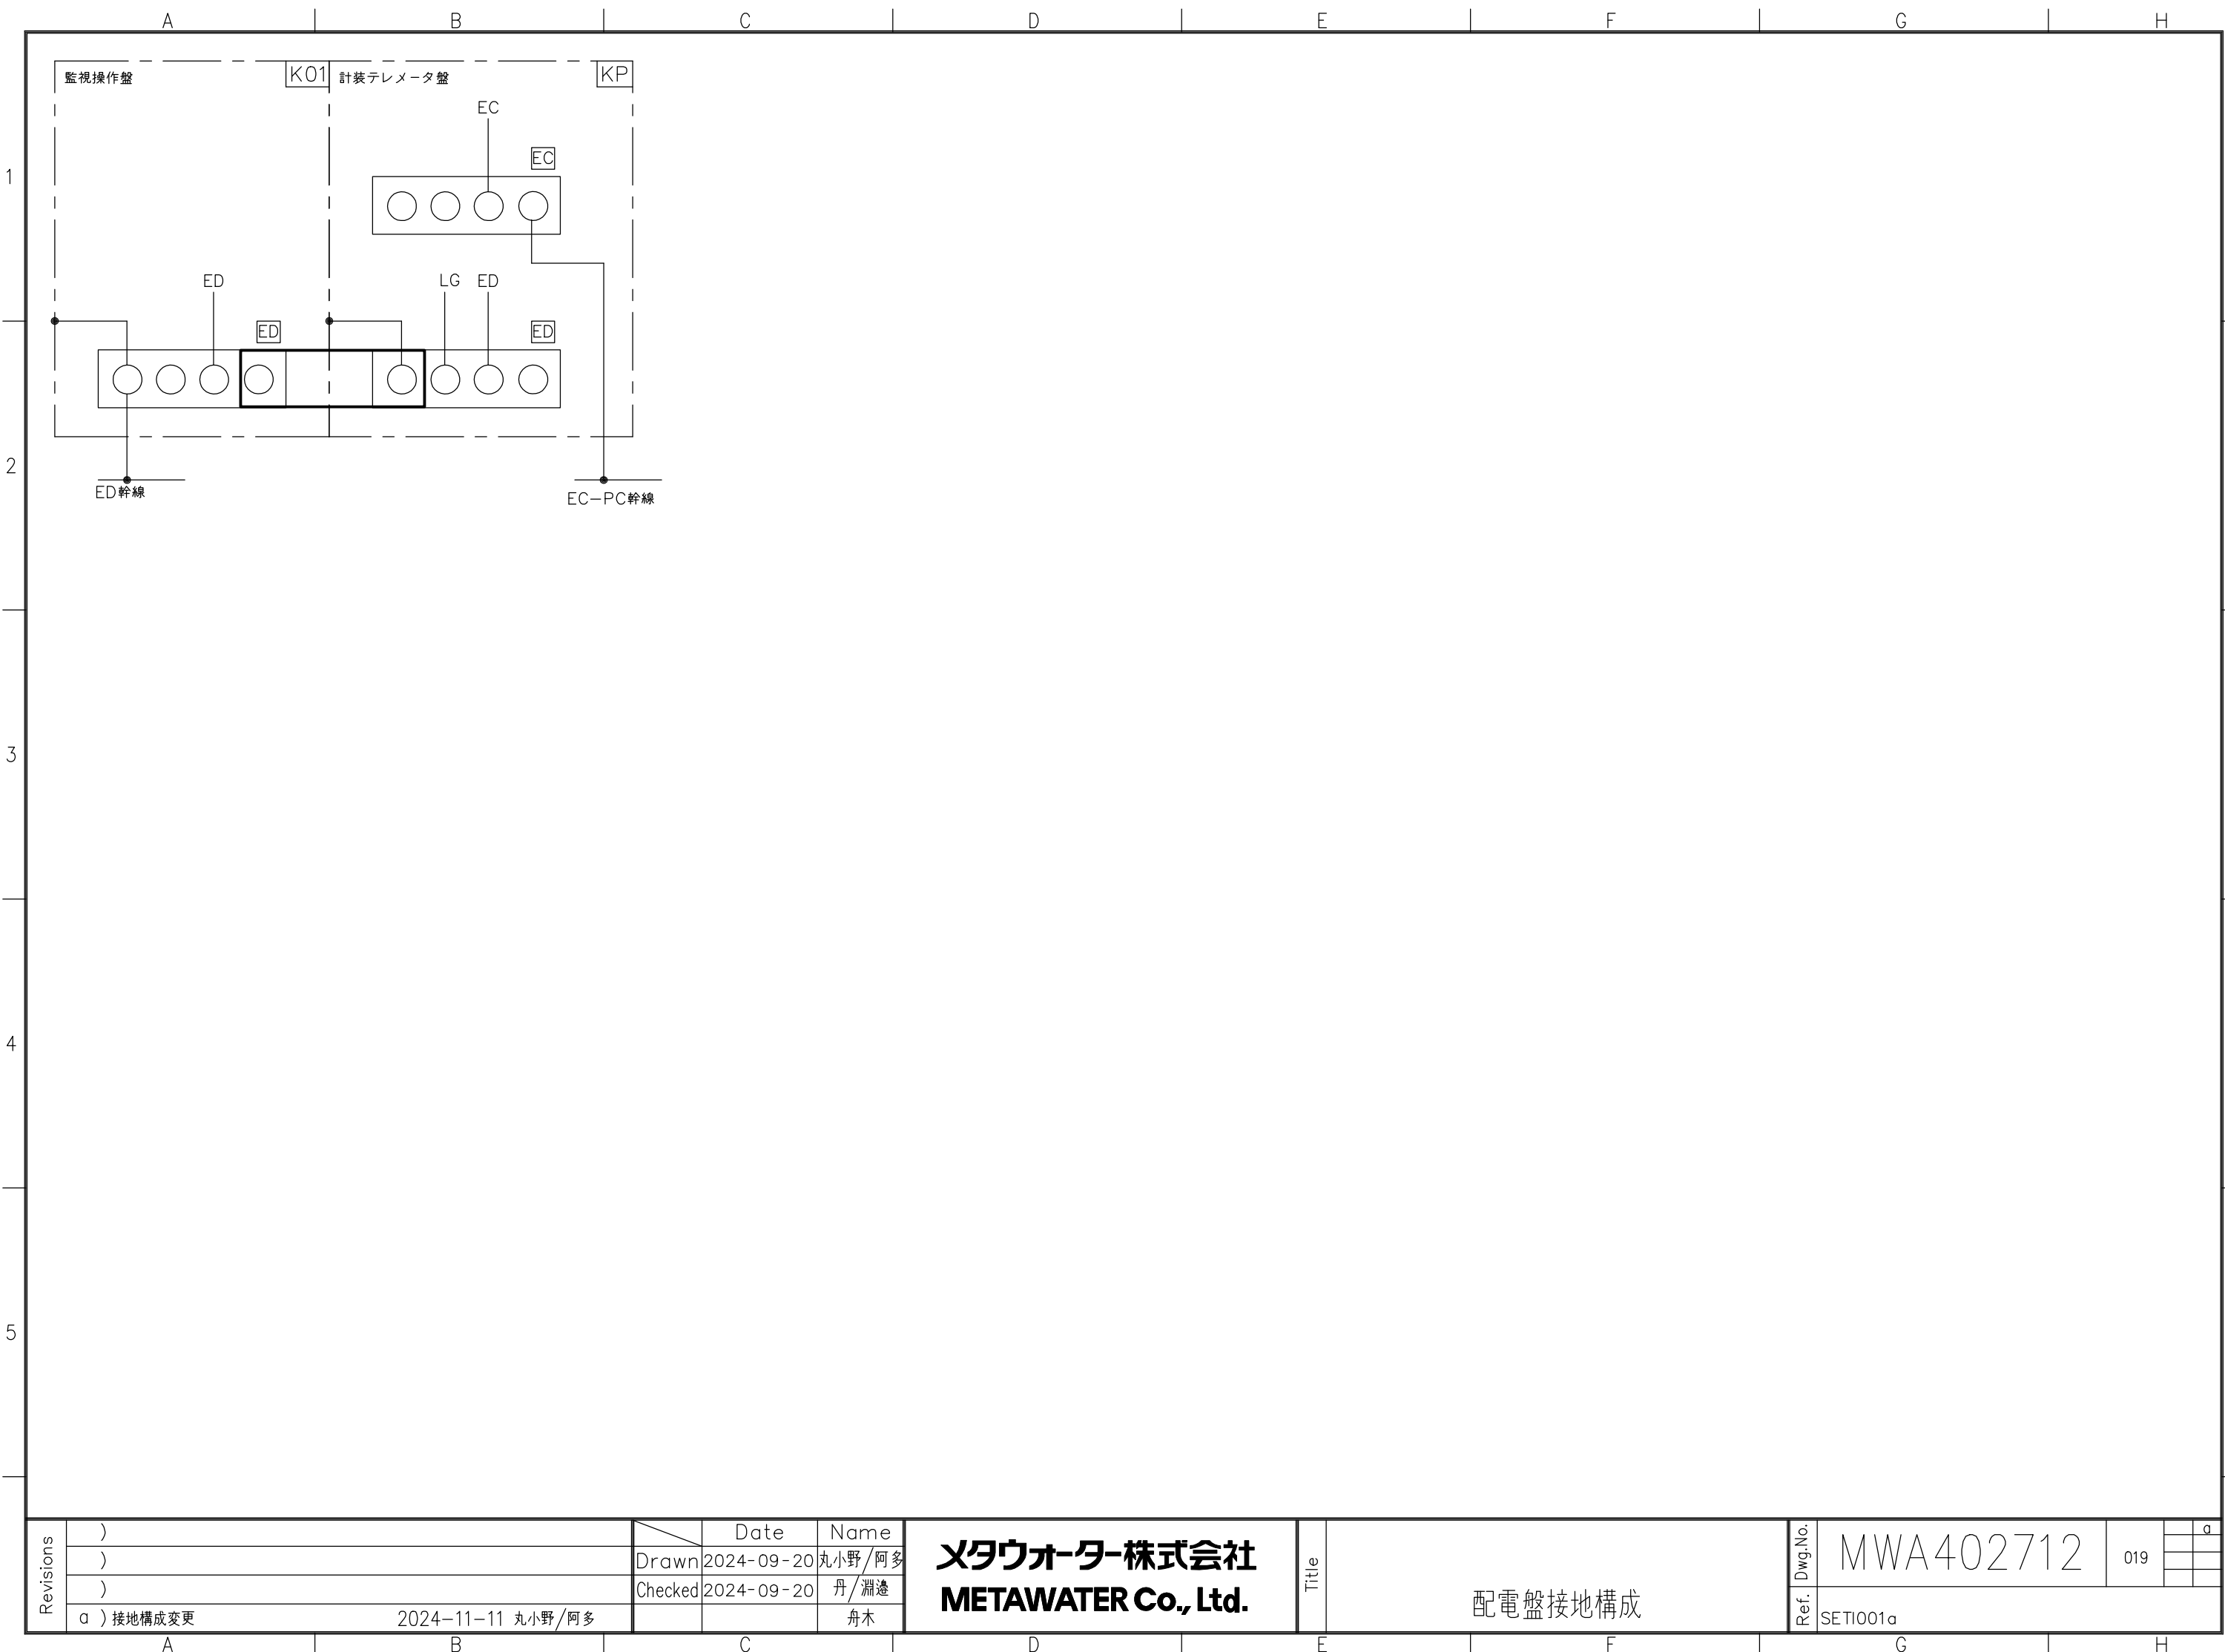

Revisions	)		Date	Name	メタウォーター株式会社 METAWATER Co., Ltd.	Title	配電盤接地構成	Dwg.No.	MWA402712	019	a	
	)	Drawn	2024-09-20	丸小野/阿多								
	)	Checked	2024-09-20	丹/淵邊								
	a) 接地構成変更			舟木								
	2024-11-11	丸小野/阿多										
								Ref.	SETI001a			


	A	B	C	D	E	F	G	H			
1	1. 接地母線への接地種別ラベルの貼付けと、展開接続図内の表現				3. シールドケーブルの末端処理						
	展開接続図内は、それぞれ下記のように表現する。				シールド付ケーブルのシールド部分の接地は、下記の何れかによる						
	(1) 盤内のそれぞれの器具からの接地回路は、各器具が要求する接地レベルを表示する。				(1) 静電遮蔽を目的としたシールド						
	盤 A機器 C機器 EA EC 接地母線 EA 接地幹線				(2) 電磁遮蔽を目的としたシールド						
	(2) 盤内機器接地部の表現は下記の2種類とする。				(2) 両端の接地を原則とし、それぞれの盤の接地母線に接続する。						
2	(1) 直接接地母線などに接続する必要のある表示。				(1) 片側のみ接地する事を原則とし、それぞれのケーブル専用用意された外線端子、又は接地する側の盤の接地母線に接続する。原則として、盤のフレーム等へ接地してはならない又、〔現場<電気室<中央〕 等のように、より上位の方で接地する事を原則とする。						
	機器 機器				(2) 但し、インバータ盤と負荷間に用いるシールドケーブルは、片側接地とする。						
	(3) 盤内の各種接地（特に安全接地）を接地母線（又は接地端子）で集約する場合は、その中で最も上位の接地記号を接地母線（又は接地端子）に貼り付け表示する。（その盤の要求する接地レベルを示す）				(3) シールド線末端処理の種類						
	盤から実際の接地幹線への接続は、各設備で決定した接地系統に従う事。				1) 外線端子への接続						
					接地母線 EC 0101 0102 シールドの片端を盤外線端子に接続する 盤内側は〔EC〕等の接地母線に接続する（盤フレームと同電位の方に接続）						
3					2) 接地母線へ直接接続（シールド接続用の端子が用意されていない場合のみ）						
					ED 0101 0102						
					3) シールドの接続先接地種別は、接地母線の接地ラベルに合わせる事。						
					4) インバータ負荷ケーブルにシールド付きを使用した場合、そのシールドの接地はインバータ本体と同じ、〔EC－VF〕に接続する 高圧インバータの場合も同様に〔EA－VF〕に接続する						
					5) 相手側で接地する場合						
4	(4) 接地母線の具体的表示				複数ページ間のインターフェースとなる回路にシールドケーブルを適用する場合で相手側盤で接地する場合には、シールドの接続先を明記せず、相手側盤内で接続する事だけを示す。従って、詳細な接続先の情報は、相手側シーケンスページを確認する事。						
	接地母線（又は接地端子）には下記の表示を行う。この表示は、原則として盤内での電気設備技術基準上の接地種別を表示する。但し、インバータ盤に関しては盤筐体の接地と同じ種別となるので、				相手側盤						
	、接続先の接地幹線種別を表示する										
	盤（機器）－接地幹線間の接続は、接地系統図の指示に従う事。但し、盤内の接地種別より同等以上のレベルでなければならない。										
	EA 電気設備技術基準によるA種接地				ED 電気設備技術基準によるD種接地						
5	EB 電気設備技術基準によるB種接地				EV 高圧インバータ専用接地						
	EC 電気設備技術基準によるC種接地				EV 低圧インバータ専用接地						
	2. 接地線接続部の末端処理										
	(1) 絶縁キャップの使用（緑色）										
	(2) 圧着端子の使用：複数の電線を一つの圧着端子に接続してはならない										
Revisions	)		Date	Name	Title	接地と末端処理		Dwg.No.			
	)										
	)		Drawn	2024-09-20				MWA402712			
	)		Checked	2024-09-20							
	)										
				舟木			Ref.	CW01_33e			
	A	B	C	D	E	F	G	H			

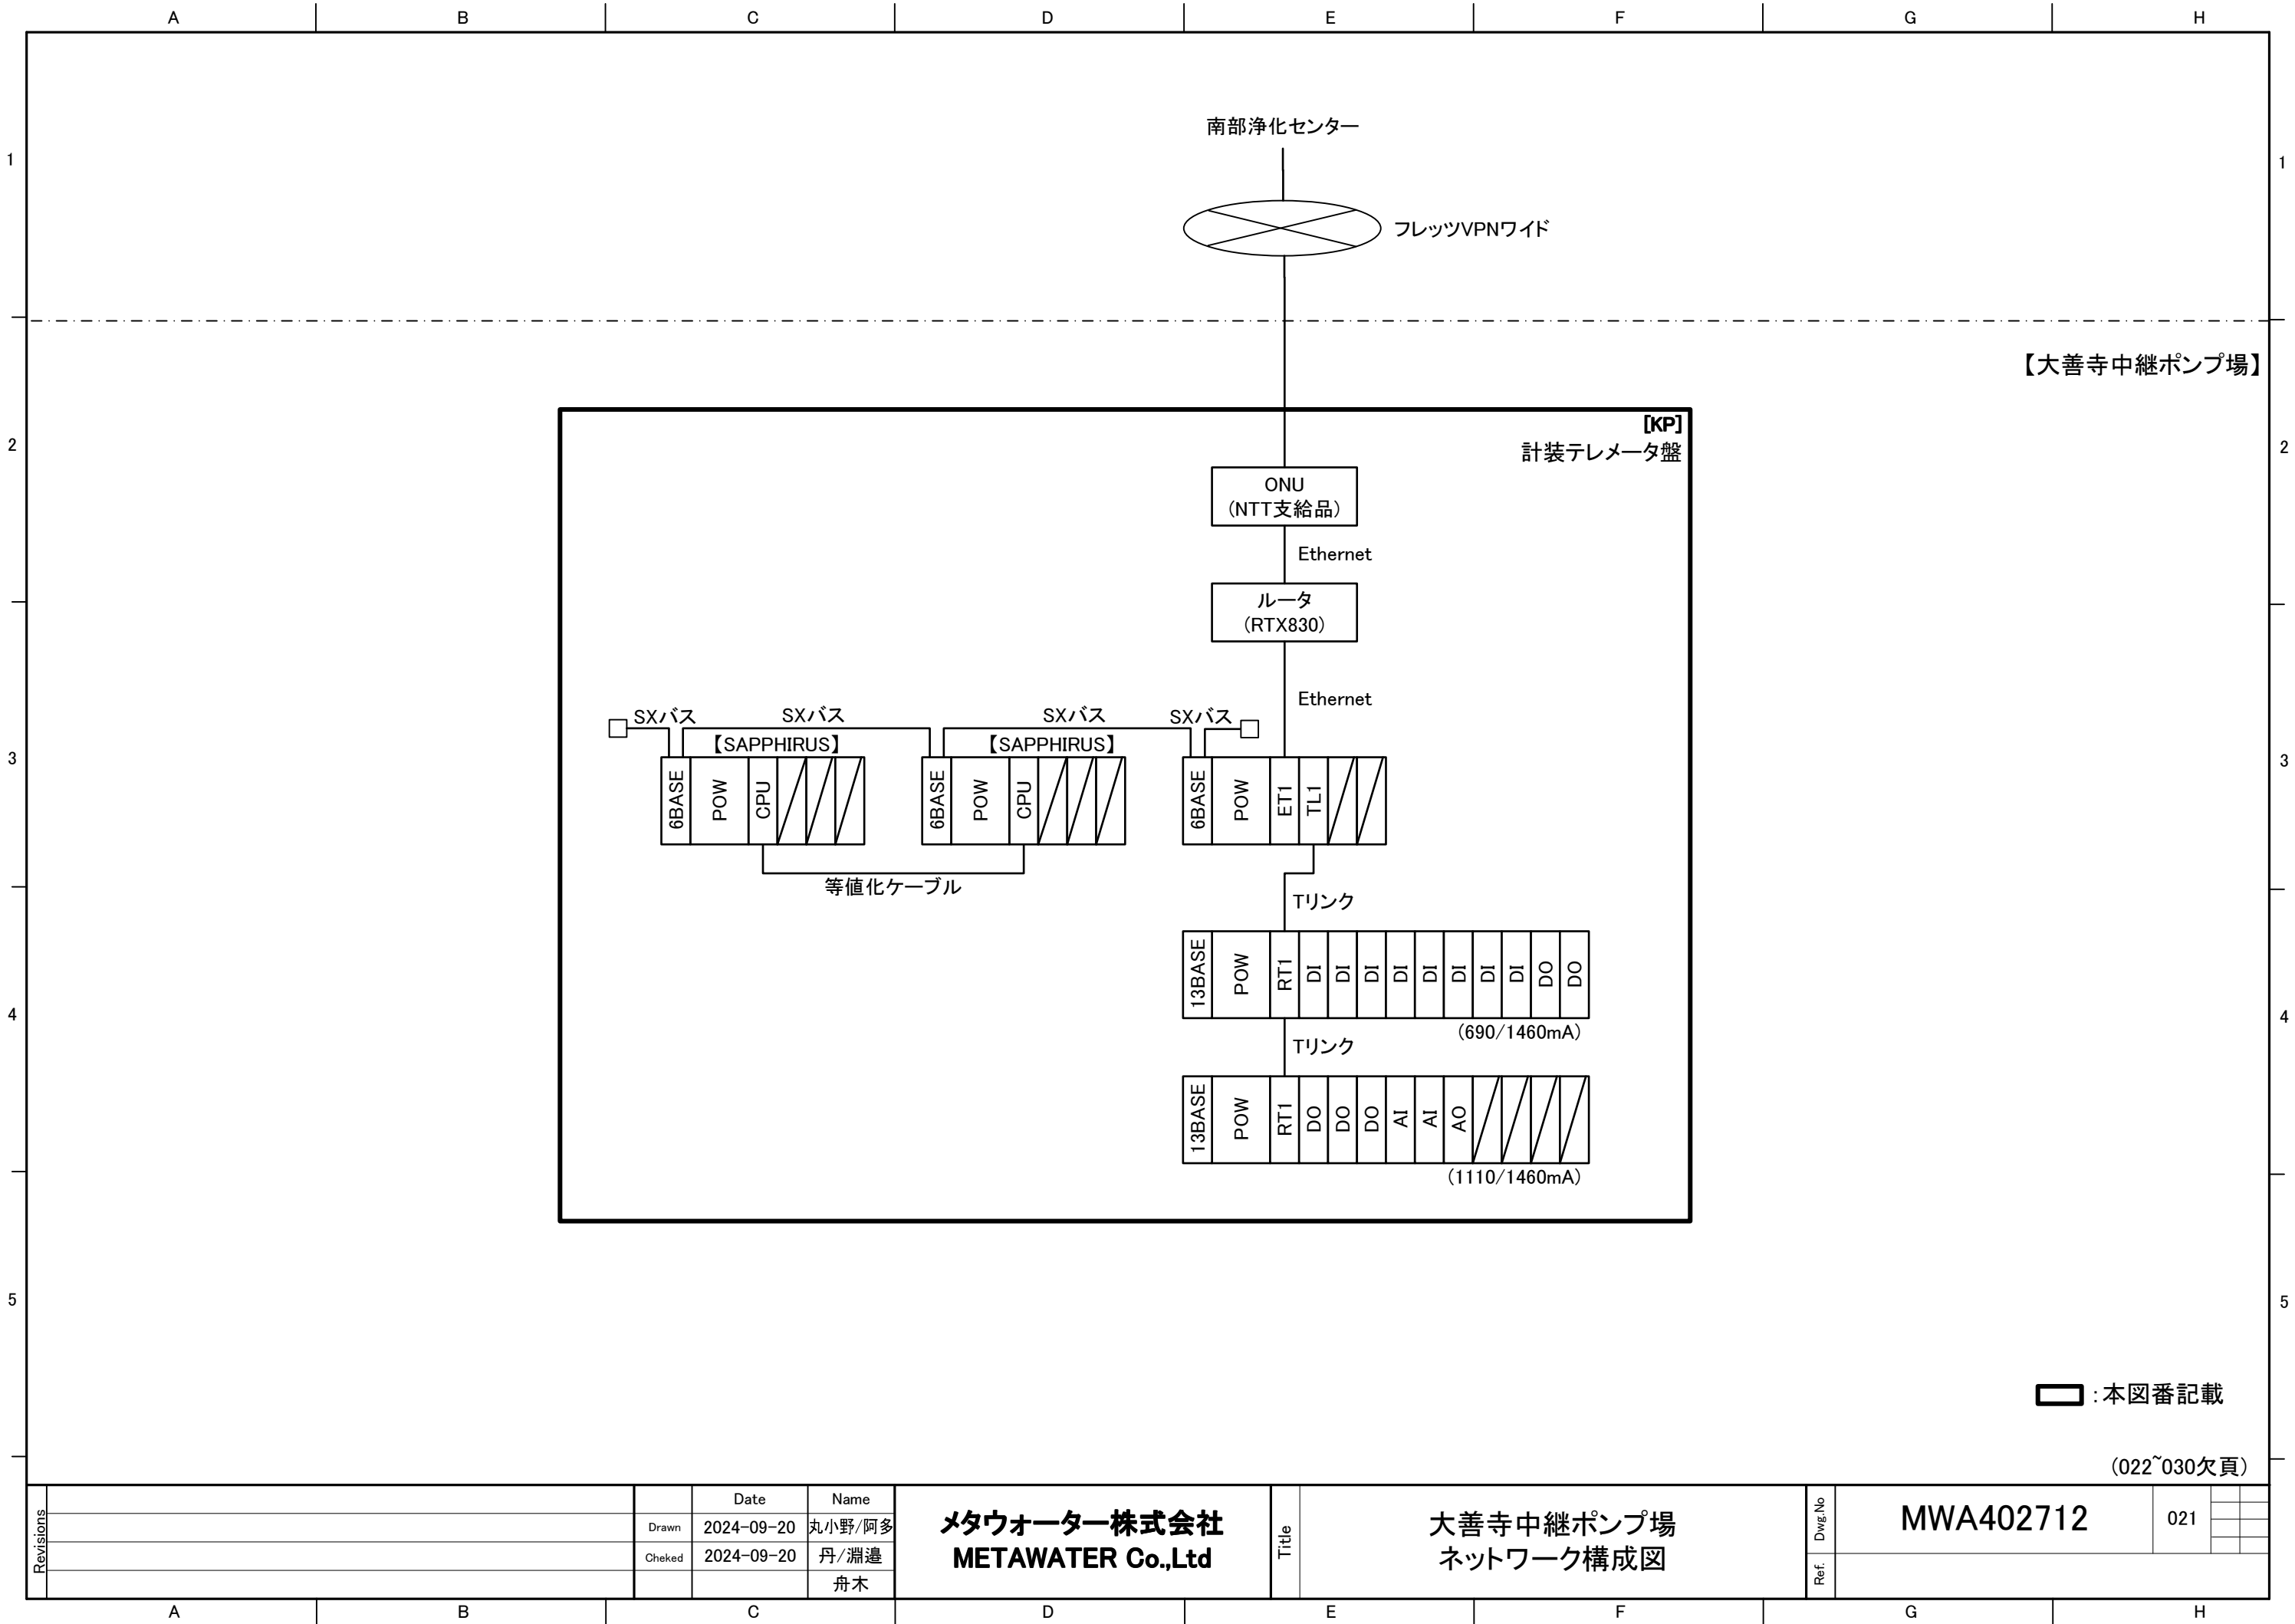


Revisions			Date	Name	メタウォーター株式会社 METAWATER Co.,Ltd	Title	大善寺中継ポンプ場 ネットワーク構成図	Dwg.No	MWA402712	021	
		Drawn	2024-09-20	丸小野/阿多							
		Cheked	2024-09-20	丹/淵邊							
				舟木							
								Ref.			





汚水ポンプ先発号機切替SW

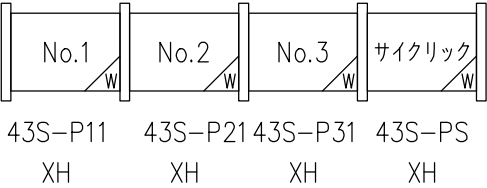


Revisions	)		Date	Name	メタウォーター株式会社 METAWATER Co., Ltd.	Title	監視操作盤 XH 名称配置図	Dwg.No.	MWA402712	036			
	)	Drawn	2024-09-20	丸小野 / 阿多									
	)	Checked	2024-09-20	丹 / 淵邊									
	)			舟木									
	)							Ref.	SETI001a				

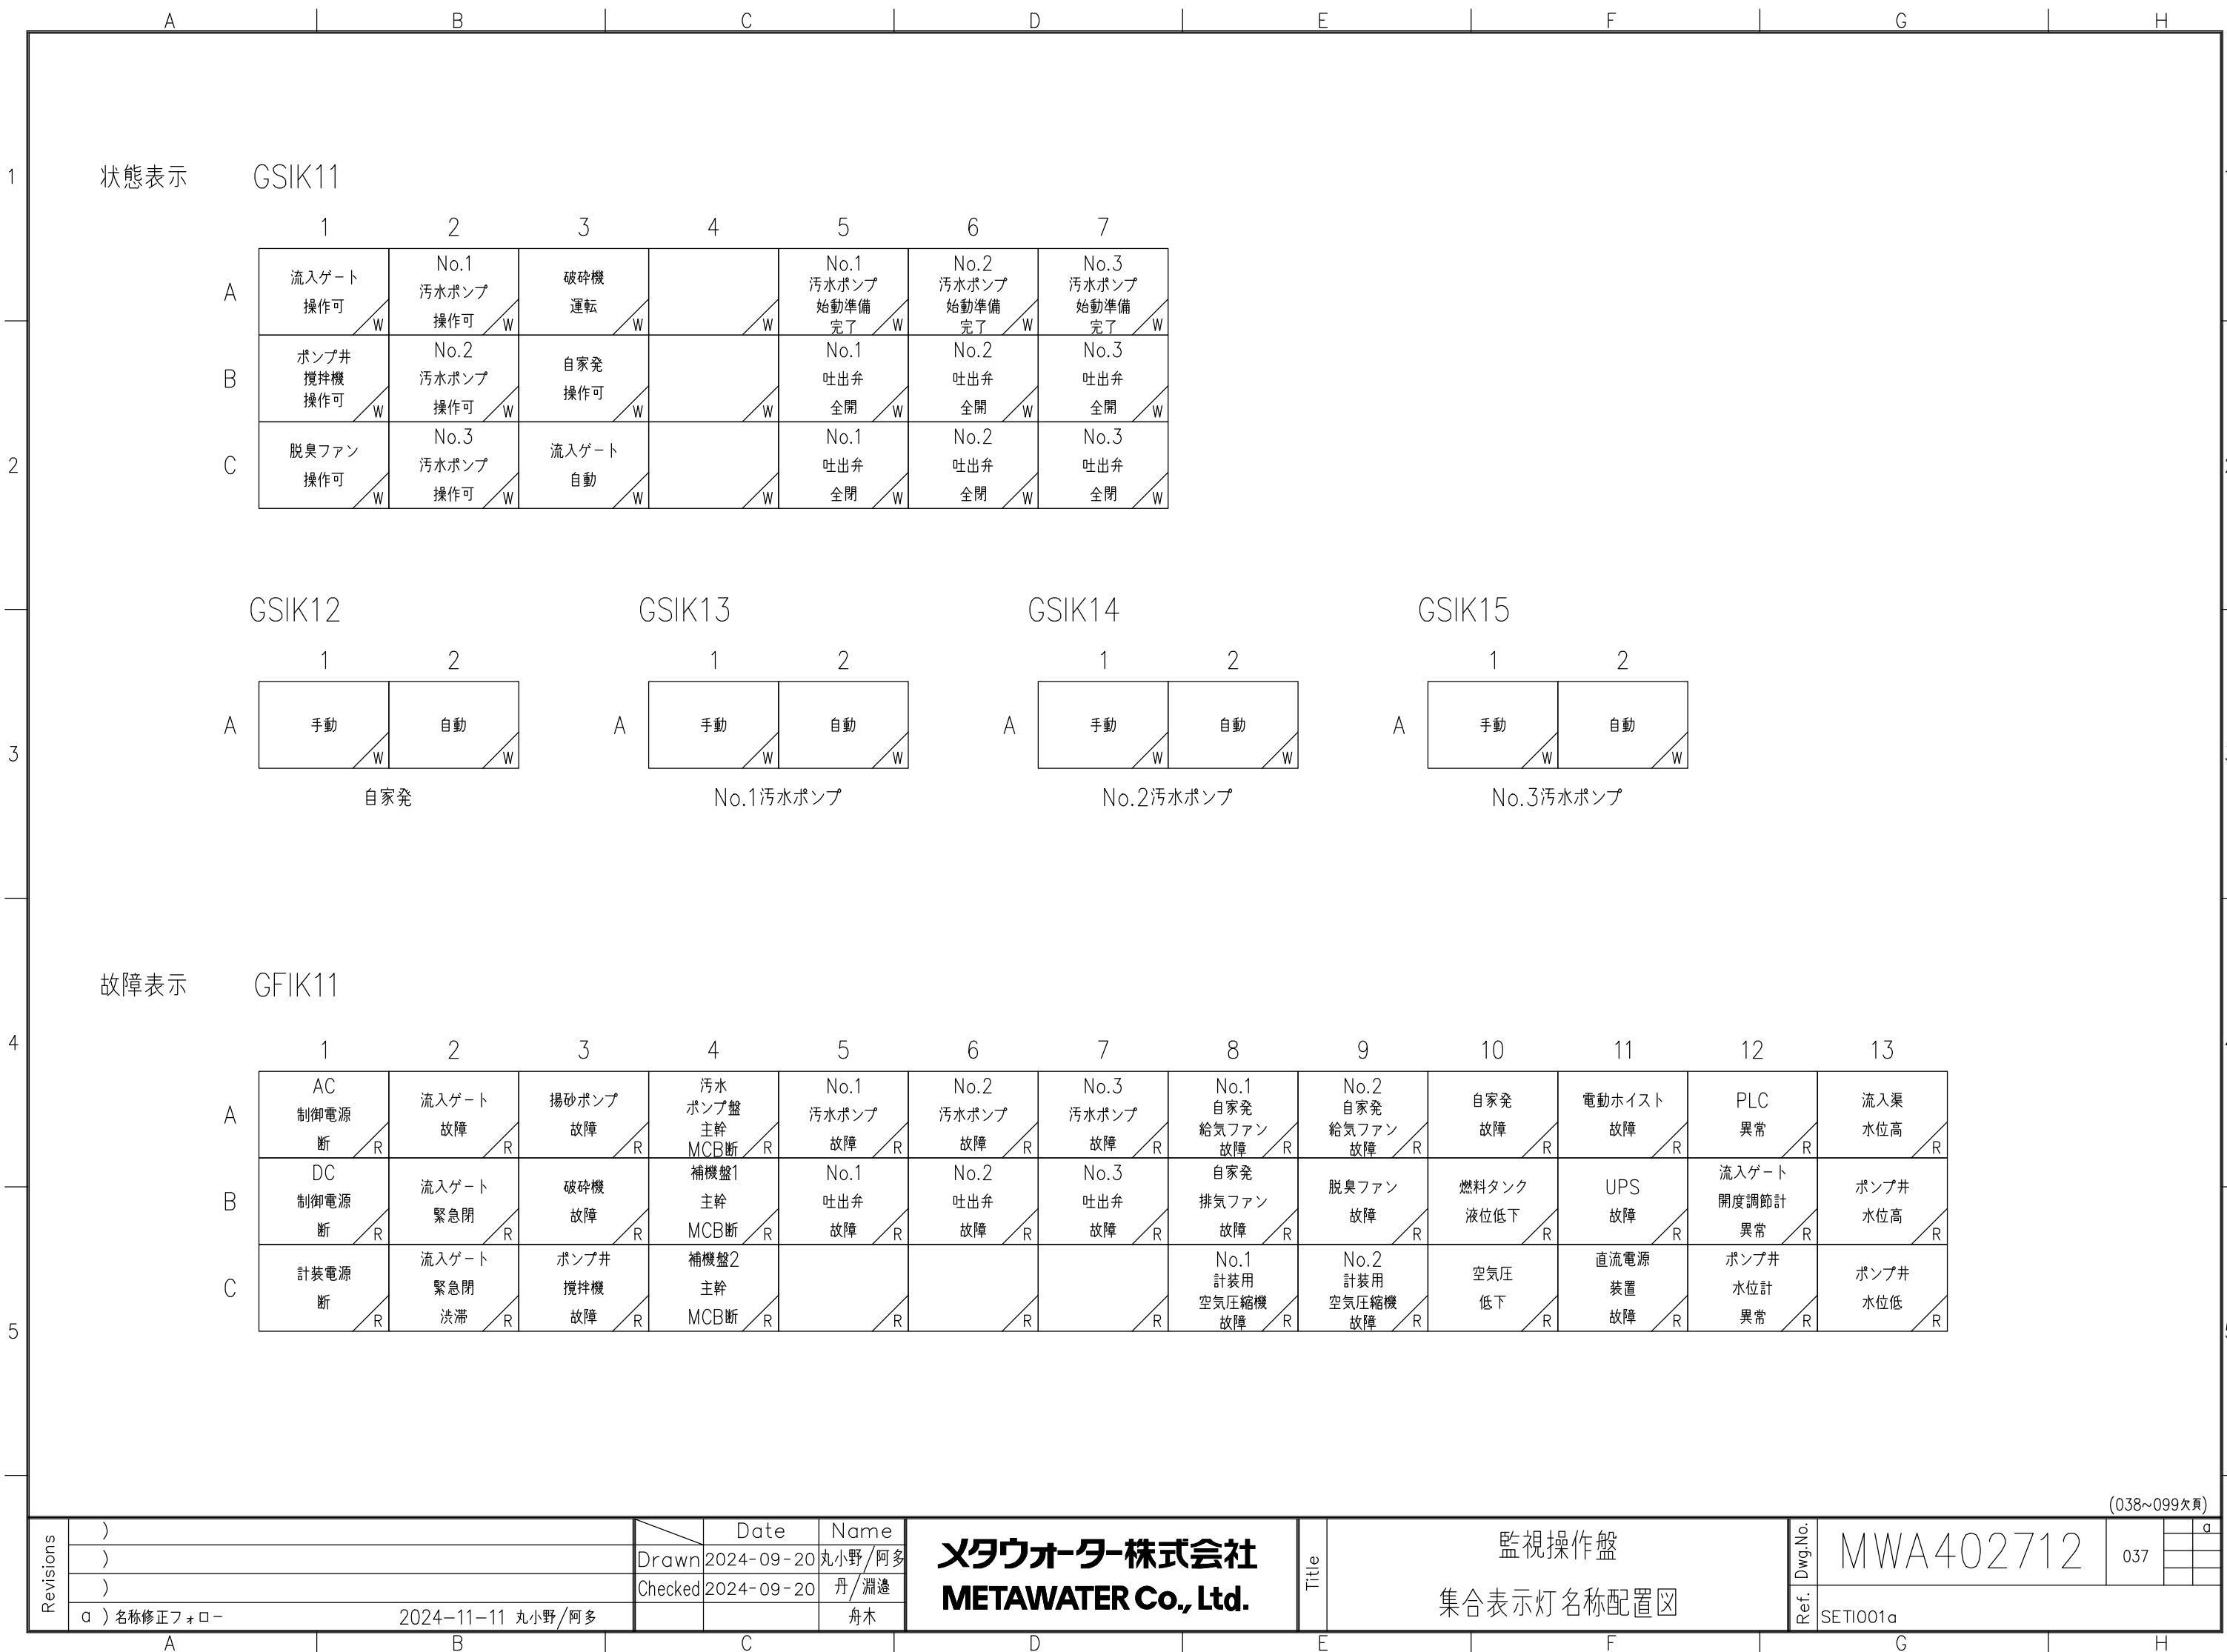

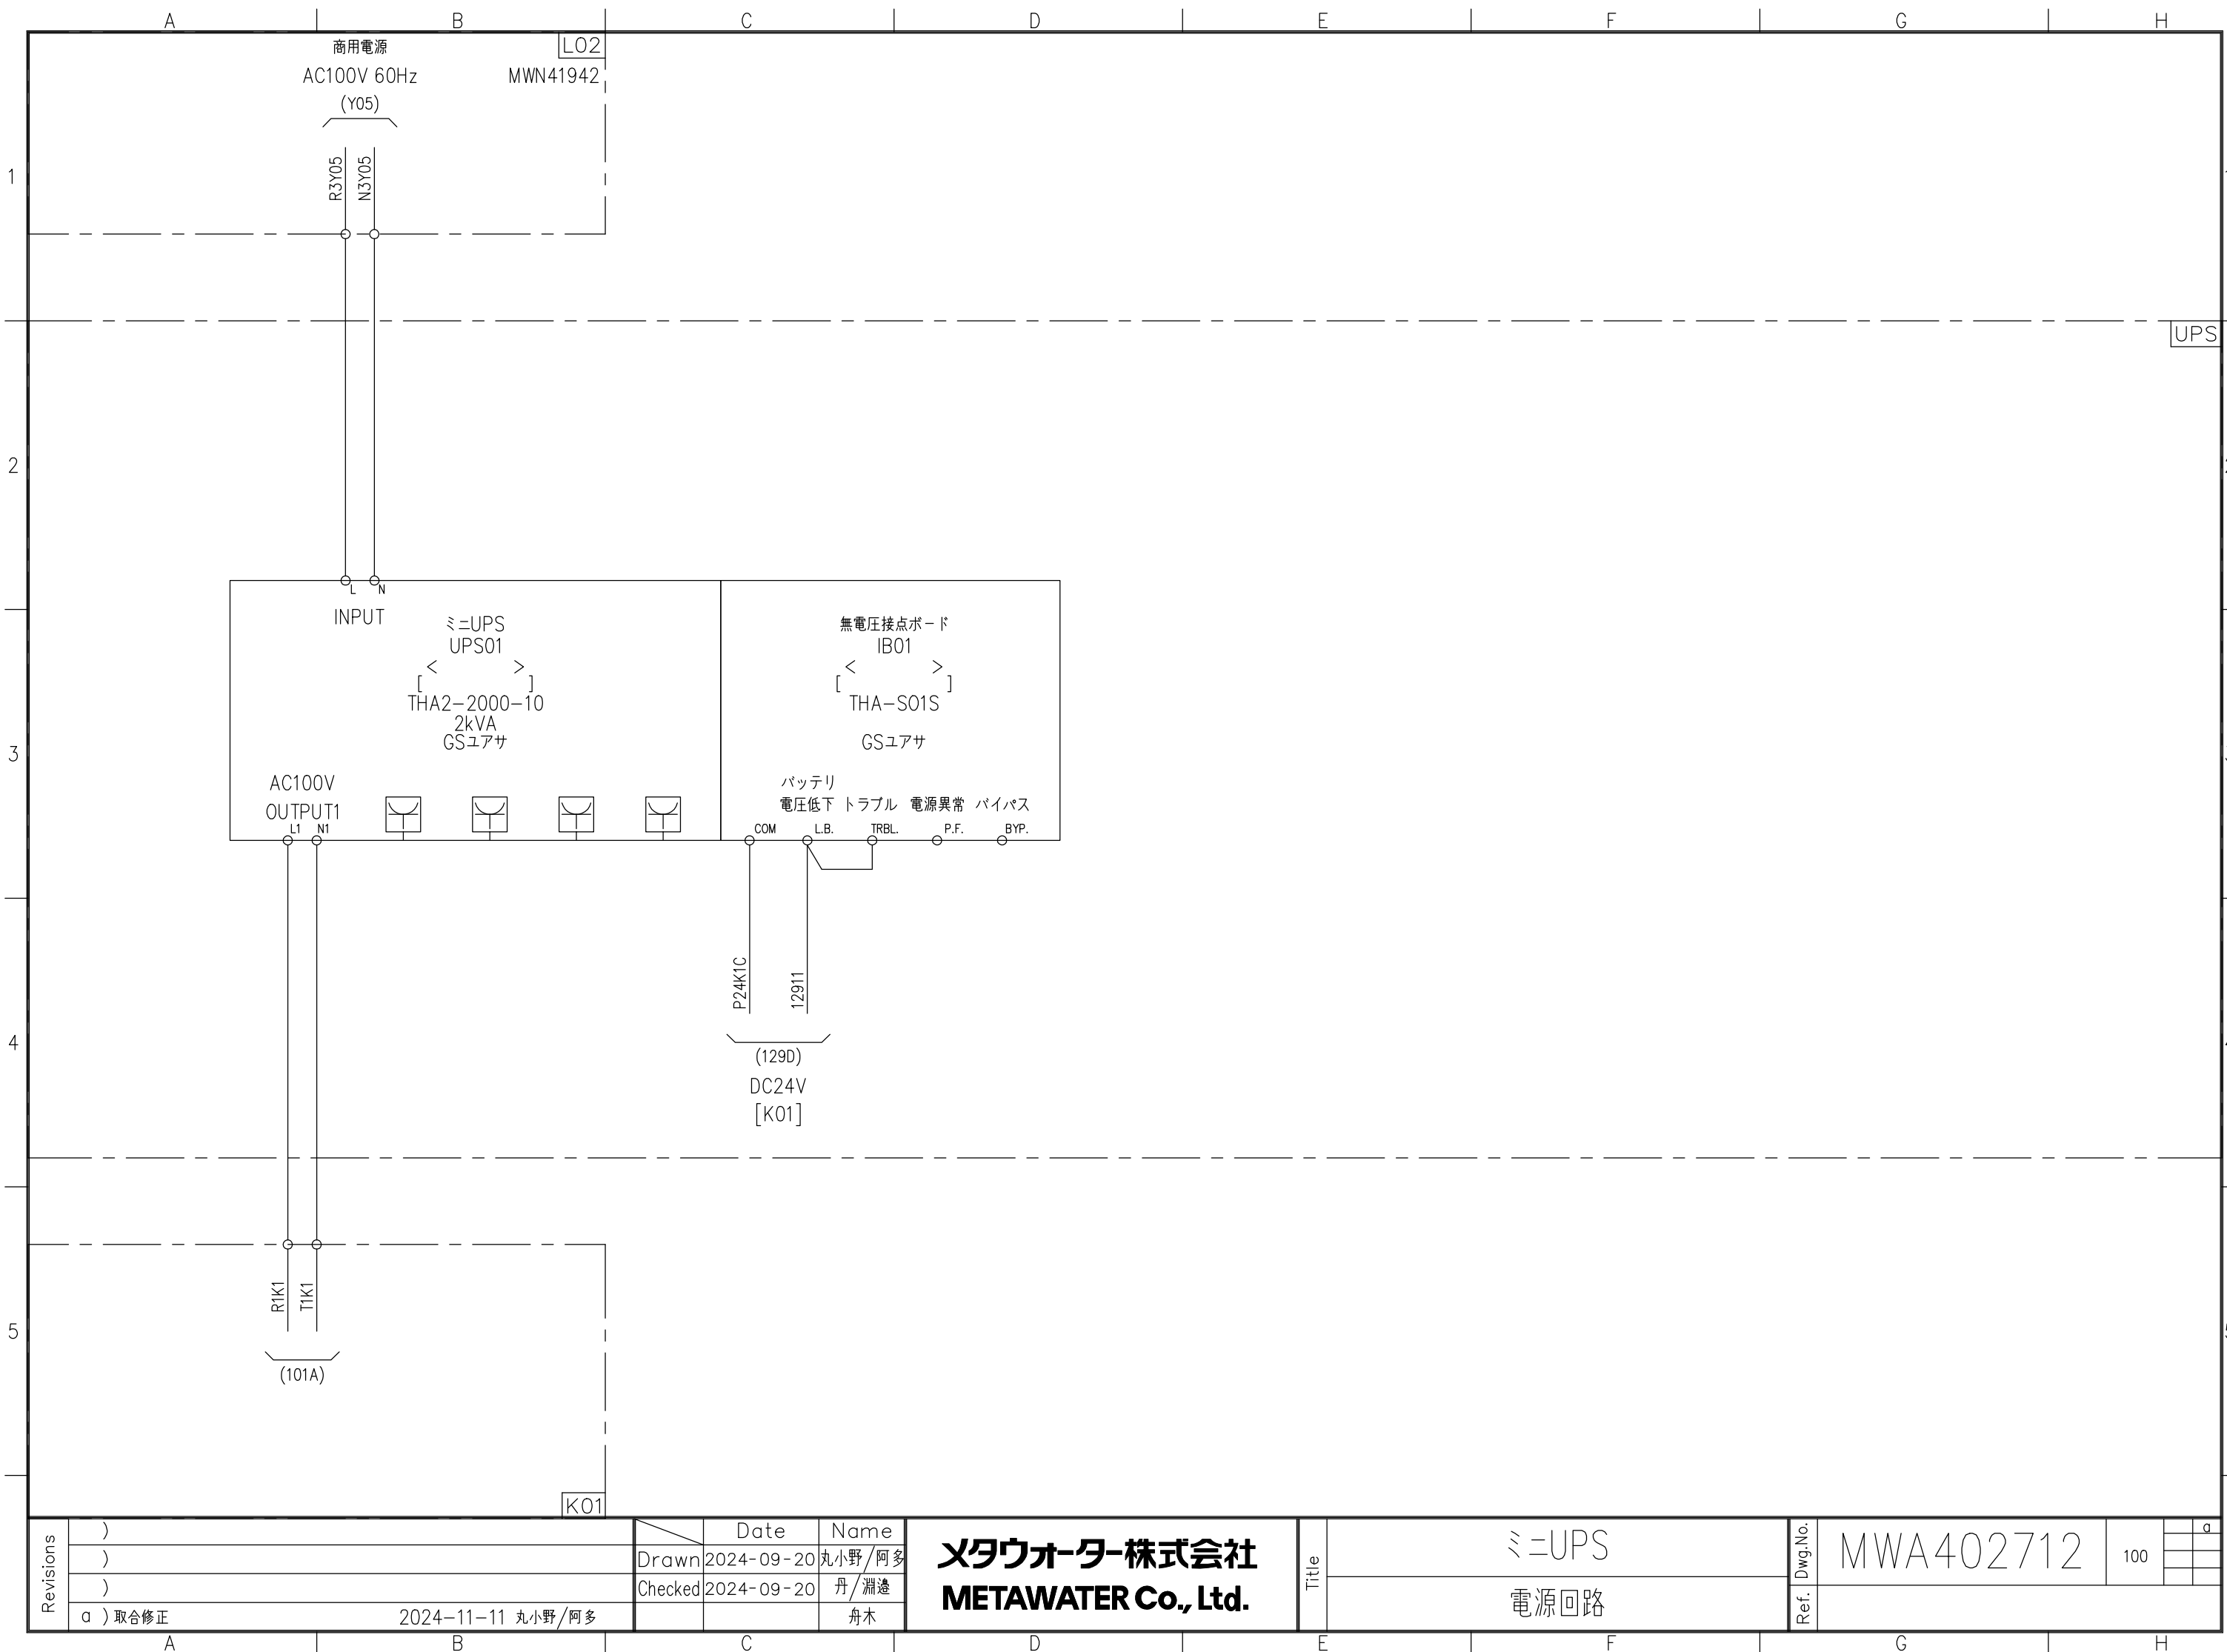

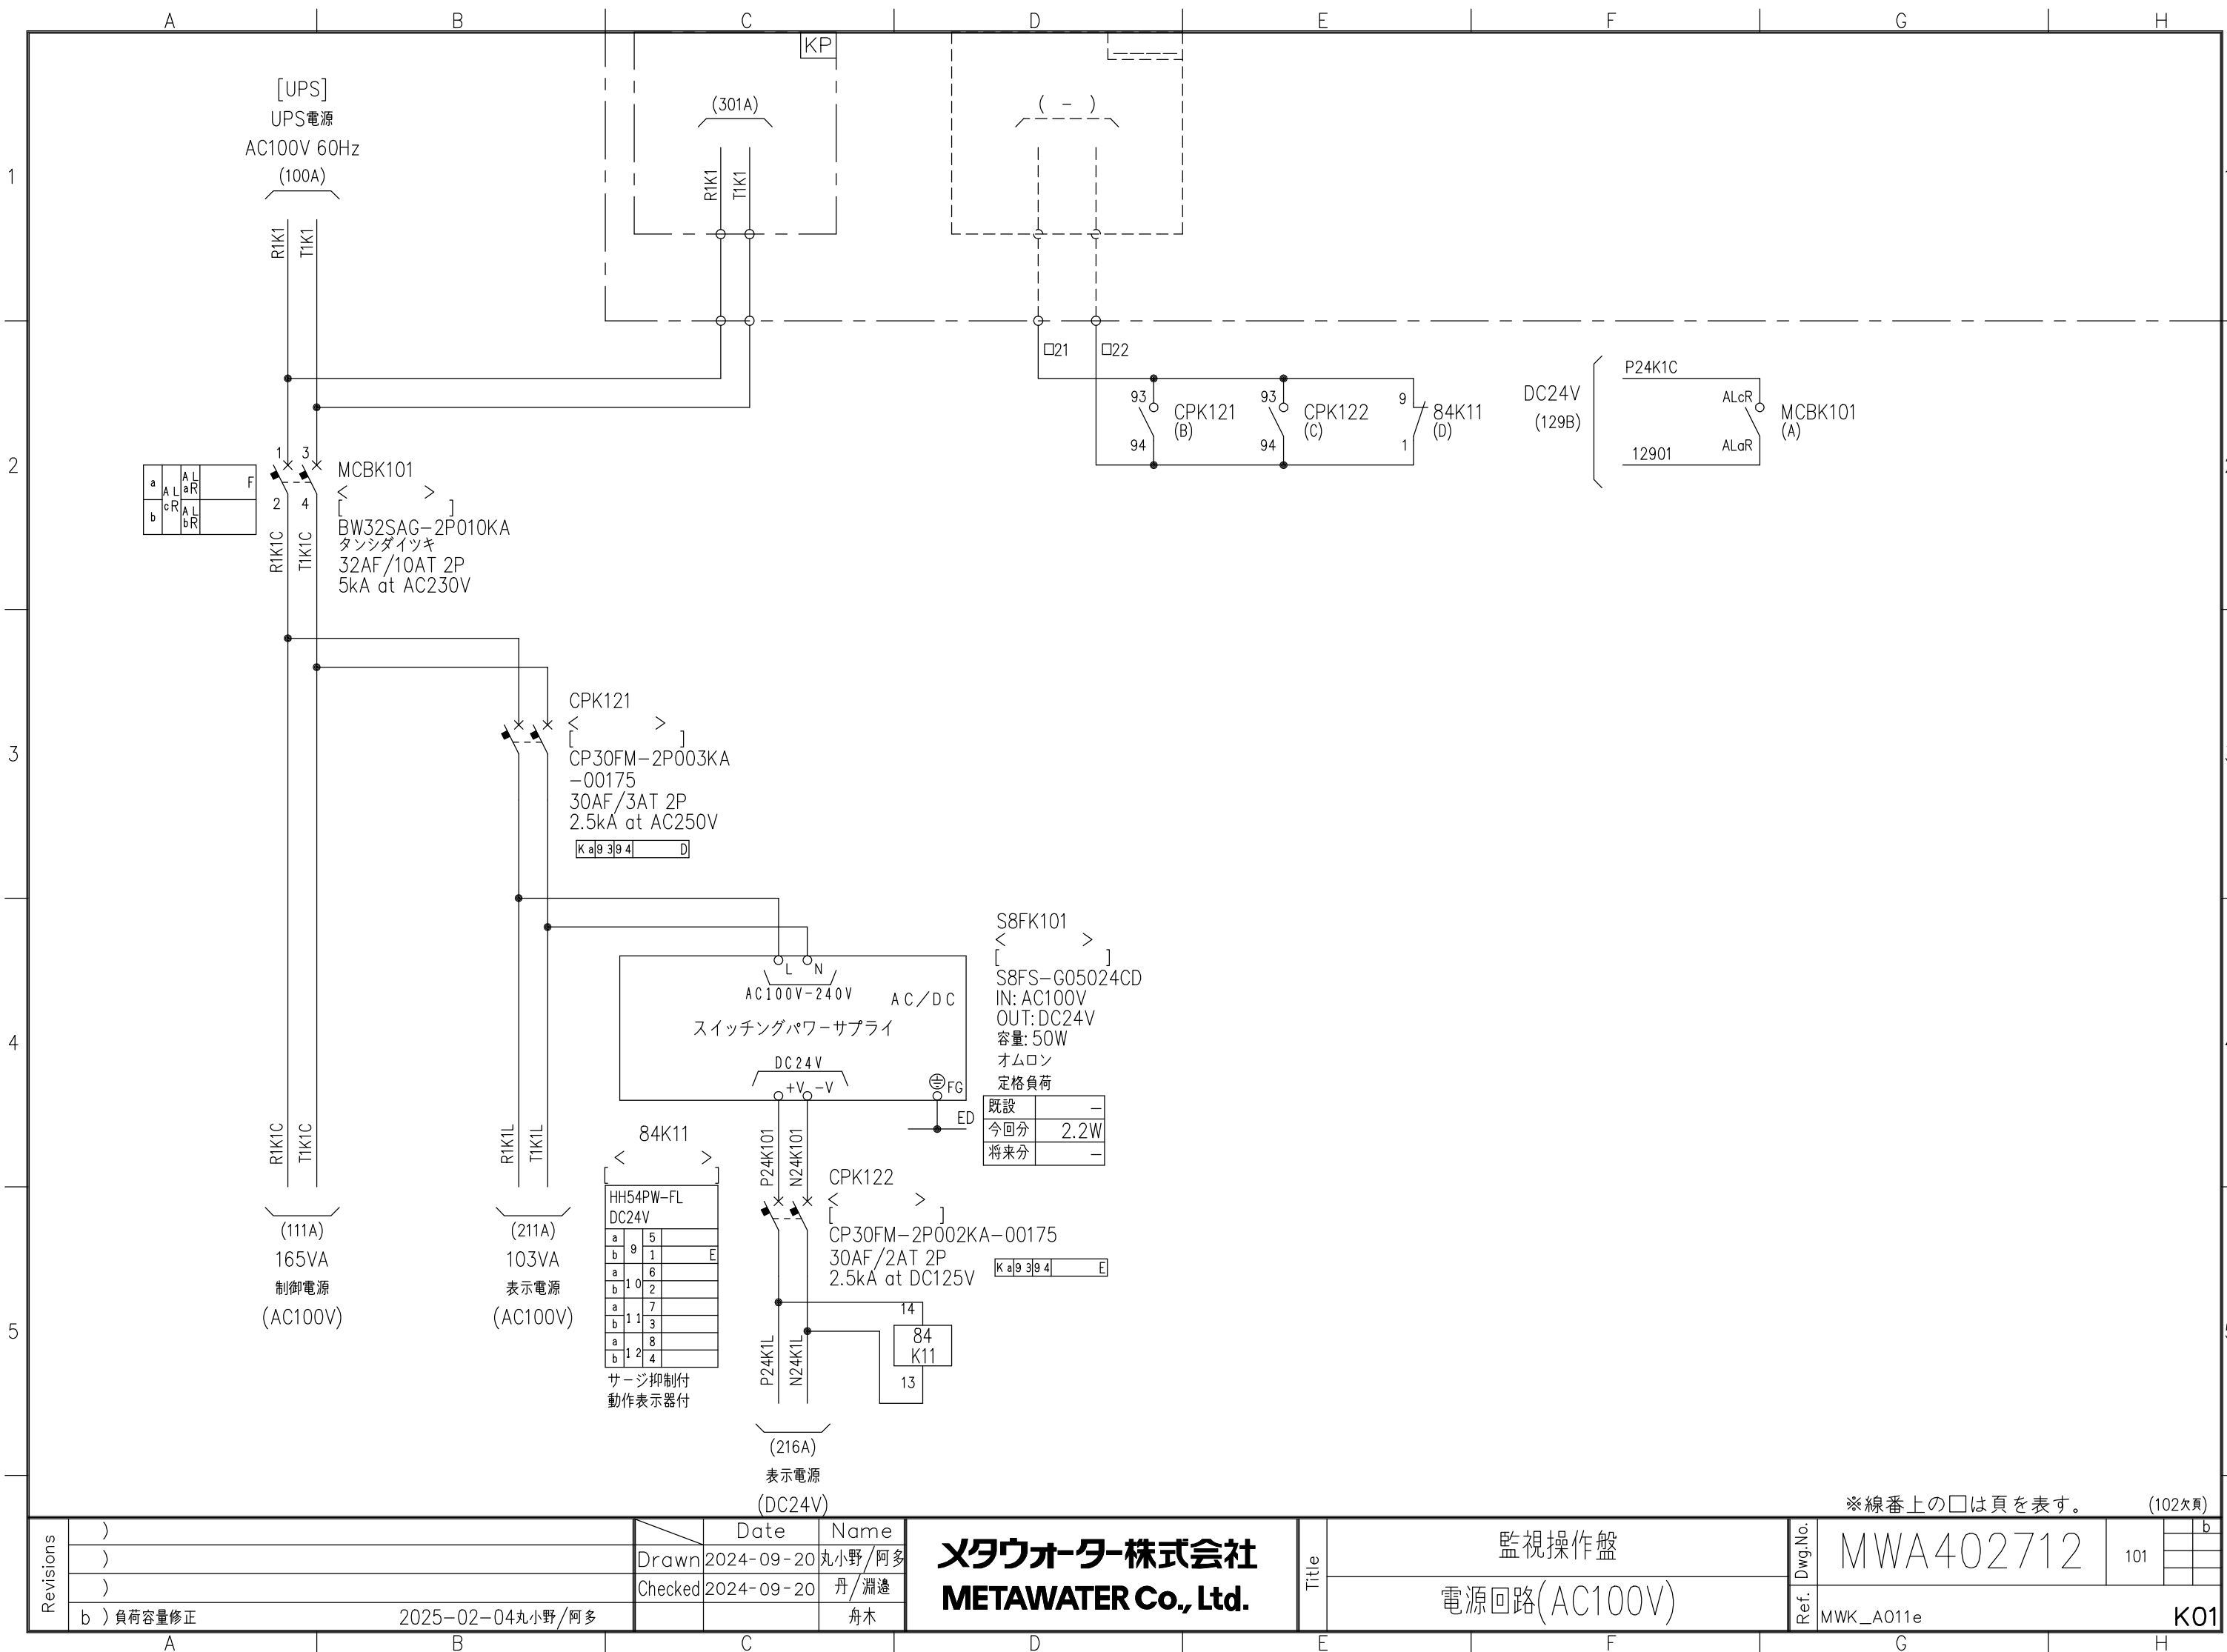

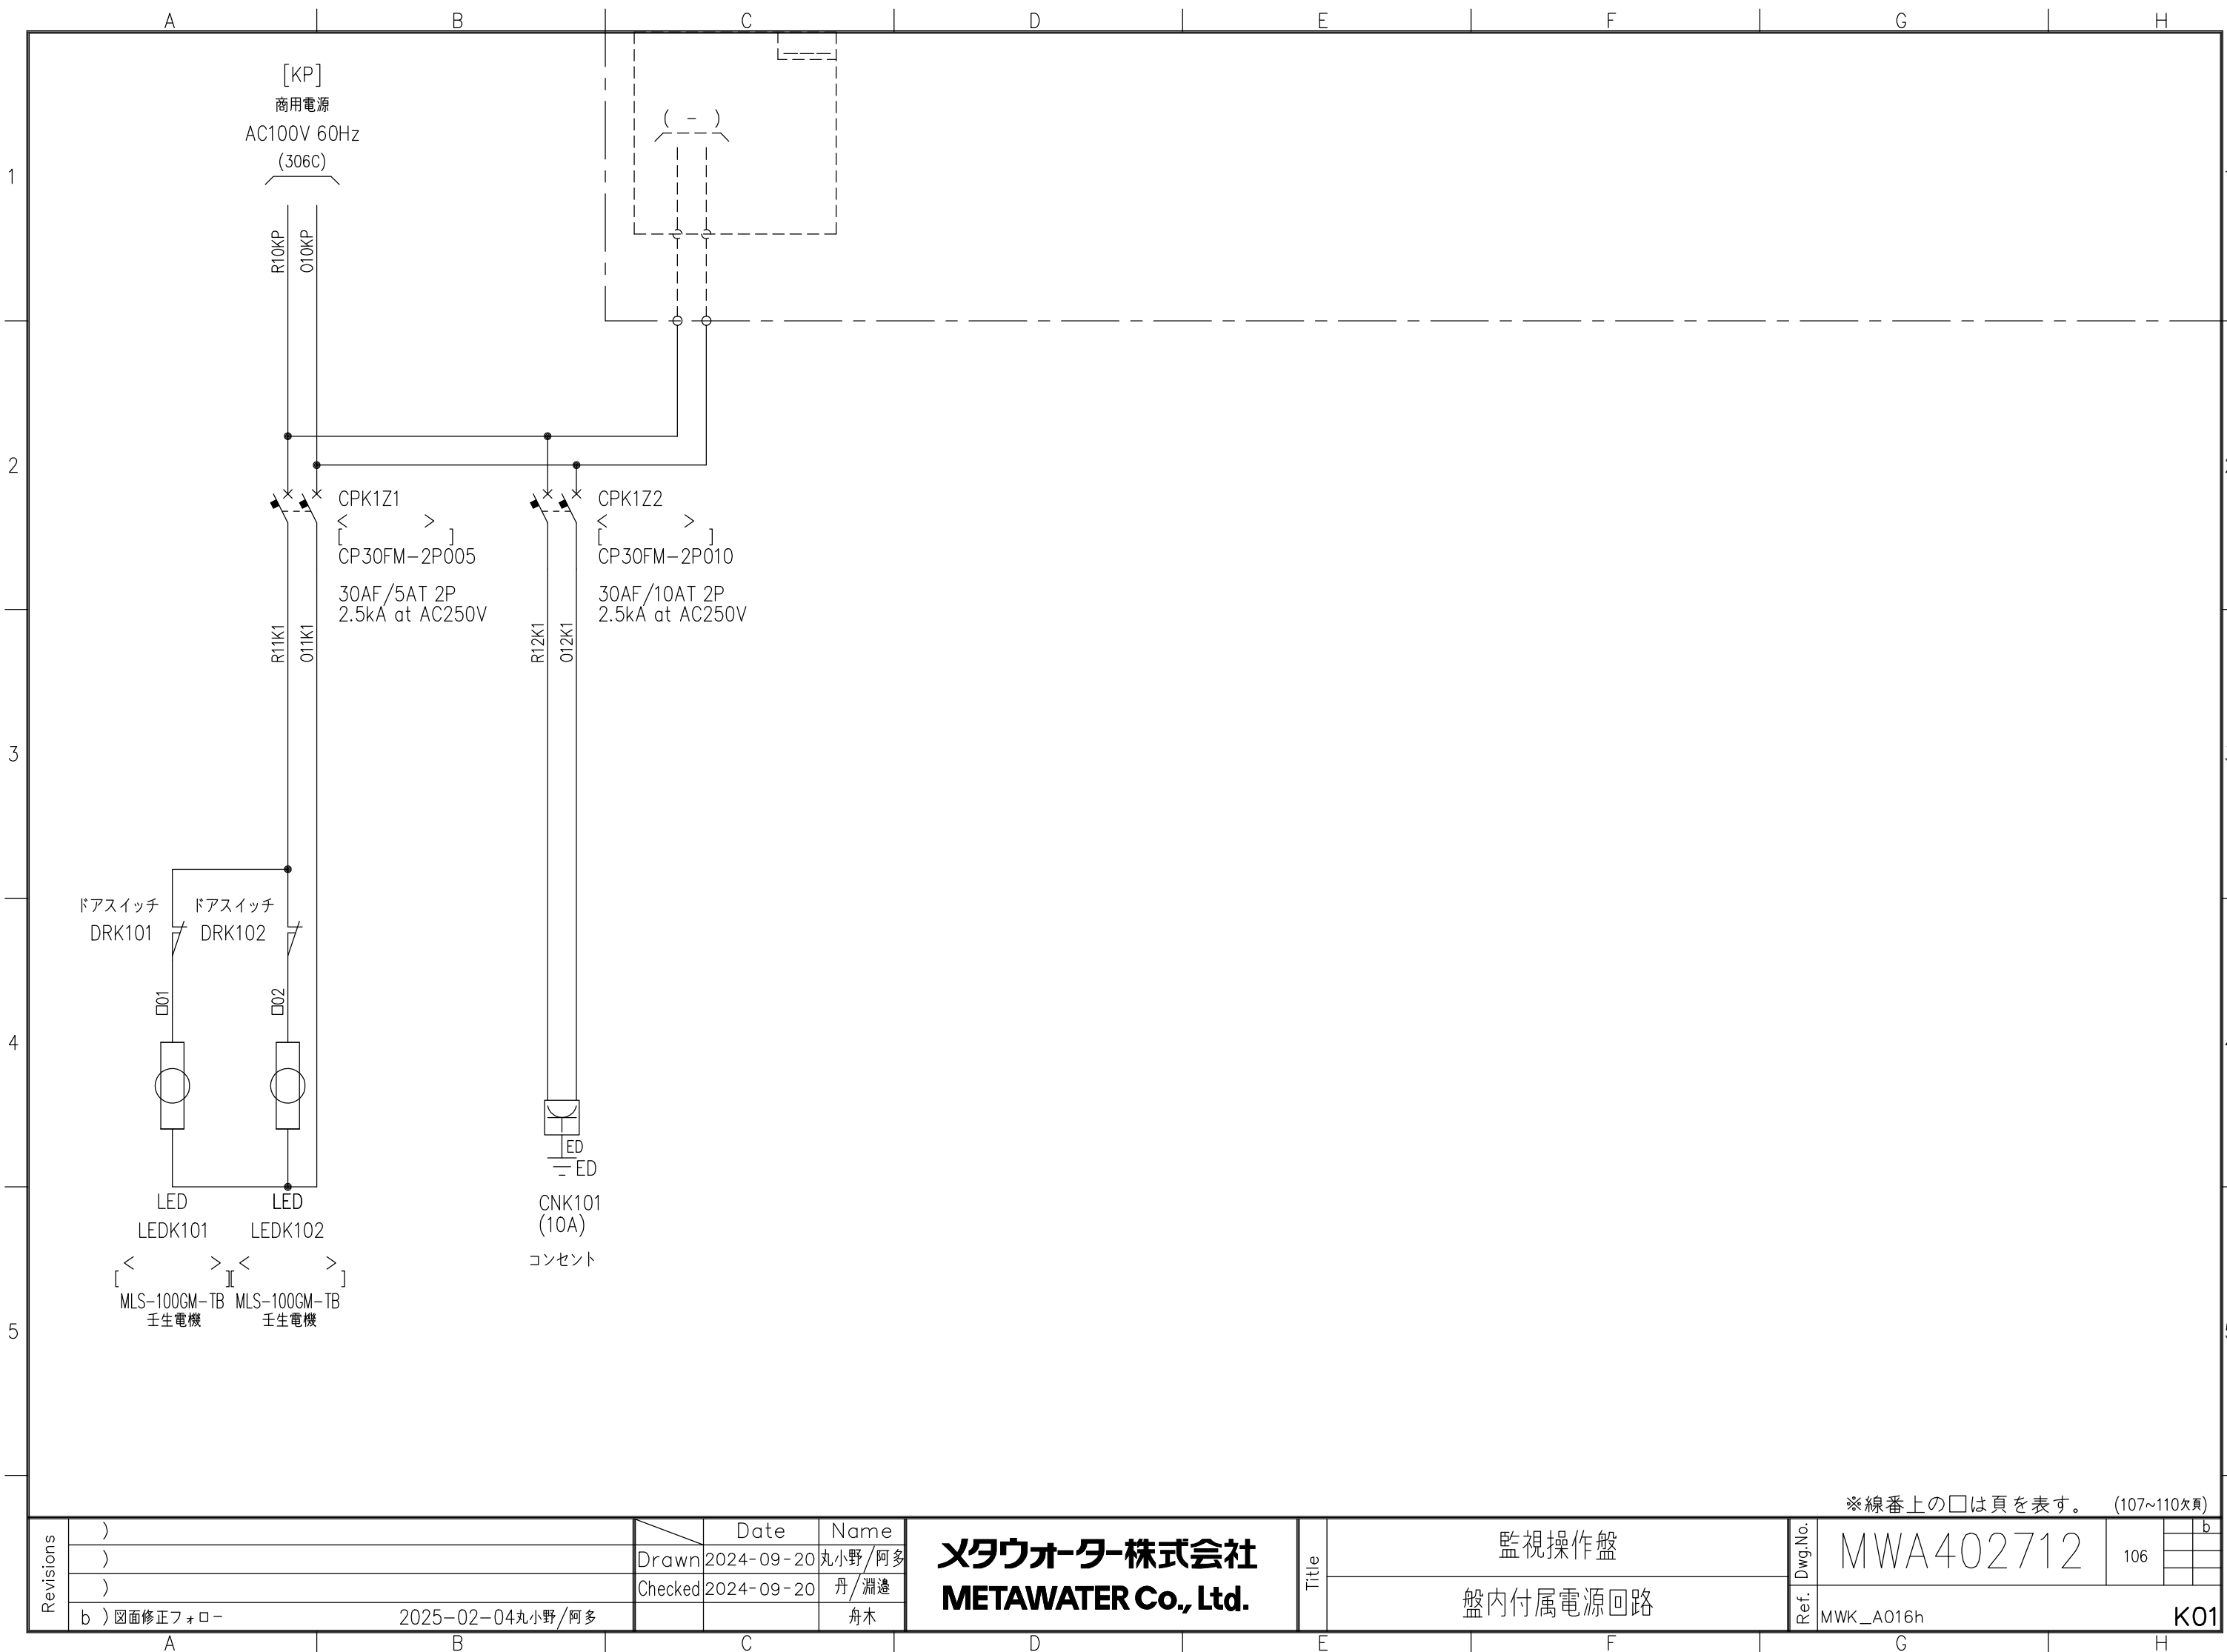


※線番上の□は頁を表す。(107~110欠頁)

Revisions	)		Date	Name	メタウォーター株式会社 METAWATER Co., Ltd.	Title	監視操作盤		Dwg.No.	MWA402712	106		b
	)	Drawn	2024-09-20	丸小野/阿多									
	)	Checked	2024-09-20	丹/淵邊			盤内付属電源回路		Ref.	MWK_A016h		K01	
	b) 図面修正フォロー		2025-02-04	丸小野/阿多									



Revisions	)		Date	Name	メタウォーター株式会社 METAWATER Co., Ltd.	Title	監視操作盤	Dwg.No.	MWA402712	111		b
	)	Drawn	2024-09-20	丸小野 / 阿多								
	)	Checked	2024-09-20	丹 / 淵邊			信号受信回路	Ref.	KW02_02_00a	K01		
	b) 取合追記	2025-02-04	丸小野 / 阿多	舟木								

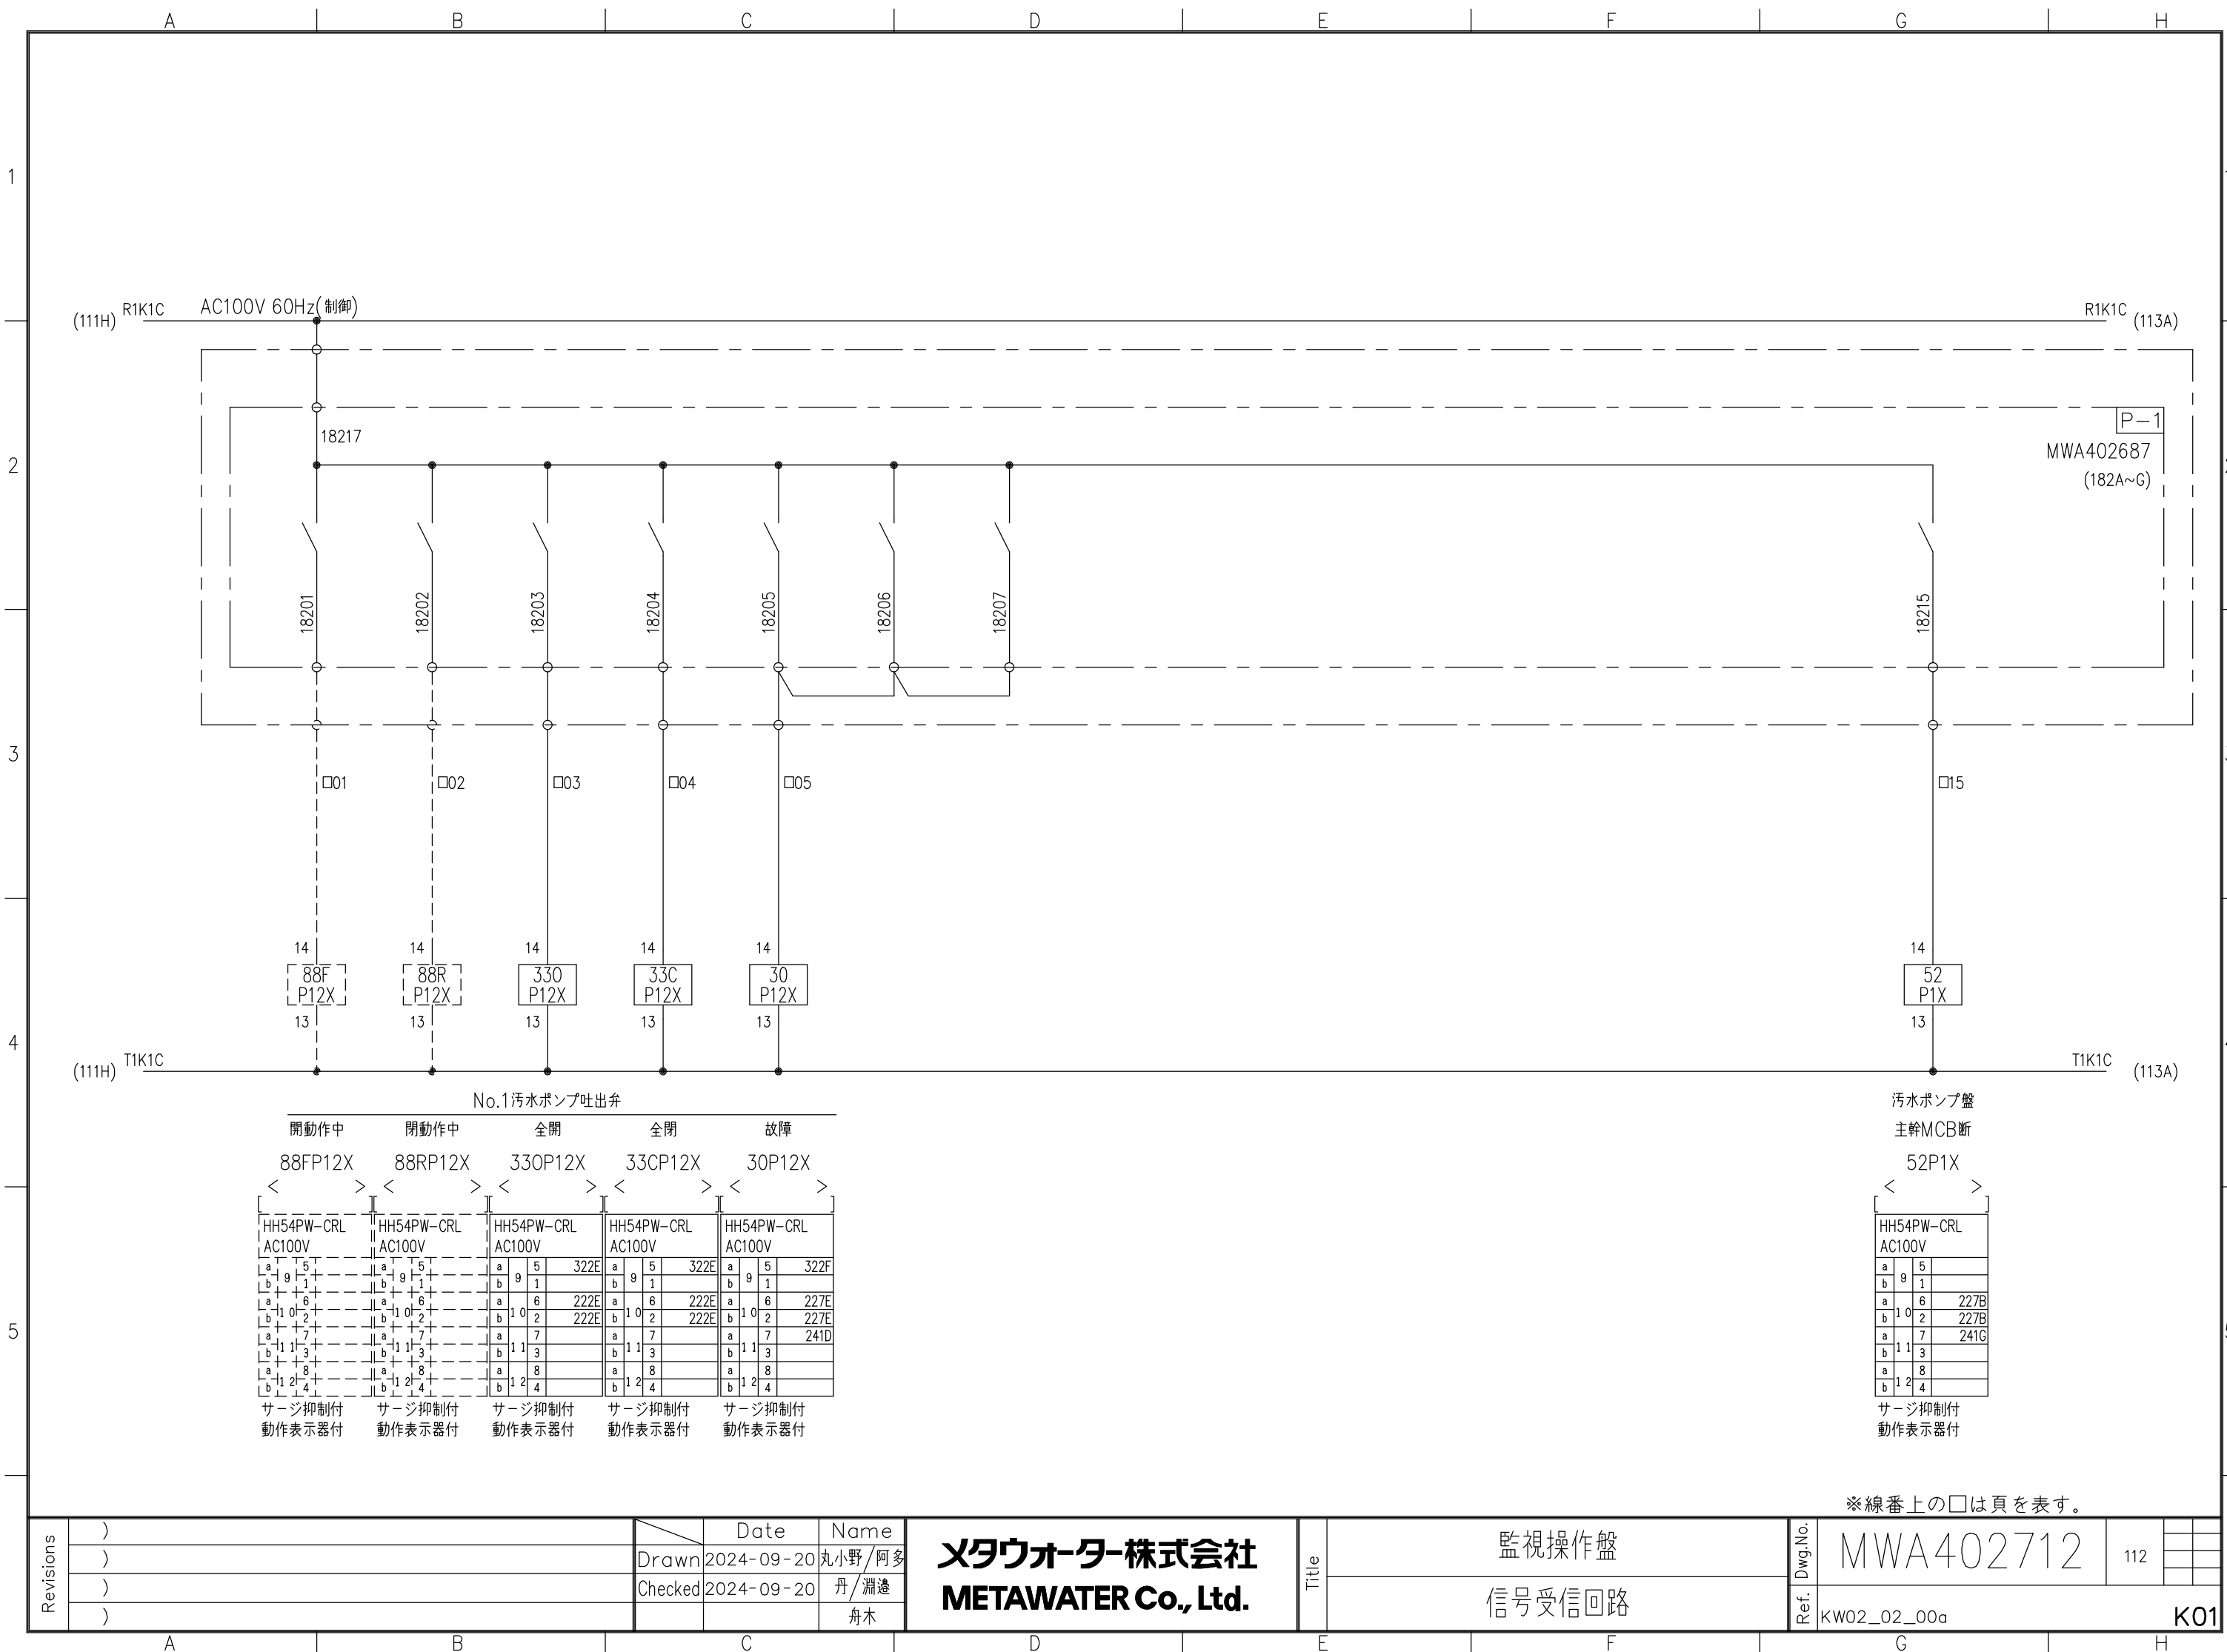




Revisions	)		Date	Name	メタウォーター株式会社 METAWATER Co., Ltd.	Title	監視操作盤	Dwg.No.	MWA402712	113		b
	)	Drawn	2024-09-20	丸小野 / 阿多								
	)	Checked	2024-09-20	丹 / 淵邊			信号受信回路	Ref.	KW02_02_00a	K01		
	b) 取合追記	2025-02-04	丸小野 / 阿多	舟木								




Revisions	)		Date	Name	メタウォーター株式会社 METAWATER Co., Ltd.	Title	監視操作盤	Dwg.No.	MWA402712	114		
	)	Drawn	2024-09-20	丸小野 / 阿多								
	)	Checked	2024-09-20	丹 / 淵邊								
	)			舟木								
							信号受信回路	Ref.	KW02_02_00a		K01	





Revisions	)		Date	Name	メタウォーター株式会社 METAWATER Co., Ltd.	Title	監視操作盤	Dwg.No.	MWA402712	115		b
	)	Drawn	2024-09-20	丸小野 / 阿多								
	)	Checked	2024-09-20	丹 / 淵邊			信号受信回路	Ref.	KW02_02_00a	K01		
	b) 取合追記	2025-02-04	丸小野 / 阿多	舟木								

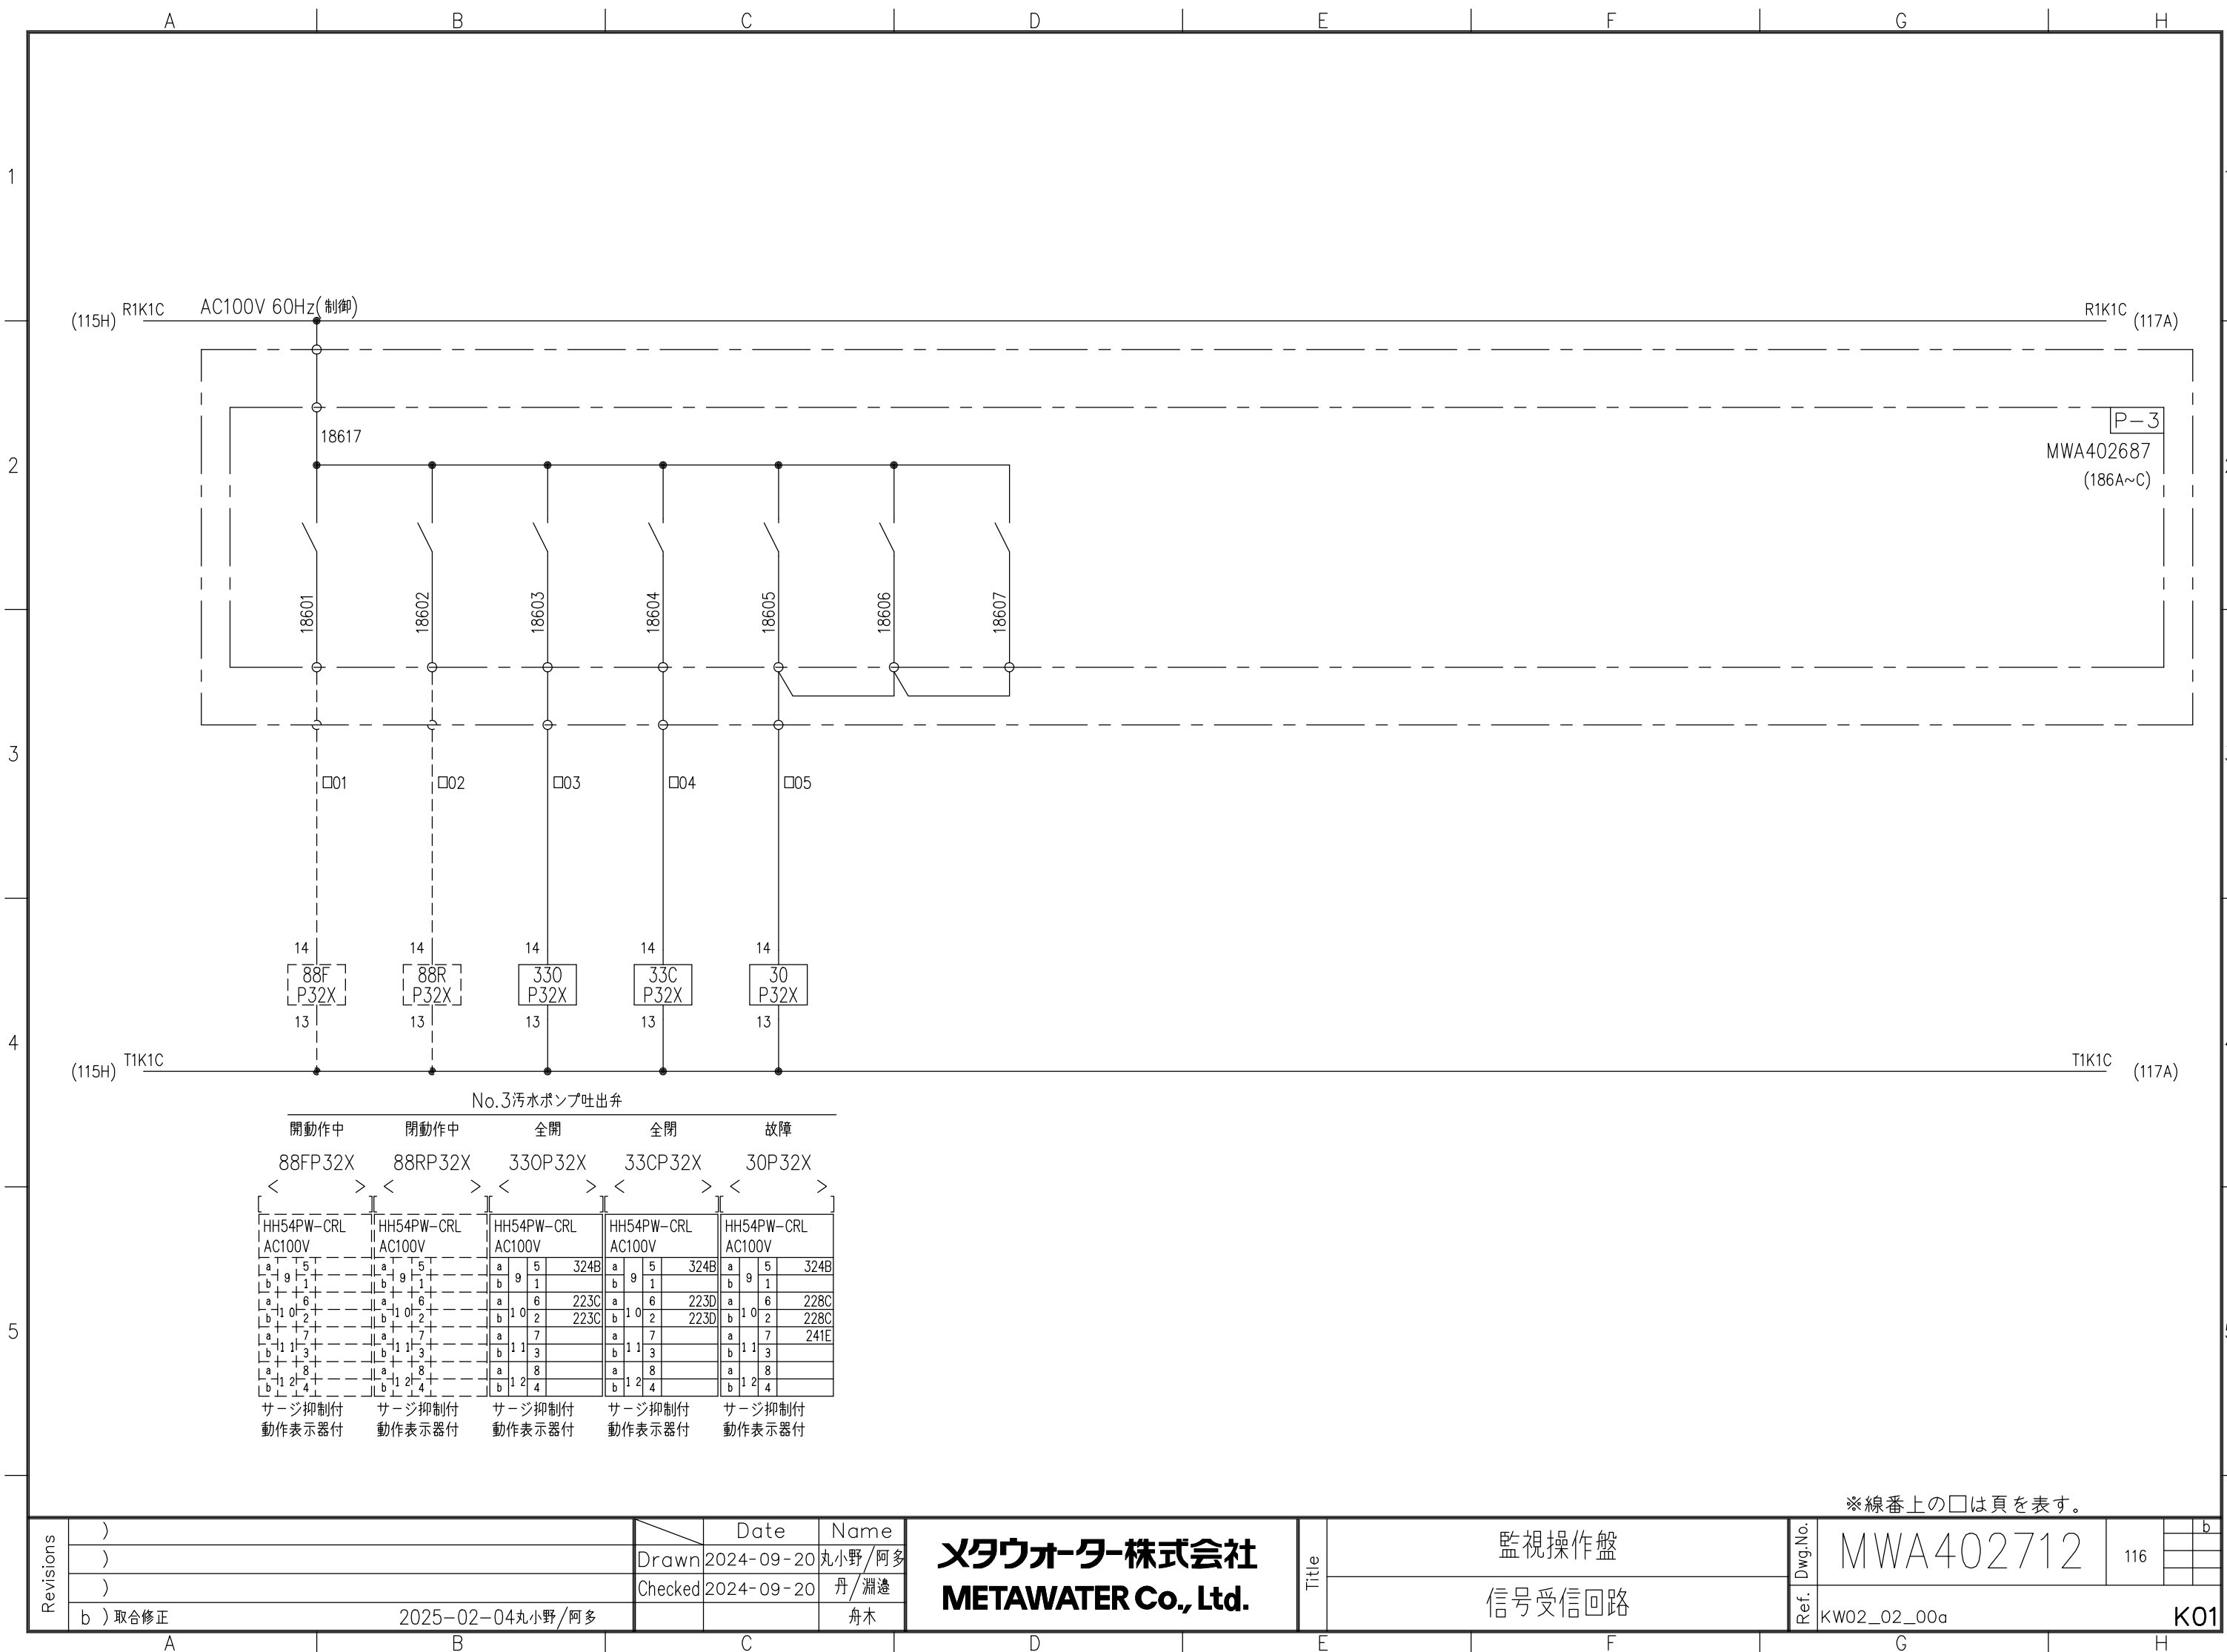



Revisions	)		Date	Name	メタウォーター株式会社 METAWATER Co., Ltd.	Title	監視操作盤	Dwg.No.	MWA402712	116		b
	)	Drawn	2024-09-20	丸小野/阿多								
	)	Checked	2024-09-20	丹/淵邊			信号受信回路	Ref.	KW02_02_00a	K01		
	b) 取合修正			2025-02-04							丸小野/阿多	舟木

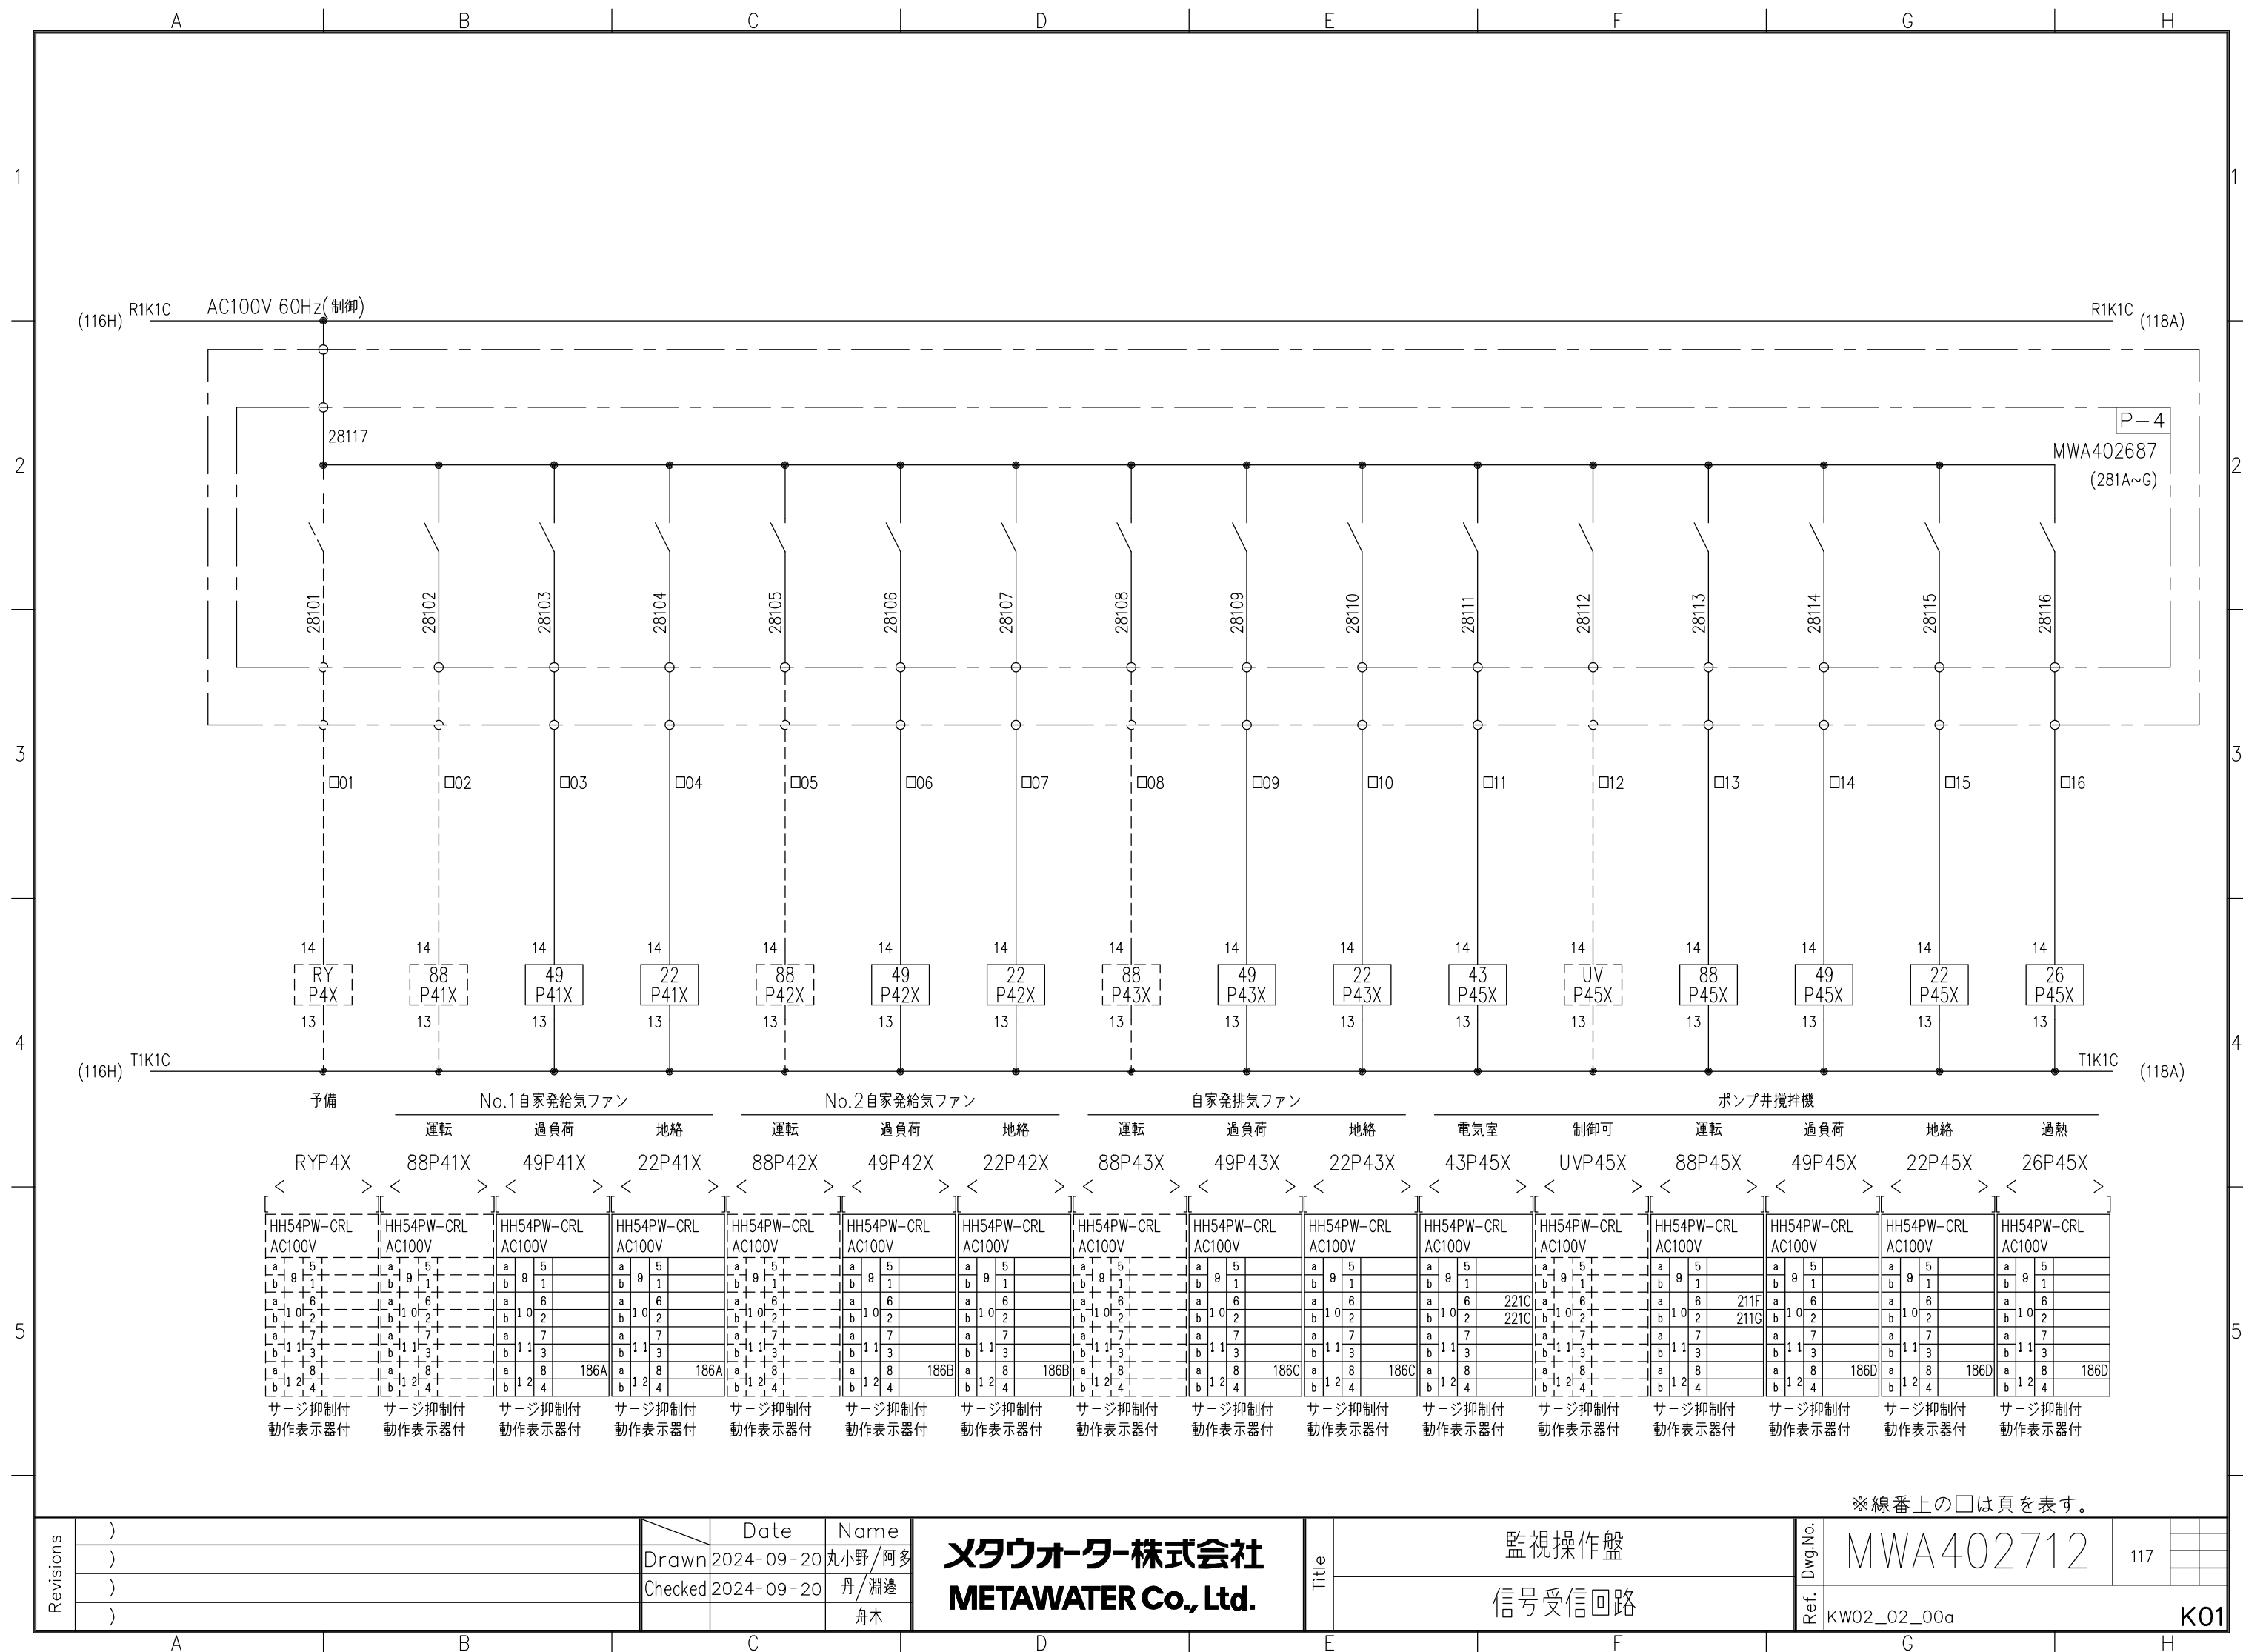

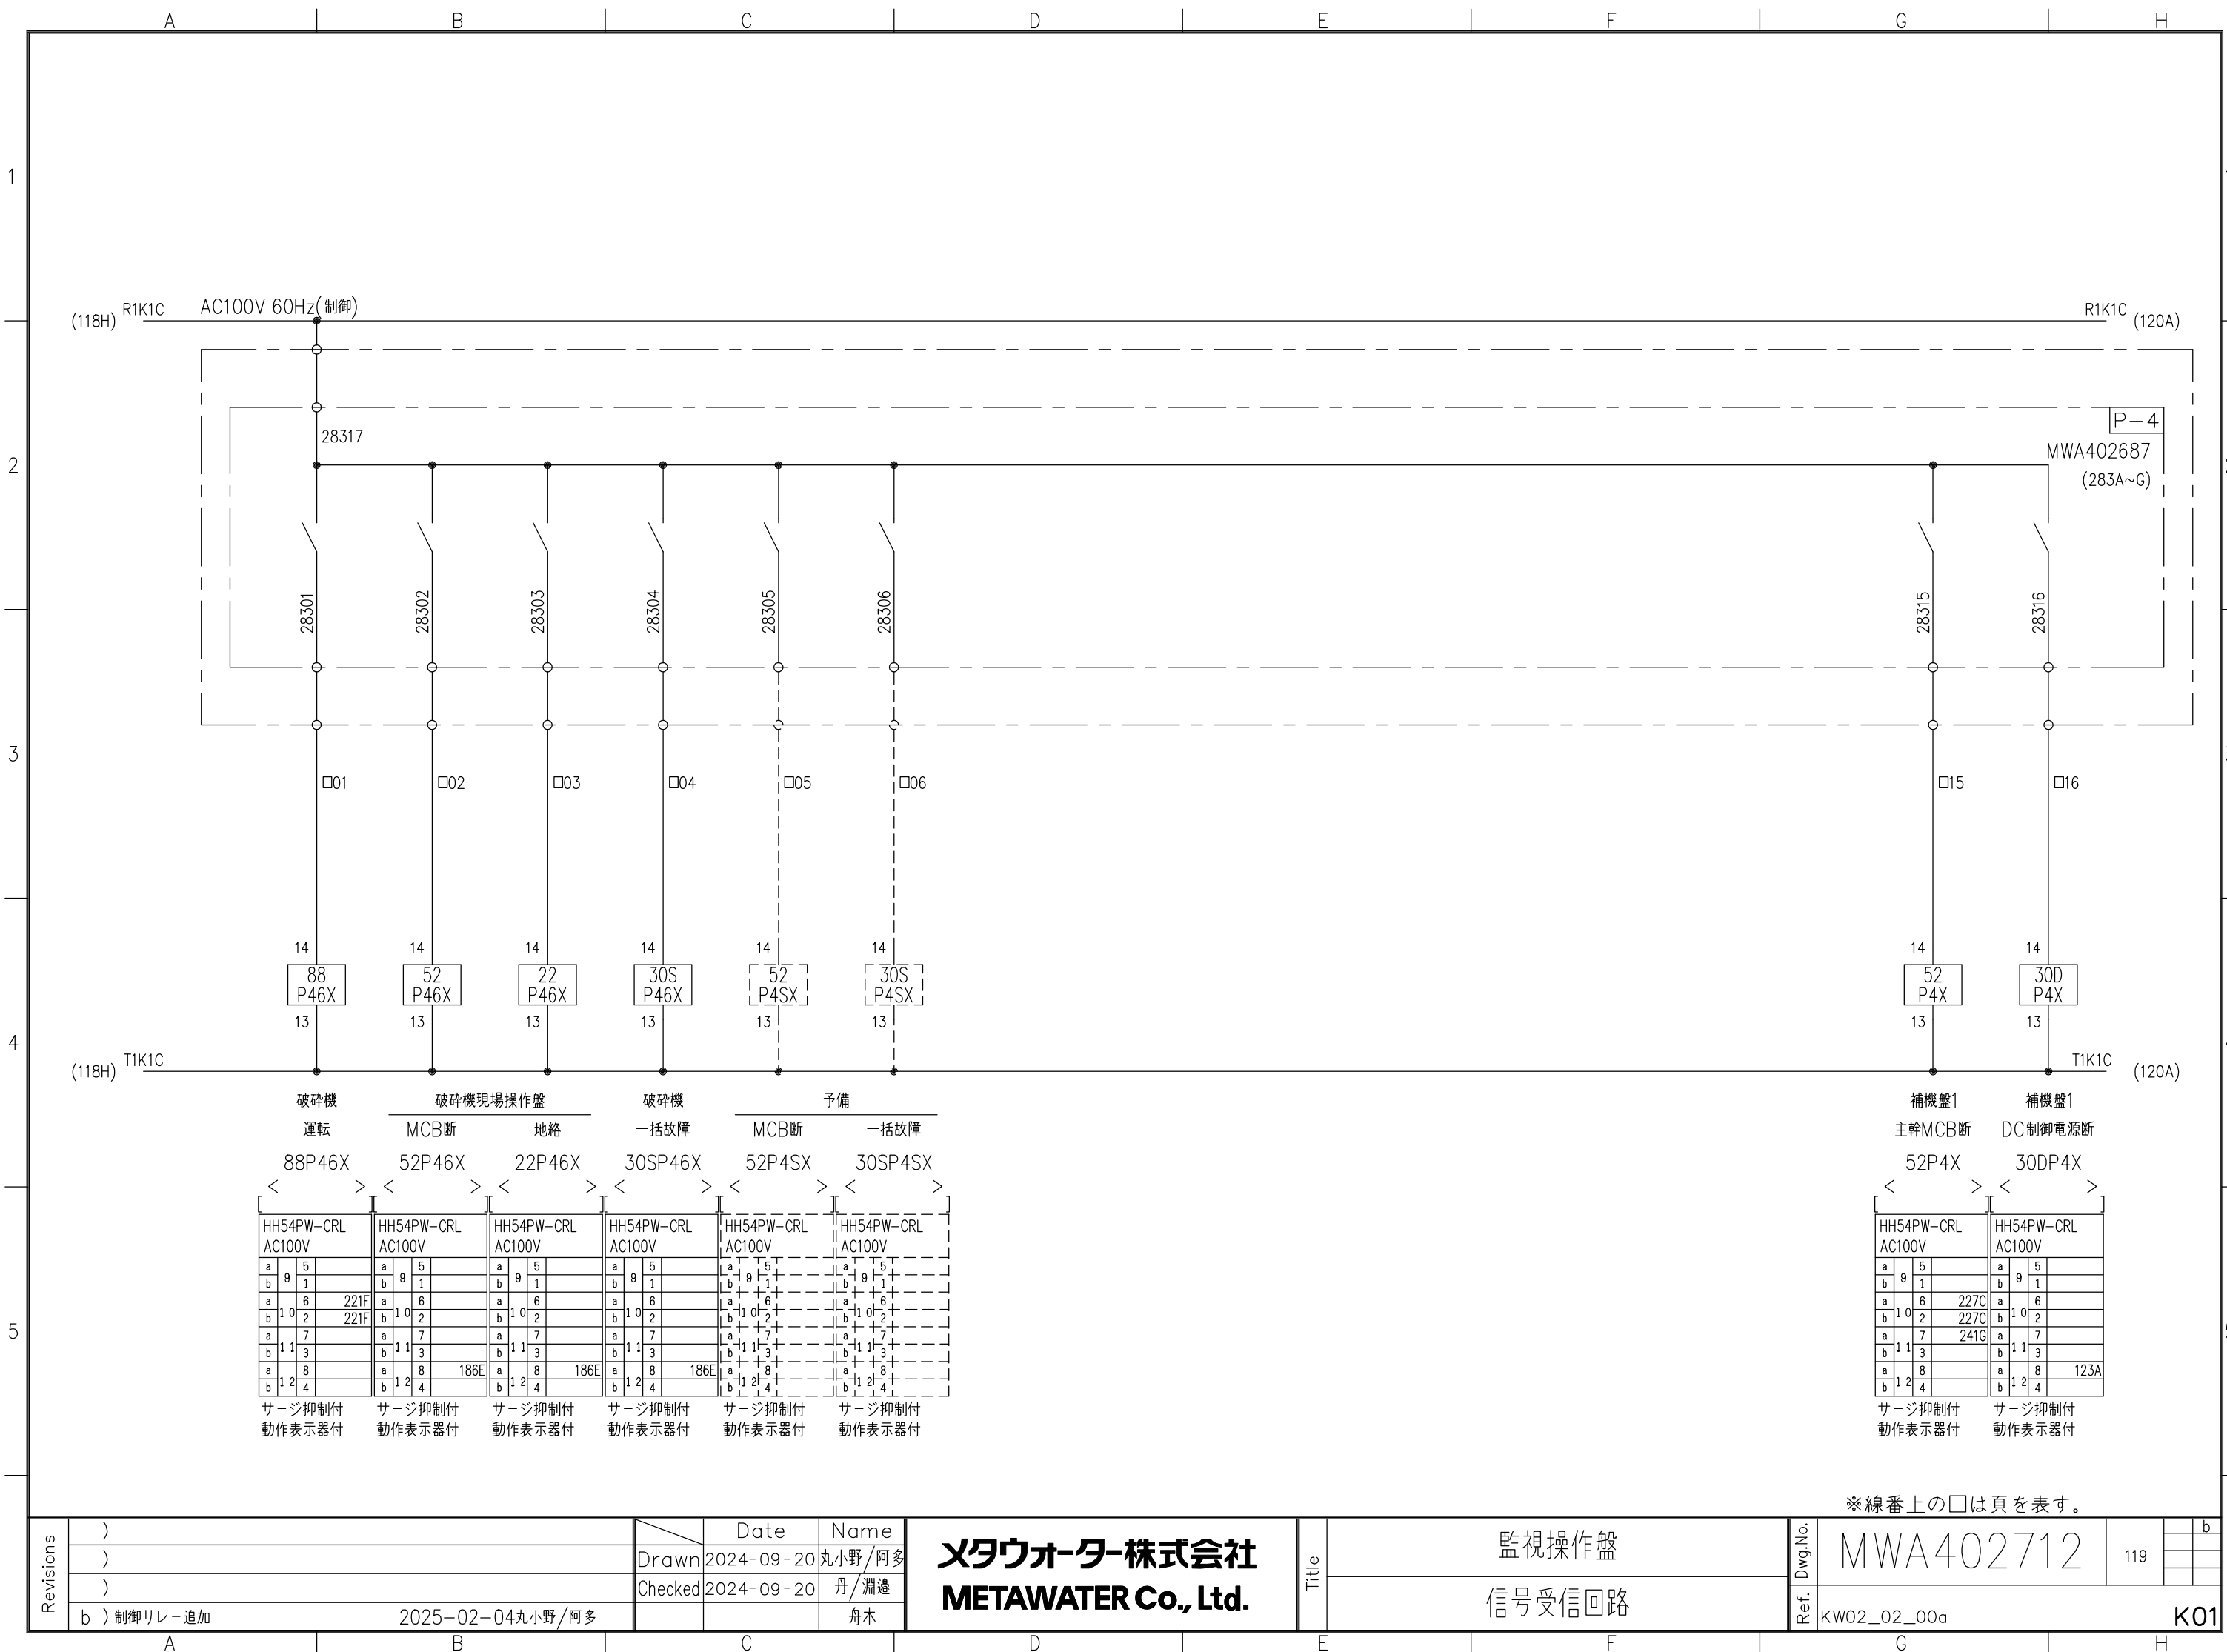

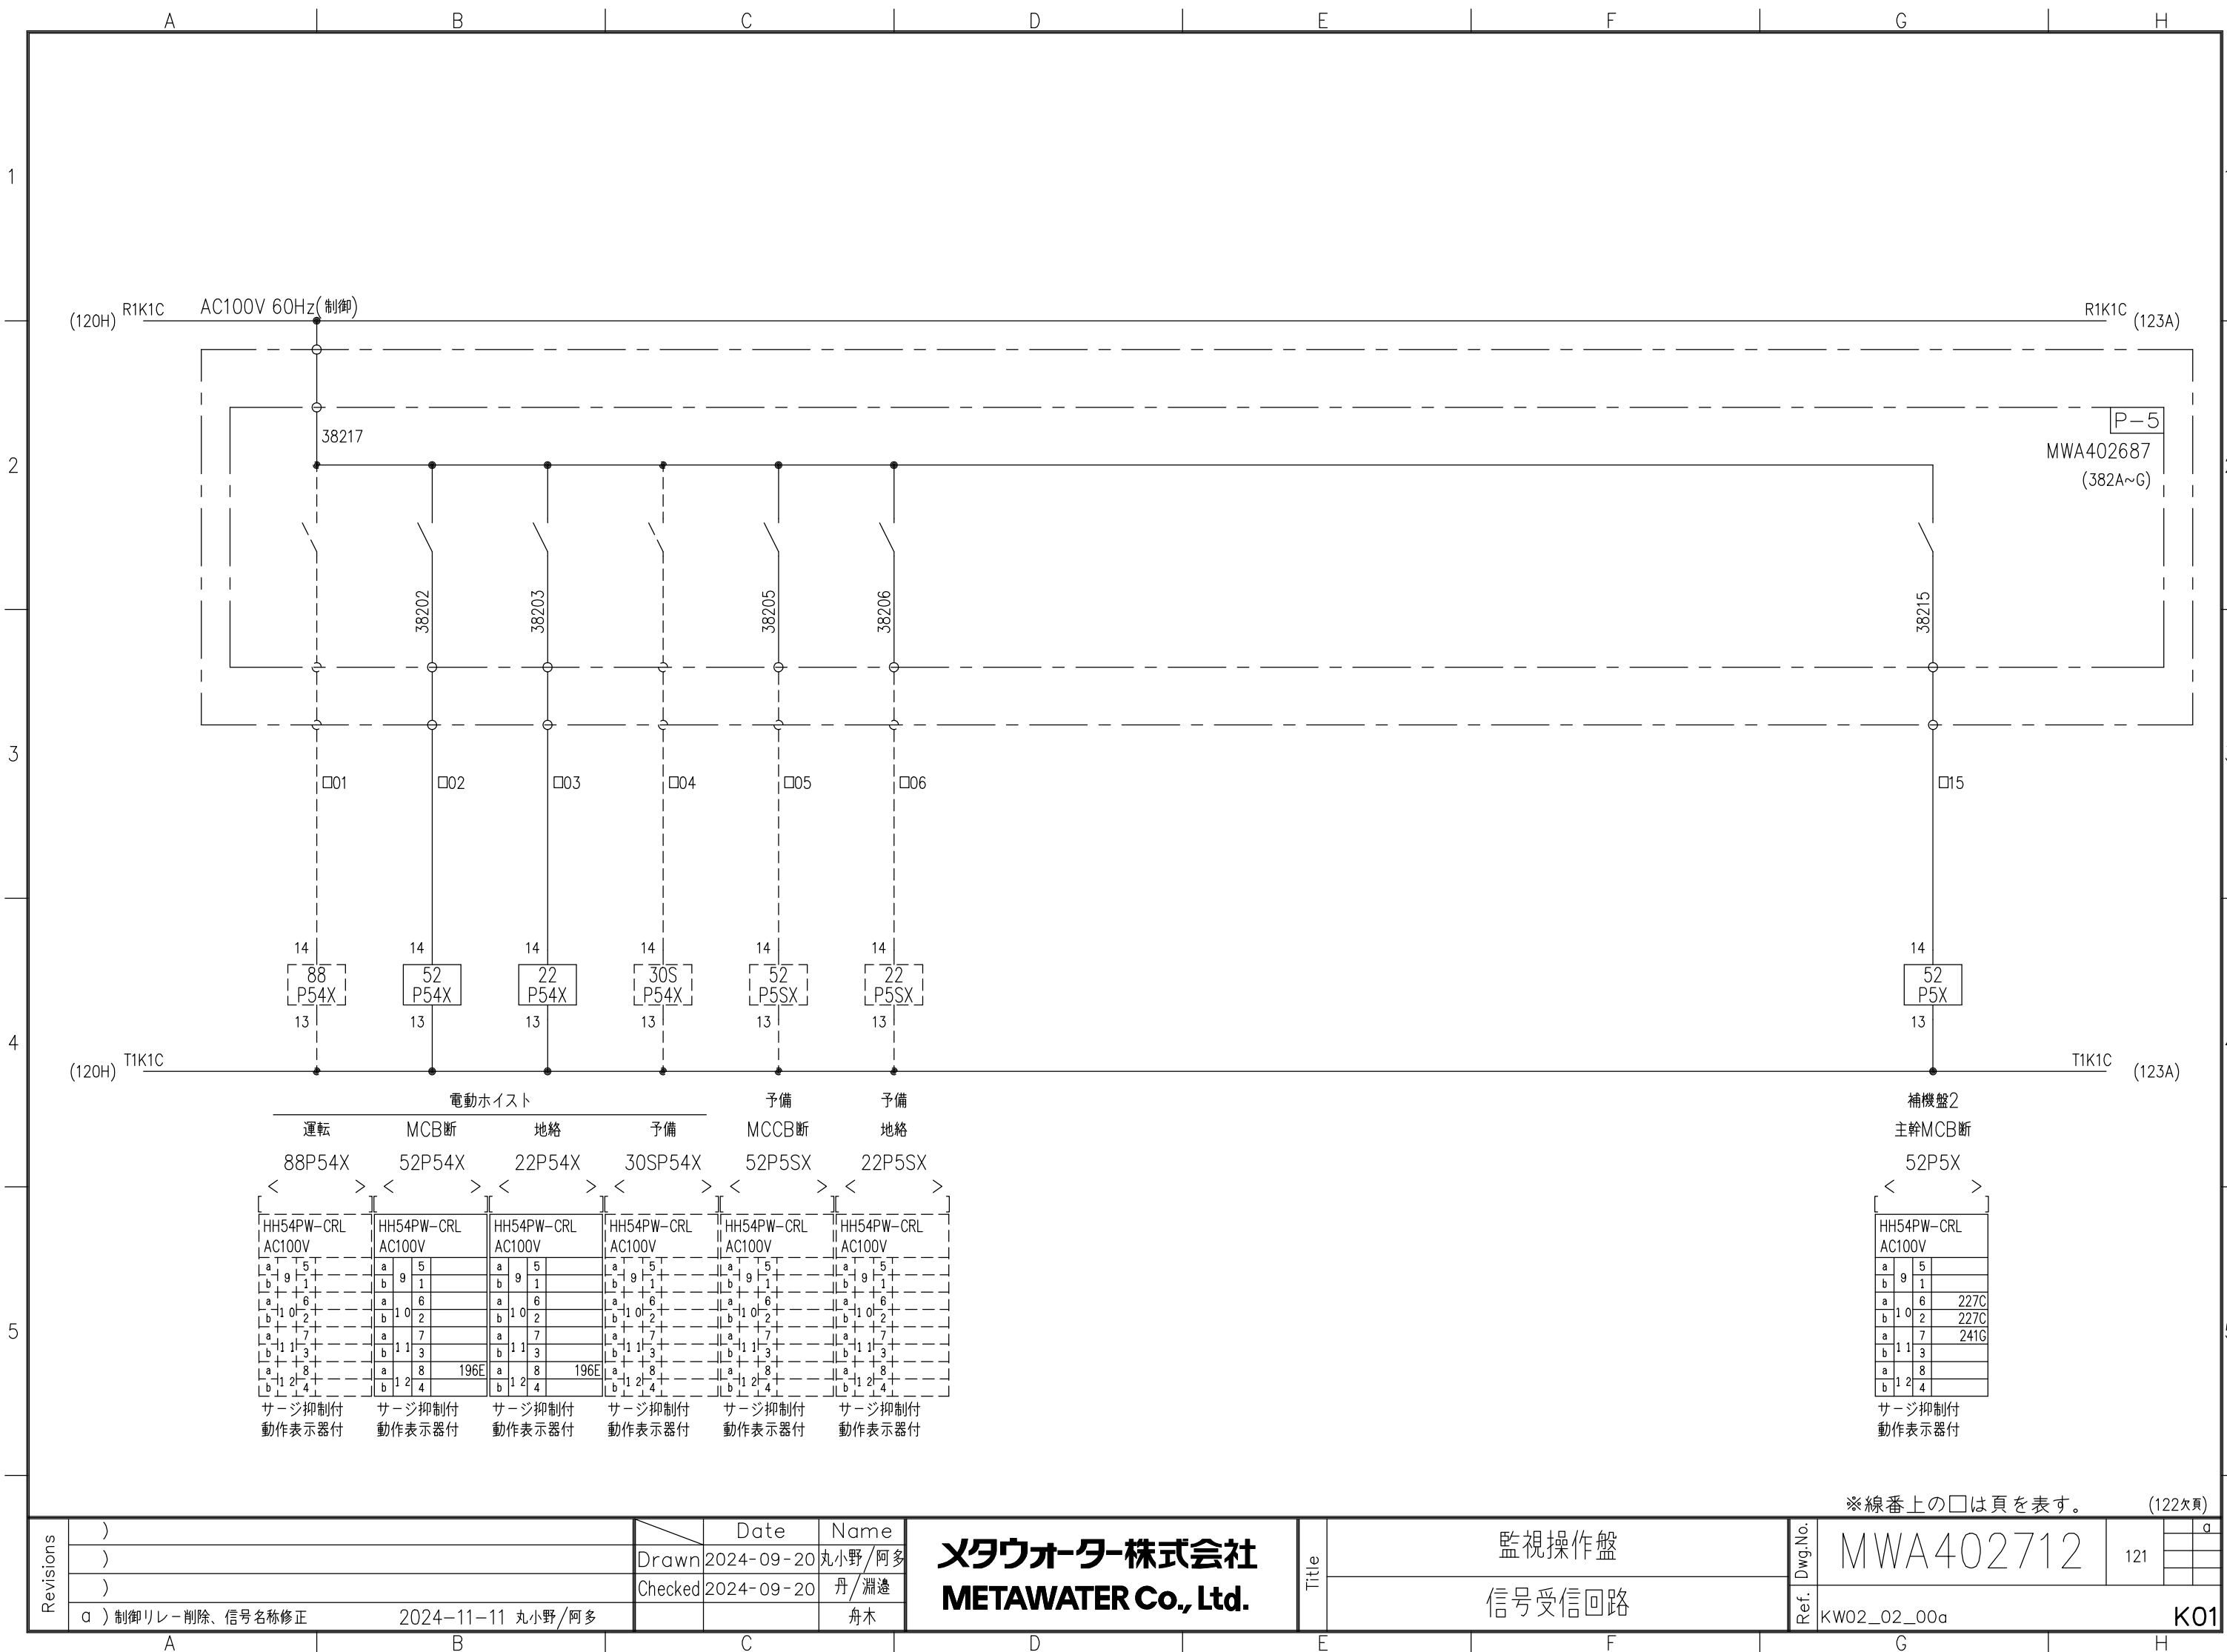


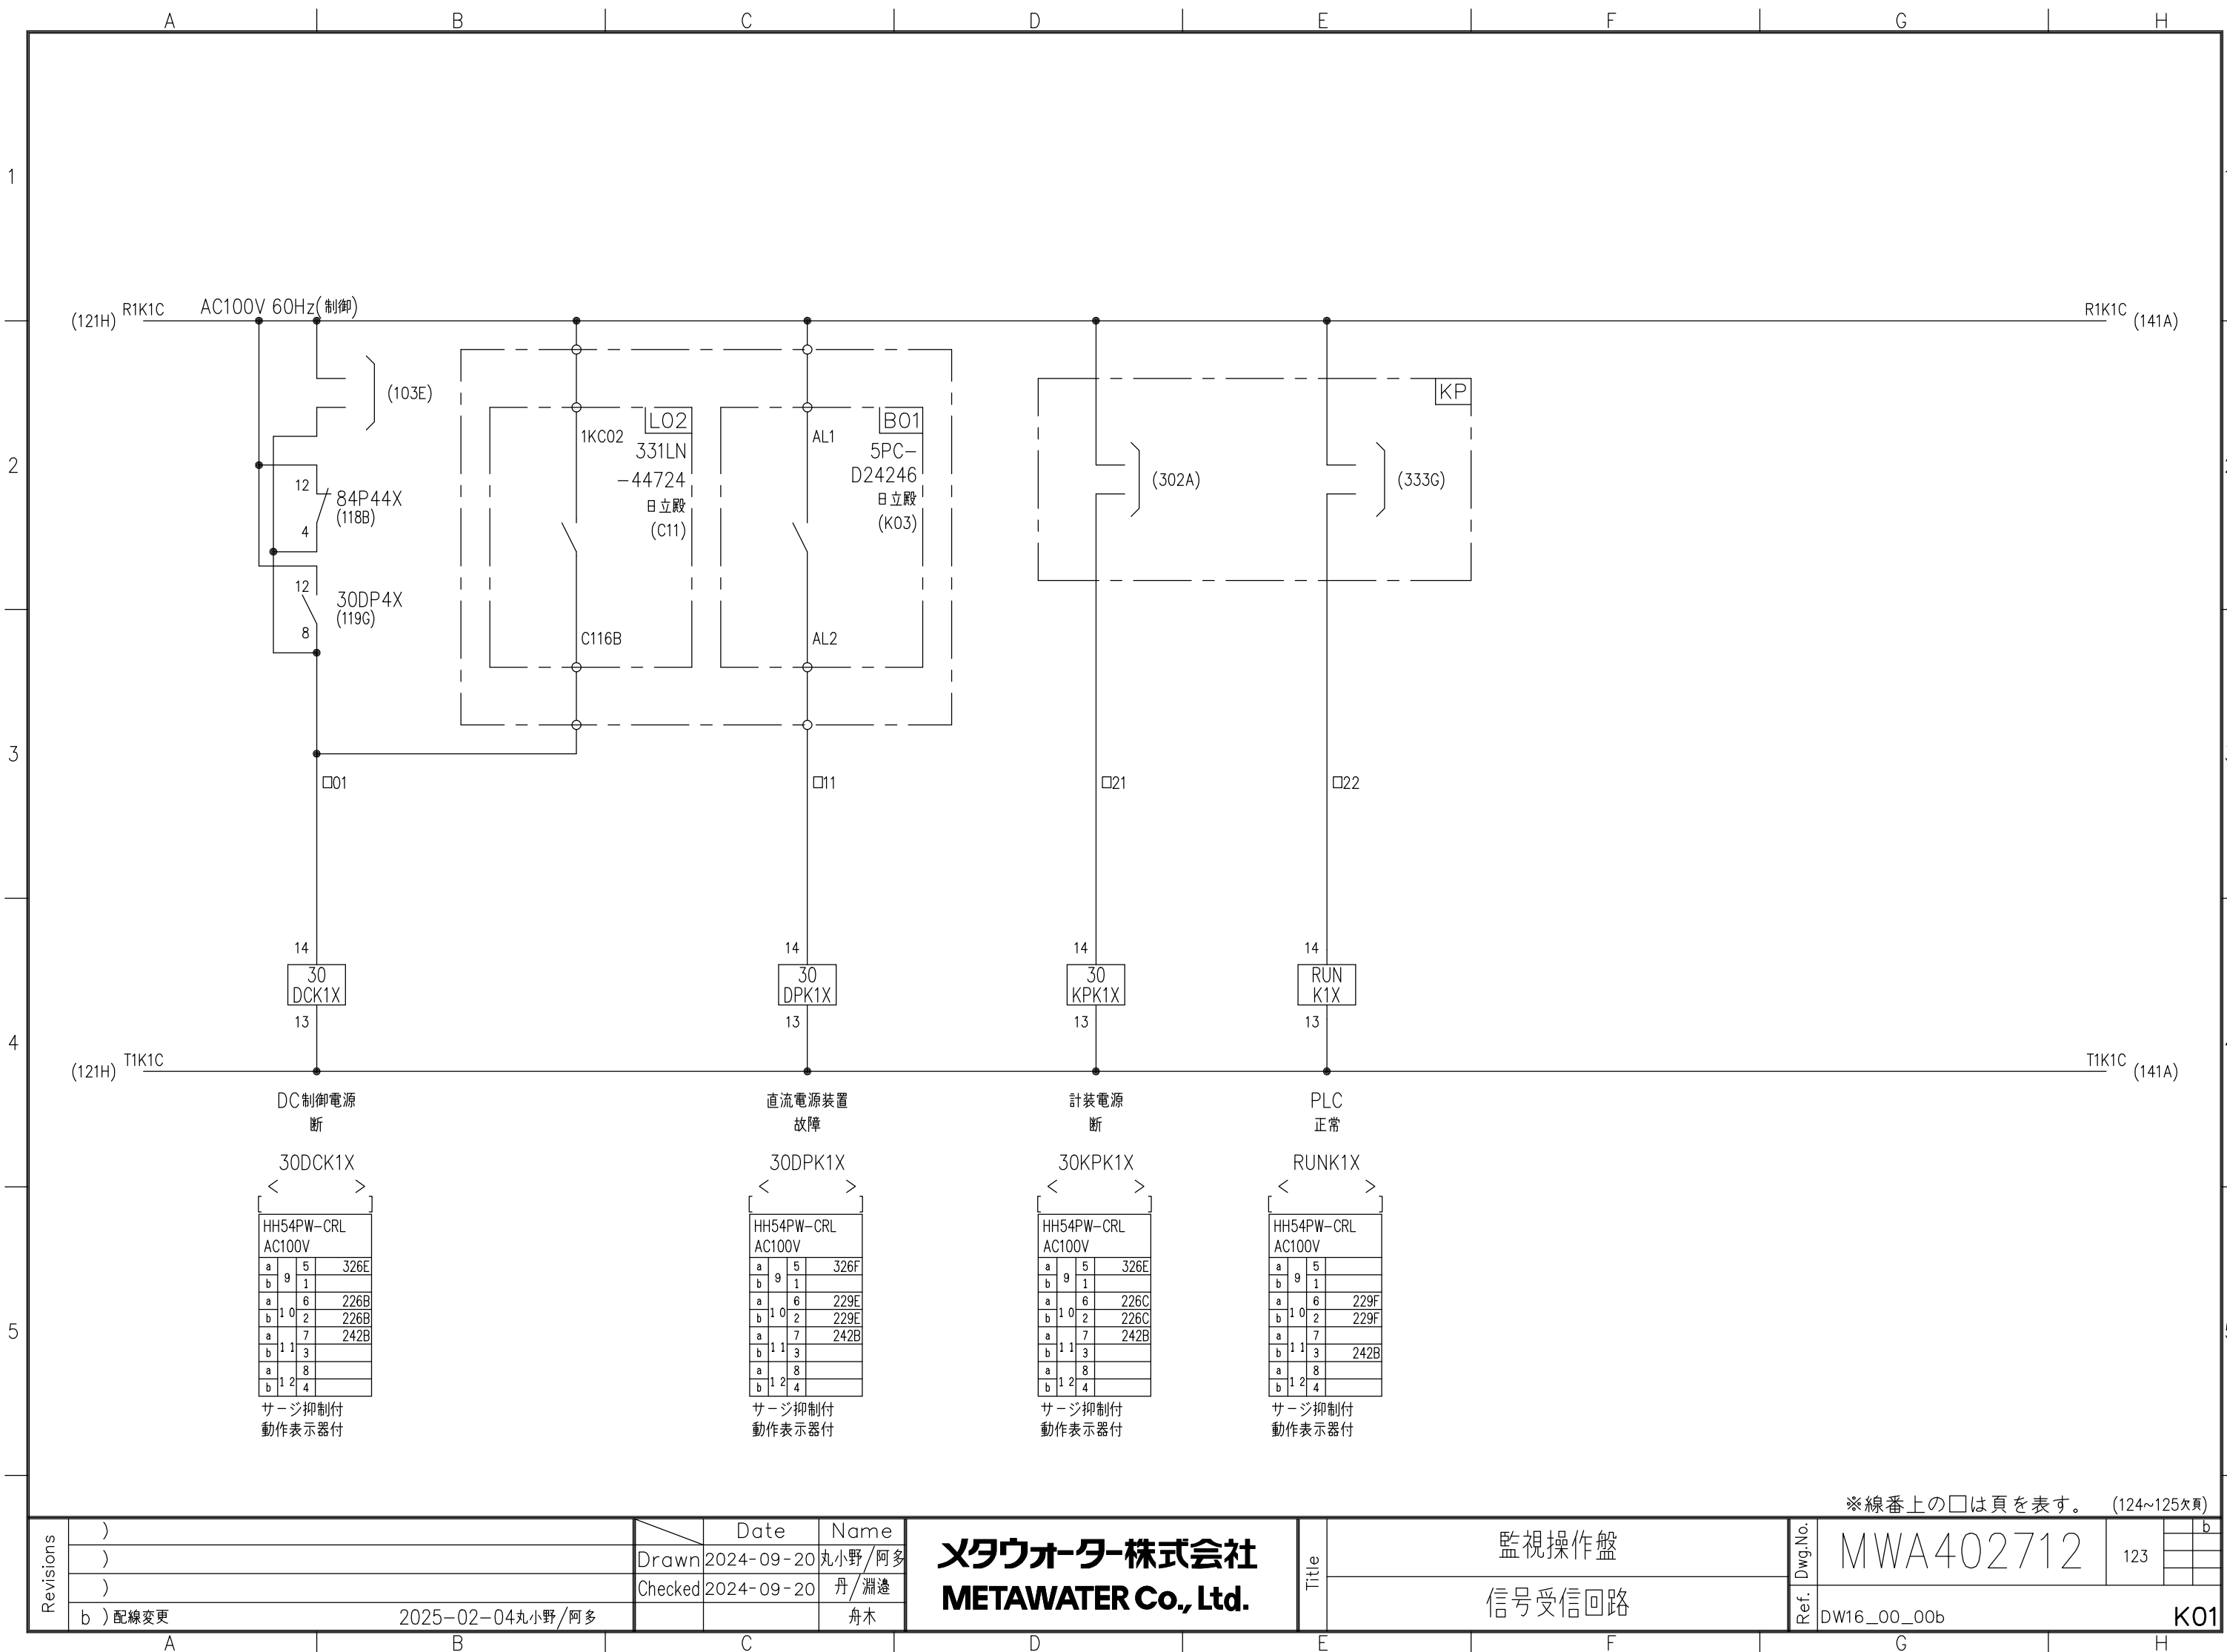

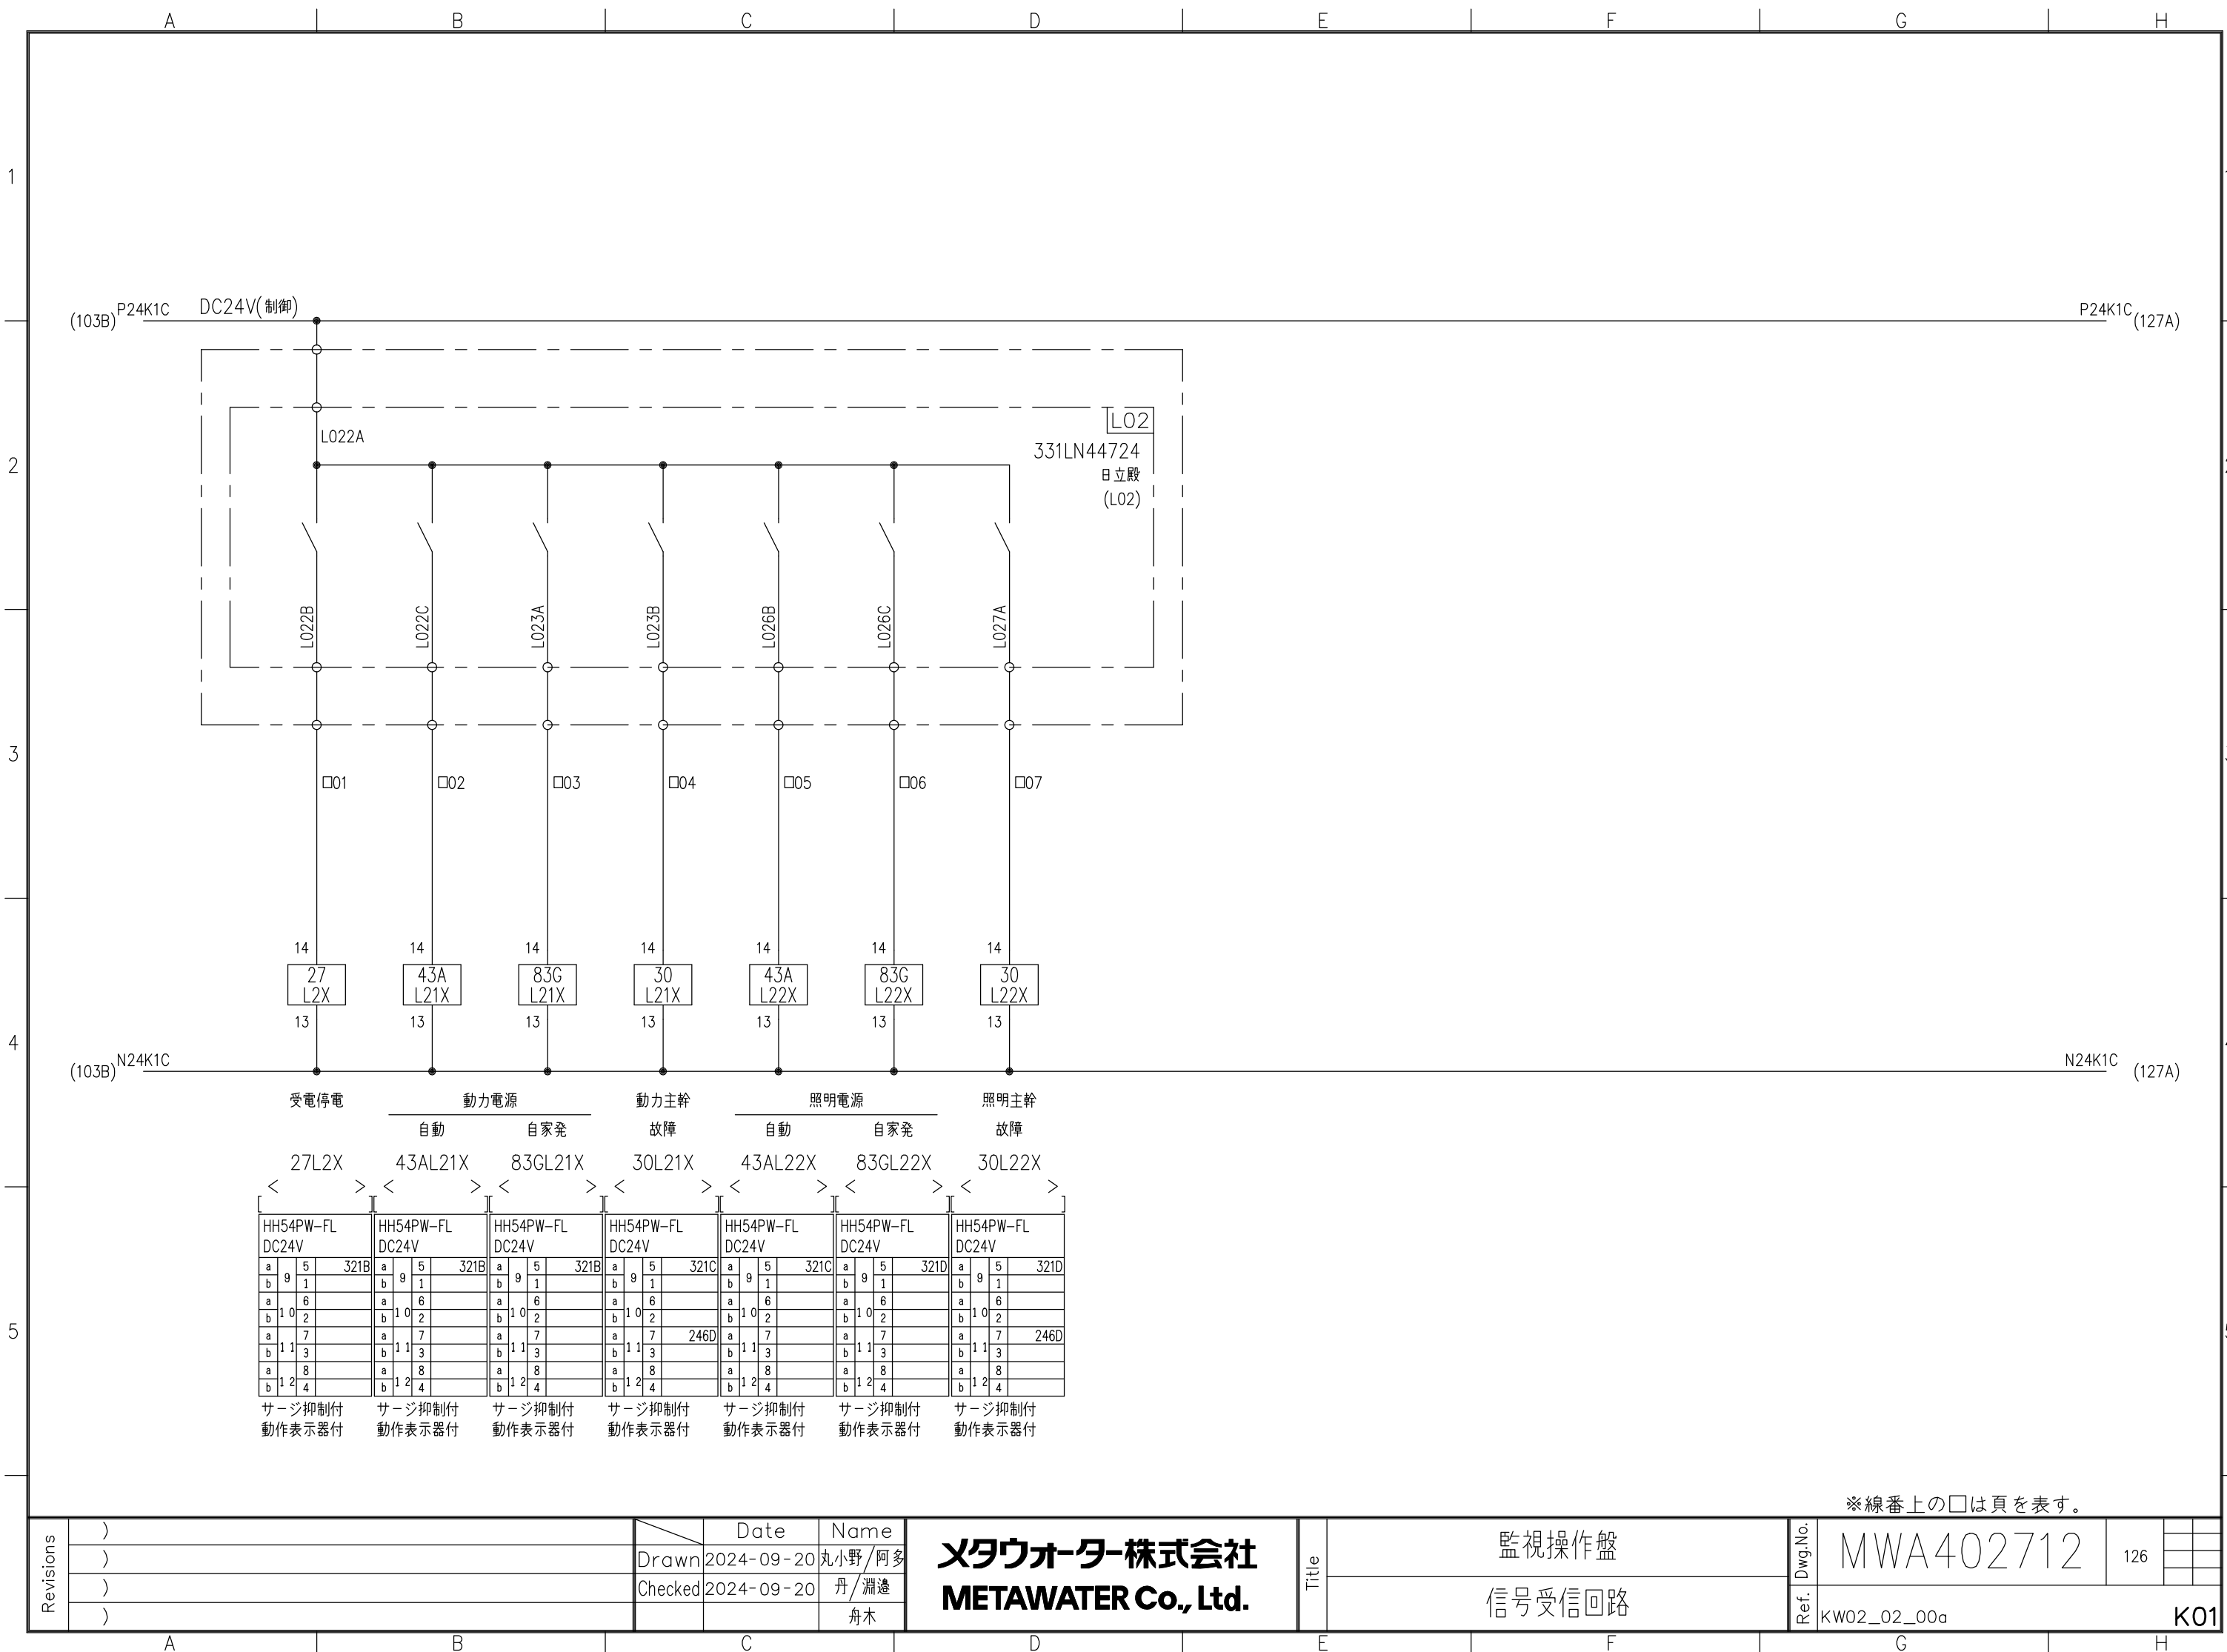

※線番上の□は頁を表す。

Revisions	)		Date	Name	メタウォーター株式会社 METAWATER Co., Ltd.	Title	監視操作盤	Dwg.No.	MWA402712	126			
	)	Drawn	2024-09-20	丸小野/阿多			信号受信回路	Ref.	KW02_02_00a K01				
	)	Checked	2024-09-20	丹/淵邊									
	)			舟木									

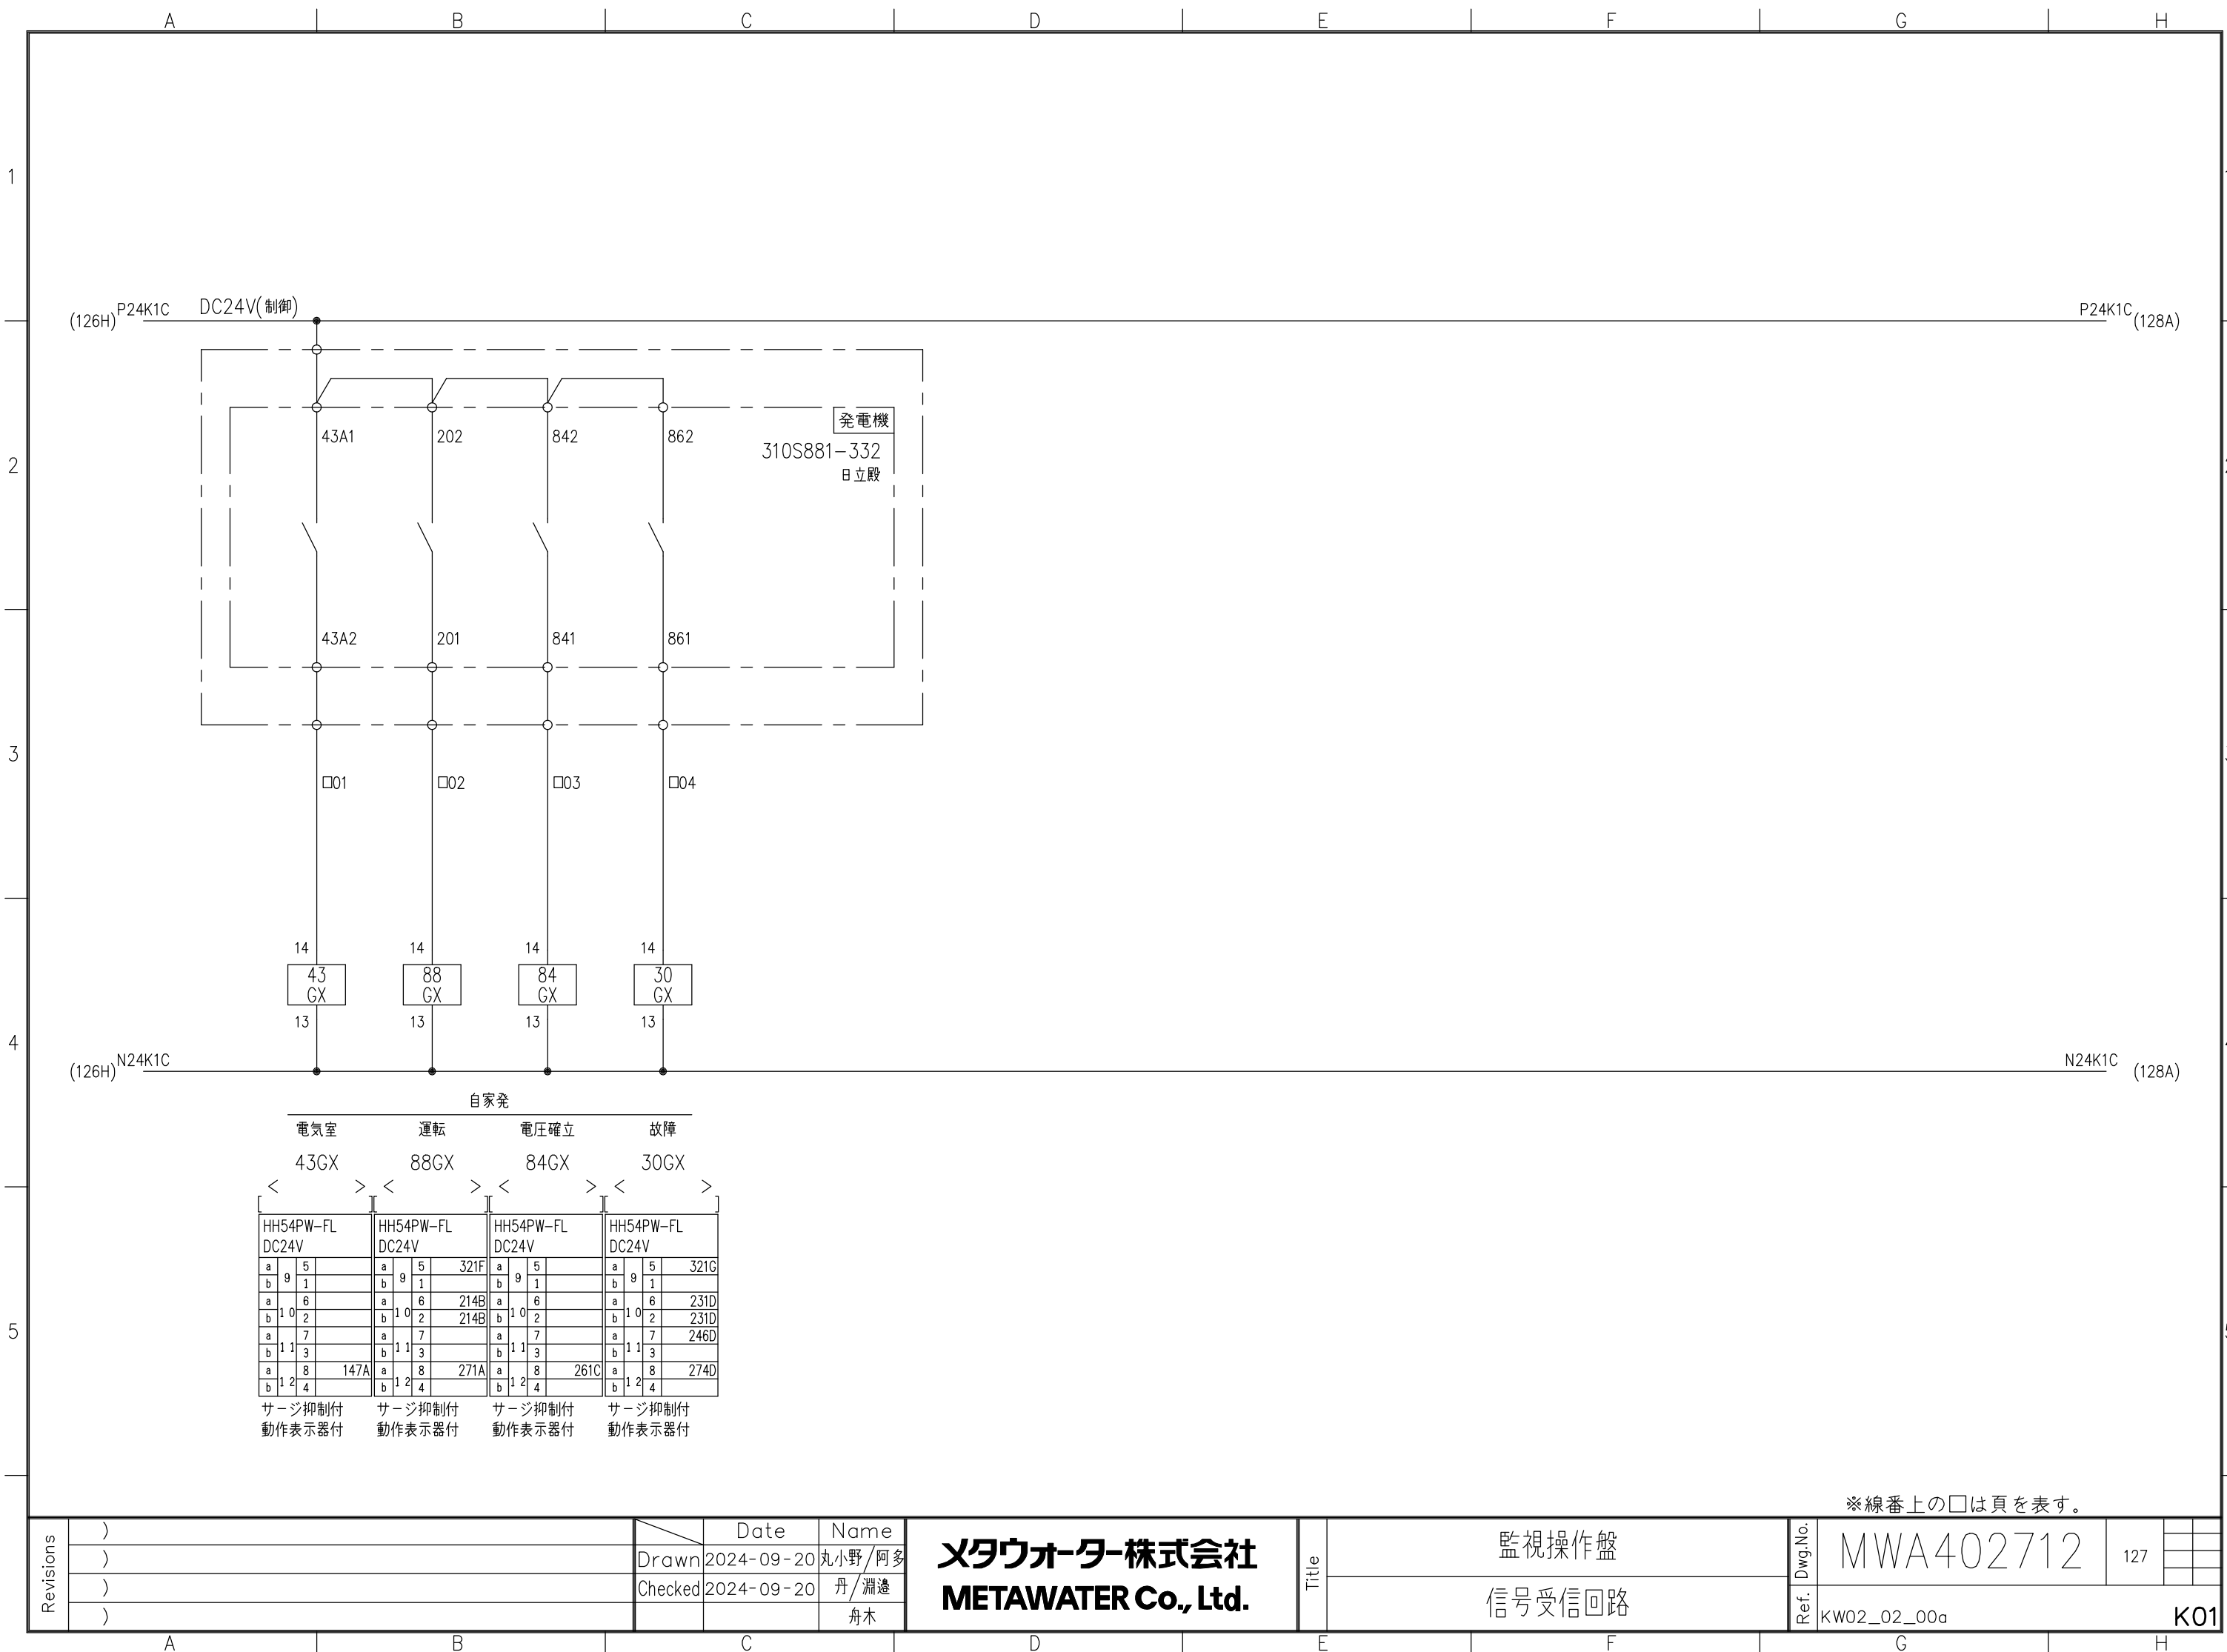

※線番上の□は頁を表す。

Revisions

)

)

)

)

Date

2024-09-20

2024-09-20

Name

丸小野/阿多

丹/淵邊

舟木

メタウォーター株式会社

METAWATER Co., Ltd.

Title

監視操作盤

信号受信回路

Dwg.No.


MWA402712

127

Ref.

KW02_02_00a

K01

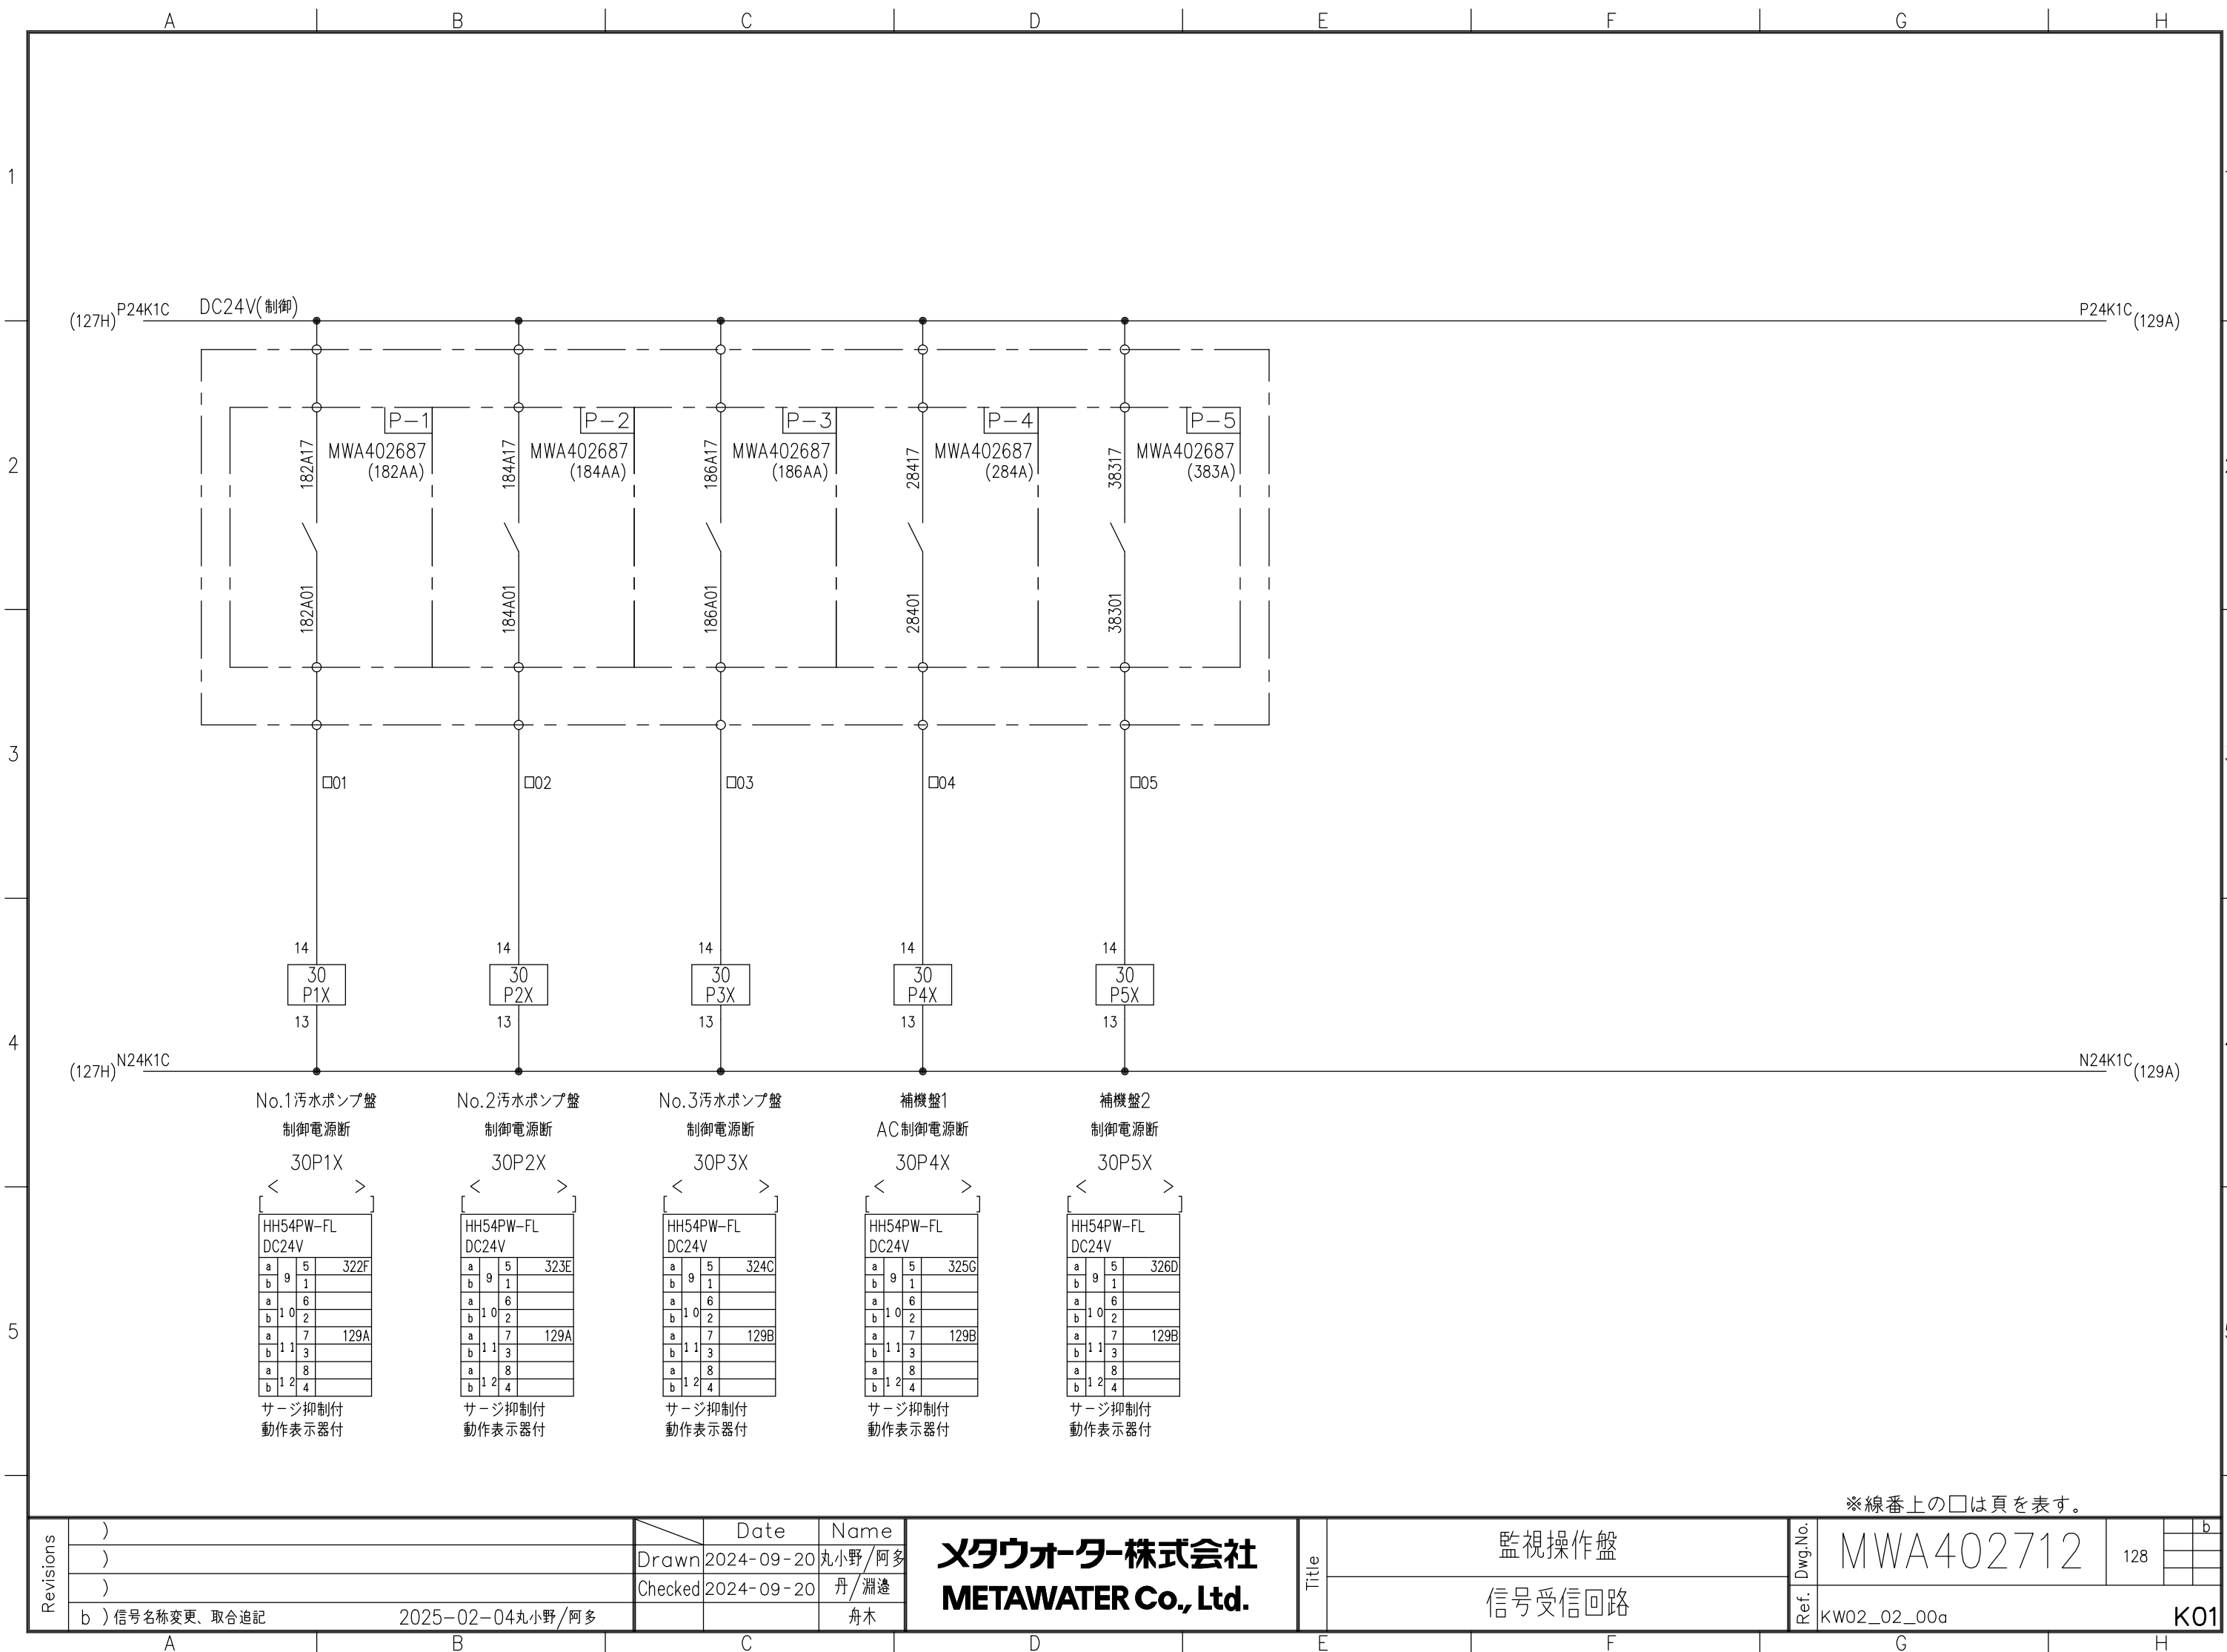

※線番上の□は頁を表す。

Revisions

)

)

)

b) 信号名称変更、取合追記

Drawn

2024-09-20

丸小野/阿多

Checked

2024-09-20

丹/淵邊

Date

2025-02-04

丸小野/阿多

Name

舟木

メタウォーター株式会社

METAWATER Co., Ltd.

Title

監視操作盤

信号受信回路

Dwg.No.


MWA402712


128

Ref.

KW02_02_00a

K01

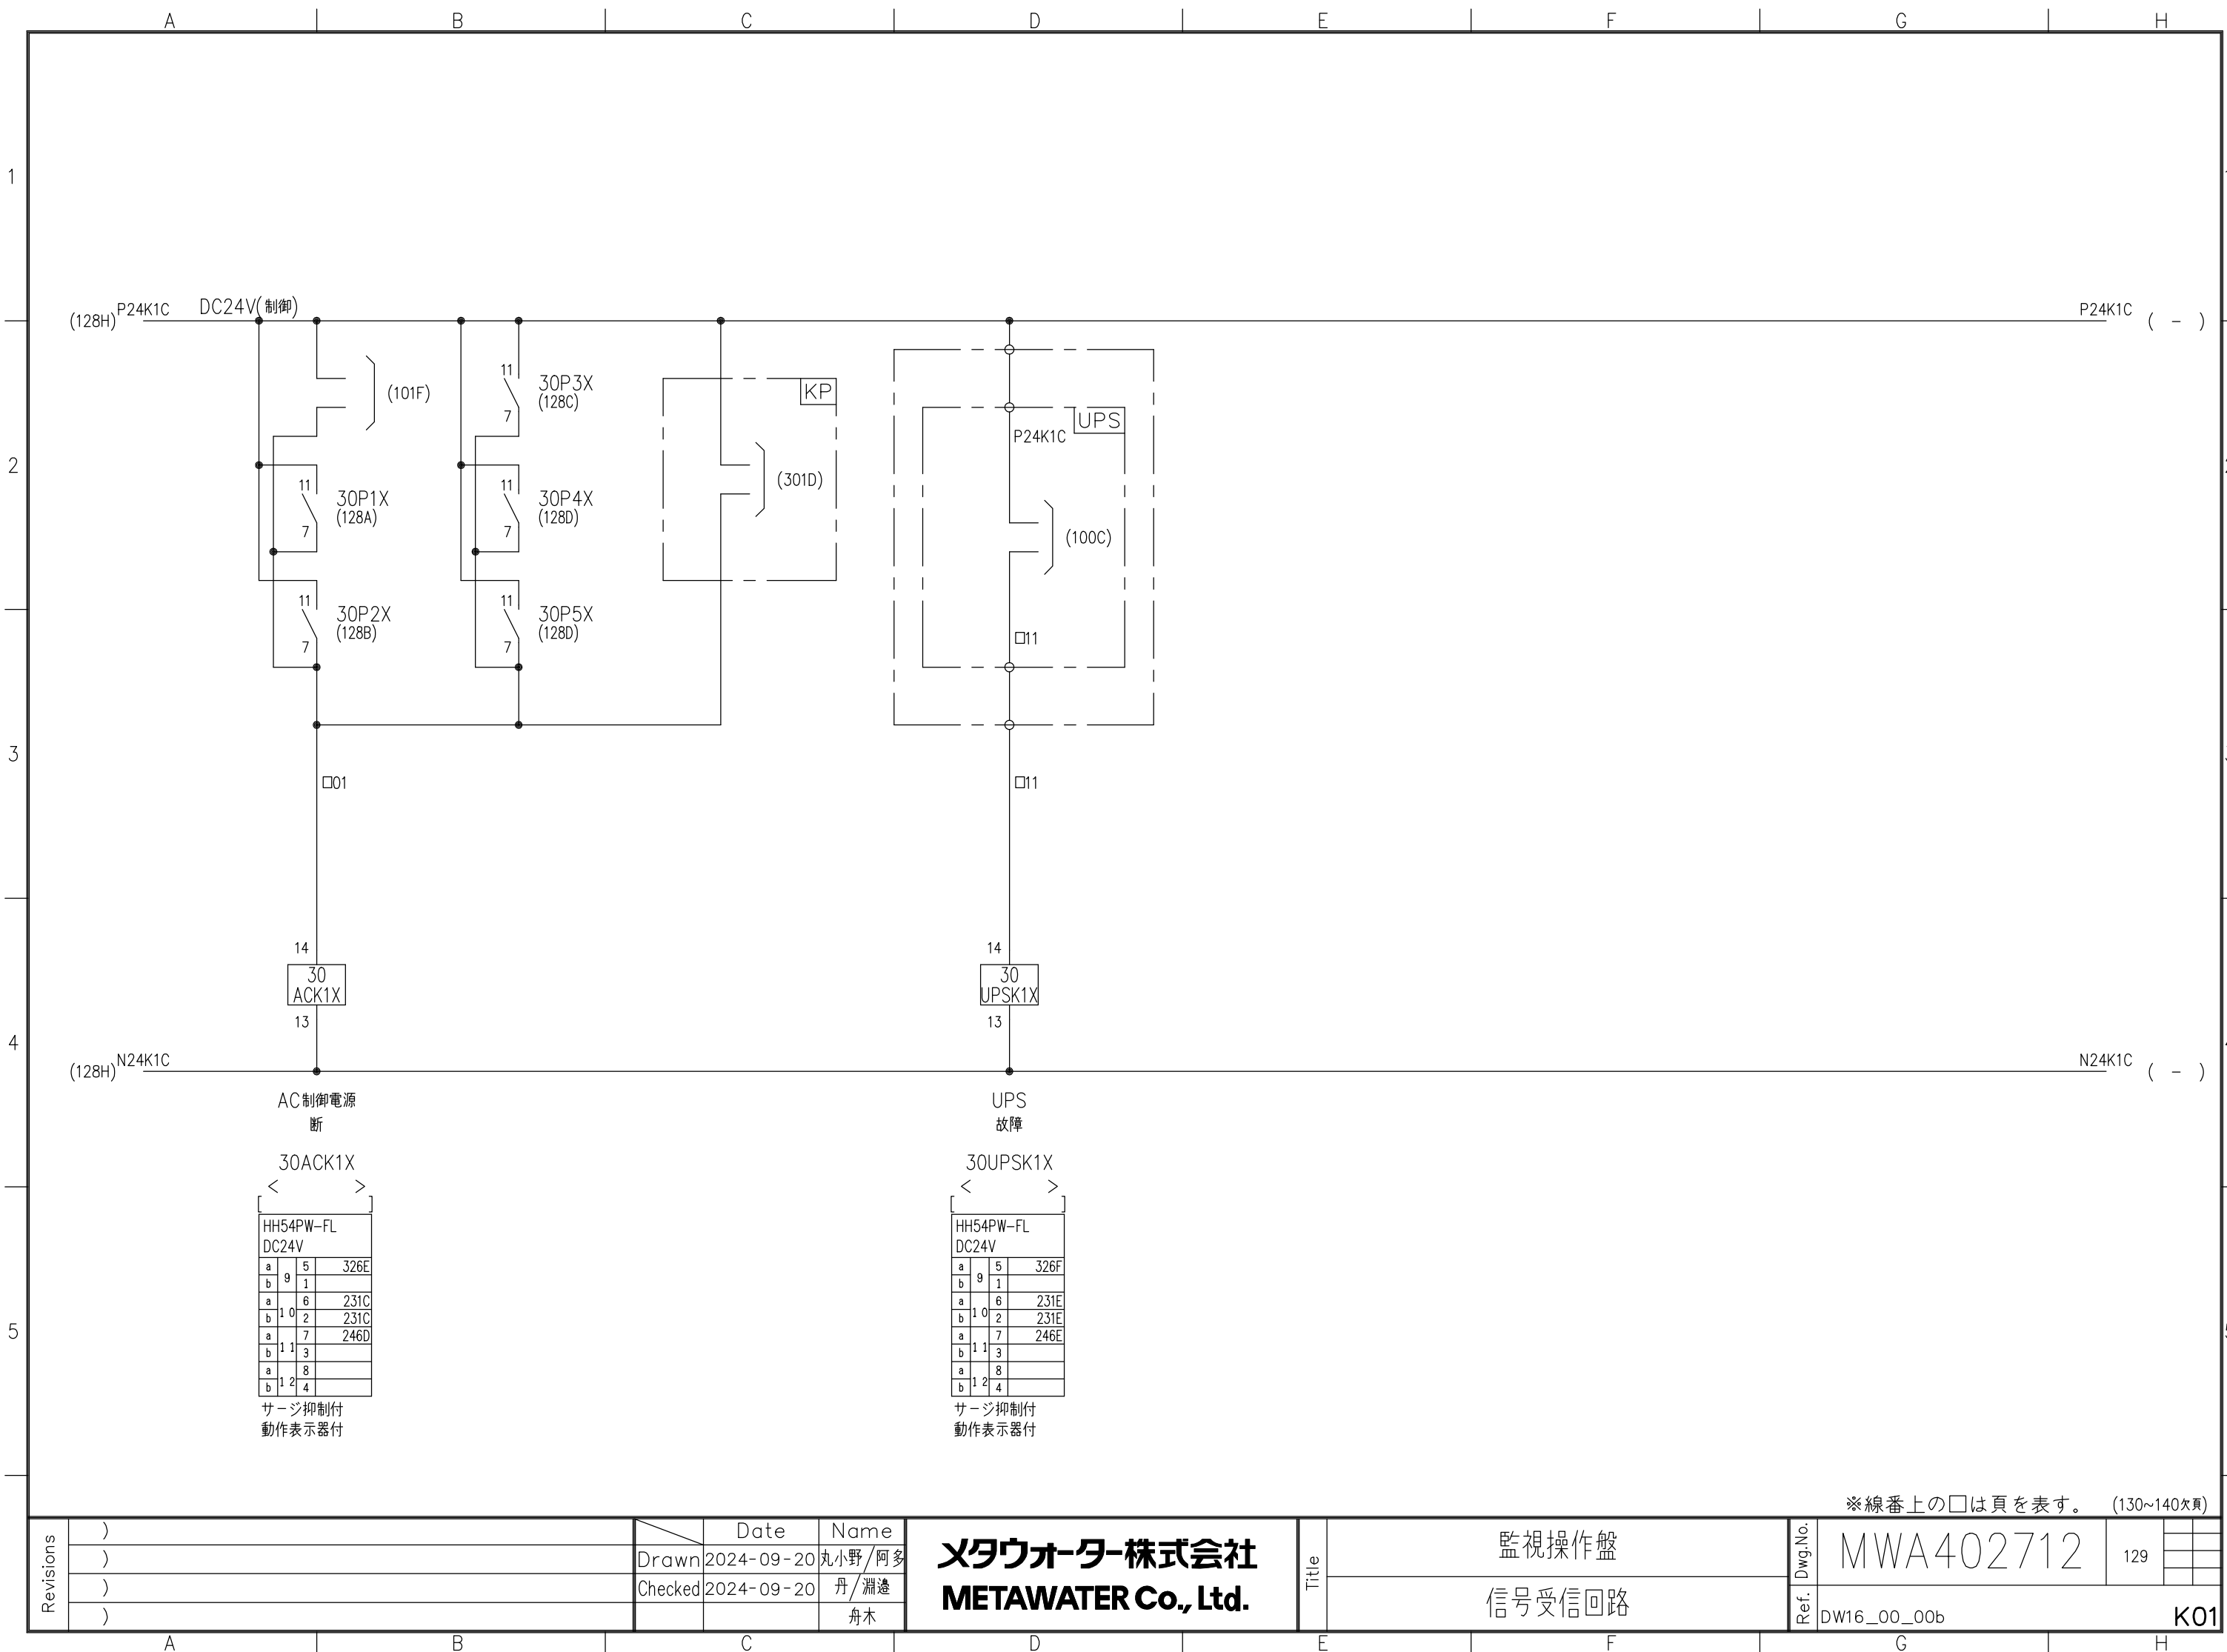

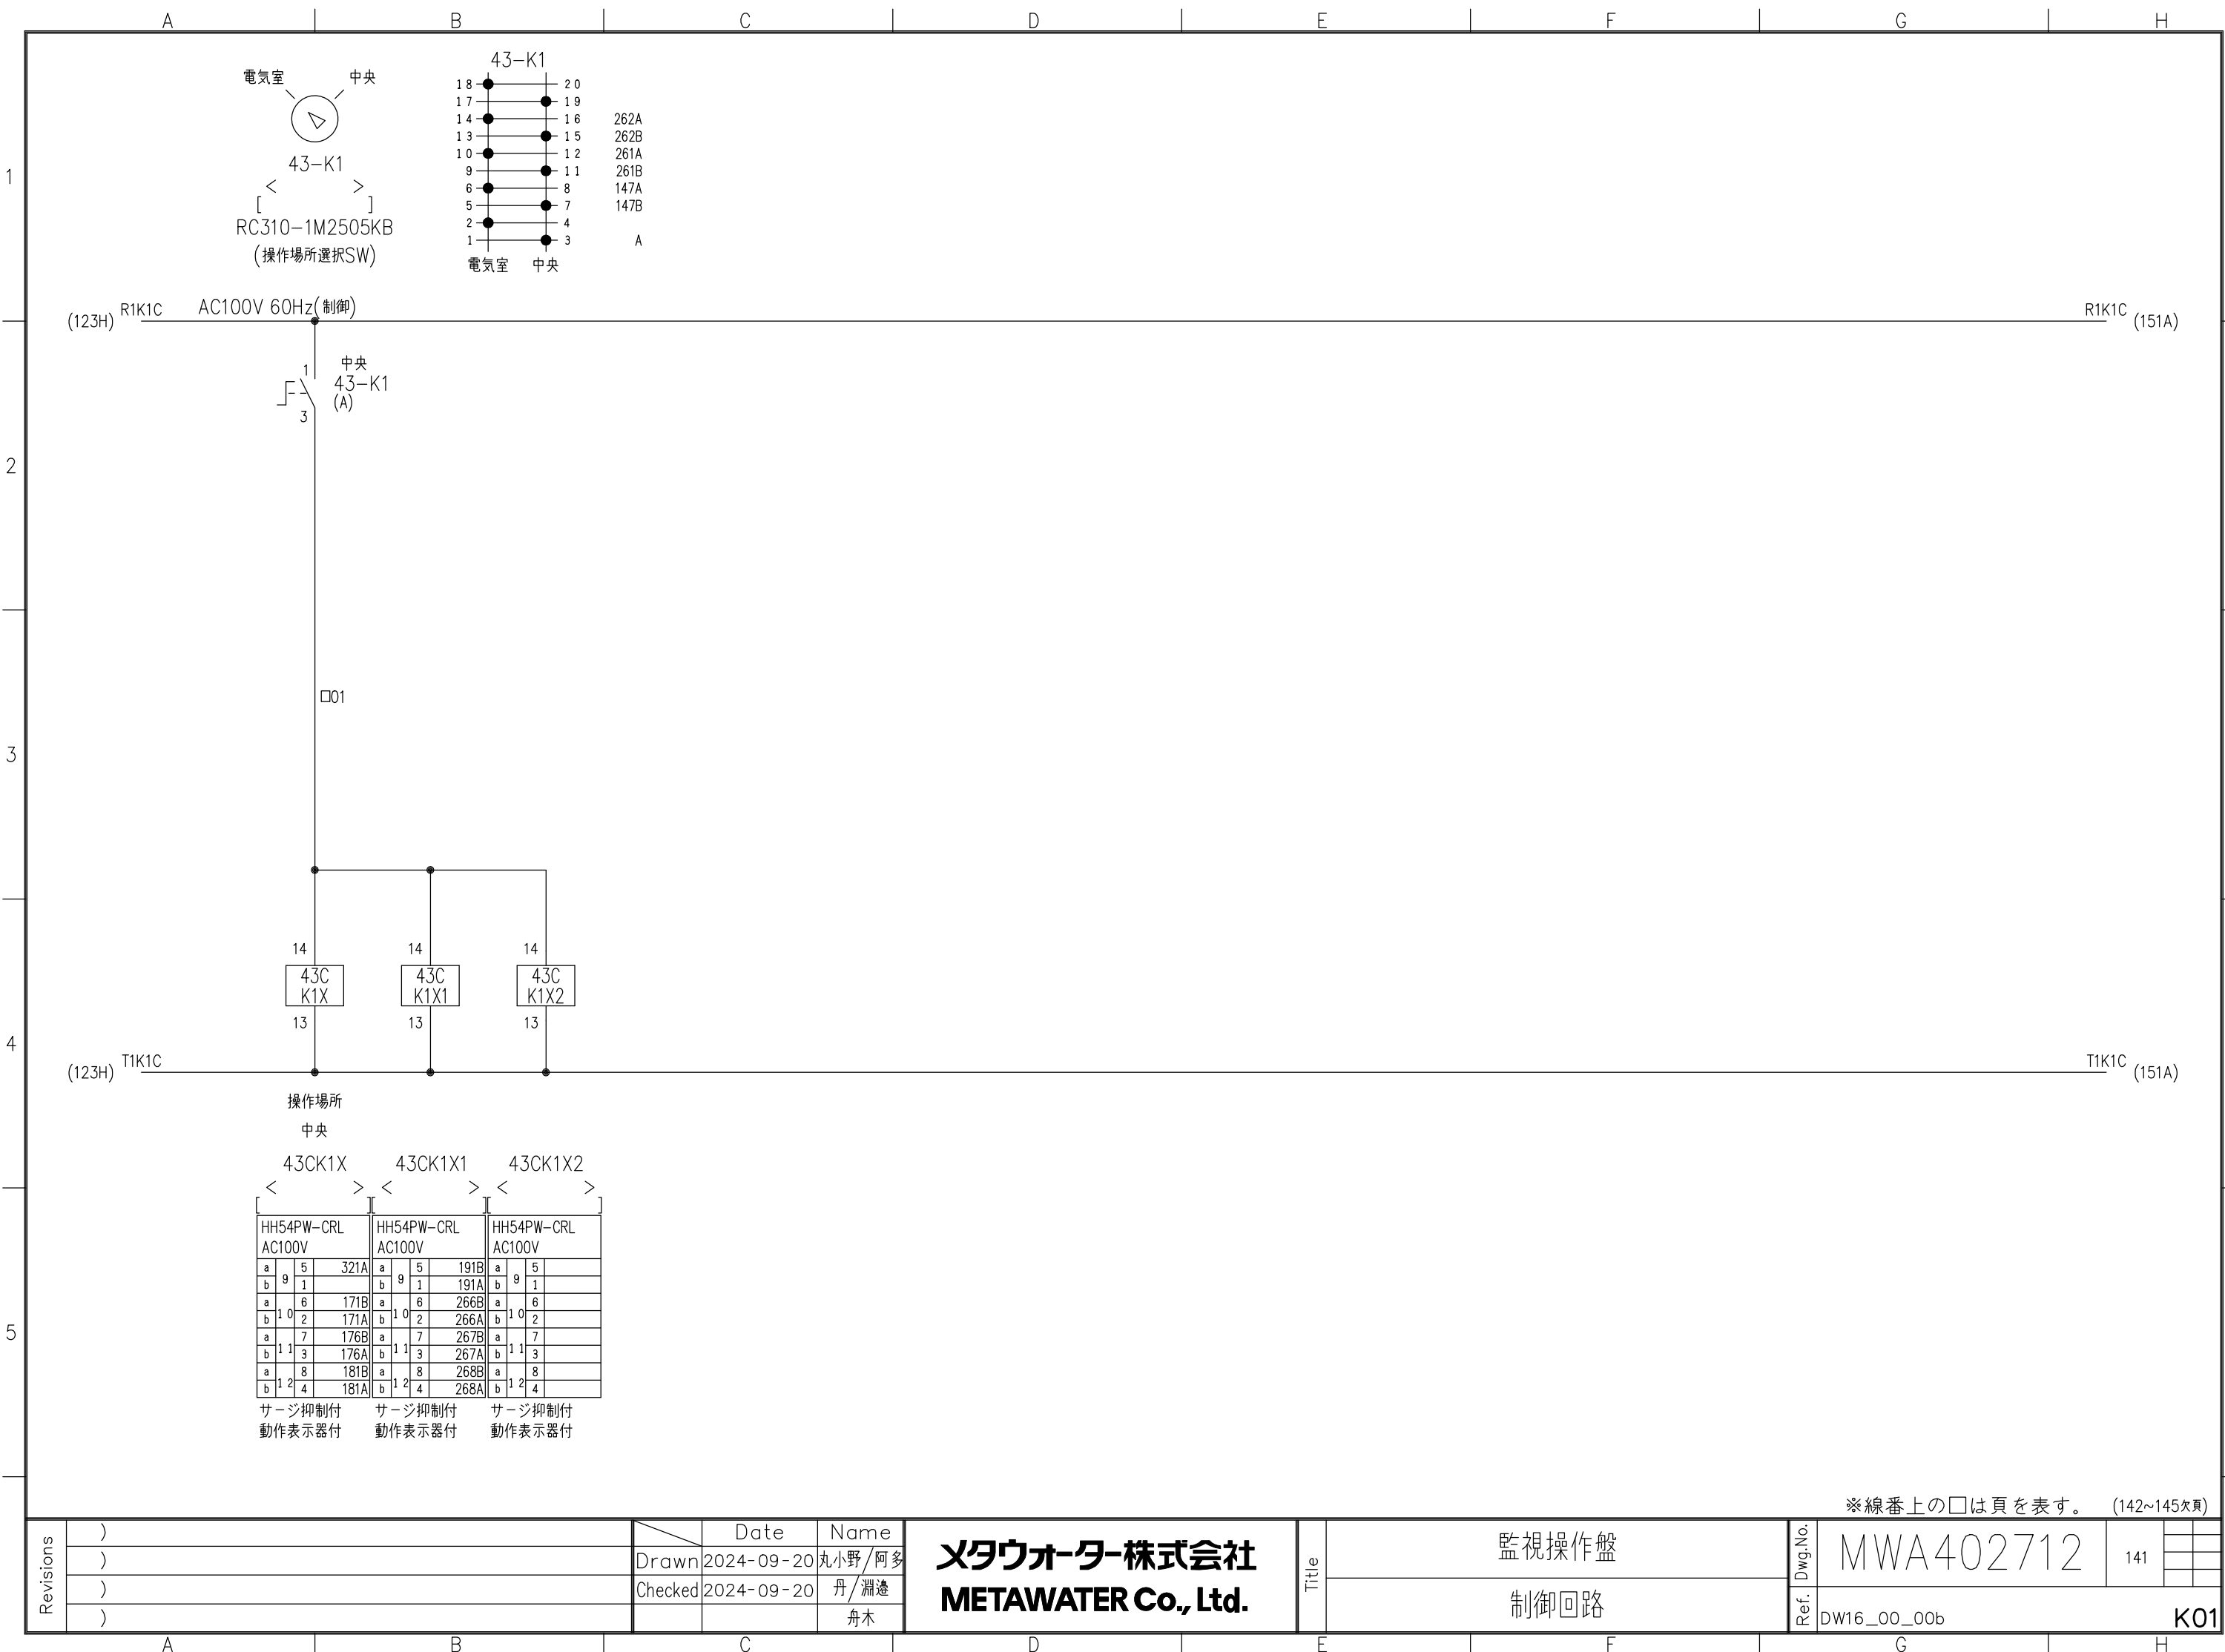

※線番上の□は頁を表す。(142~145欠頁)

Revisions

)

)

)

)

Date

2024-09-20

2024-09-20

Name

丸小野/阿多

丹/淵邊

舟木

メタウォーター株式会社

METAWATER Co., Ltd.

Title

監視操作盤

制御回路

Dwg.No.

MWA402712

141


Ref.

DW16_00_00b

K01


※線番上の□は頁を表す。

Revisions	)		Date	Name	メタウォーター株式会社 METAWATER Co., Ltd.	Title	自家発設備	Dwg.No.	MWA402712	146		
	)	Drawn	2024-09-20	丸小野/阿多								
	)	Checked	2024-09-20	丹/淵達								
	)			舟木								
							制御回路	Ref.	DW16_00_00b KO			

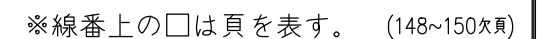

メタウォーター株式会社
METAWATER Co., Ltd.


汚水ポンプ自動制御条件

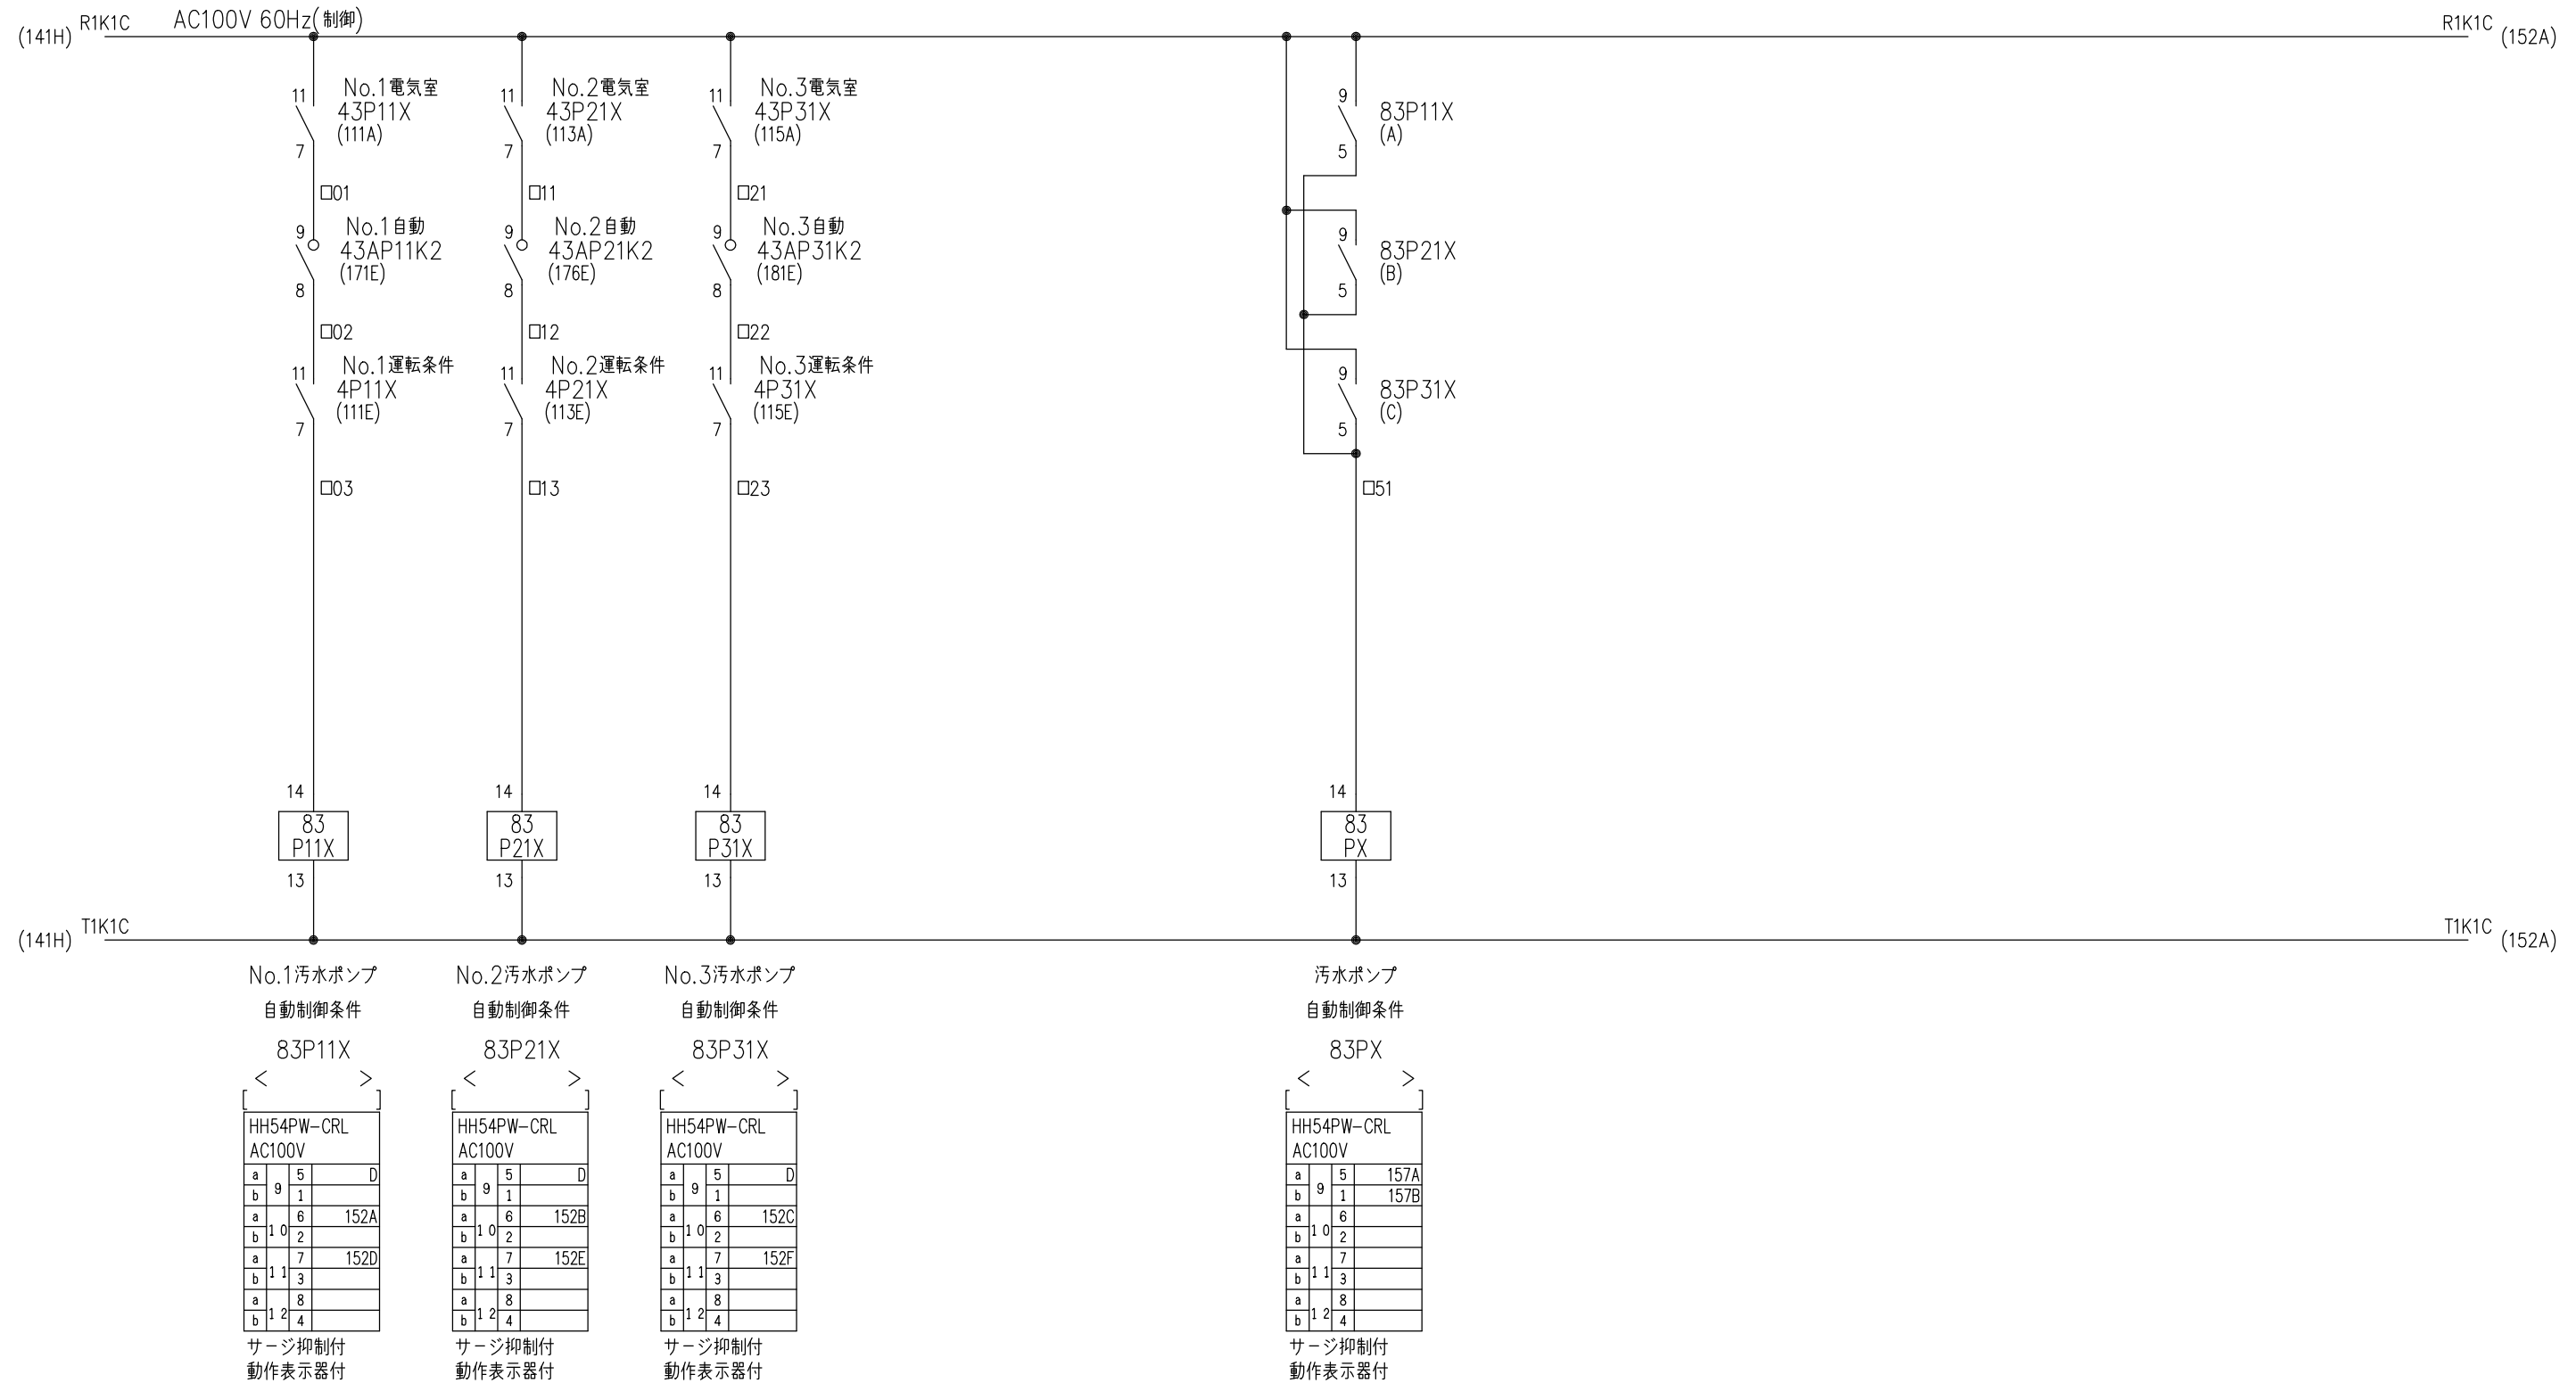

※線番上の□は頁を表す。


Revisions	)		Date	Name	メタウォーター株式会社 METAWATER Co., Ltd.	Title	汚水ポンプ	Dwg.No.	MWA402712	151			
	)	Drawn	2024-09-20	丸小野 / 阿多									
	)	Checked	2024-09-20	丹 / 淵邊			台数制御回路	Ref.	VDW16_00_02a	K01			
	)			舟木									

自動制御対象号機

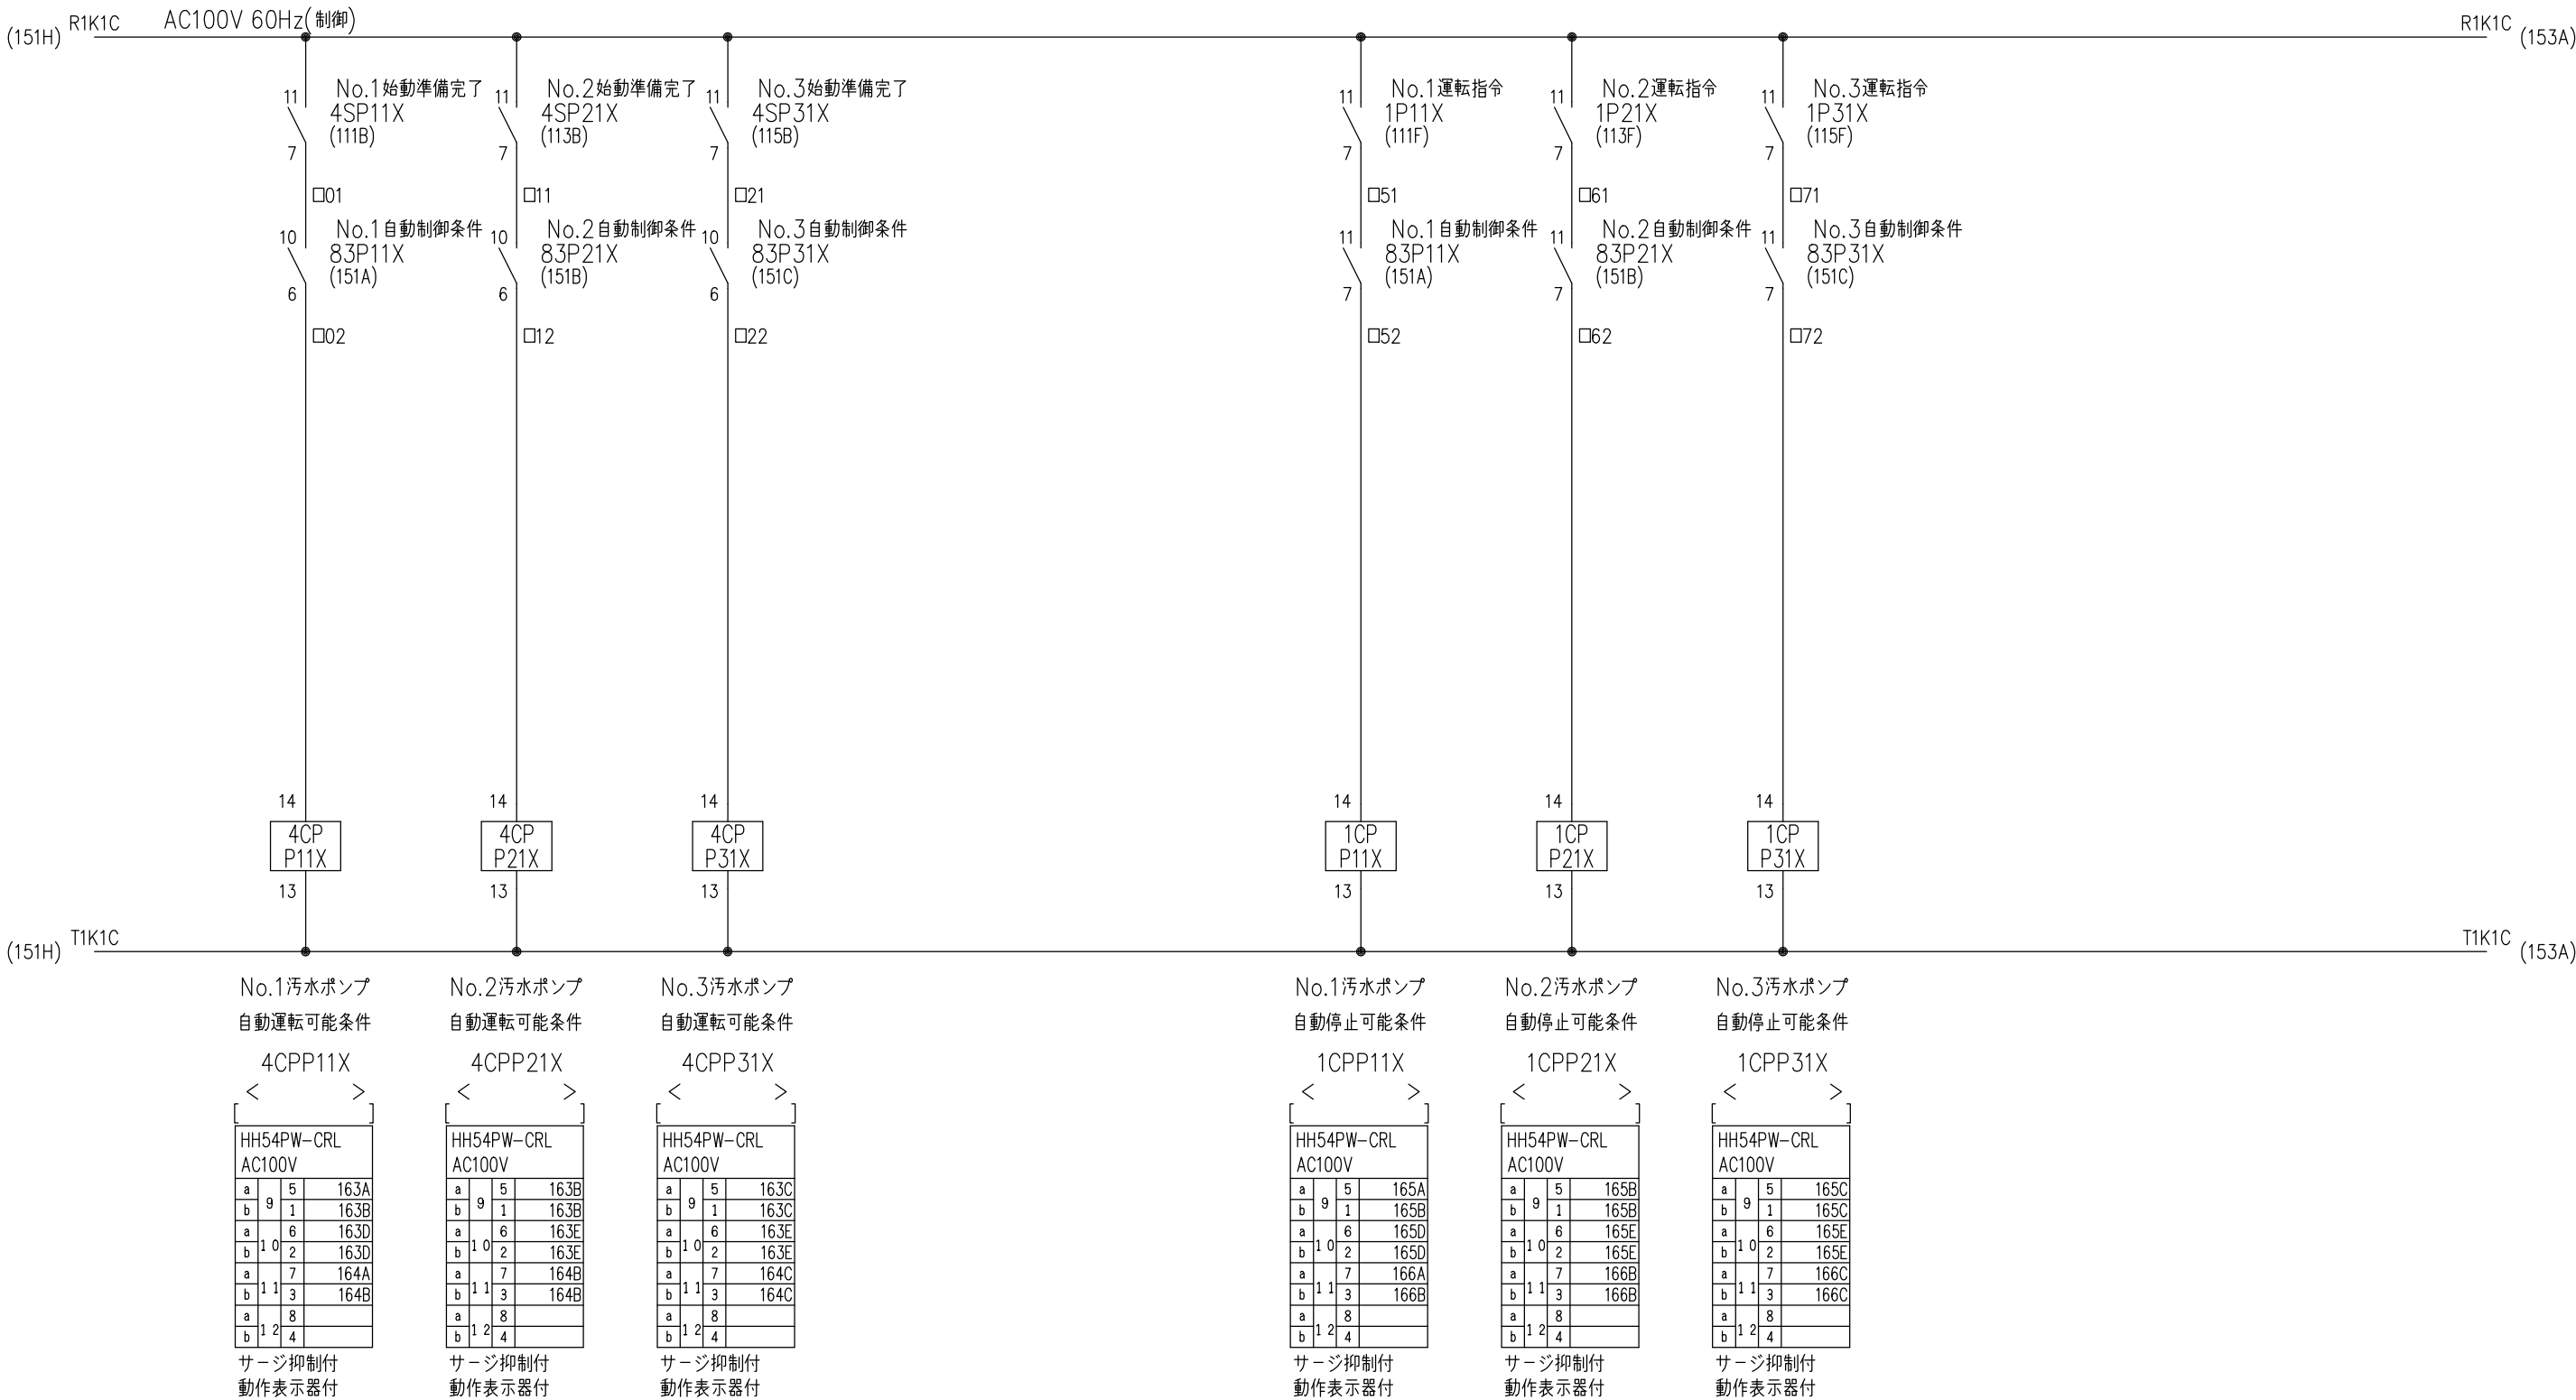


※線番上の□は頁を表す。

Revisions	)		Date	Name	メタウォーター株式会社 METAWATER Co., Ltd.	Title		Dwg.No.	MWA402712	152		
	)	Drawn	2024-09-20	丸小野 / 阿多								
	)	Checked	2024-09-20	丹 / 淵邊								
	)			舟木								
							Ref.	VDW16_00_02a			K01	

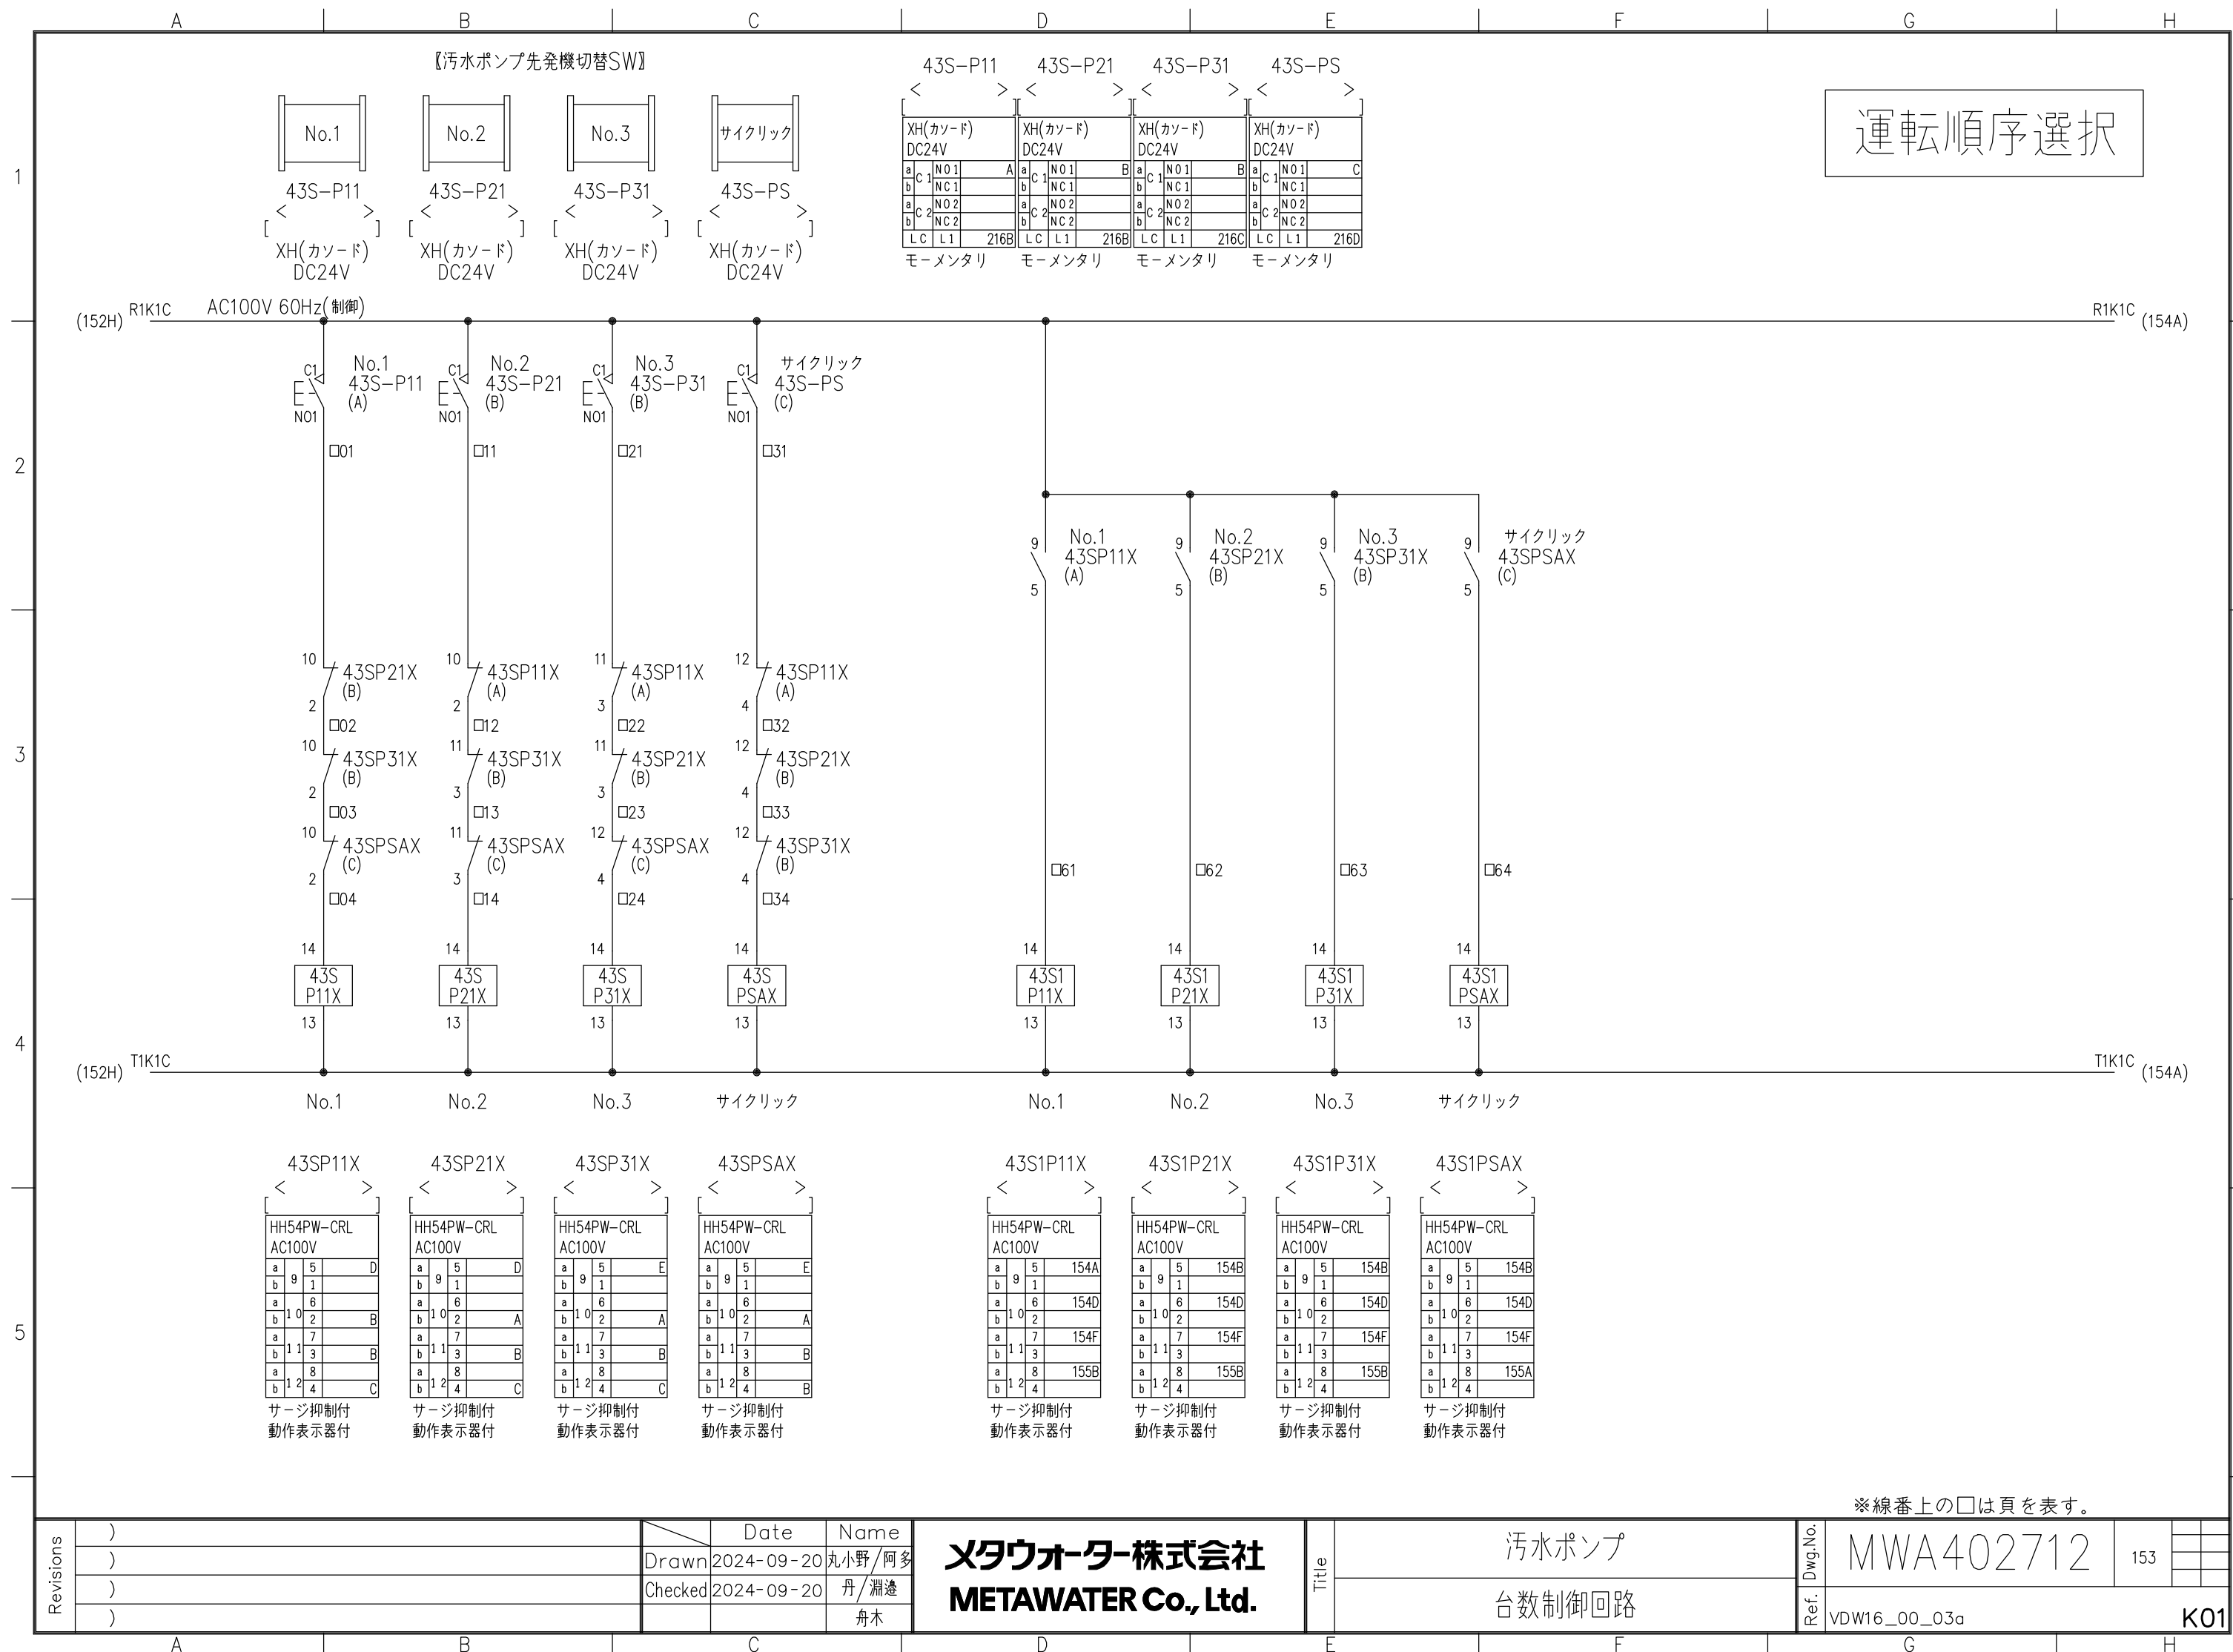


運転順序選択

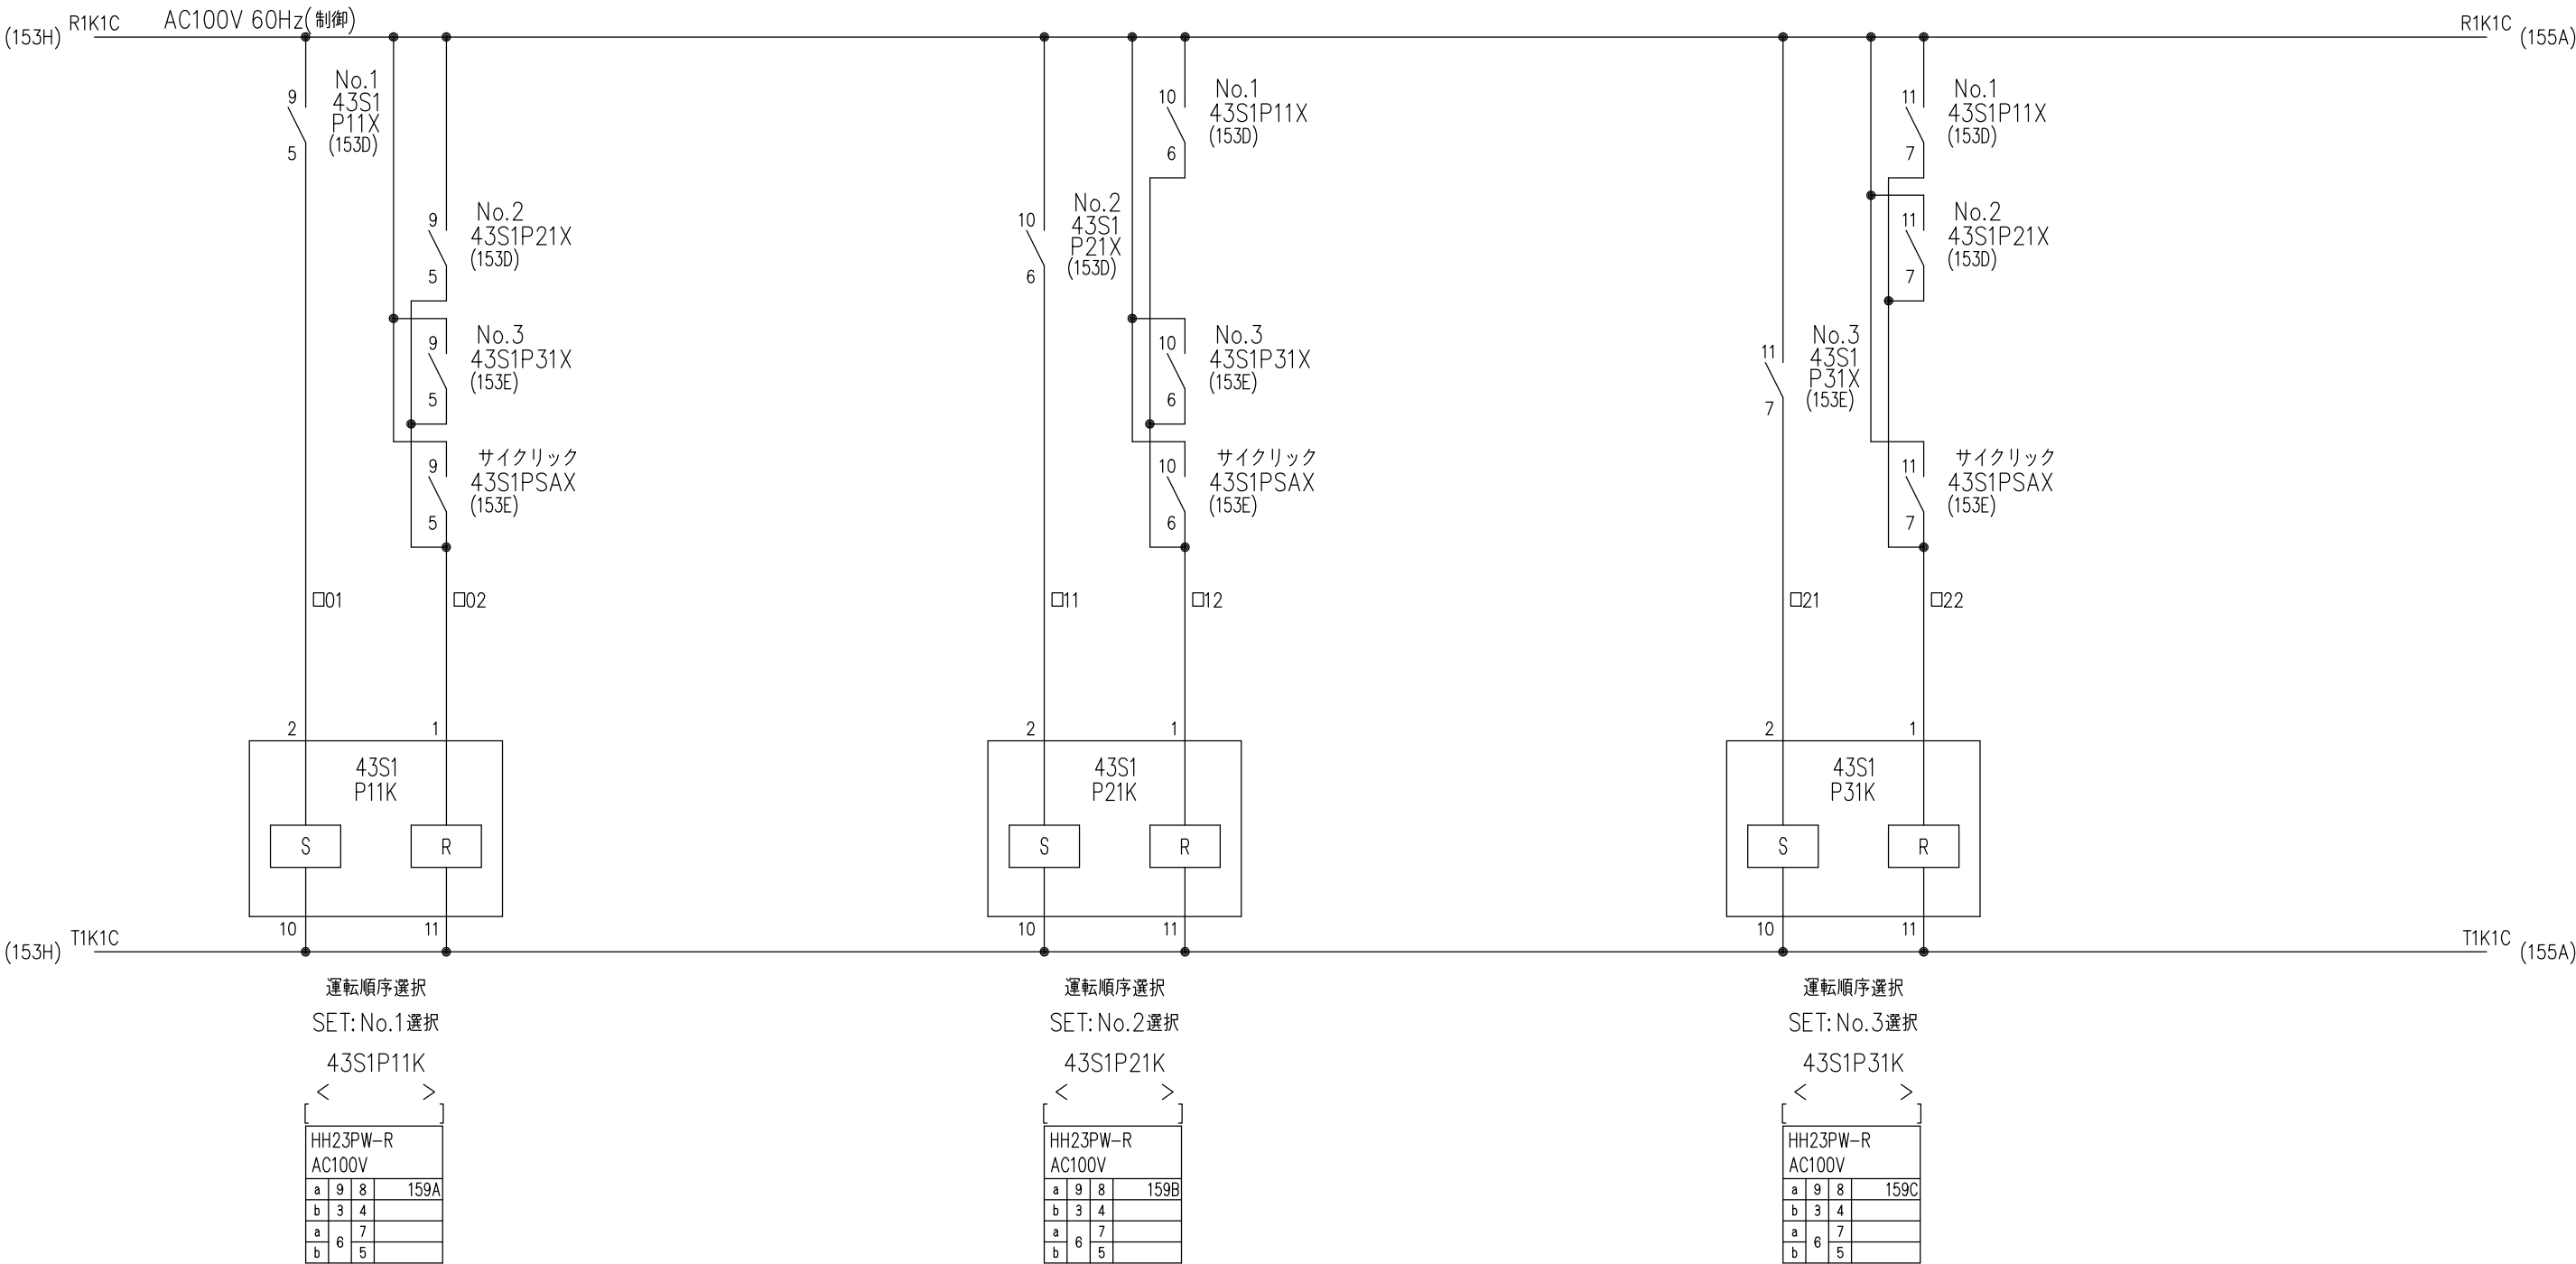

※線番上の□は頁を表す。

Revisions	)		Date	Name	メタウォーター株式会社 METAWATER Co., Ltd.	Title	汚水ポンプ 台数制御回路	Dwg.No.	MWA402712	154	
	)										
	)										
	)										
		Drawn	2024-09-20	丸小野/阿多				Ref.	VDW16_00_01		K01
		Checked	2024-09-20	丹/淵邊							
				舟木							

運轉順序選択

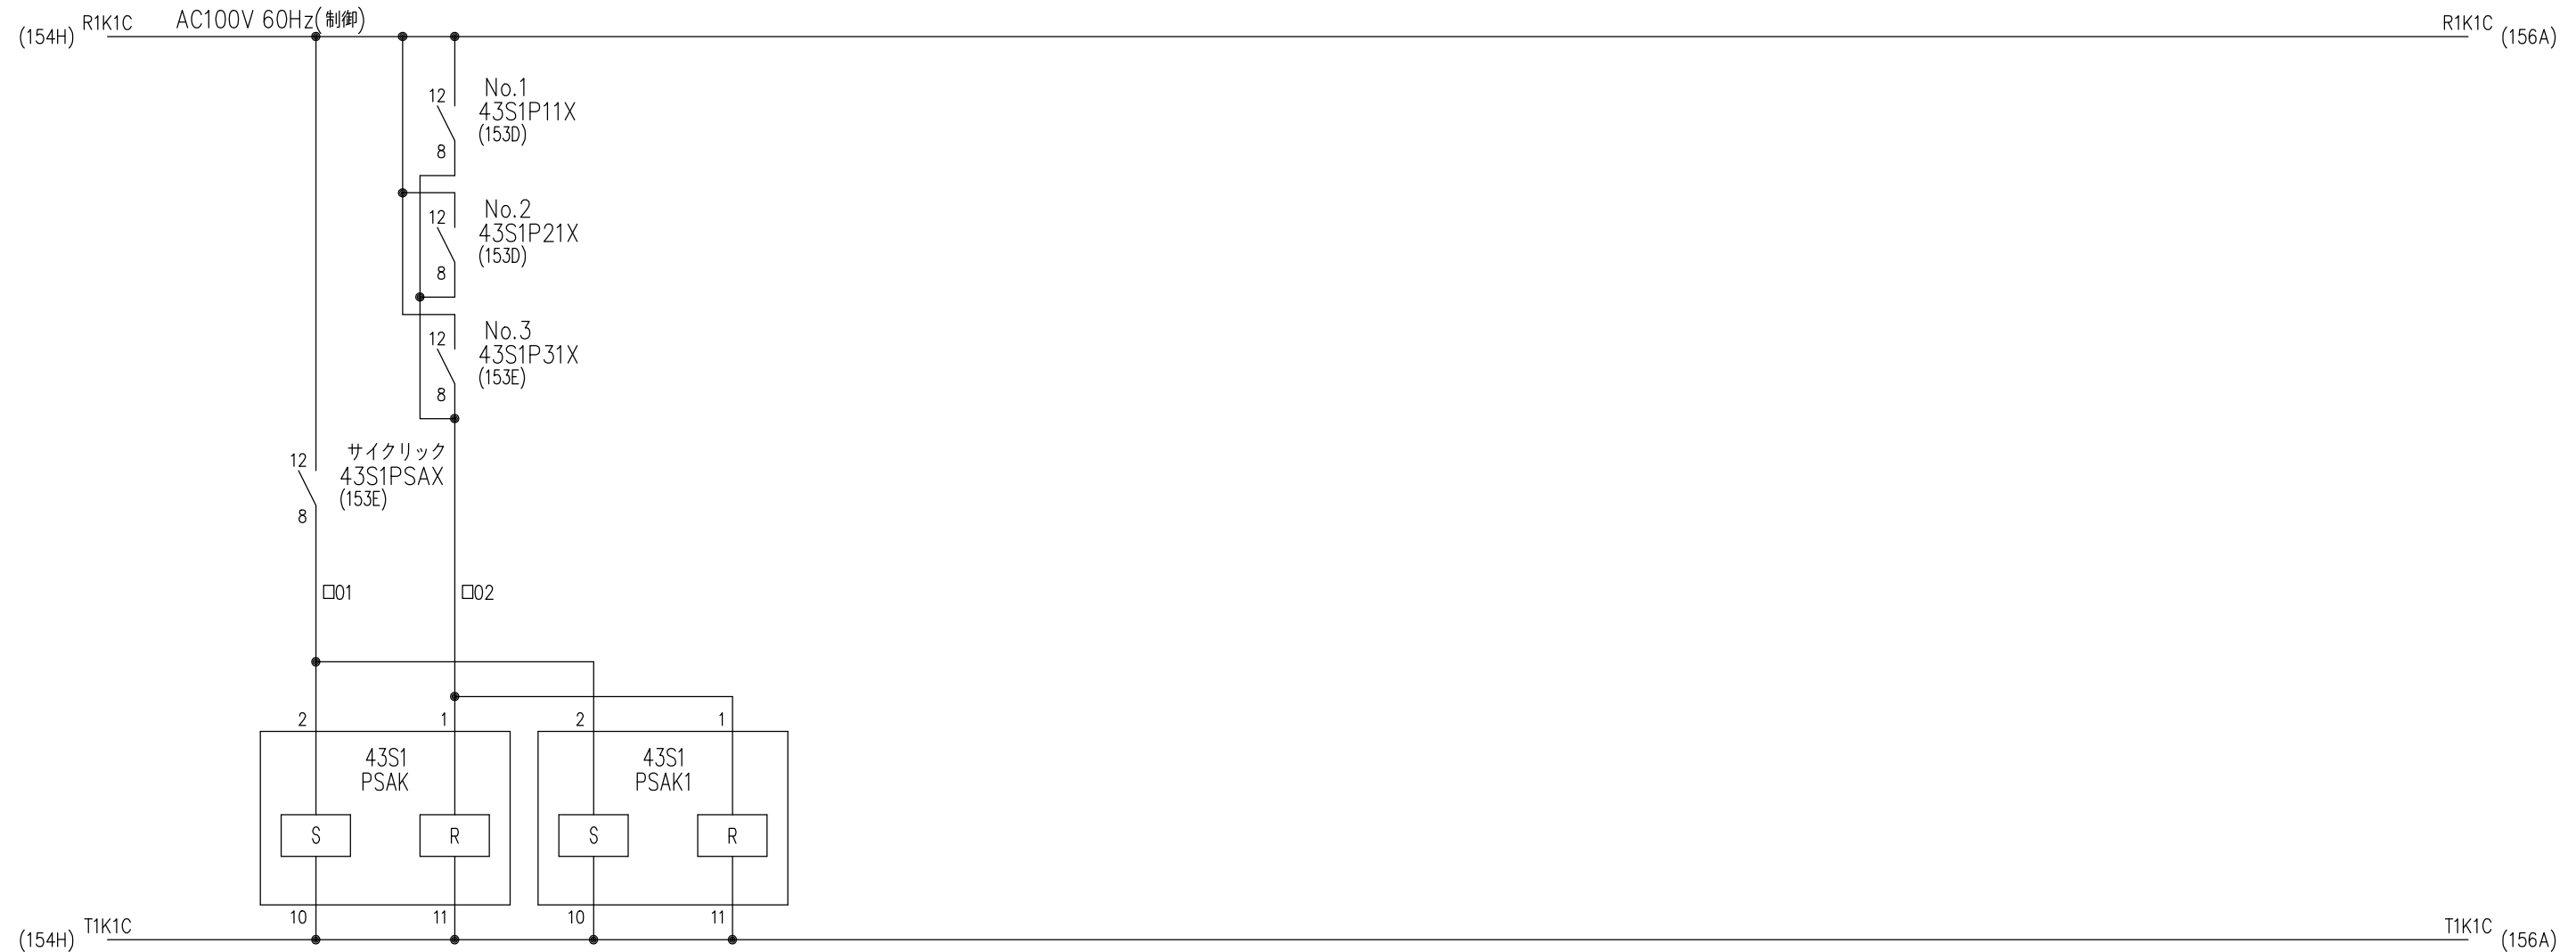

運転順序選択
SET: サイクリックモード


43S1PSAK
< >
[
HH23PW-R
AC100V
a 9 8 157A
b 3 4 157B
a 6 7
b 5

43S1PSAK1
< >
[
HH23PW-R
AC100V
a 9 8
b 3 4
a 6 7 216D
b 5 216D

※線番上の□は頁を表す。

Revisions	)		Date	Name	メタウォーター株式会社 METAWATER Co., Ltd.	Title		Dwg.No.	MWA402712	155		
	)	Drawn	2024-09-20	丸小野 / 阿多								
	)	Checked	2024-09-20	丹 / 淵邊								
	)			舟木								
								Ref.	VDW16_00_01	K01		
									汚水ポンプ			
									台数制御回路			

運転順序メモリ

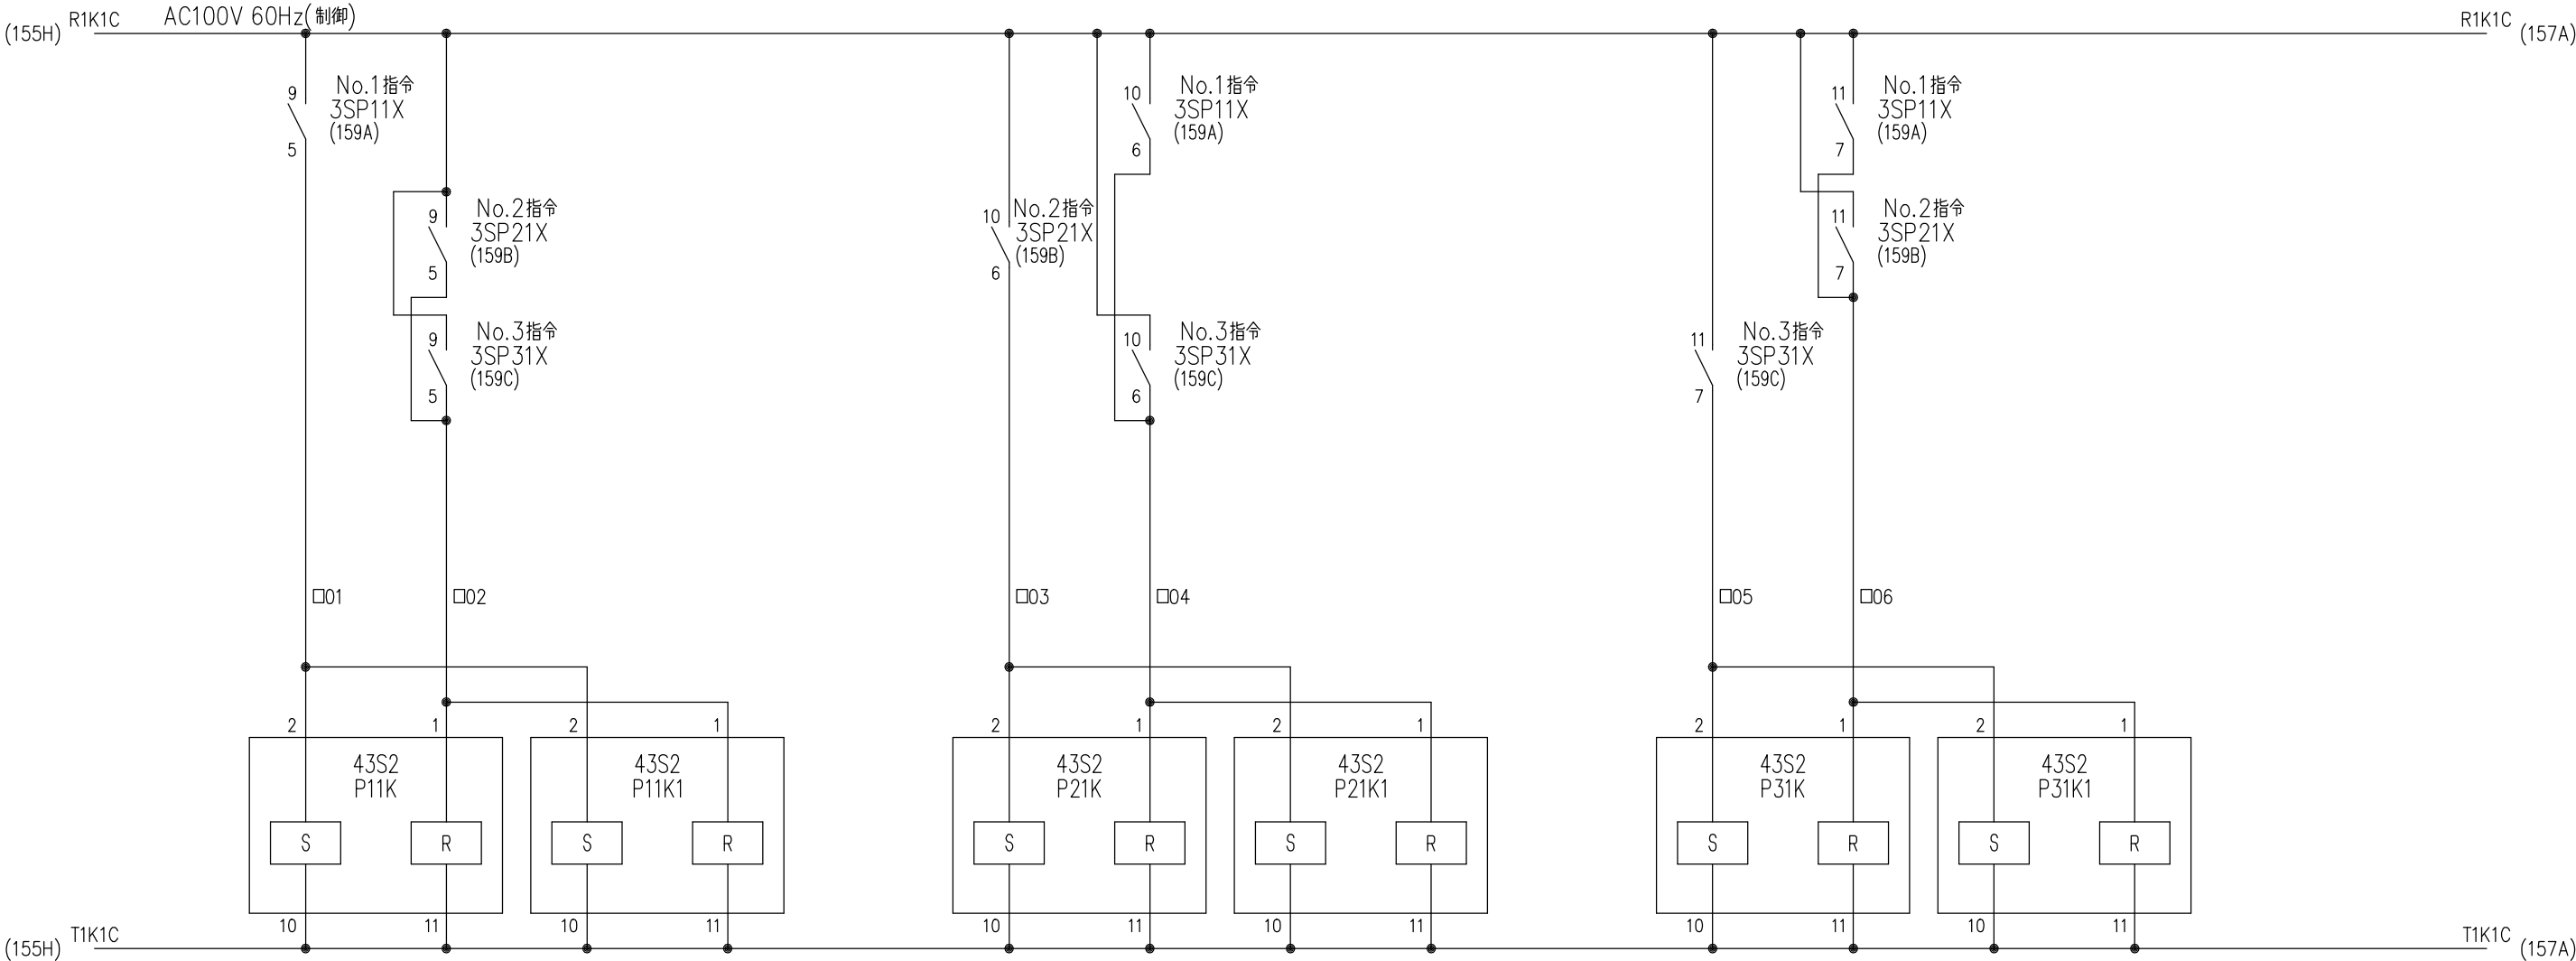

運転順序メモリ

SET:No.1

43S2P11K

< >

HH23PW-R AC100V			
a	9	8	158D
b	3	4	
a	7	216B	
b	6	216B	

43S2P11K1

< >

HH23PW-R AC100V			
a	9	8	160A
b	3	4	
a	7		
b	6	5	

運転順序メモリ

SET:No.2

43S2P21K

< >

HH23PW-R AC100V			
a	9	8	158E
b	3	4	
a	7	216B	
b	6	5	216C

43S2P21K1

< >

HH23PW-R AC100V			
a	9	8	160B
b	3	4	
a	7		
b	6	5	

運転順序メモリ

SET:No.3

43S2P31K

< >

HH23PW-R AC100V			
a	9	8	158F
b	3	4	
a	7	216C	
b	6	5	216C

43S2P31K1


< >

HH23PW-R AC100V			
a	9	8	160B
b	3	4	
a	7		
b	6	5	

※線番上の□は頁を表す。

Revisions	)		Date	Name	メタウォーター株式会社 METAWATER Co., Ltd.	Title	汚水ポンプ	Dwg.No.	MWA402712	156		
	)	Drawn	2024-09-20	丸小野/阿多								
	)	Checked	2024-09-20	丹/淵邊								
	)			舟木								
							台数制御回路	Ref.	VDW16_00_01			K01


運転順序切替

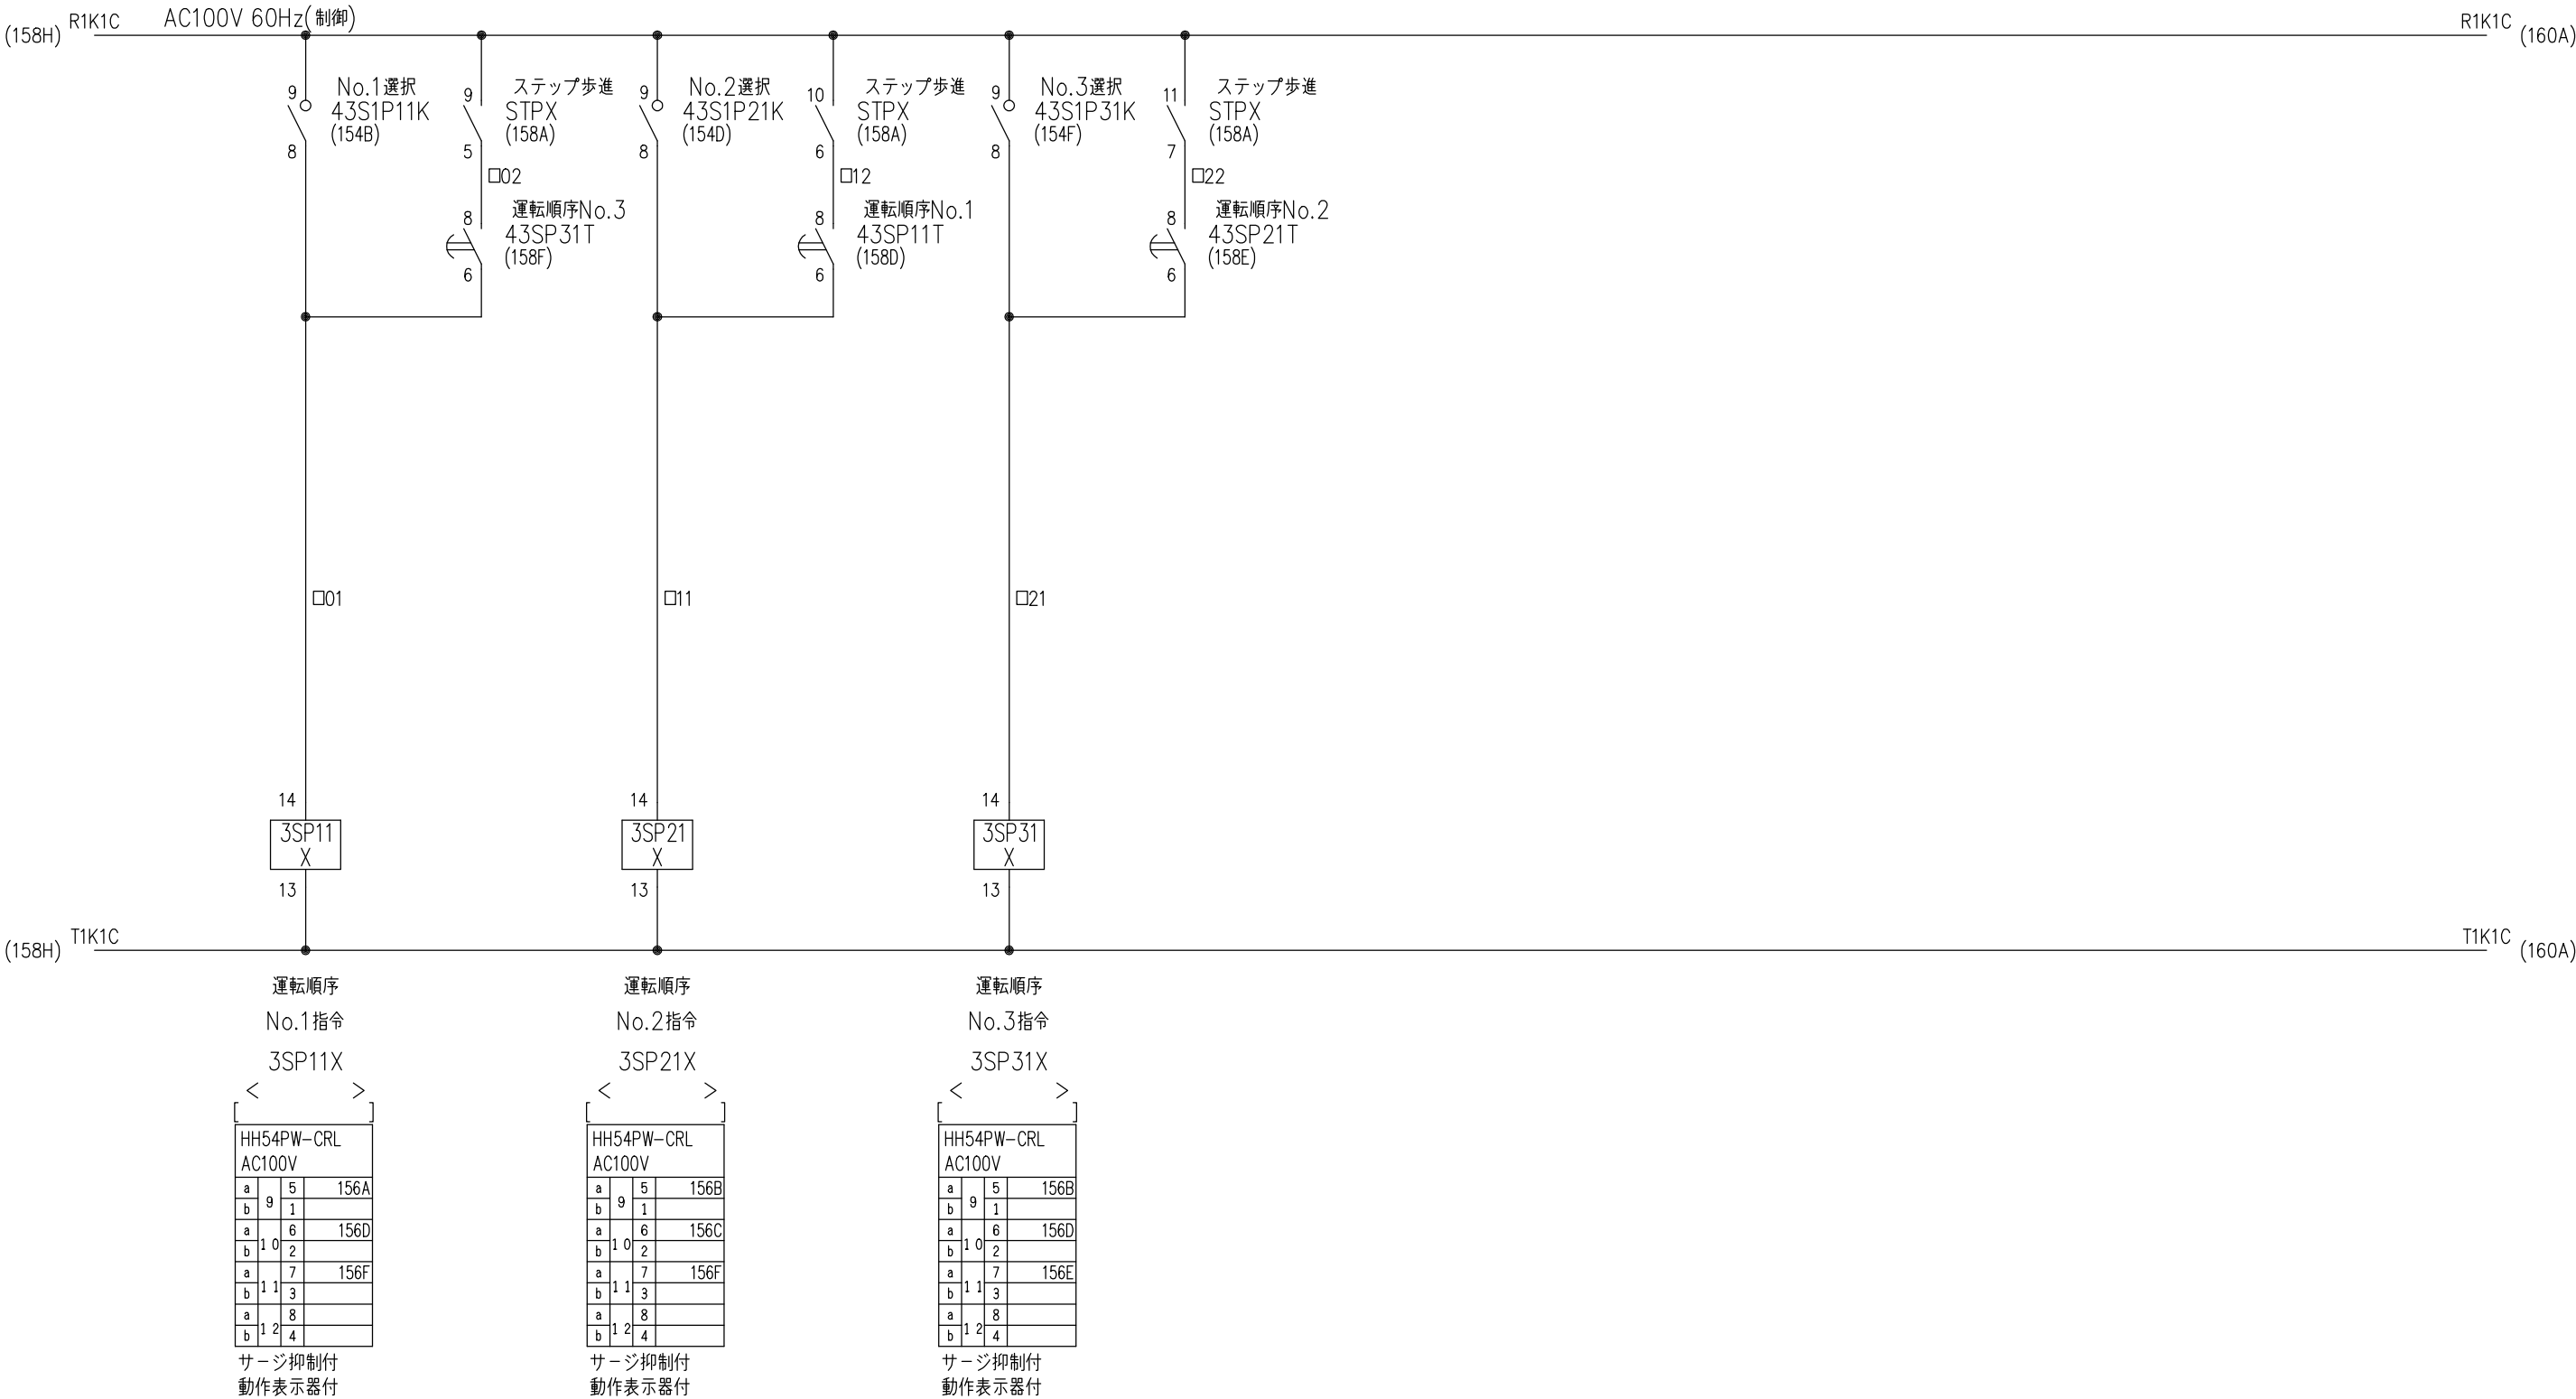

※線番上の□は頁を表す。

Revisions	)		Date	Name	メタウォーター株式会社 METAWATER Co., Ltd.	Title	汚水ポンプ	Dwg.No.	MWA402712	159			
	)	Drawn	2024-09-20	丸小野/阿多									
	)	Checked	2024-09-20	丹/淵邊			台数制御回路	Ref.	VDW16_00_01	K01			
	)			舟木									

運転・停止順序切替

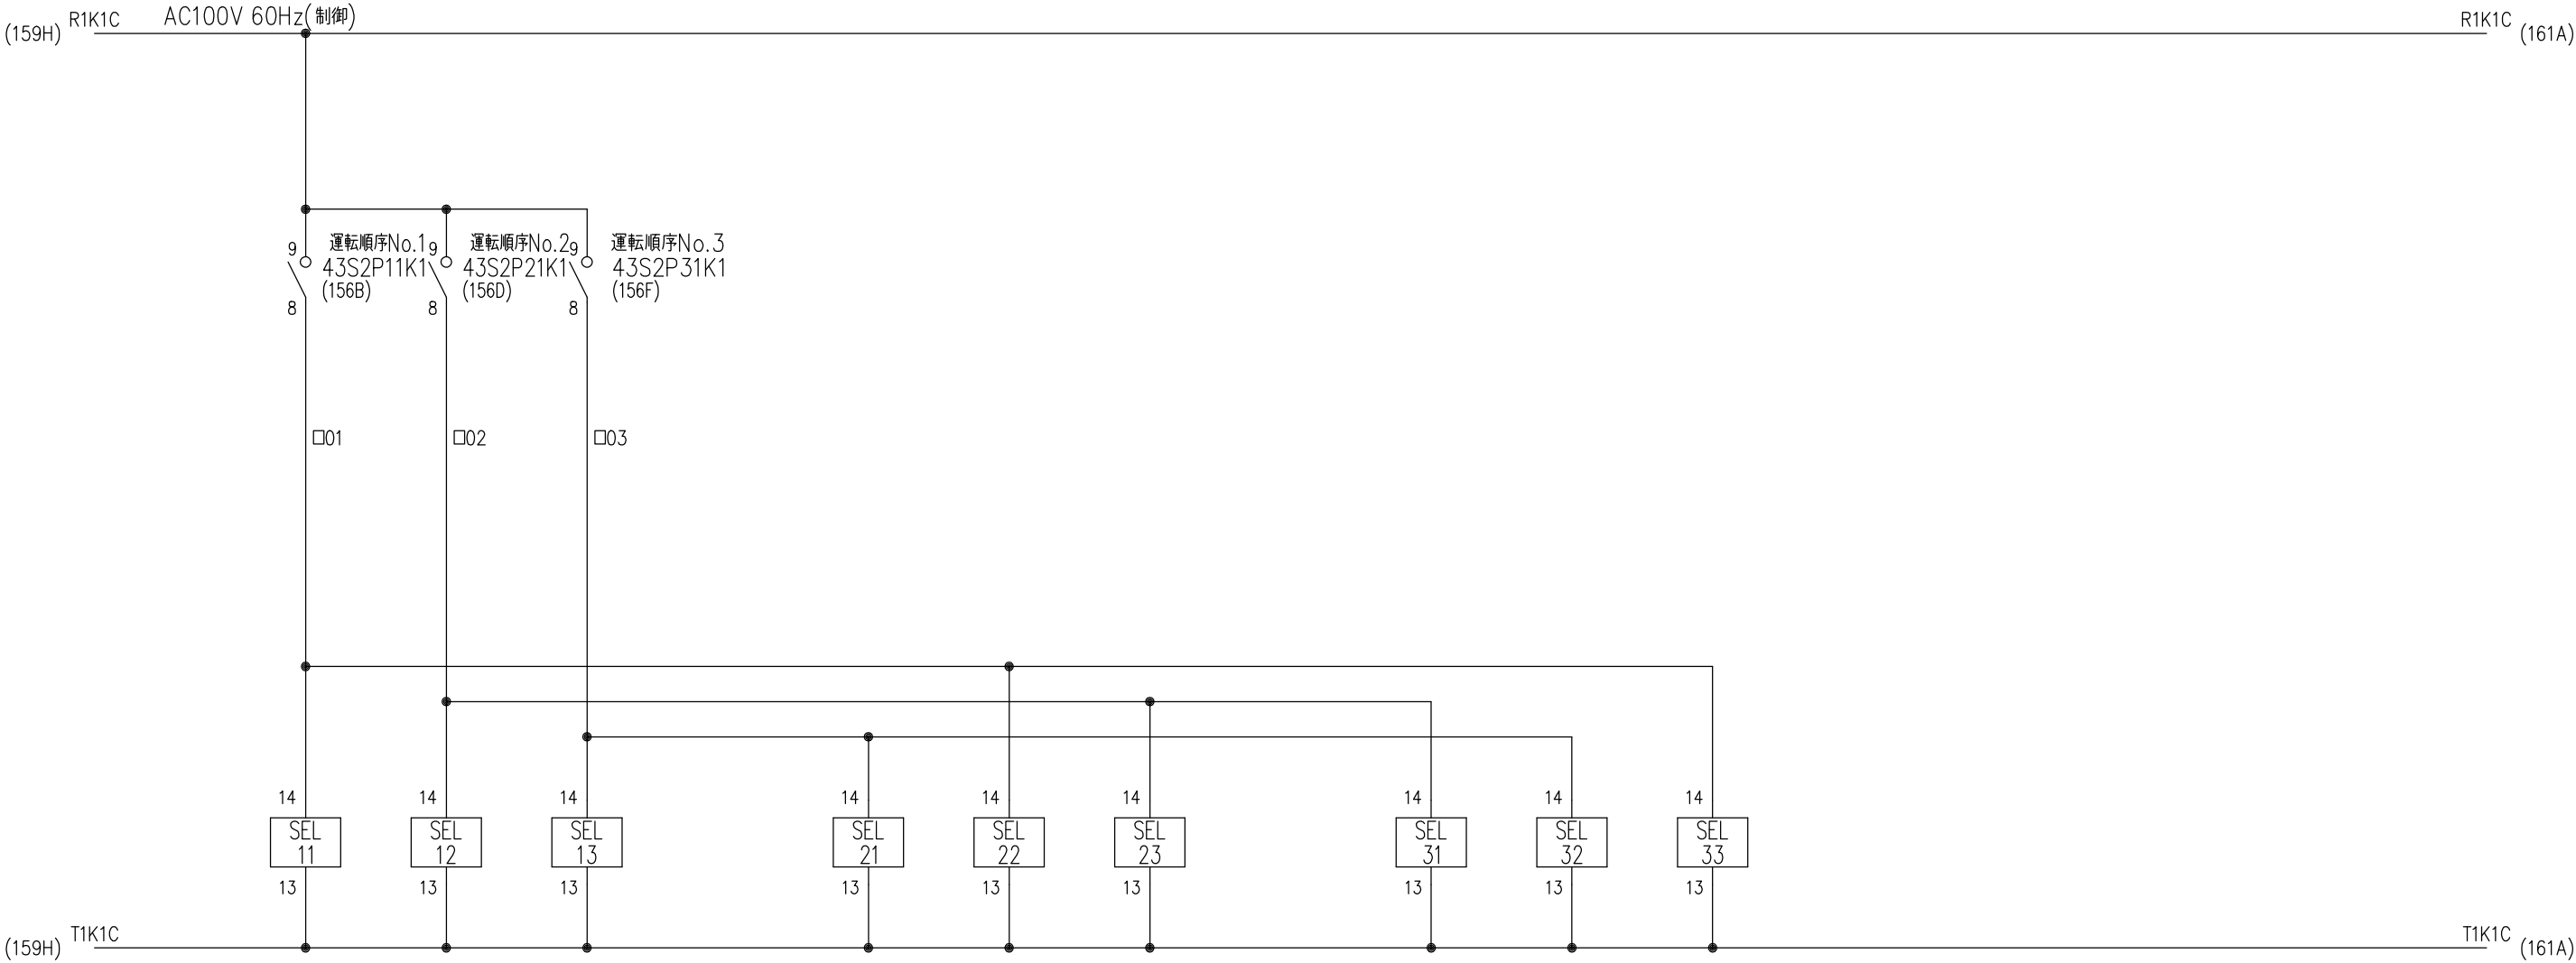

SEL11		SEL12		SEL13	
< >		< >		< >	
HH54PW-CRL AC100V		HH54PW-CRL AC100V		HH54PW-CRL AC100V	
a	5 163A	a	5 163B	a	5 163C
b	9 1	b	9 1	b	9 1
a	6 166A	a	6 166B	a	6 166C
b	10 2	b	10 2	b	10 2
a	7	a	7	a	7
b	11 3	b	11 3	b	11 3
a	8	a	8	a	8
b	12 4	b	12 4	b	12 4
サージ抑制付 動作表示器付		サージ抑制付 動作表示器付		サージ抑制付 動作表示器付	


SEL21		SEL22		SEL23	
< >		< >		< >	
HH54PW-CRL AC100V		HH54PW-CRL AC100V		HH54PW-CRL AC100V	
a	5 163D	a	5 163E	a	5 163E
b	9 1	b	9 1	b	9 1
a	6 165D	a	6 165E	a	6 165E
b	10 2	b	10 2	b	10 2
a	7	a	7	a	7
b	11 3	b	11 3	b	11 3
a	8	a	8	a	8
b	12 4	b	12 4	b	12 4
サージ抑制付 動作表示器付		サージ抑制付 動作表示器付		サージ抑制付 動作表示器付	

SEL31		SEL32		SEL33	
< >		< >		< >	
HH54PW-CRL AC100V		HH54PW-CRL AC100V		HH54PW-CRL AC100V	
a	5 164A	a	5 164B	a	5 164C
b	9 1	b	9 1	b	9 1
a	6 165A	a	6 165B	a	6 165C
b	10 2	b	10 2	b	10 2
a	7	a	7	a	7
b	11 3	b	11 3	b	11 3
a	8	a	8	a	8
b	12 4	b	12 4	b	12 4
サージ抑制付 動作表示器付		サージ抑制付 動作表示器付		サージ抑制付 動作表示器付	

※線番上の□は頁を表す。

Revisions	)		Date	Name	メタウォーター株式会社 METAWATER Co., Ltd.	Title	汚水ポンプ	Dwg.No.	MWA402712	160	
	)	Drawn	2024-09-20	丸小野/阿多							
	)	Checked	2024-09-20	丹/淵邊							
	)			舟木							

ポンプ運転台数

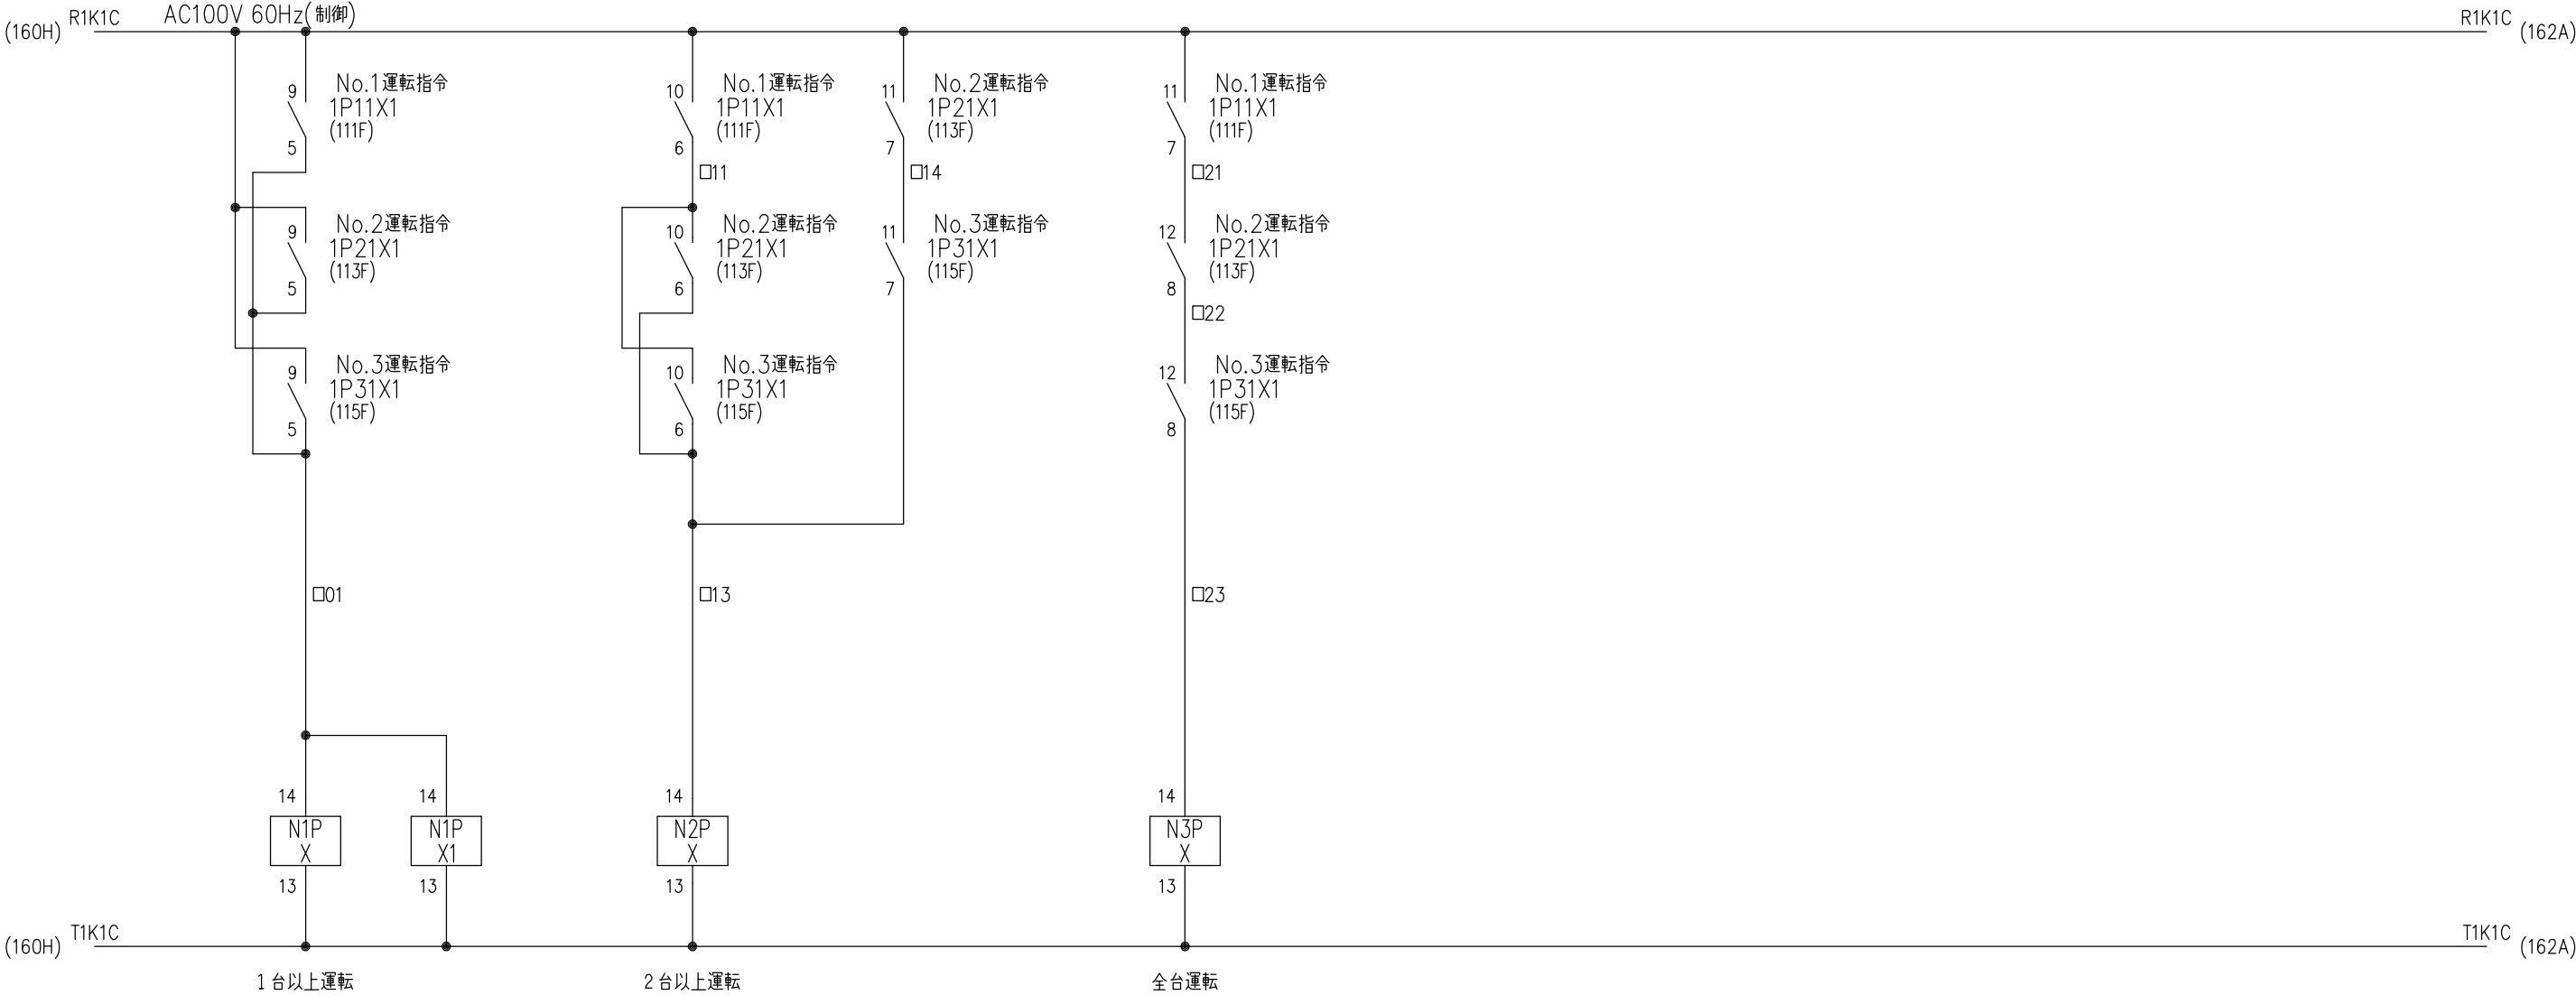

< N1PX >				< N1PX1 >			
HH54PW-CRL AC100V				HH54PW-CRL AC100V			
a	9	5	162B	a	9	5	167C
b	1			b	1		
a		6		a		6	
b	10	2	162A	b	10	2	
a		7	162C	a		7	
b	11	3		b	11	3	
a		8	157A	a		8	
b	12	4		b	12	4	
サージ抑制付 動作表示器付				サージ抑制付 動作表示器付			


< N2PX >			
HH54PW-CRL AC100V			
a	9	5	162C
b	1		
a		6	
b	10	2	162C
a		7	162D
b	11	3	
a		8	167E
b	12	4	
サージ抑制付 動作表示器付			

< N3PX >			
HH54PW-CRL AC100V			
a	9	5	162E
b	1		
a		6	
b	10	2	162D
a		7	167F
b	11	3	
a		8	
b	12	4	
サージ抑制付 動作表示器付			

※線番上の□は頁を表す。

Revisions	)		Date	Name	メタウォーター株式会社 METAWATER Co., Ltd.	Title	汚水ポンプ	Dwg.No.	MWA402712	161	
	)	Drawn	2024-09-20	丸小野 / 阿多							
	)	Checked	2024-09-20	丹 / 淵邊							
	)			舟木							
							台数制御回路	Ref.	VDW16_00_04		K01

追加・削除要求

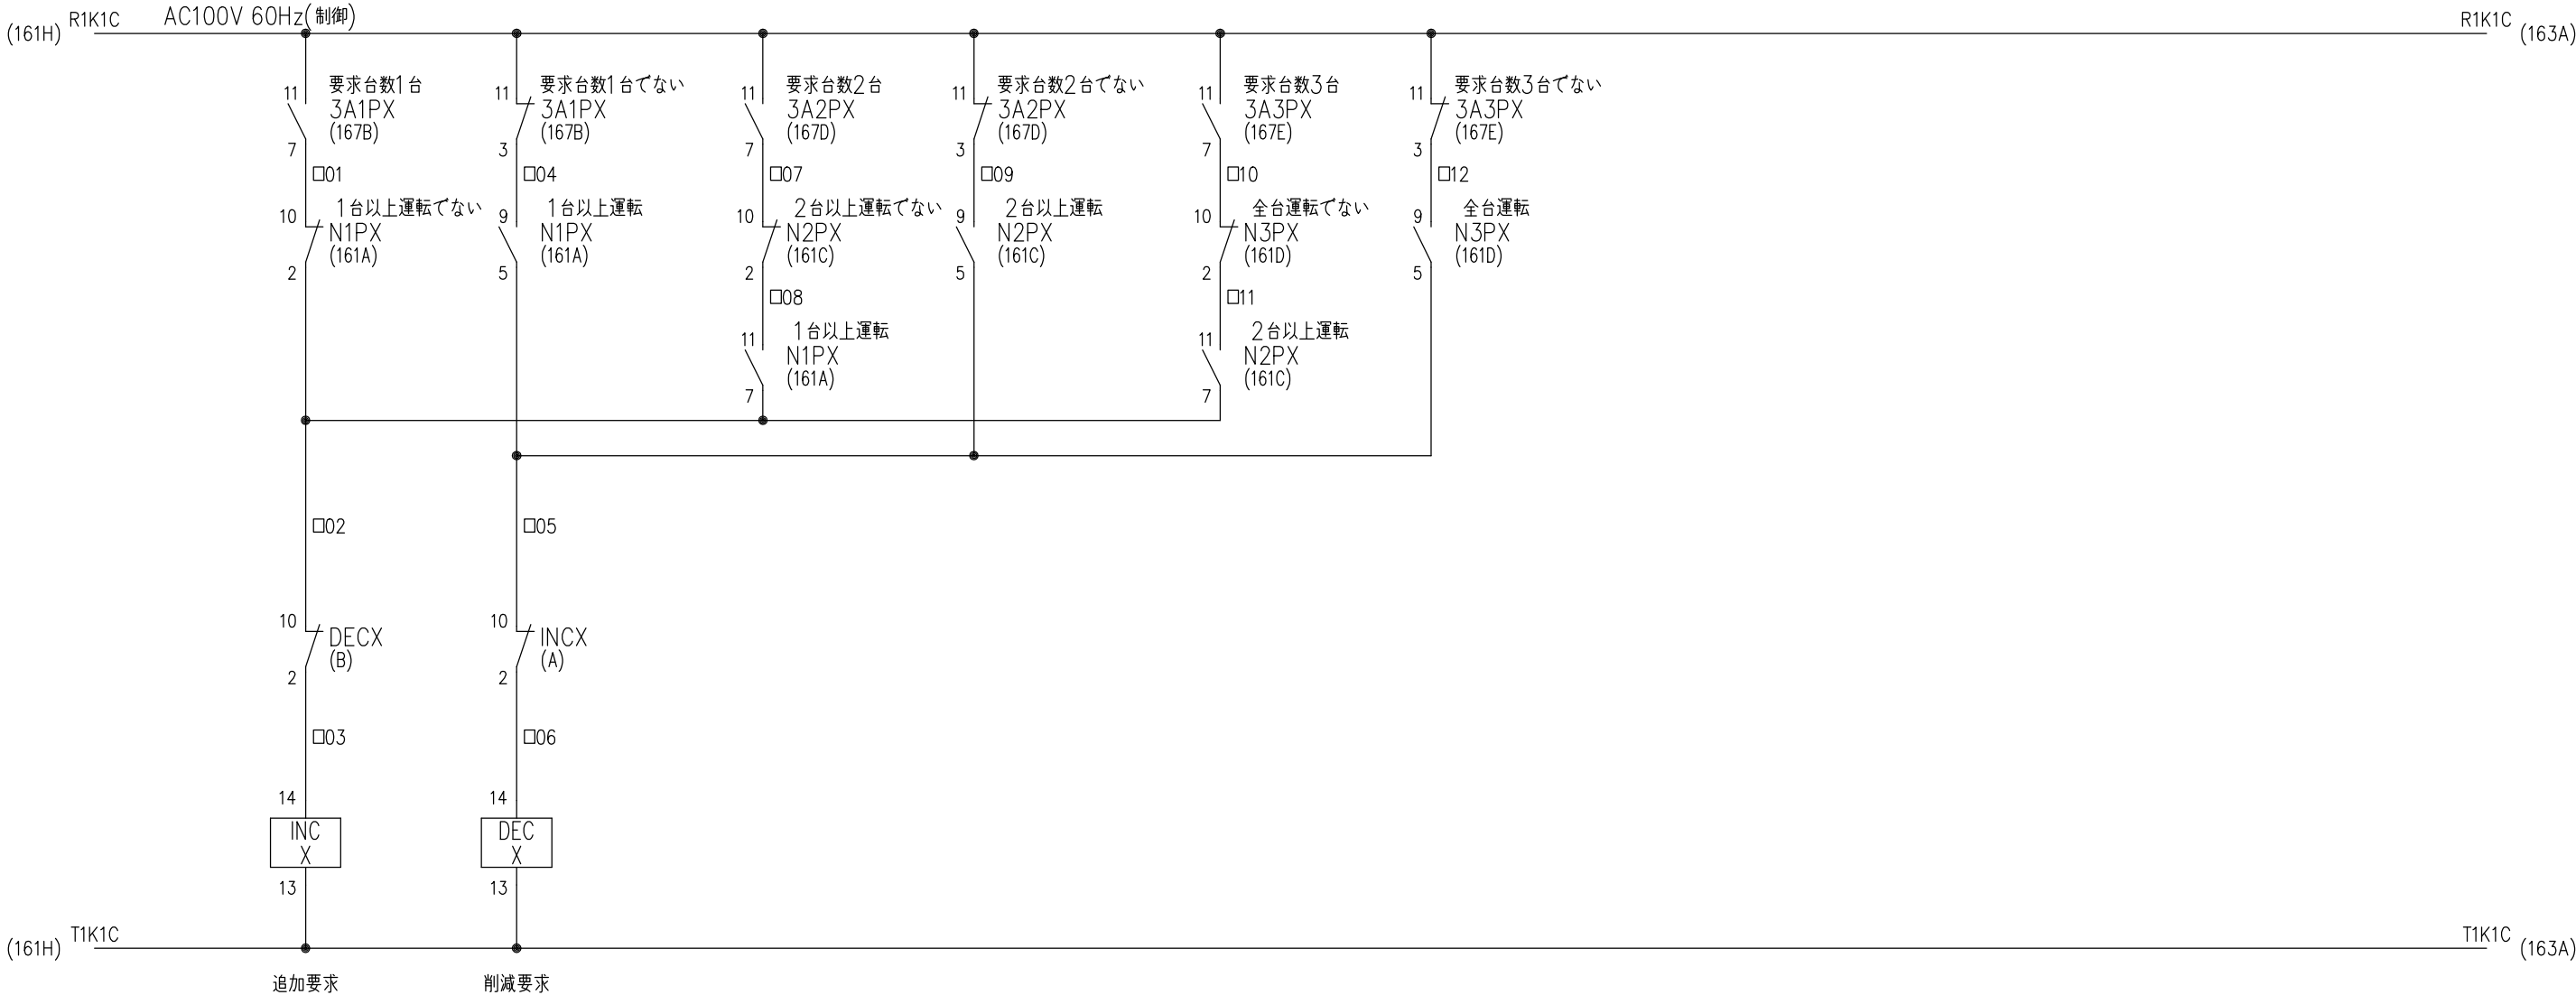

INCX

< >			
HH54PW-CRL			
AC100V			
a	5	163A	
b	9	1	
a	6		
b	10	2	B
a	7		
b	11	3	
a	8		
b	12	4	

サージ抑制付
動作表示器付

DECX

< >			
HH54PW-CRL			
AC100V			
a	5	165A	
b	9	1	
a	6		
b	10	2	A
a	7		
b	11	3	
a	8		
b	12	4	


サージ抑制付
動作表示器付

※線番上の□は頁を表す。

Revisions	)	Date	Name	Title	汚水ポンプ	Dwg.No.	MWA402712	162		
	)									
	)				台数制御回路	Ref.	VDW16_00_05			K01
	)									

A	B	C	D	E	F	G	H
---	---	---	---	---	---	---	---

ポンプ運転指令

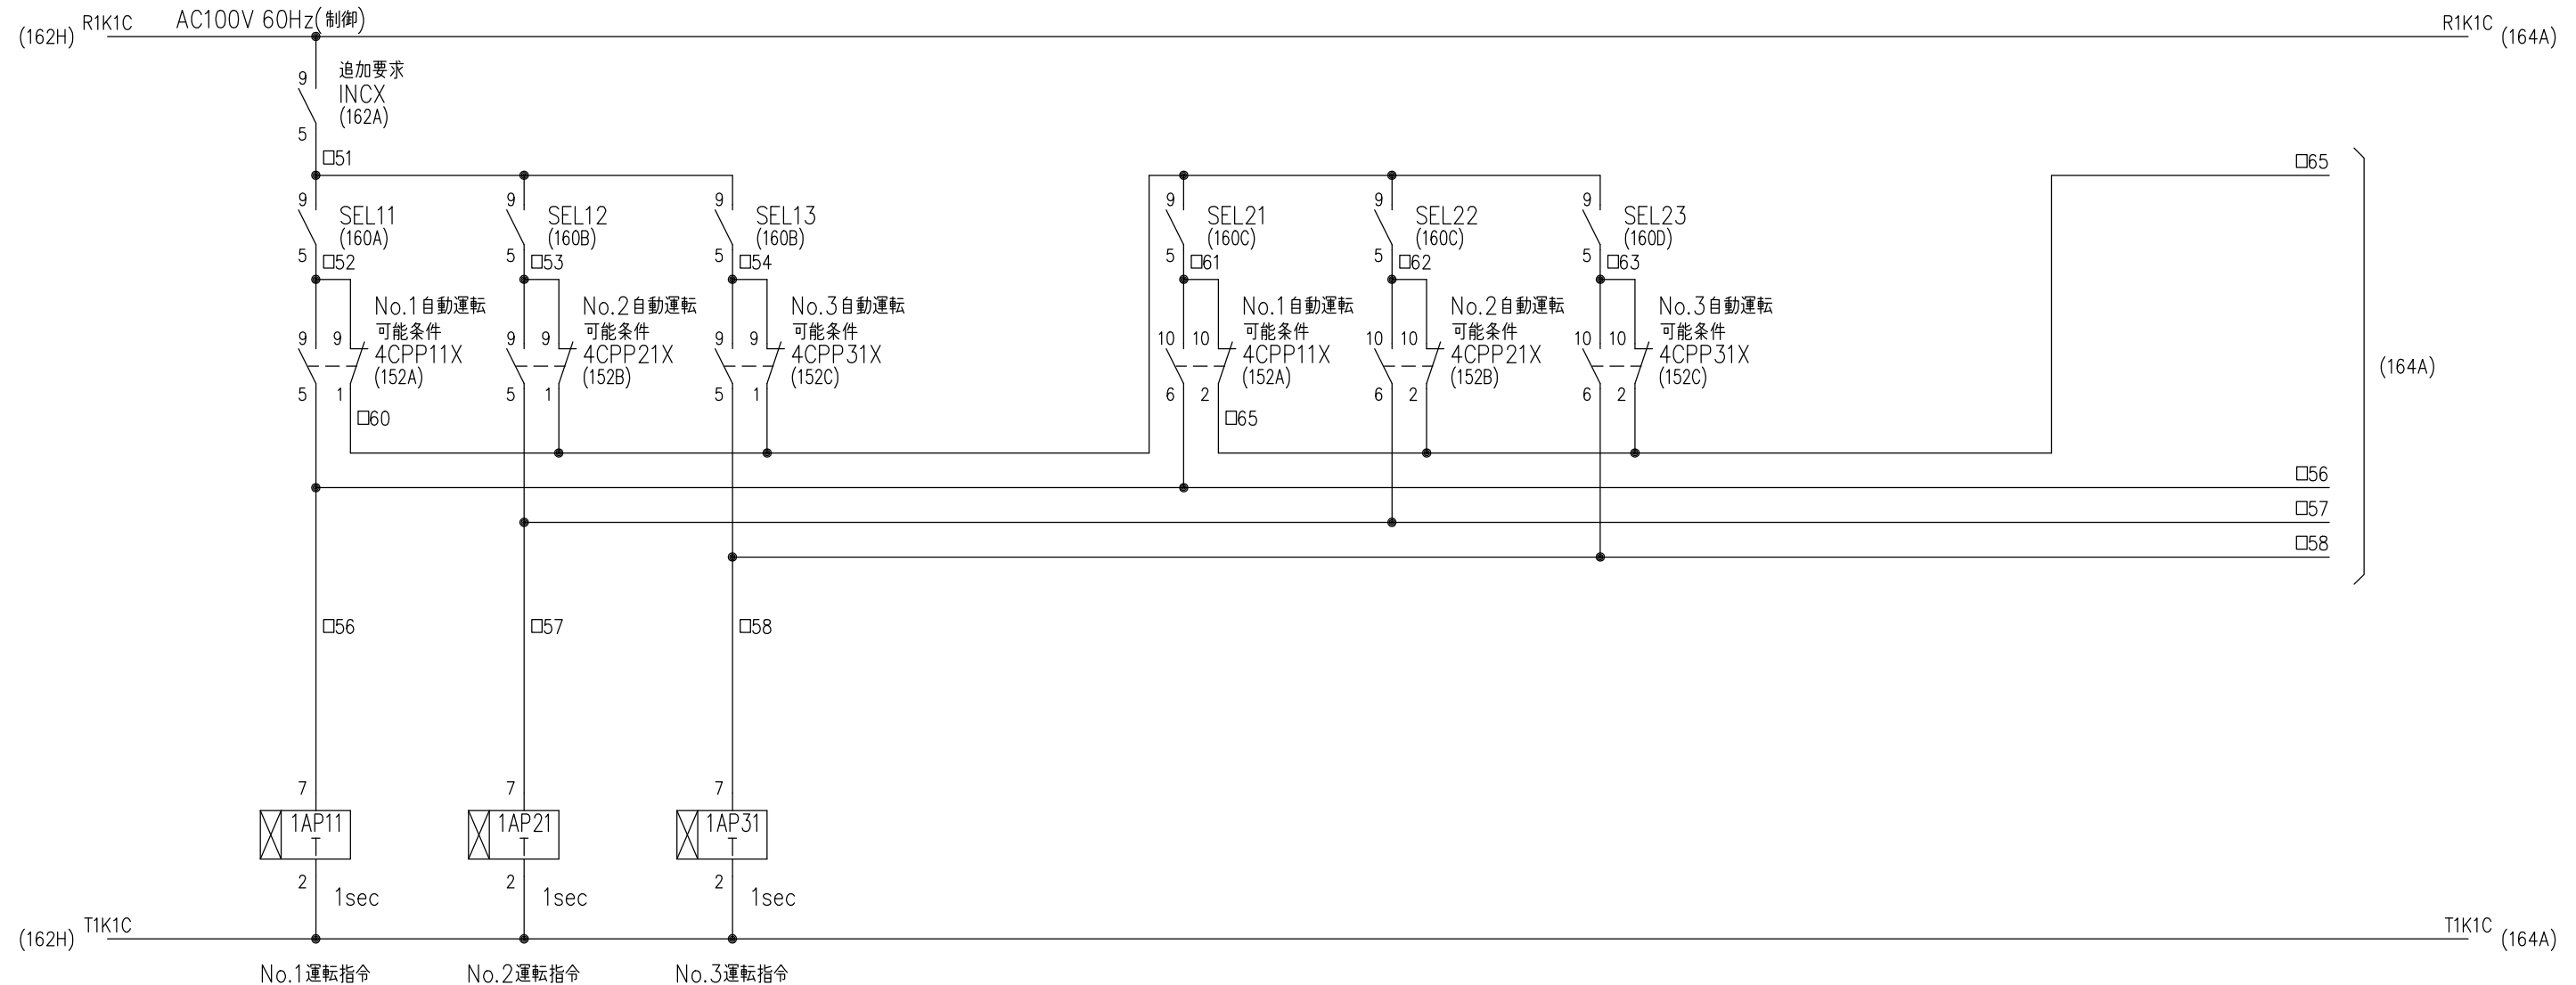

1AP11T			
<		>	
MS4SA-AP AC100V			
T a	8	6	2660
T b		5	
T a	1	3	
T b		4	


1AP21T			
<		>	
MS4SA-AP			
AC100V			
T a	8	6	2670
T b		5	
T a	1	3	
T b		4	

1AP31T			
<		>	
MS4SA-AP			
AC100V			
T a		6	2680
T b	8	5	
T a		3	
T b	1	4	

※線番上の□は頁を表す。

Revisions	)		Date	Name	メタウォーター株式会社 METAWATER Co., Ltd.	Title	汚水ポンプ	Dwg.No.	MWA402712	163				
	)	Drawn	2024-09-20	丸小野 / 阿多				台数制御回路	Ref.	VDW16_00_06	K01			
	)	Checked	2024-09-20	丹 / 淵邊										
	)			舟木										

ポンプ停止指令

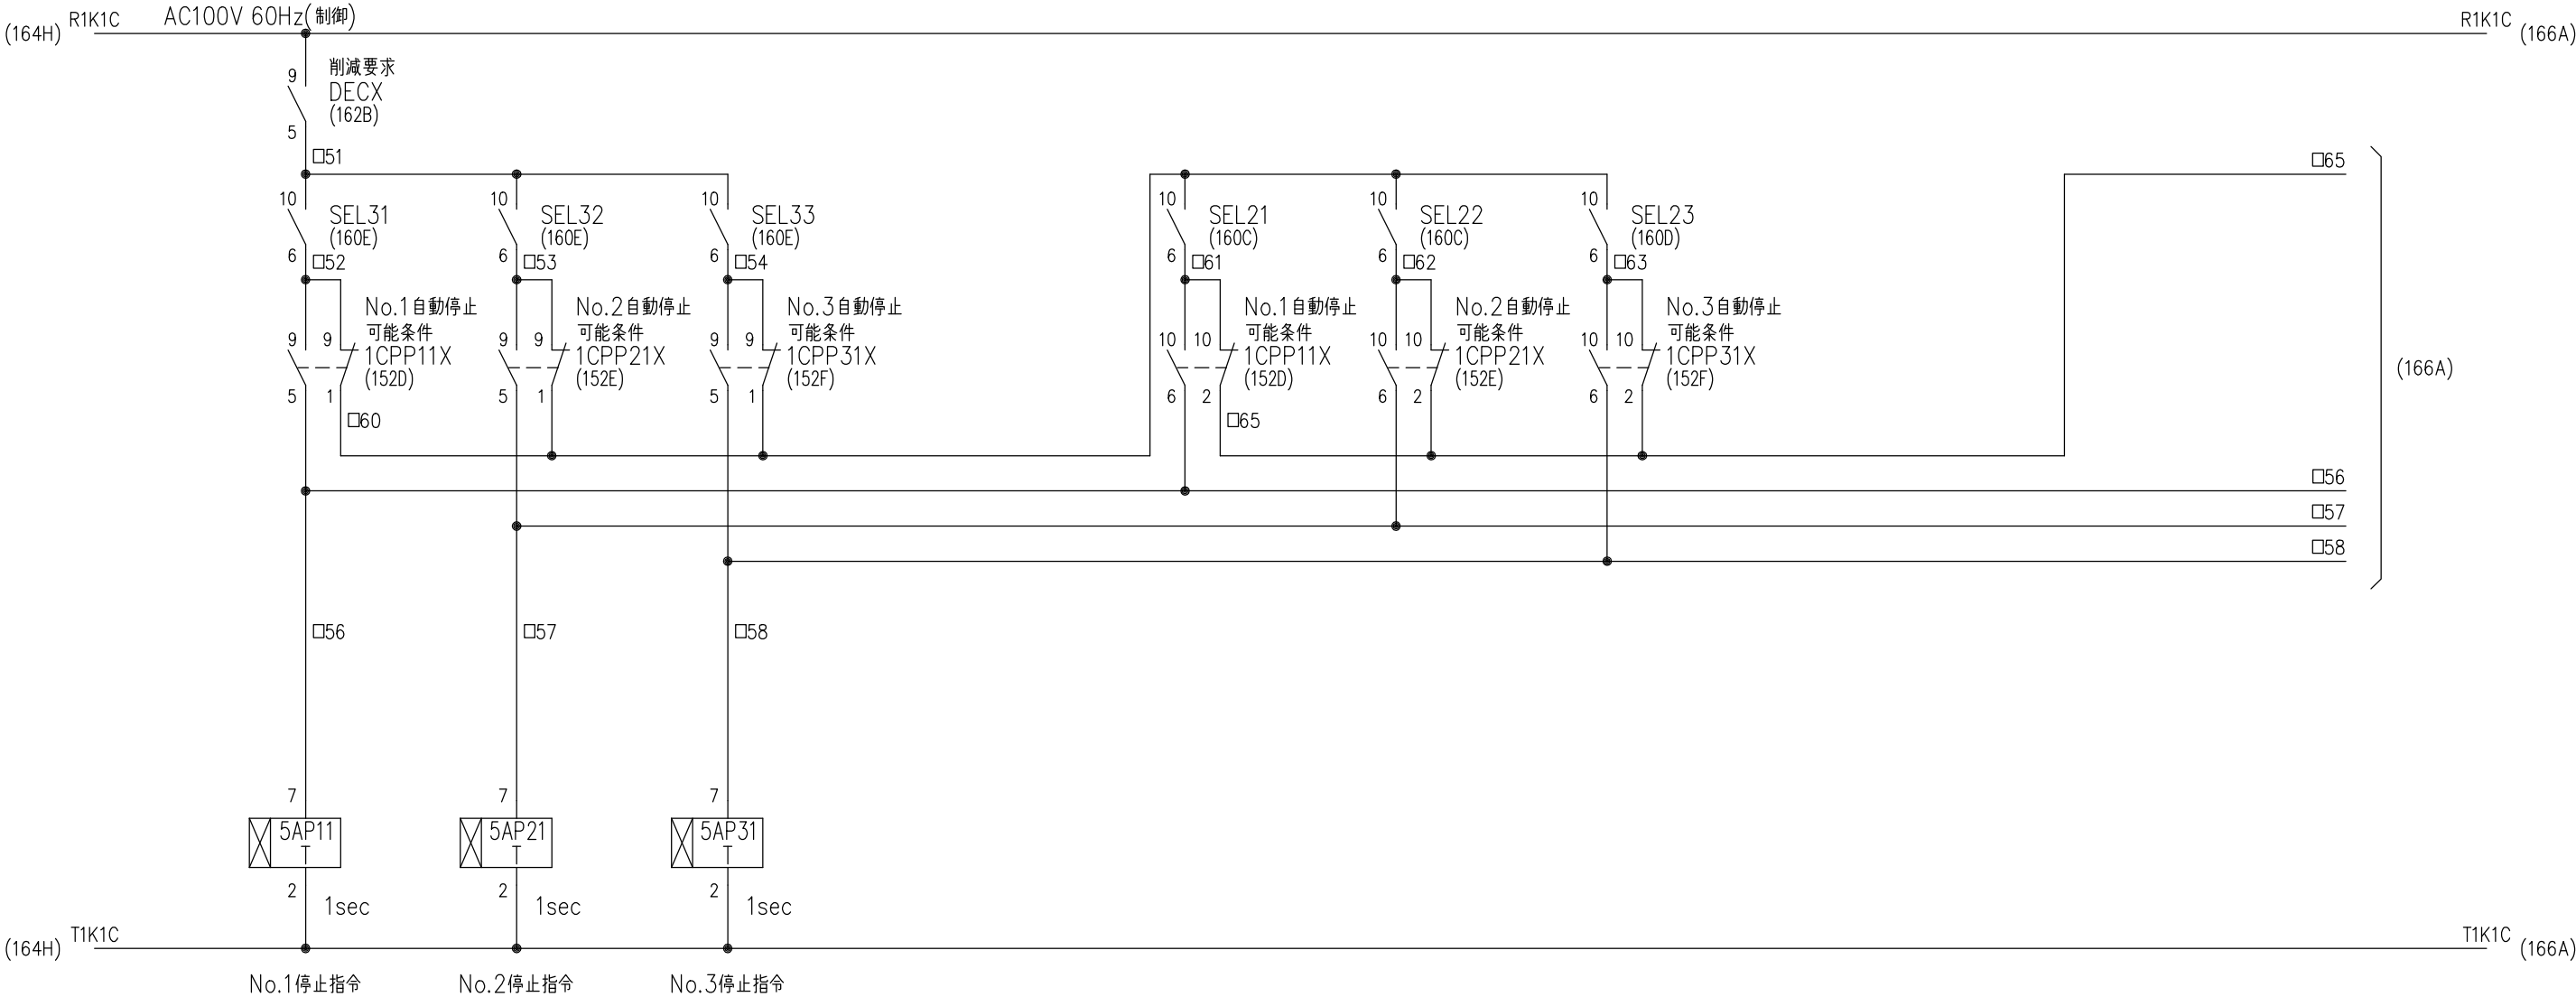

5AP11T			
<		>	
MS4SA-AP			
AC100V			
T a		6	266D
T b	8	5	
T a		3	
T b	1	4	

5AP21T			
<		>	
MS4SA-AP			
AC100V			
T a	8	6	267D
T b		5	
T a	1	3	
T b		4	


5AP31T			
<		>	
[			
MS4SA-AP			
AC100V			
T a	8	6	268D
T b		5	
T a	1	3	
T b		4	

※線番上の□は頁を表す。

Revisions	)		Date	Name	メタウォーター株式会社 METAWATER Co., Ltd.	Title		Dwg.No.	MWA402712	165	
	)	Drawn	2024-09-20	丸小野 / 阿多							
	)	Checked	2024-09-20	丹 / 淵邊							
	)			舟木							
							Ref.	VDW16_00_08a			K01

ポンプ停止指令


(165H) R1K1C AC100V 60Hz(制御) R1K1C (167A)

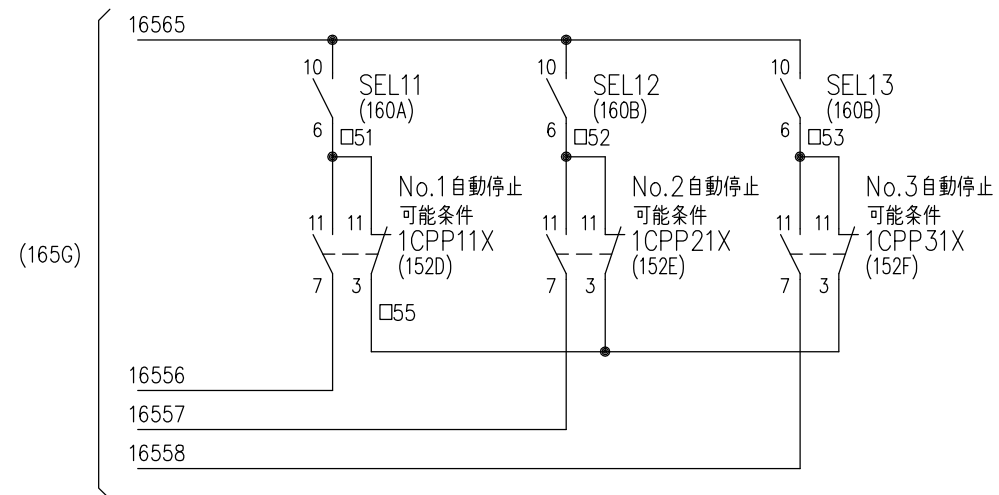

(165H) T1K1C T1K1C (167A)

※線番上の□は頁を表す。

Revisions	)		Date	Name	メタウォーター株式会社 METAWATER Co., Ltd.	Title	汚水ポンプ	Dwg.No.	MWA402712	166			
	)	Drawn	2024-09-20	丸小野 / 阿多									
	)	Checked	2024-09-20	丹 / 淵邊			台数制御回路	Ref.	VDW16_00_09a	K01			
	)			舟木									

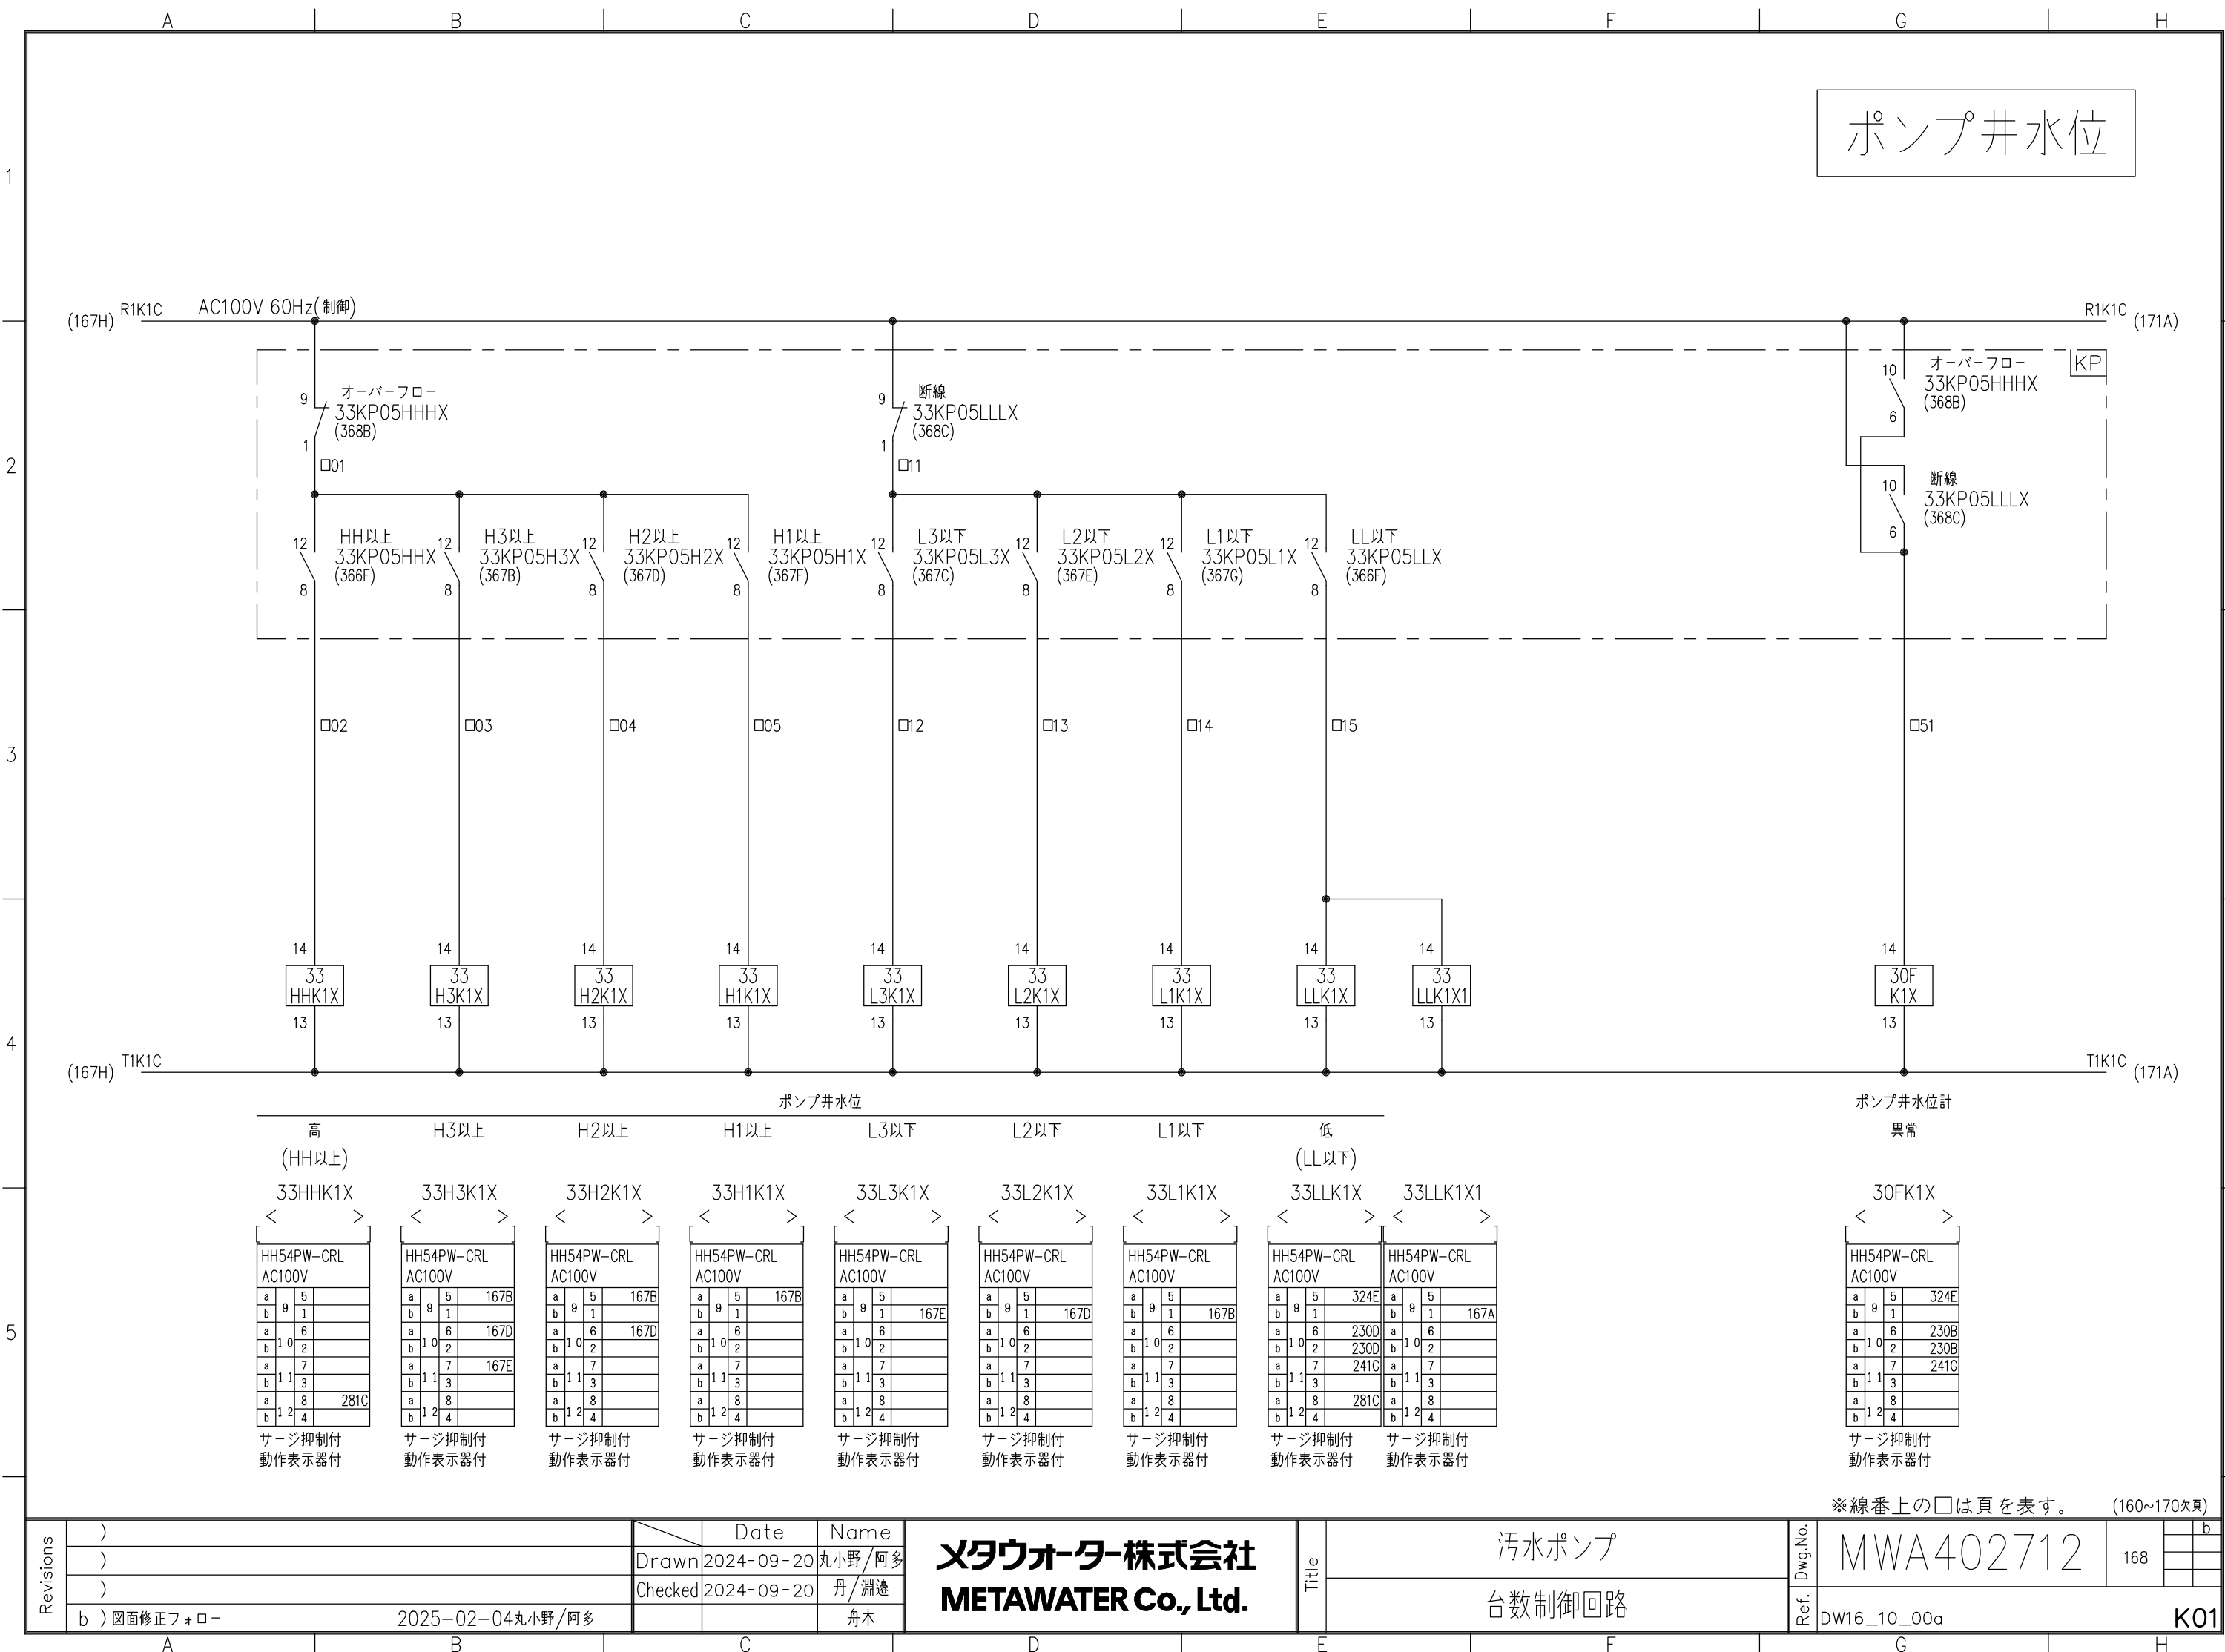

※線番上の□は頁を表す。(160~170欠頁)

Revisions

)

)

)

b) 図面修正フォロー

Drawn

2024-09-20

丸小野/阿多

Checked

2024-09-20

丹/淵邊

Date

2025-02-04

丸小野/阿多

Name

舟木

メタウォーター株式会社

METAWATER Co., Ltd.

Title

汚水ポンプ

台数制御回路

Dwg.No.


MWA402712


168

Ref.

DW16_10_00a

K01

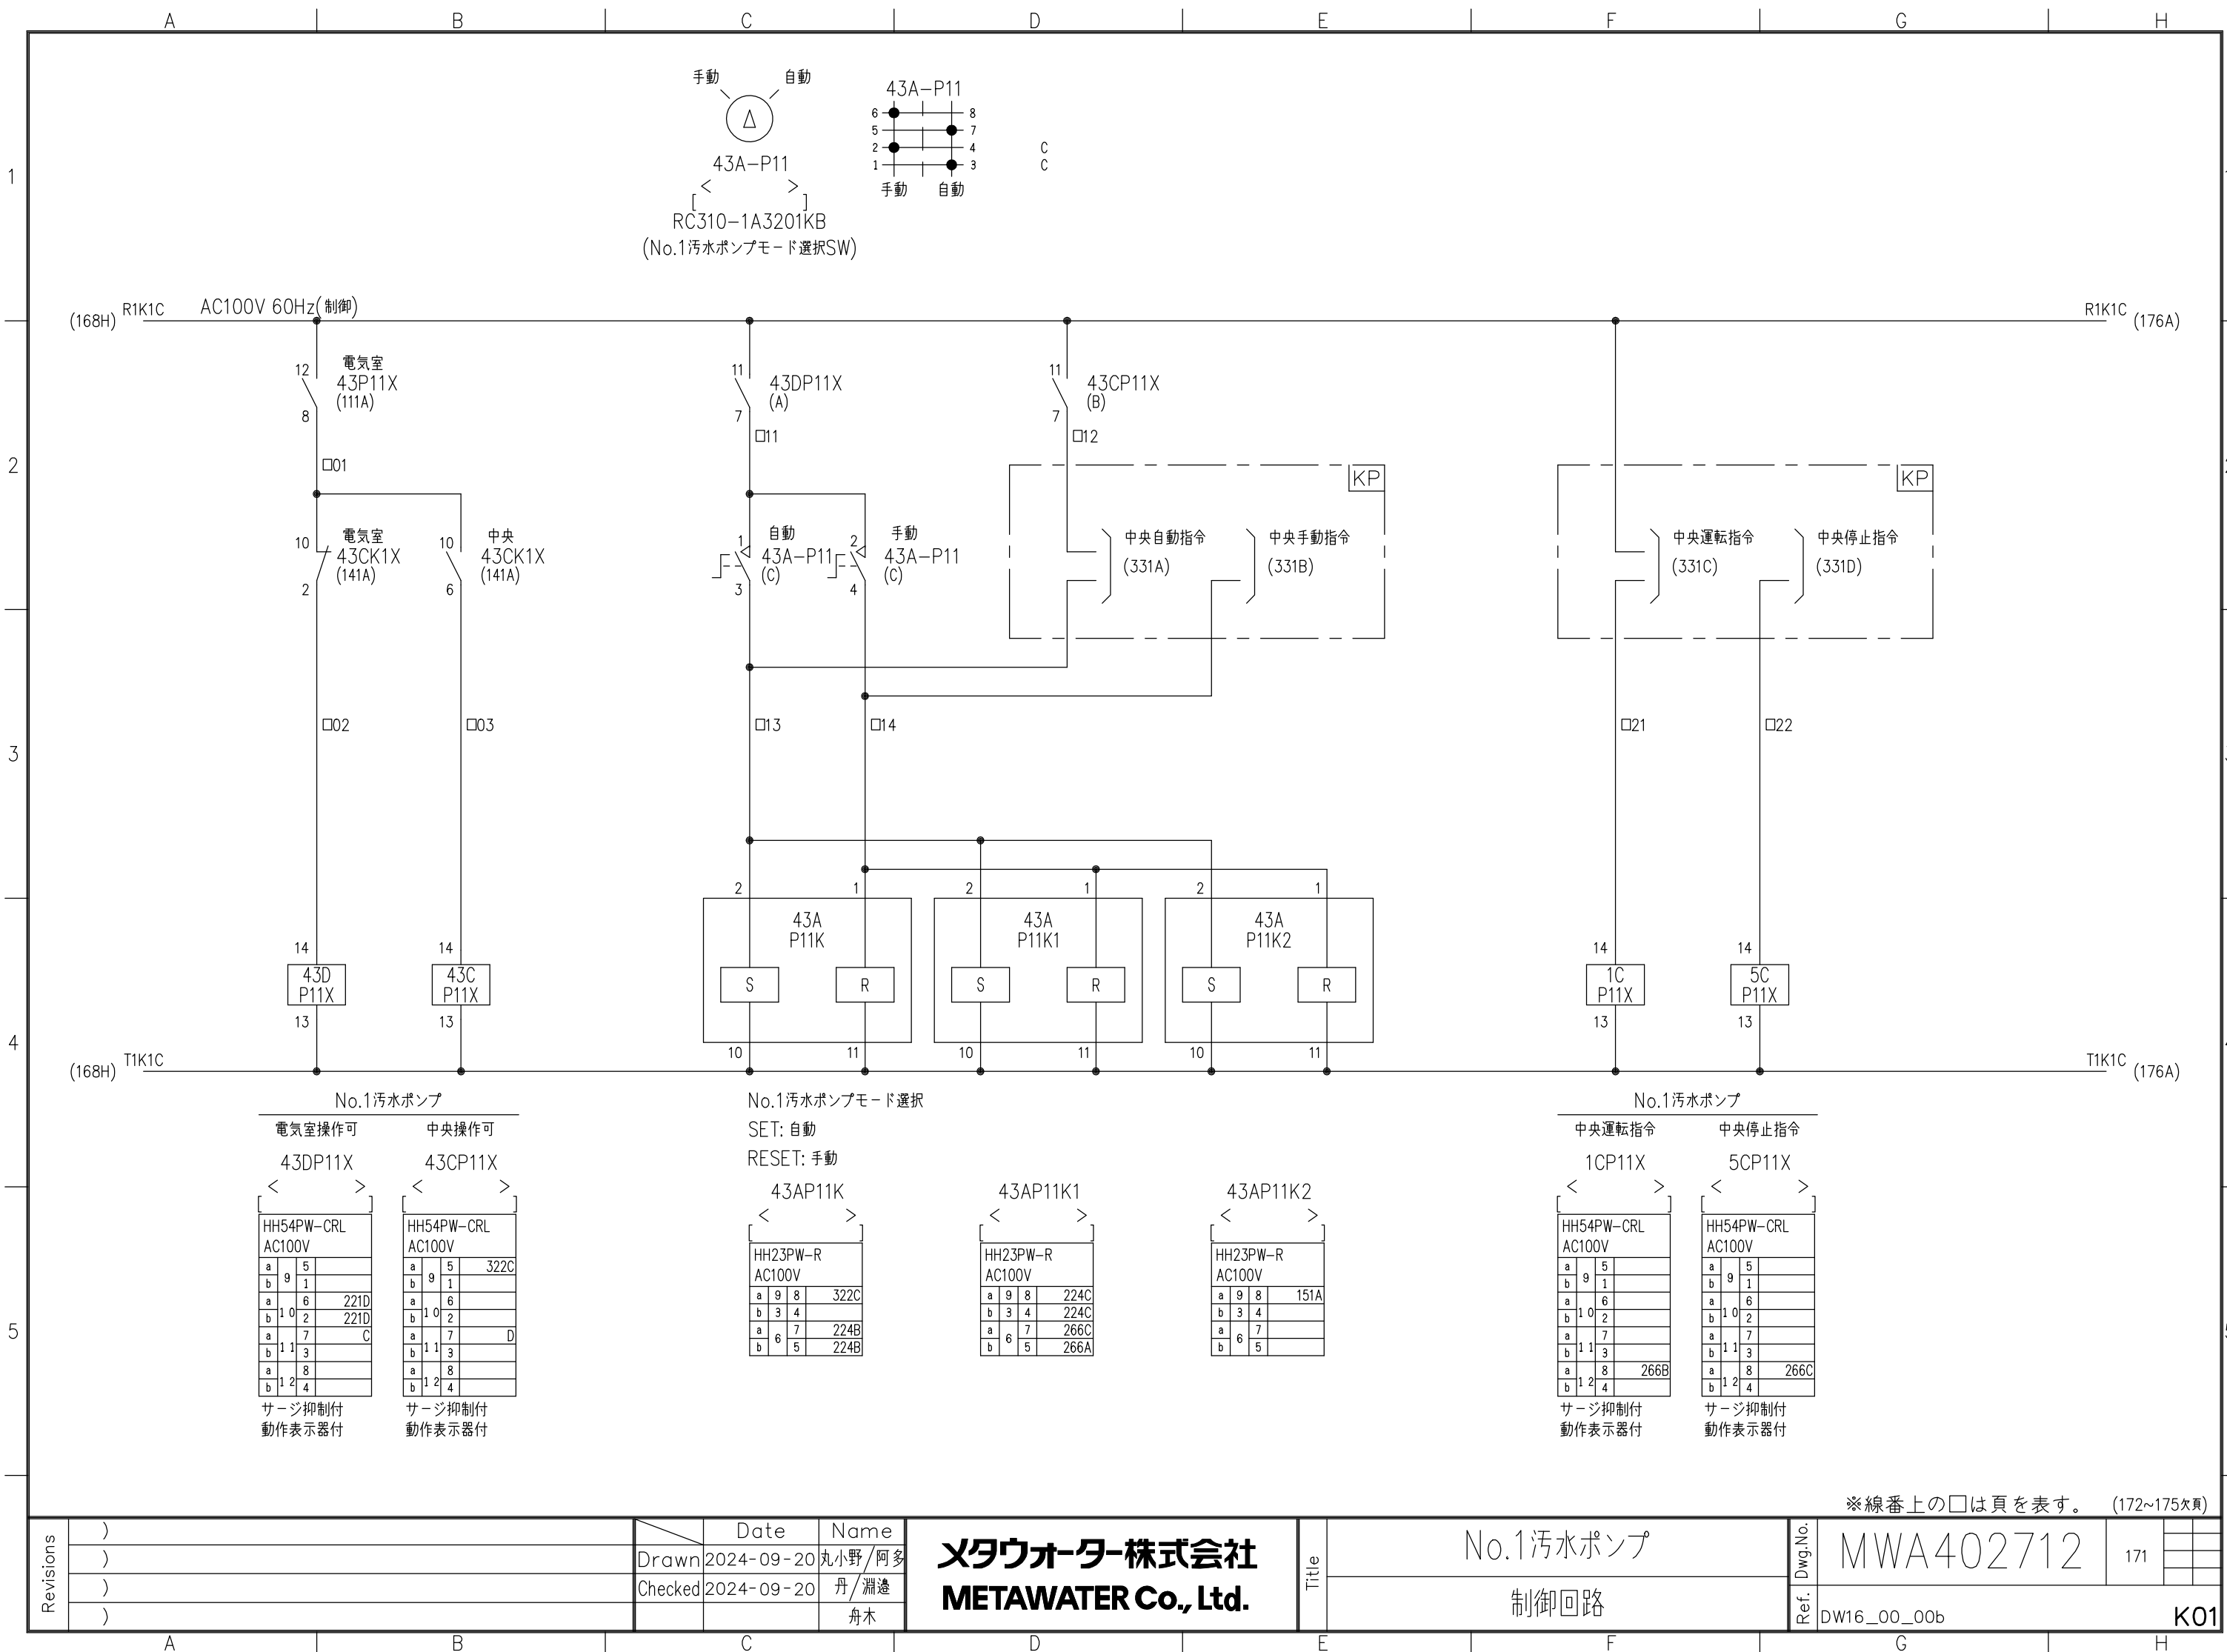

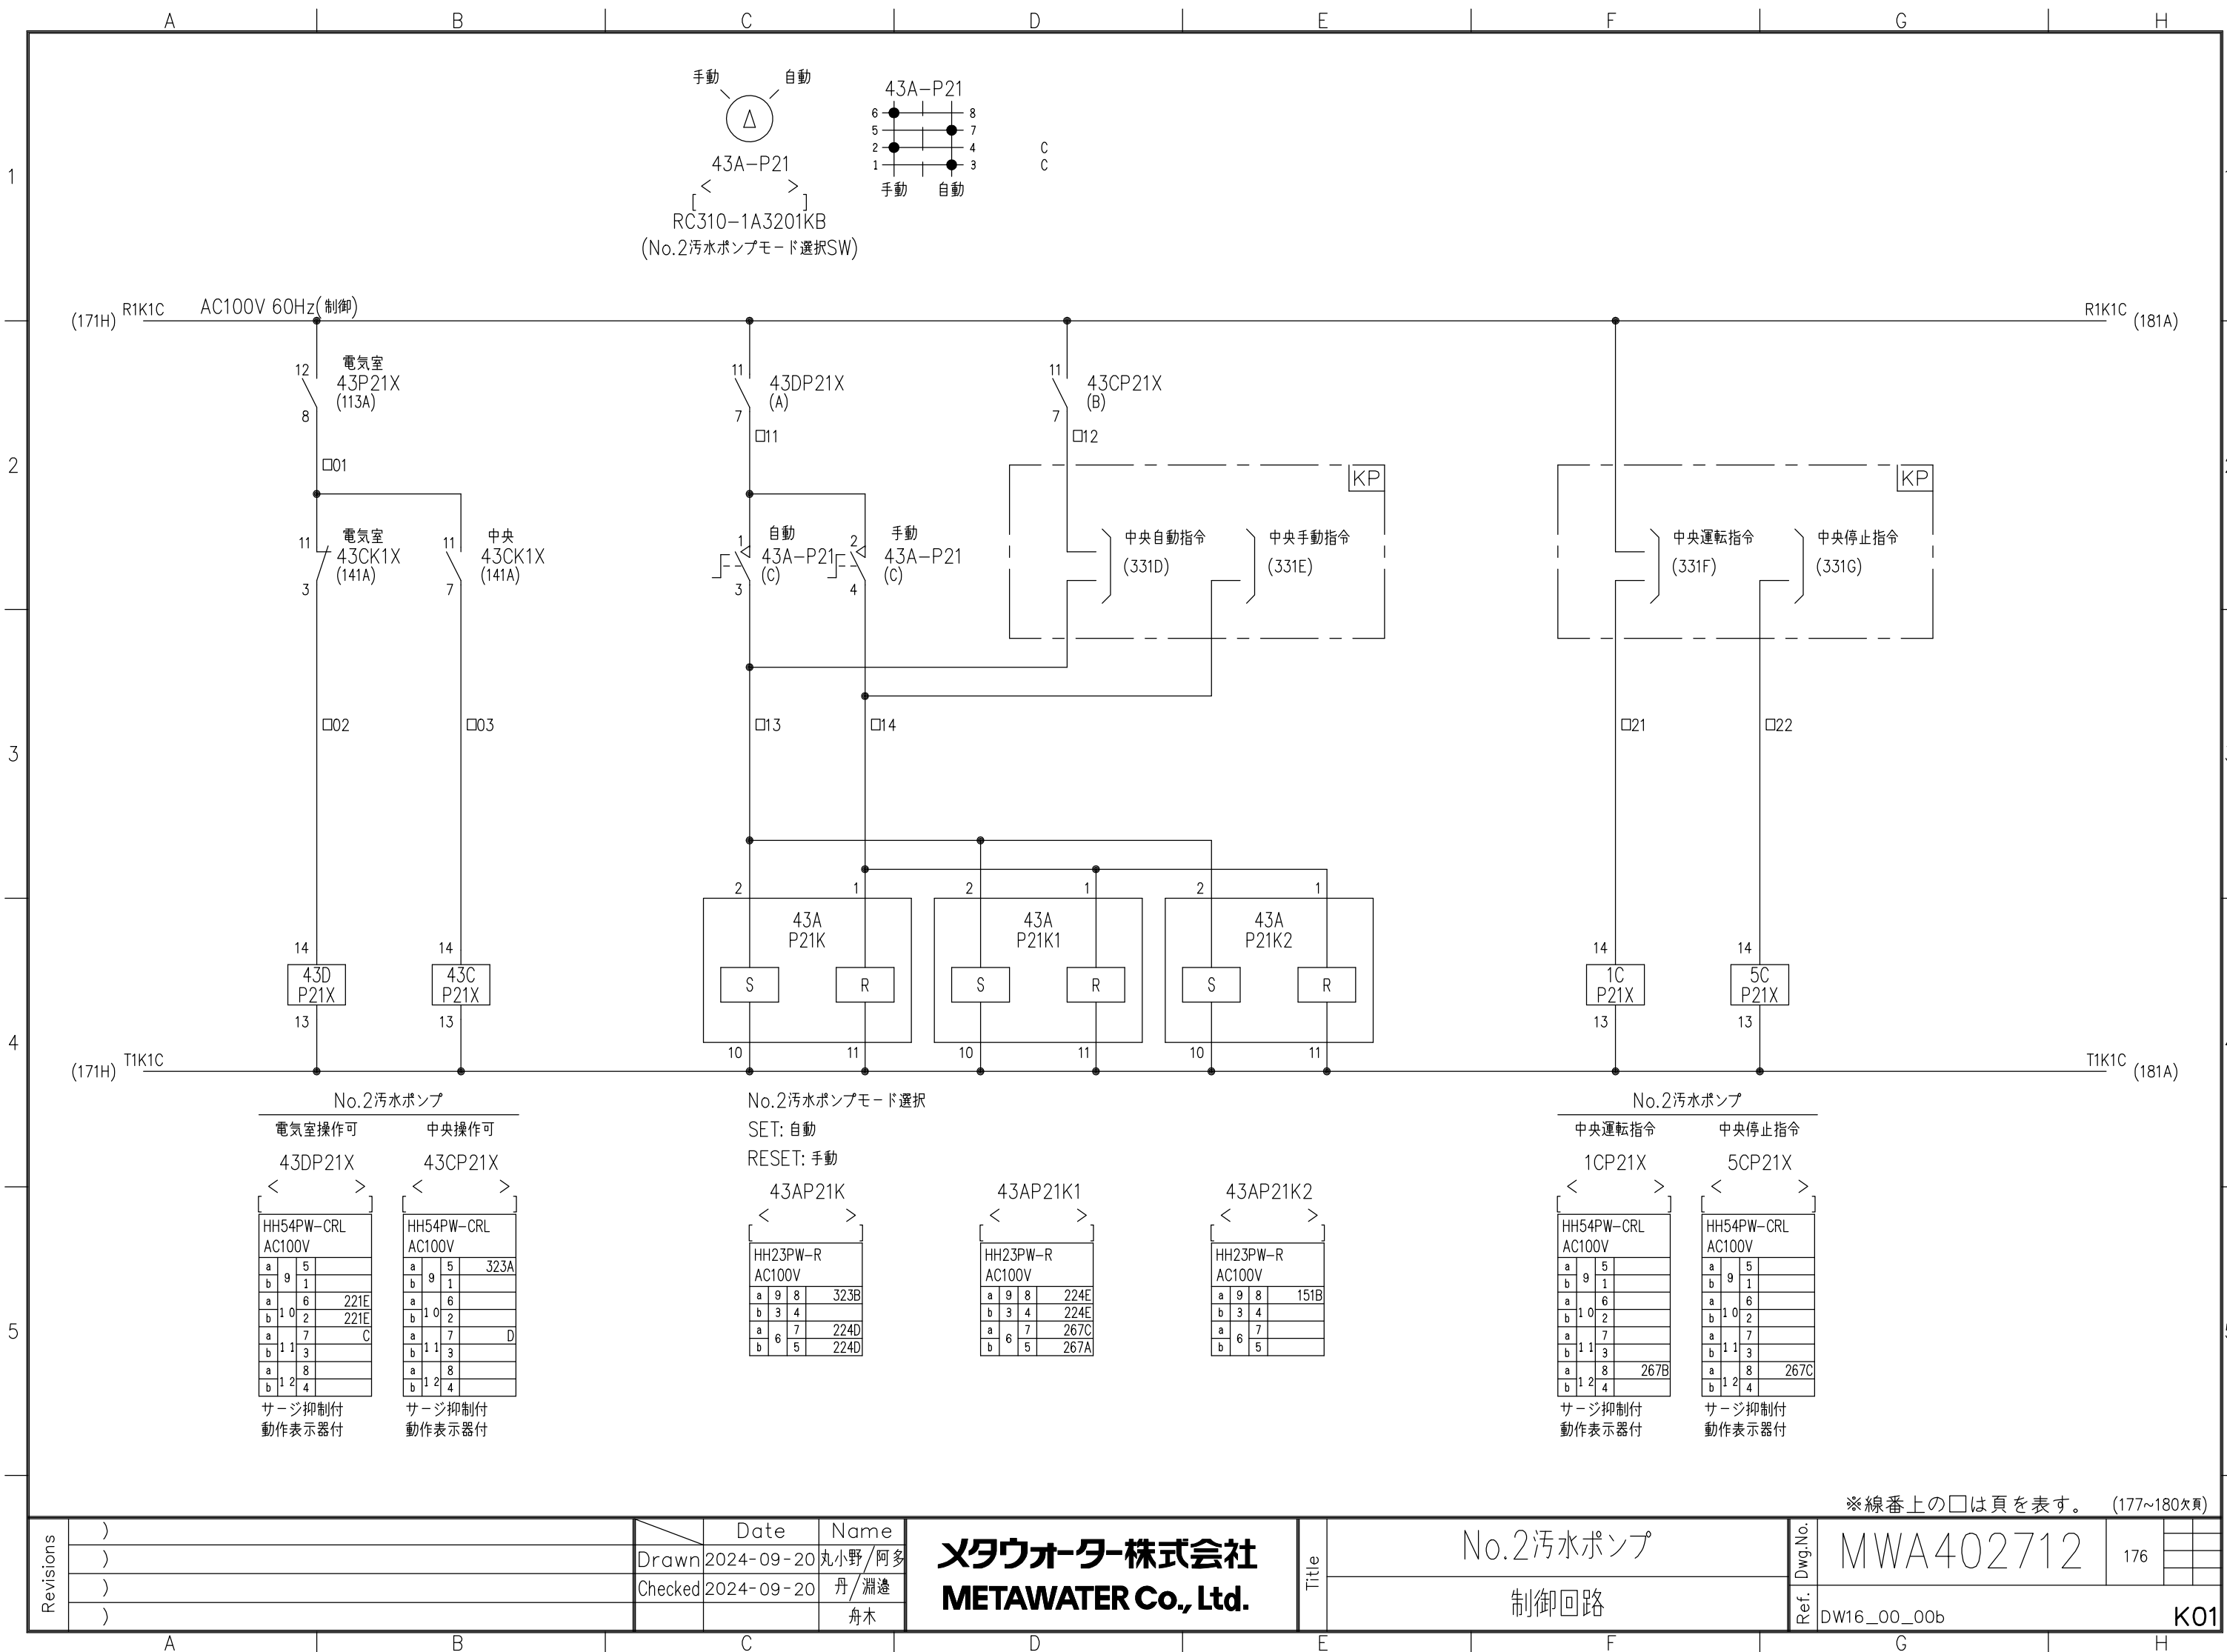



Revisions	)	Date Name
	)	
	)	
	)	


メタウォーター株式会社
METAWATER Co., Ltd.


Title	No.2汚水ポンプ	Dwg.No.	MWA402712	176		
	制御回路	Ref.	DW16_00_00b			K01


K01

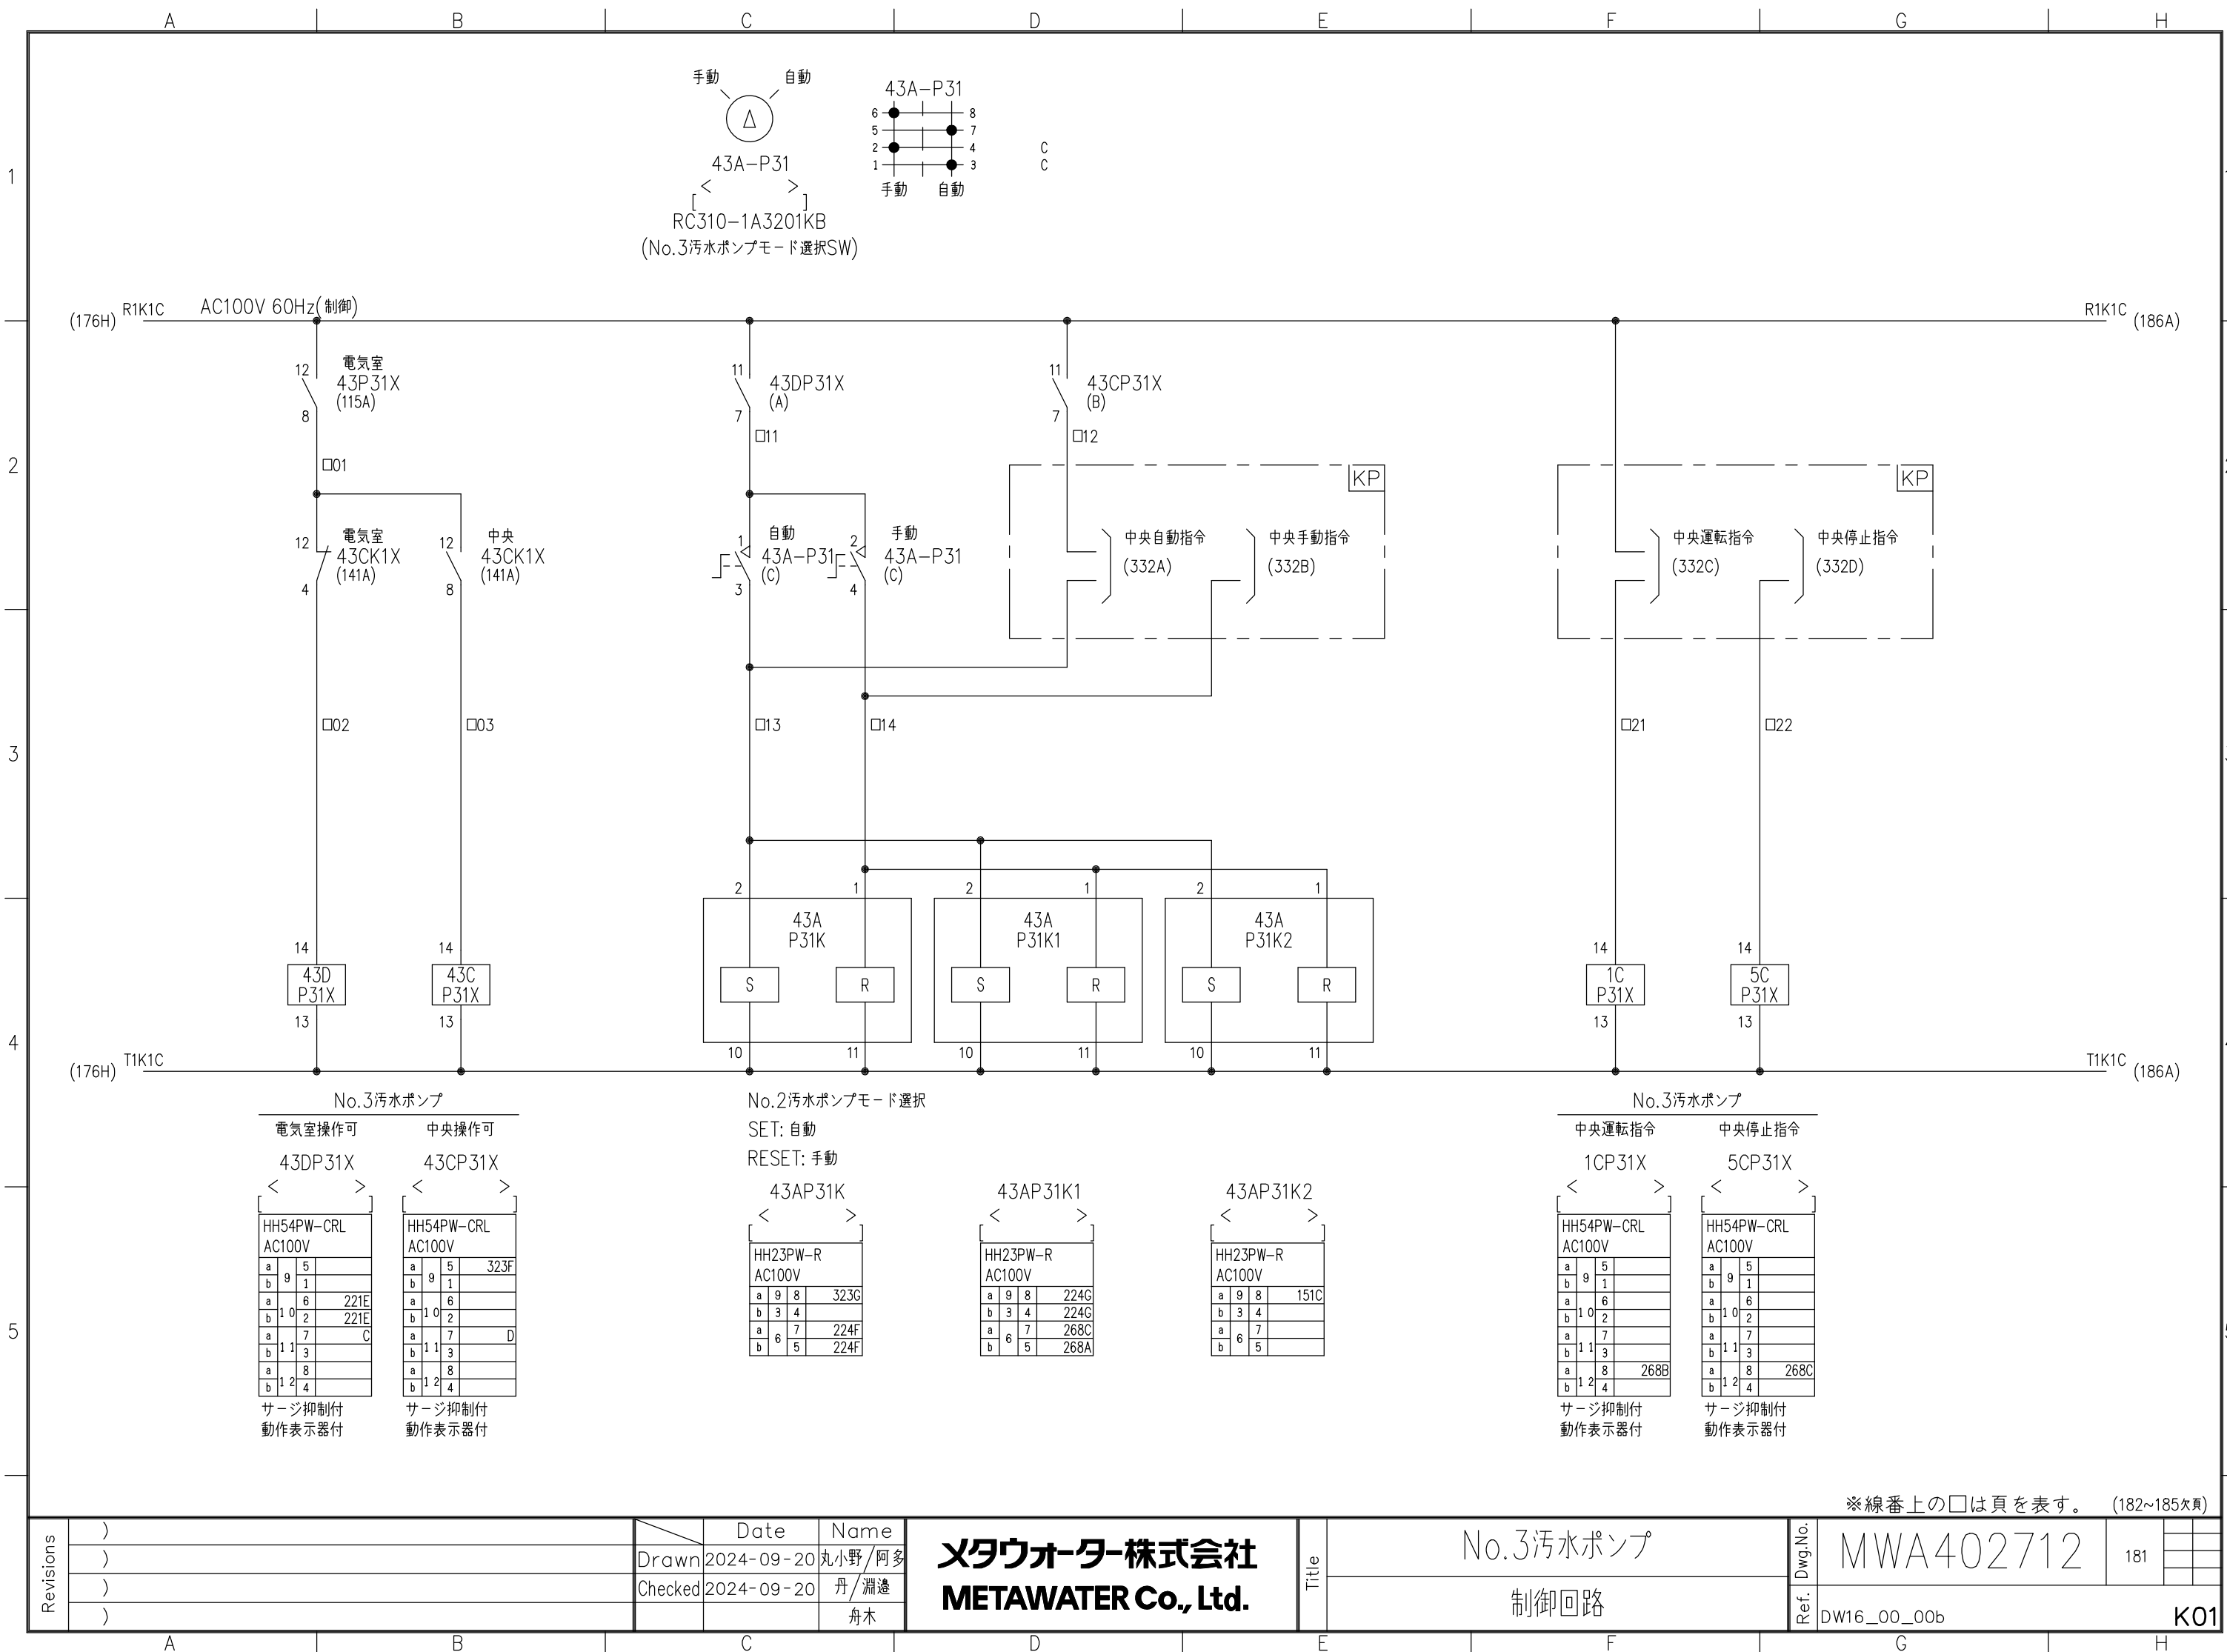


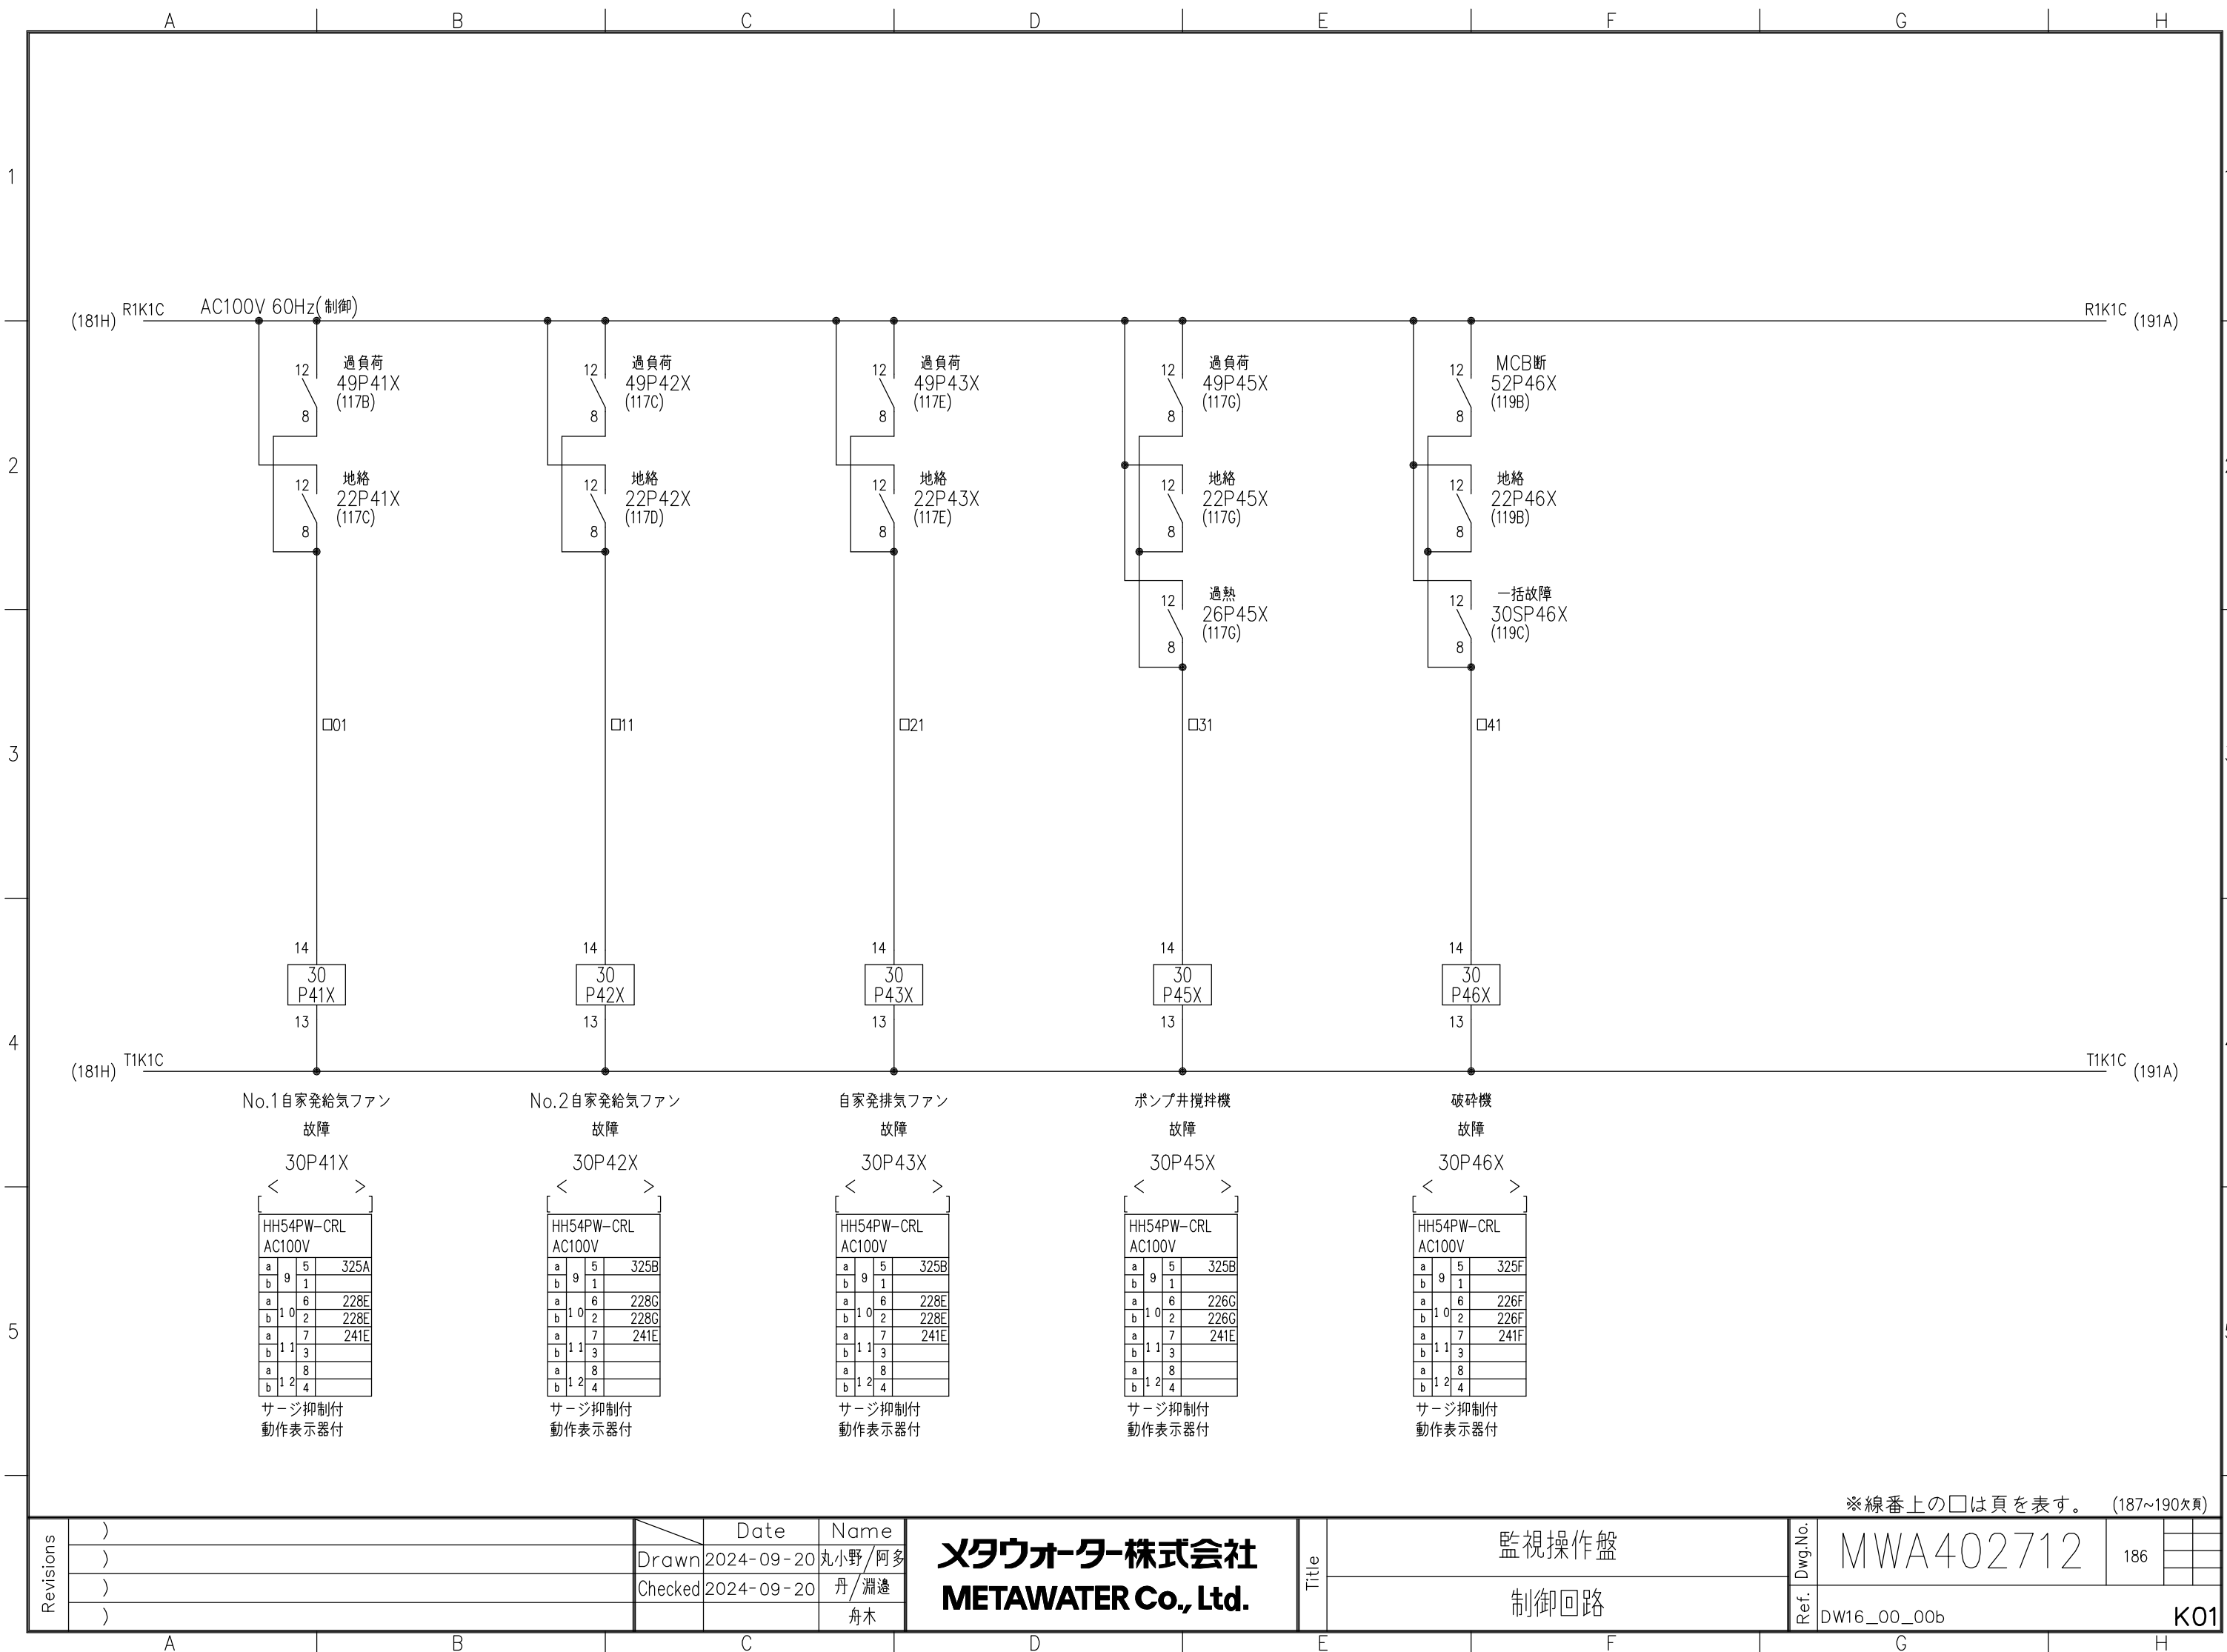


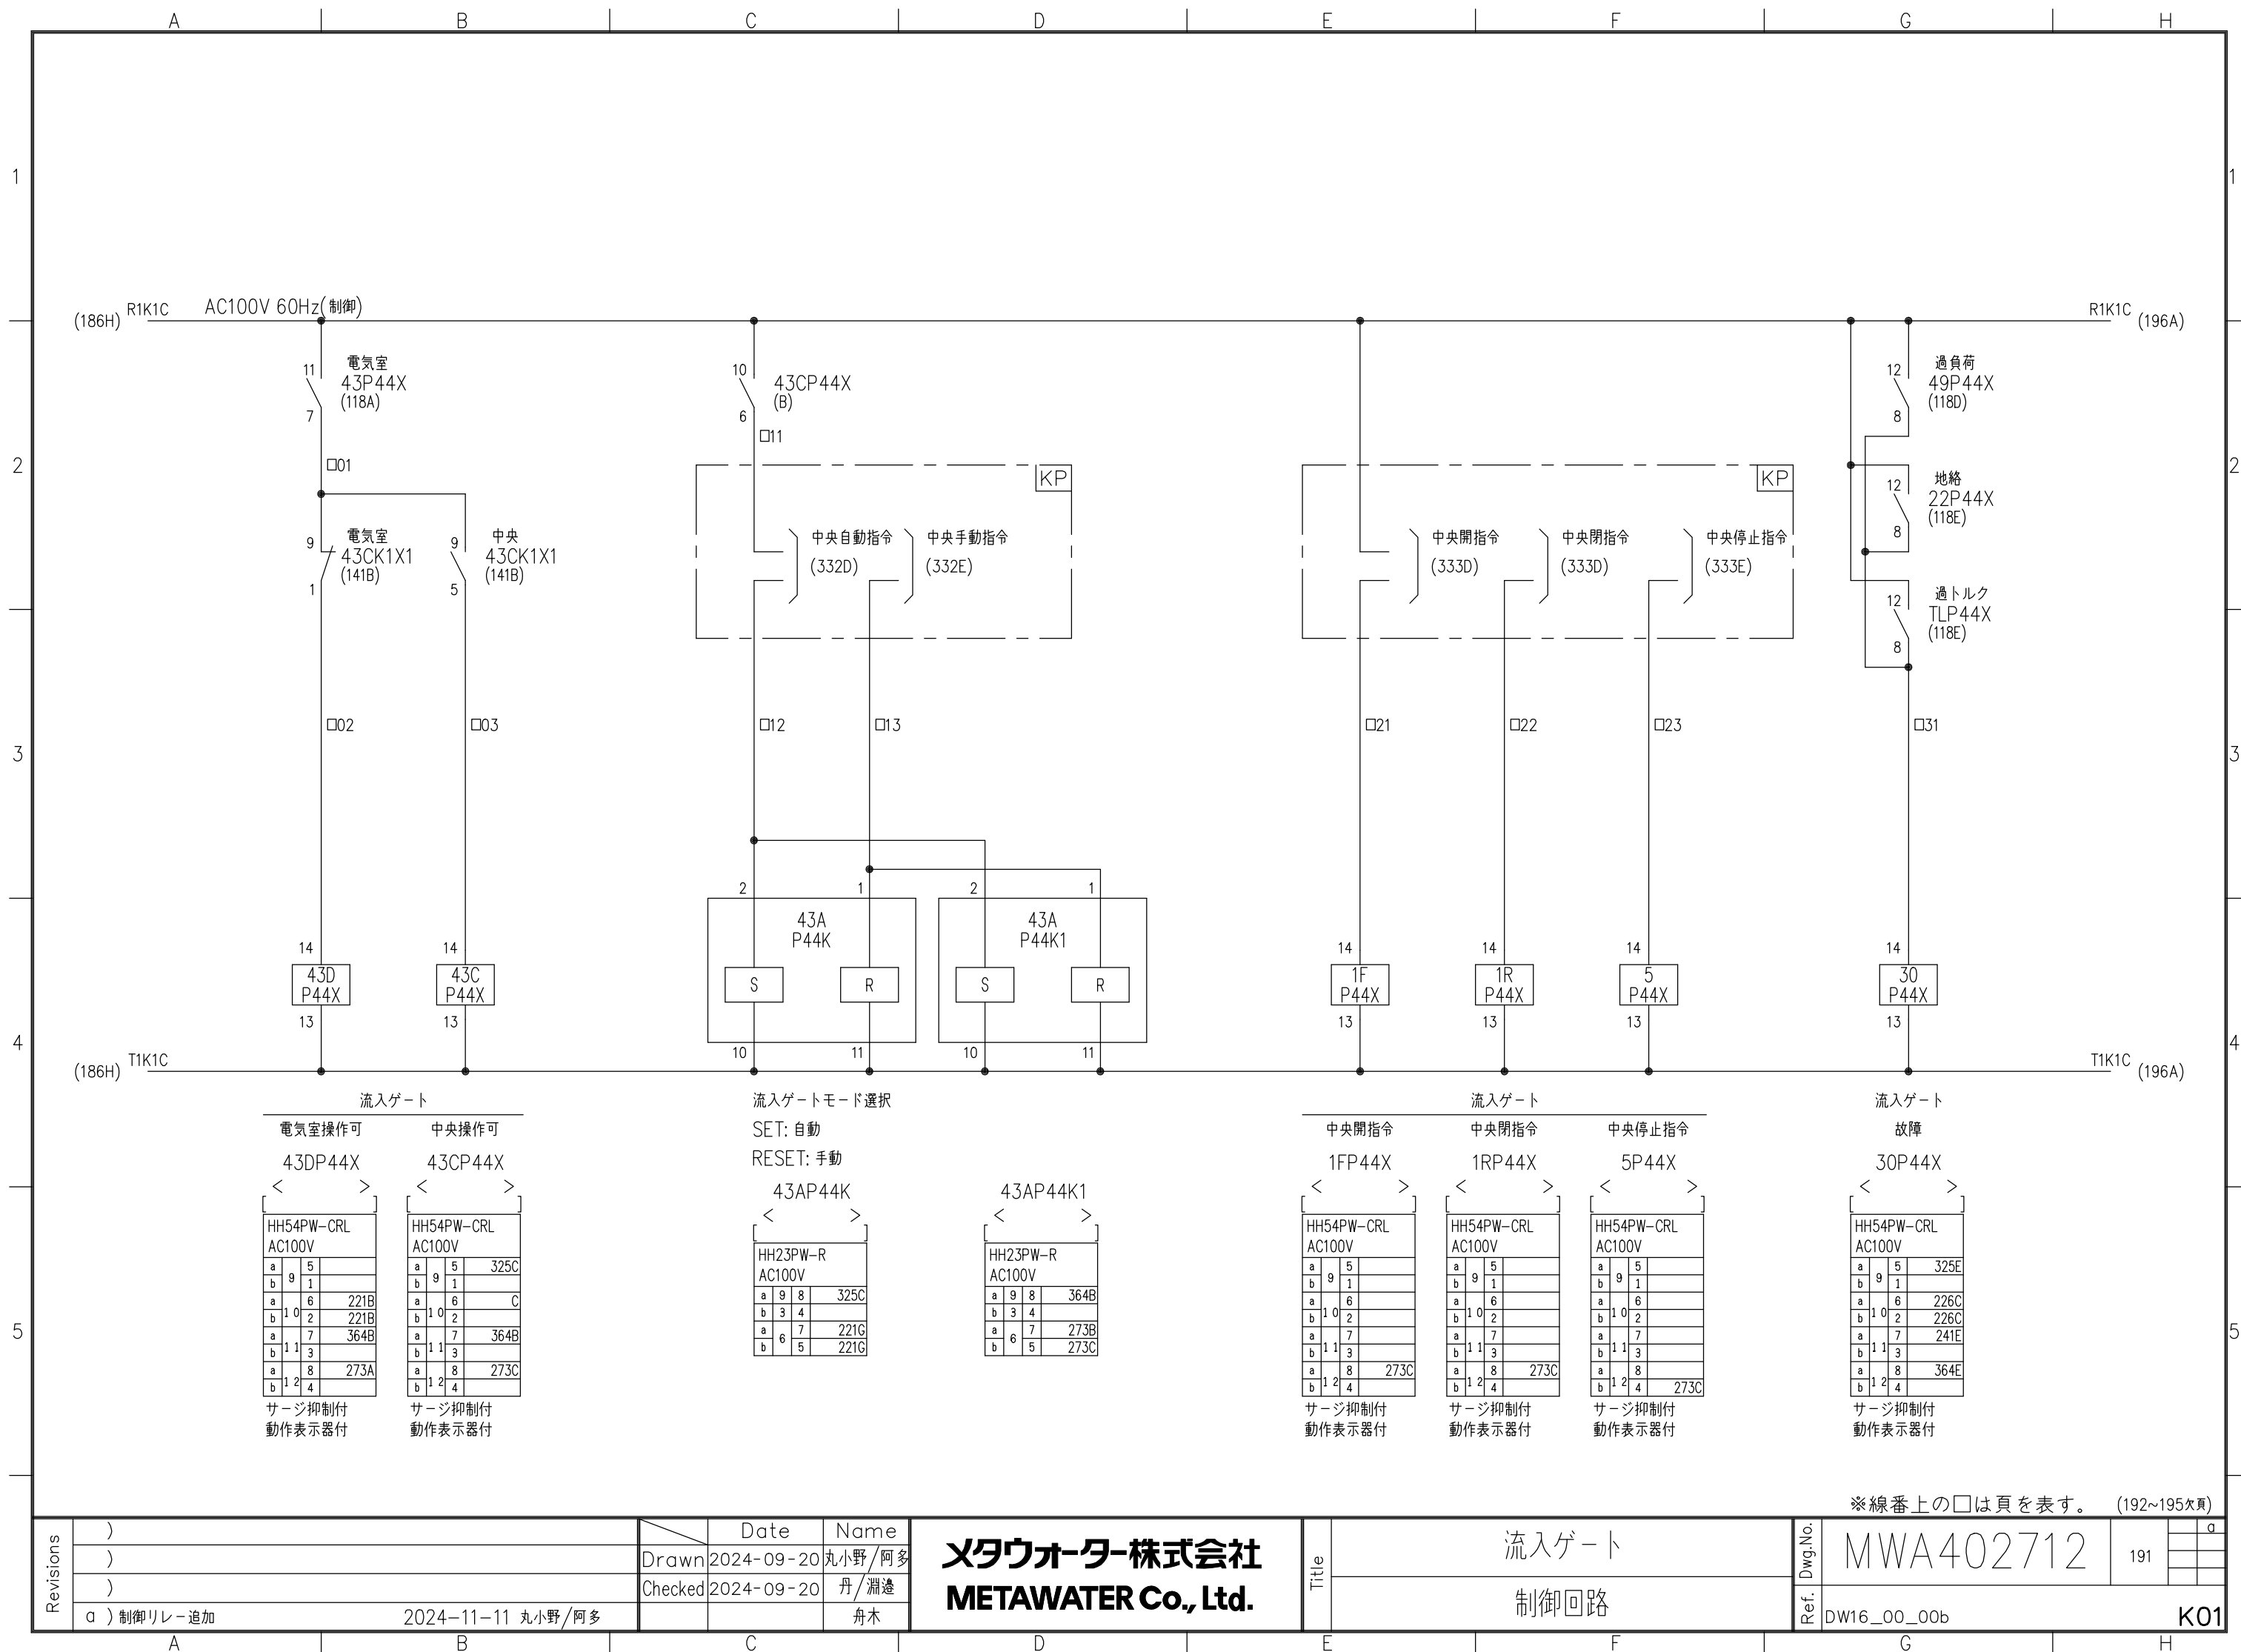


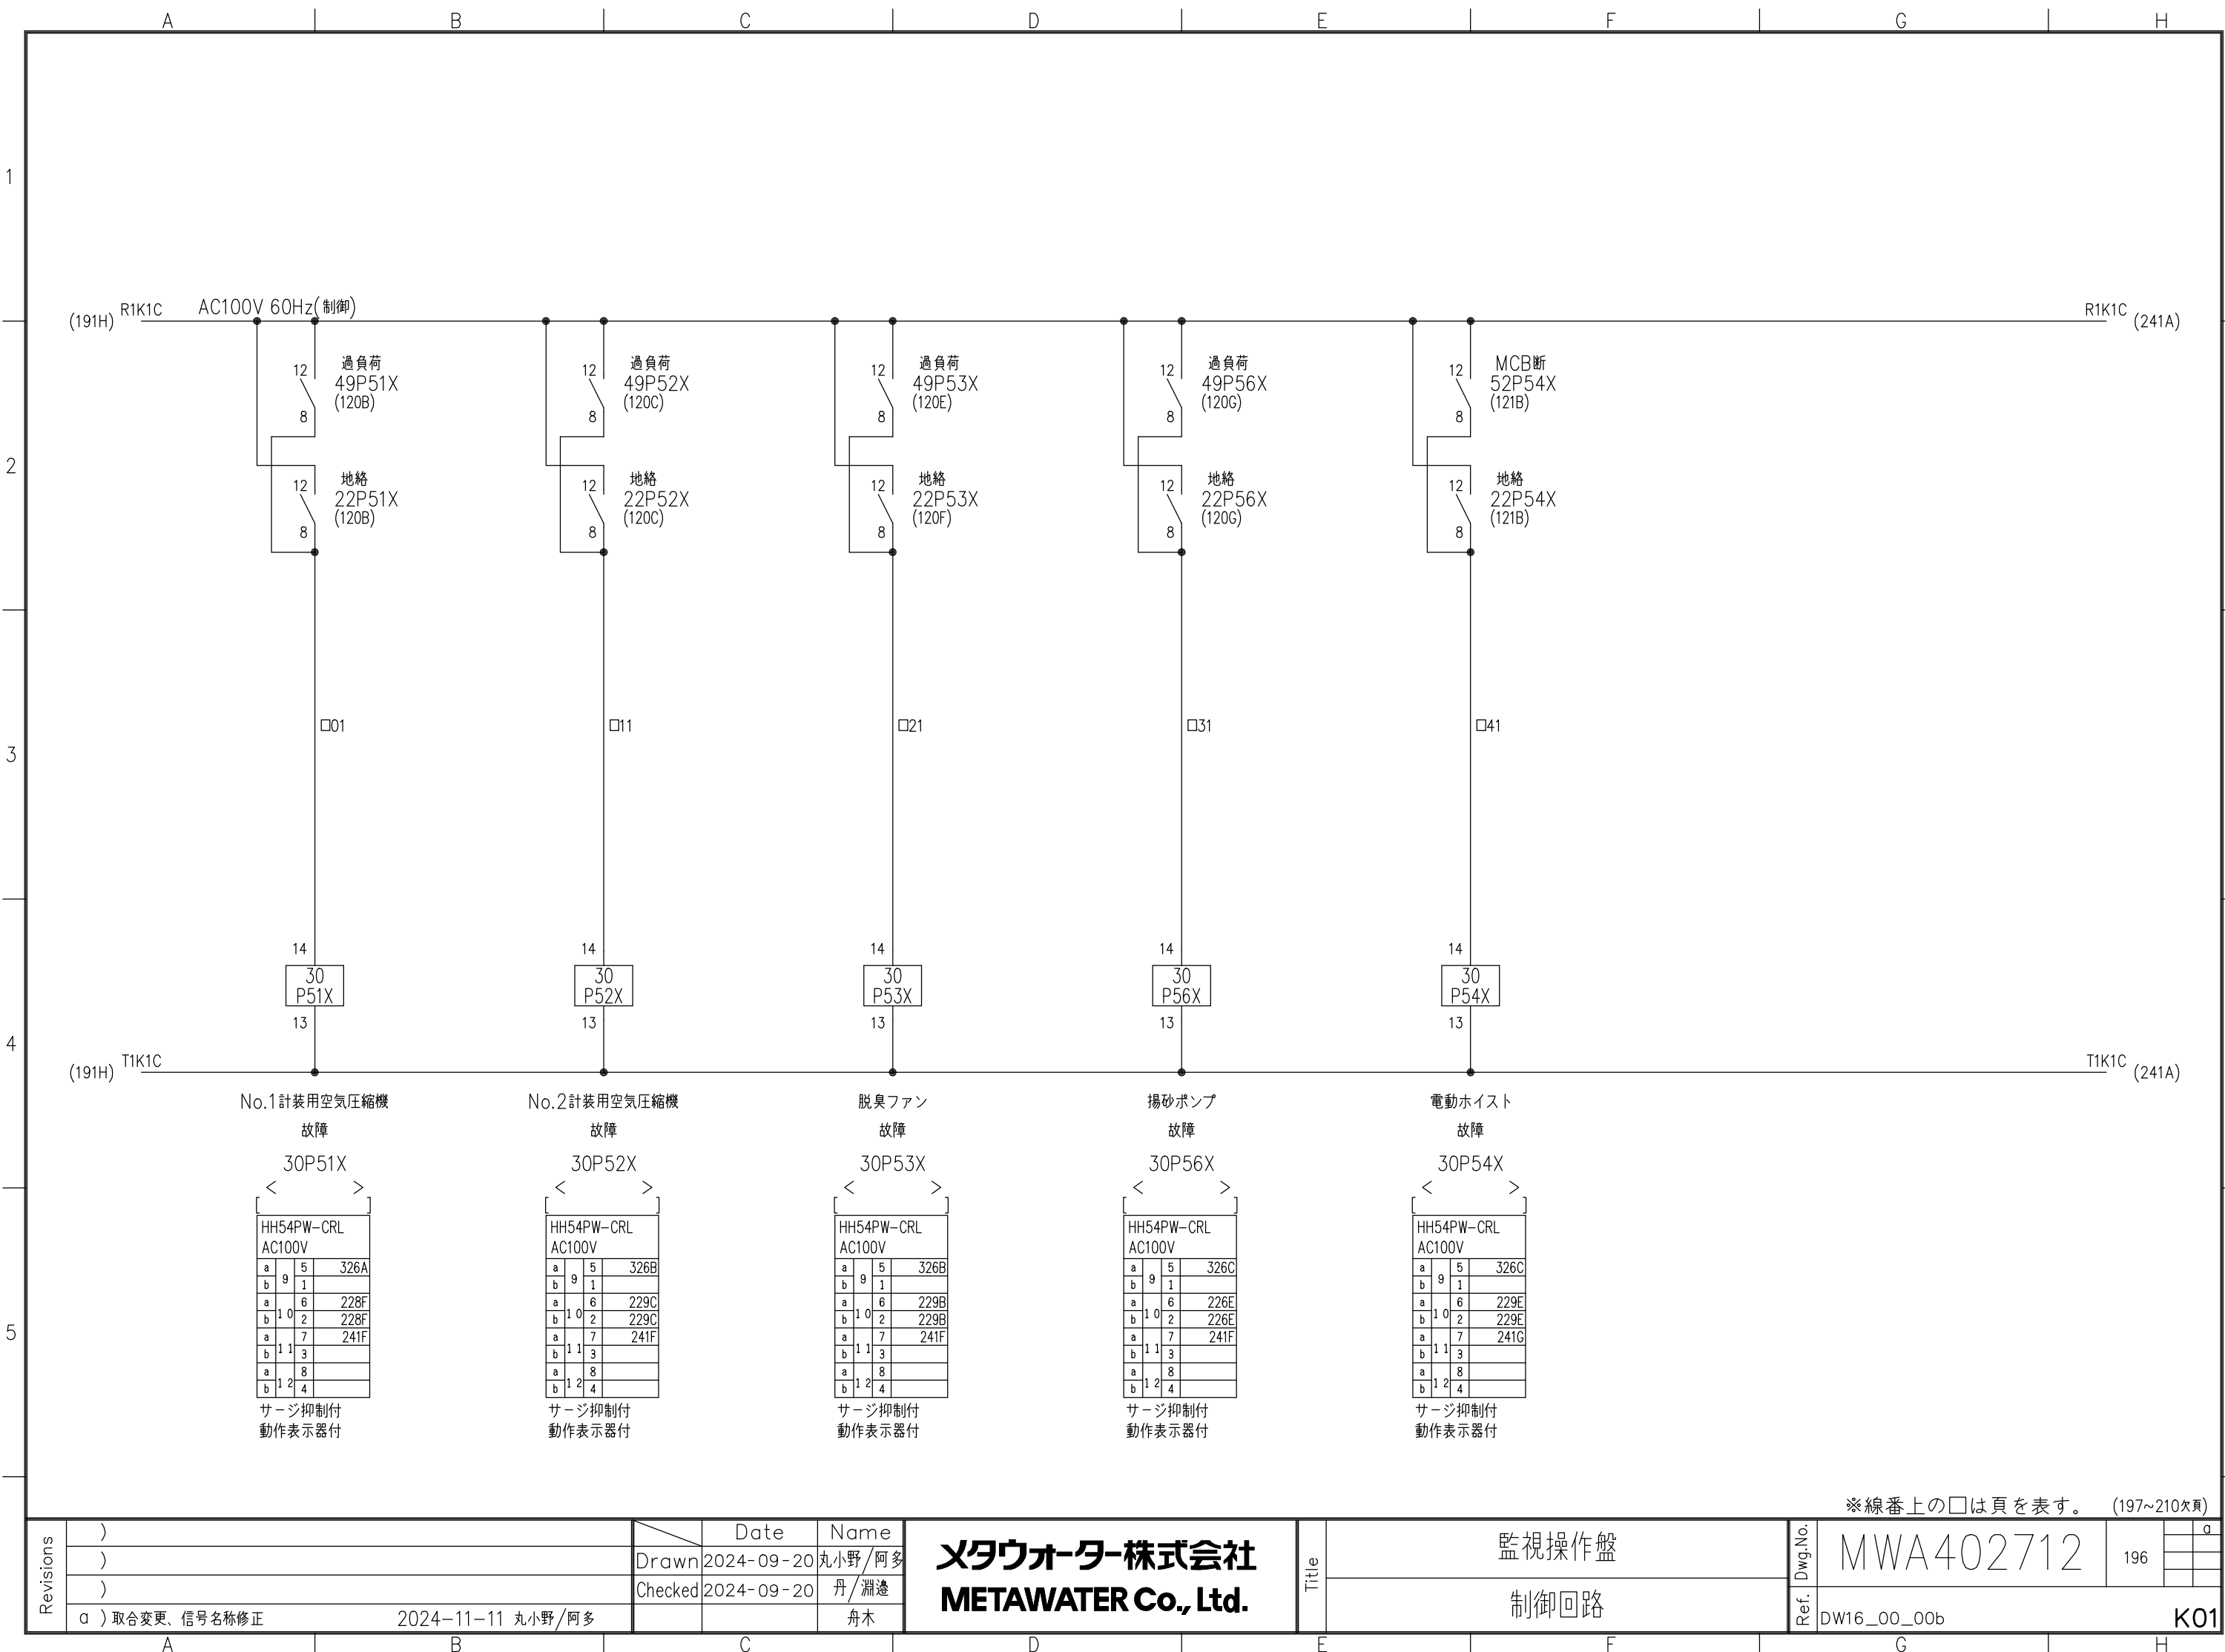

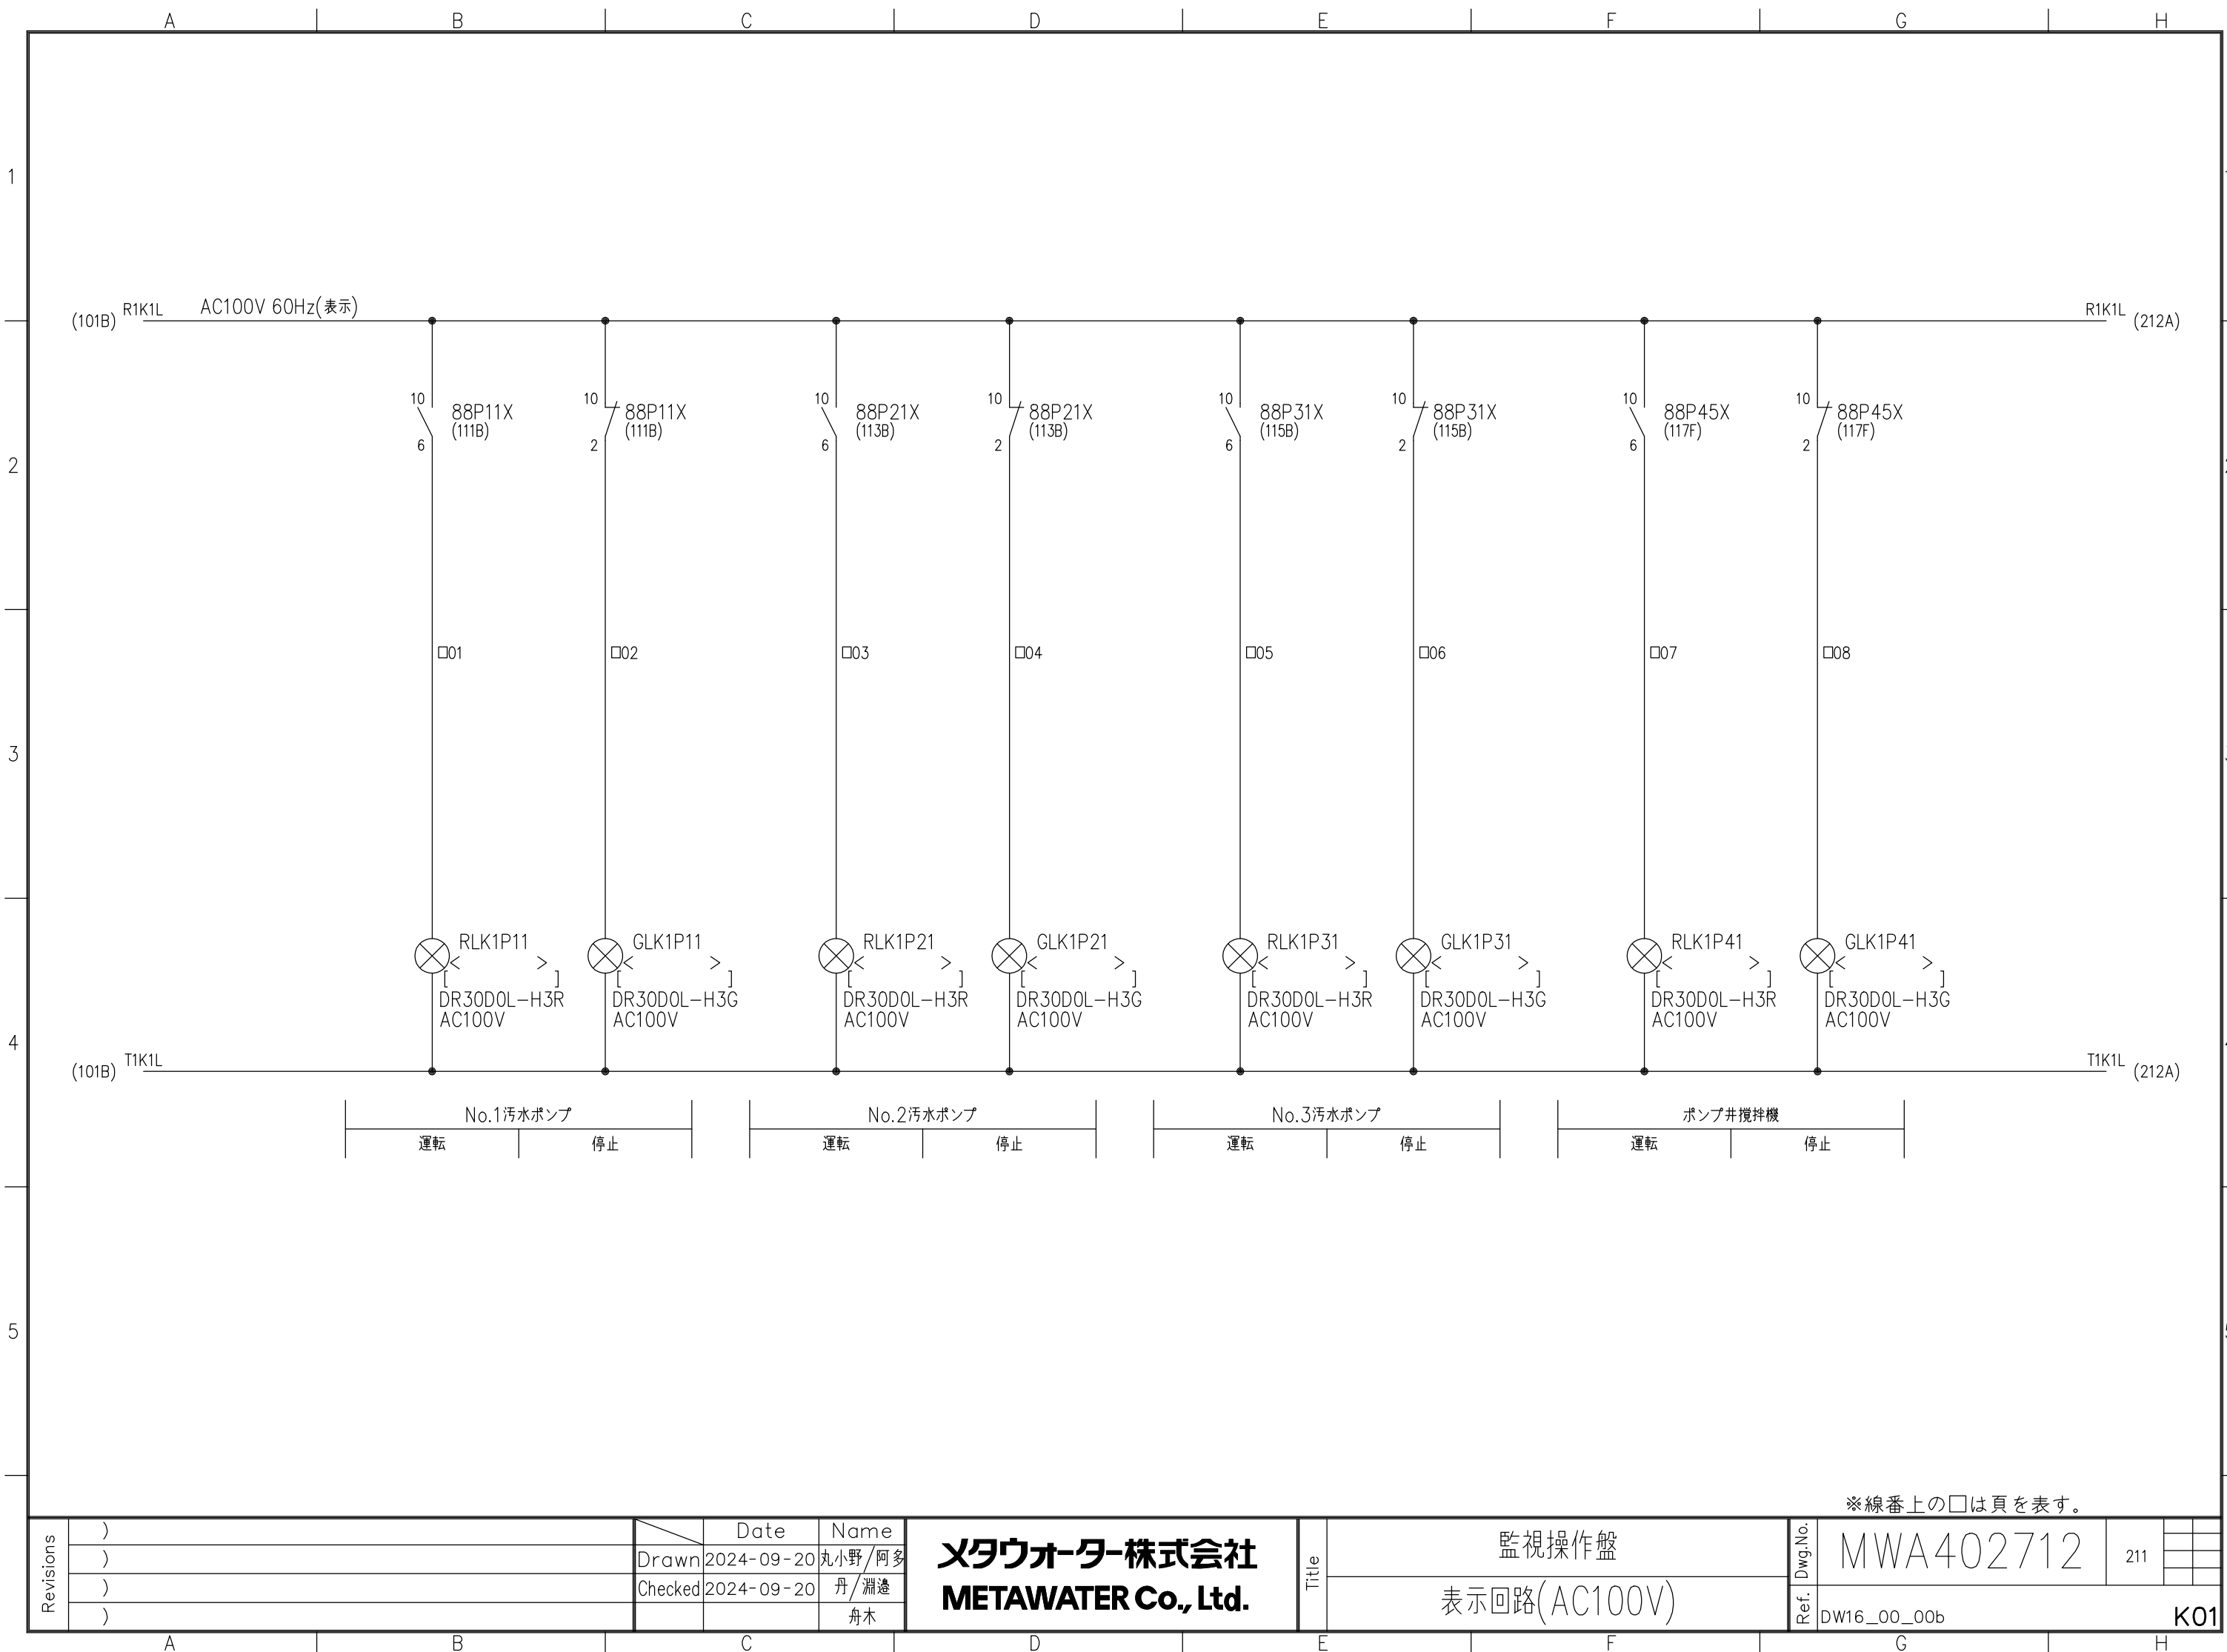

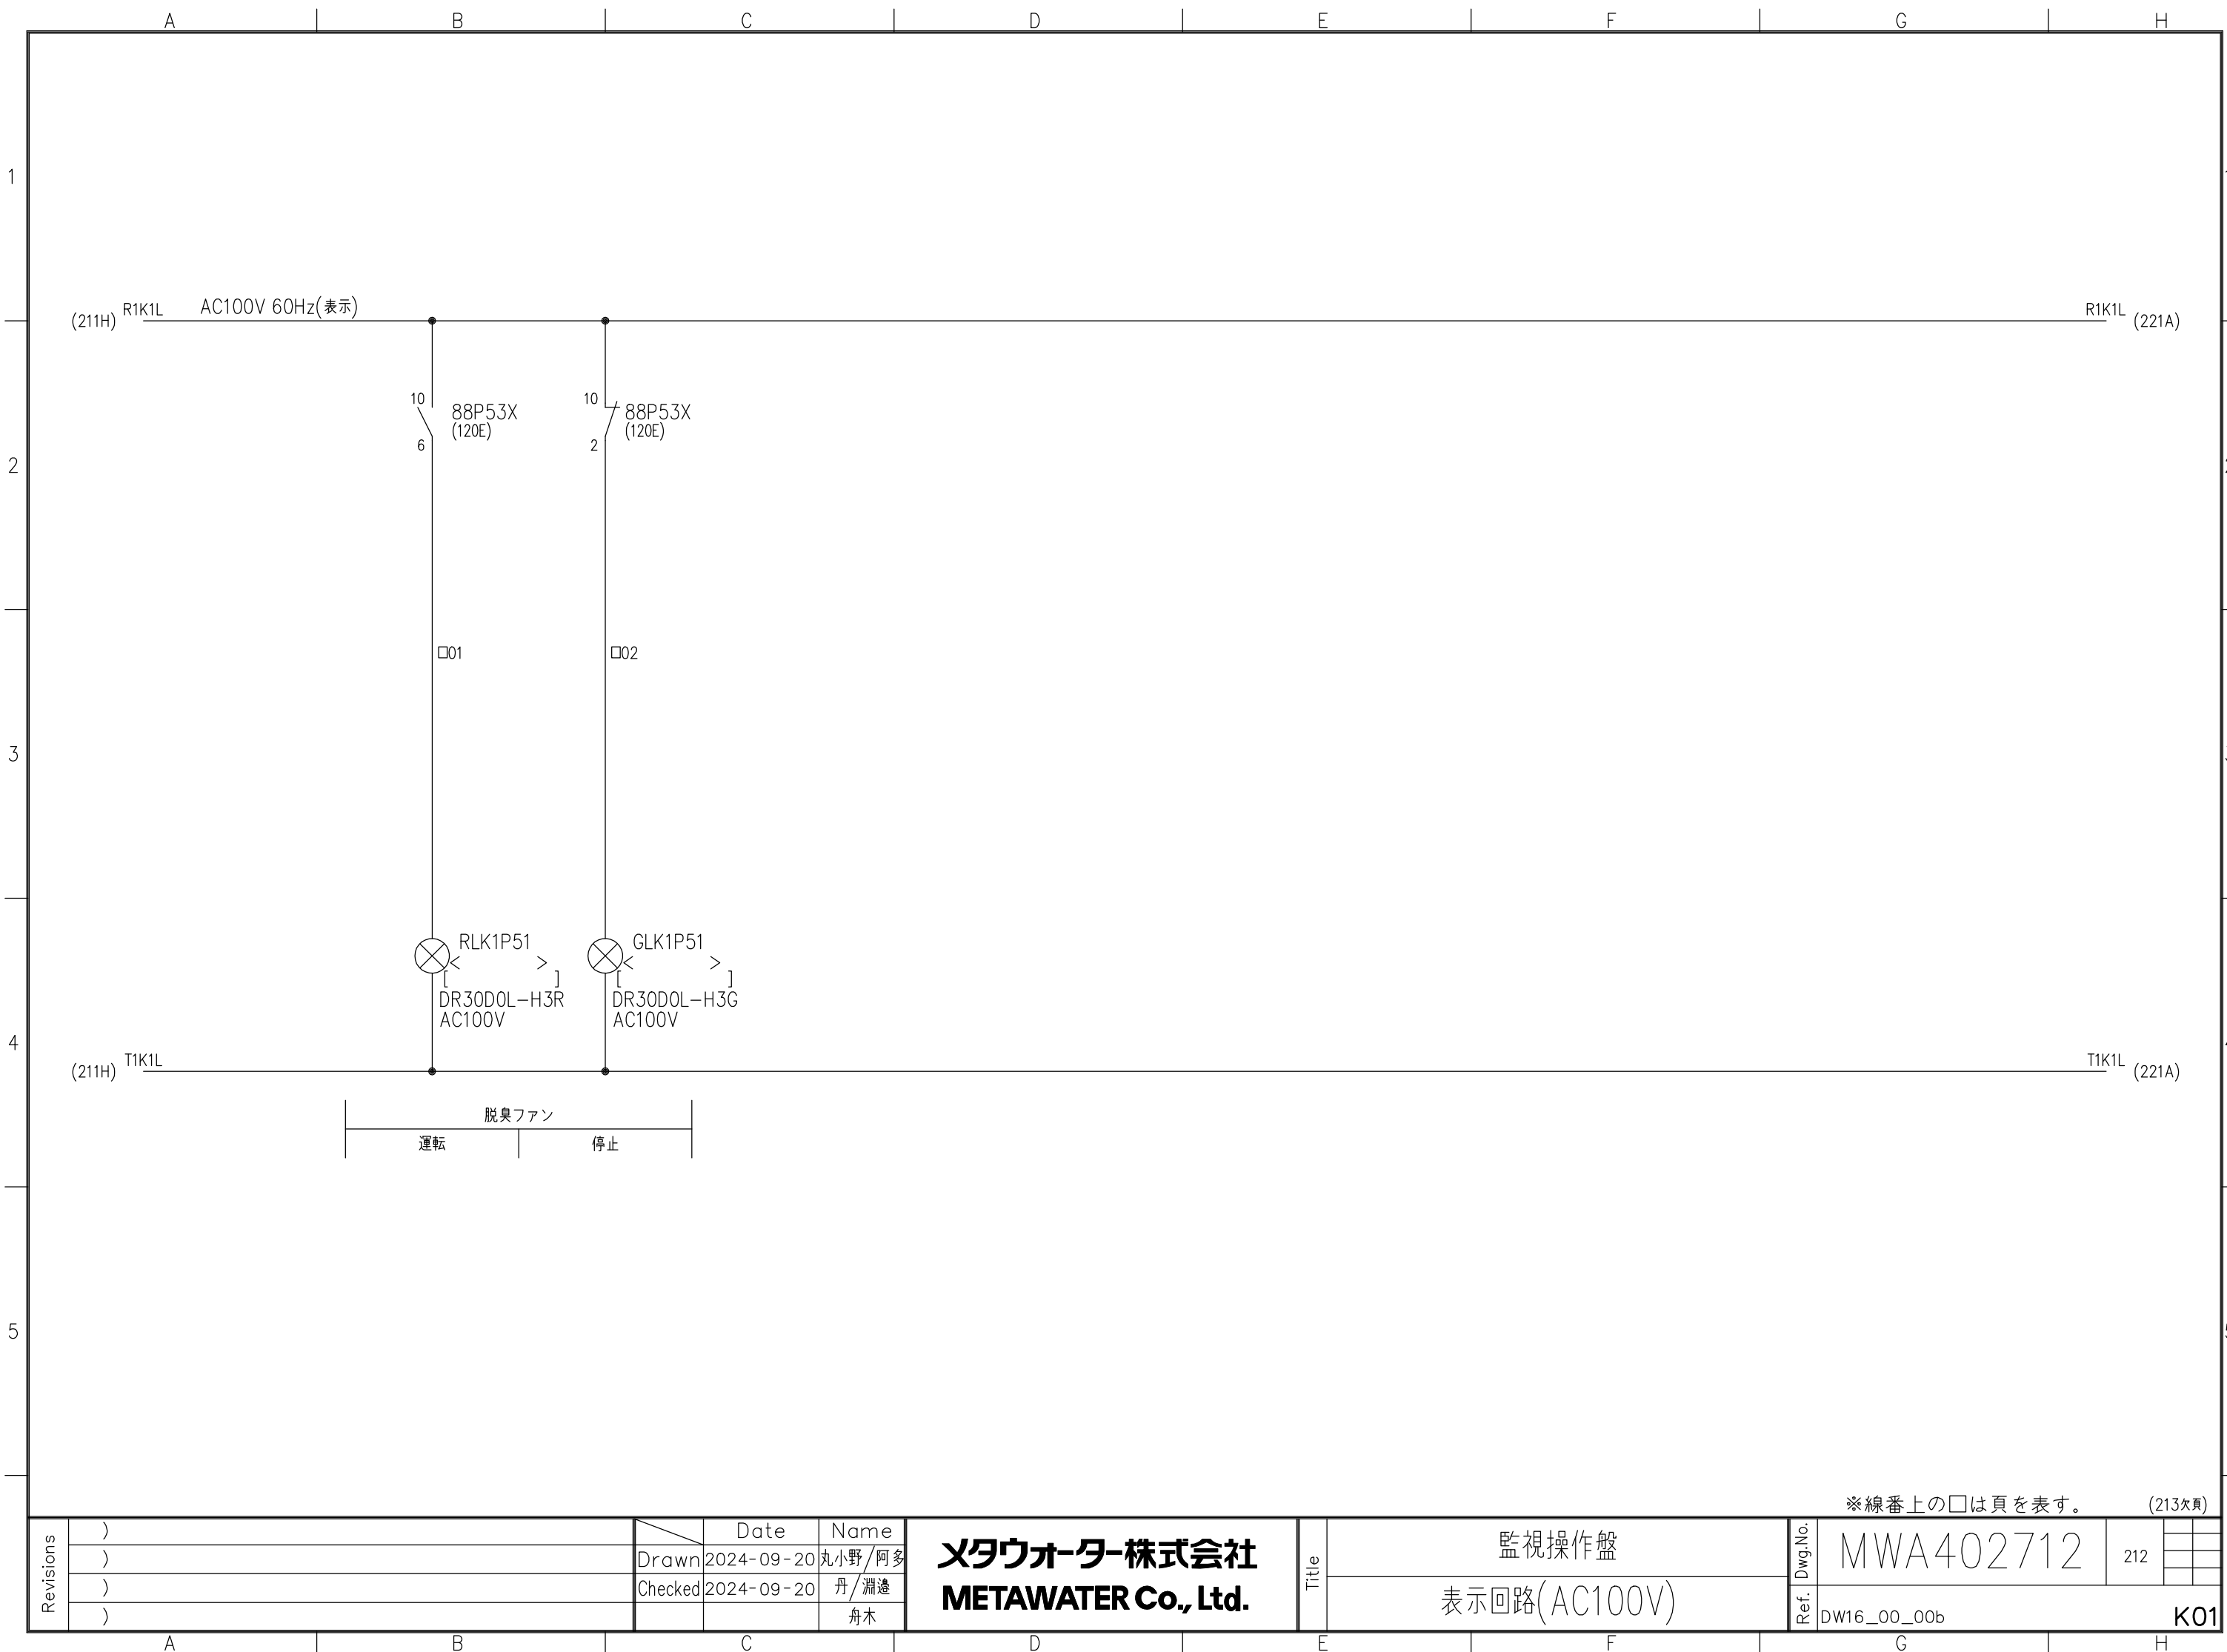


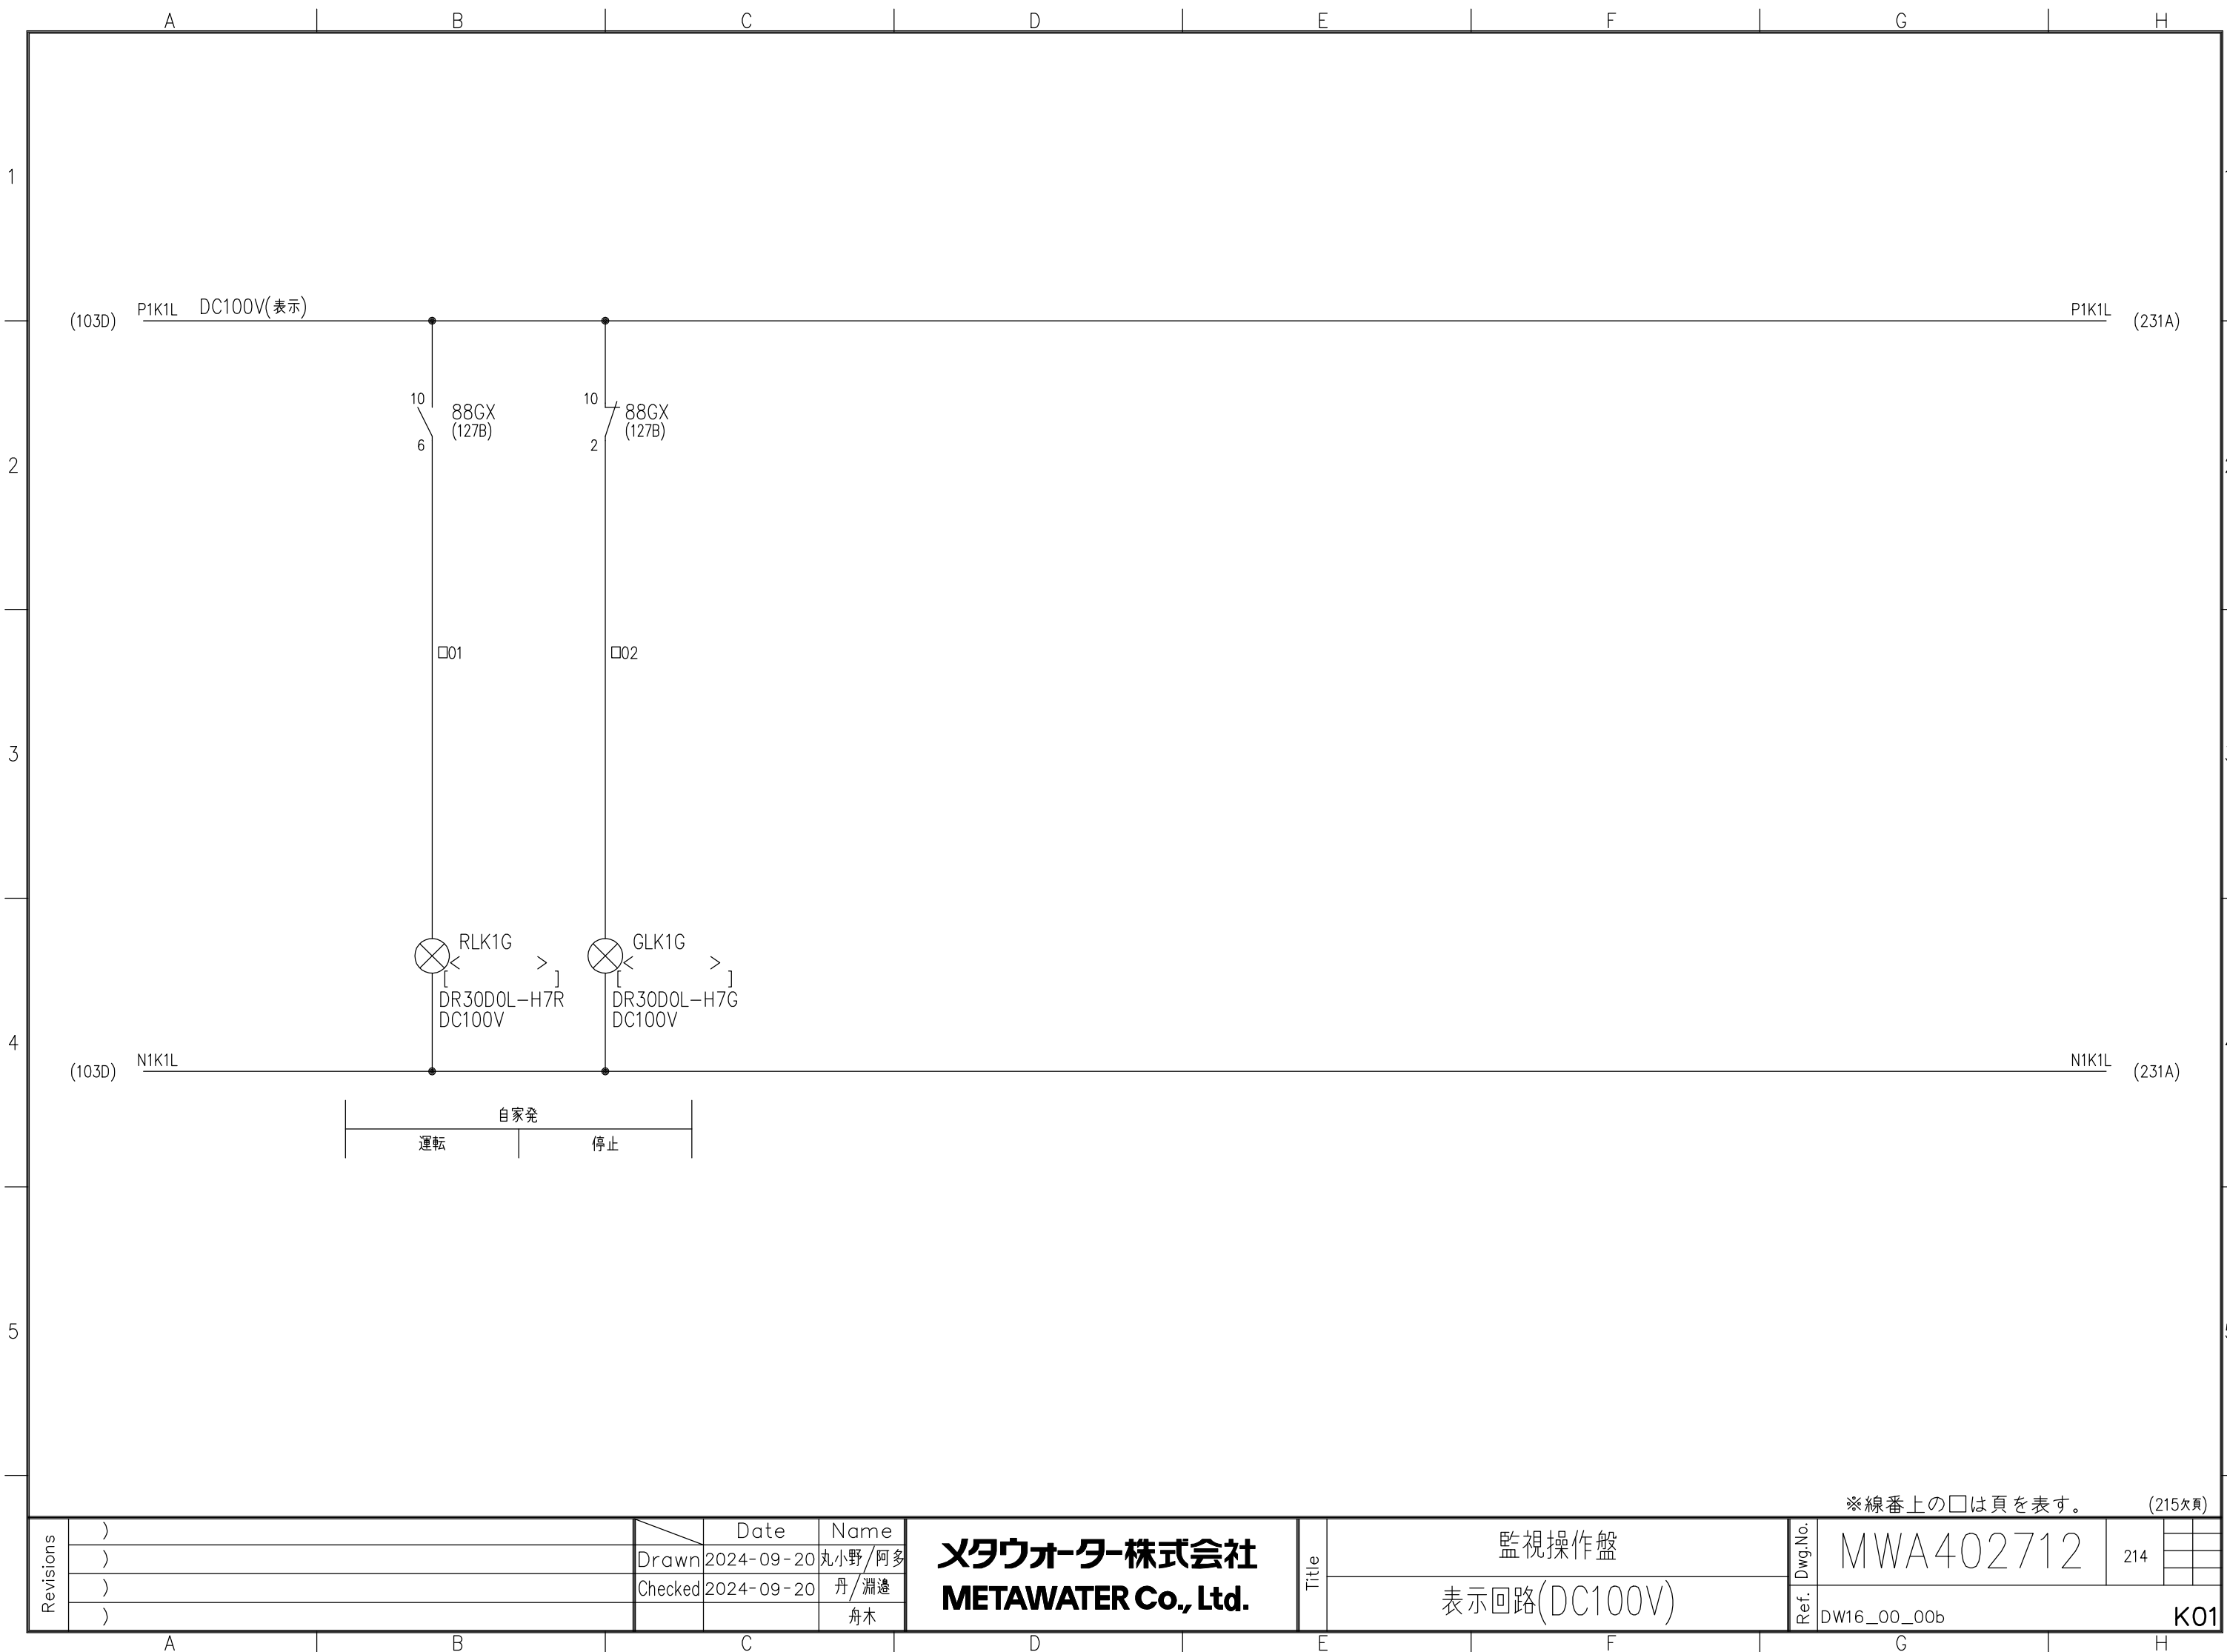


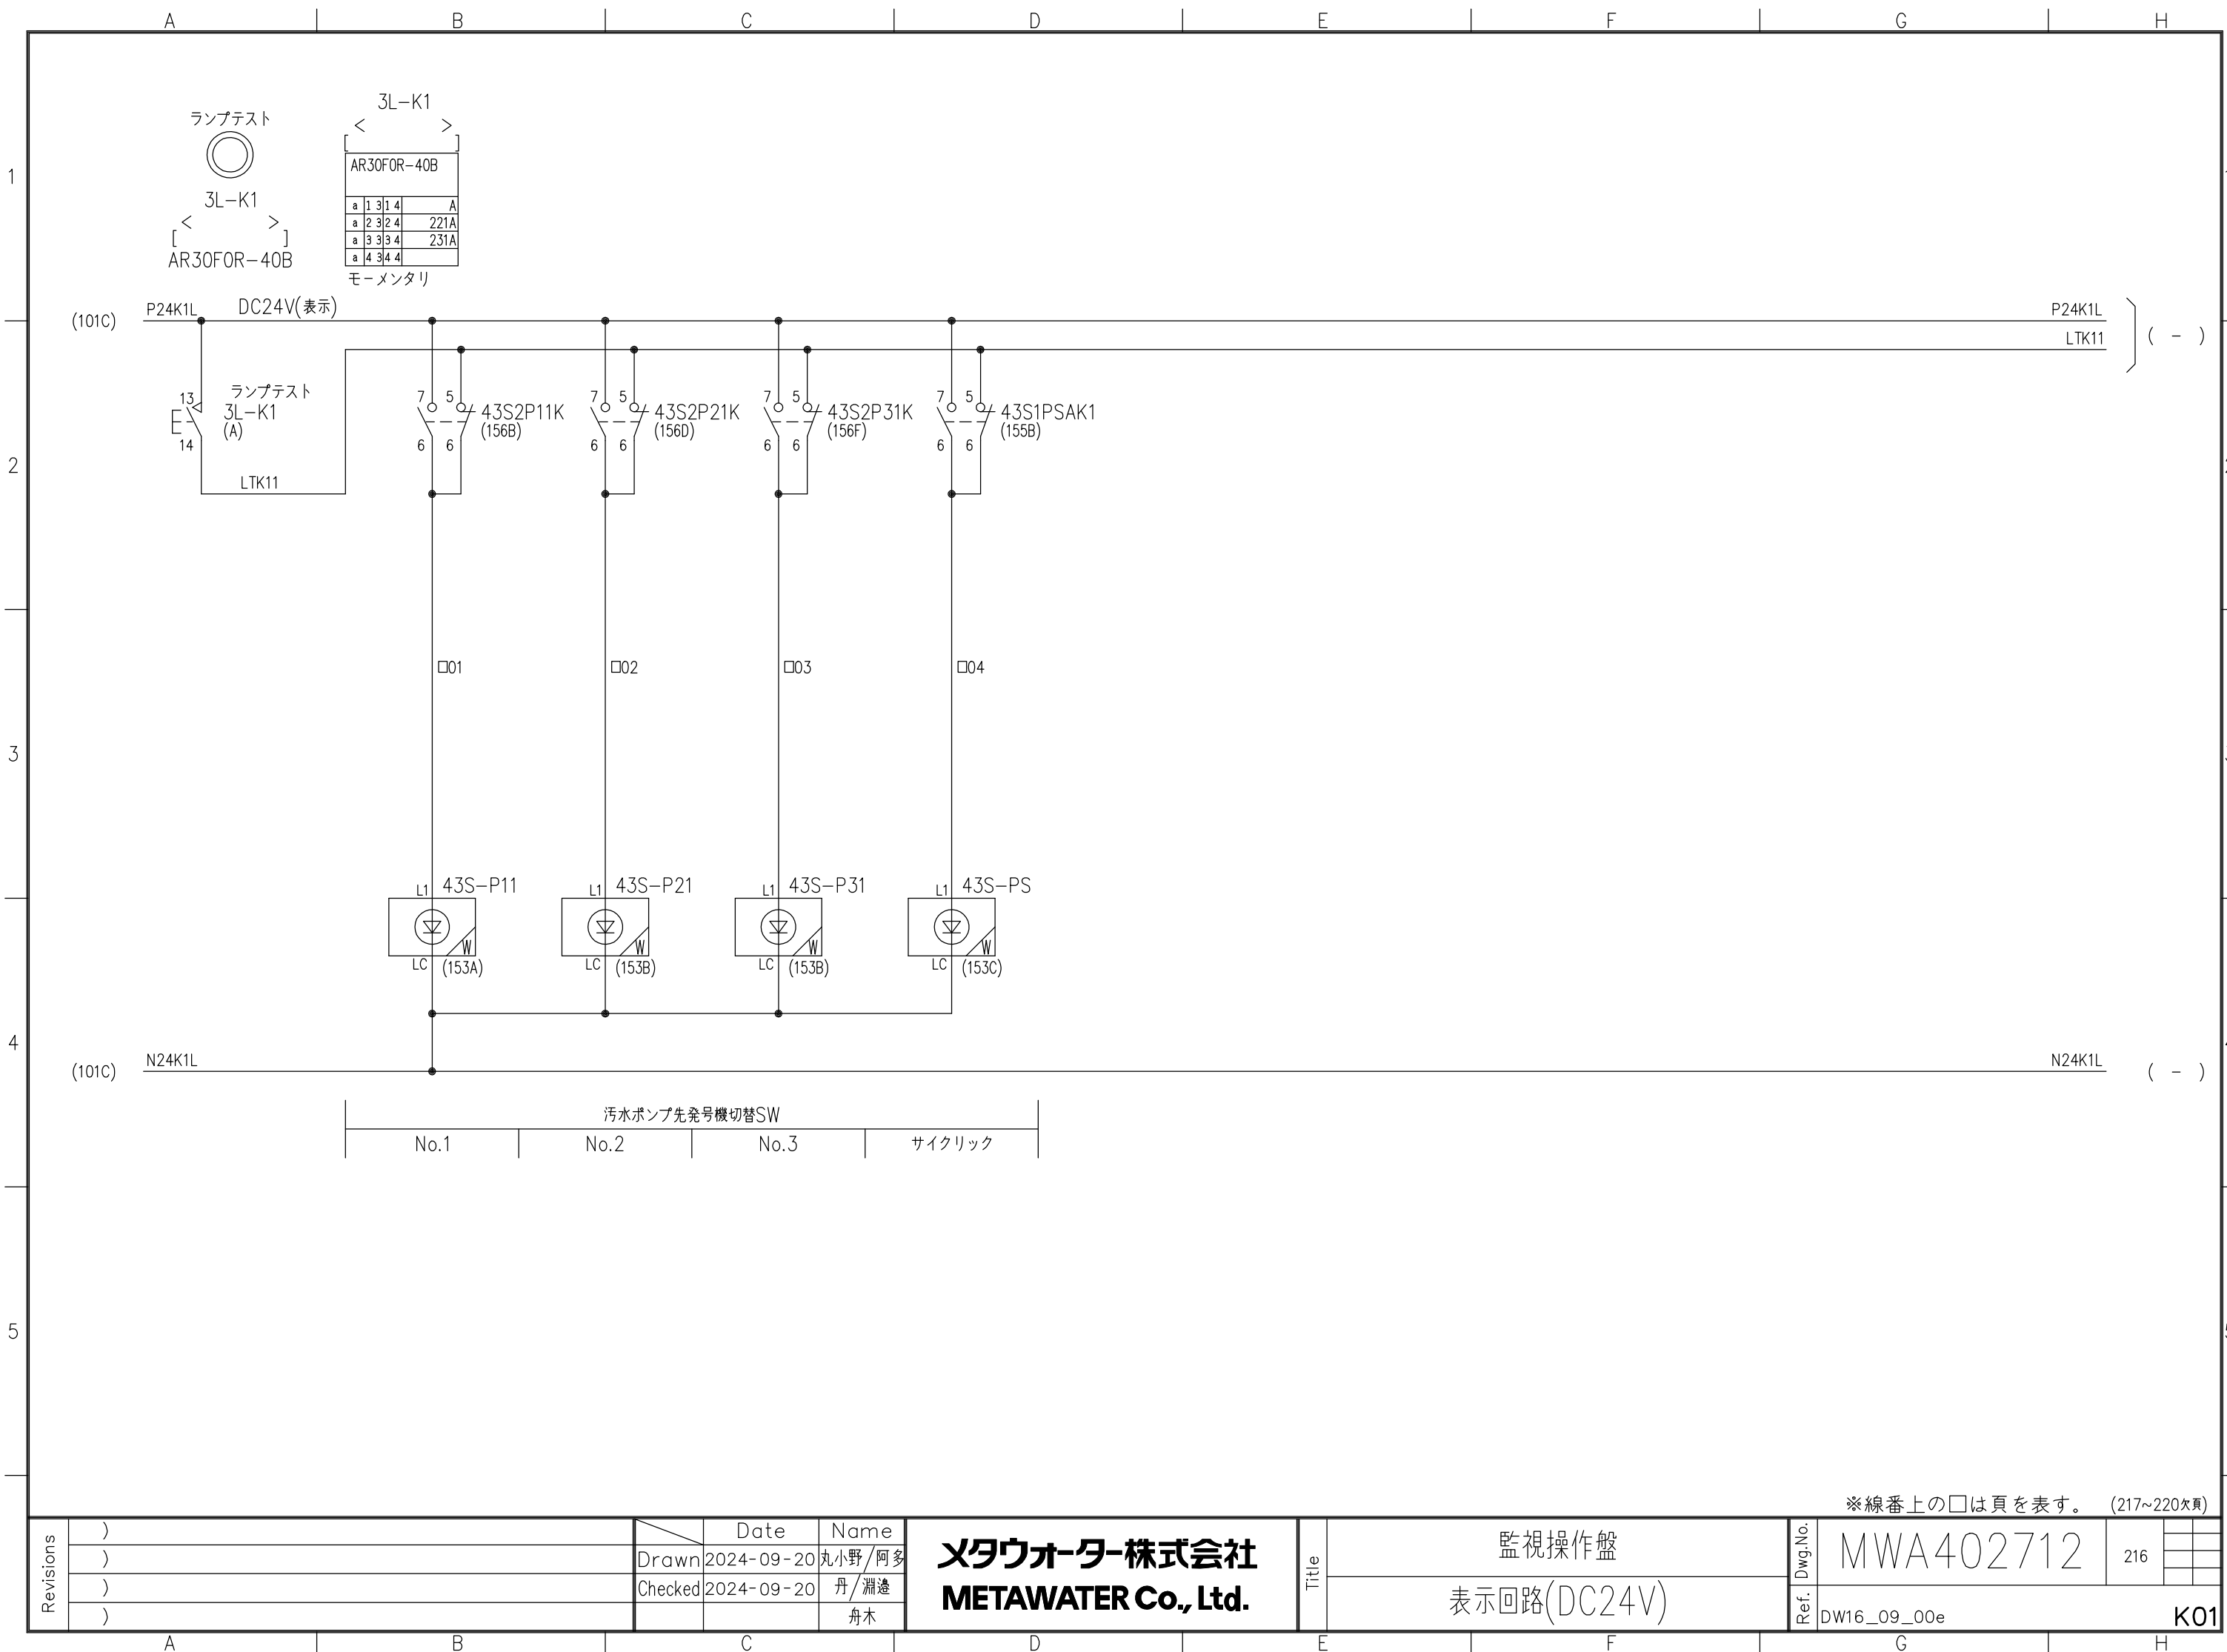


※線番上の□は頁を表す。(217~220欠頁)

Revisions	)		Date	Name	メタウォーター株式会社 METAWATER Co., Ltd.	Title	監視操作盤		Dwg.No.	MWA402712	216					
	)	Drawn	2024-09-20	丸小野/阿多			表示回路(DC24V)		Ref.	DW16_09_00e						K01
	)	Checked	2024-09-20	丹/淵邊												
	)			舟木												

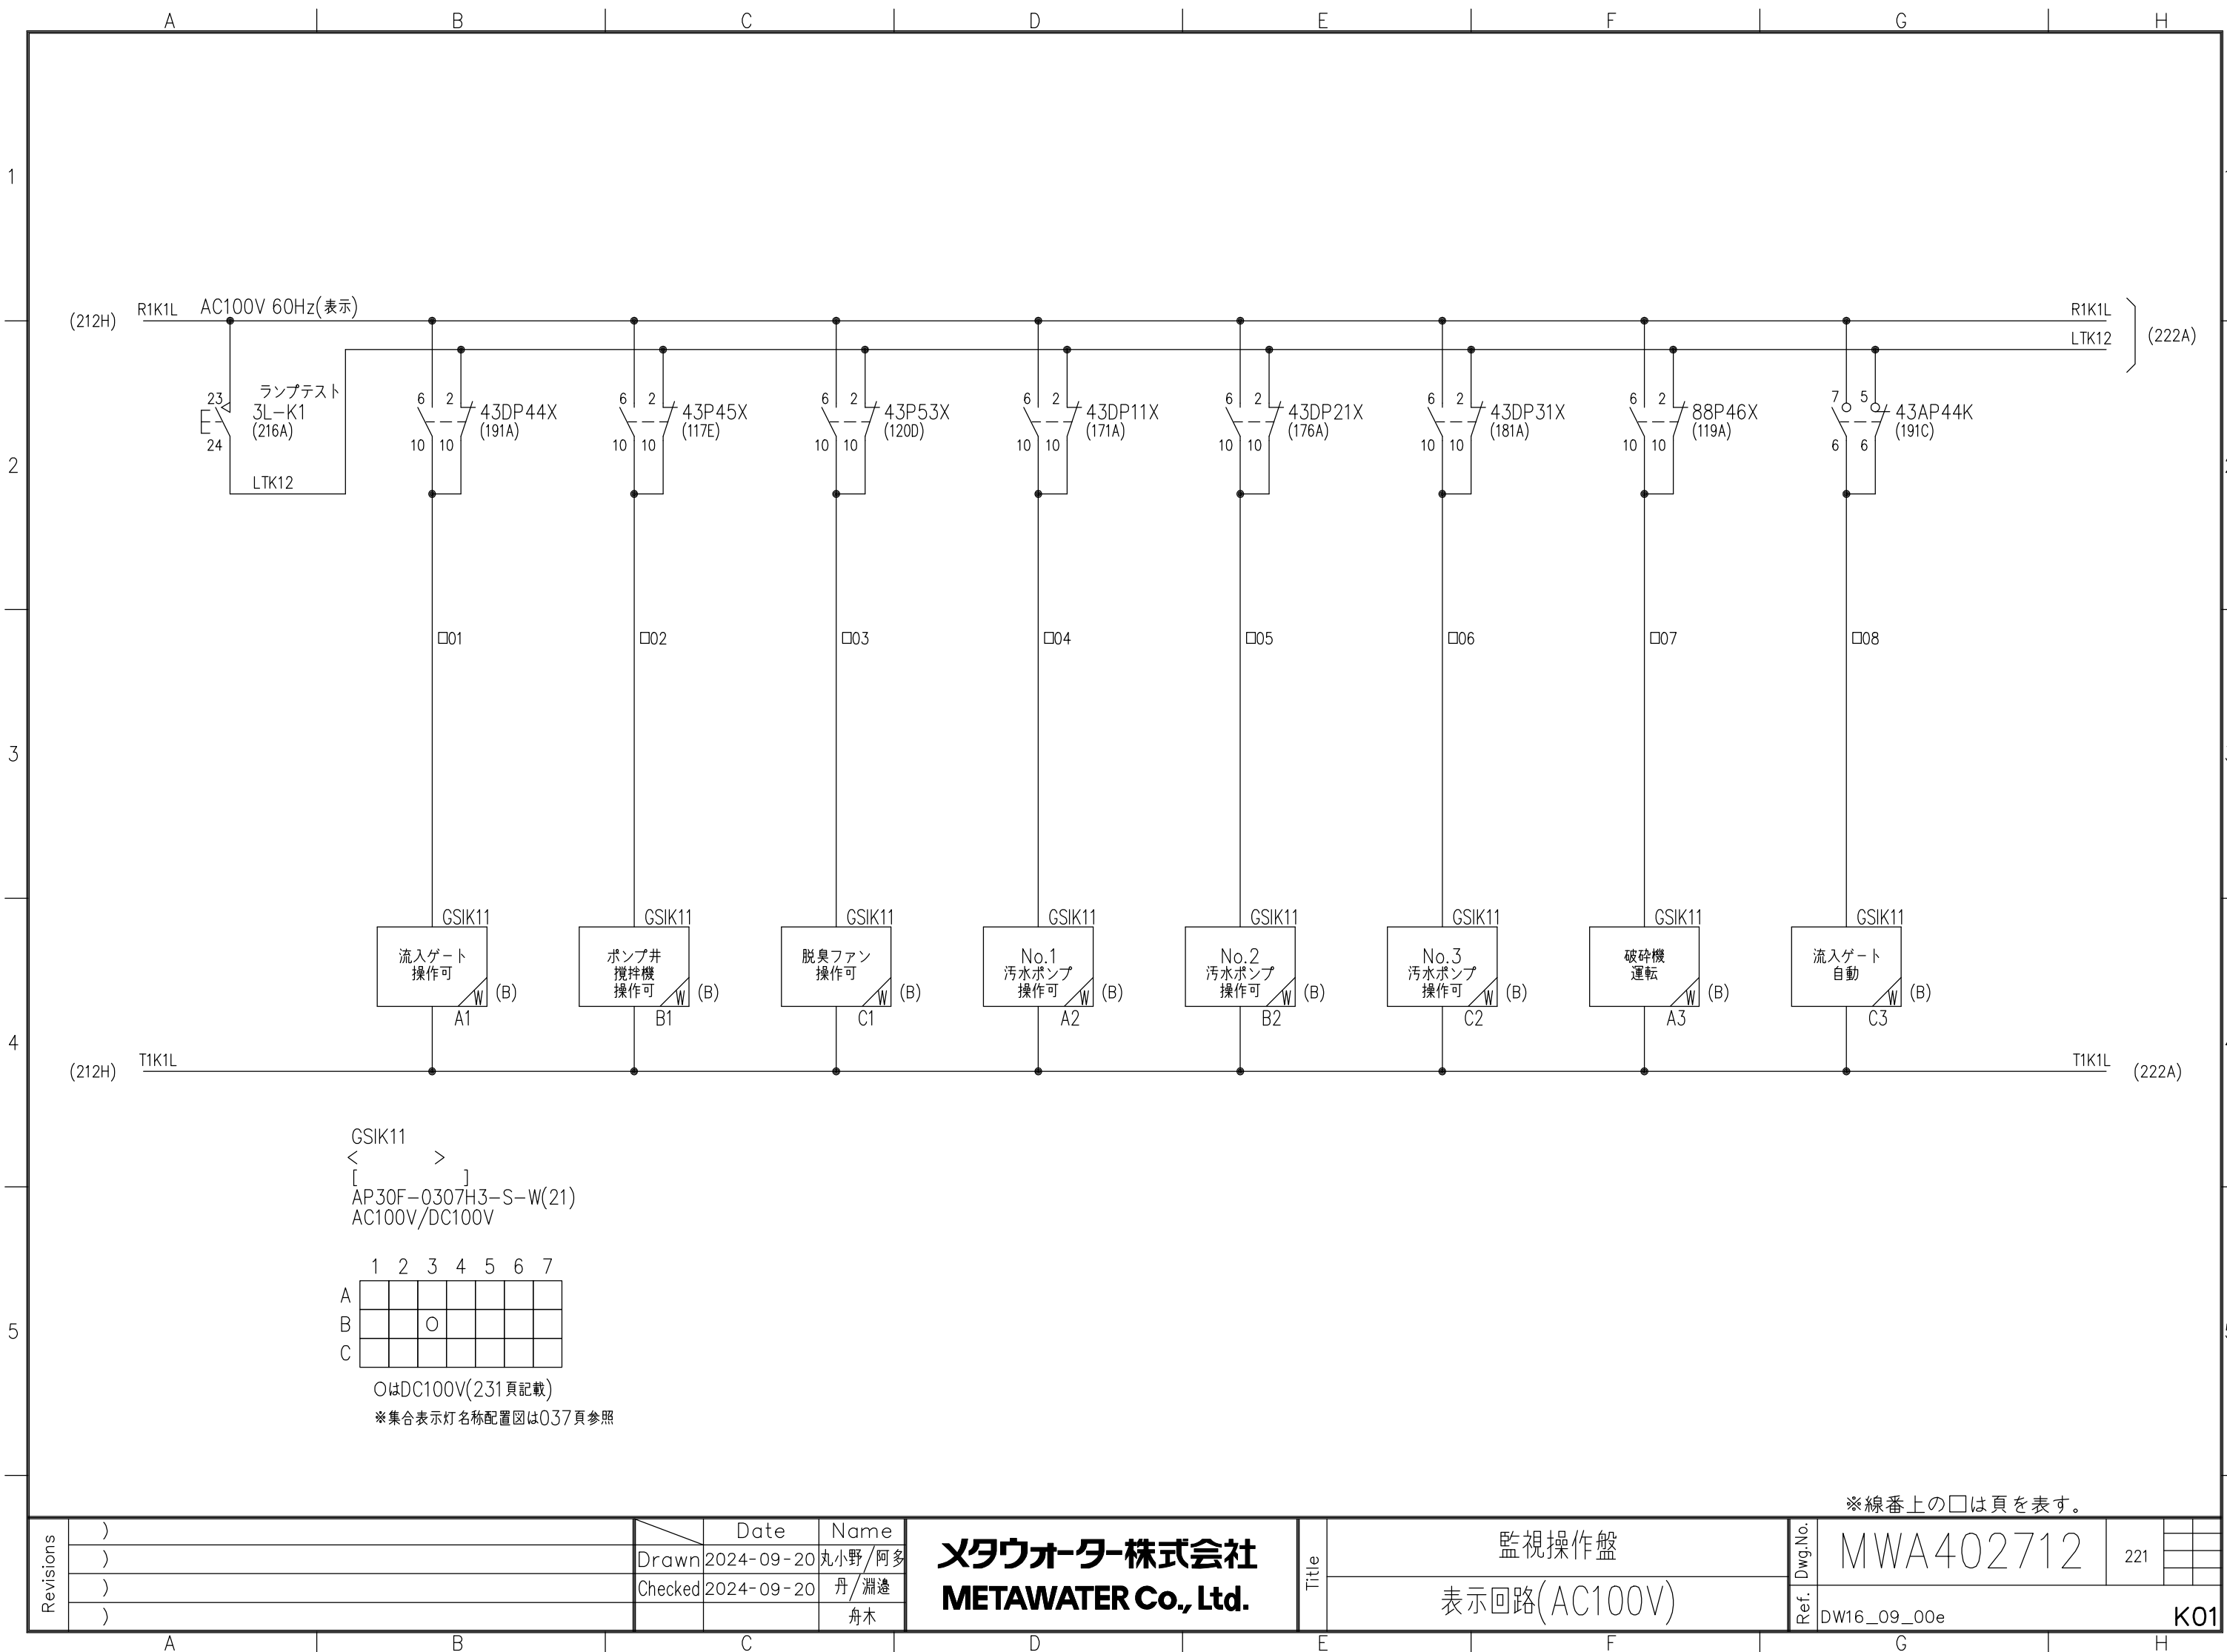

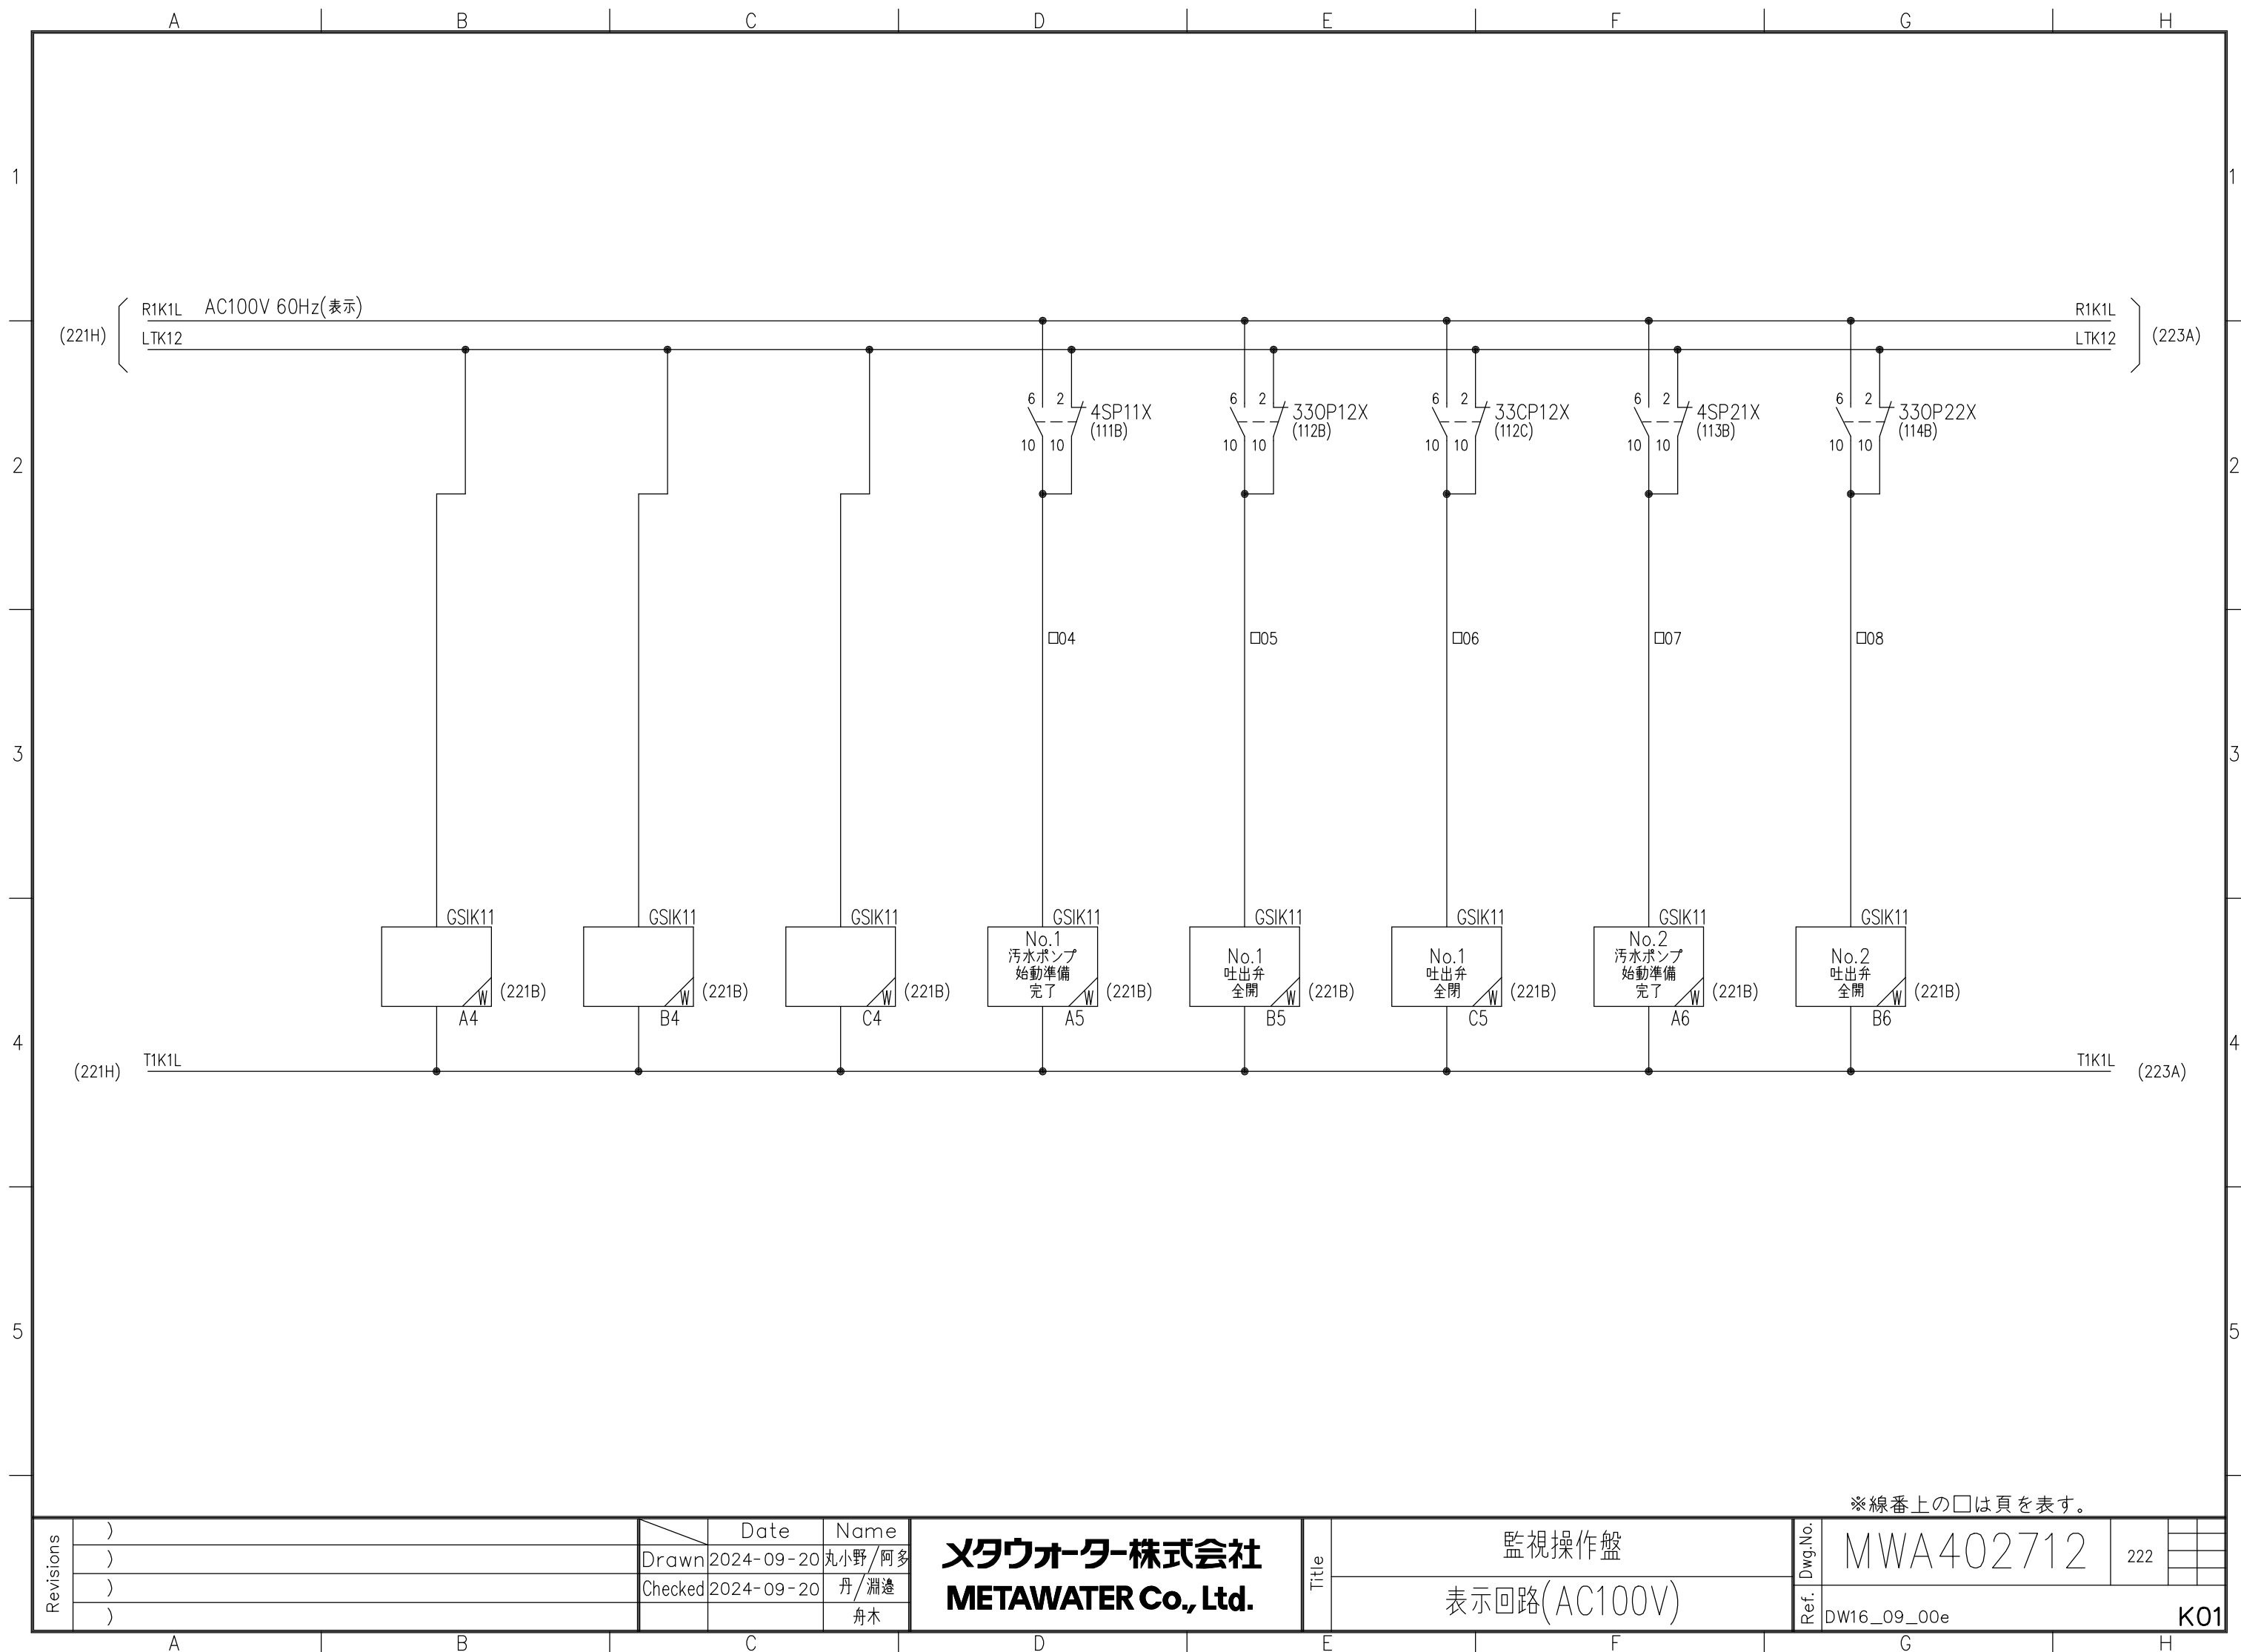

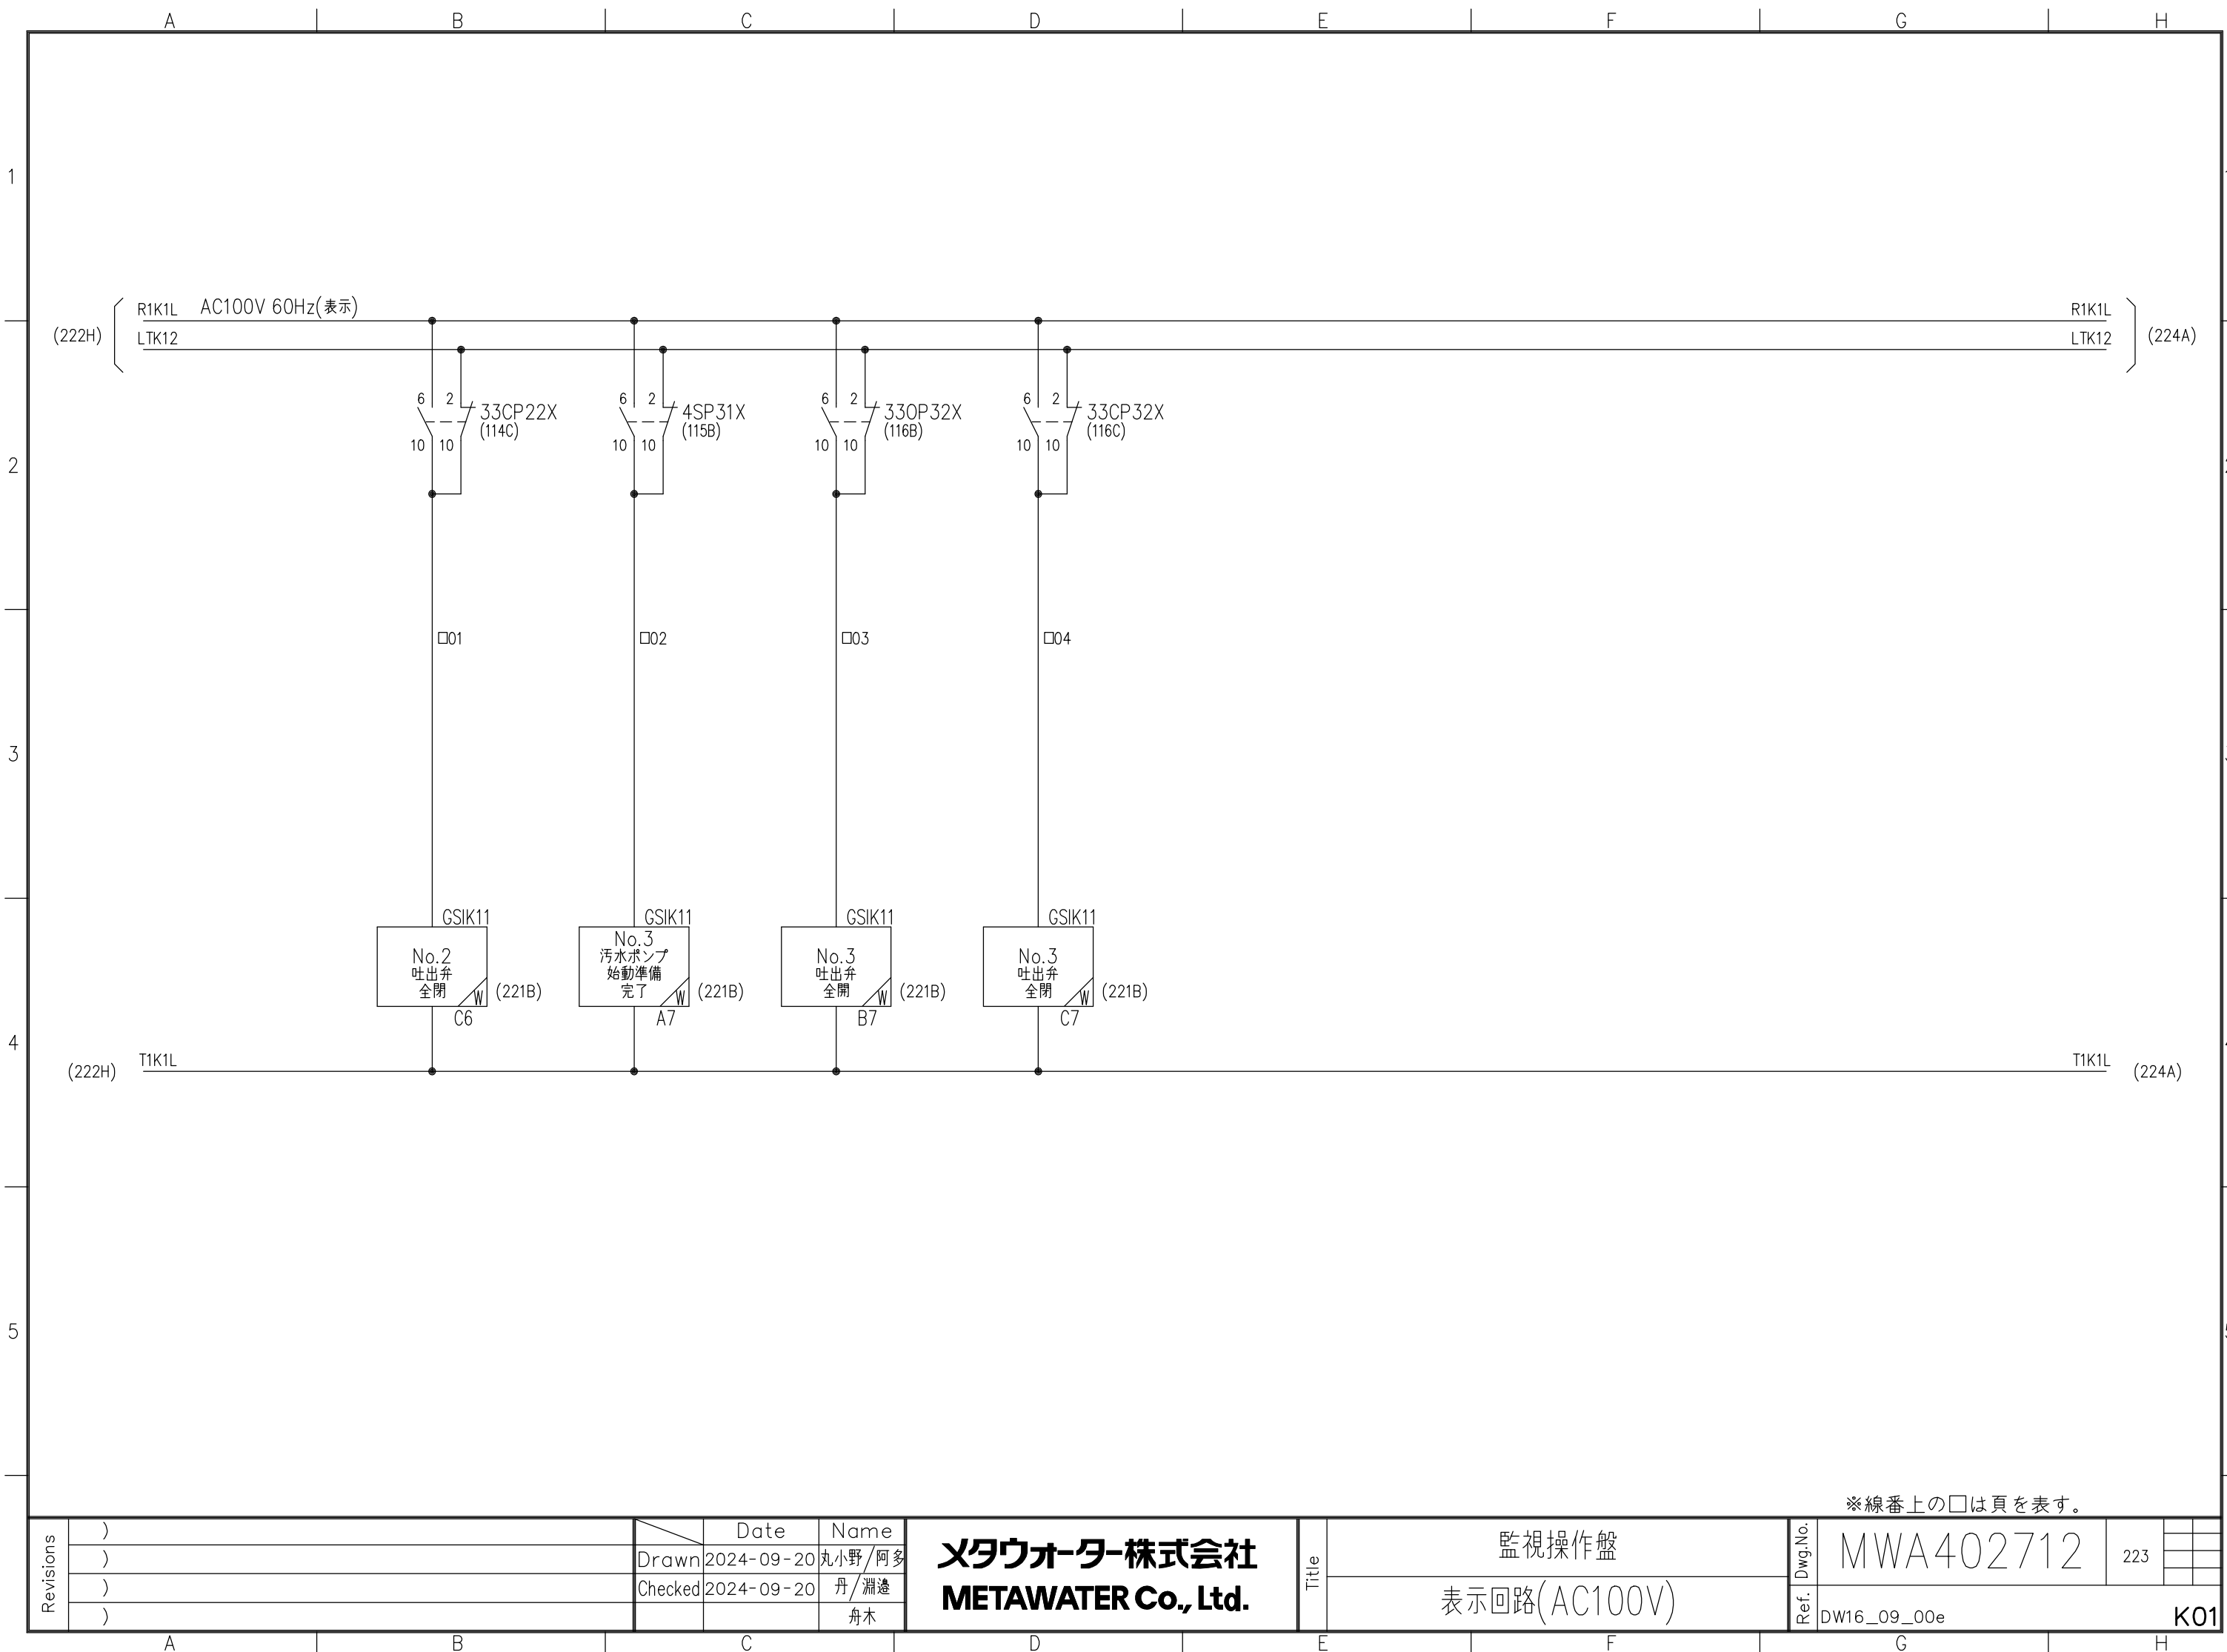

Revisions	)
	)
	)
	)


	Date	Name
Drawn	2024-09-20	丸小野/阿多
Checked	2024-09-20	丹/淵邊
		舟木


メタウォーター株式会社
METAWATER Co., Ltd.


Title	監視操作盤
	表示回路(AC100V)

Dwg.No.	MWA402712	223
Ref.	DW16_09_00e	K01




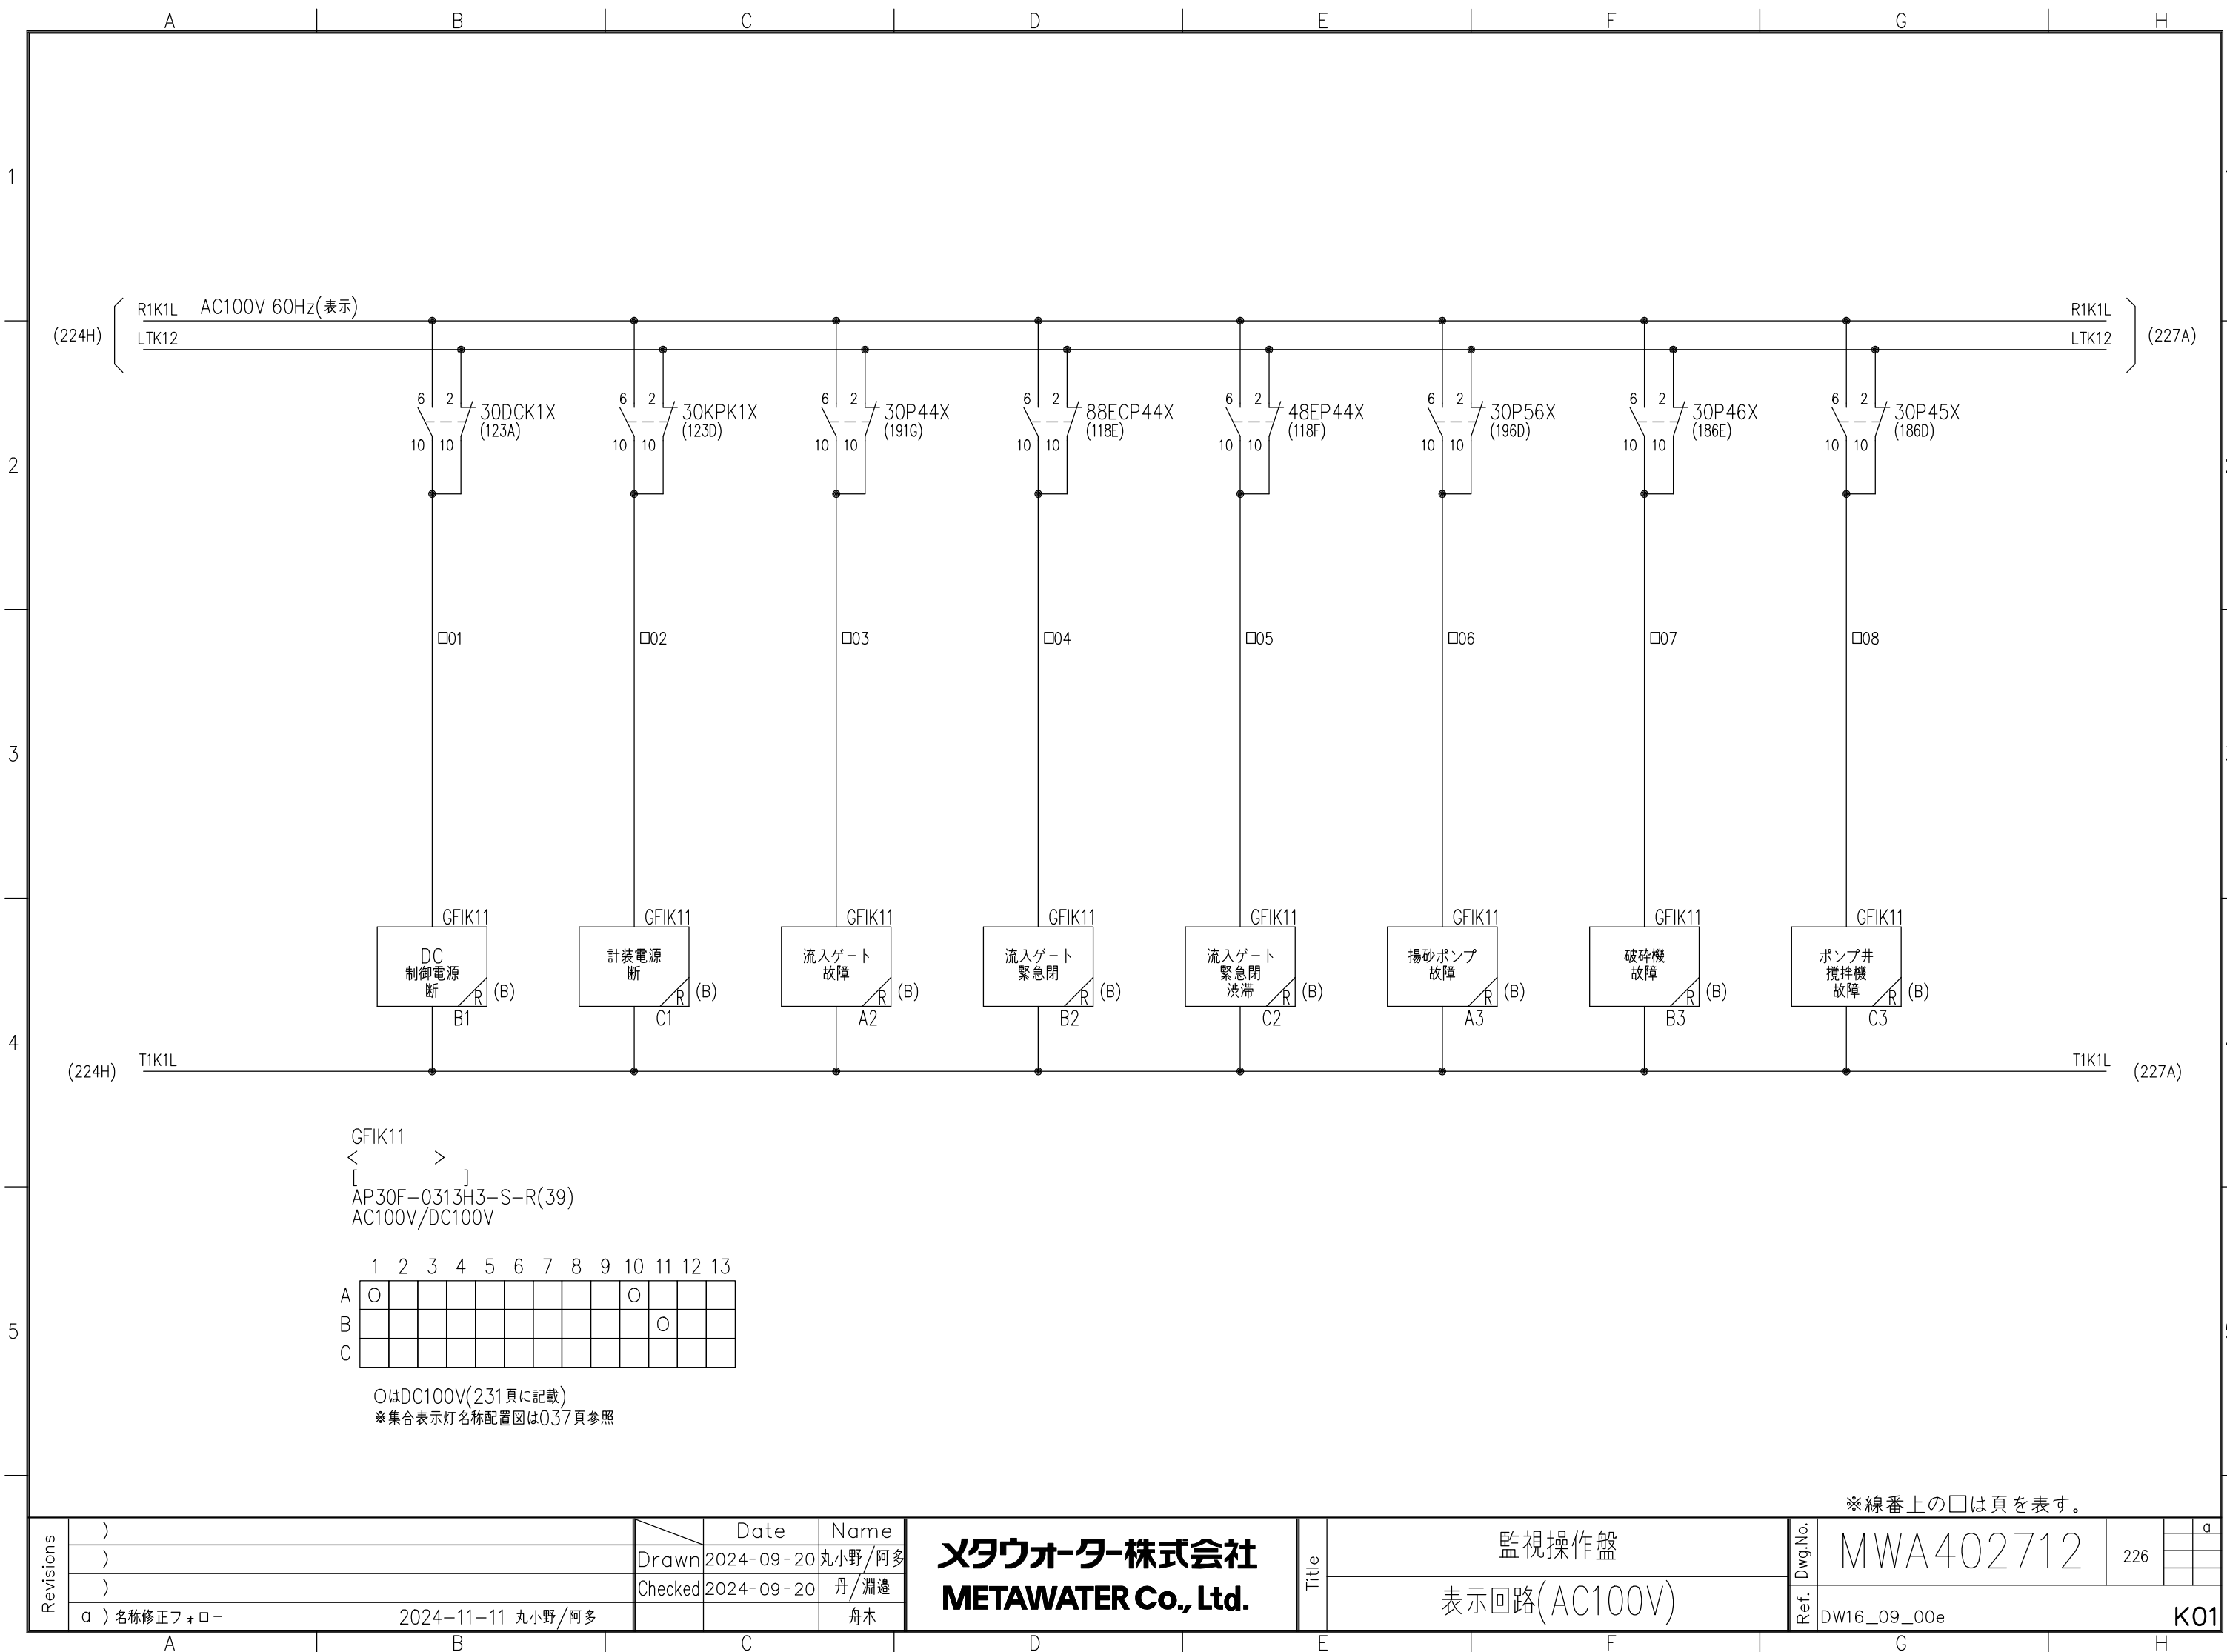


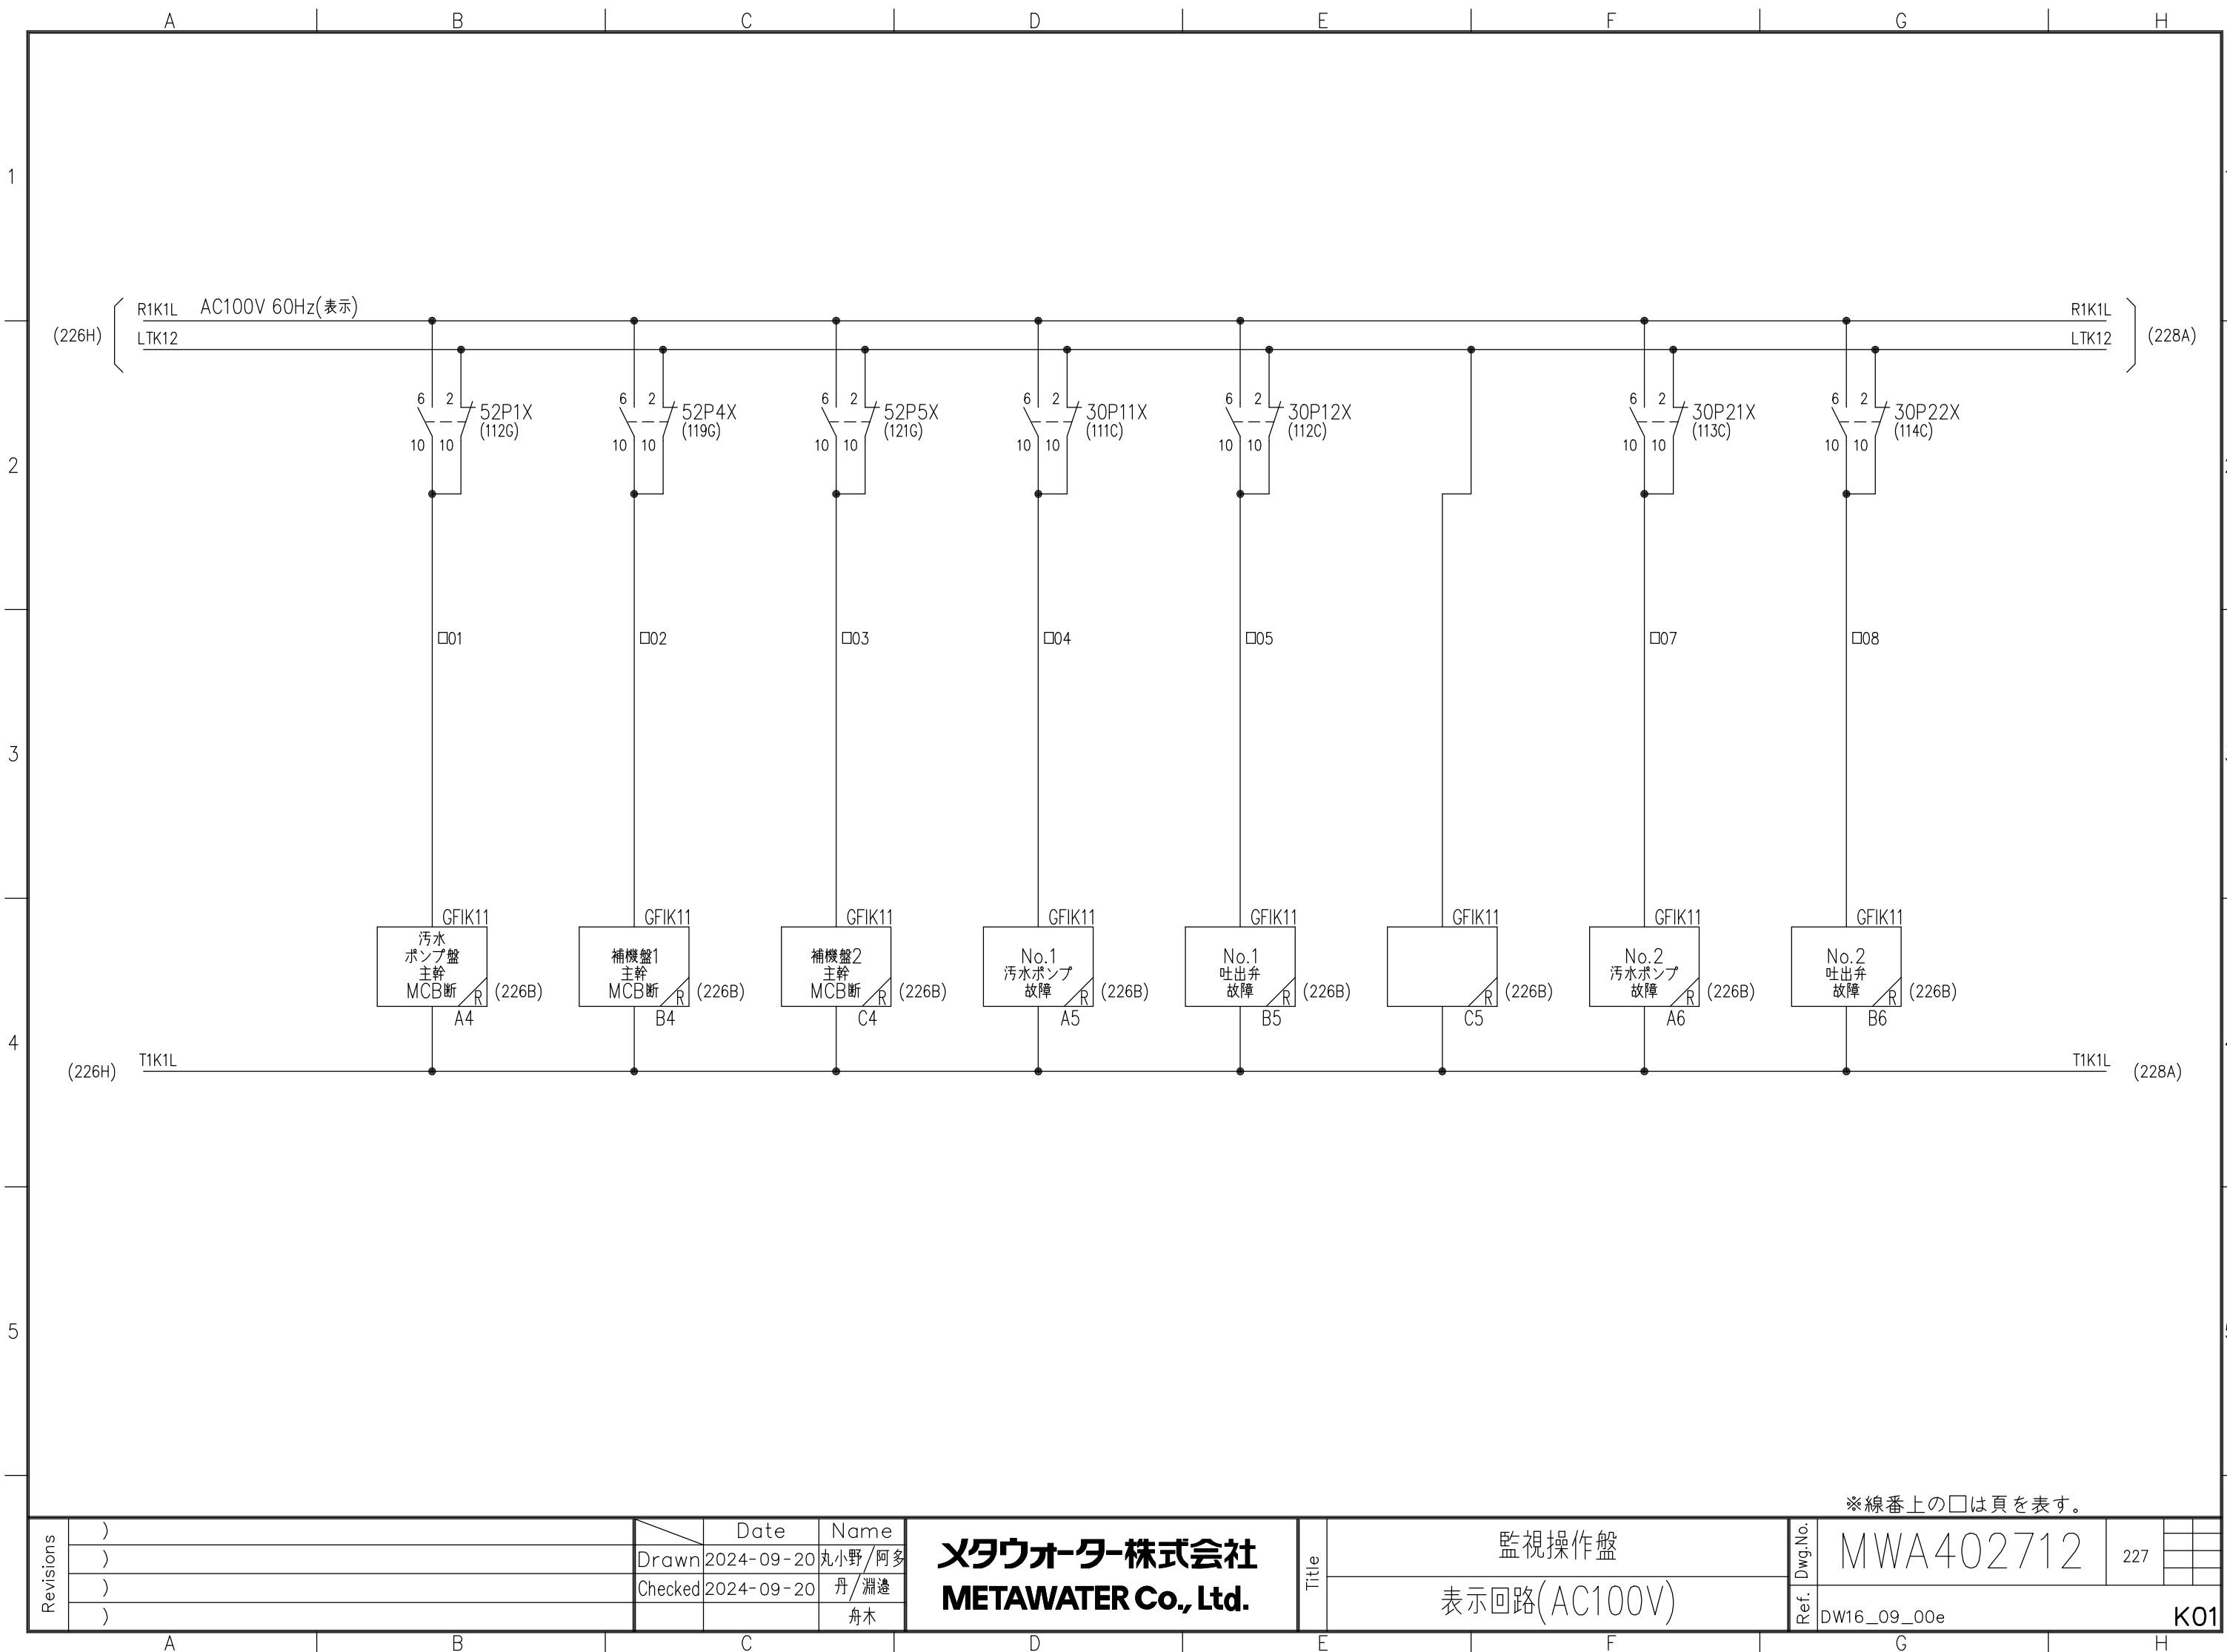


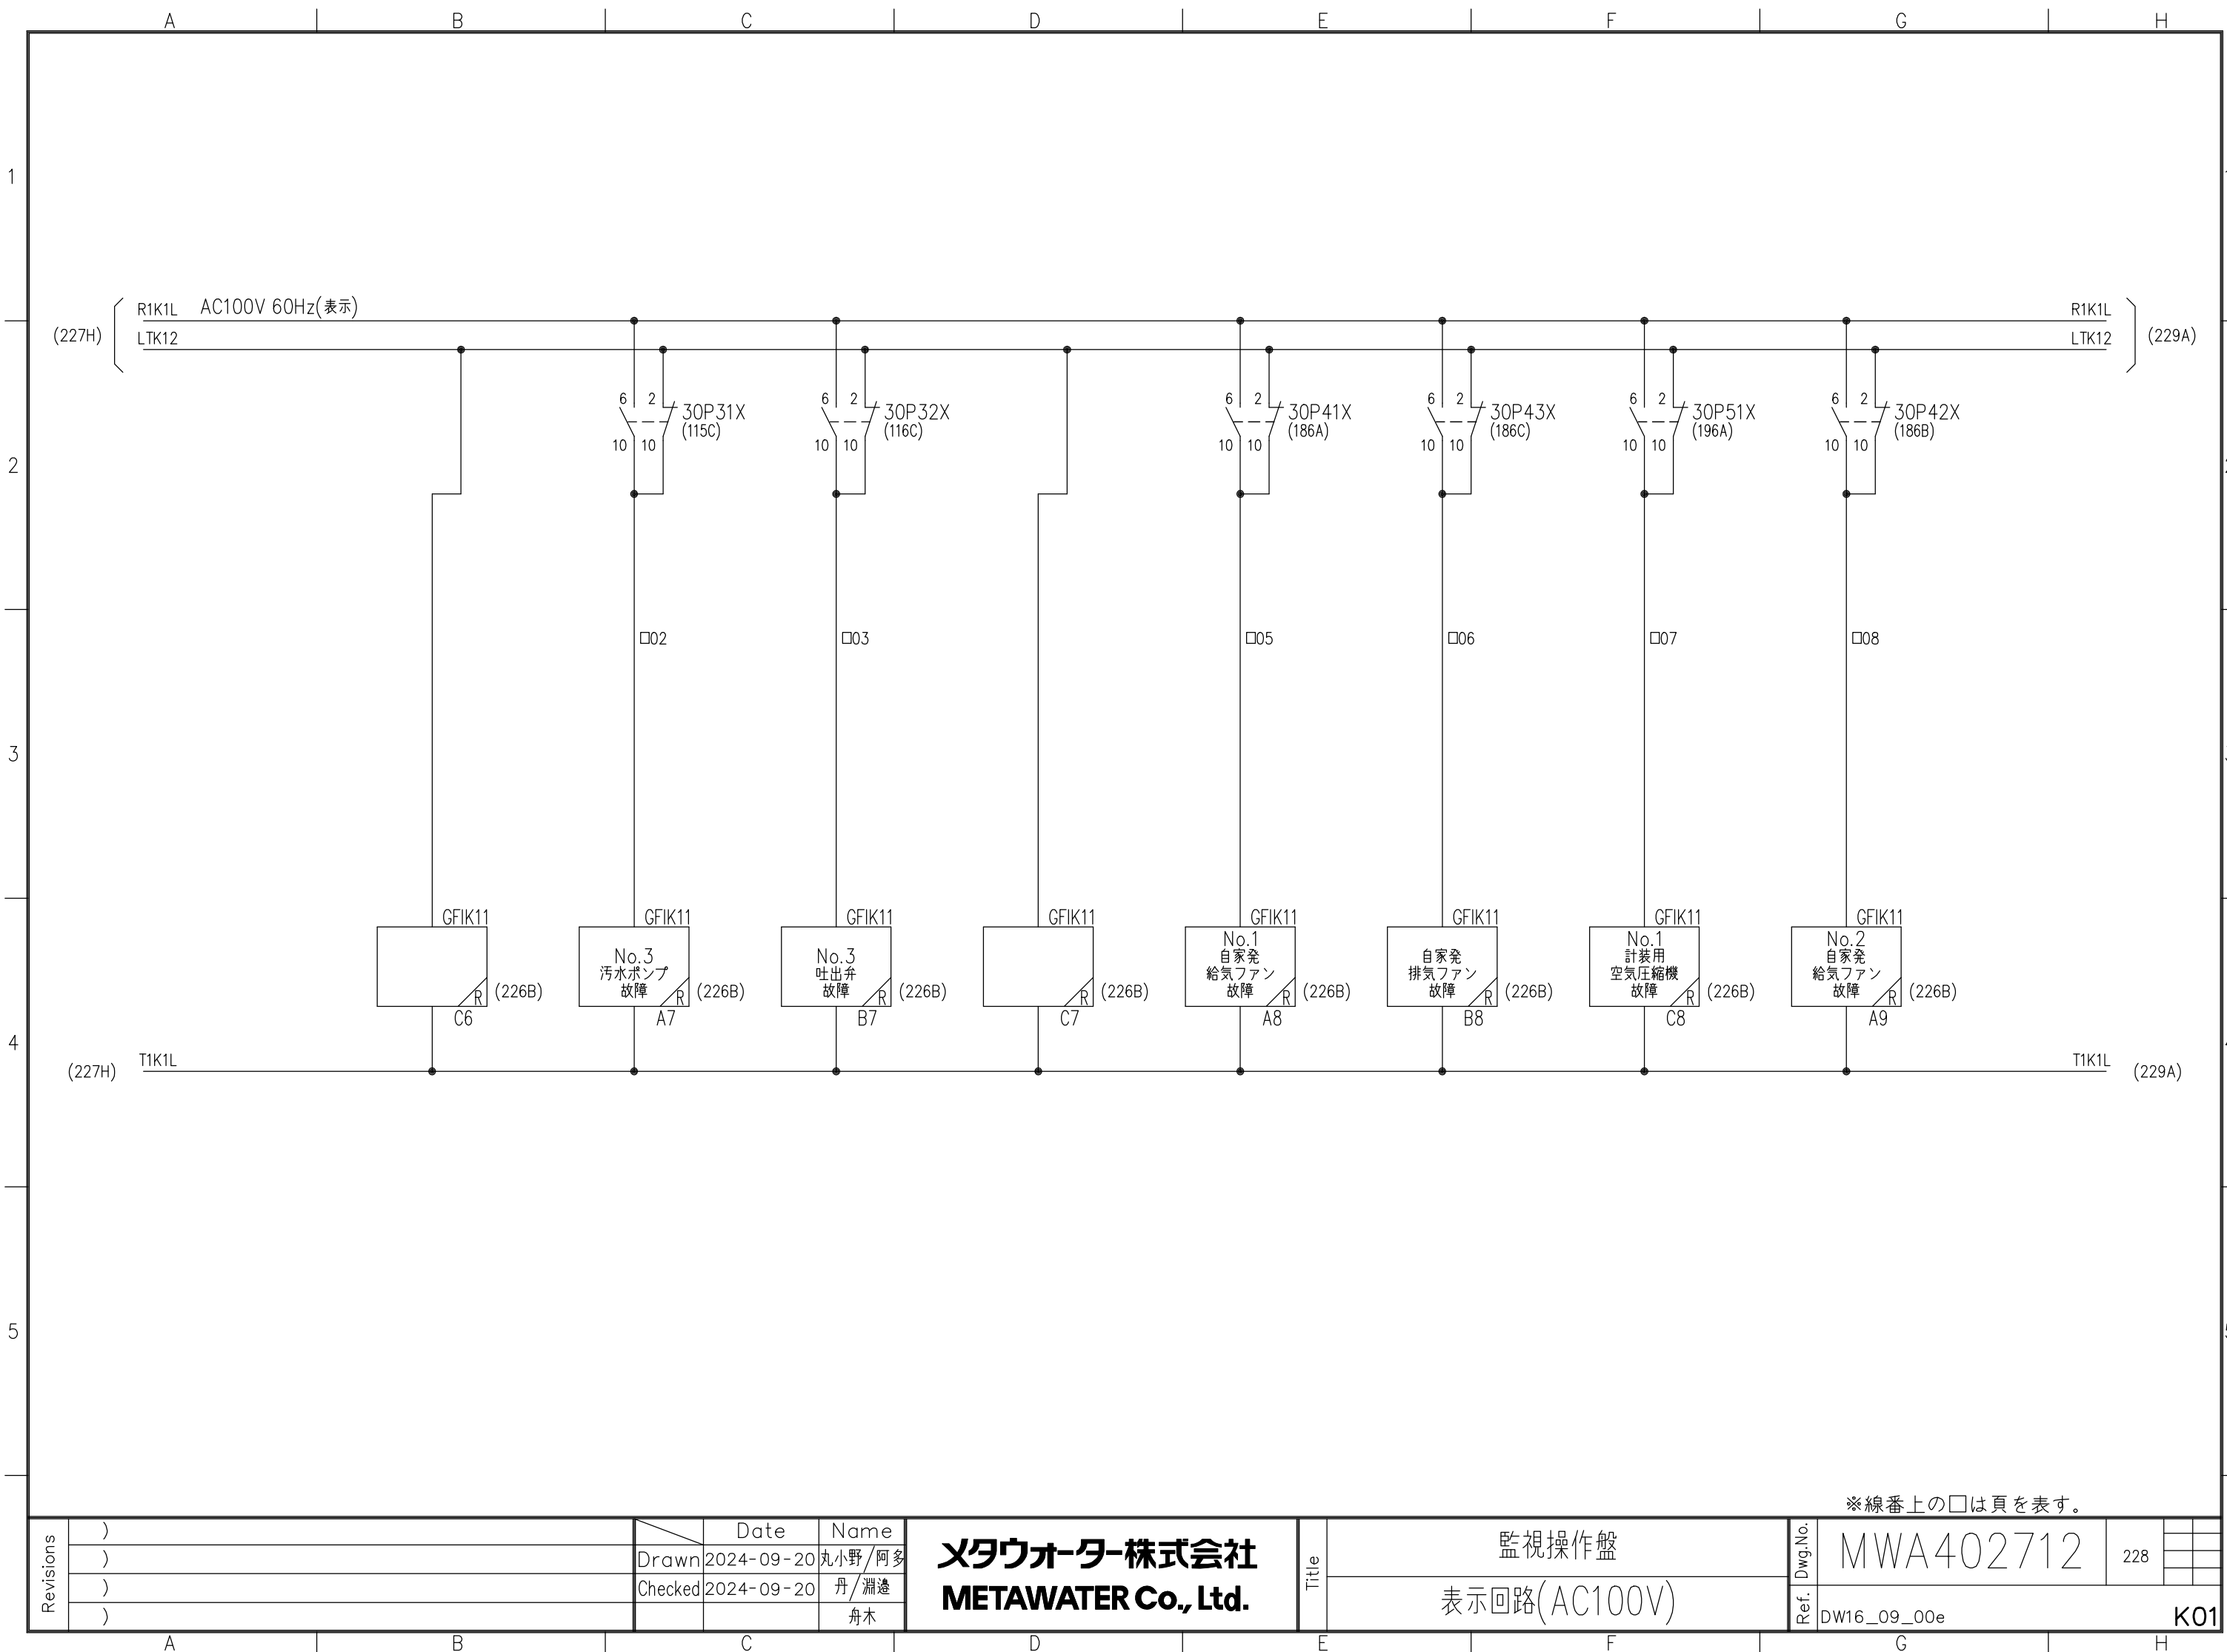

Revisions	)		Date	Name	メタウォーター株式会社 METAWATER Co., Ltd.	Title	監視操作盤	Dwg.No.	MWA402712	228		
	)	Drawn	2024-09-20	丸小野/阿多								
	)	Checked	2024-09-20	丹/淵邊			表示回路(AC100V)	Ref.	DW16_09_00e	K01		
	)			舟木								

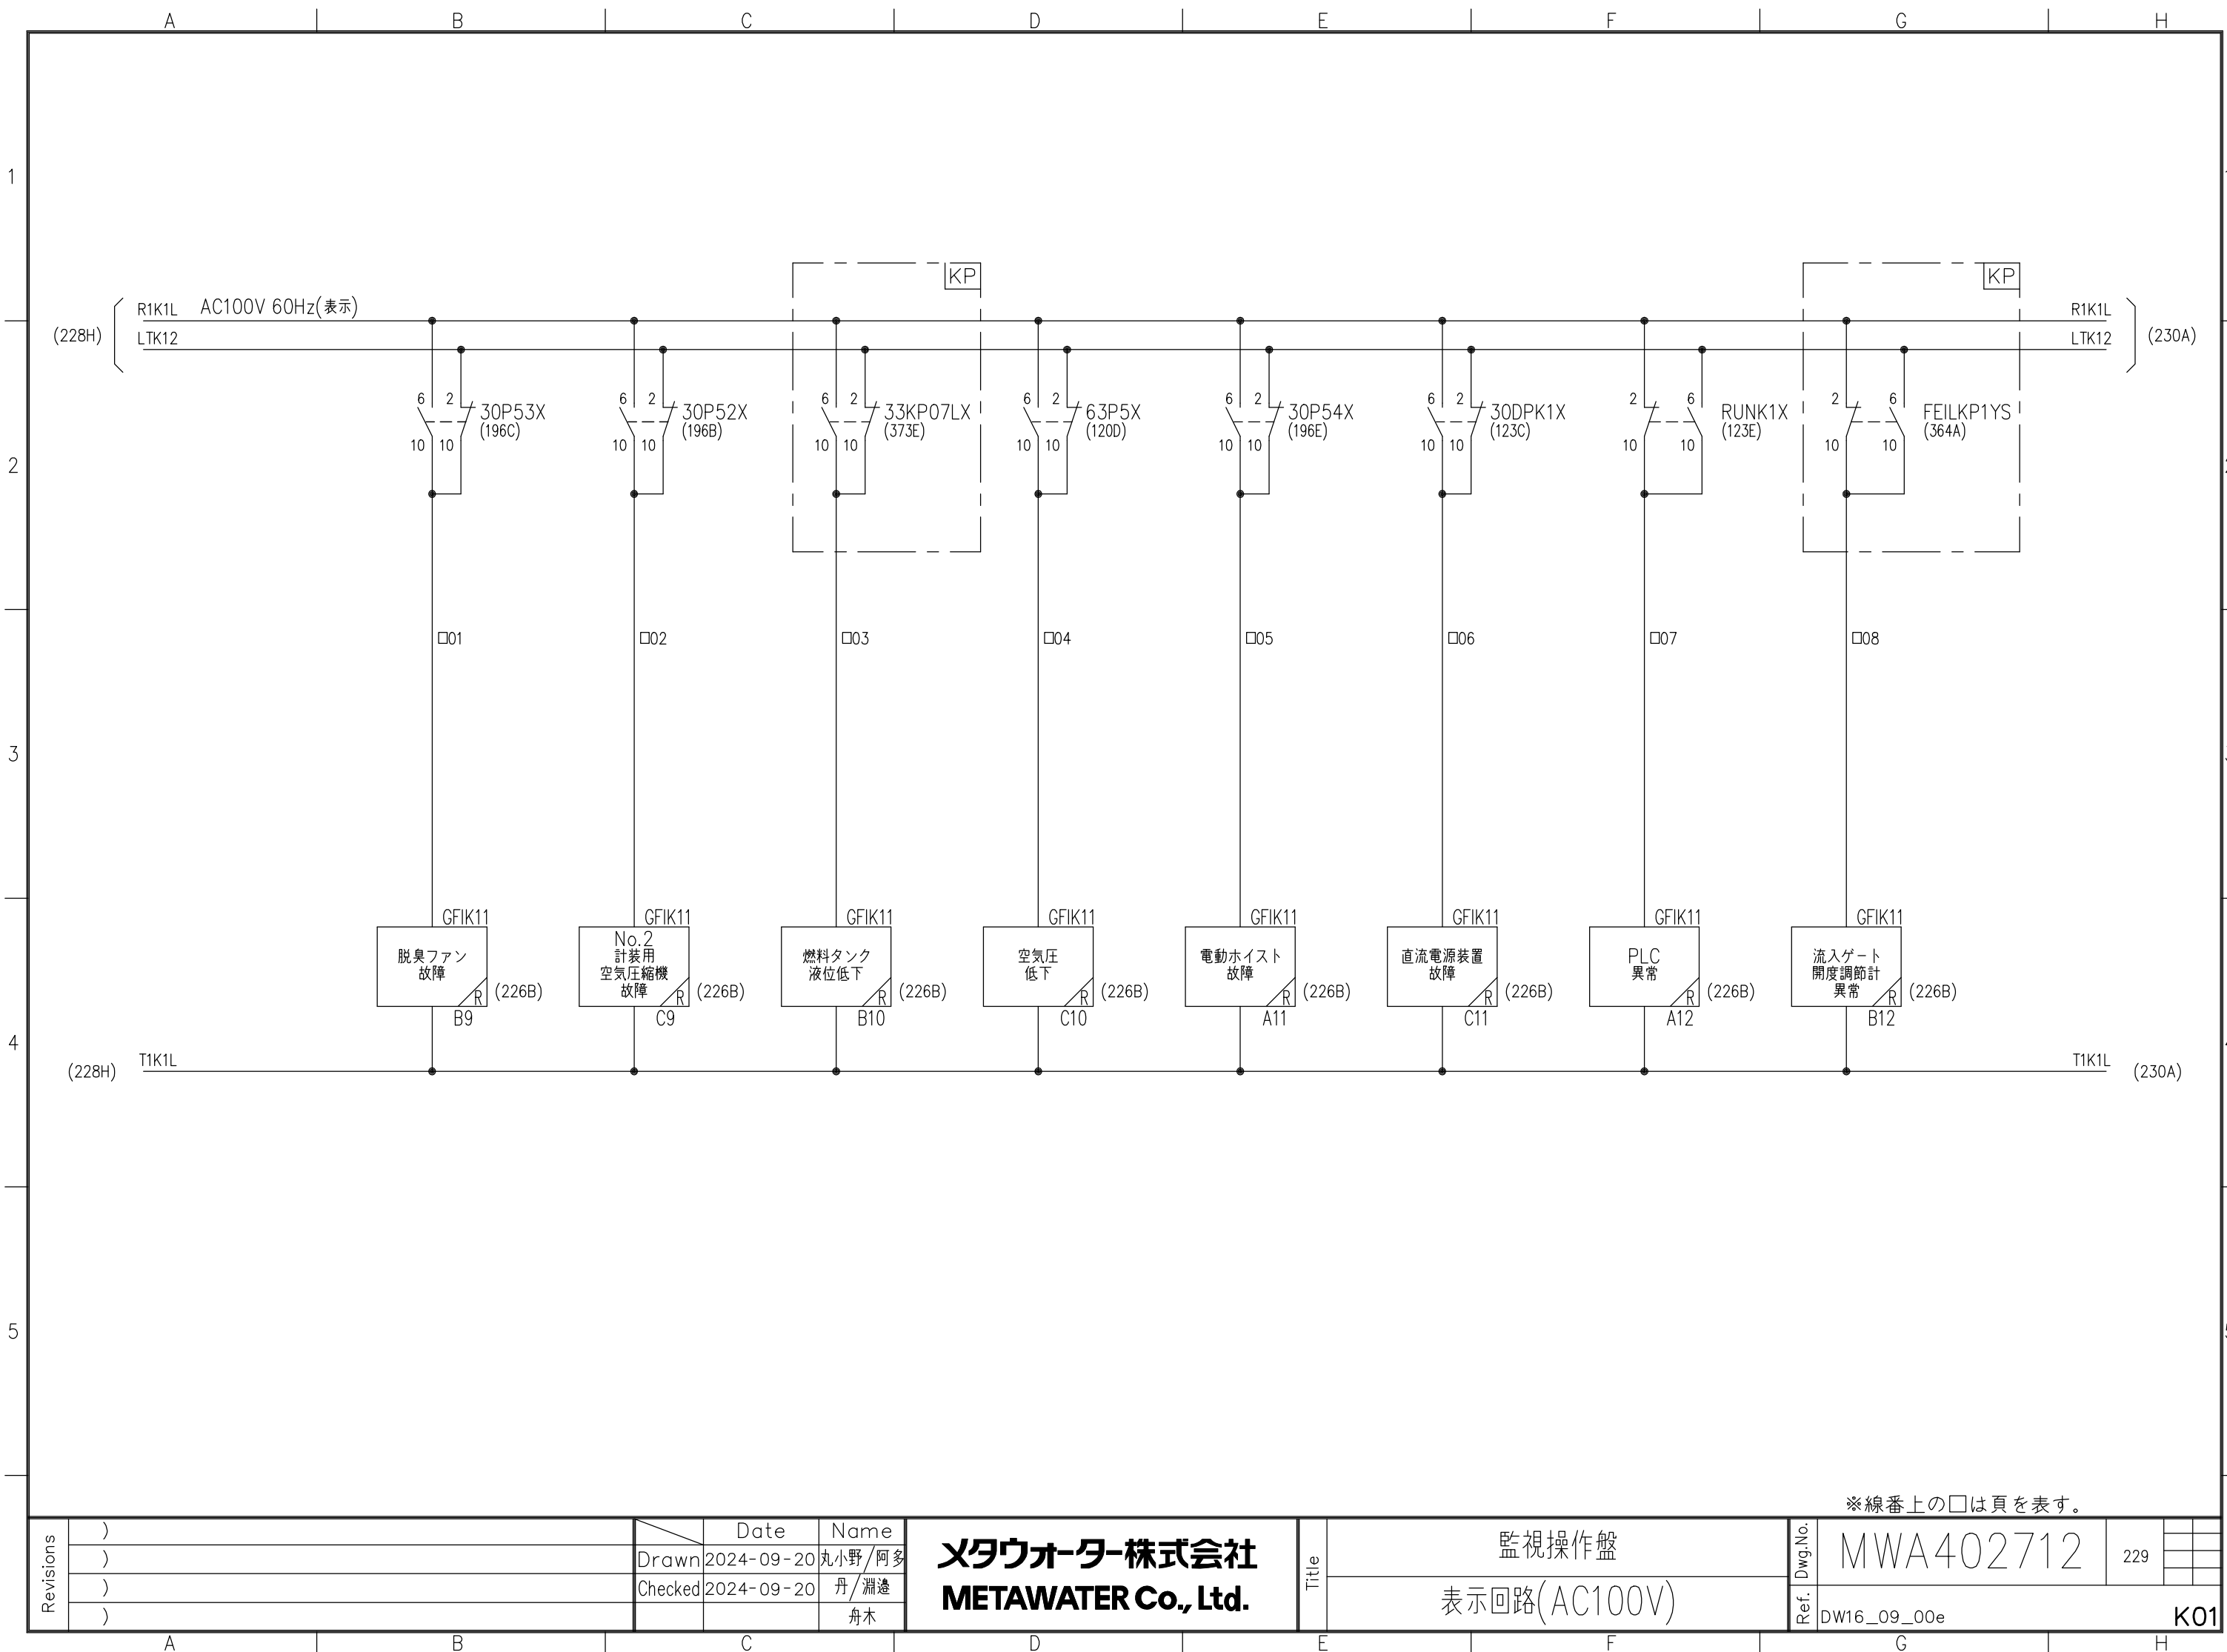


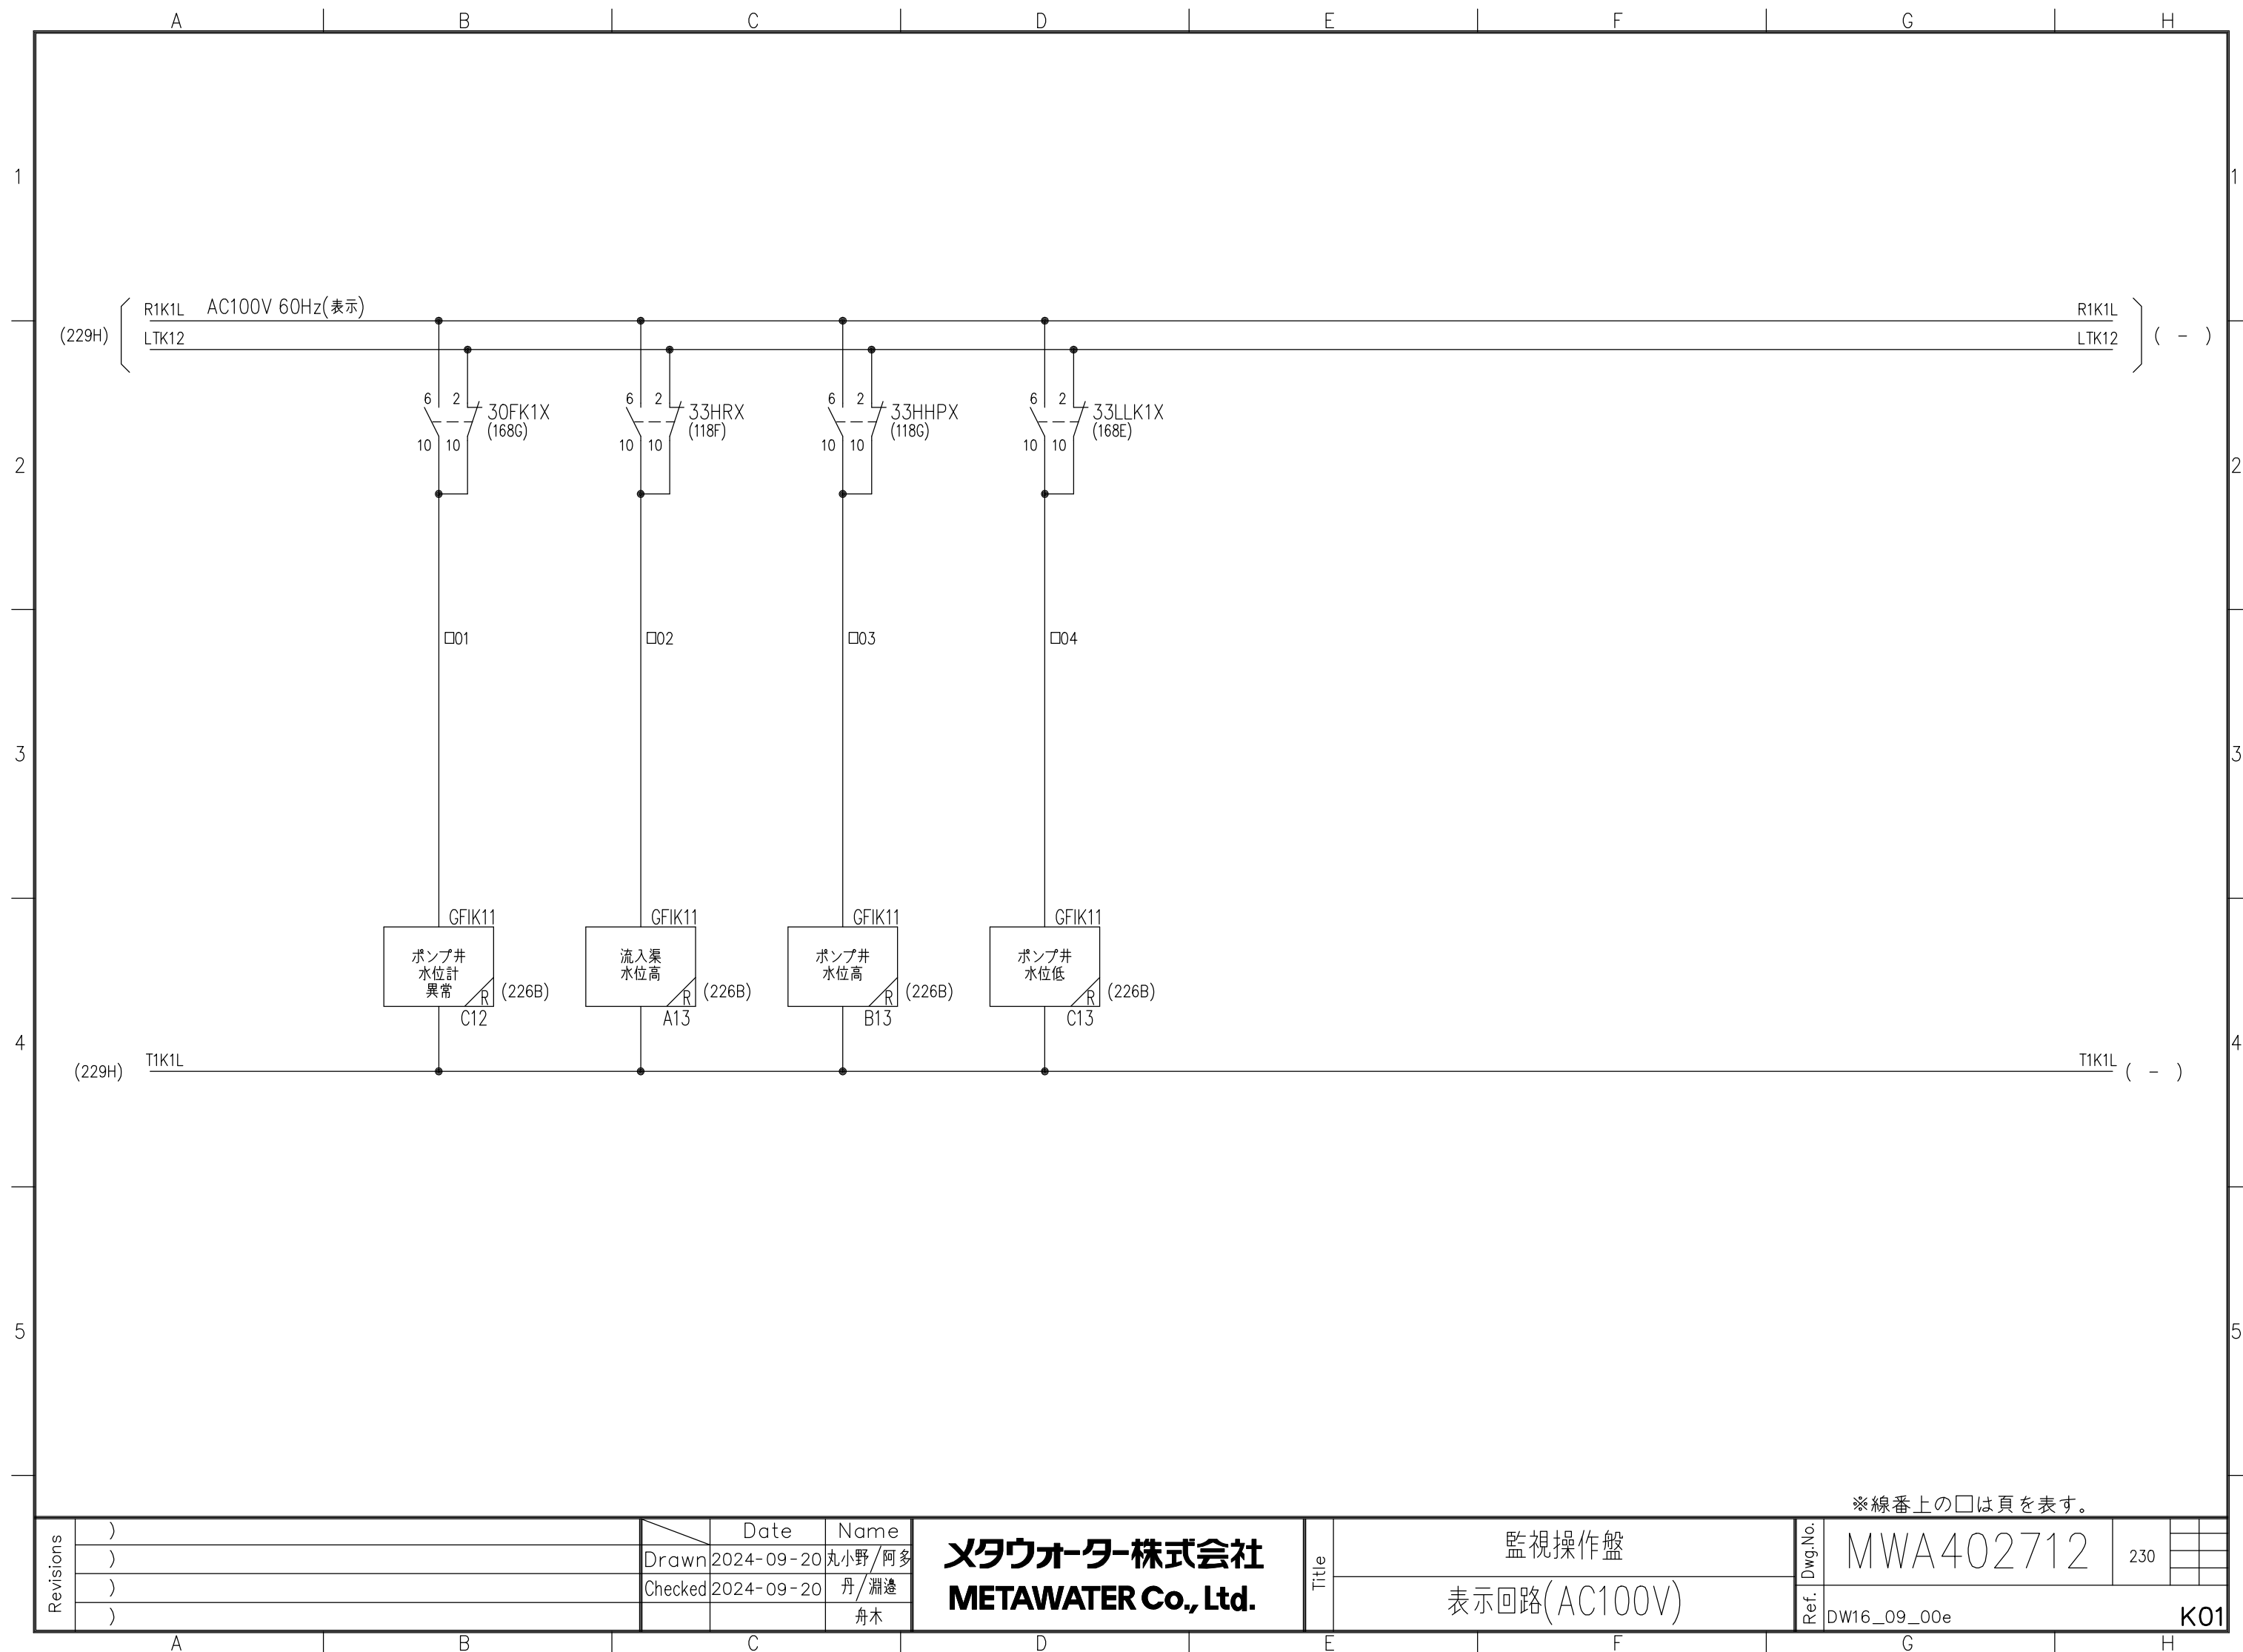


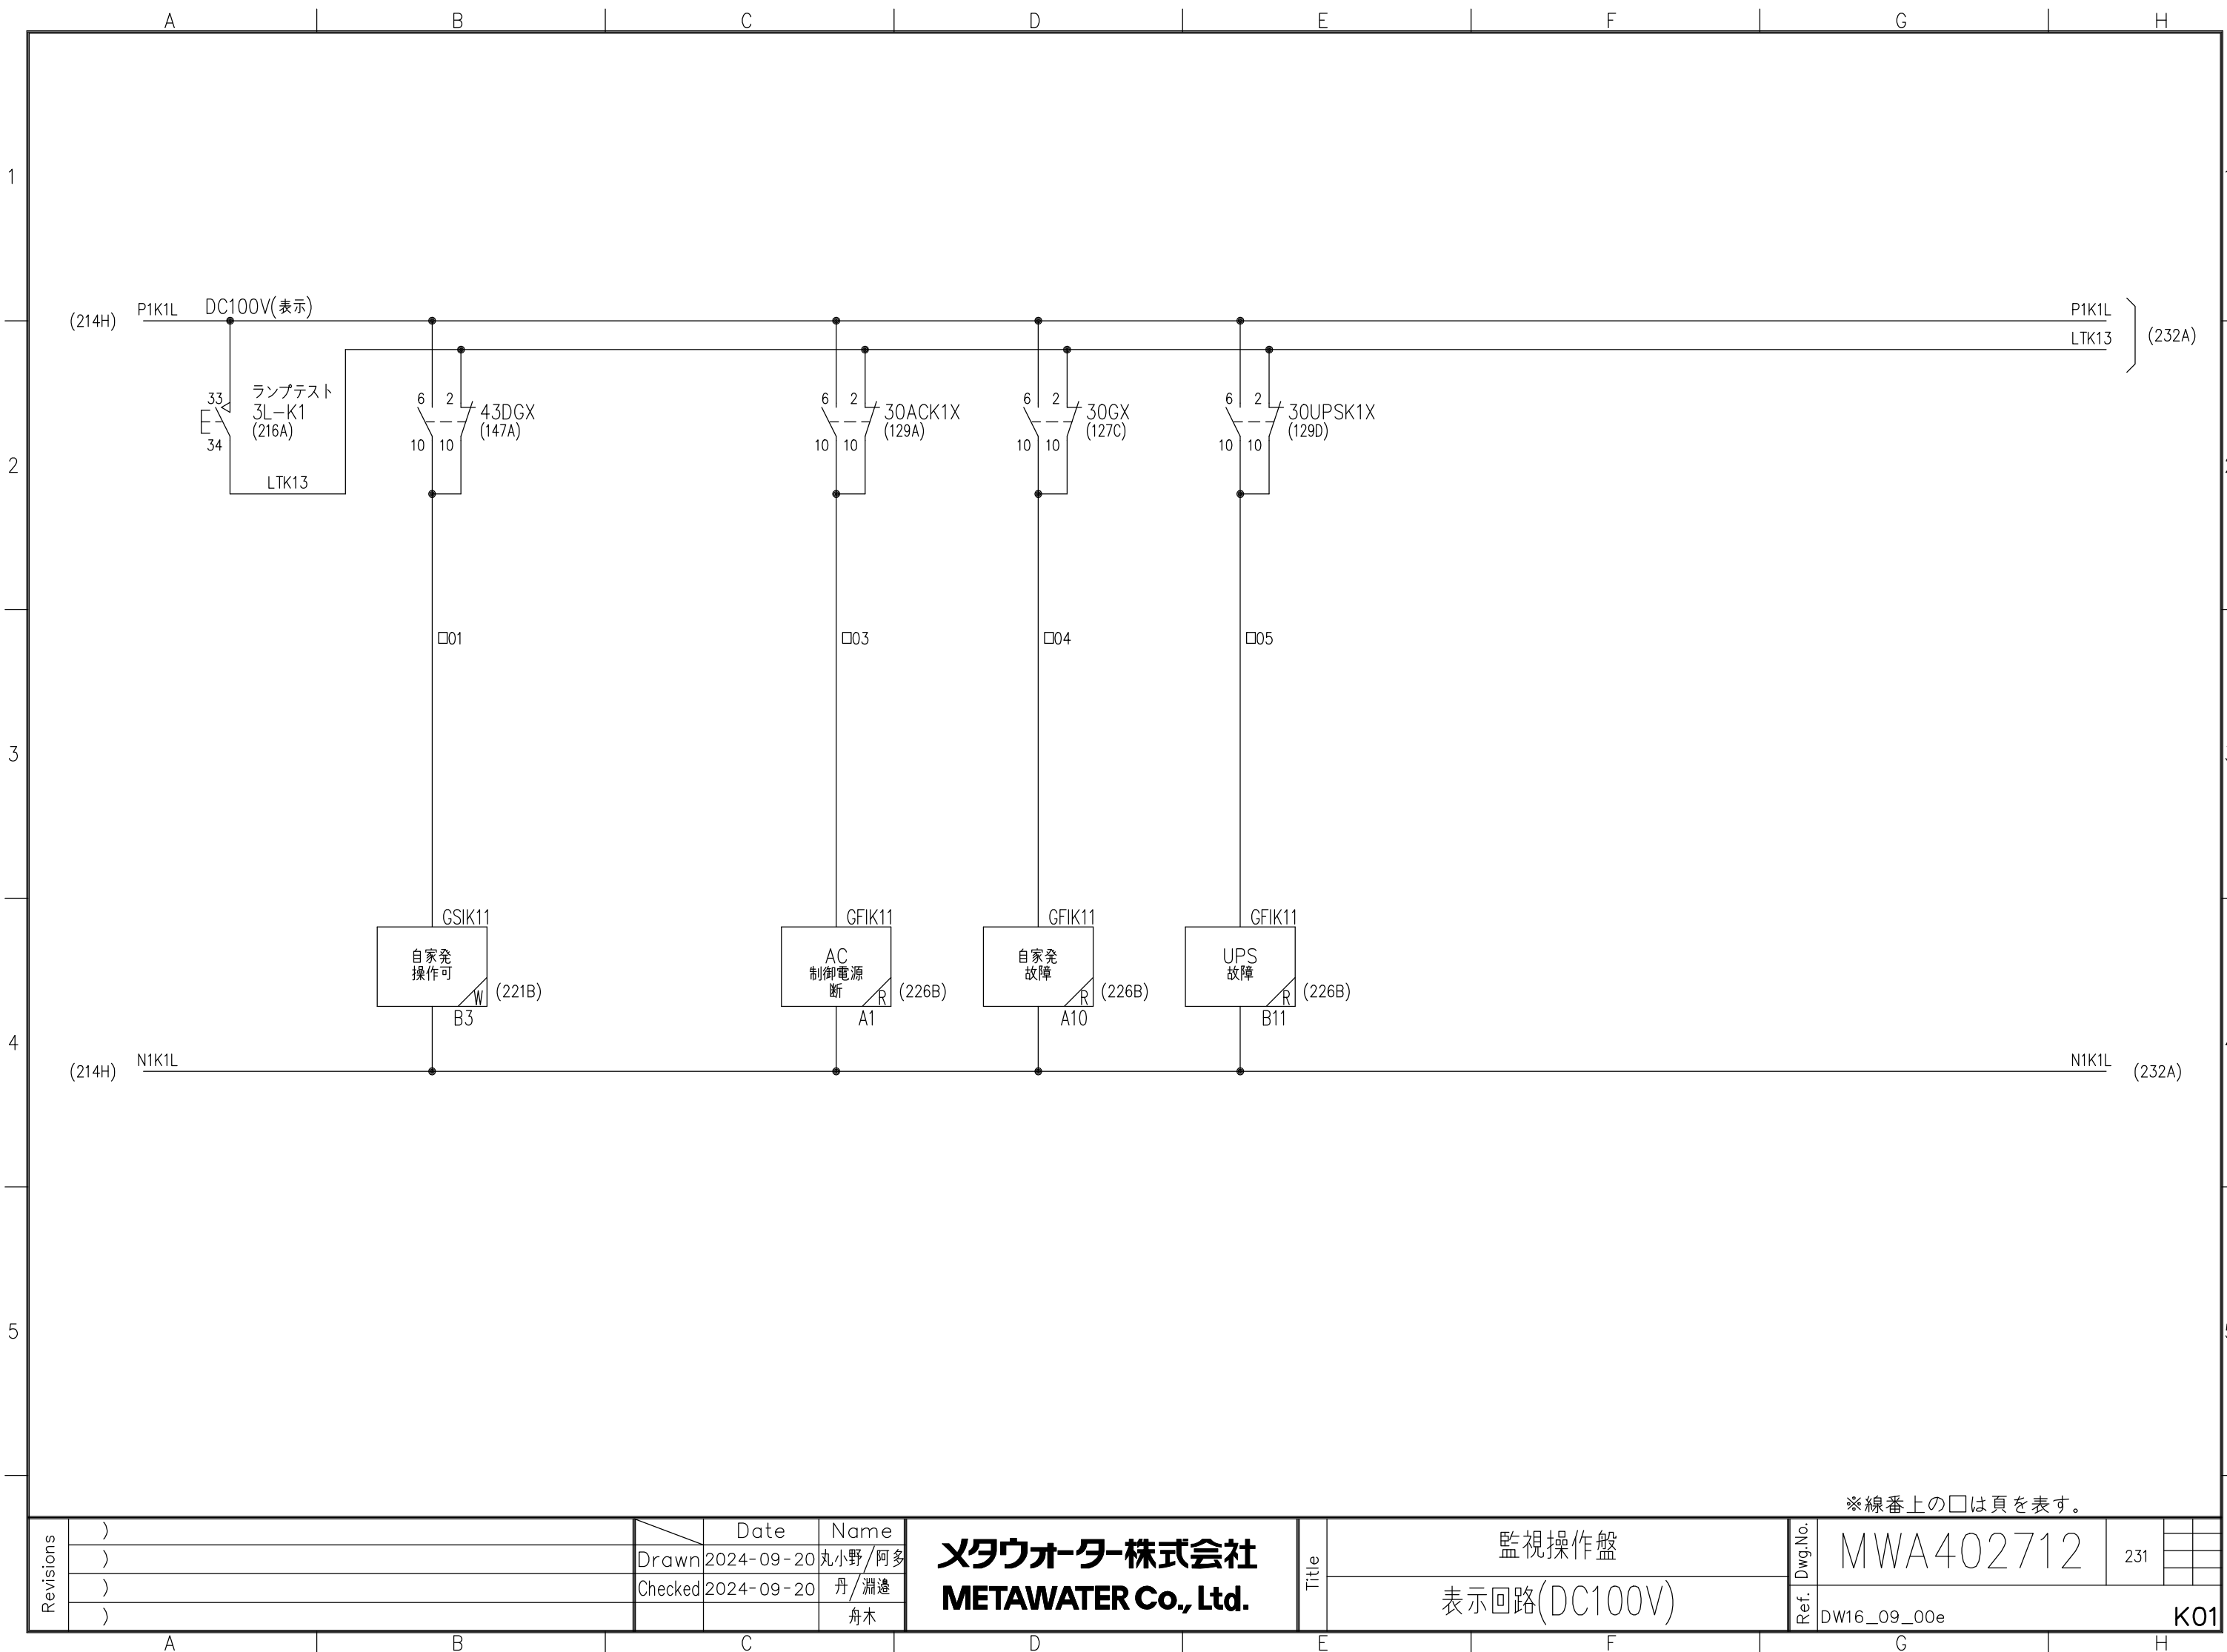



※線番上の□は頁を表す。


Revisions	)		Date	Name	メタウォーター株式会社 METAWATER Co., Ltd.	Title	監視操作盤		Dwg.No.	MWA402712	231	
	)	Drawn	2024-09-20	丸小野/阿多			表示回路(DC100V)		Ref.	DW16_09_00e		
	)	Checked	2024-09-20	丹/淵邊								
	)			舟木				K01				

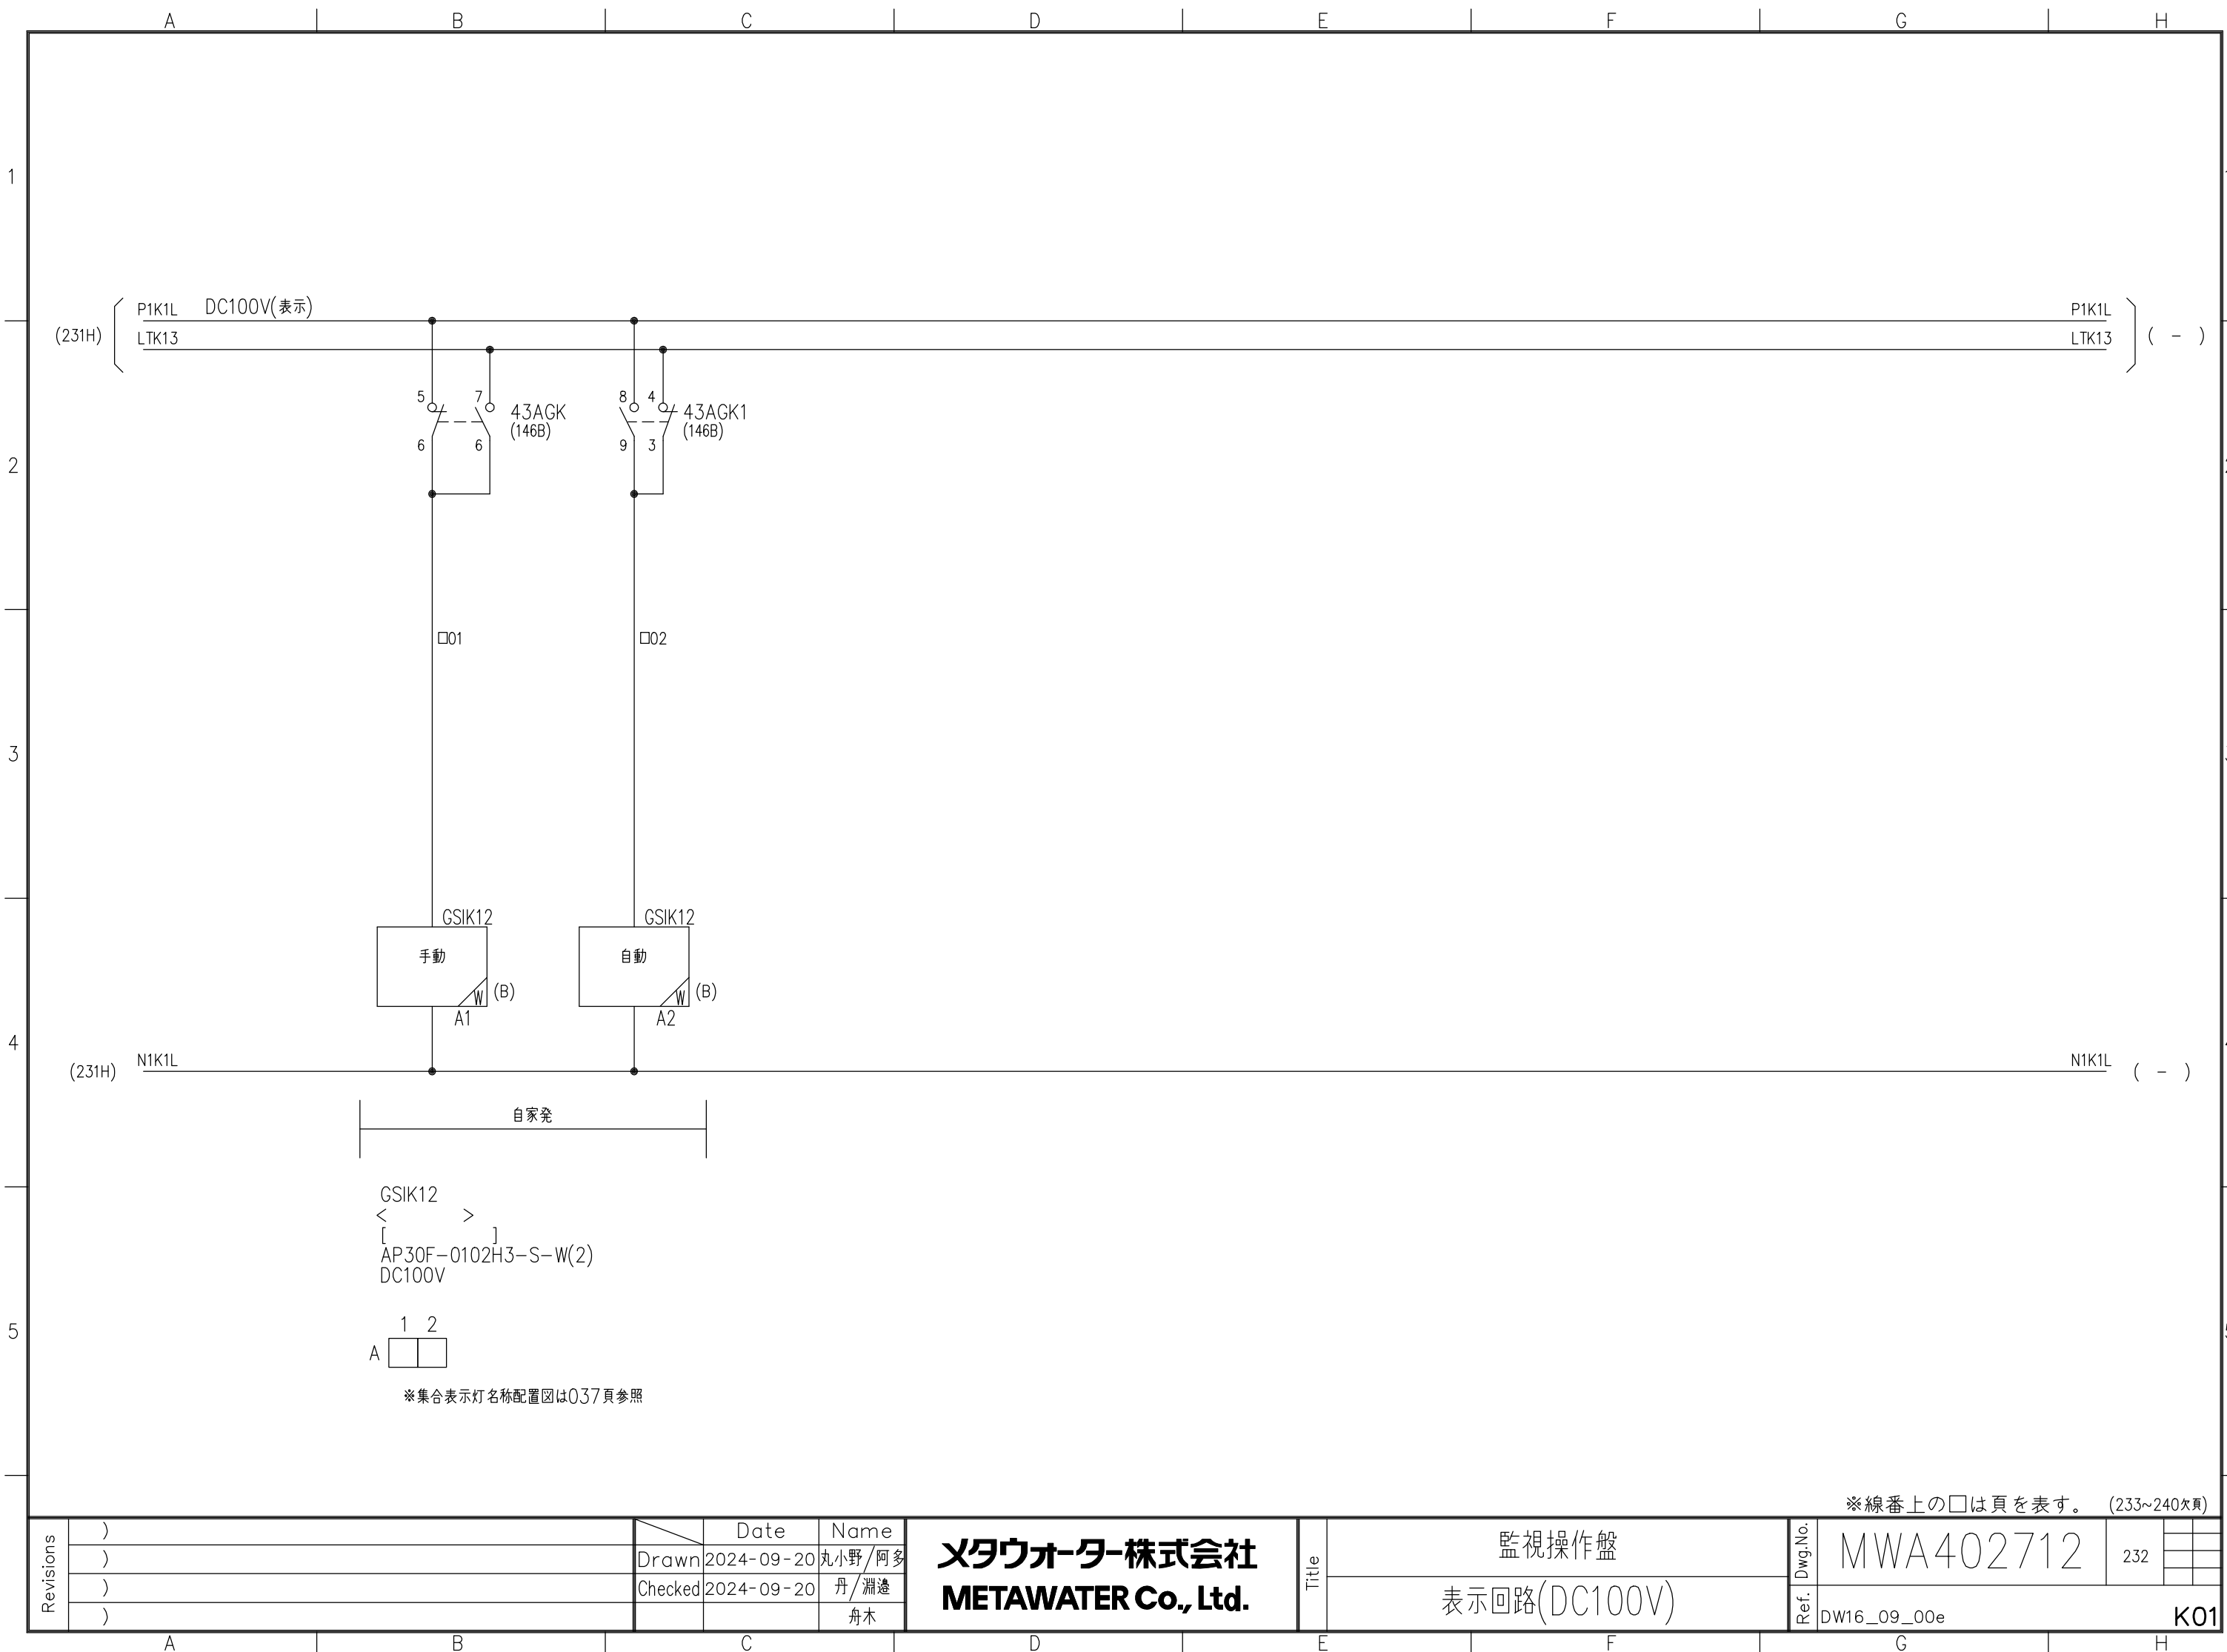


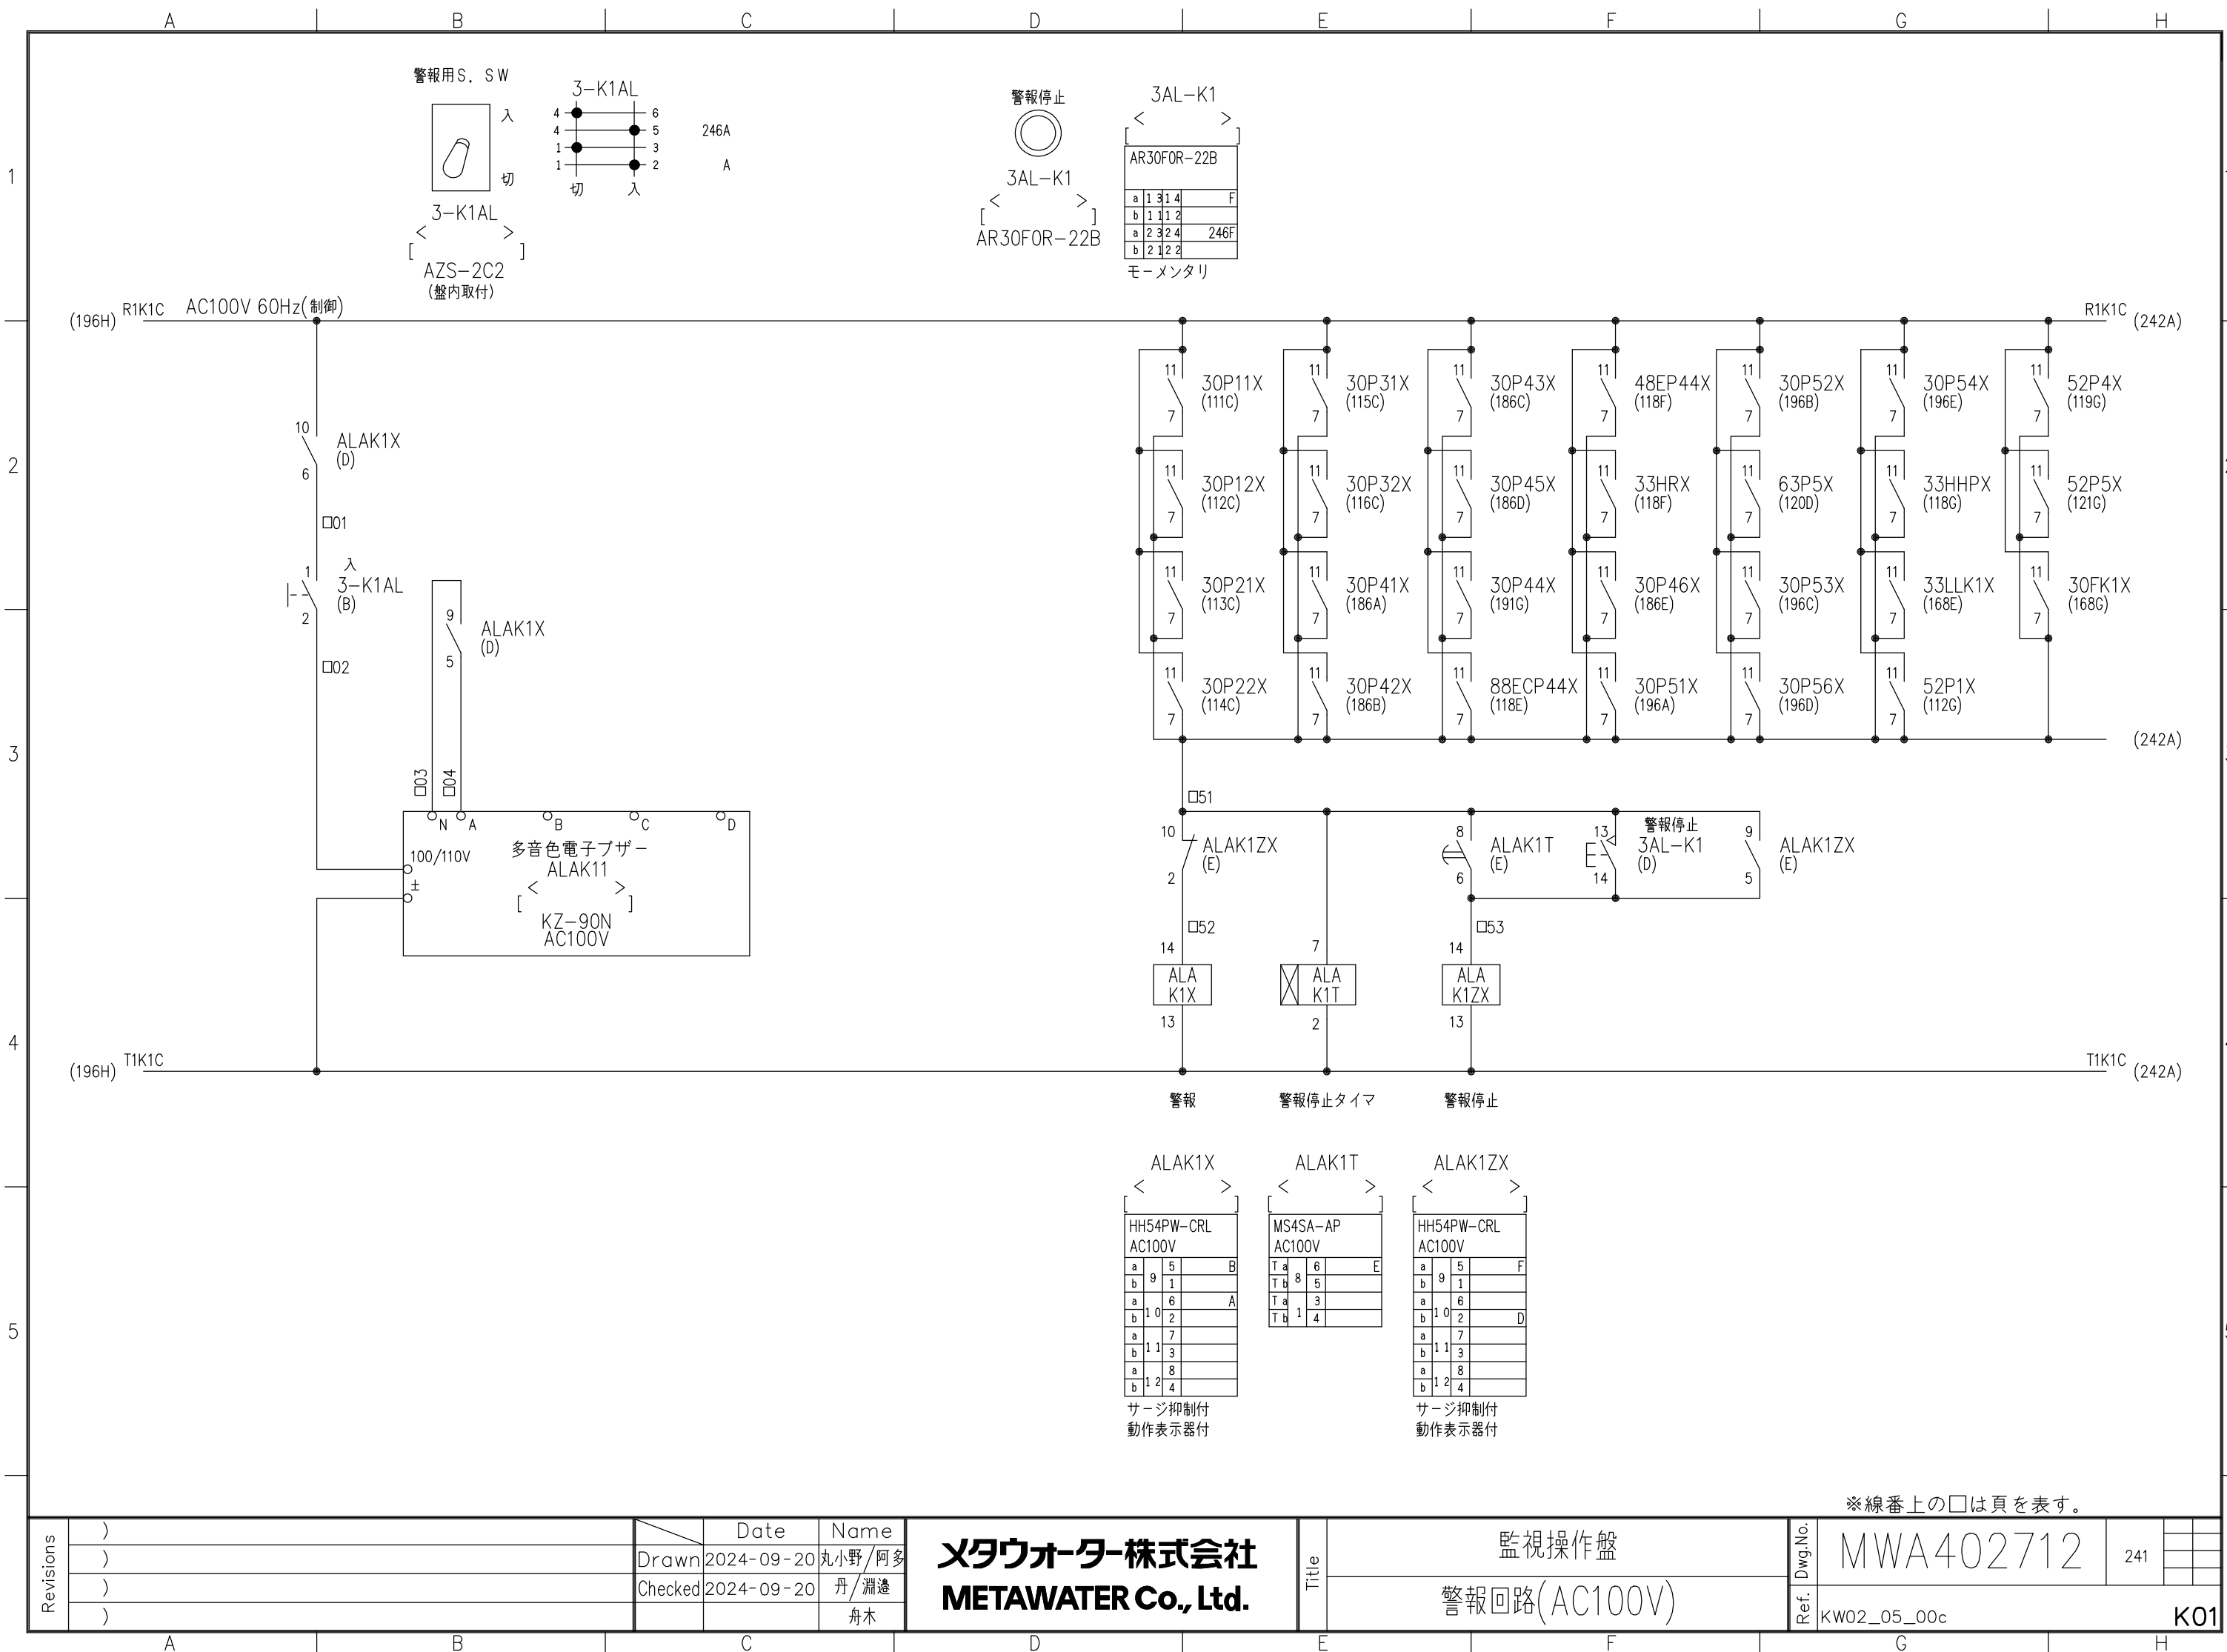


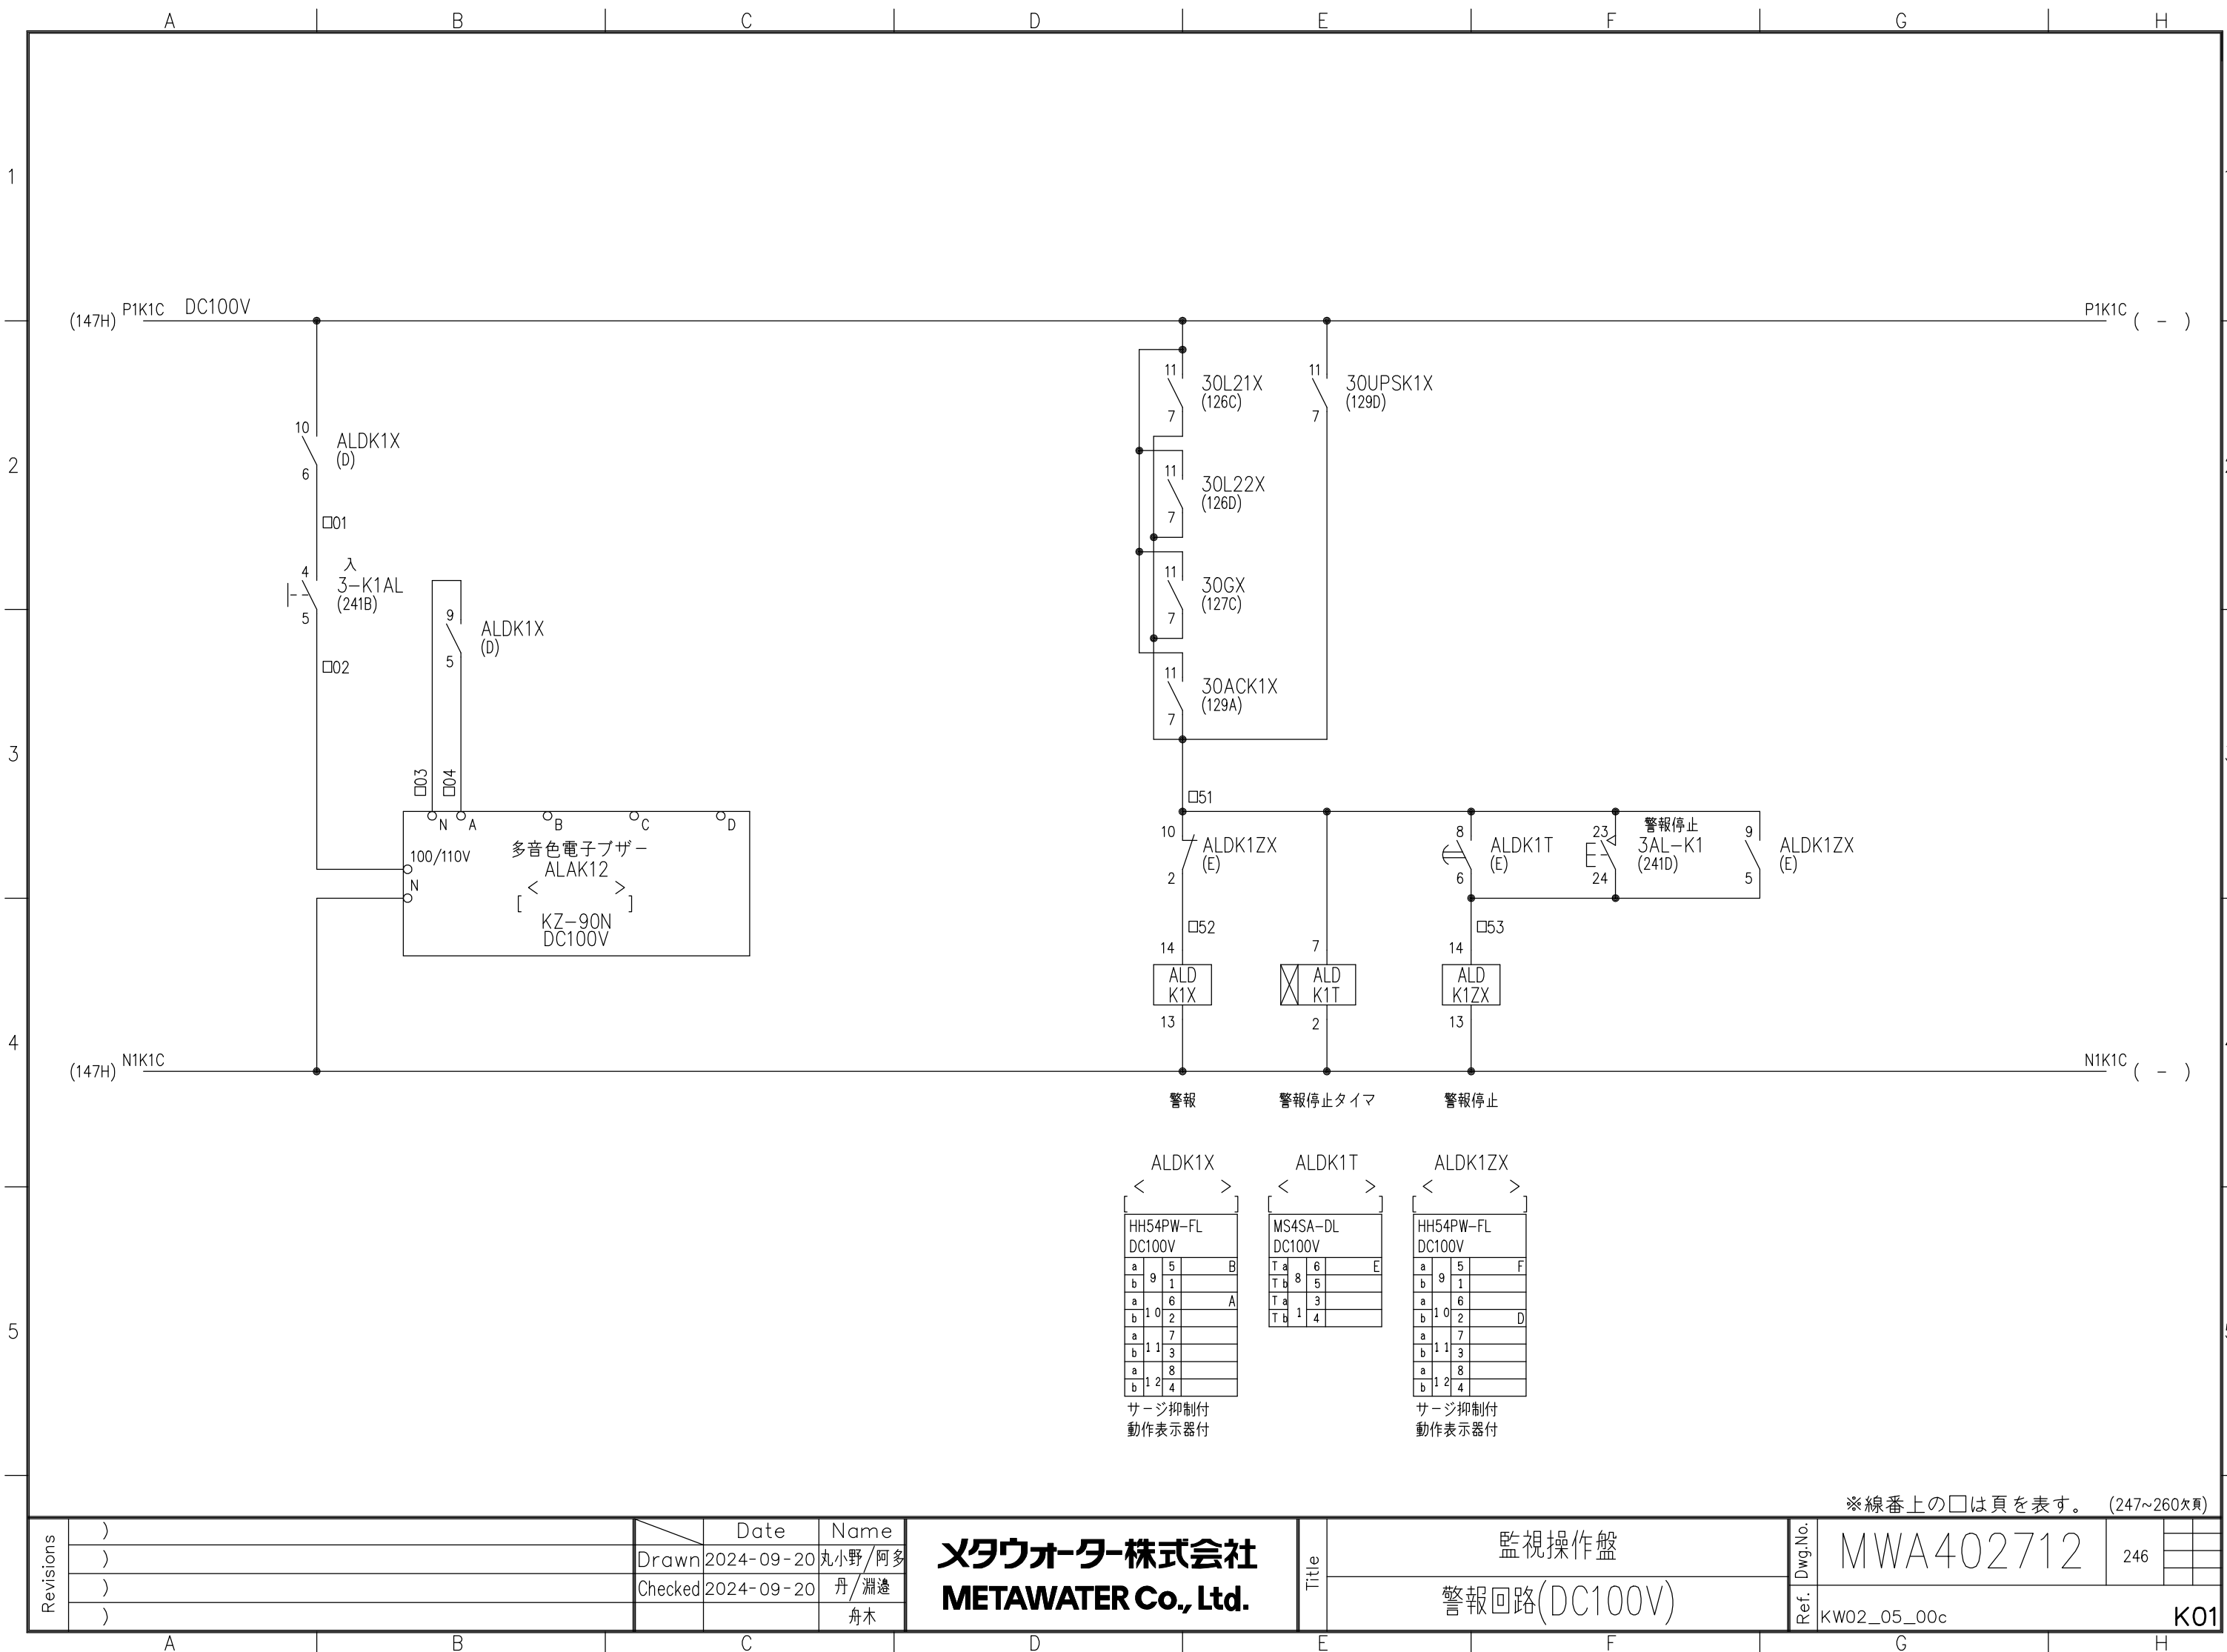


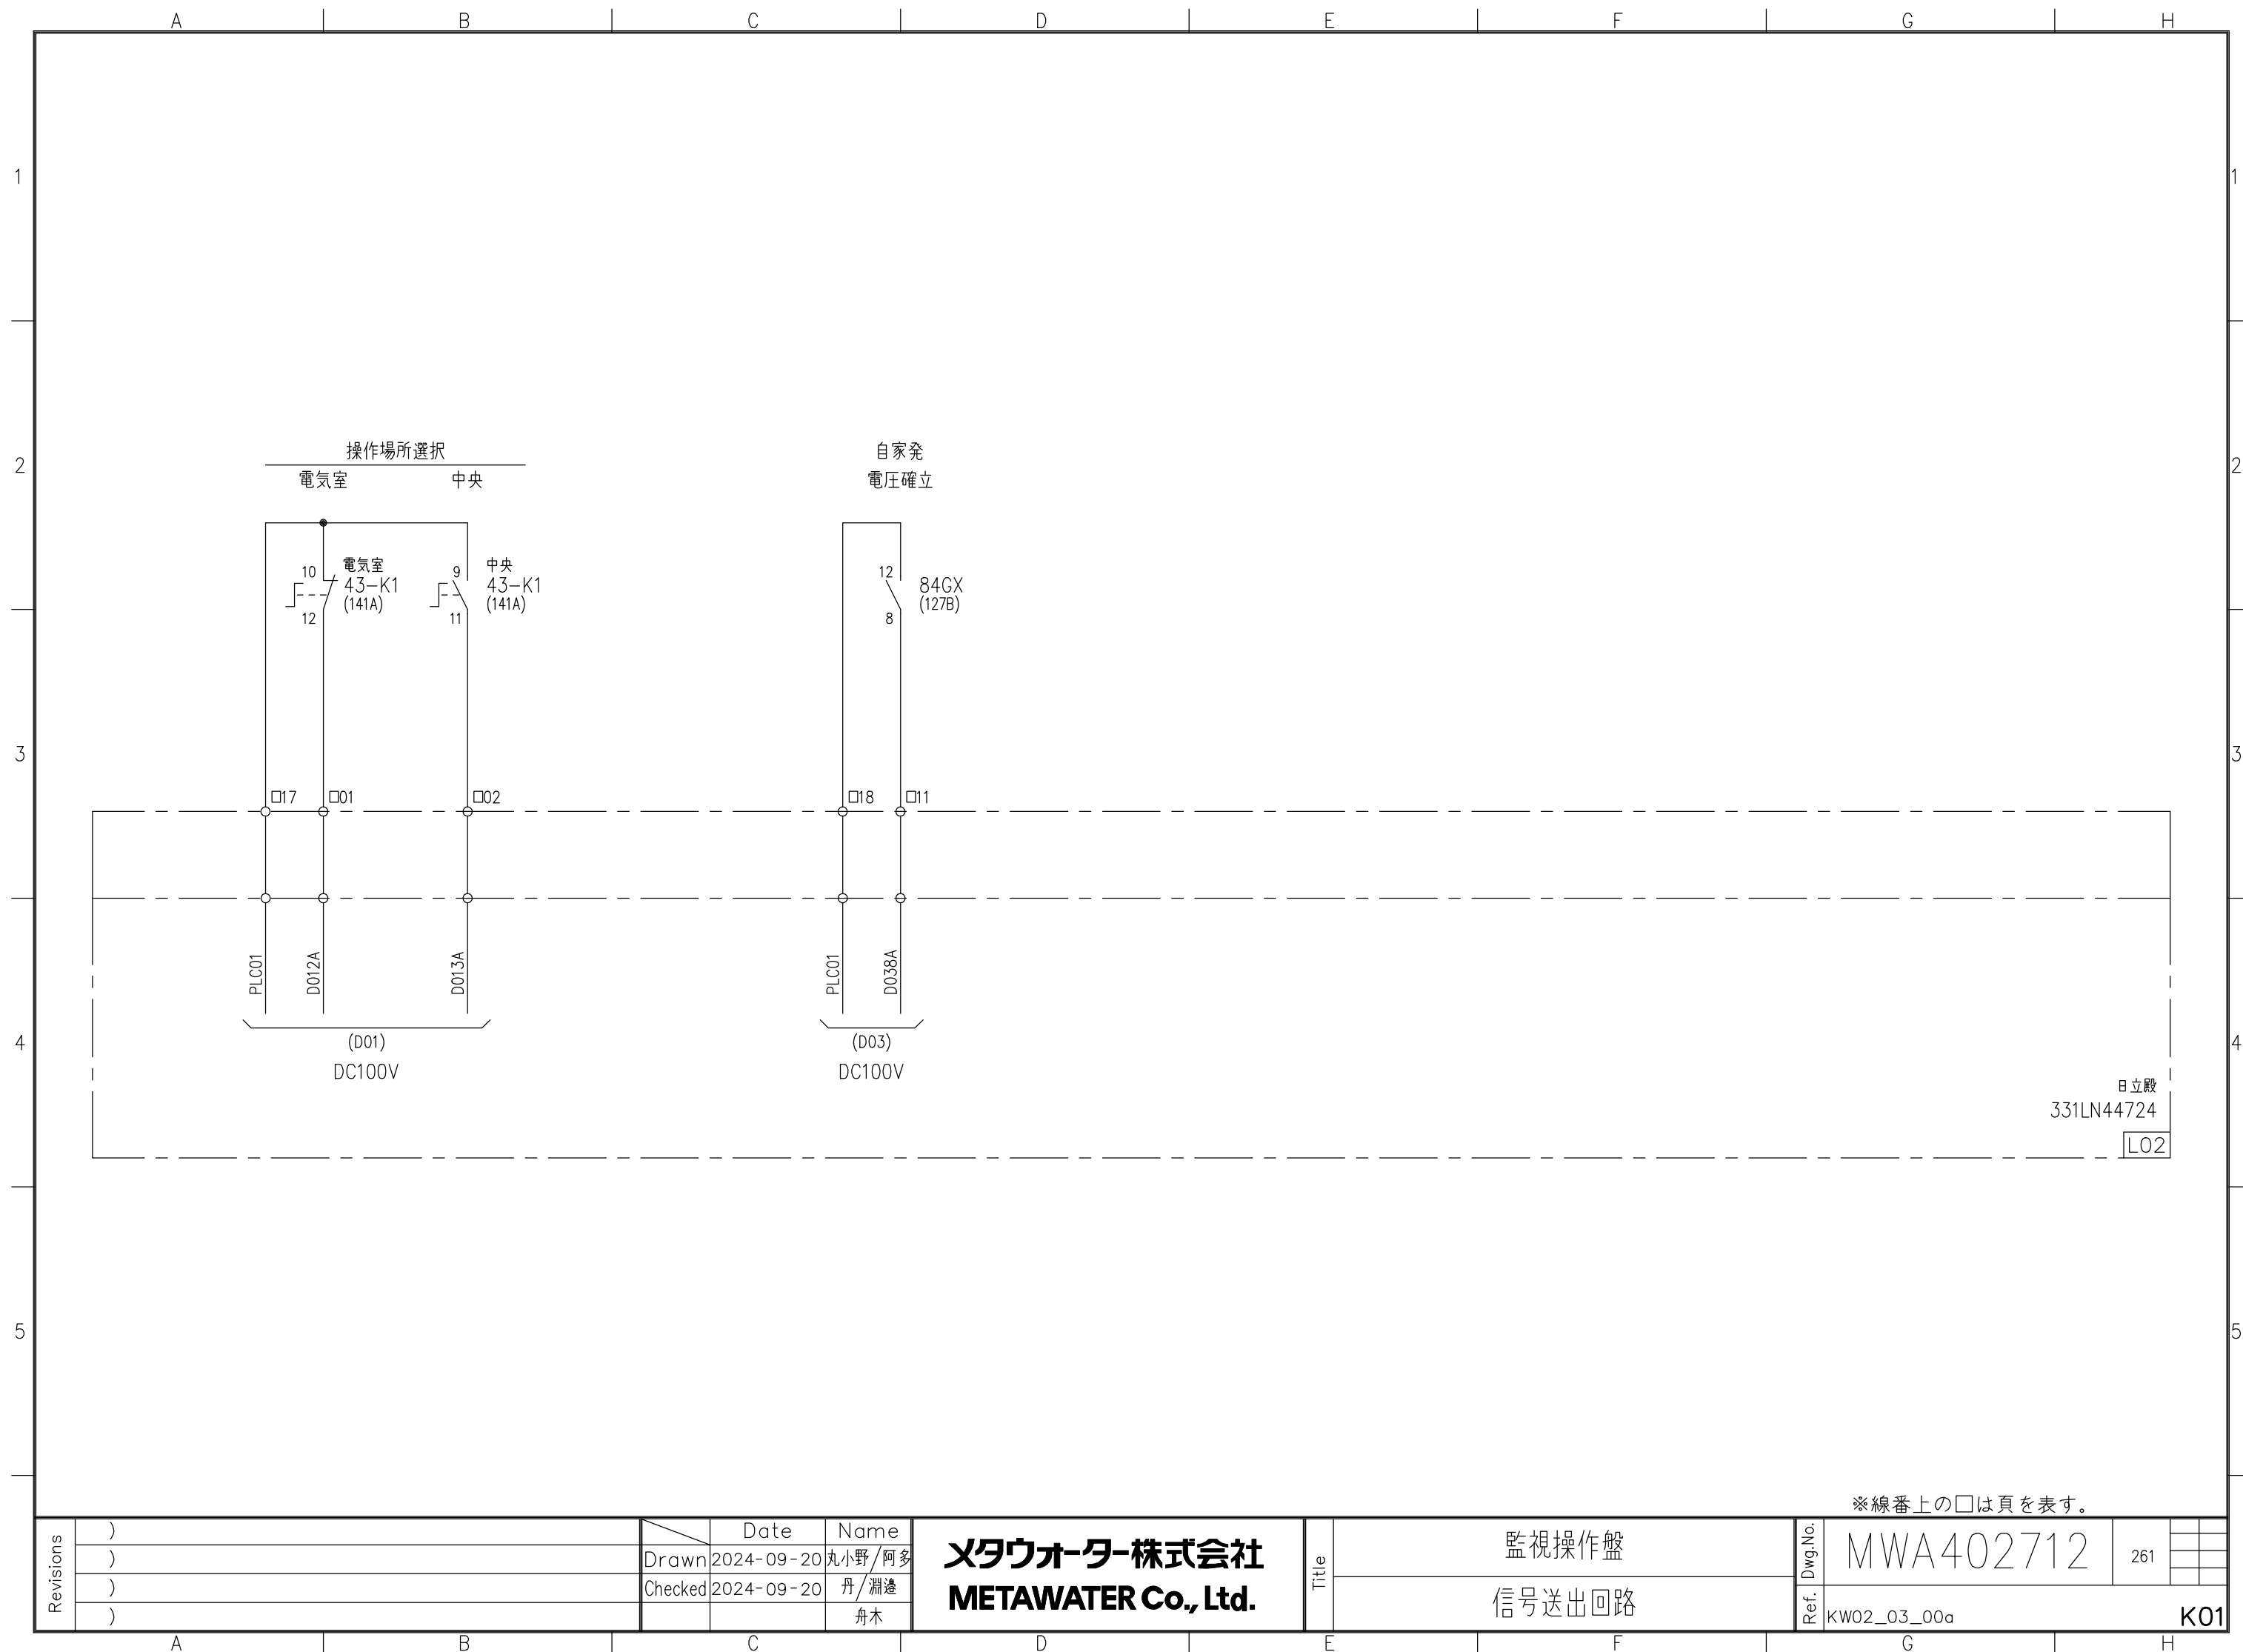


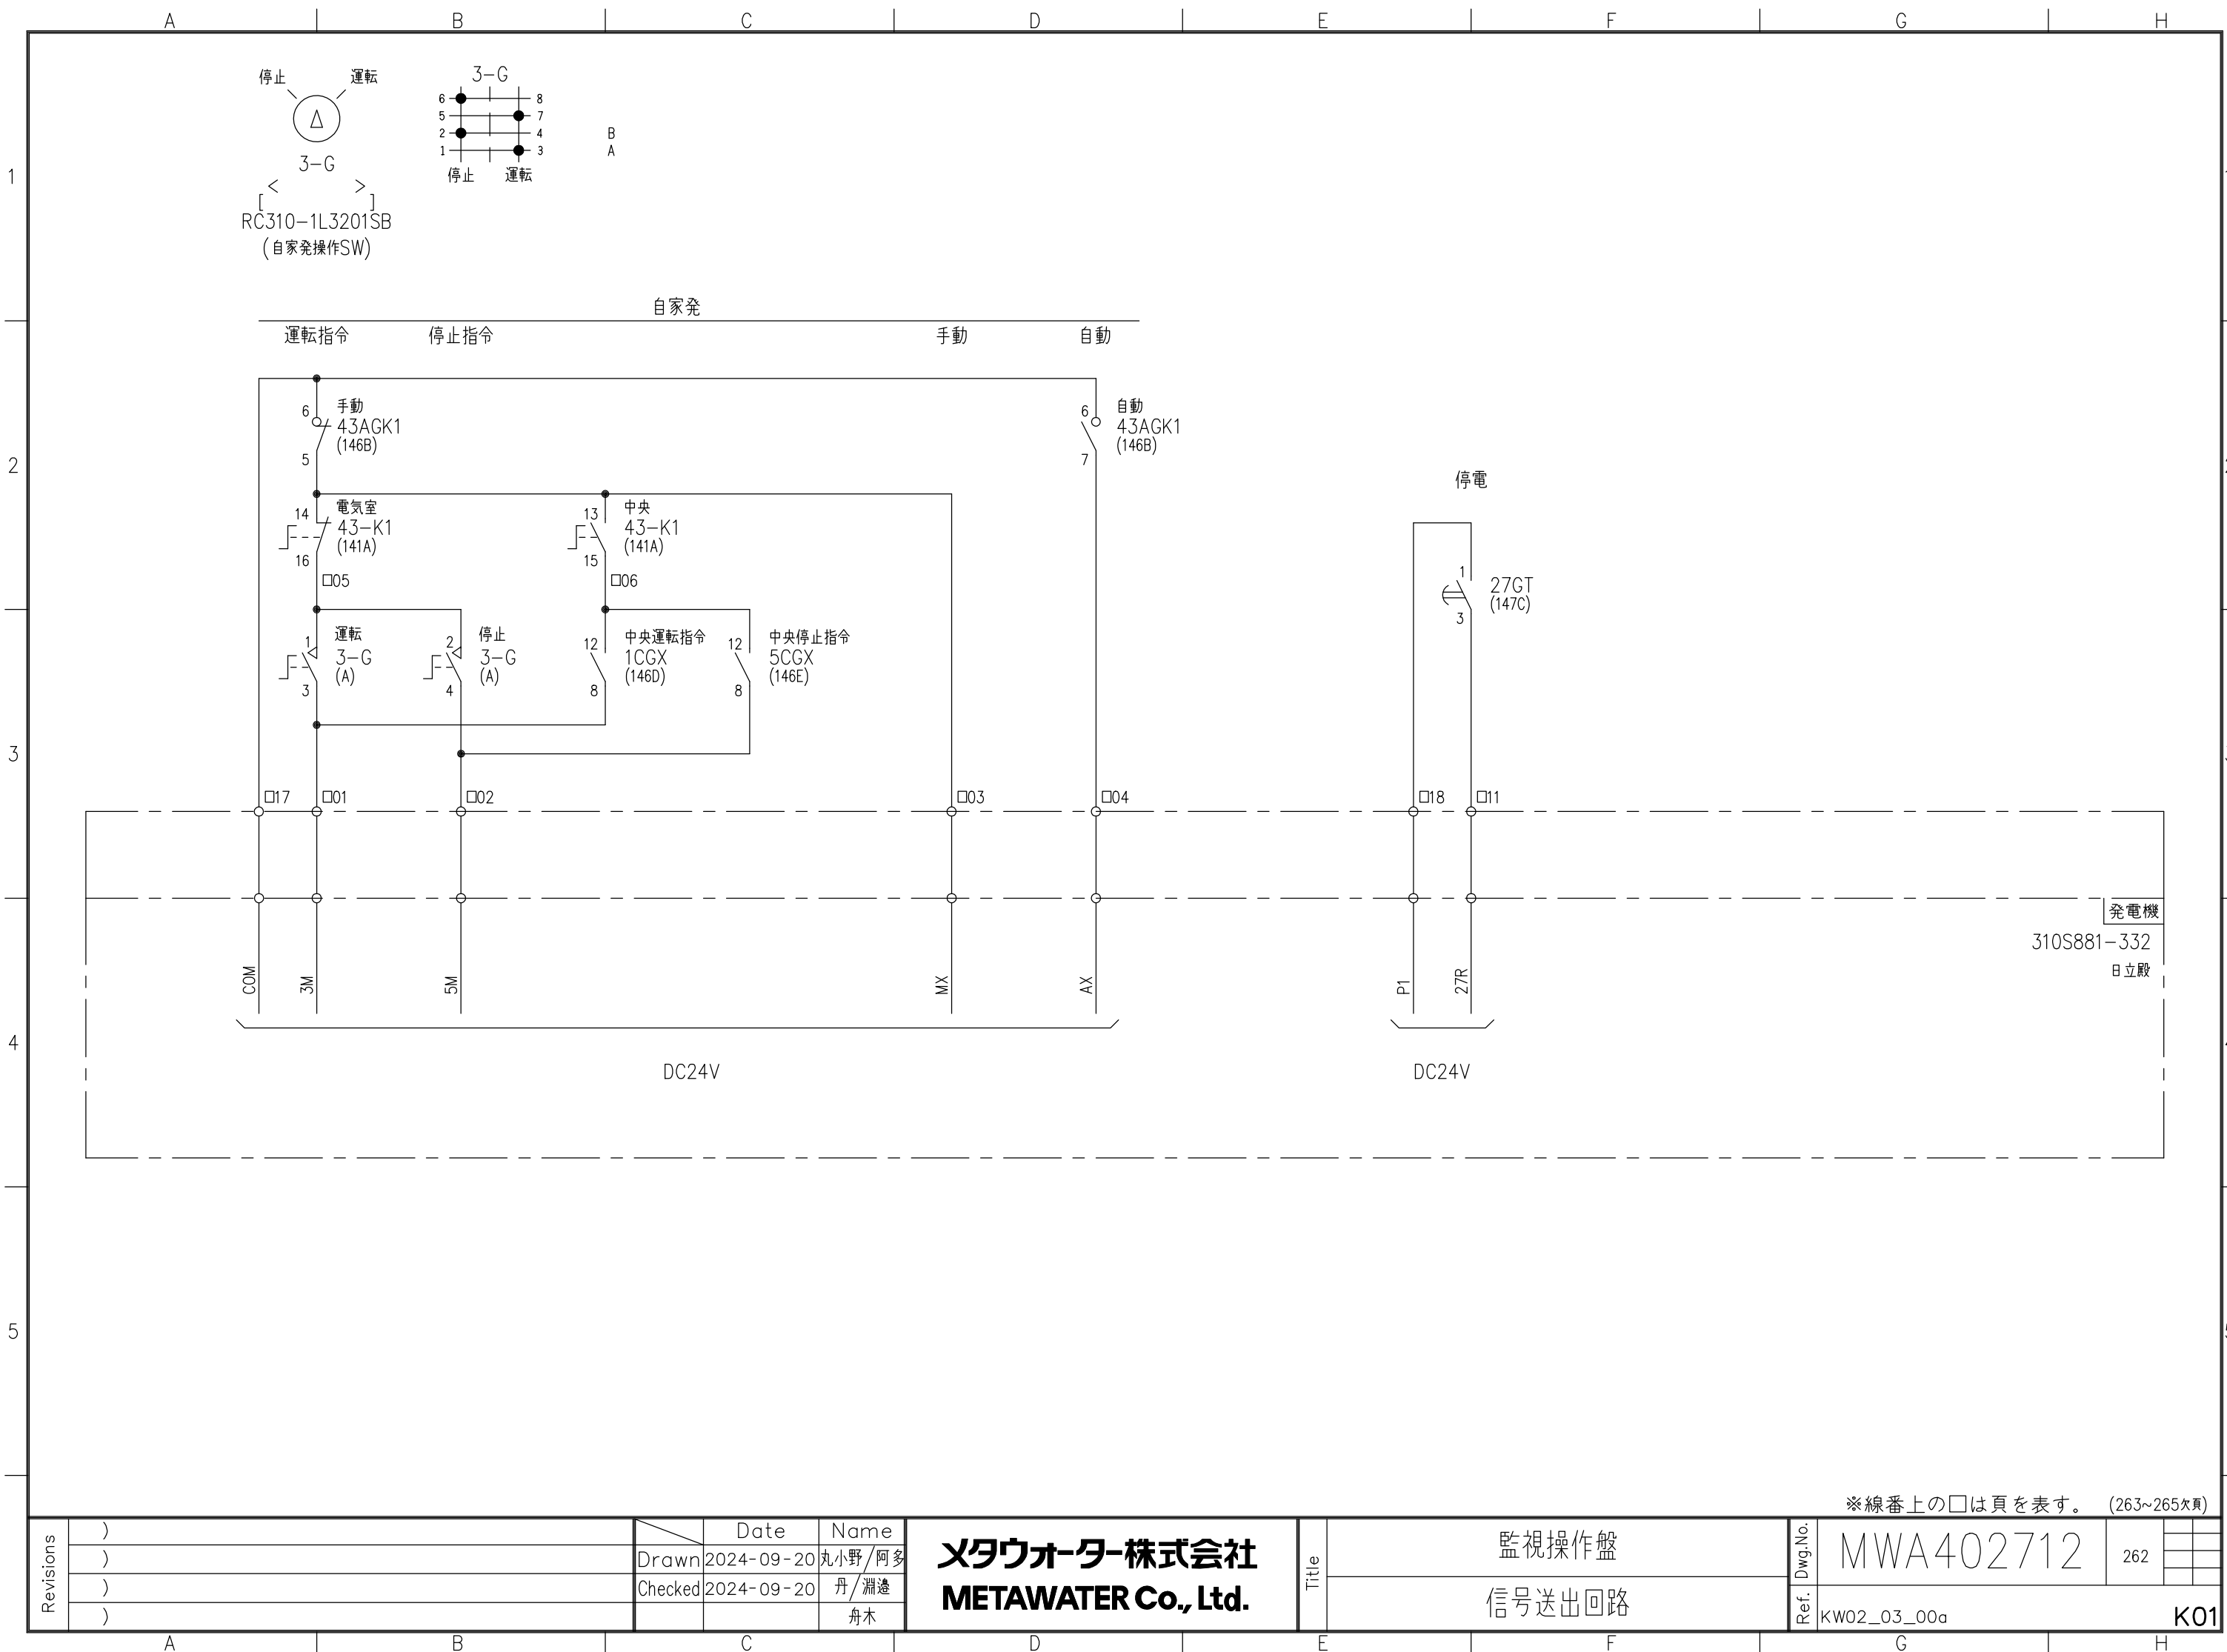

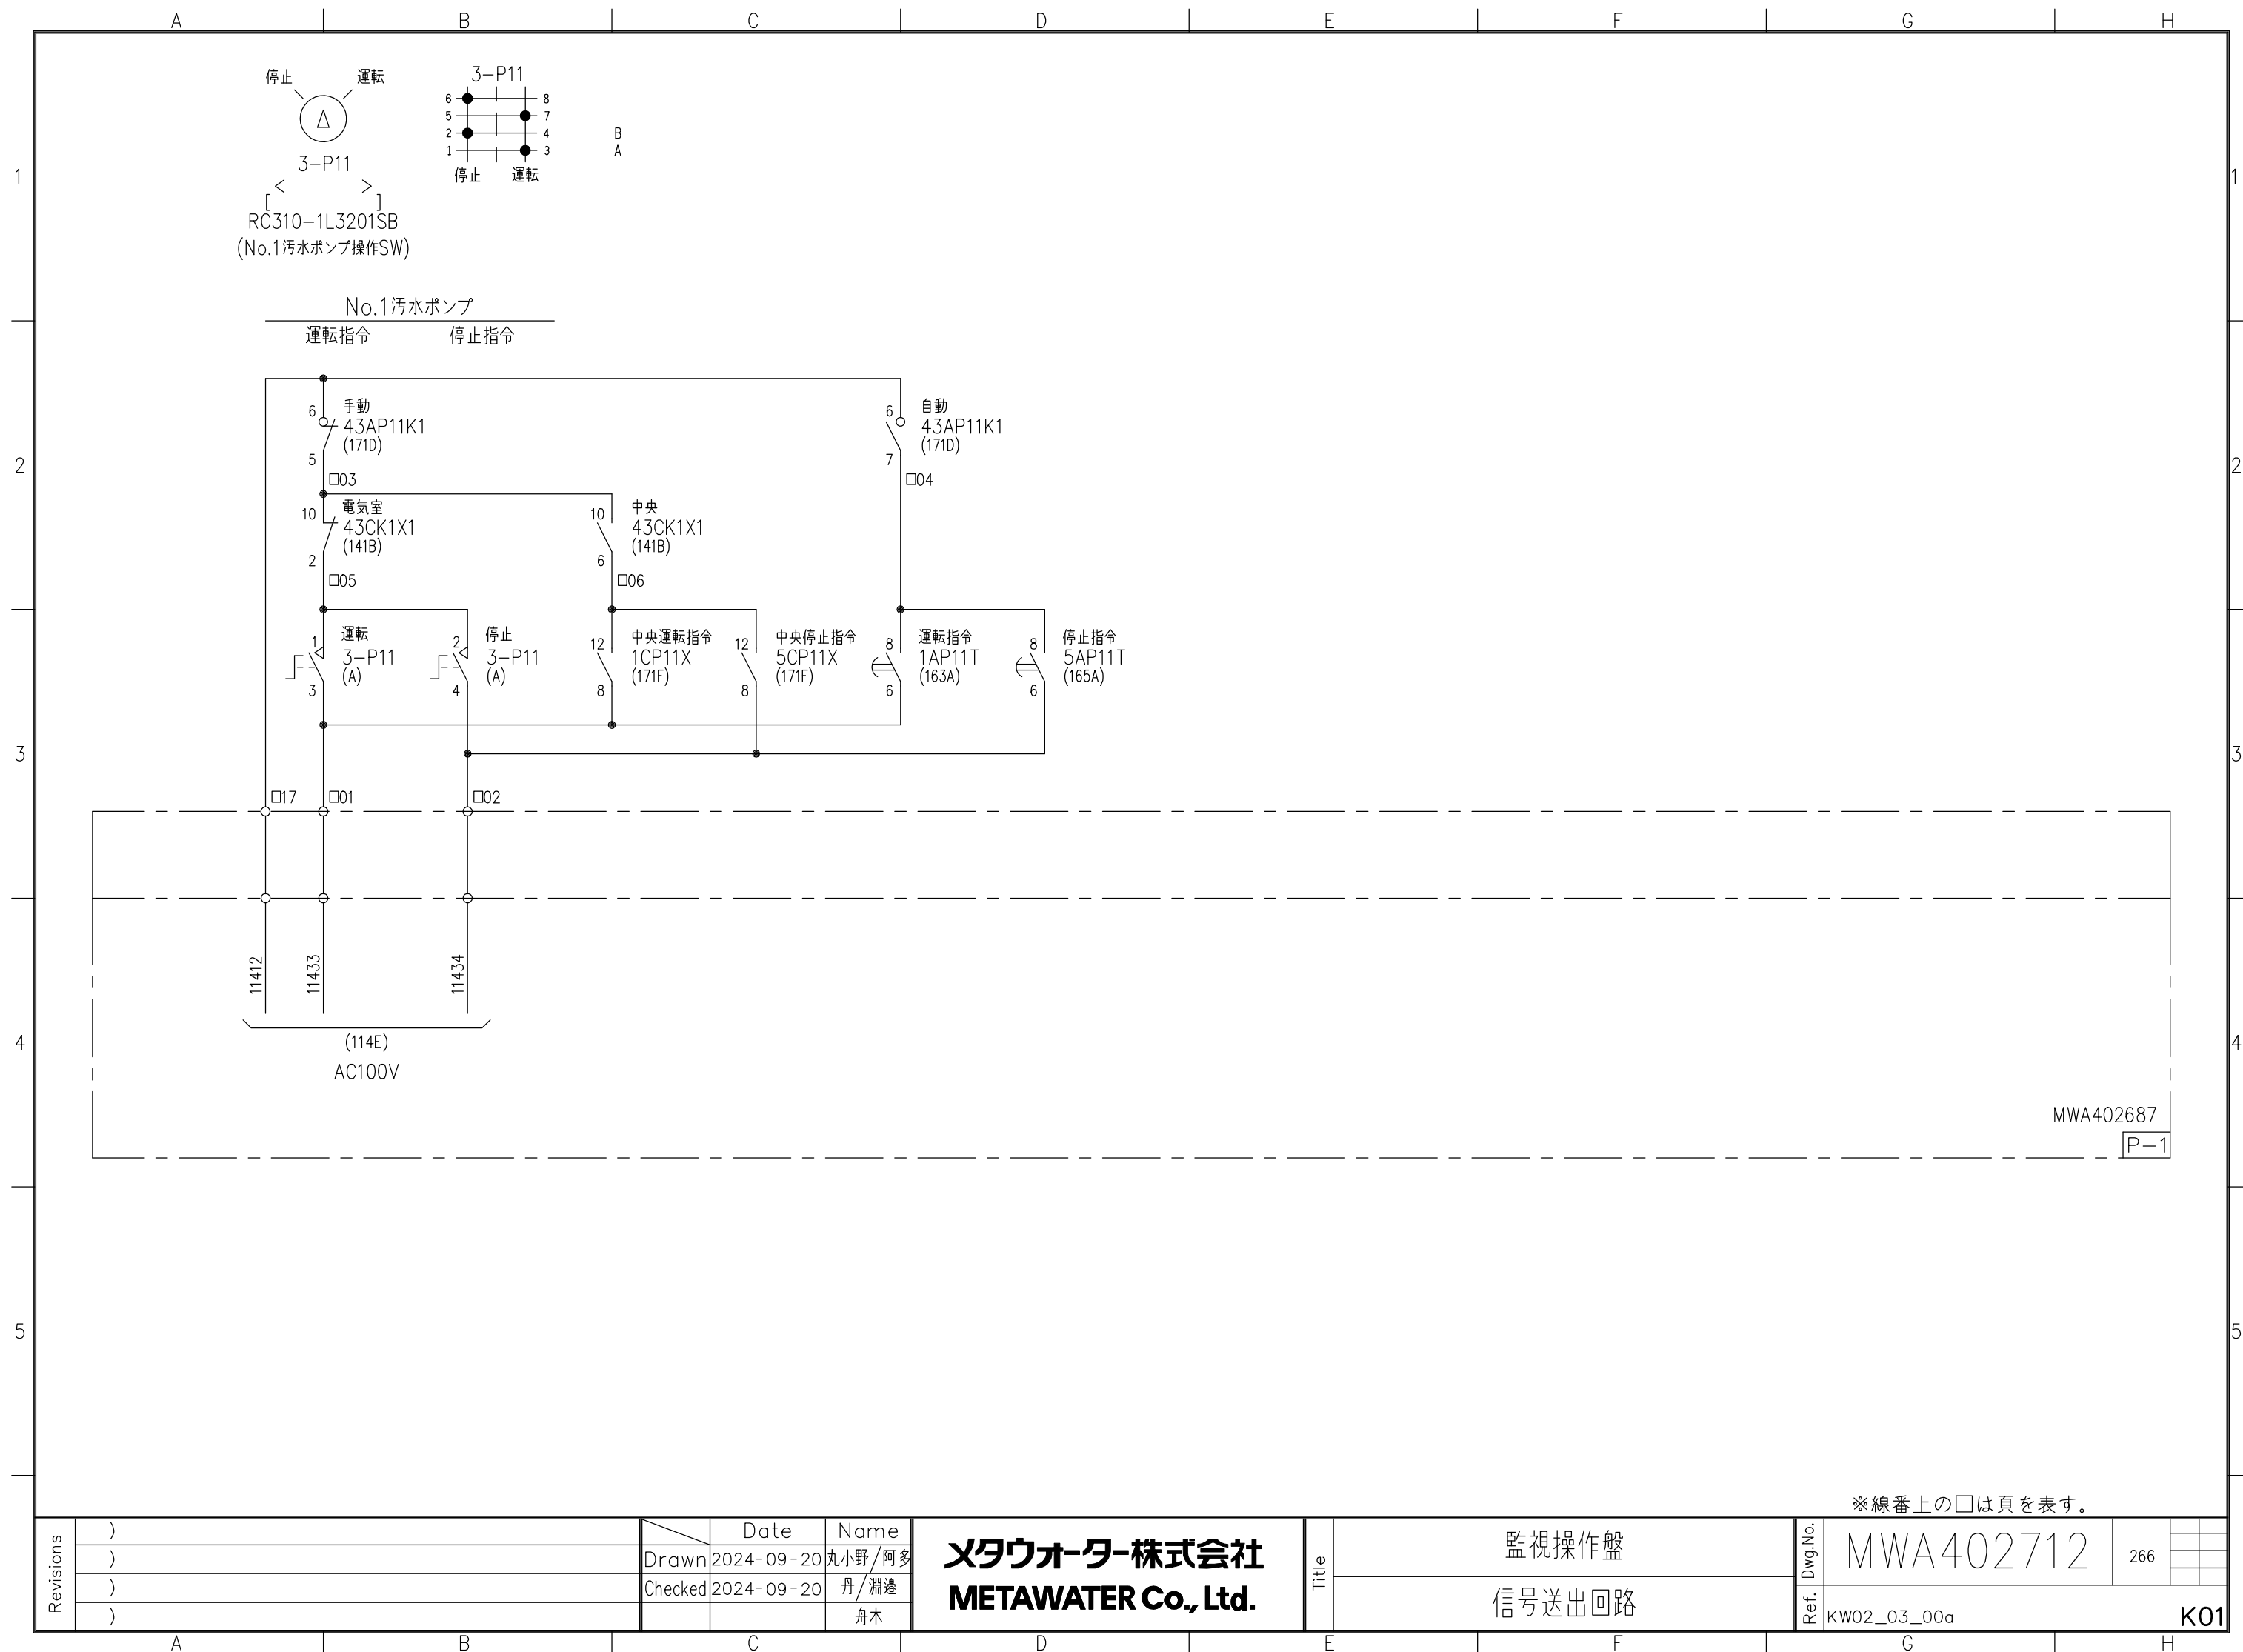

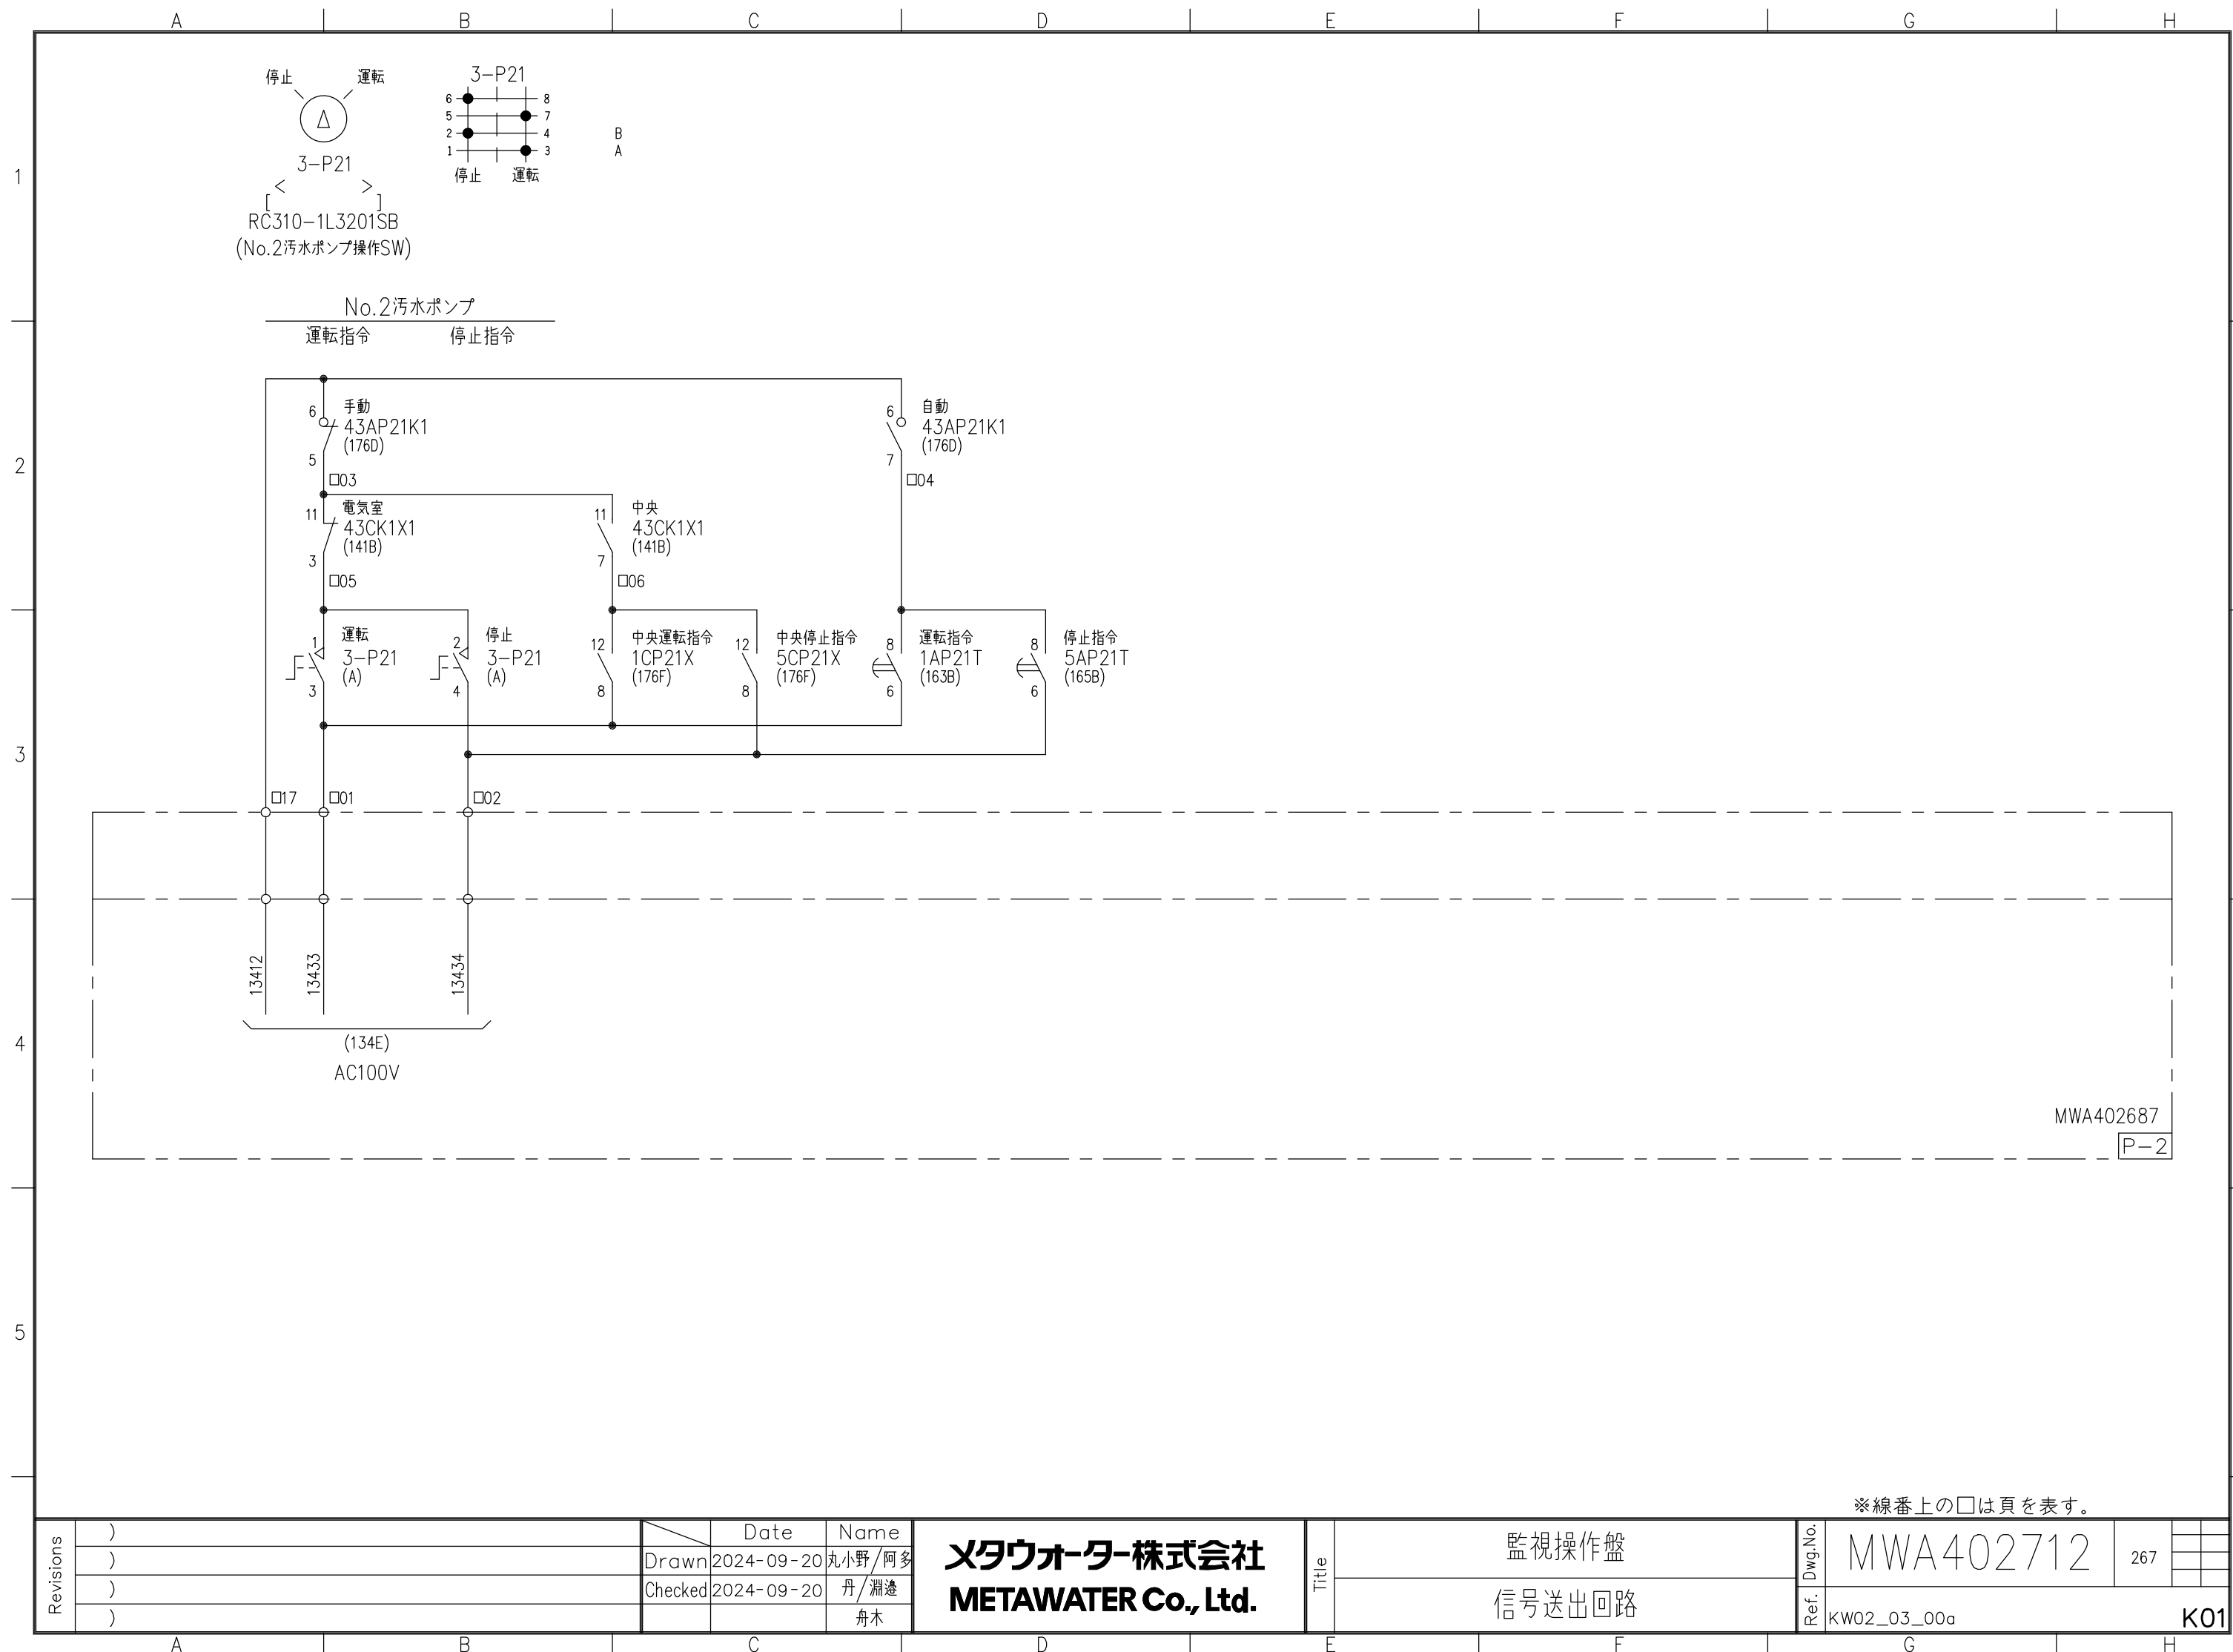

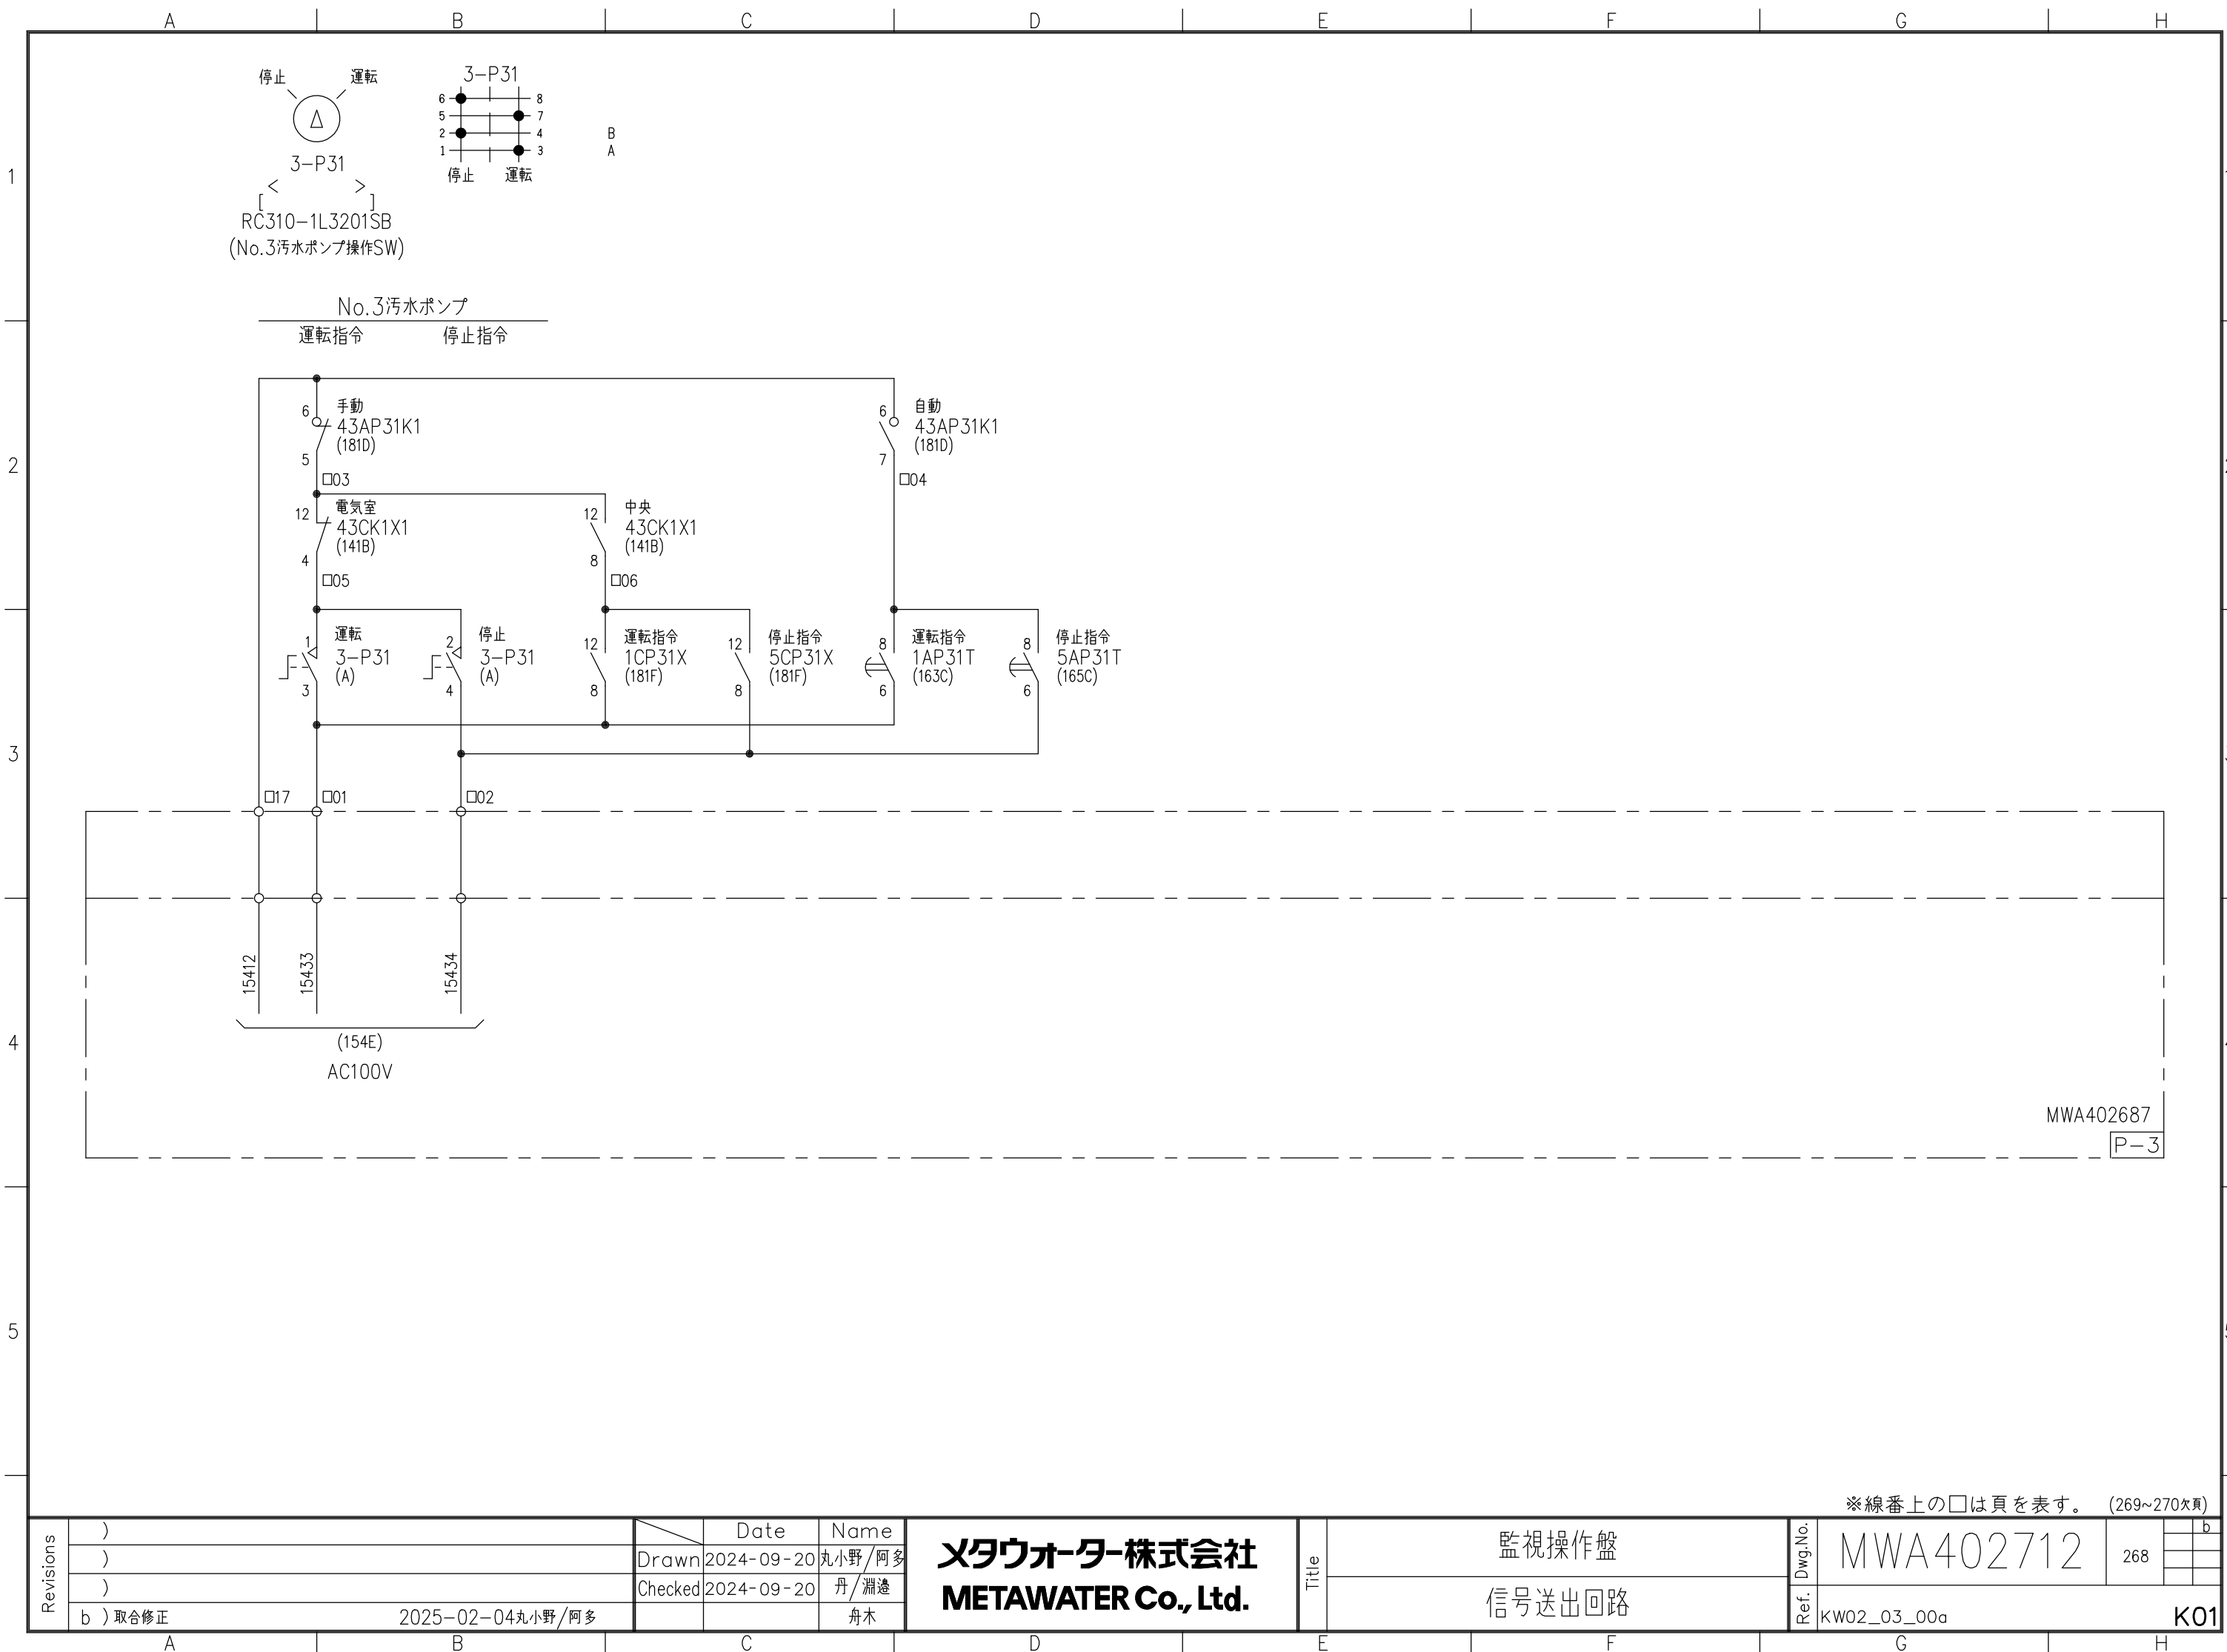

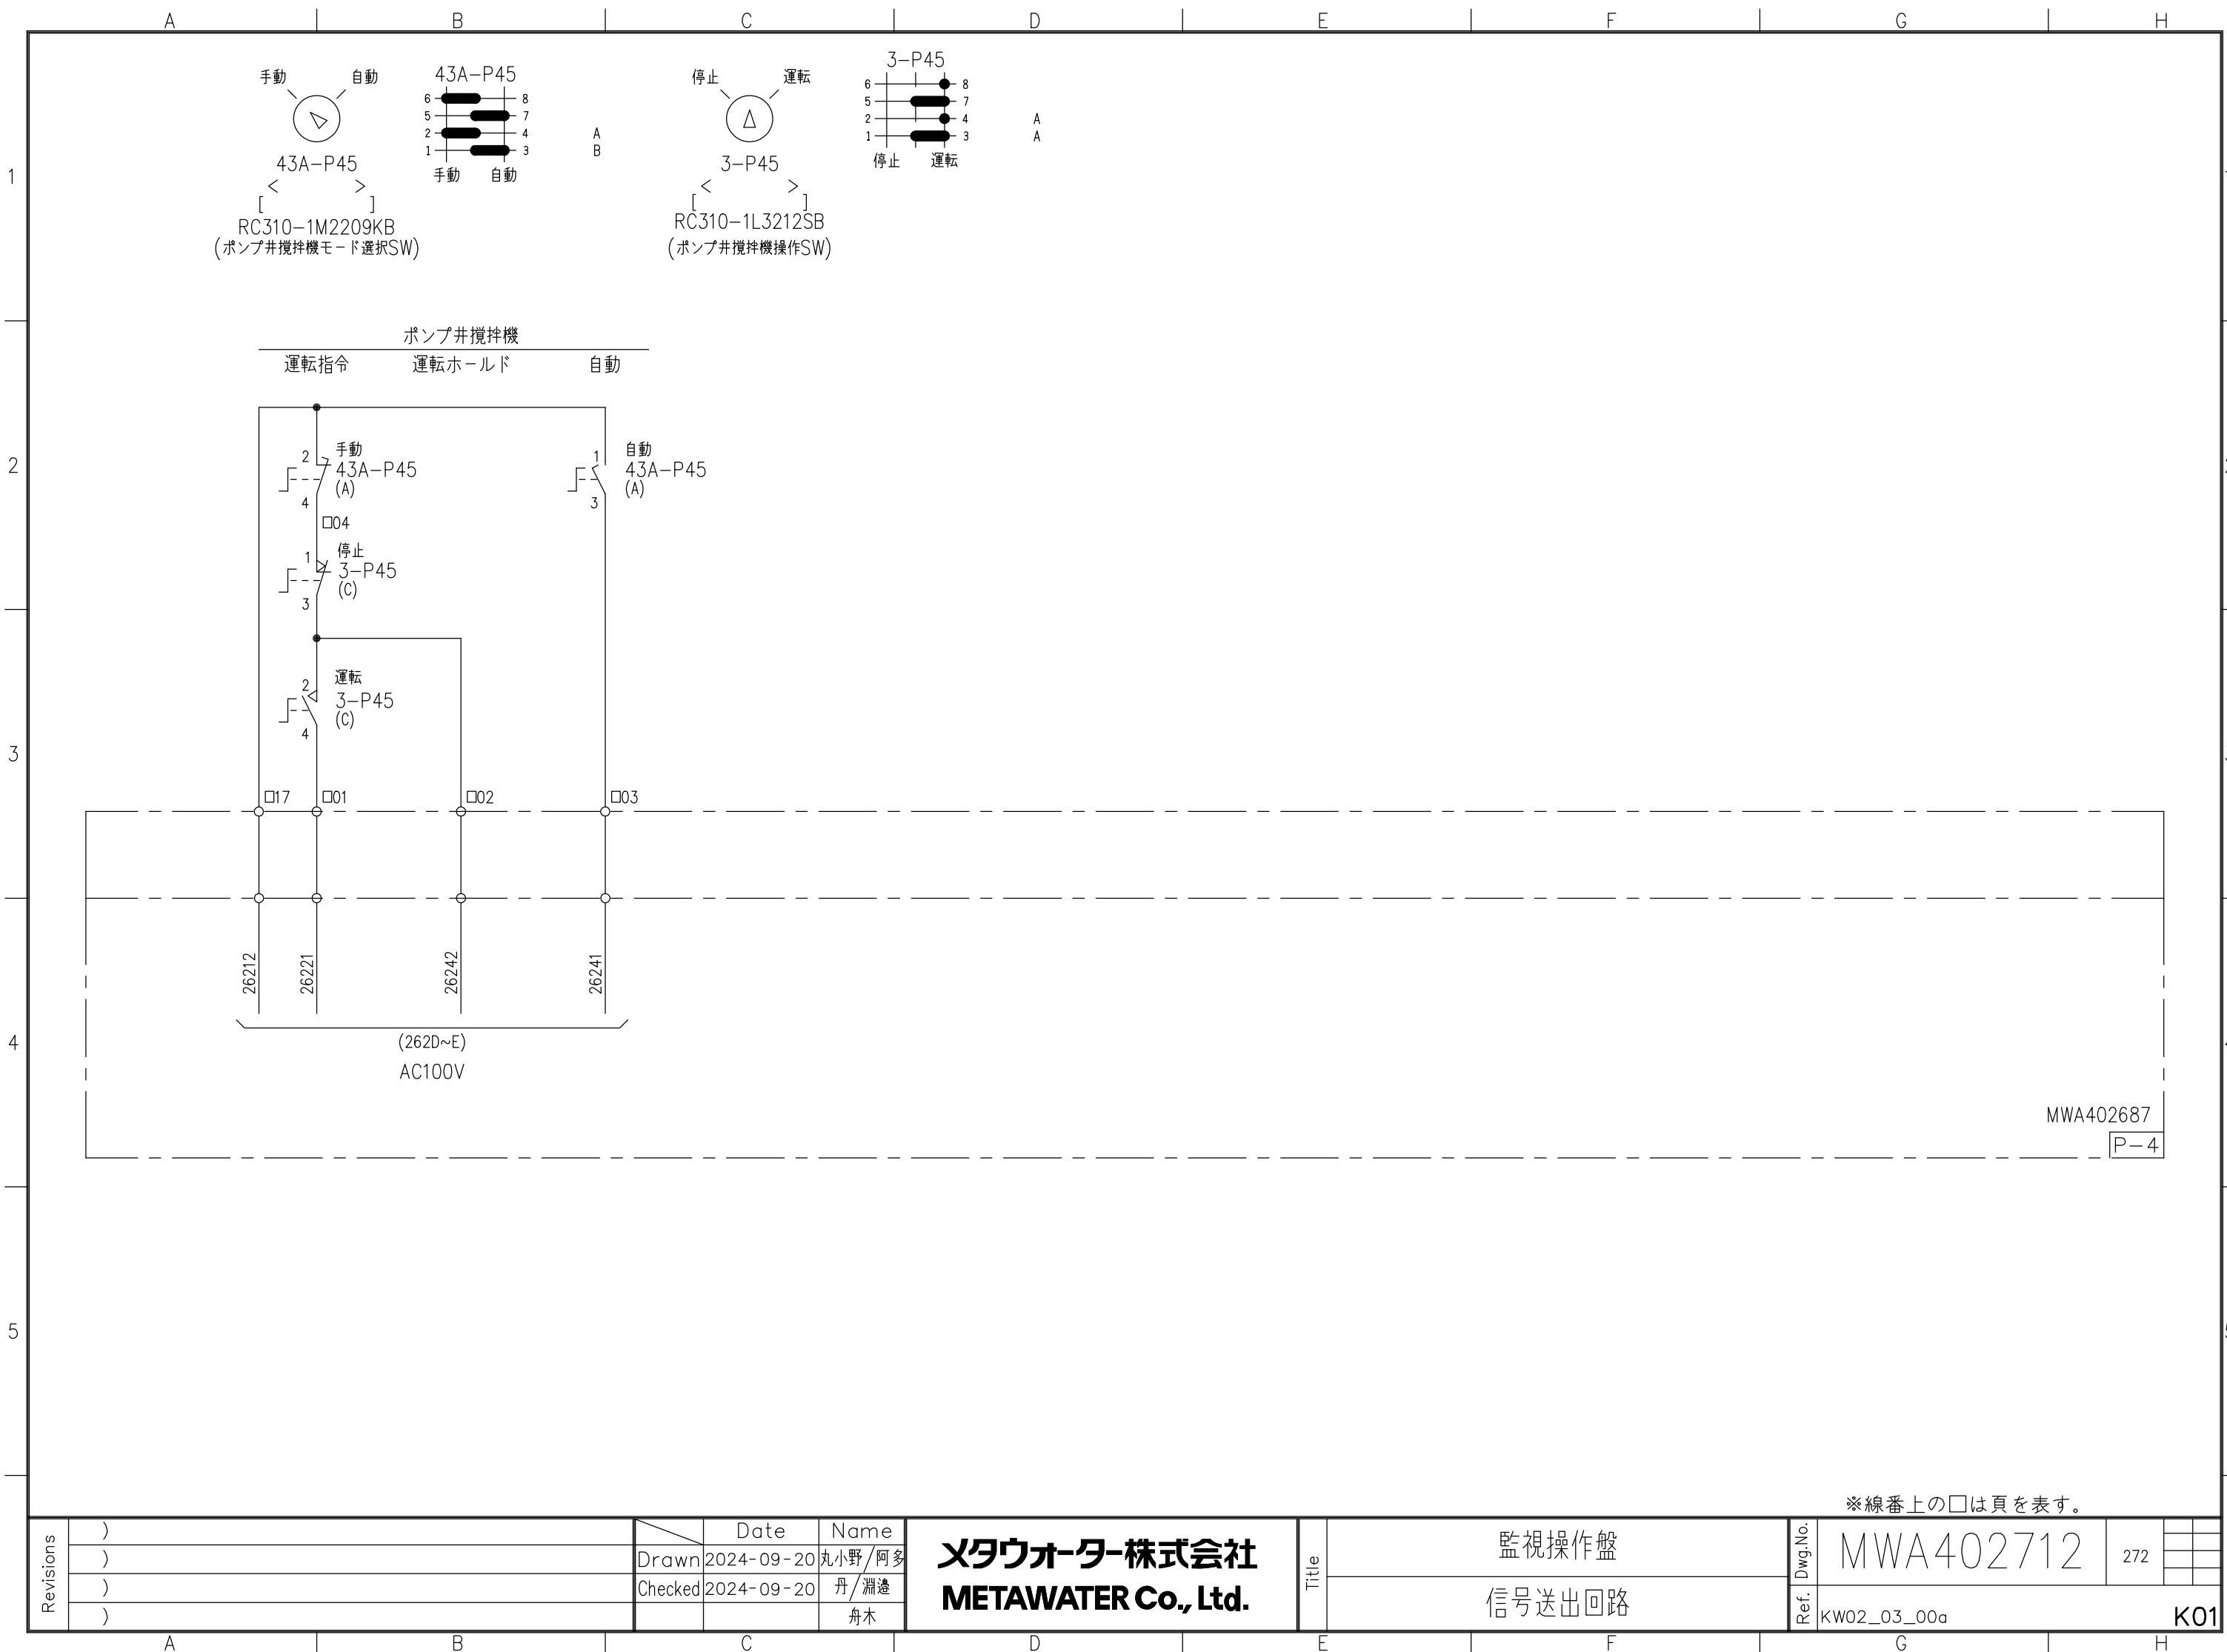

※線番上の□は頁を表す。

Revisions

)

)

)

)

Drawn

2024-09-20

丸小野/阿多

Checked

2024-09-20

丹/淵邊

舟木

メタウォーター株式会社

METAWATER Co., Ltd.

Title

監視操作盤

信号送出回路

Dwg.No.


MWA402712

272


Ref.


KW02_03_00a

K01

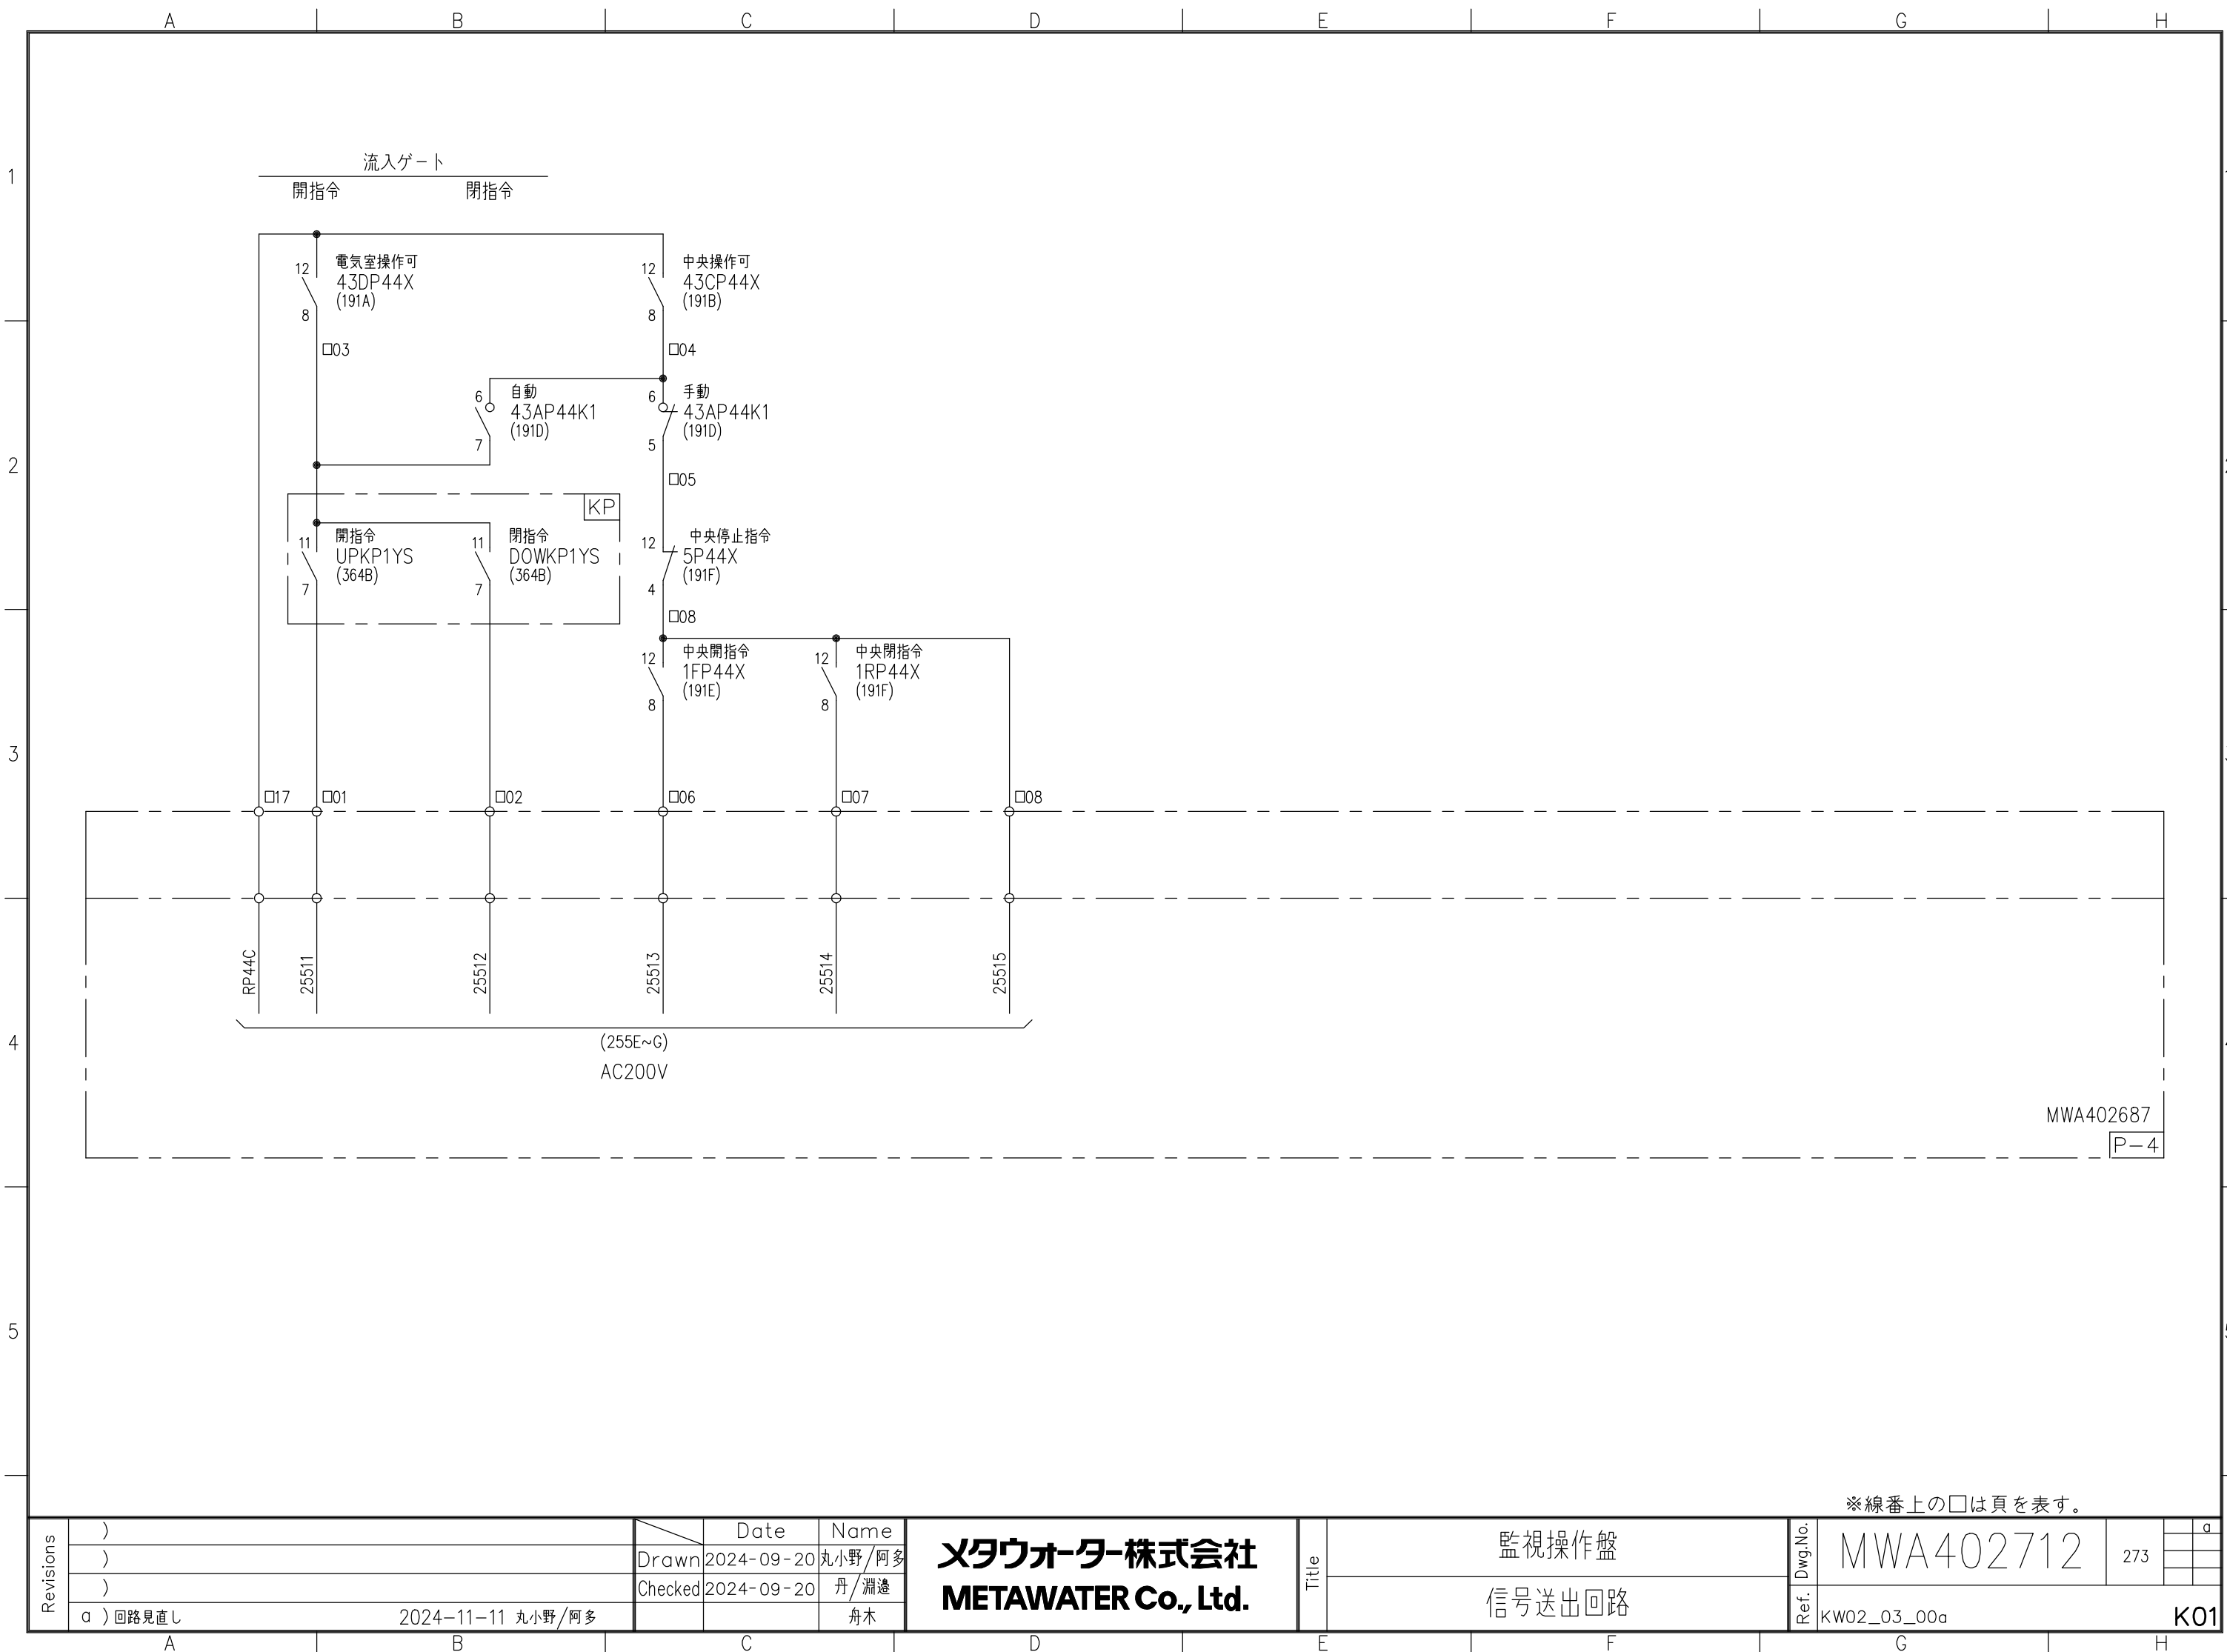

Revisions	)		Date	Name	メタウォーター株式会社 METAWATER Co., Ltd.	Title	監視操作盤	Dwg.No.	MWA402712	273		a
	)	Drawn	2024-09-20	丸小野/阿多								
	)	Checked	2024-09-20	丹/淵邊			信号送出回路	Ref.	KW02_03_00a	K01		
	a) 回路見直し			舟木								

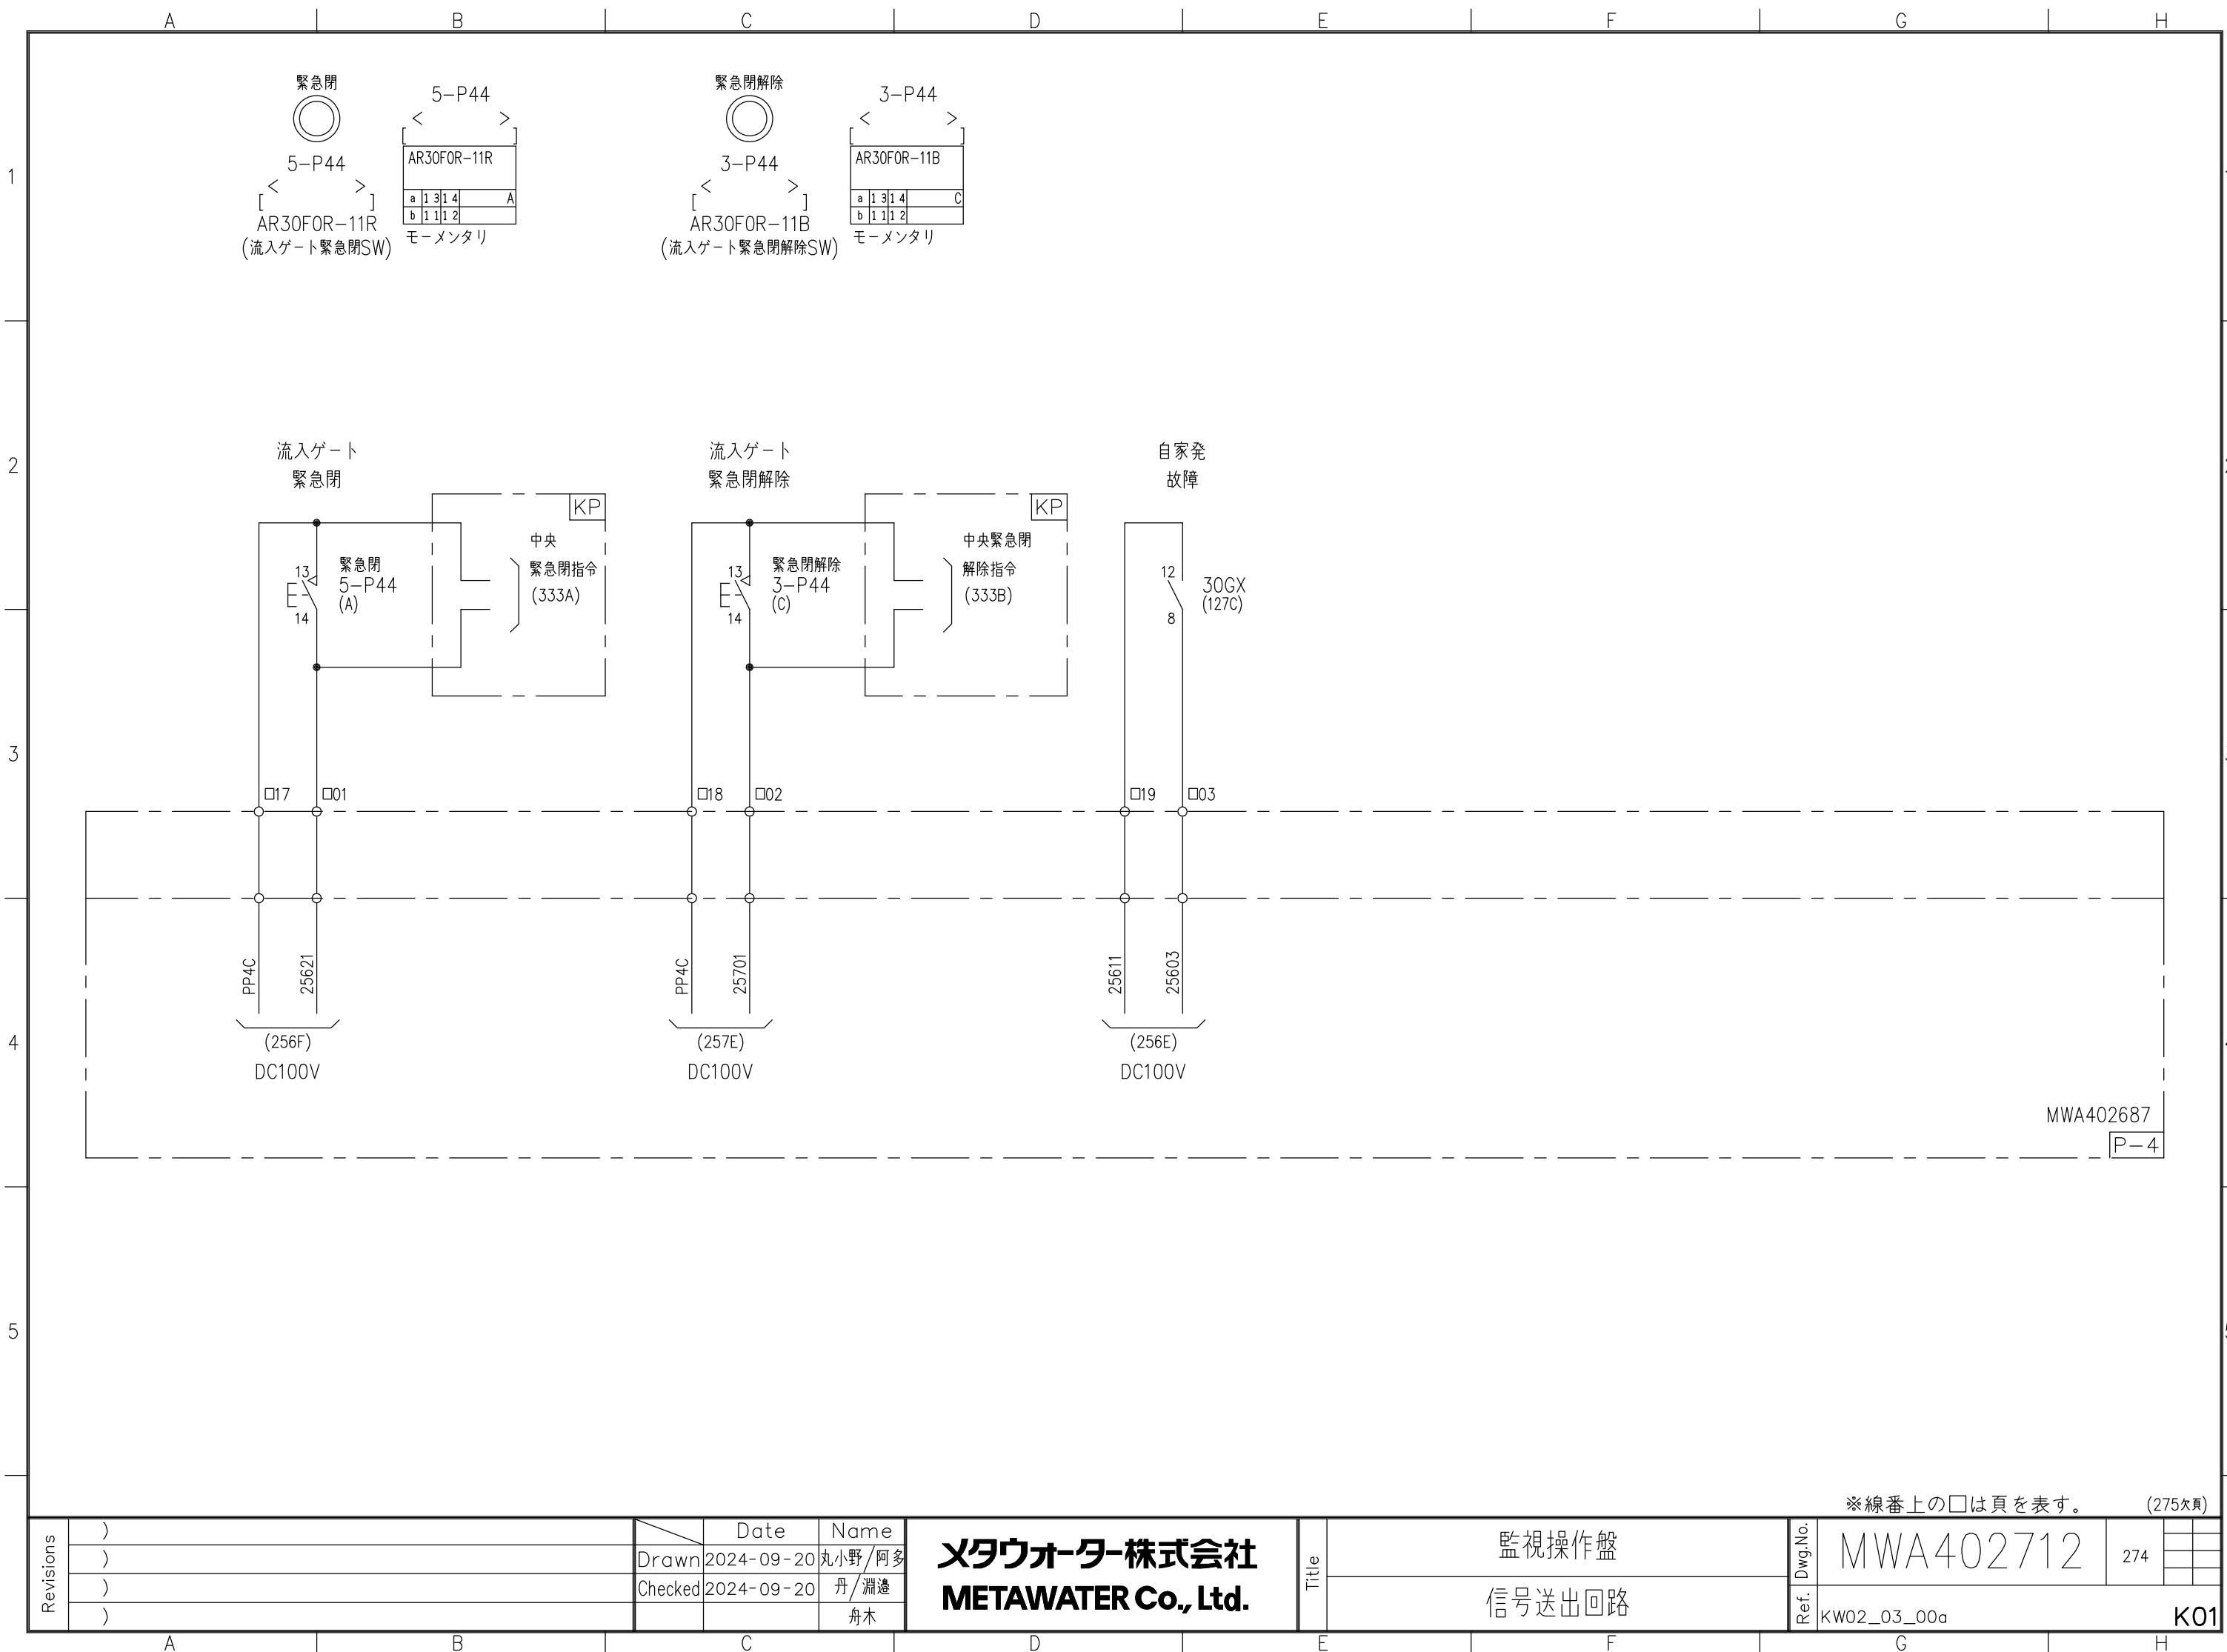

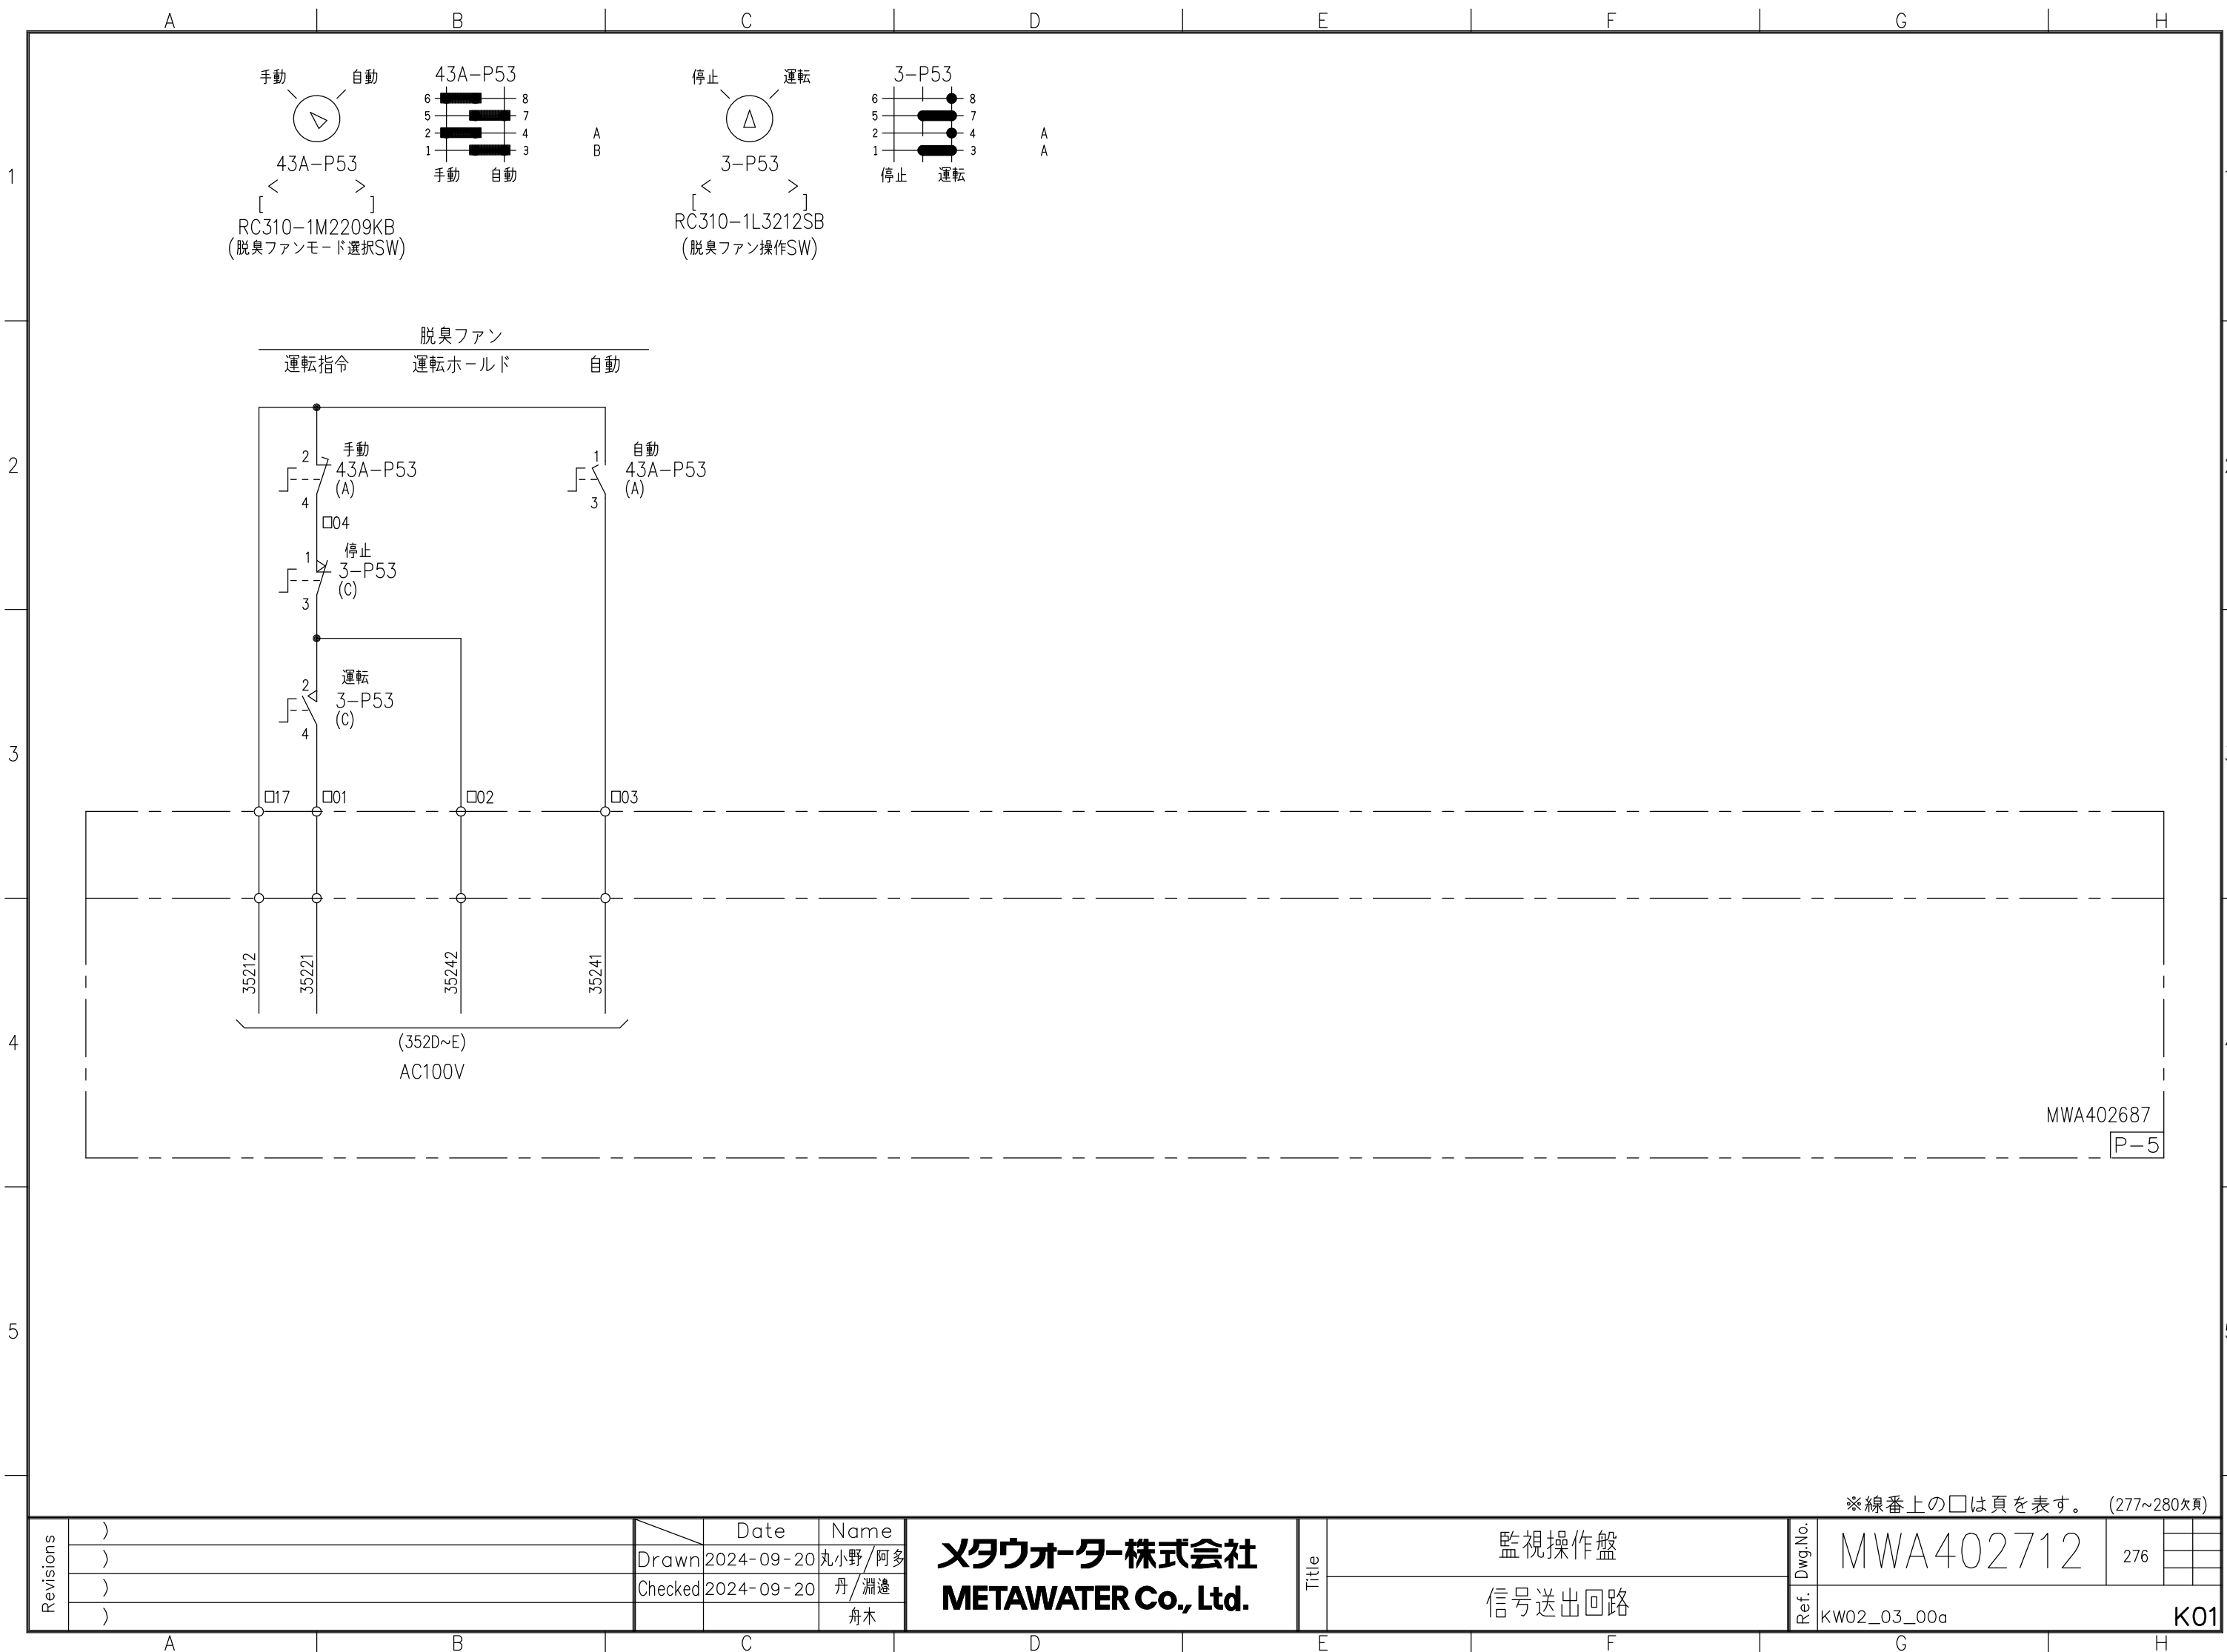

脱臭ファン

運転指令

運転ホールド

自動

2 手動

4 43A-P53

4 (A)

1 停止

3 3-P53

3 (C)

2 運転

4 3-P53

4 (C)

1 自動

3 43A-P53

3 (A)

□04

□17

□01

□02

□03

35212

35221

35242

35241

(352D~E)


AC100V

MWA402687

P-5


※線番上の□は頁を表す。(277~280欠頁)


Revisions	)	Date	Name	メタウォーター株式会社 METAWATER Co., Ltd.	Title	監視操作盤	Dwg.No.	MWA402712	276	Ref.	KW02_03_00a	K01
	)					信号送出回路						
	)											
	)											

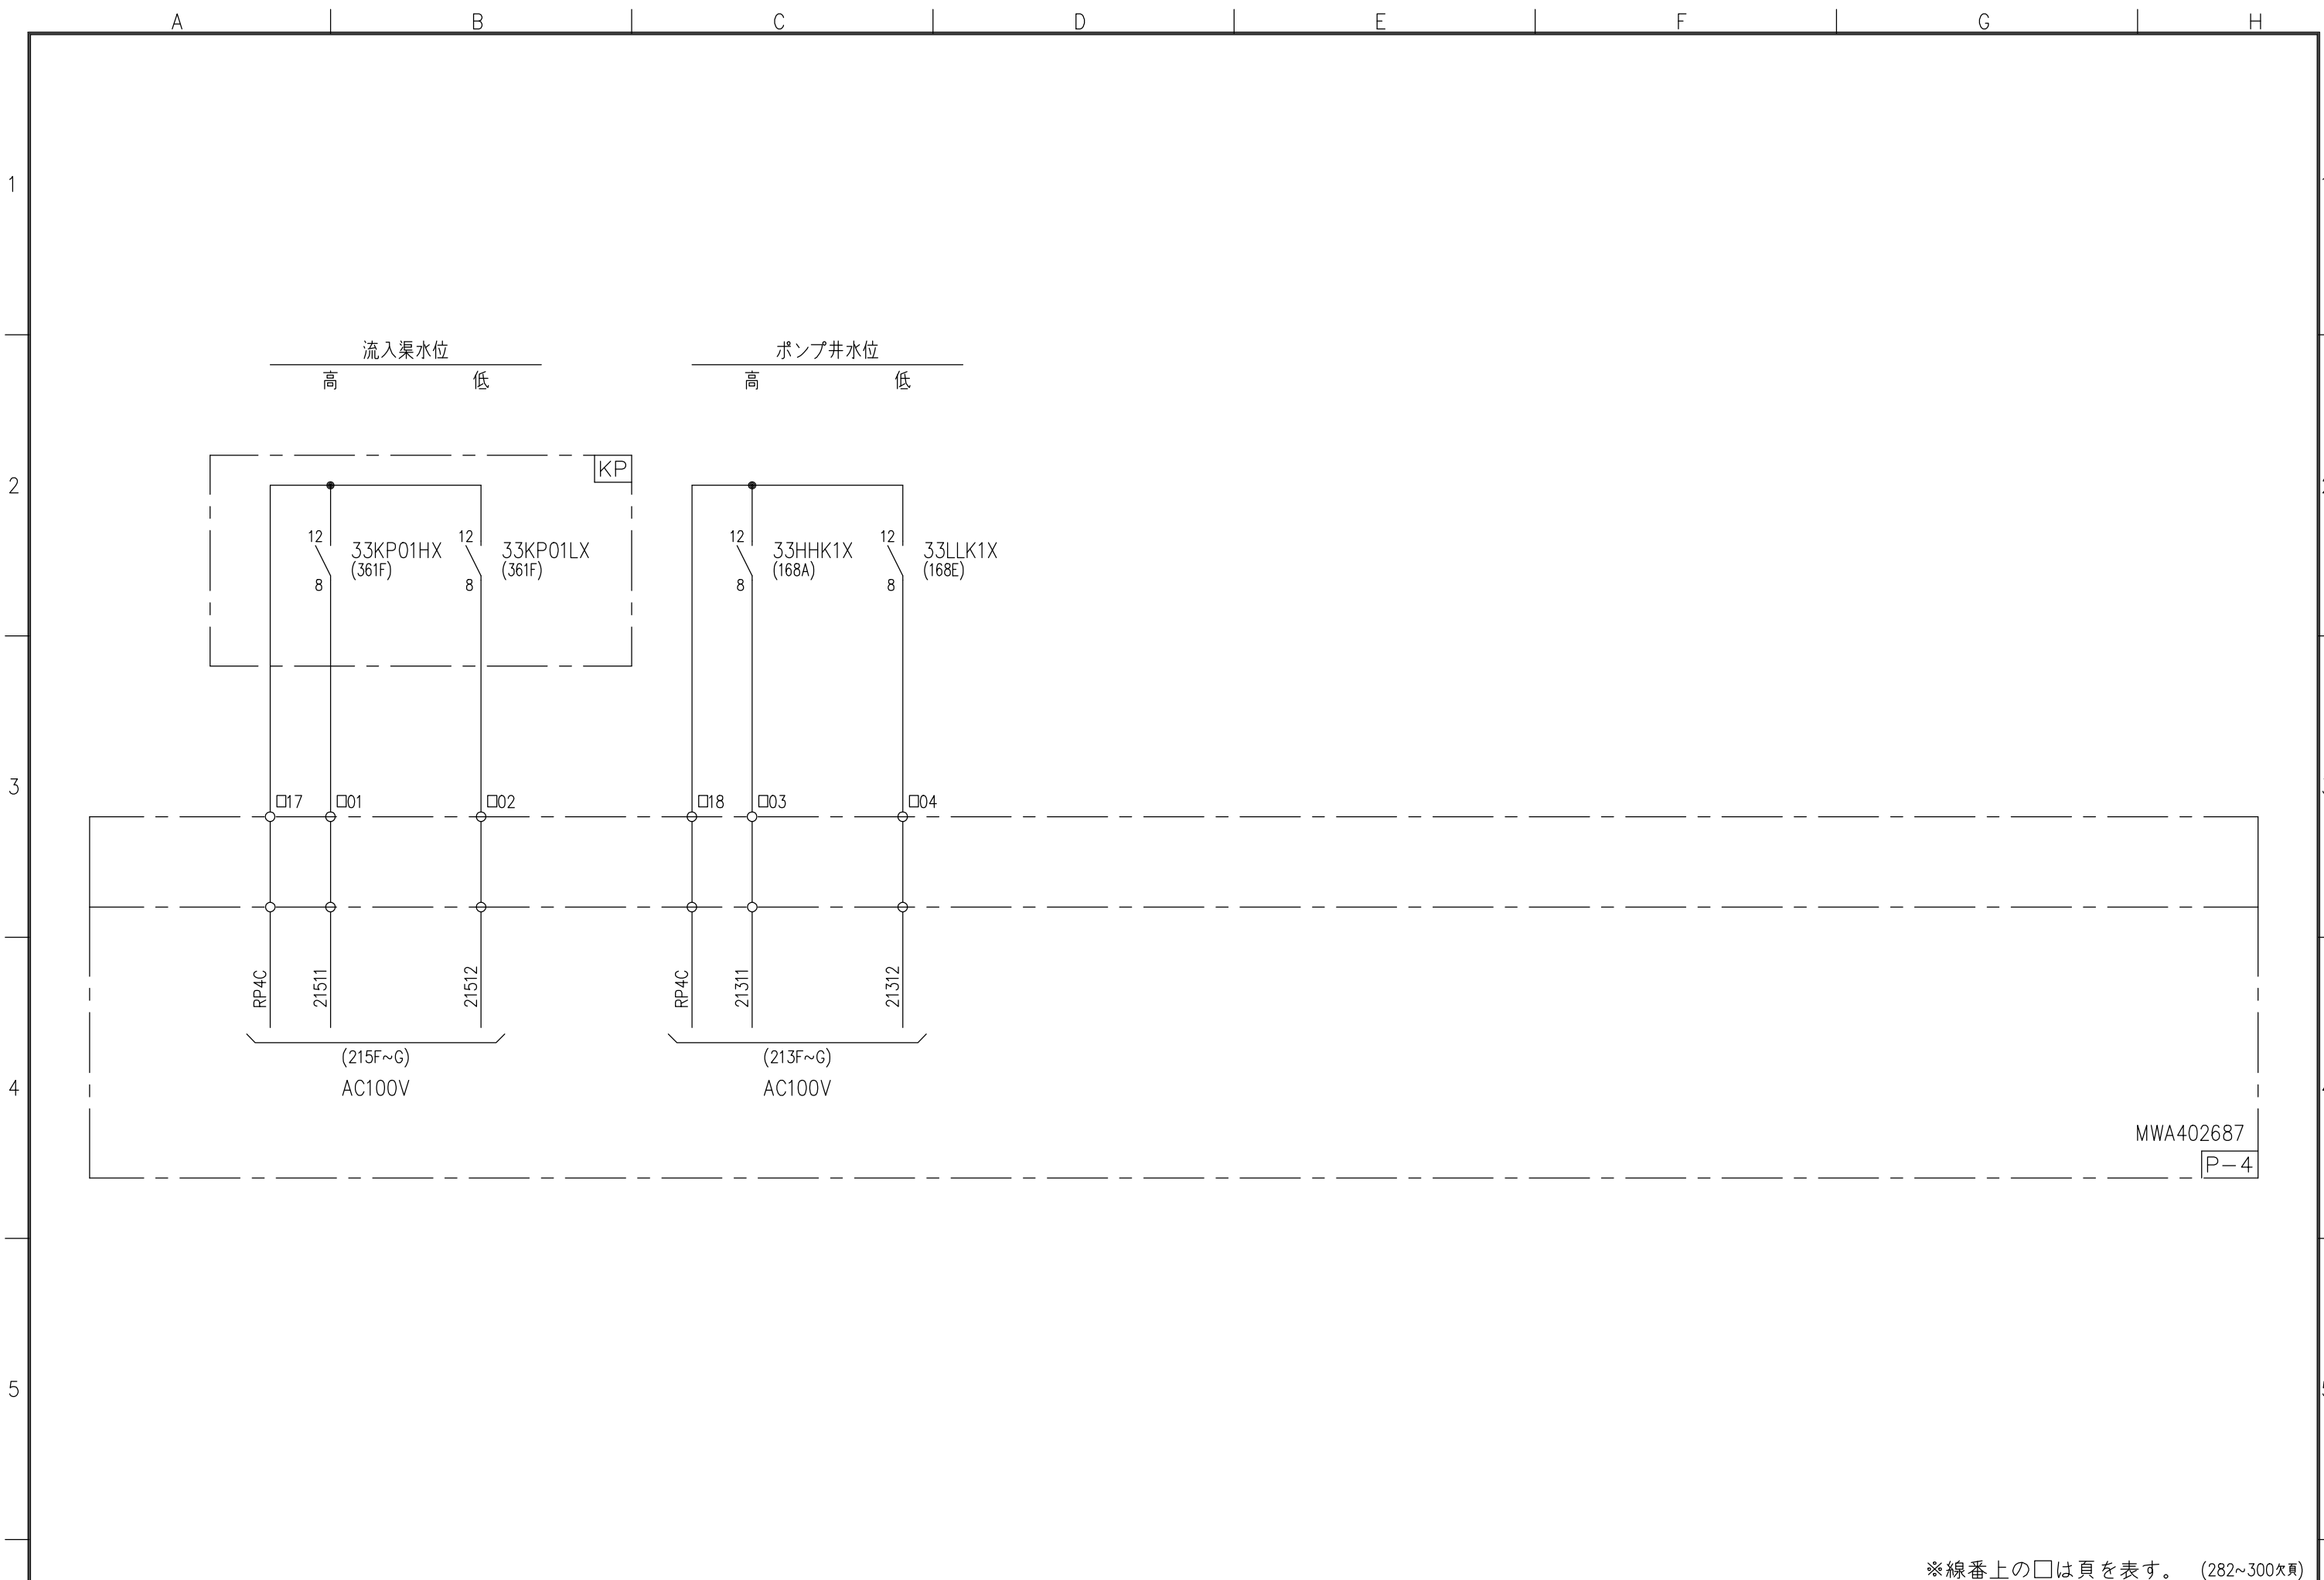

※線番上の□は頁を表す。(282~300欠頁)

Revisions	)		Date	Name	メタウォーター株式会社 METAWATER Co., Ltd.	Title	監視操作盤		Dwg.No.	MWA402712	281			
	)	Drawn	2024-09-20	丸小野 / 阿多			信号送出回路		Ref.	KW02_03_00a				
	)	Checked	2024-09-20	丹 / 淵邊										
	)			舟木			K01							

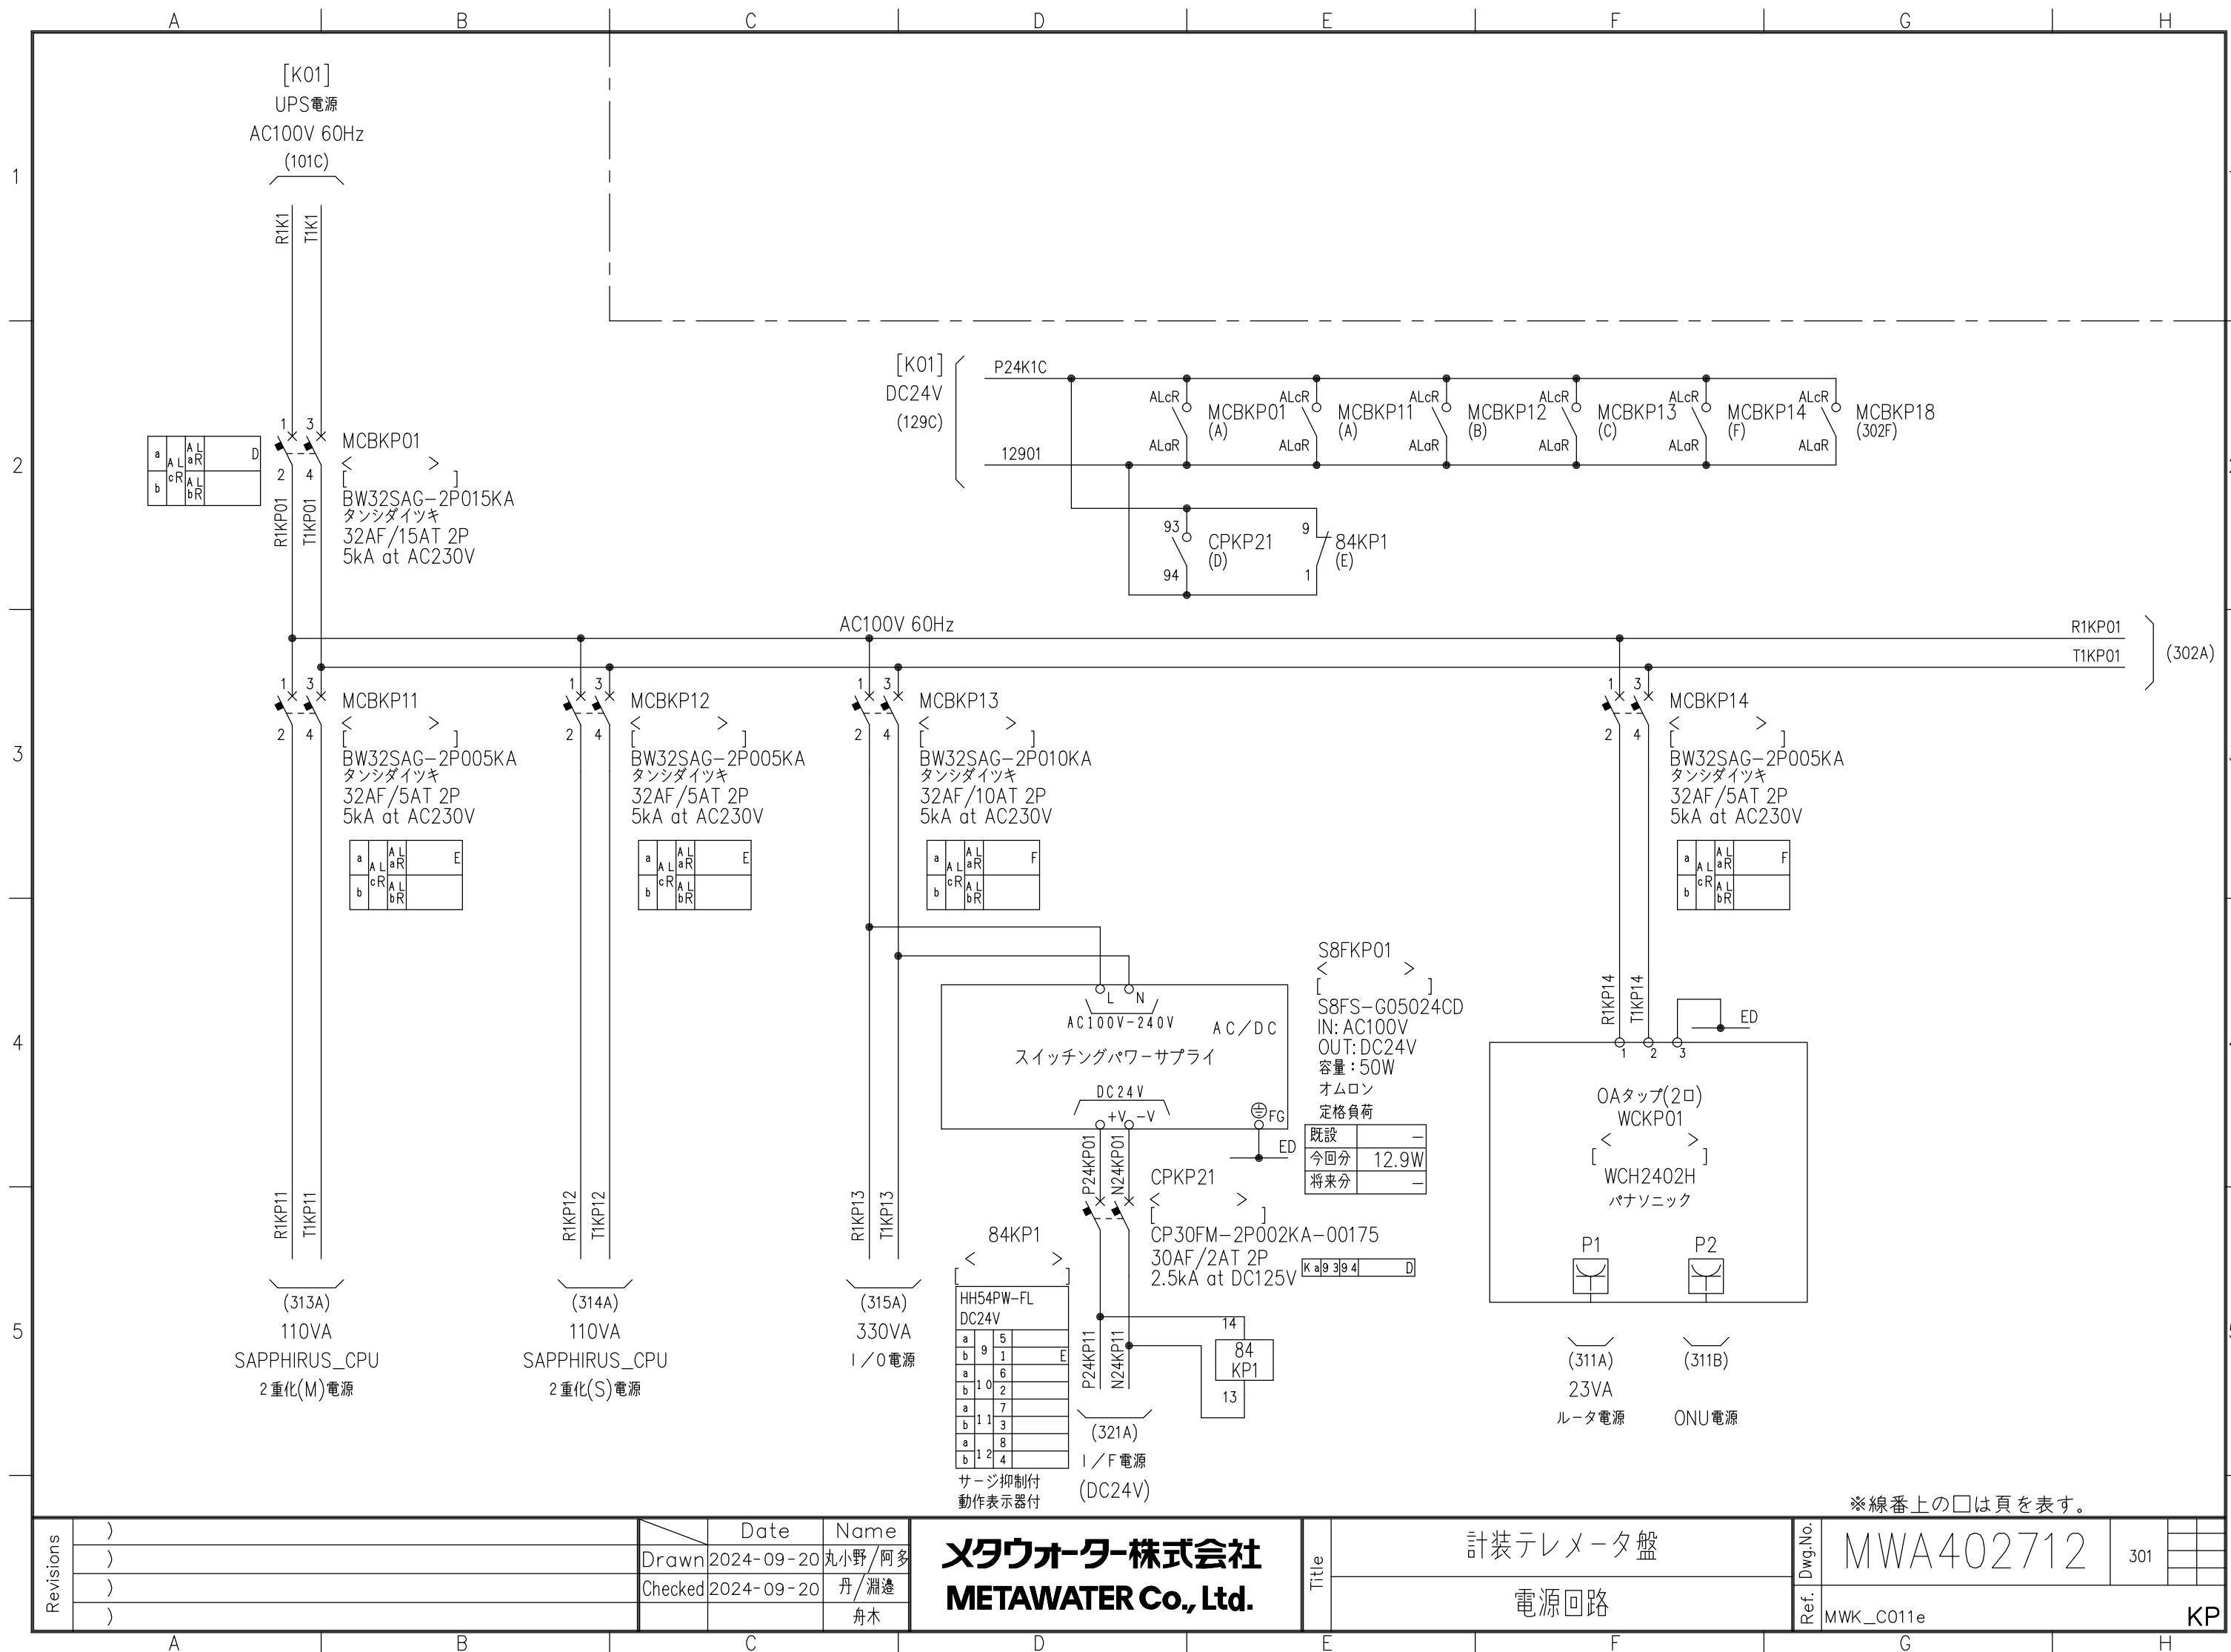

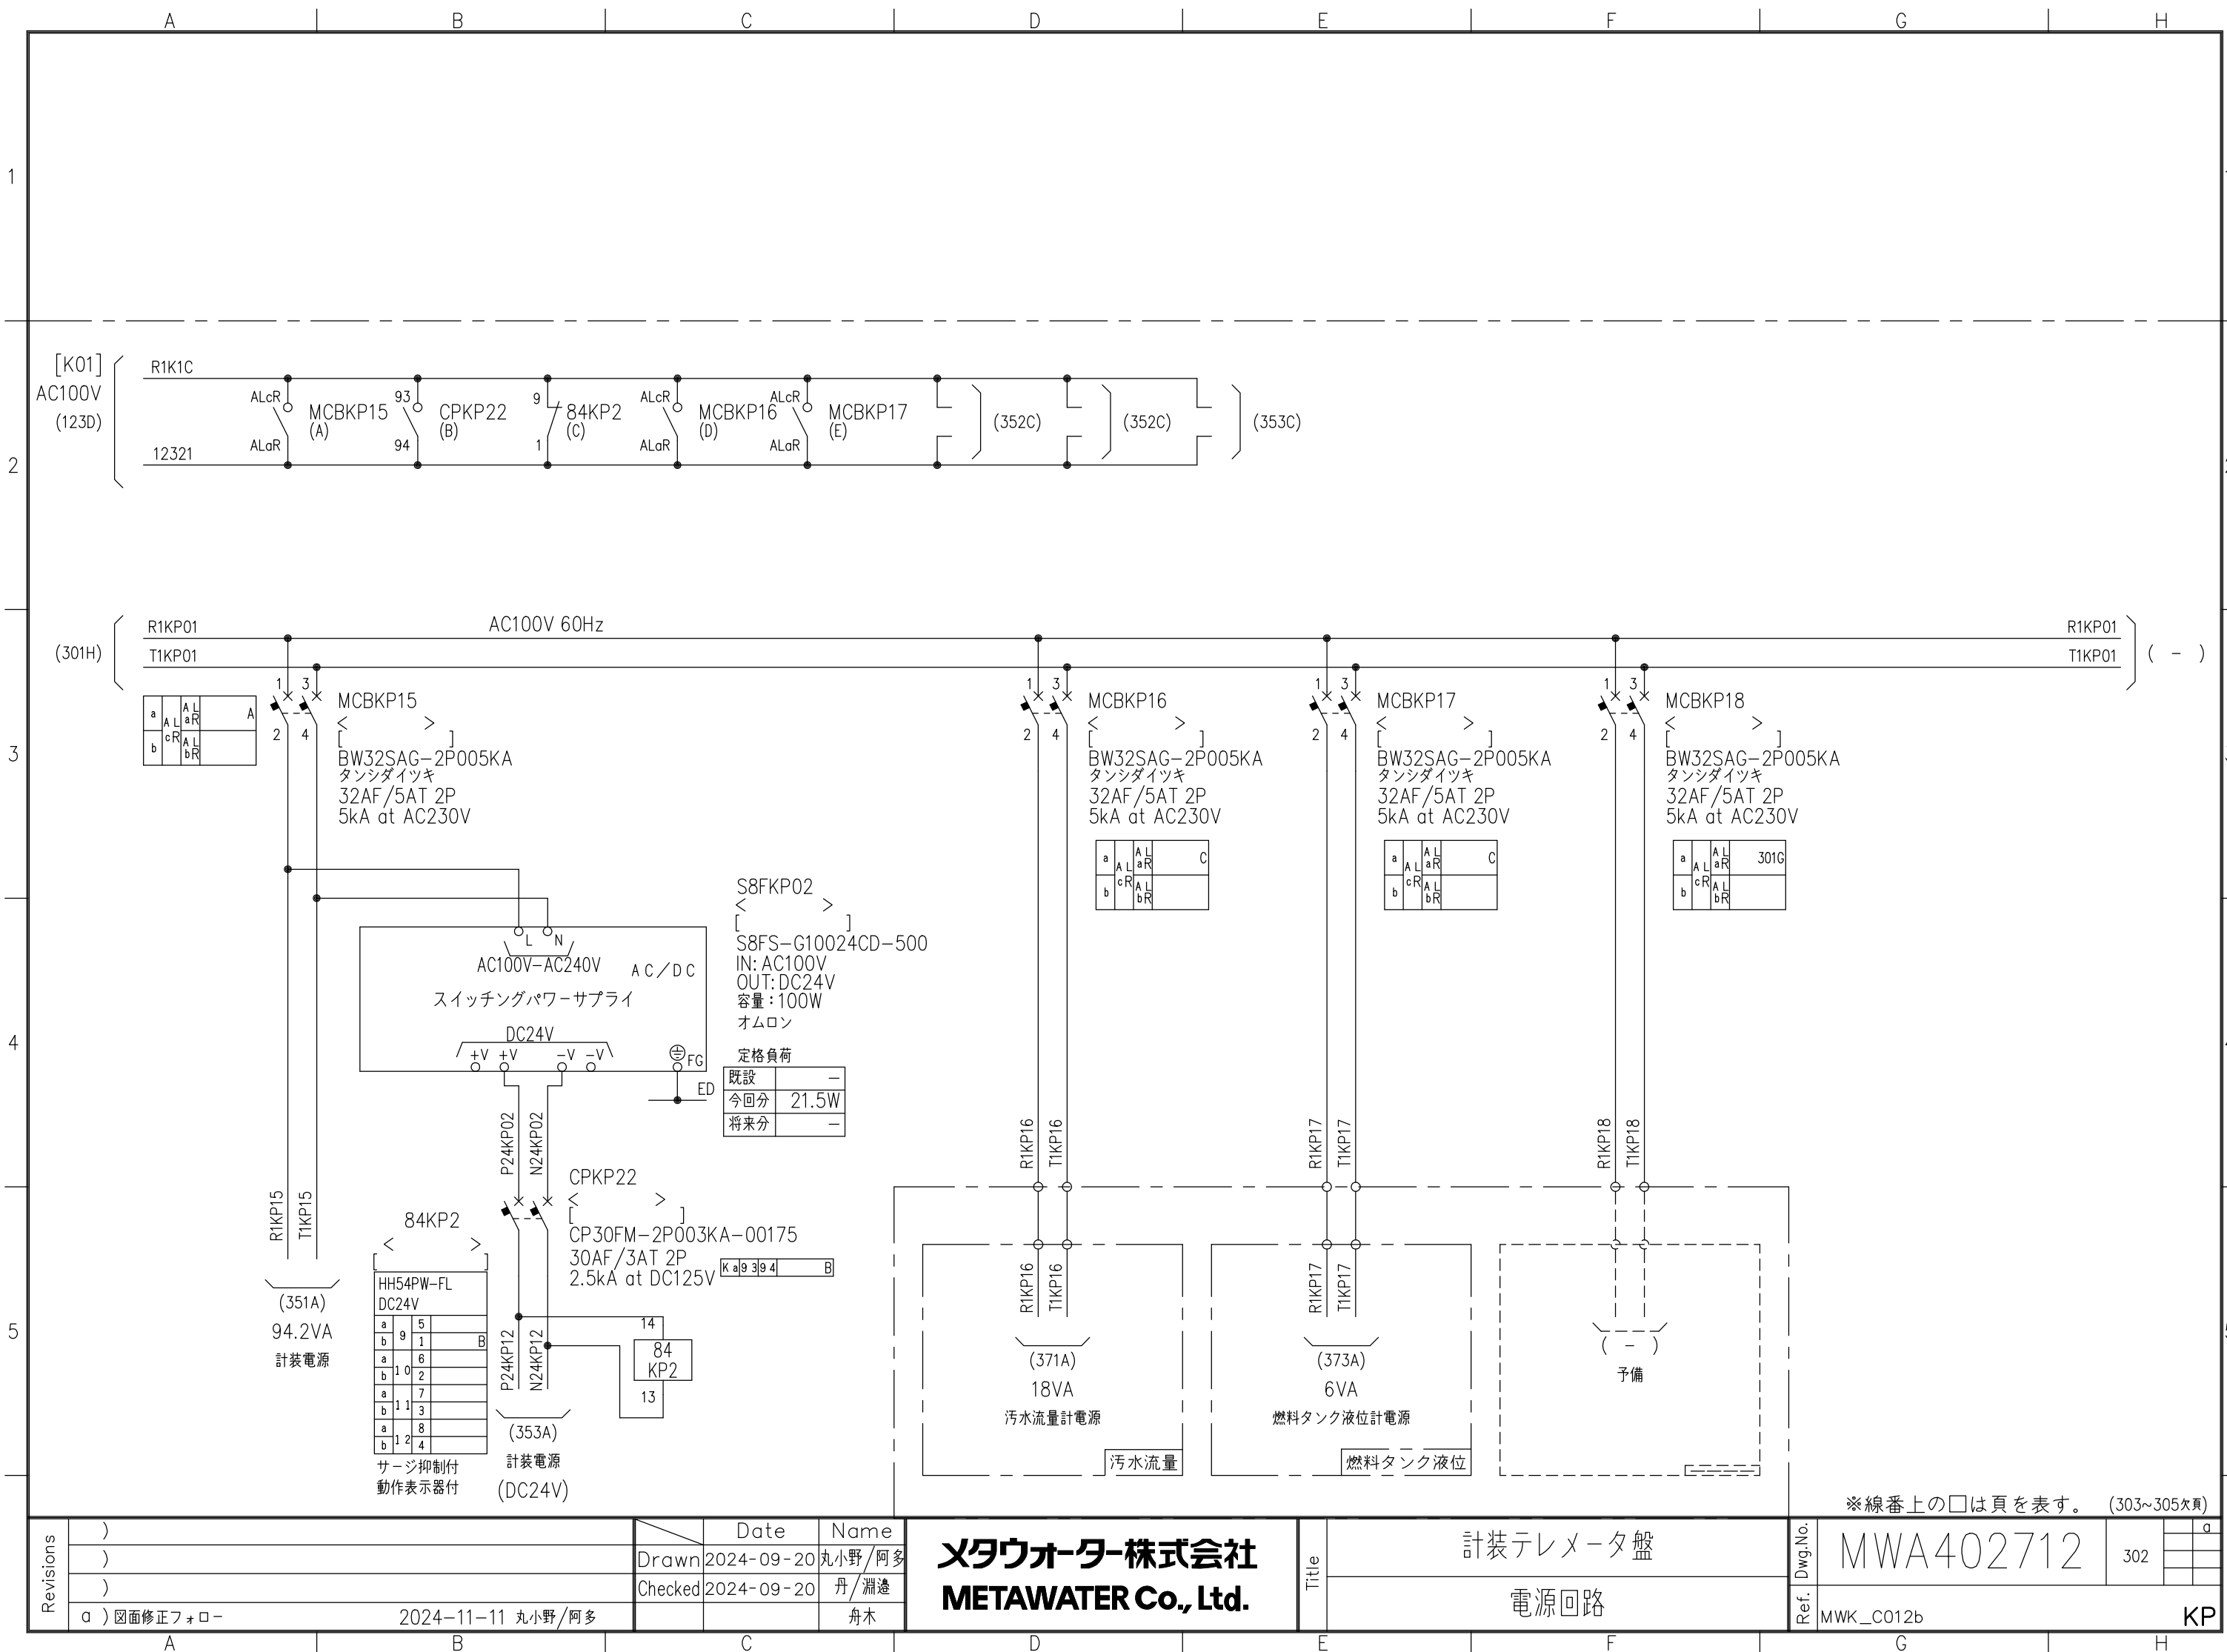


※線番上の□は頁を表す。(303~305欠頁)


Revisions	)	Drawn	Date	Name
	)		2024-09-20	丸小野/阿多
	)	Checked	2024-09-20	丹/淵邊
	a) 図面修正フォロー		2024-11-11	丸小野/阿多

メタウォーター株式会社
METAWATER Co., Ltd.


Title	計装テレメータ盤	Dwg.No.	MWA402712	302		a
	電源回路	Ref.	MWK_C012b			KP

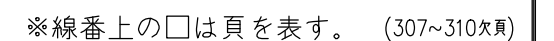


メタウォーター株式会社
METAWATER Co., Ltd.

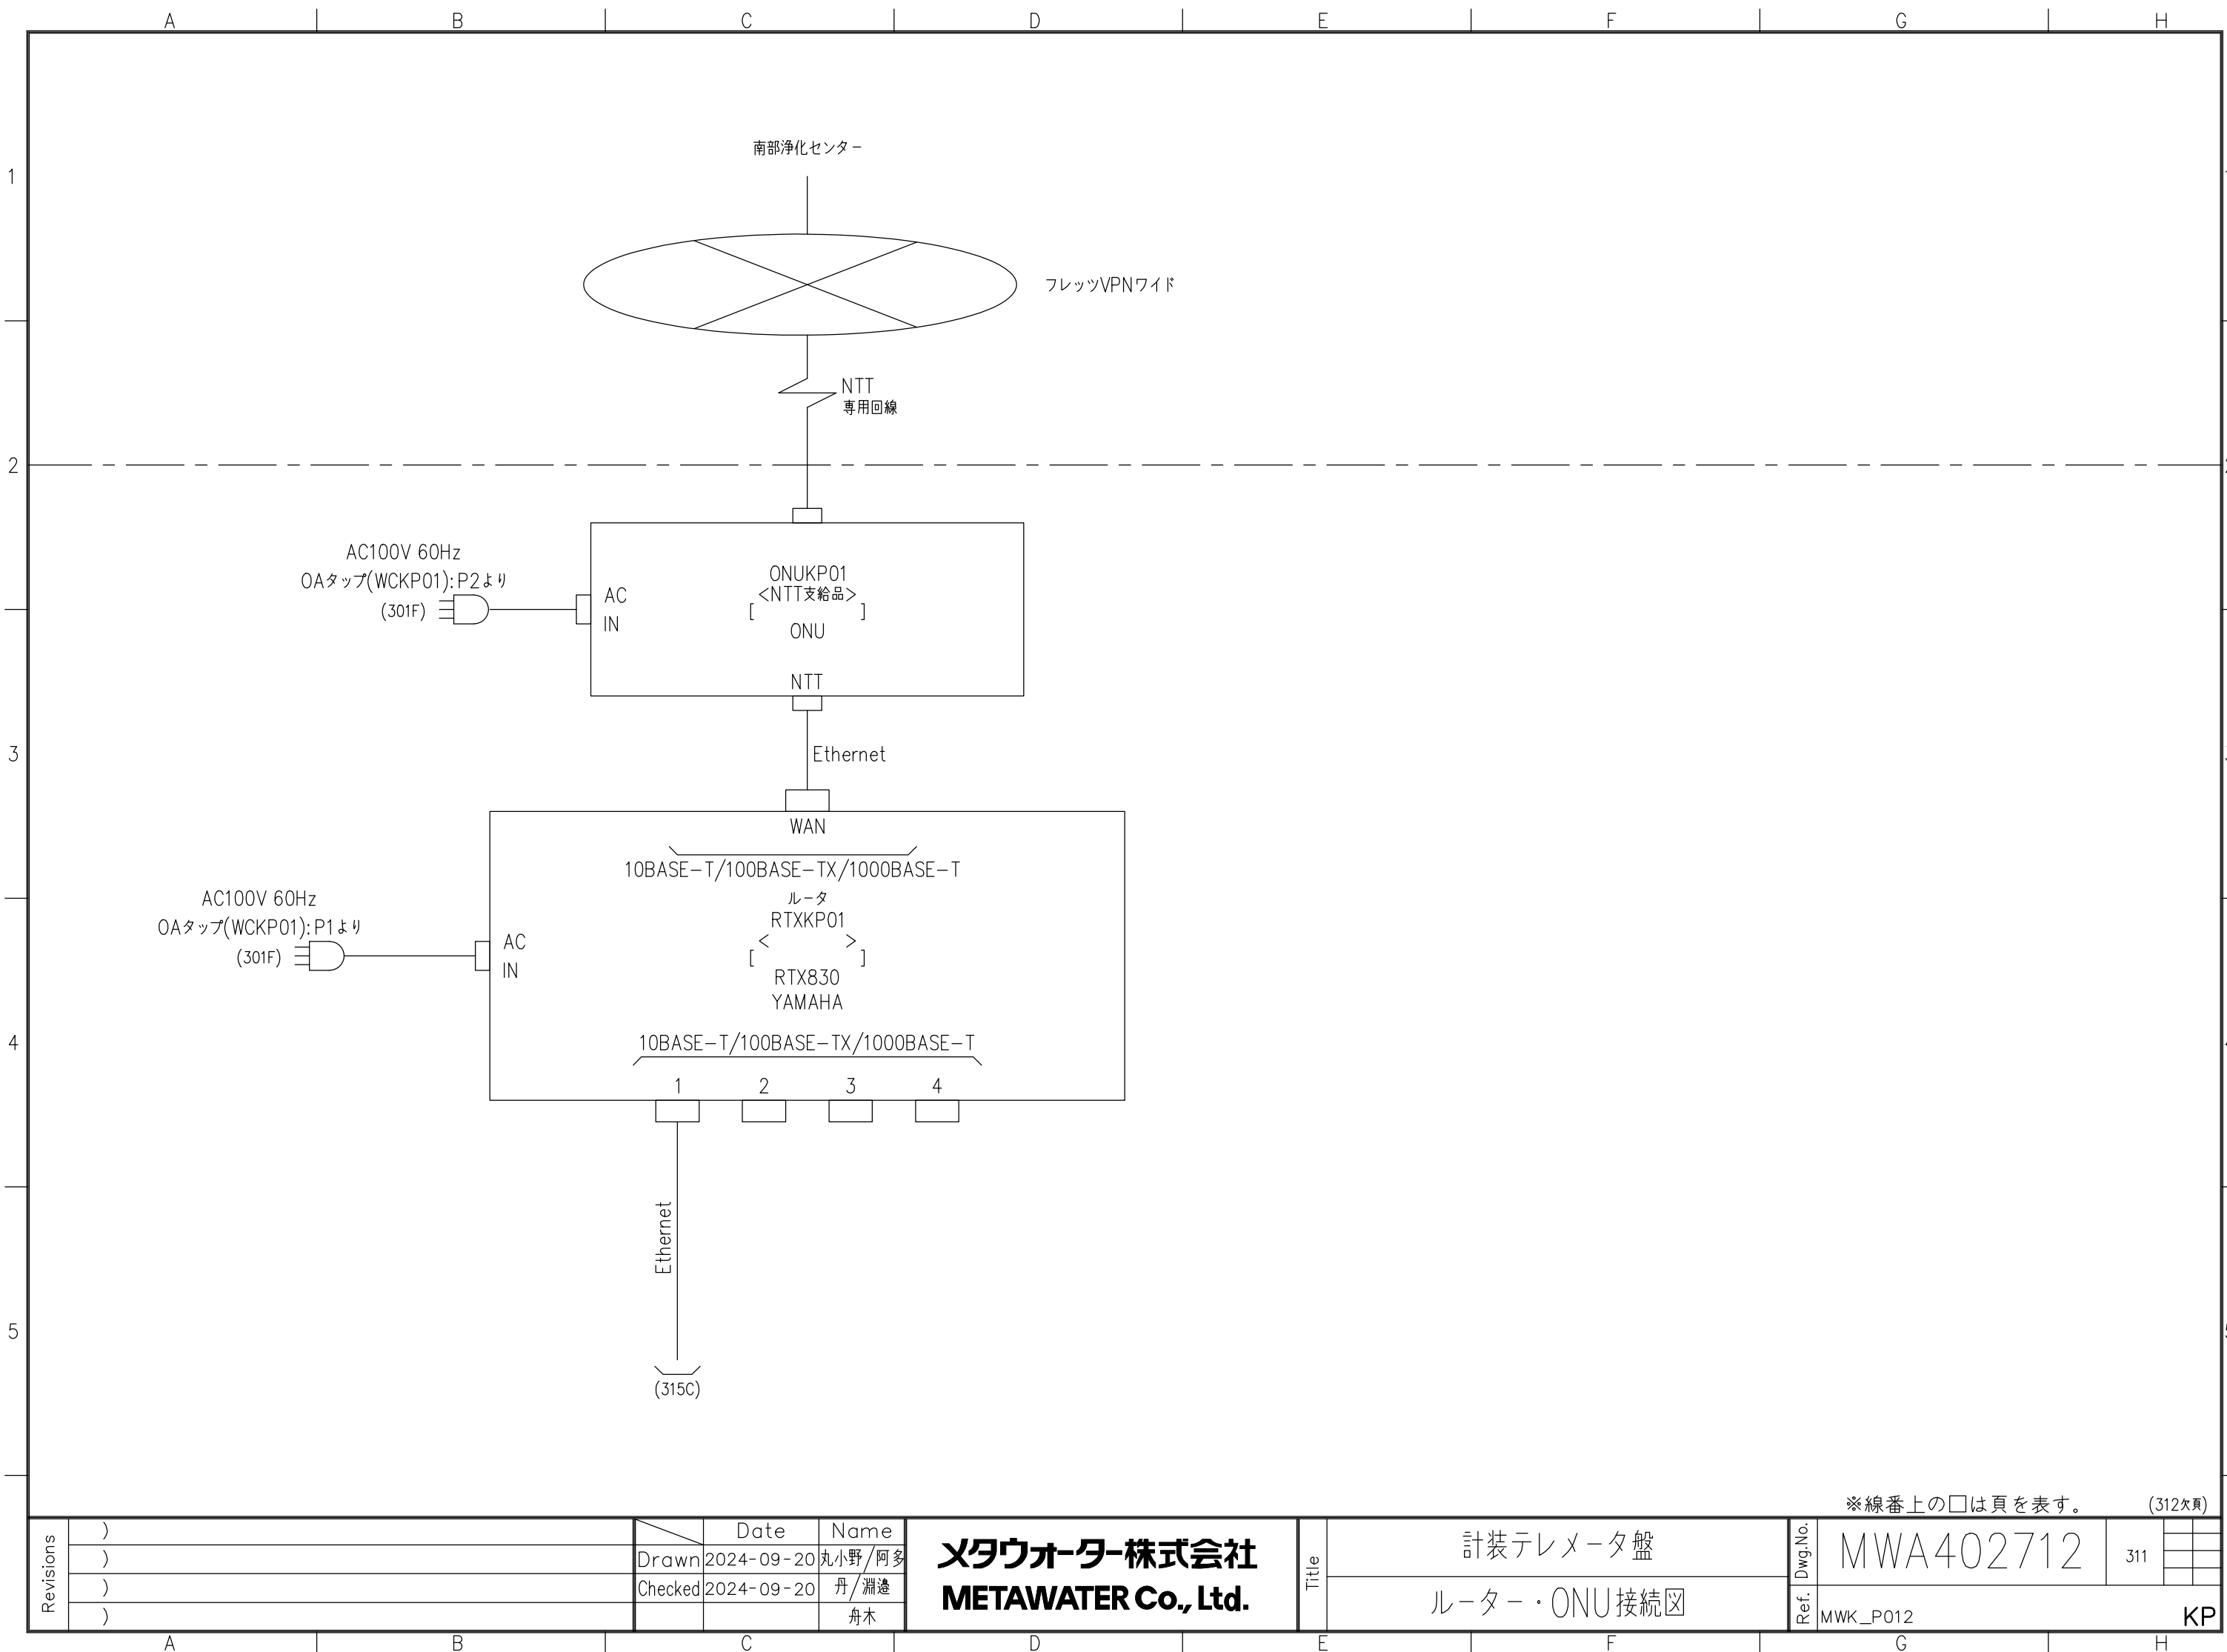



Revisions	)		Date	Name	メタウォーター株式会社 METAWATER Co., Ltd.	Title	計装テレメータ盤		Dwg.No.	MWA402712	311		
	)	Drawn	2024-09-20	丸小野/阿多			ルーター・ONU接続図		Ref.	MWK_P012	KP		
	)	Checked	2024-09-20	丹/淵邊									
	)			舟木									

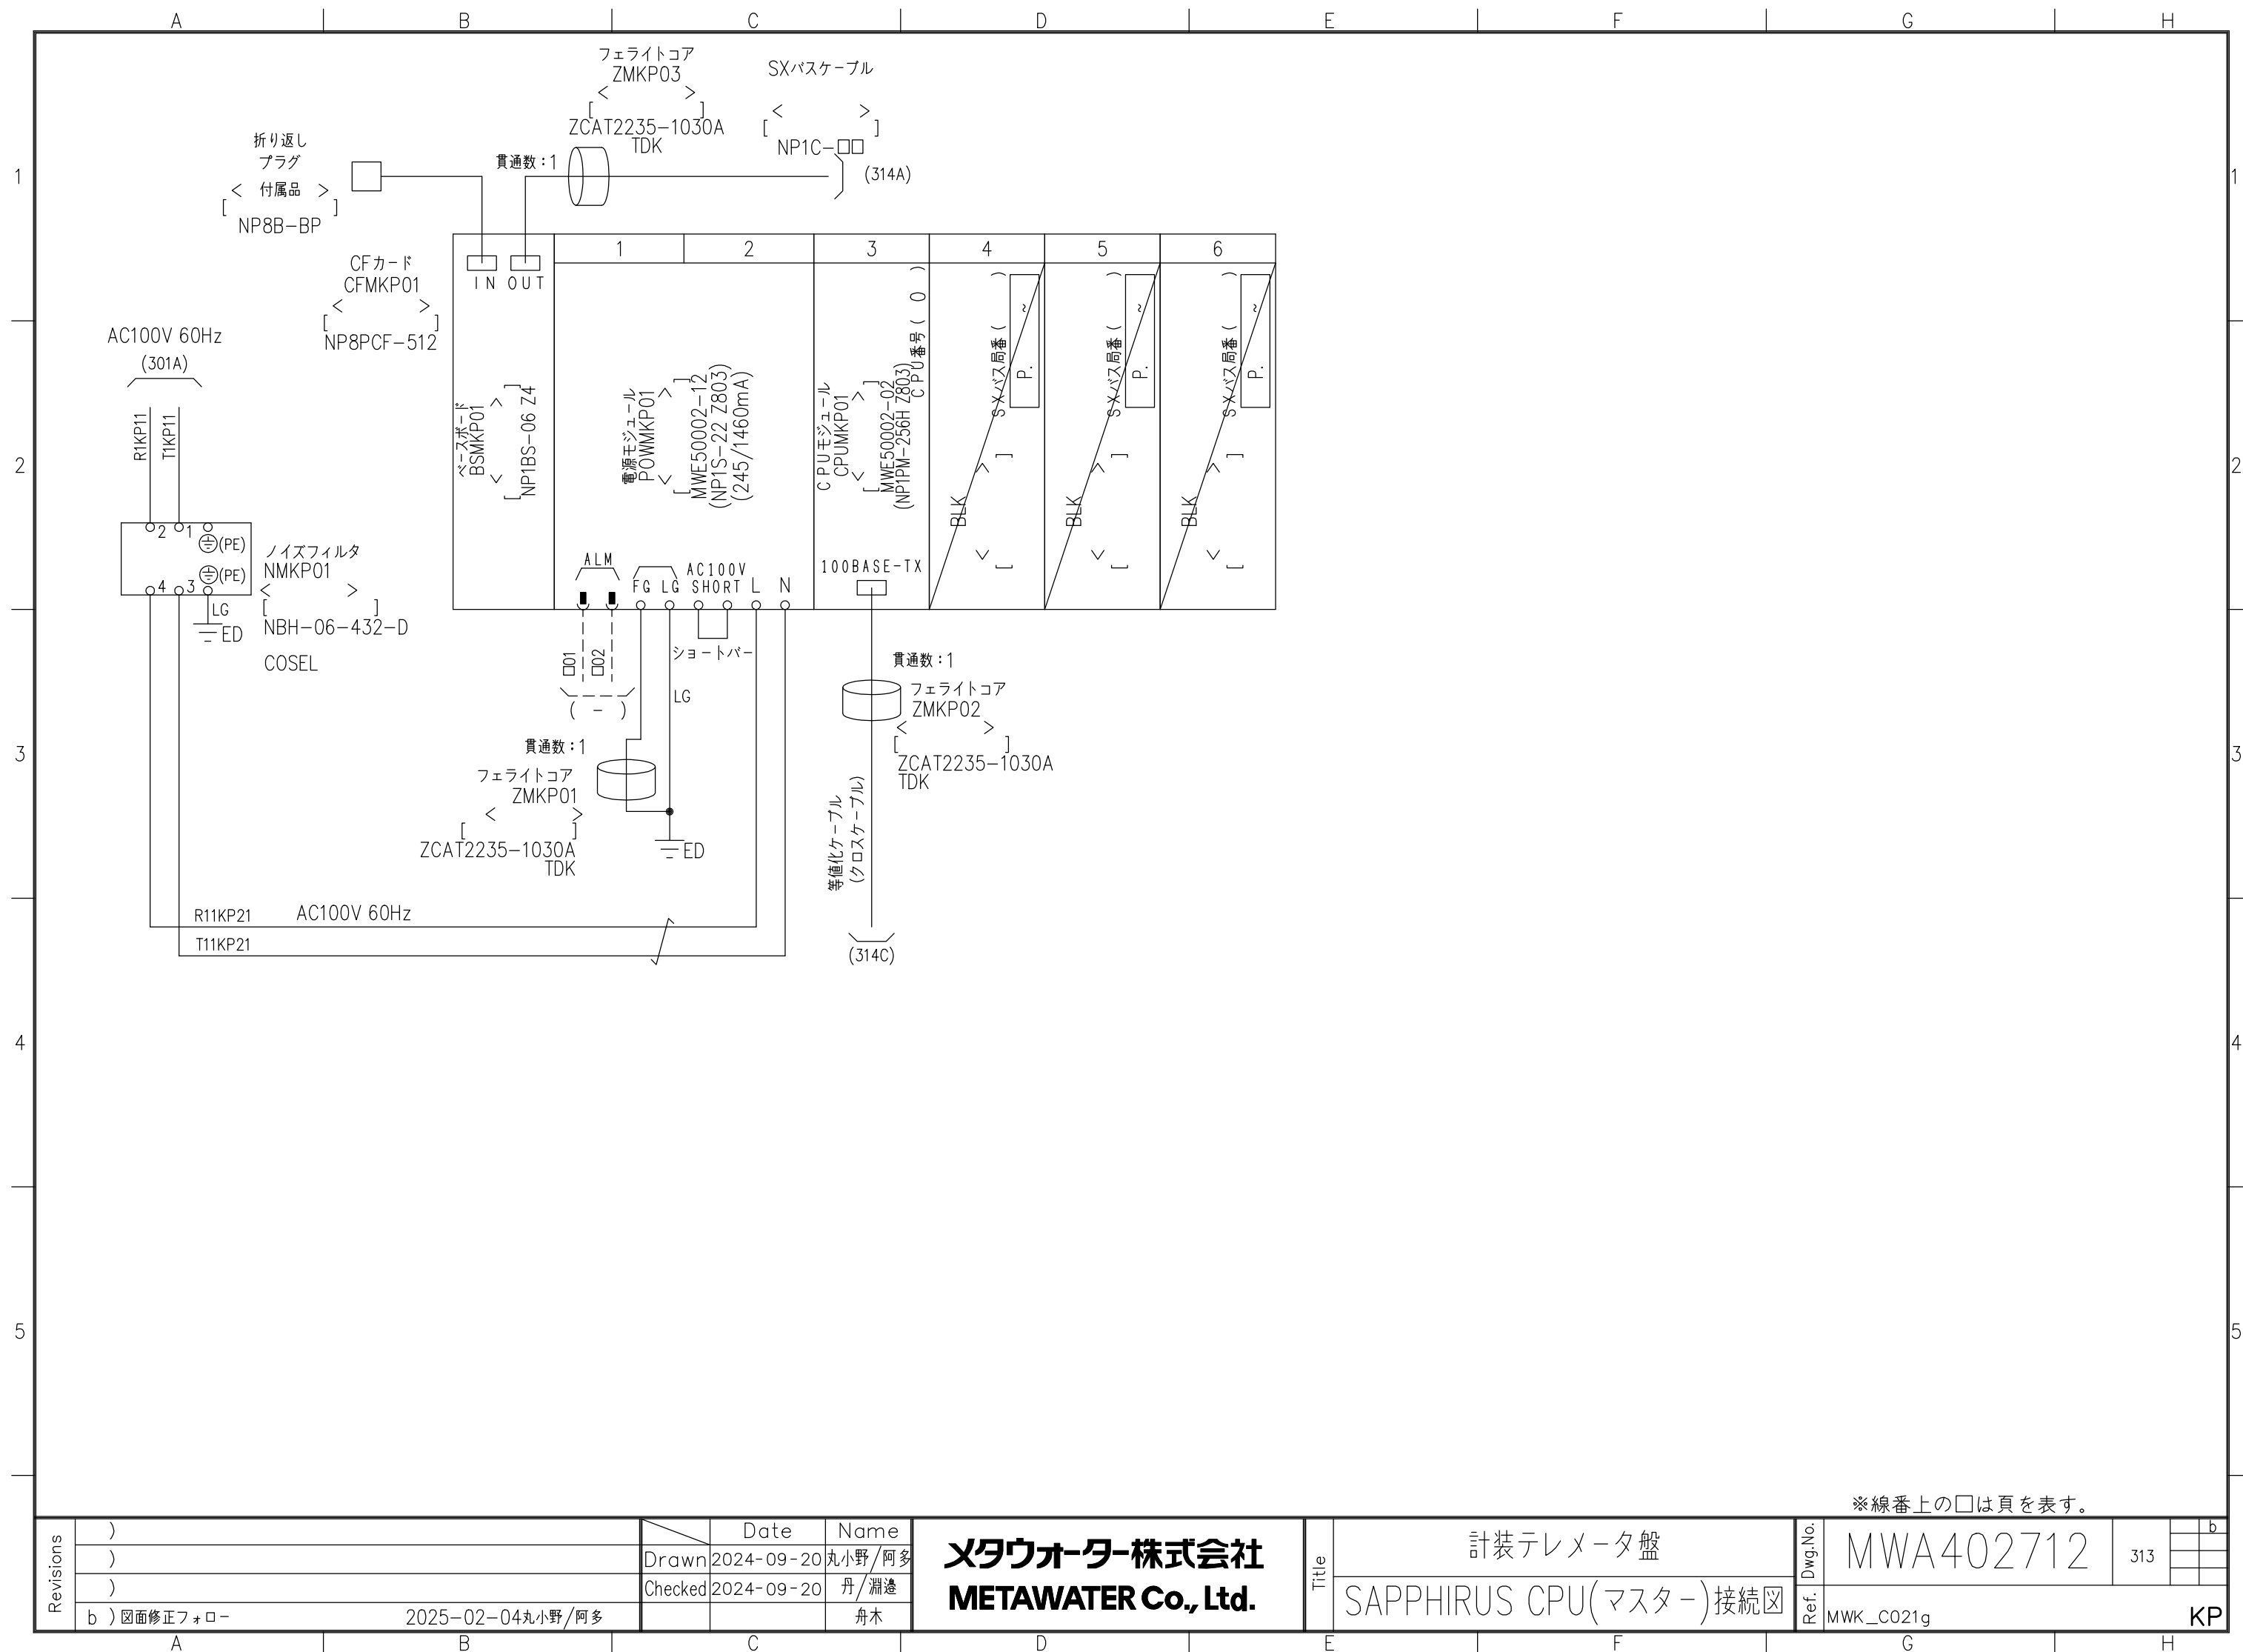

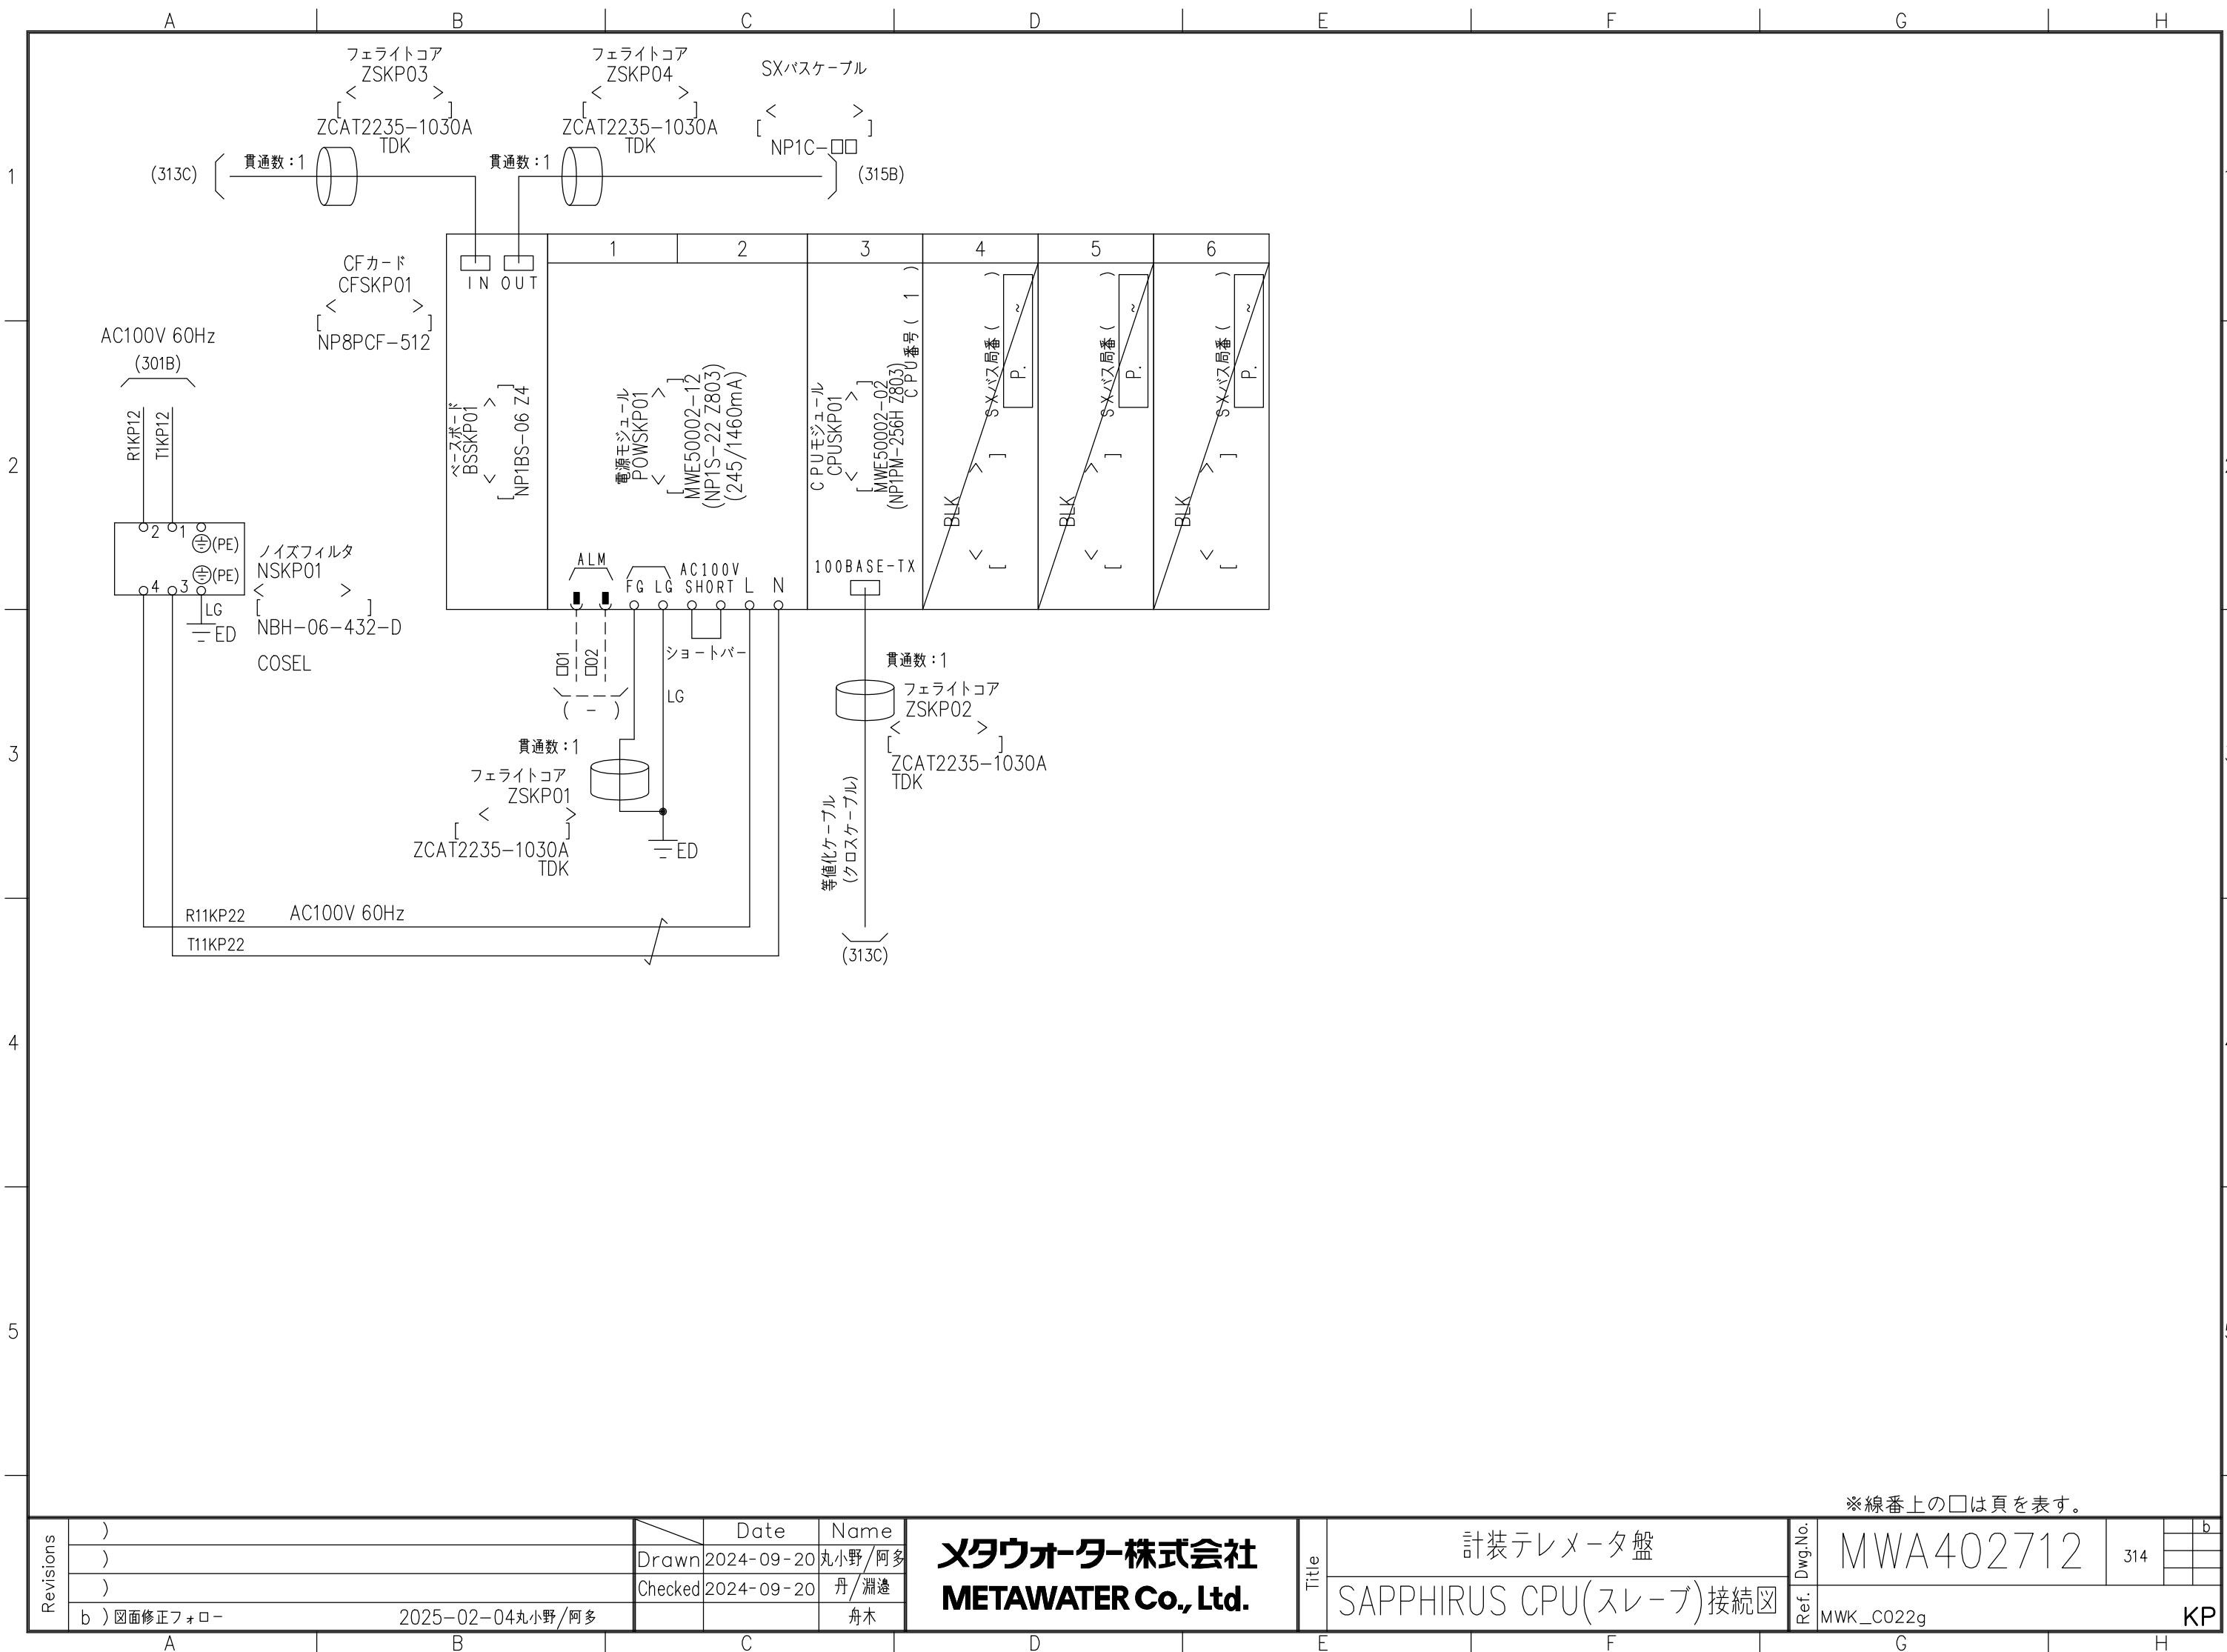


Revisions	)		Date	Name	メタウォーター株式会社 METAWATER Co., Ltd.	Title	計装テレメータ盤		Dwg.No.	MWA402712	314	b
	)	Drawn	2024-09-20	丸小野/阿多			SAPPHIRUS CPU(スレーブ)接続図					
	)	Checked	2024-09-20	丹/淵邊			Ref.	MWK_C022g	KP			
	b) 図面修正フォロー			舟木								

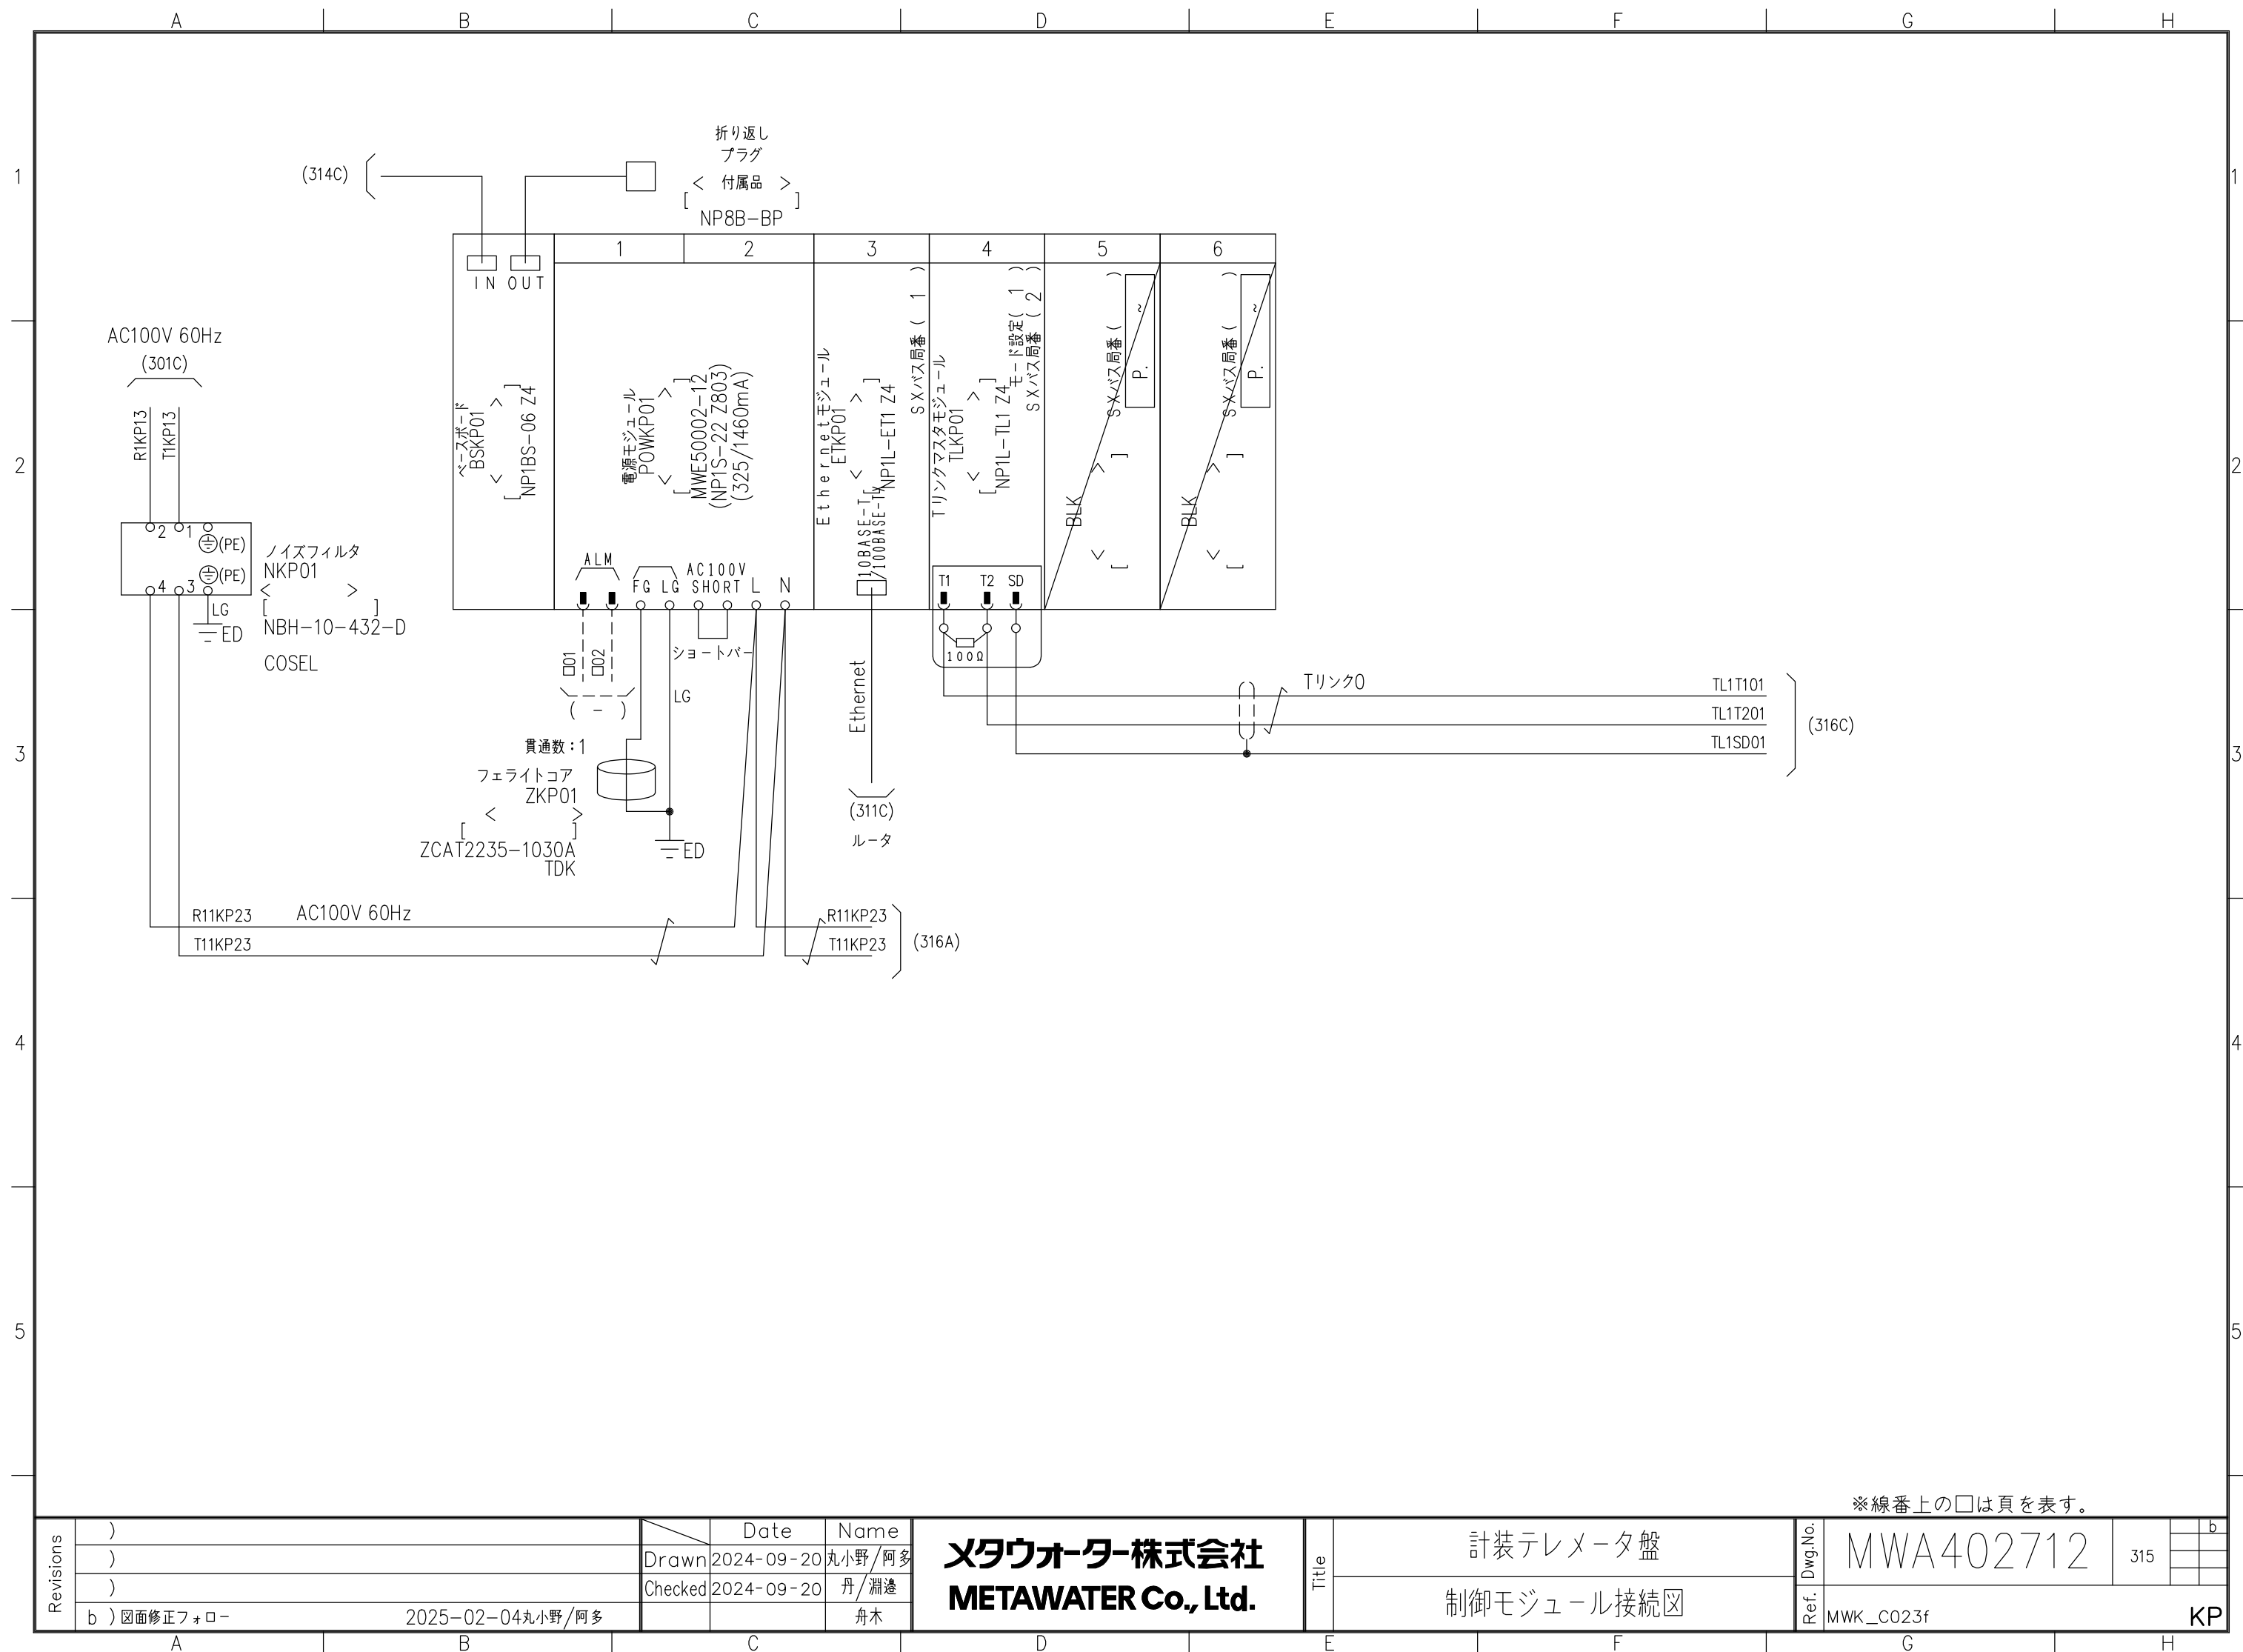


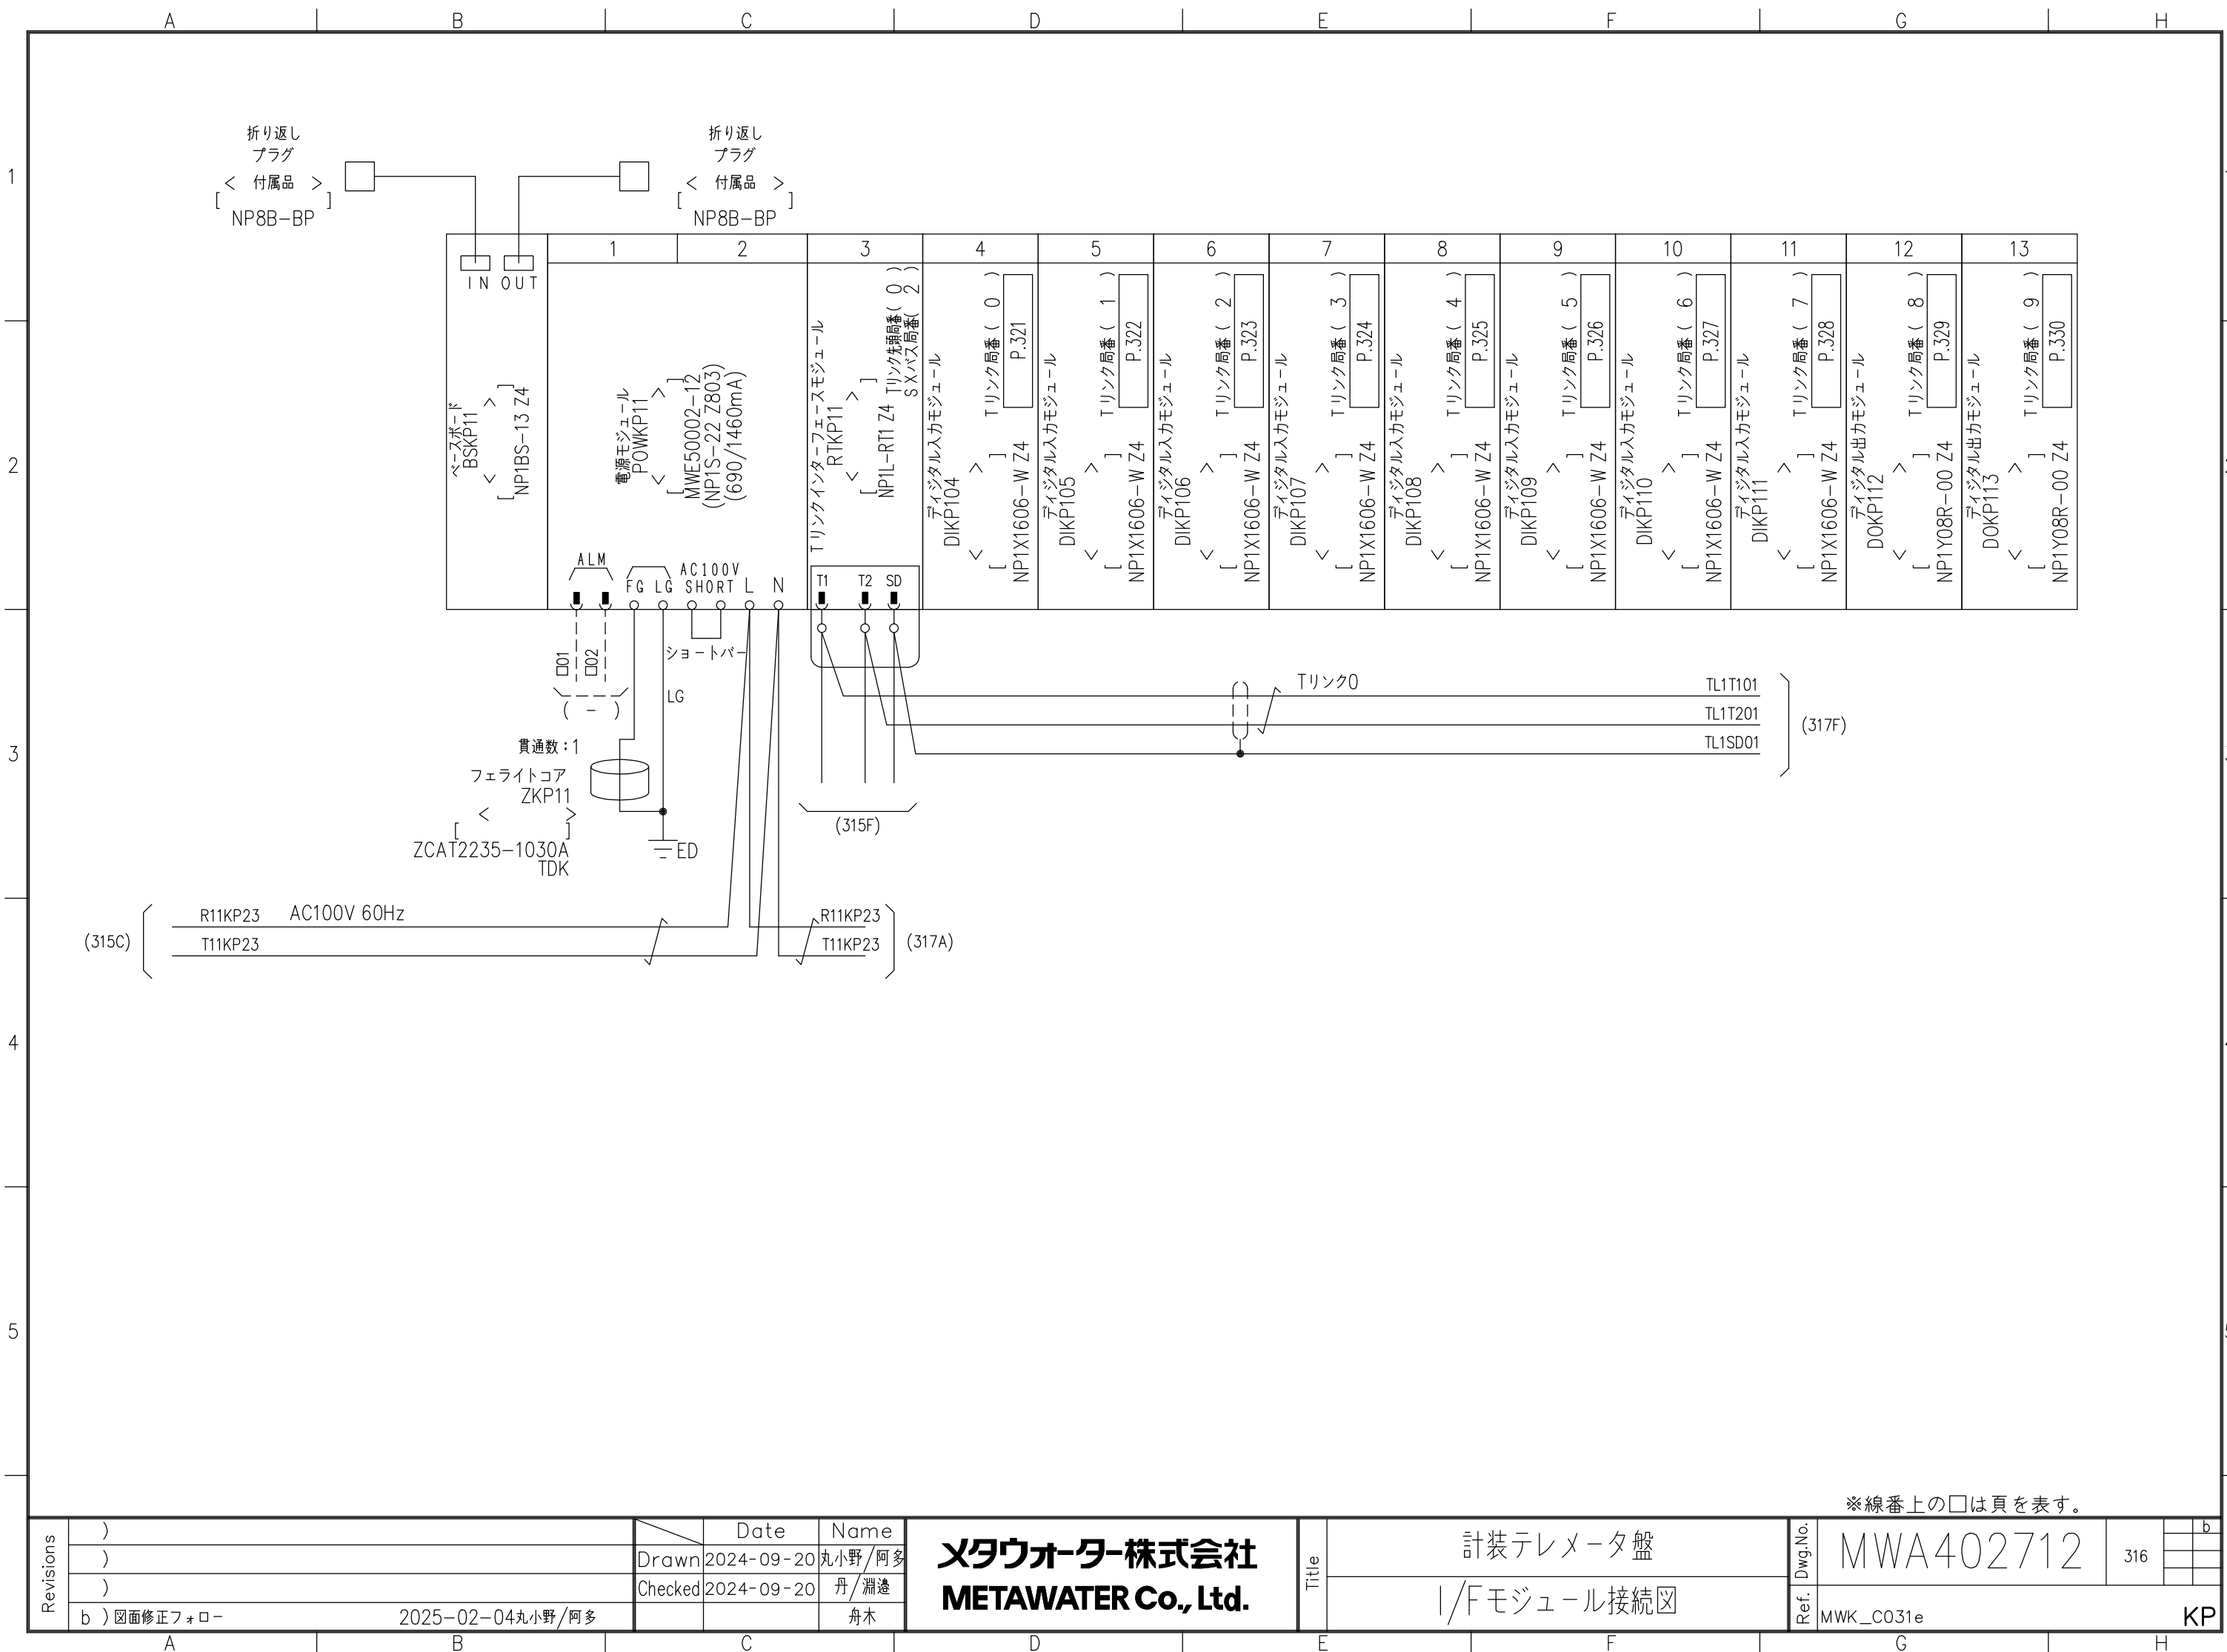

※線番上の□は頁を表す。

Revisions	)		Date	Name	メタウォーター株式会社 METAWATER Co., Ltd.	Title	計装テレメータ盤		Dwg.No.	MWA402712	316		b
	)	Drawn	2024-09-20	丸小野/阿多			I/Fモジュール接続図	Ref.	MWK_C031e	KP			
	)	Checked	2024-09-20	丹/淵邊									
	b) 図面修正フォロー		2025-02-04	丸小野/阿多							舟木		

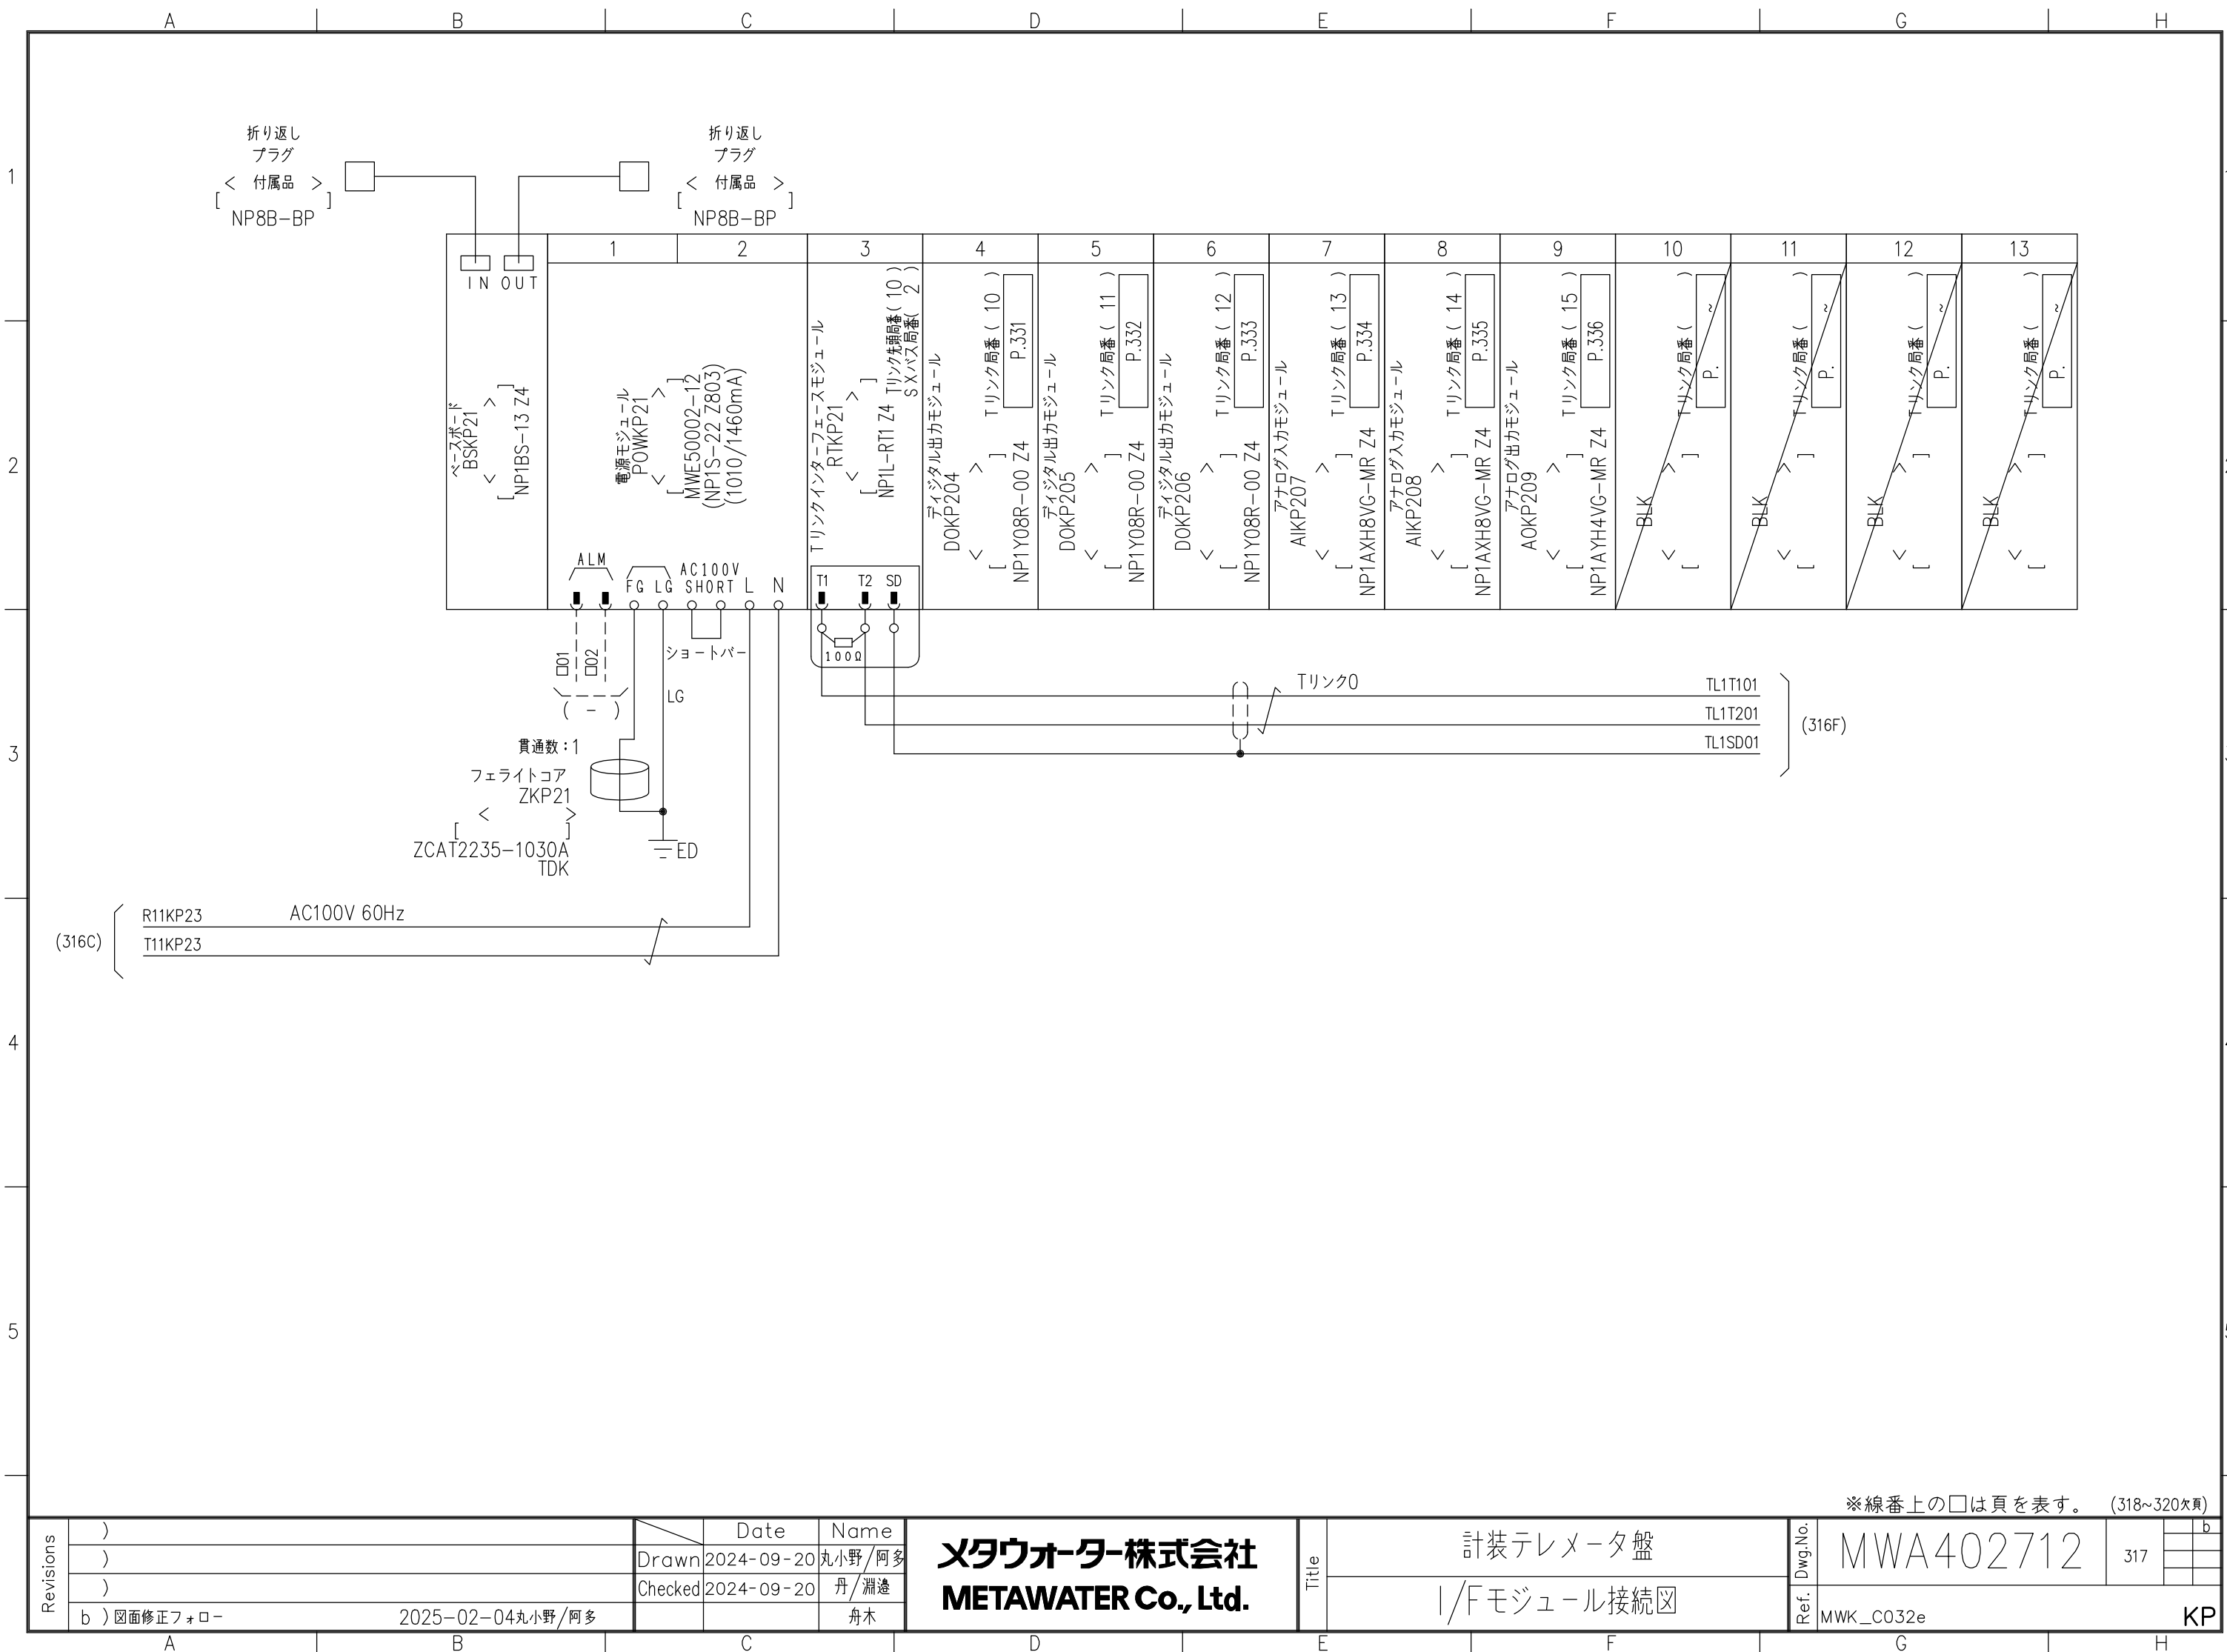

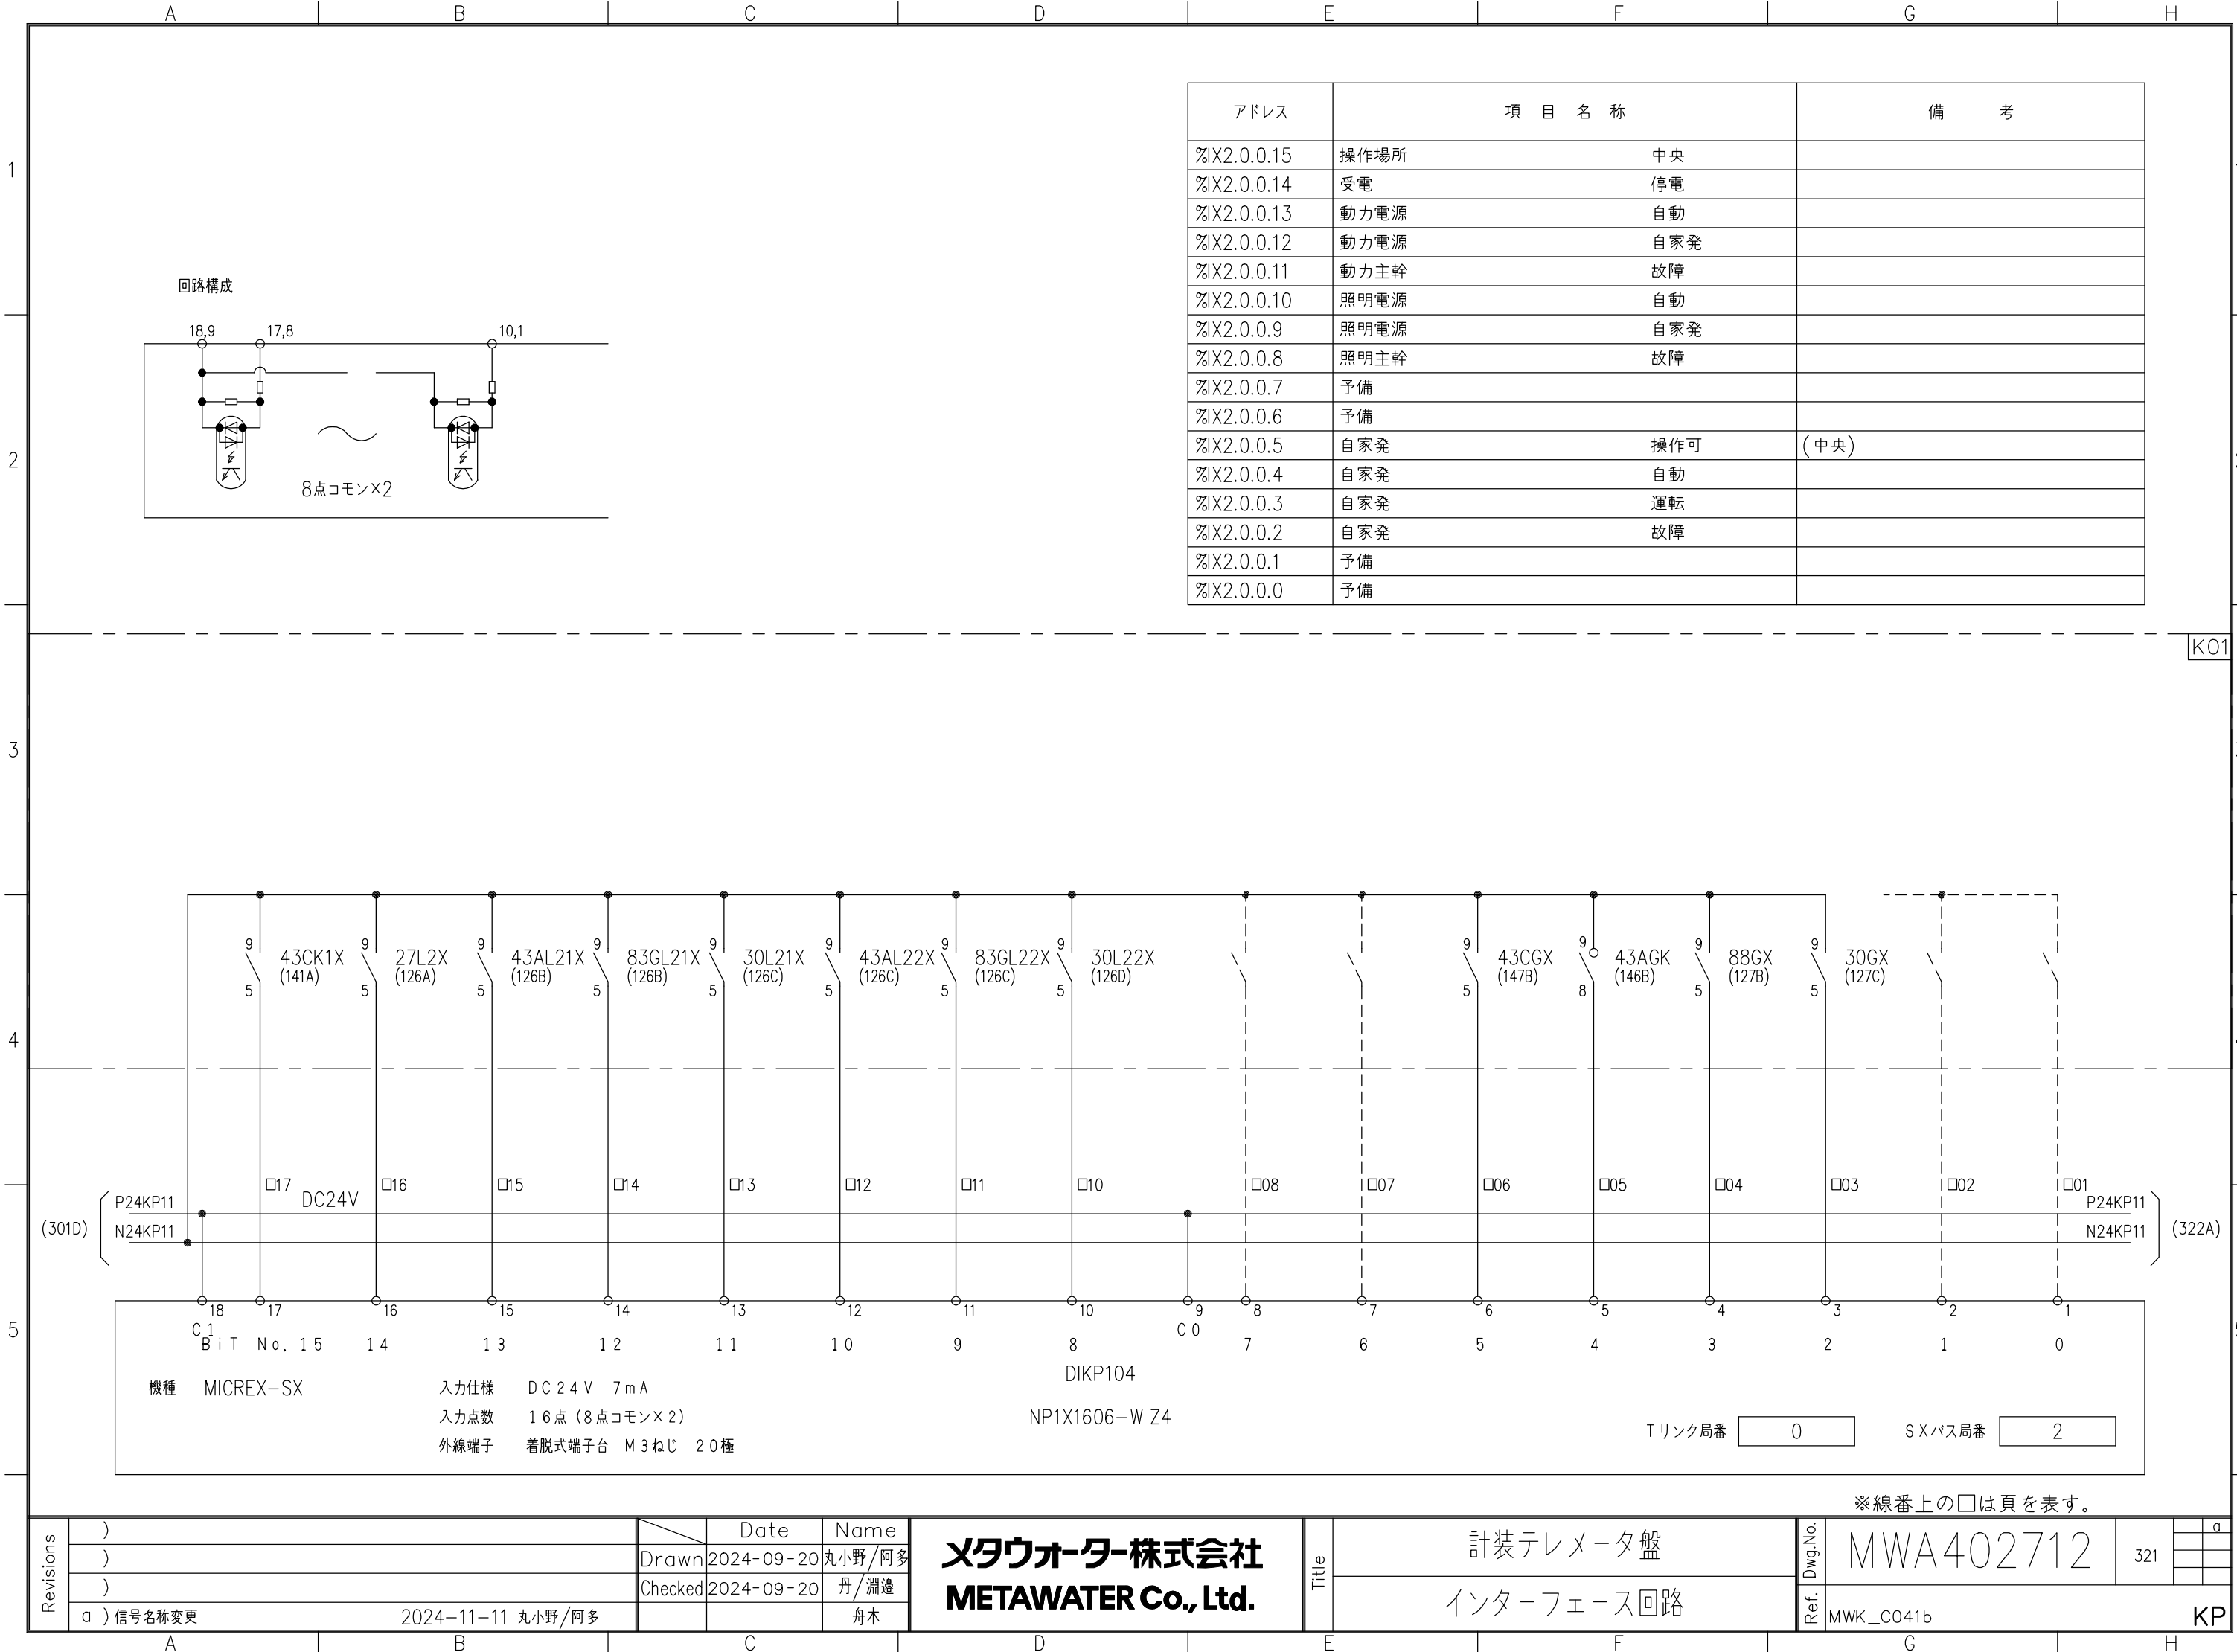

9

5

43AL22X
(126C)

9

5

9

5

83GL22X
(126C)

9

5

9

5

30L22X
(126D)

9

5

43CGX
(147B)

9

8

9

5

43AGK
(146B)

9

5

88GX
(127B)

9

5

30GX
(127C)

P24KP11

N24KP11

(301D)

□17

DC24V

□16

□15

□14

□13

□12

□11

□10

□08

□07

□06

□05

□04

□03

□02

□01

P24KP11

N24KP11

(322A)

C 1

18

17

16

15

14

13

12

11

10

9

C 0

8

7

6

5

4

3

2

1

0

機種

MICREX-SX

入力仕様

DC 2 4 V 7 m A

入力点数

1 6 点 (8 点コモン×2)

外線端子

着脱式端子台 M 3 ねじ 2 0 極

DIKP104

NP1X1606-W Z4

Tリンク局番

0

SXバス局番

2

※線番上の□は頁を表す。

Revisions

)

)

)

a) 信号名称変更

2024-11-11

丸小野/阿多

Date

2024-09-20

2024-09-20

Name

丸小野/阿多

丹/淵邊

舟木

メタウォーター株式会社

METAWATER Co., Ltd.

Title

計装テレメータ盤

インターフェース回路

Dwg.No.


MWA402712



321


Ref.

MWK_C041b

KP

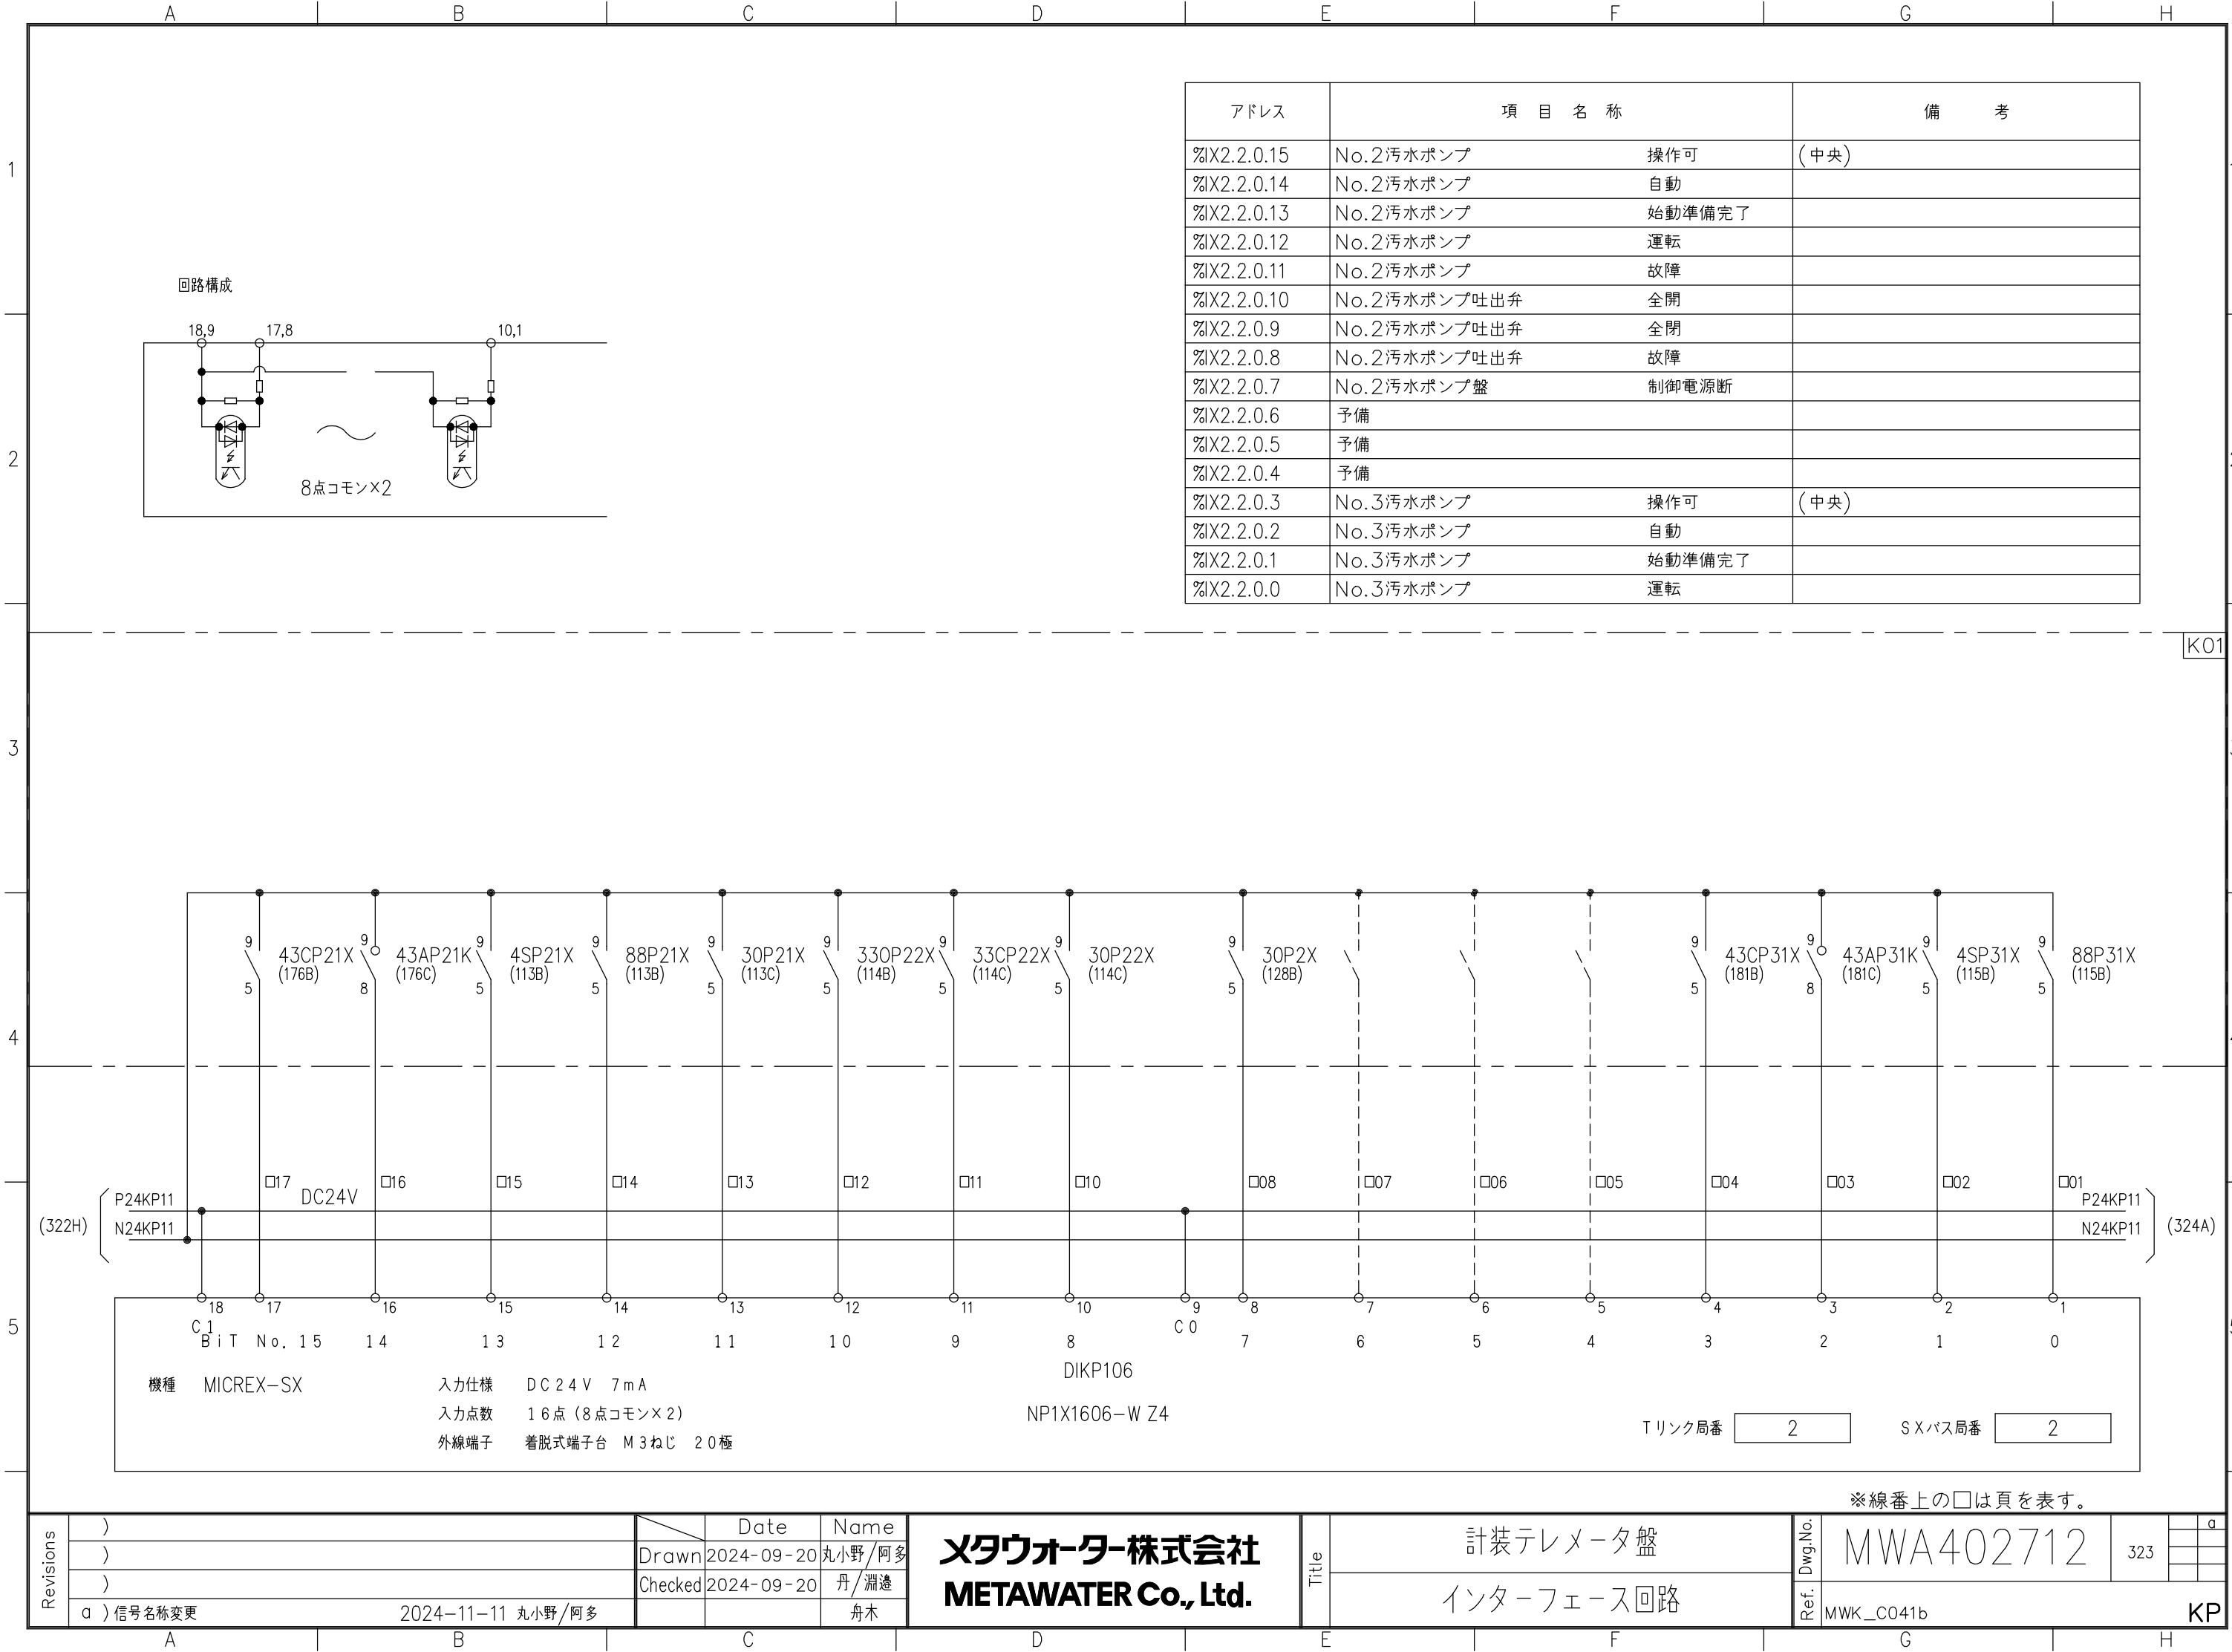

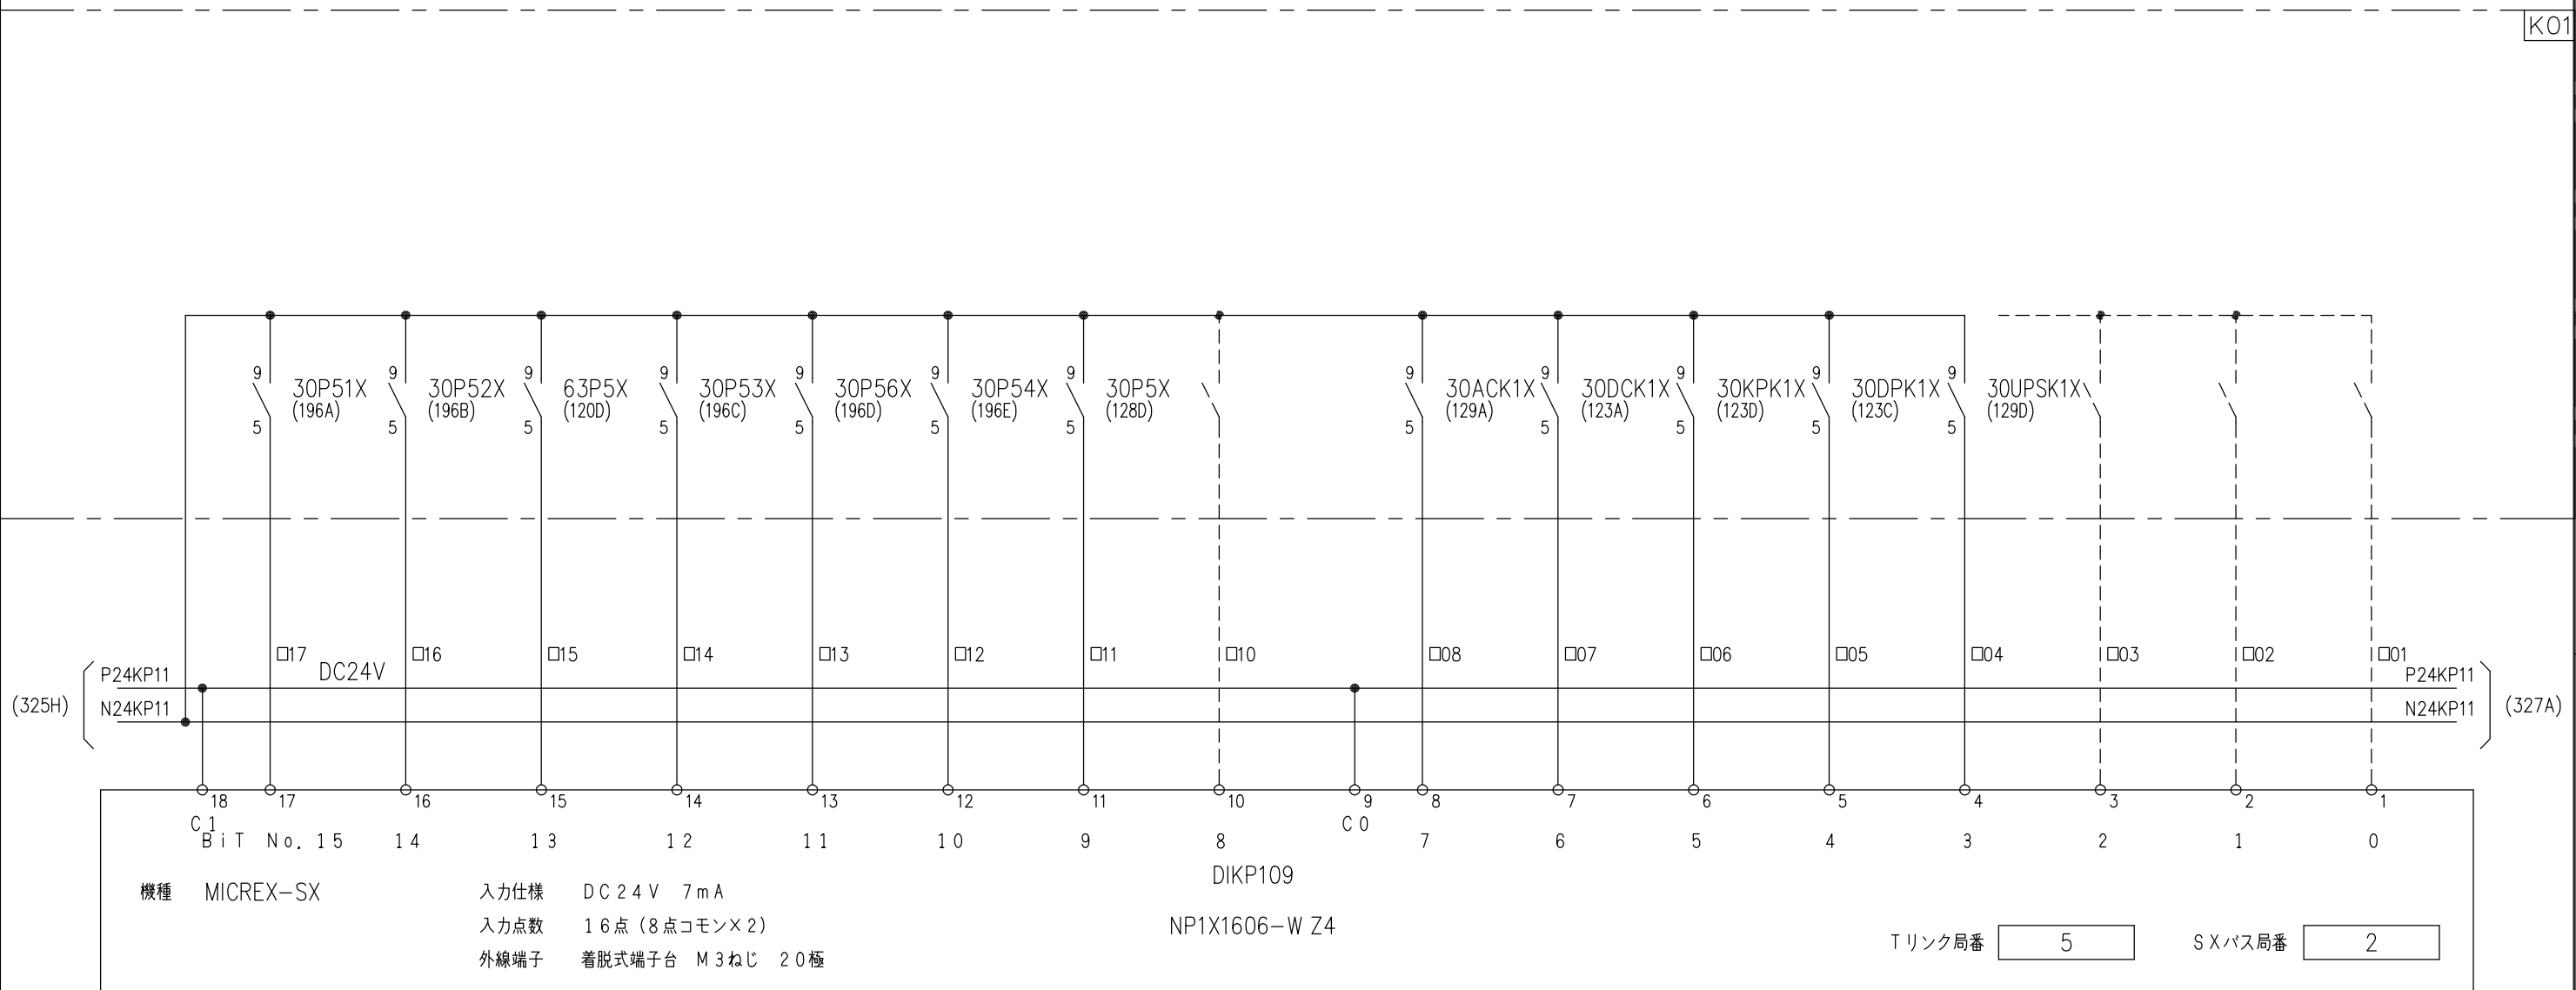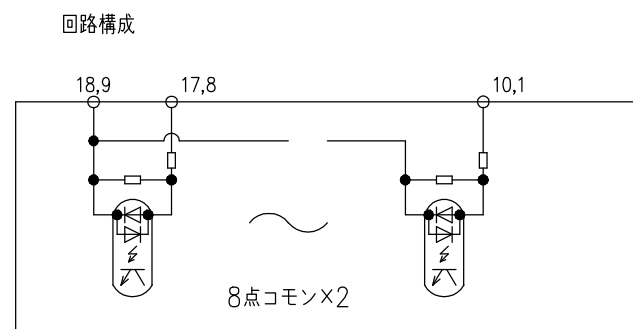

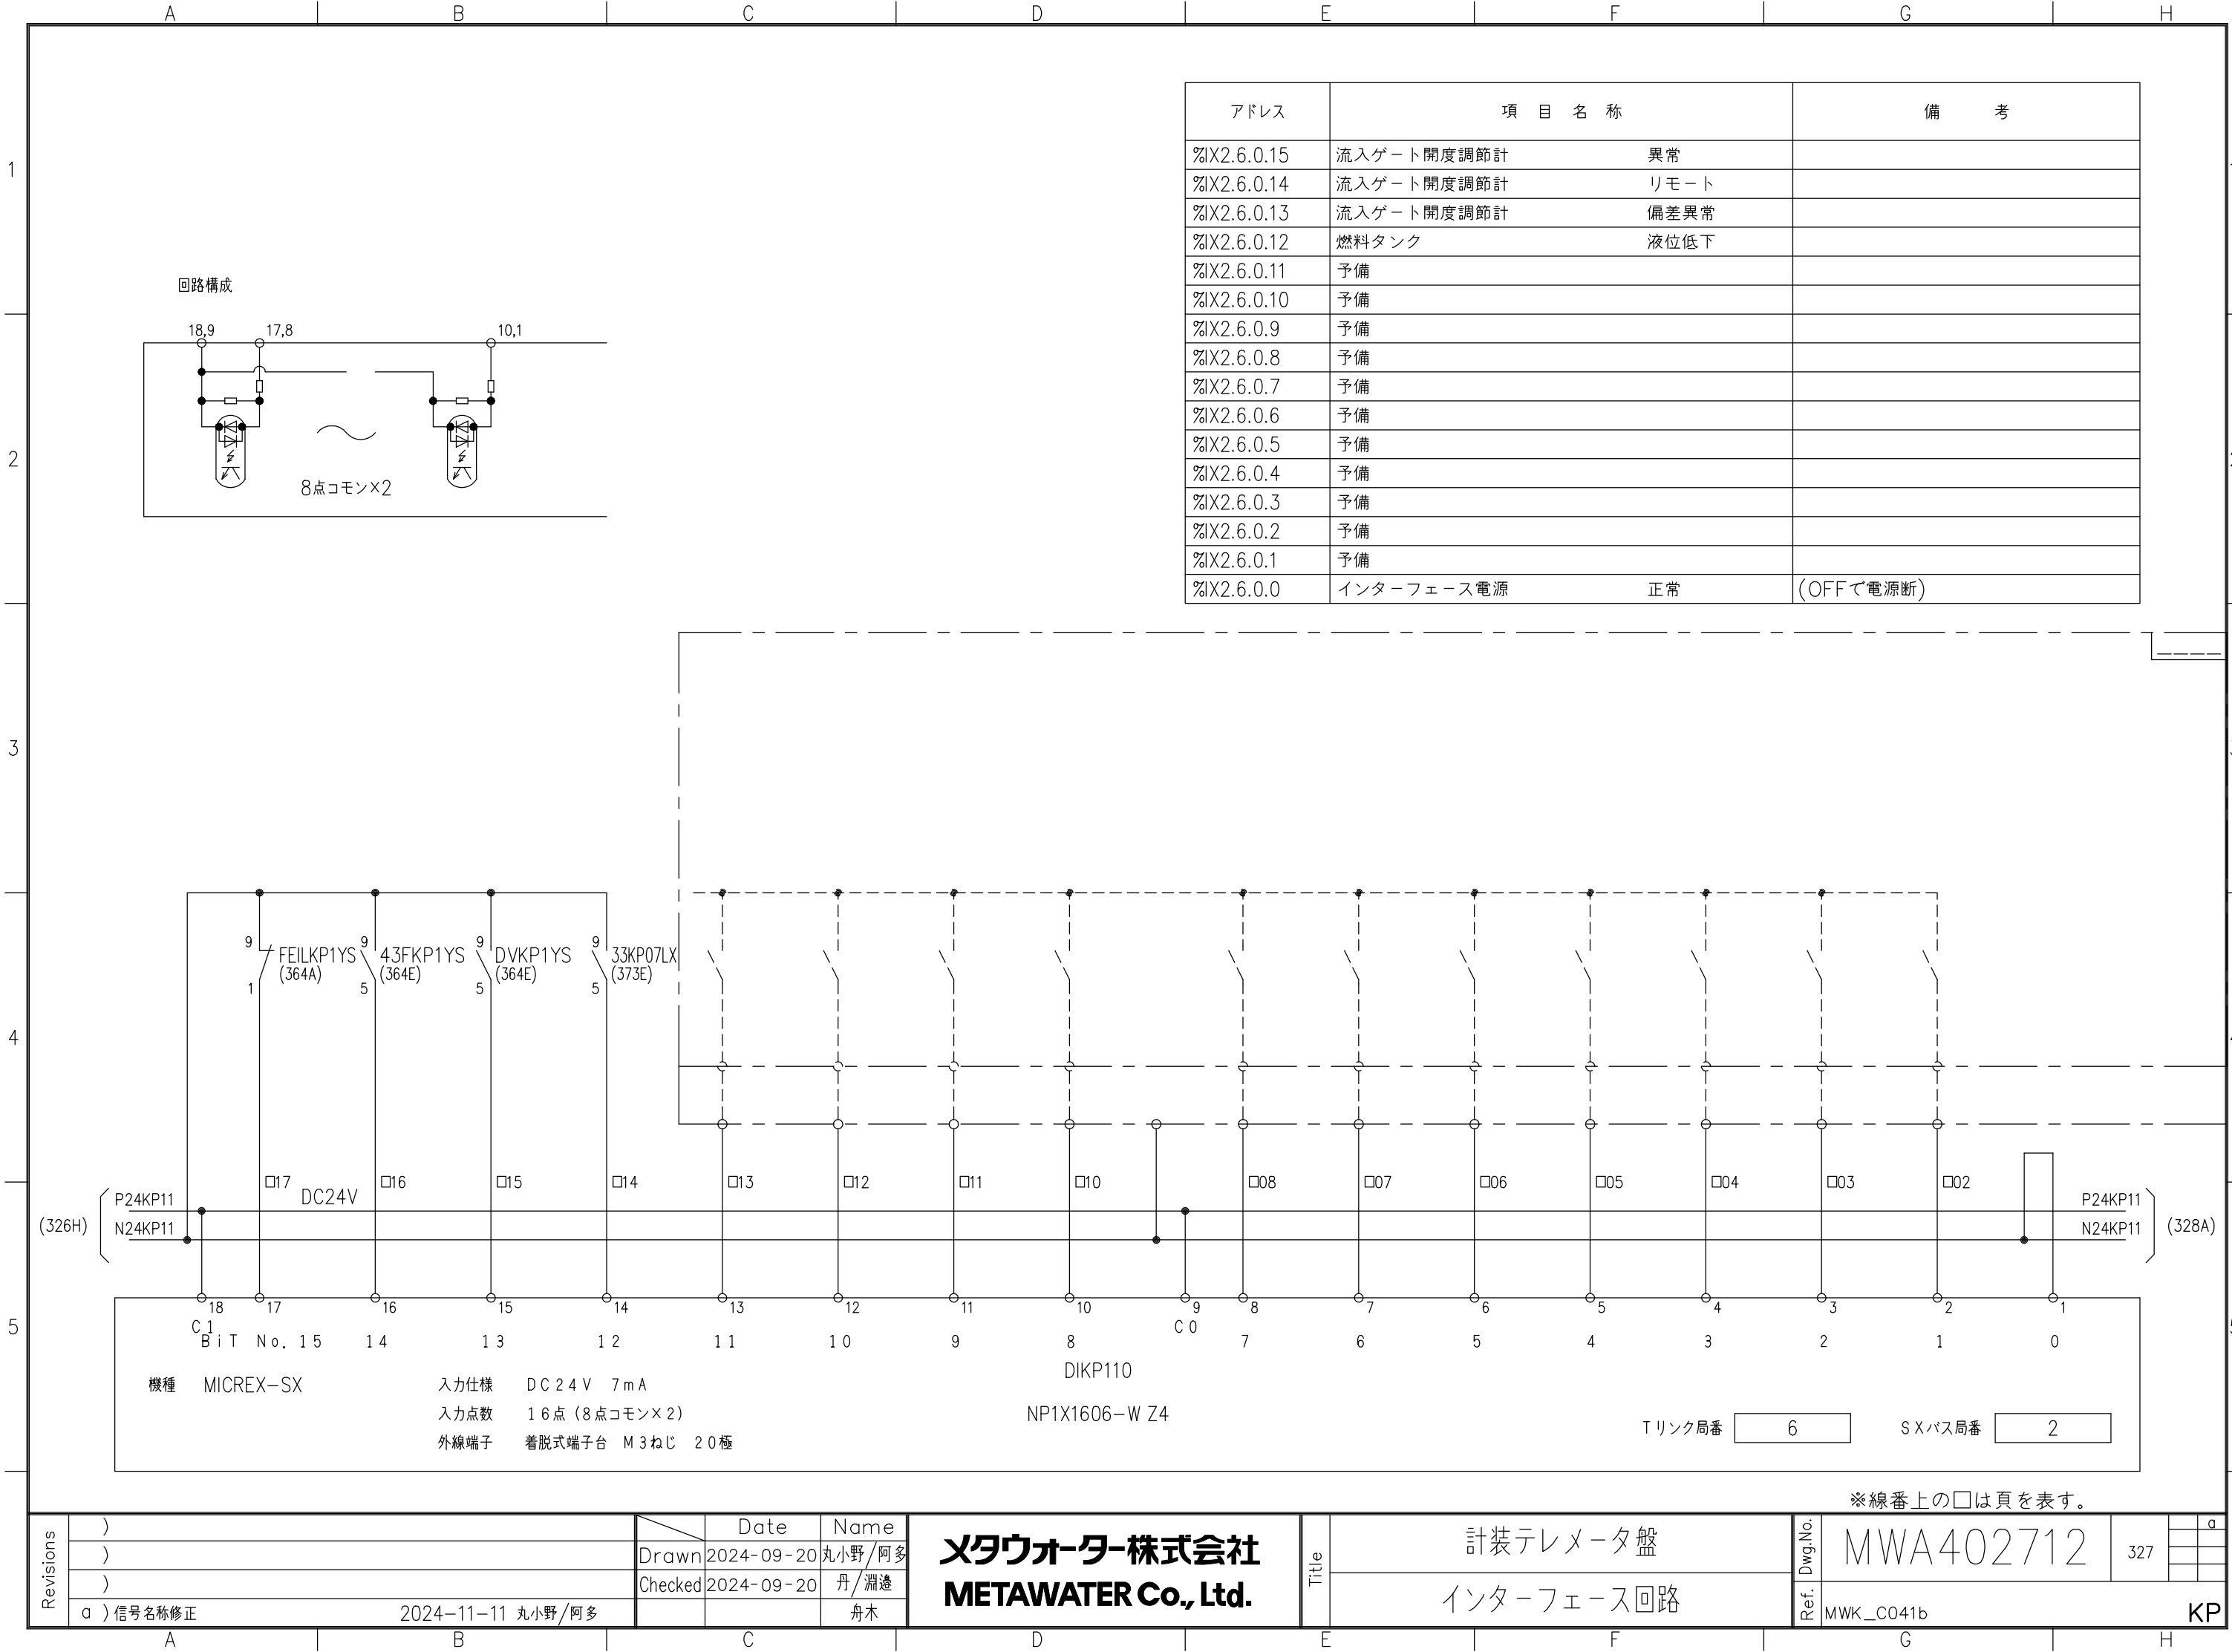

9

5

33KP07LX
(373E)

□17

DC24V

□16

□15

□14

□13

□12

□11

□10

□08

□07

□06

□05

□04

□03

□02

P24KP11
N24KP11

(326H)

18

17

16

15

14

13

12

11

10

9

8

7

6

5

4

3

2

1

0

C 1

BIT No. 15

14

13

12

11

10

9

C 0

7

6

5

4

3

2

1

0

機種

MICREX-SX

入力仕様

DC 24V 7mA

入力点数

16点 (8点コモン×2)

外線端子

着脱式端子台 M3ねじ 20極

DIKP110

NP1X1606-W Z4

Tリンク局番

6

SXバス局番

2

P24KP11
N24KP11

(328A)

※線番上の□は頁を表す。

Revisions

)

)

)

a) 信号名称修正

Drawn

2024-09-20

丸小野/阿多

Checked

2024-09-20

丹/淵邊

舟木

Date

2024-09-20

2024-09-20

Name

丸小野/阿多

丹/淵邊

舟木

メタウォーター株式会社

METAWATER Co., Ltd.

Title

計装テレメータ盤

インターフェース回路

Dwg.No.

MWA402712


327

Ref.

MWK_C041b

KP

a

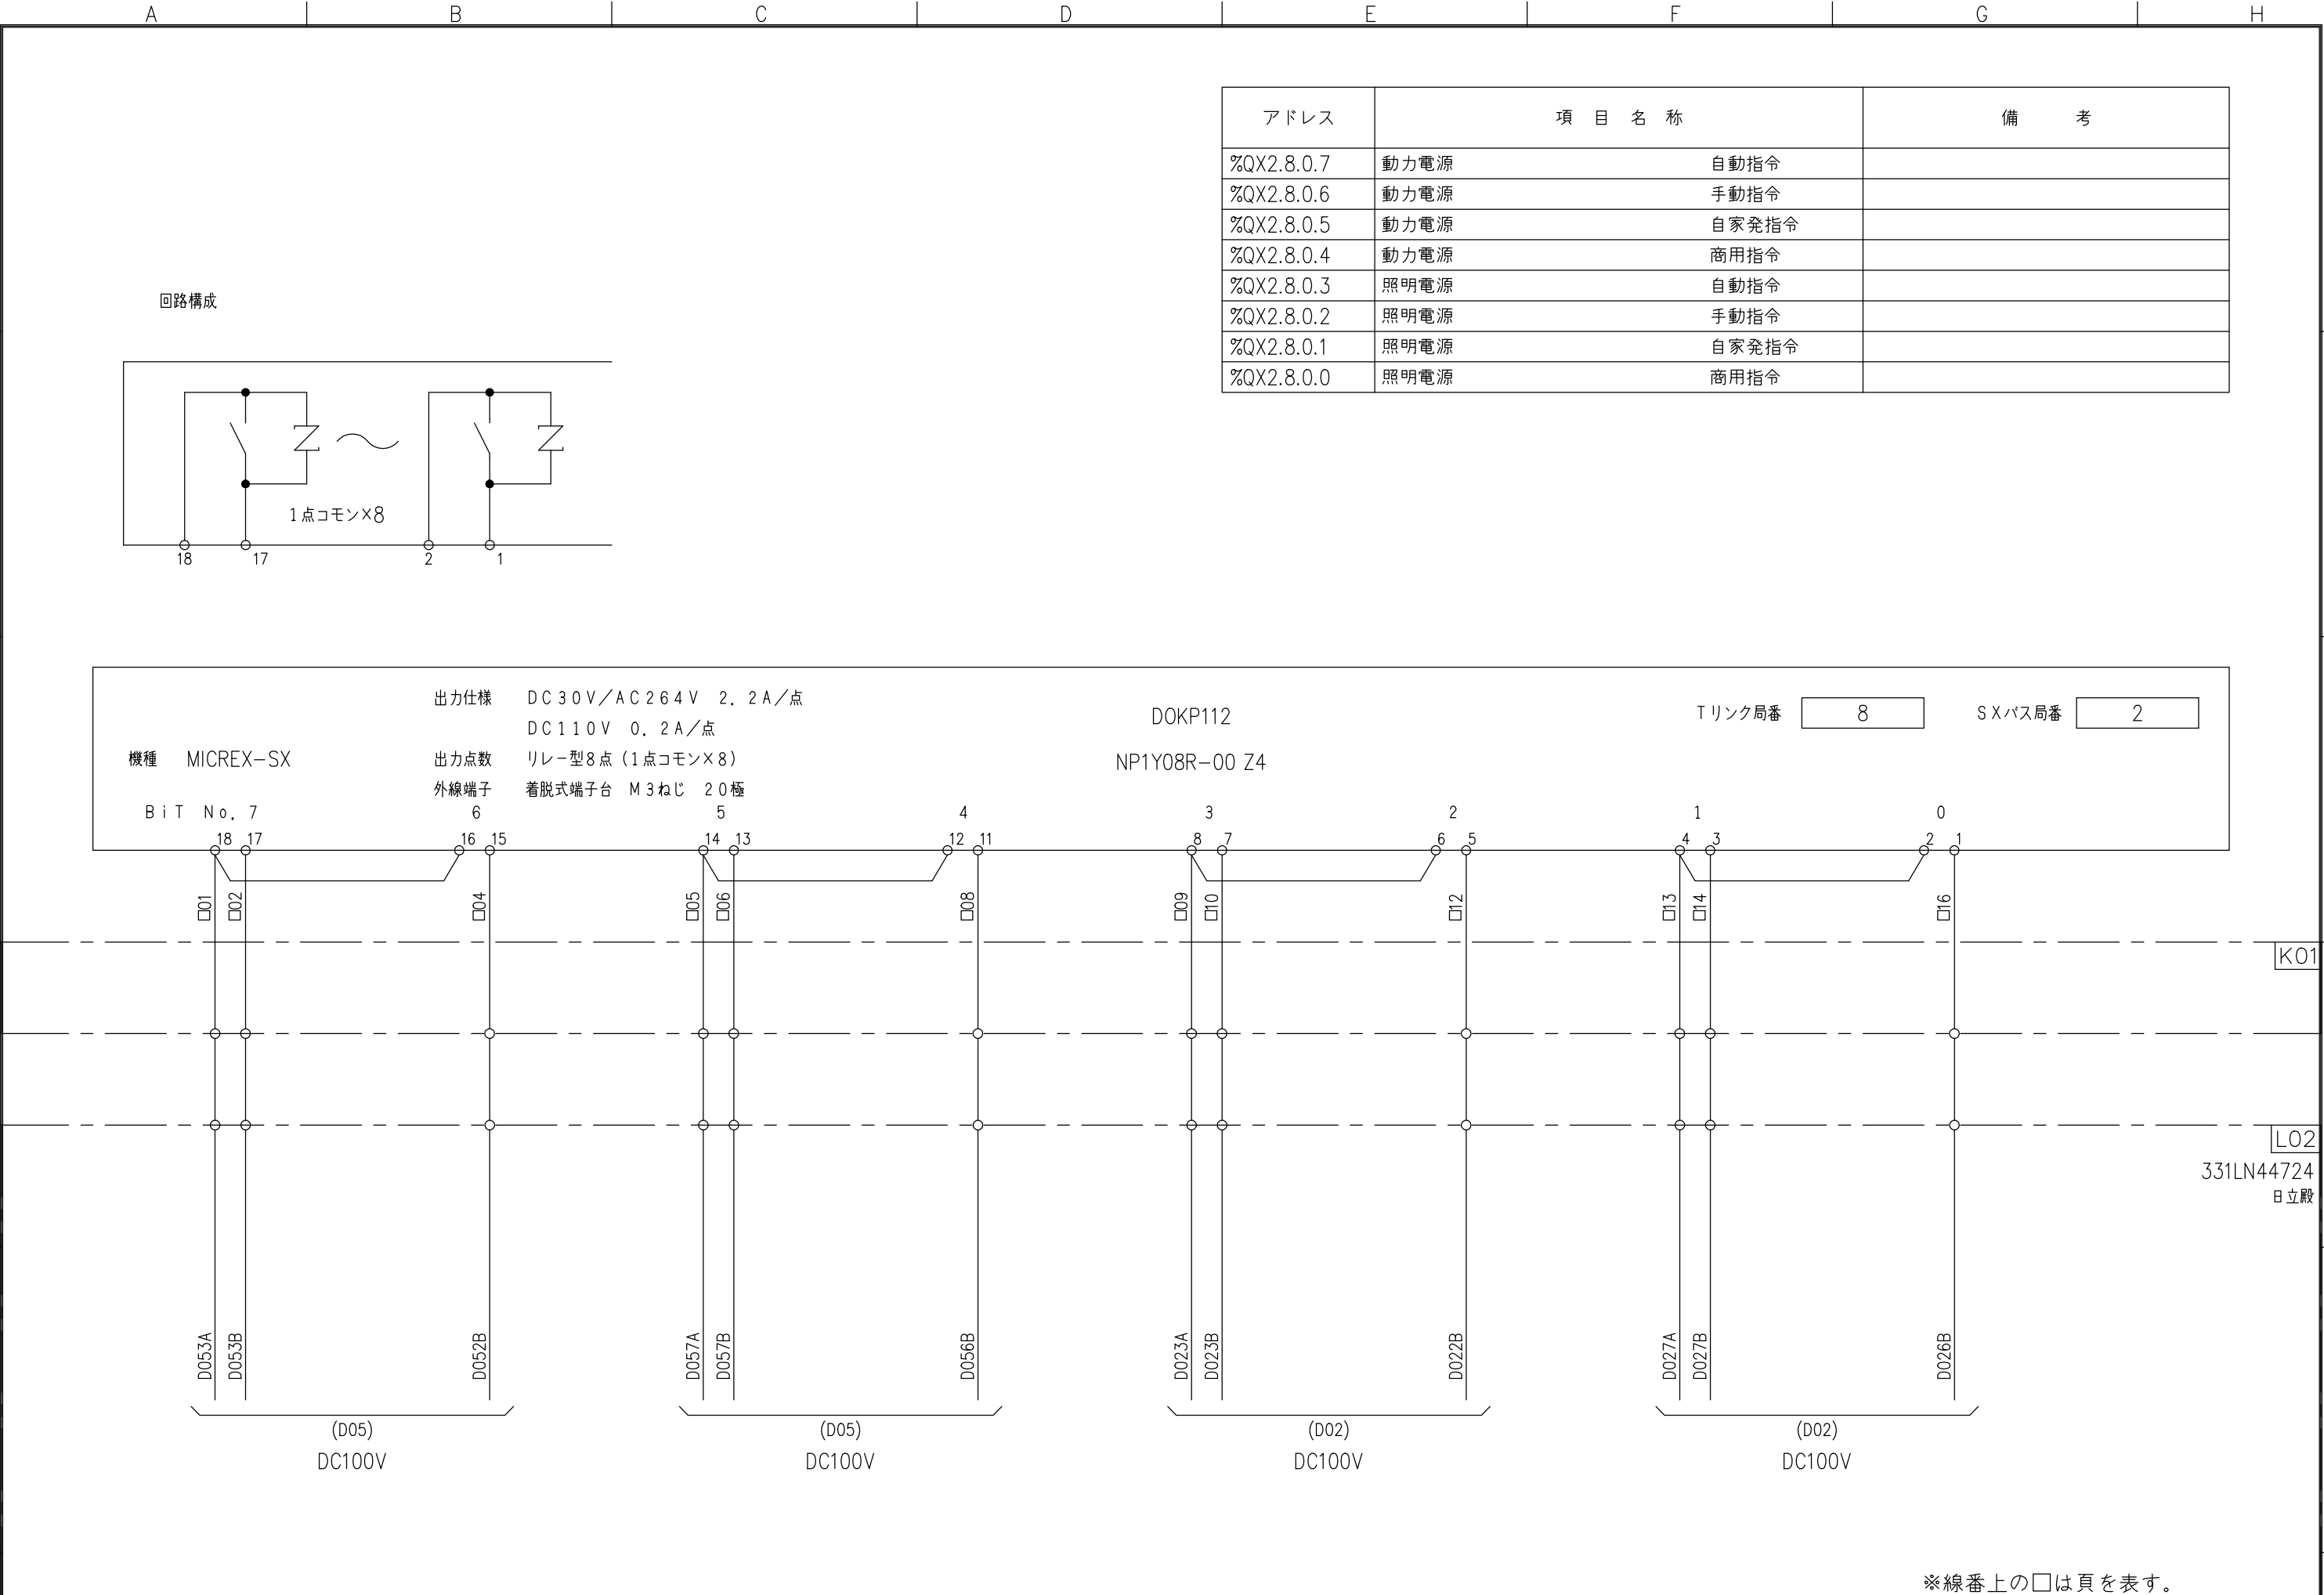


K01

L02


331LN44724


日立殿

アドレス	項目名称	備考
%QX2.8.0.7	動力電源	自動指令
%QX2.8.0.6	動力電源	手動指令
%QX2.8.0.5	動力電源	自家発指令
%QX2.8.0.4	動力電源	商用指令
%QX2.8.0.3	照明電源	自動指令
%QX2.8.0.2	照明電源	手動指令
%QX2.8.0.1	照明電源	自家発指令
%QX2.8.0.0	照明電源	商用指令

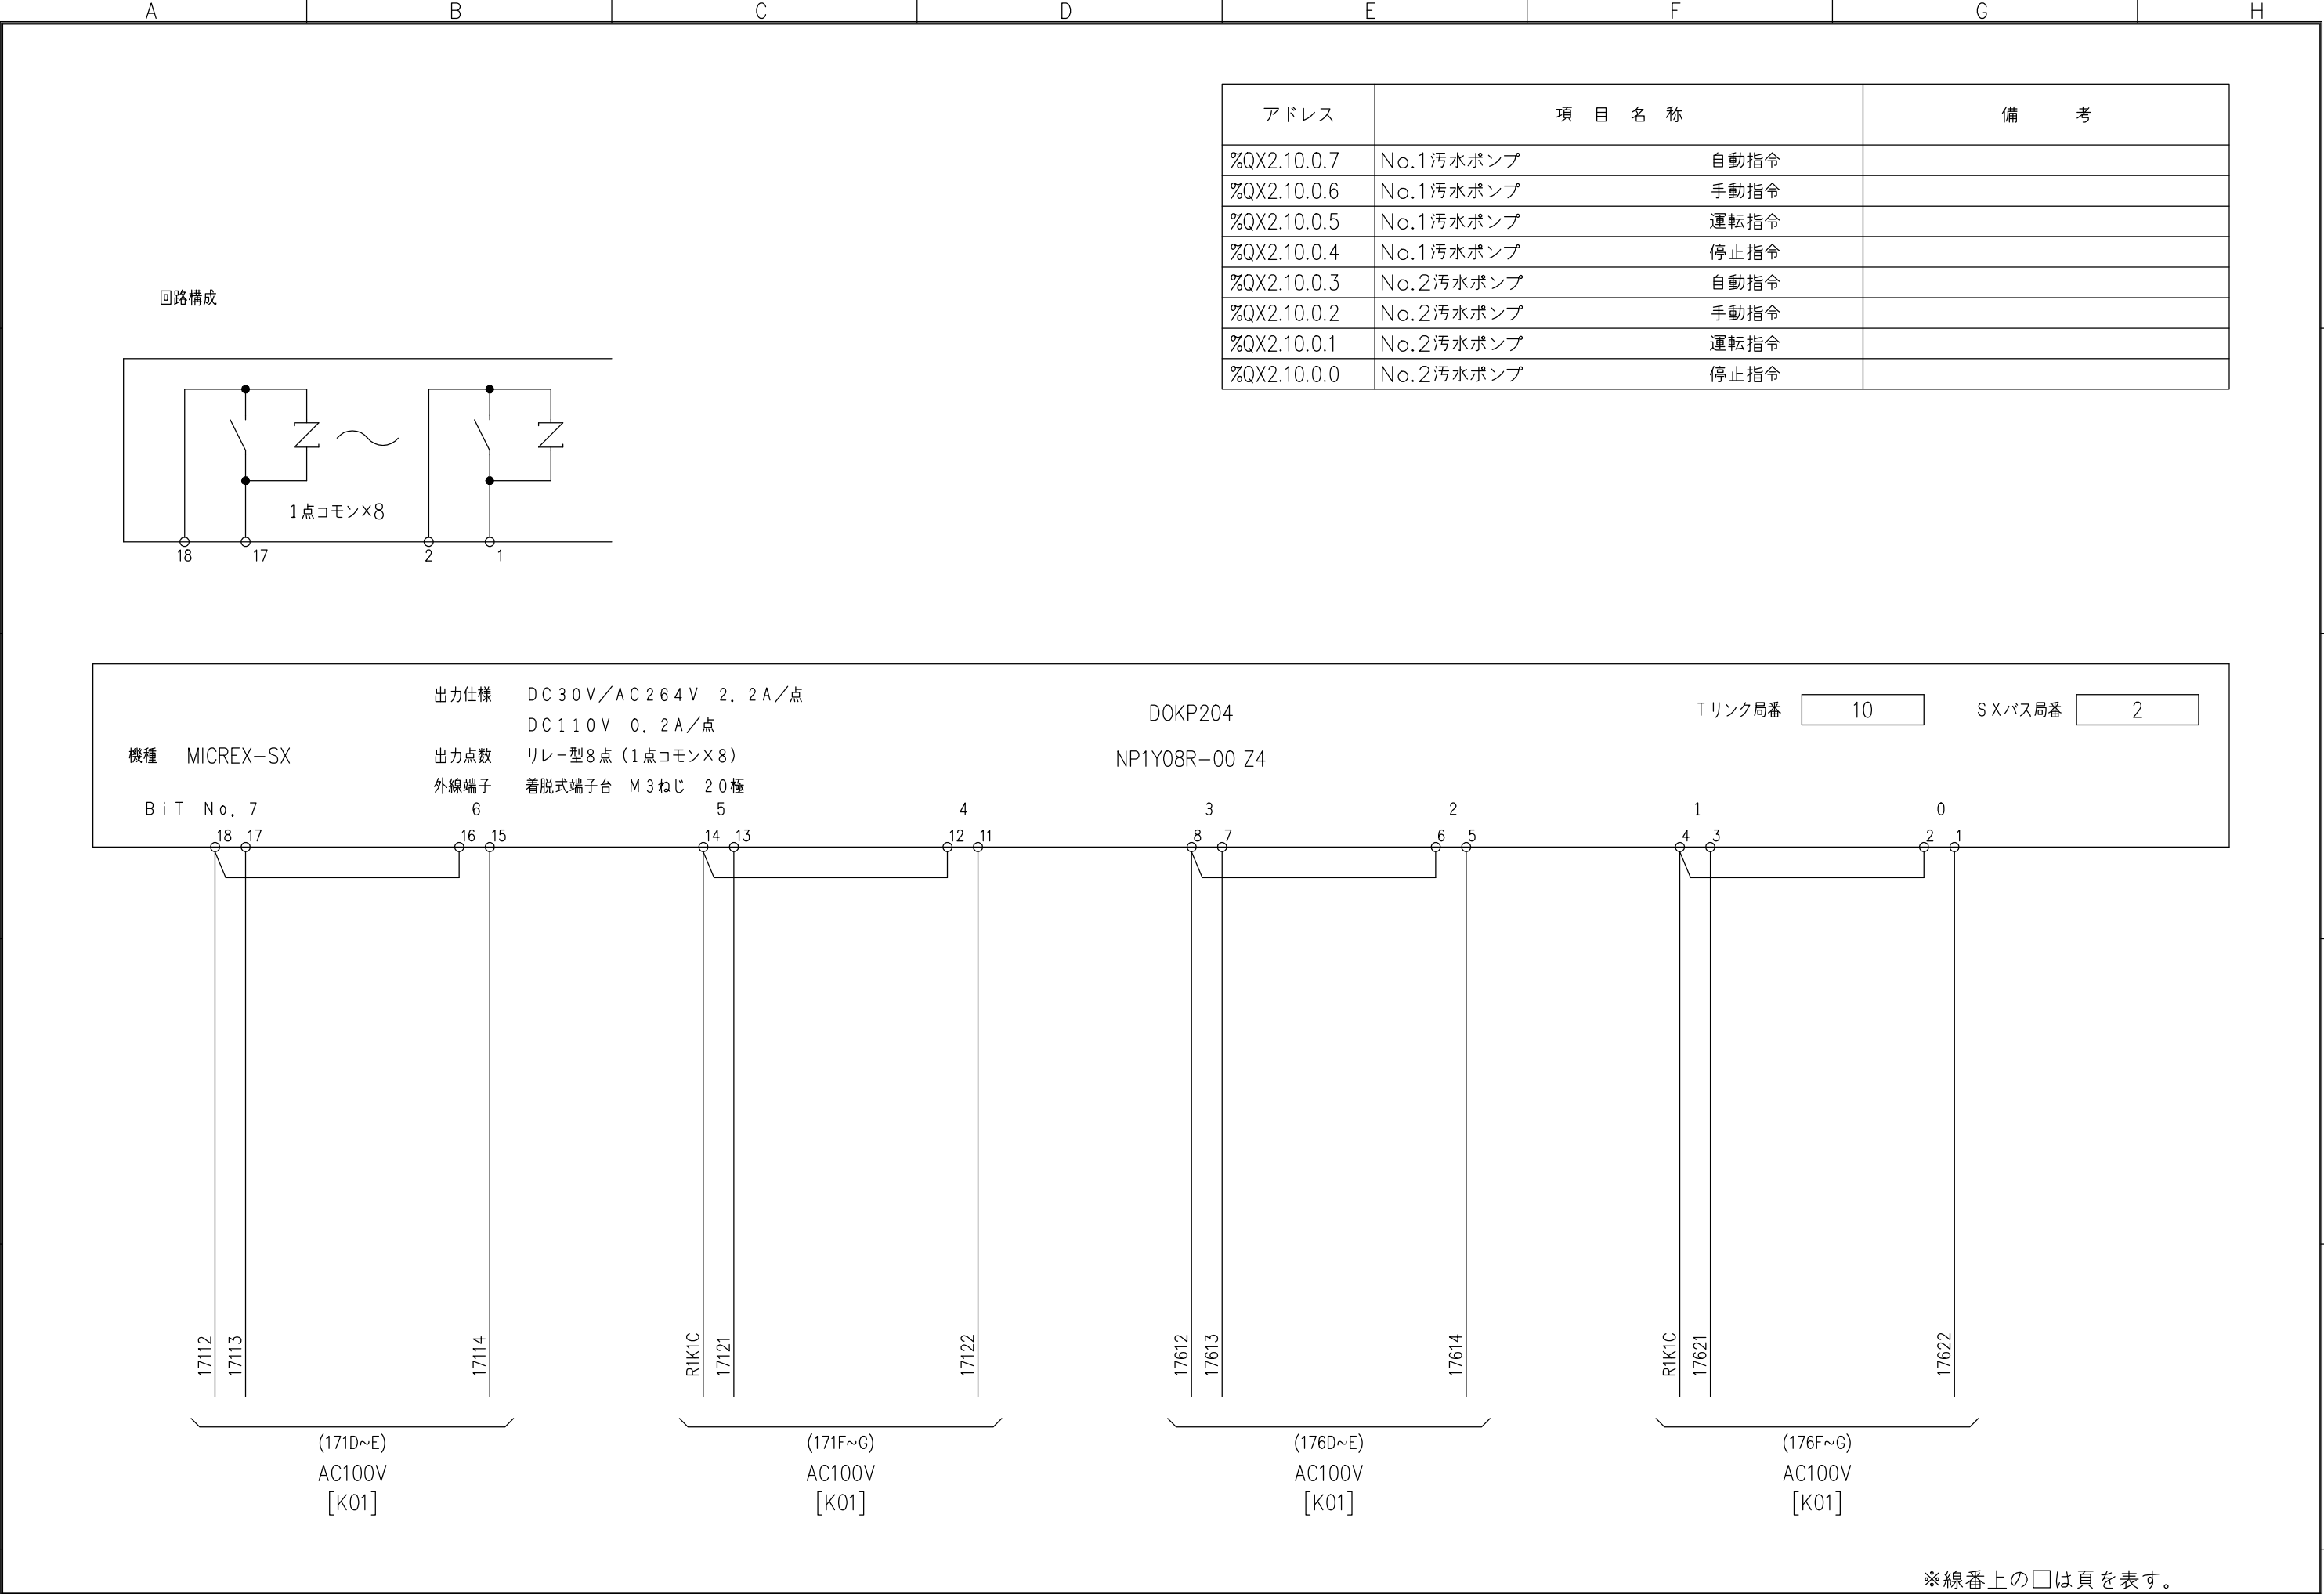

アドレス	項目名称		備考
%QX2.10.0.7	No.1汚水ポンプ	自動指令	
%QX2.10.0.6	No.1汚水ポンプ	手動指令	
%QX2.10.0.5	No.1汚水ポンプ	運転指令	
%QX2.10.0.4	No.1汚水ポンプ	停止指令	
%QX2.10.0.3	No.2汚水ポンプ	自動指令	
%QX2.10.0.2	No.2汚水ポンプ	手動指令	
%QX2.10.0.1	No.2汚水ポンプ	運転指令	
%QX2.10.0.0	No.2汚水ポンプ	停止指令	

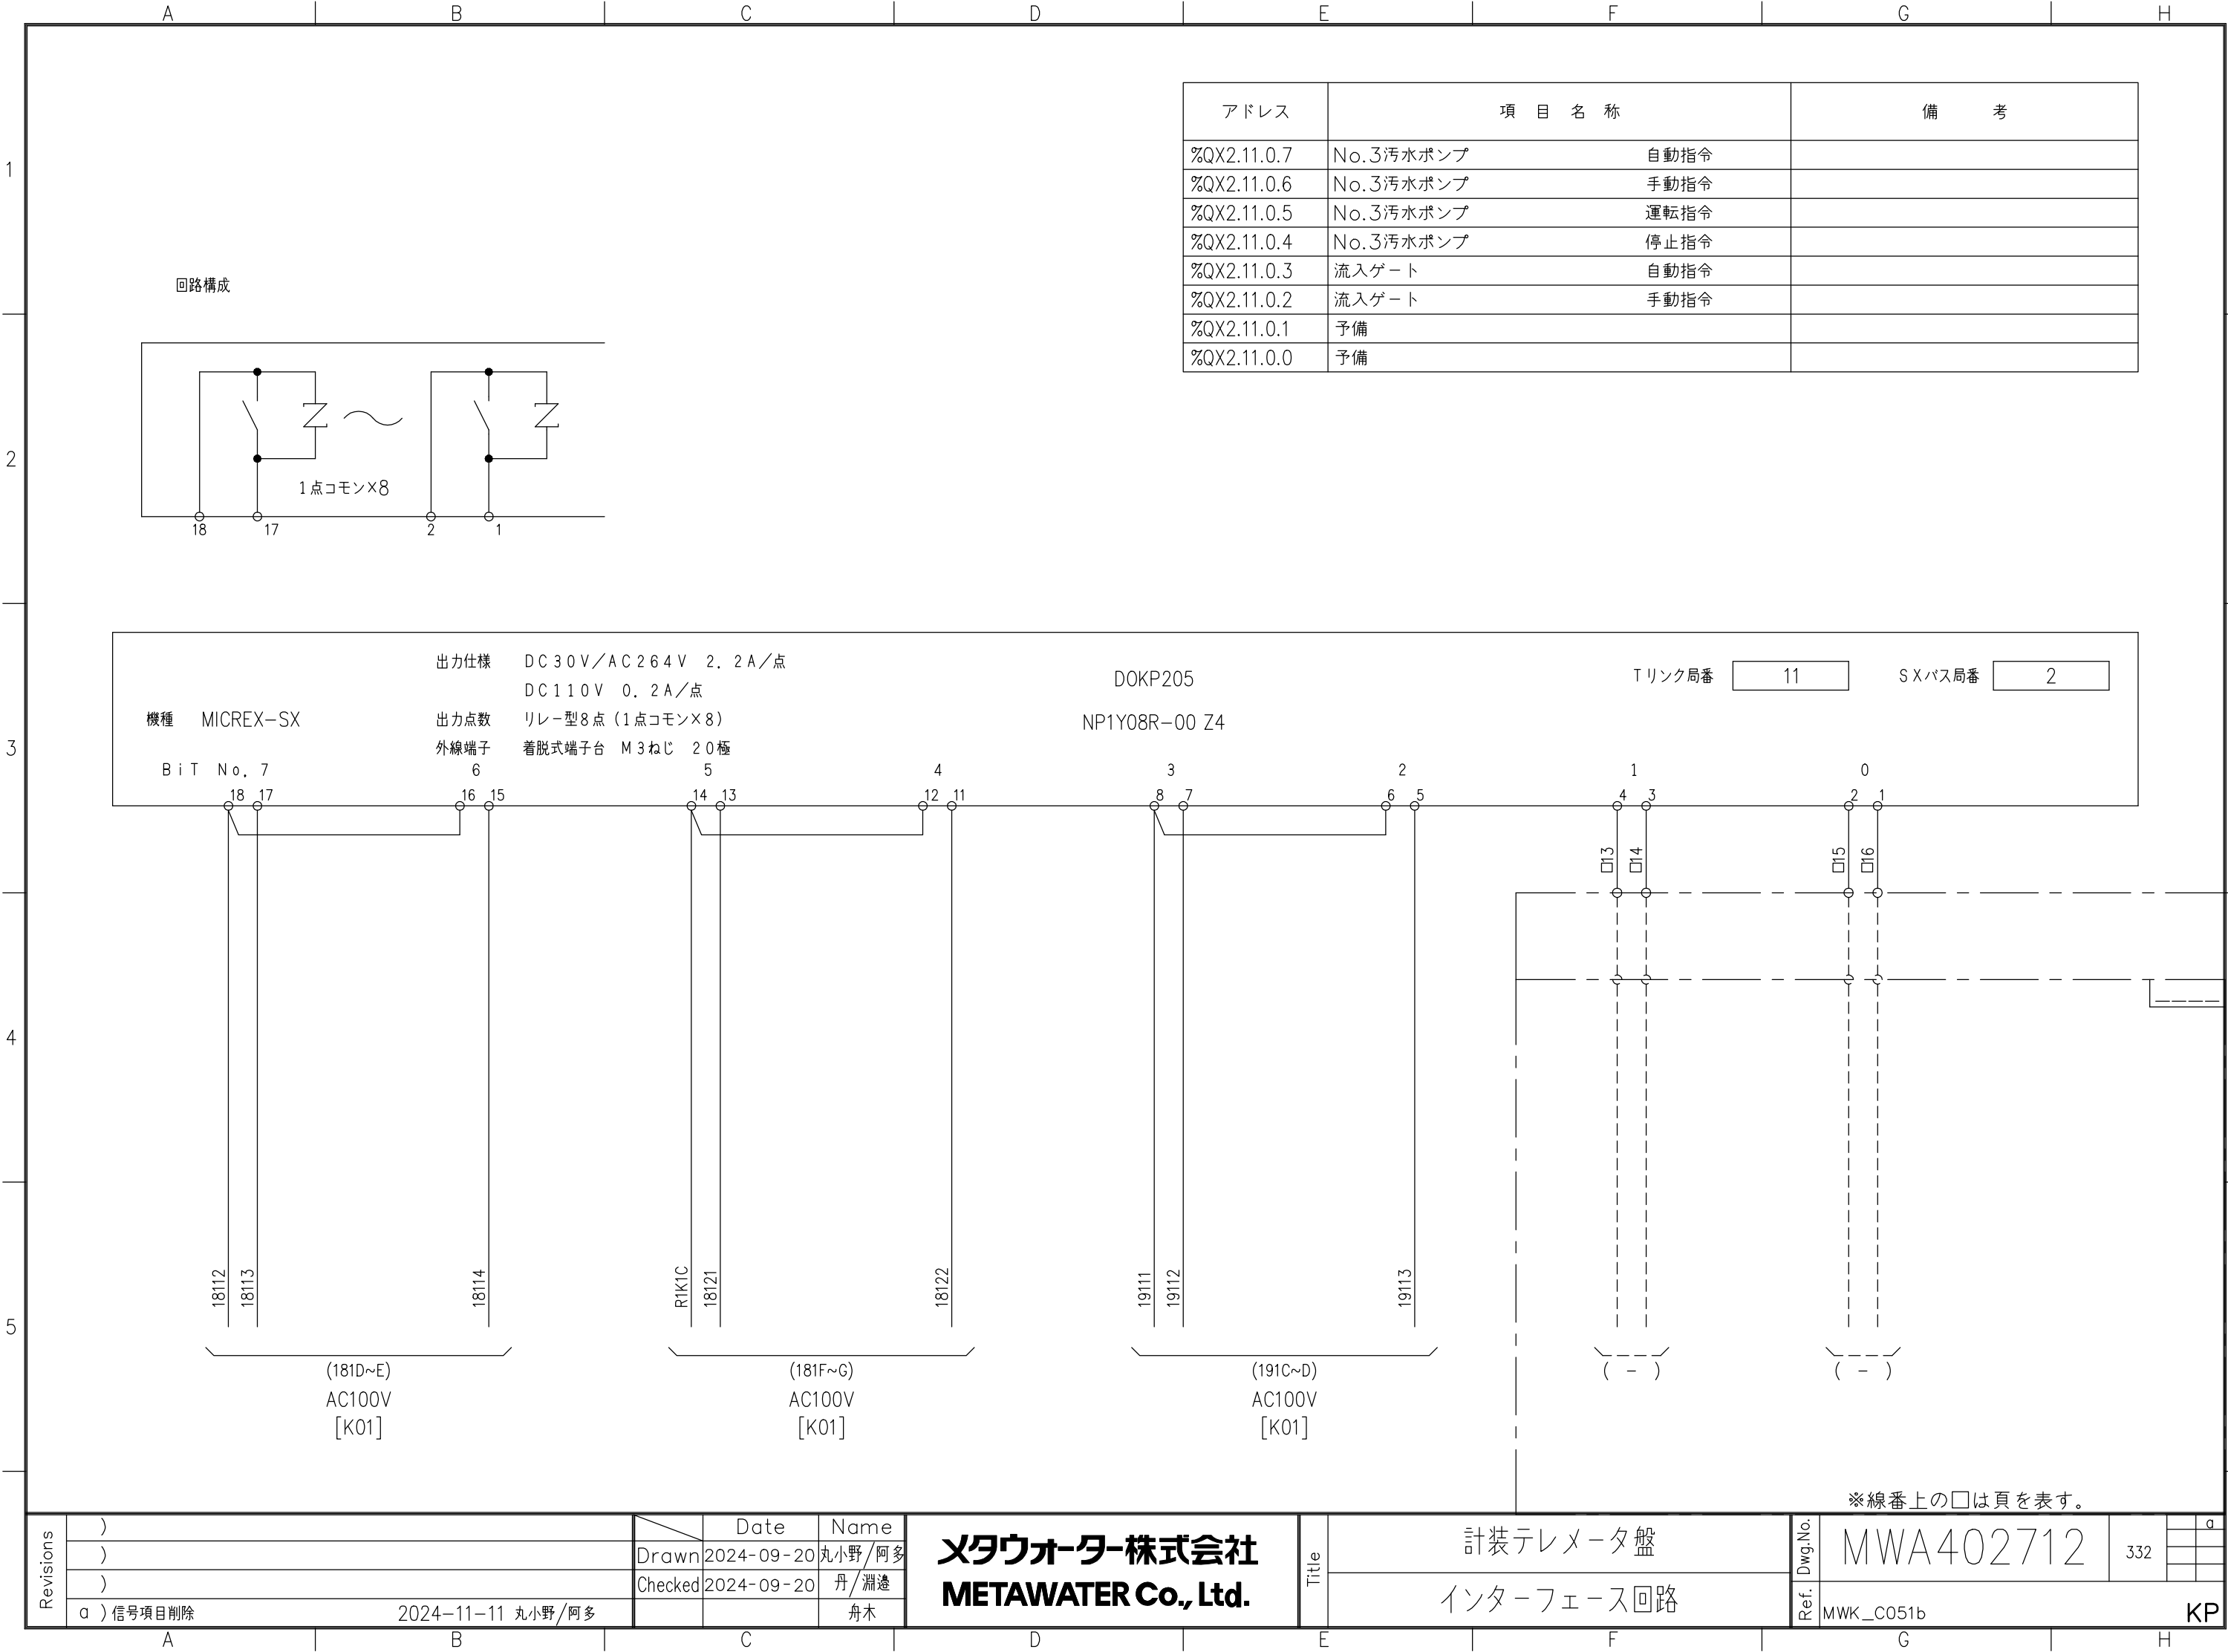

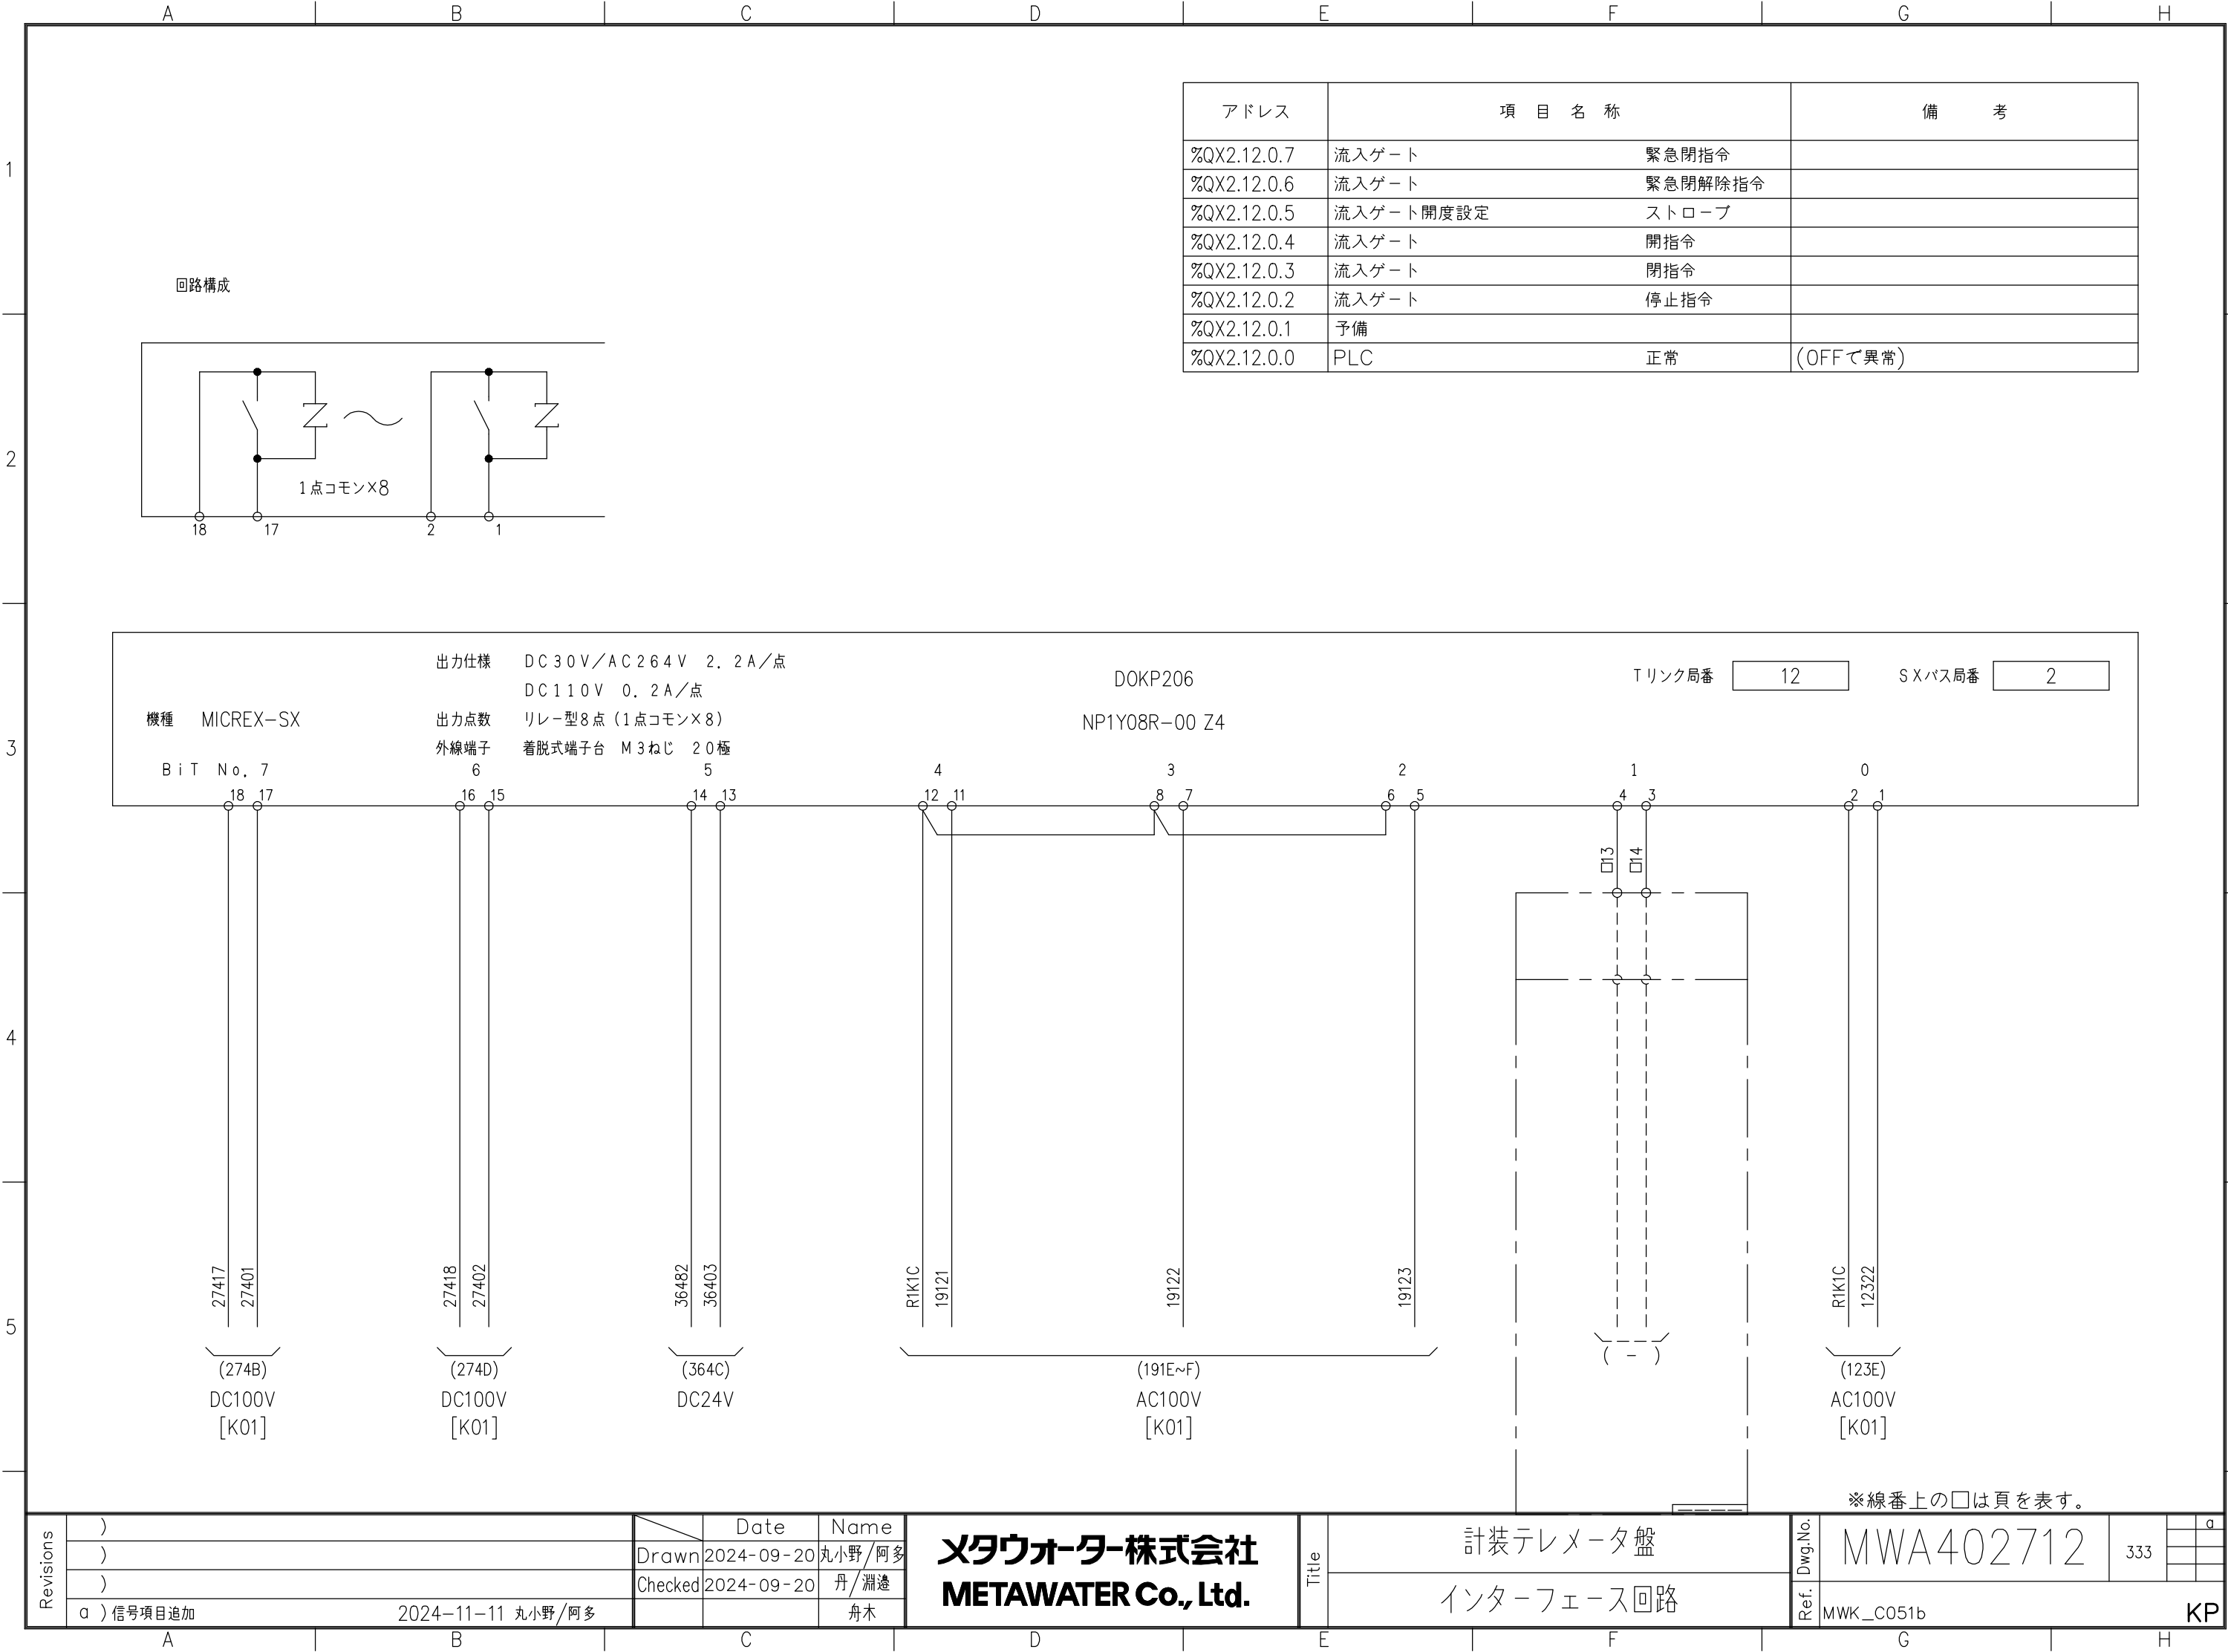

1

2

3

4

5

アドレス	CH. NO.	項目名称	備考	ソフト個別設定仕様	
				入力レンジ	デジタル値
%W2.14.0	01	No.1汚水ポンプ電流	0.0~60.0A		
%W2.14.1	02	No.2汚水ポンプ電流	0.0~60.0A		
%W2.14.2	03	No.3汚水ポンプ電流	0.0~60.0A		
%W2.14.3	04	予備			
%W2.14.4	05	予備			
%W2.14.5	06	予備			
%W2.14.6	07	予備			
%W2.14.7	08	予備			
%QW2.14.8			未使用		
%QW2.14.9			未使用		
%QW2.14.10			未使用		
%QW2.14.11			未使用		

Range設定

スイッチ番号	入力レンジ	変換値範囲
0 工場出荷時	-10~10V	-32000~32000
1	0~10V	0~32000
2	0~5V	
3	1~5V	
4	-10~10V	0~10000
5	0~10V	
6	0~5V	
7	1~5V	
8	ソフト設定レンジ動作モード	
9	未使用（スイッチ番号0の動作）	

Average設定

スイッチ番号	移動平均処理回数
0 工場出荷時	1回（移動平均処理なし）
1	8回
2	16回
3	32回
4~9	未使用（移動平均処理なし）

機種MICREX-SX

入力点数8点

外線端子着脱式端子台 M3ねじ 20極

AIKP208

NP1AXH8VG-MR Z4

※レンジ設定“8”の時は「ソフト個別設定仕様」欄記入

アベレージスイッチ0

レンジスイッチ7

Tリンク局番14

SXバス局番2

機種MICREX-SX

入力点数8点

外線端子着脱式端子台 M3ねじ 20極

AIKP208

NP1AXH8VG-MR Z4

※レンジ設定“8”の時は「ソフト個別設定仕様」欄記入

アベレージスイッチ0

レンジスイッチ7

Tリンク局番14

SXバス局番2

Revisions

)

)

)

)

Date

2024-09-20

2024-09-20

Name

丸小野/阿多

丹/淵邊

舟木

メタウォーター株式会社

METAWATER Co., Ltd.

Title

計装テレメータ盤

インターフェース回路

Dwg.No.

MWA402712

335

Ref.

KW03_27_01d

KP

※線番上の□は頁を表す。

1

アドレス	CH. NO.	項目名称	備考	ソフト個別設定仕様	
				出力レンジ	デジタル値
%W2.15.0			モジュールステータス		
%W2.15.1			動作スイッチNo.		
%W2.15.2			未使用		
%W2.15.3			未使用		
%QW2.15.4	01	流入ゲート開度設定	0~100%		
%QW2.15.5	02	予備			
%QW2.15.6	03	予備			
%QW2.15.7	04	予備			

Range設定

スイッチ番号	出力レンジ	変換値範囲
0	0~10V	0~16000
1	0~5V	
2	1~5V	
3	-10~10V	-16000~16000
4	0~10V	0~10000
5	0~5V	
6	1~5V	
7	未使用（スイッチ番号0の動作）	
8	ソフト設定レンジ動作モード	
9	未使用（スイッチ番号0の動作）	

3

※レンジ設定“8”の時は「ソフト個別設定仕様」欄記入

機種MICREX-SX

出力点数4点

外線端子着脱式端子台 M3ねじ 20極

AOKP209

NP1AYH4VG-MR Z4

レンジスイッチ6

Tリンク局番15

SXバス局番2

CH.No.1

V+1

V-2

NC3

NC4

□01

□02

DC1~5V

(364F)

CH.No.2

V+5

V-6

NC7

NC8

□03

□04

DC1~5V

()

CH.No.3

V+9

V-10

NC11

NC12

□05

□06

DC1~5V

()

CH.No.4

V+13

V-14

NC15

NC16

SLD17

SLD18

SLD19

SLD20

□07

□08

DC1~5V

()

Revisions

)

)

)

)

Drawn

2024-09-20

丸小野/阿多

Checked

2024-09-20

丹/淵邊

舟木

メタウォーター株式会社

METAWATER Co., Ltd.

Title

計装テレメータ盤

インターフェース回路

Dwg.No.

MWA402712


Ref.


KW03_31_01d

336

KP


※線番上の□は頁を表す。(337~350欠頁)

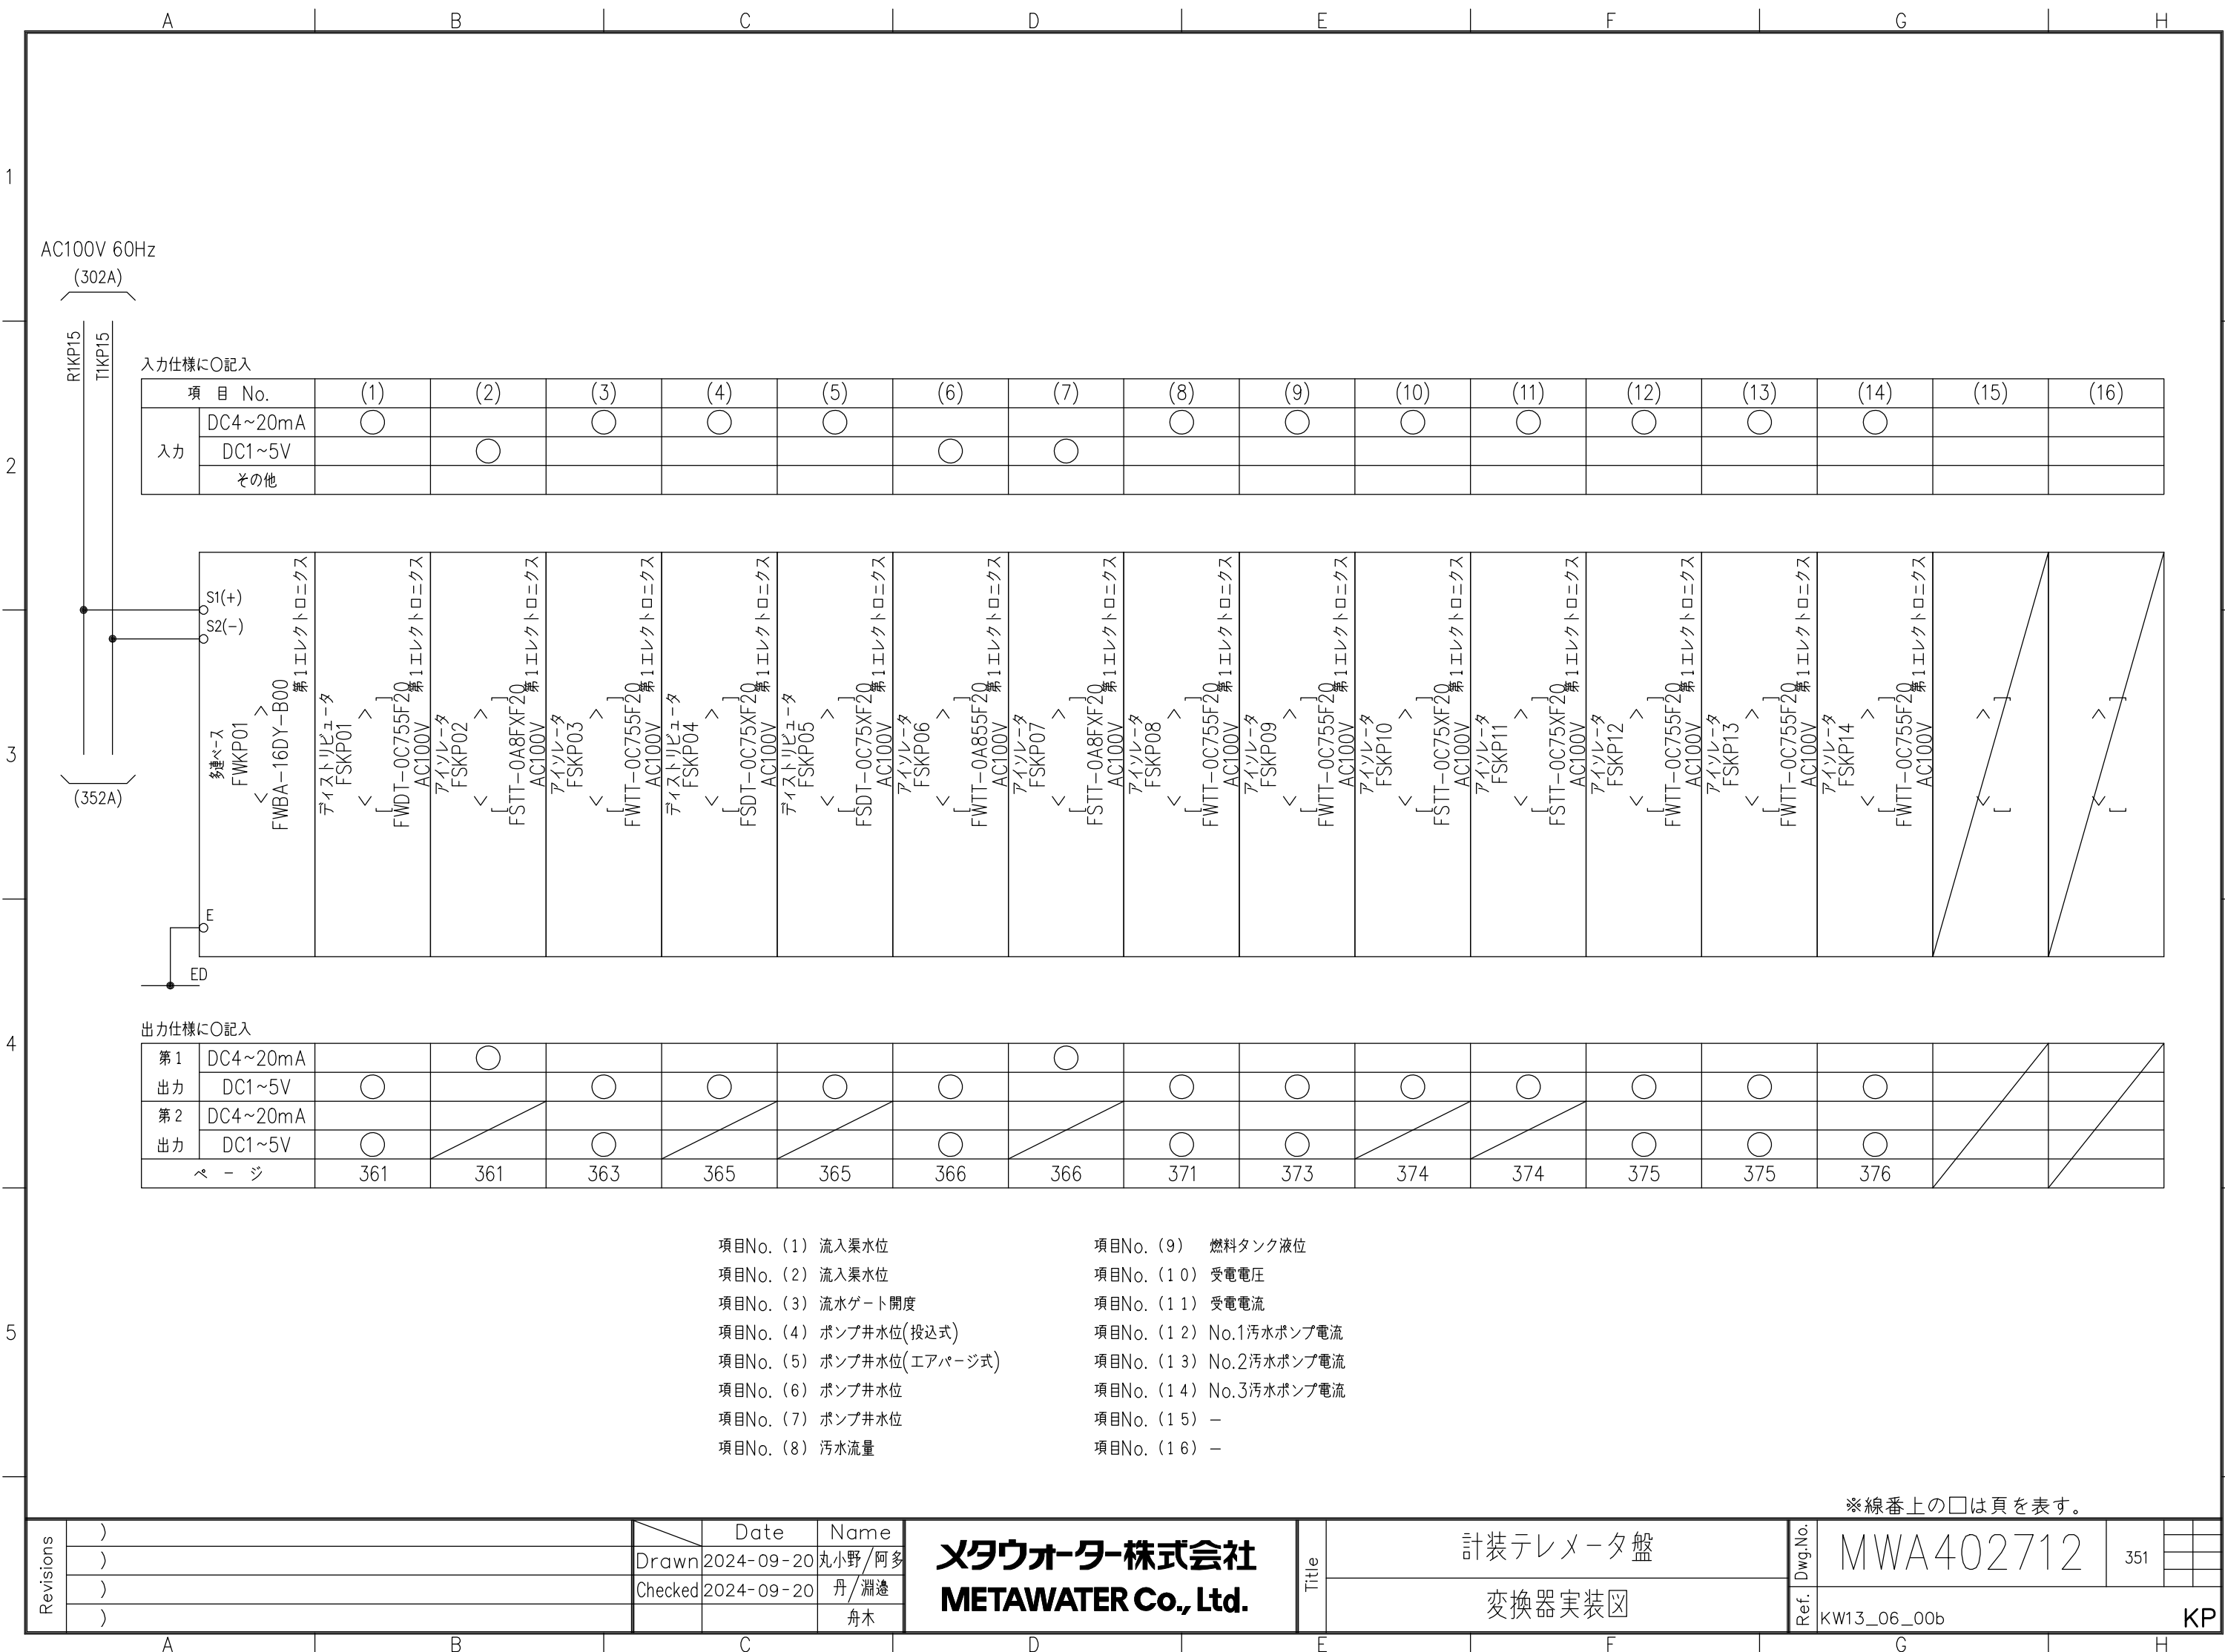

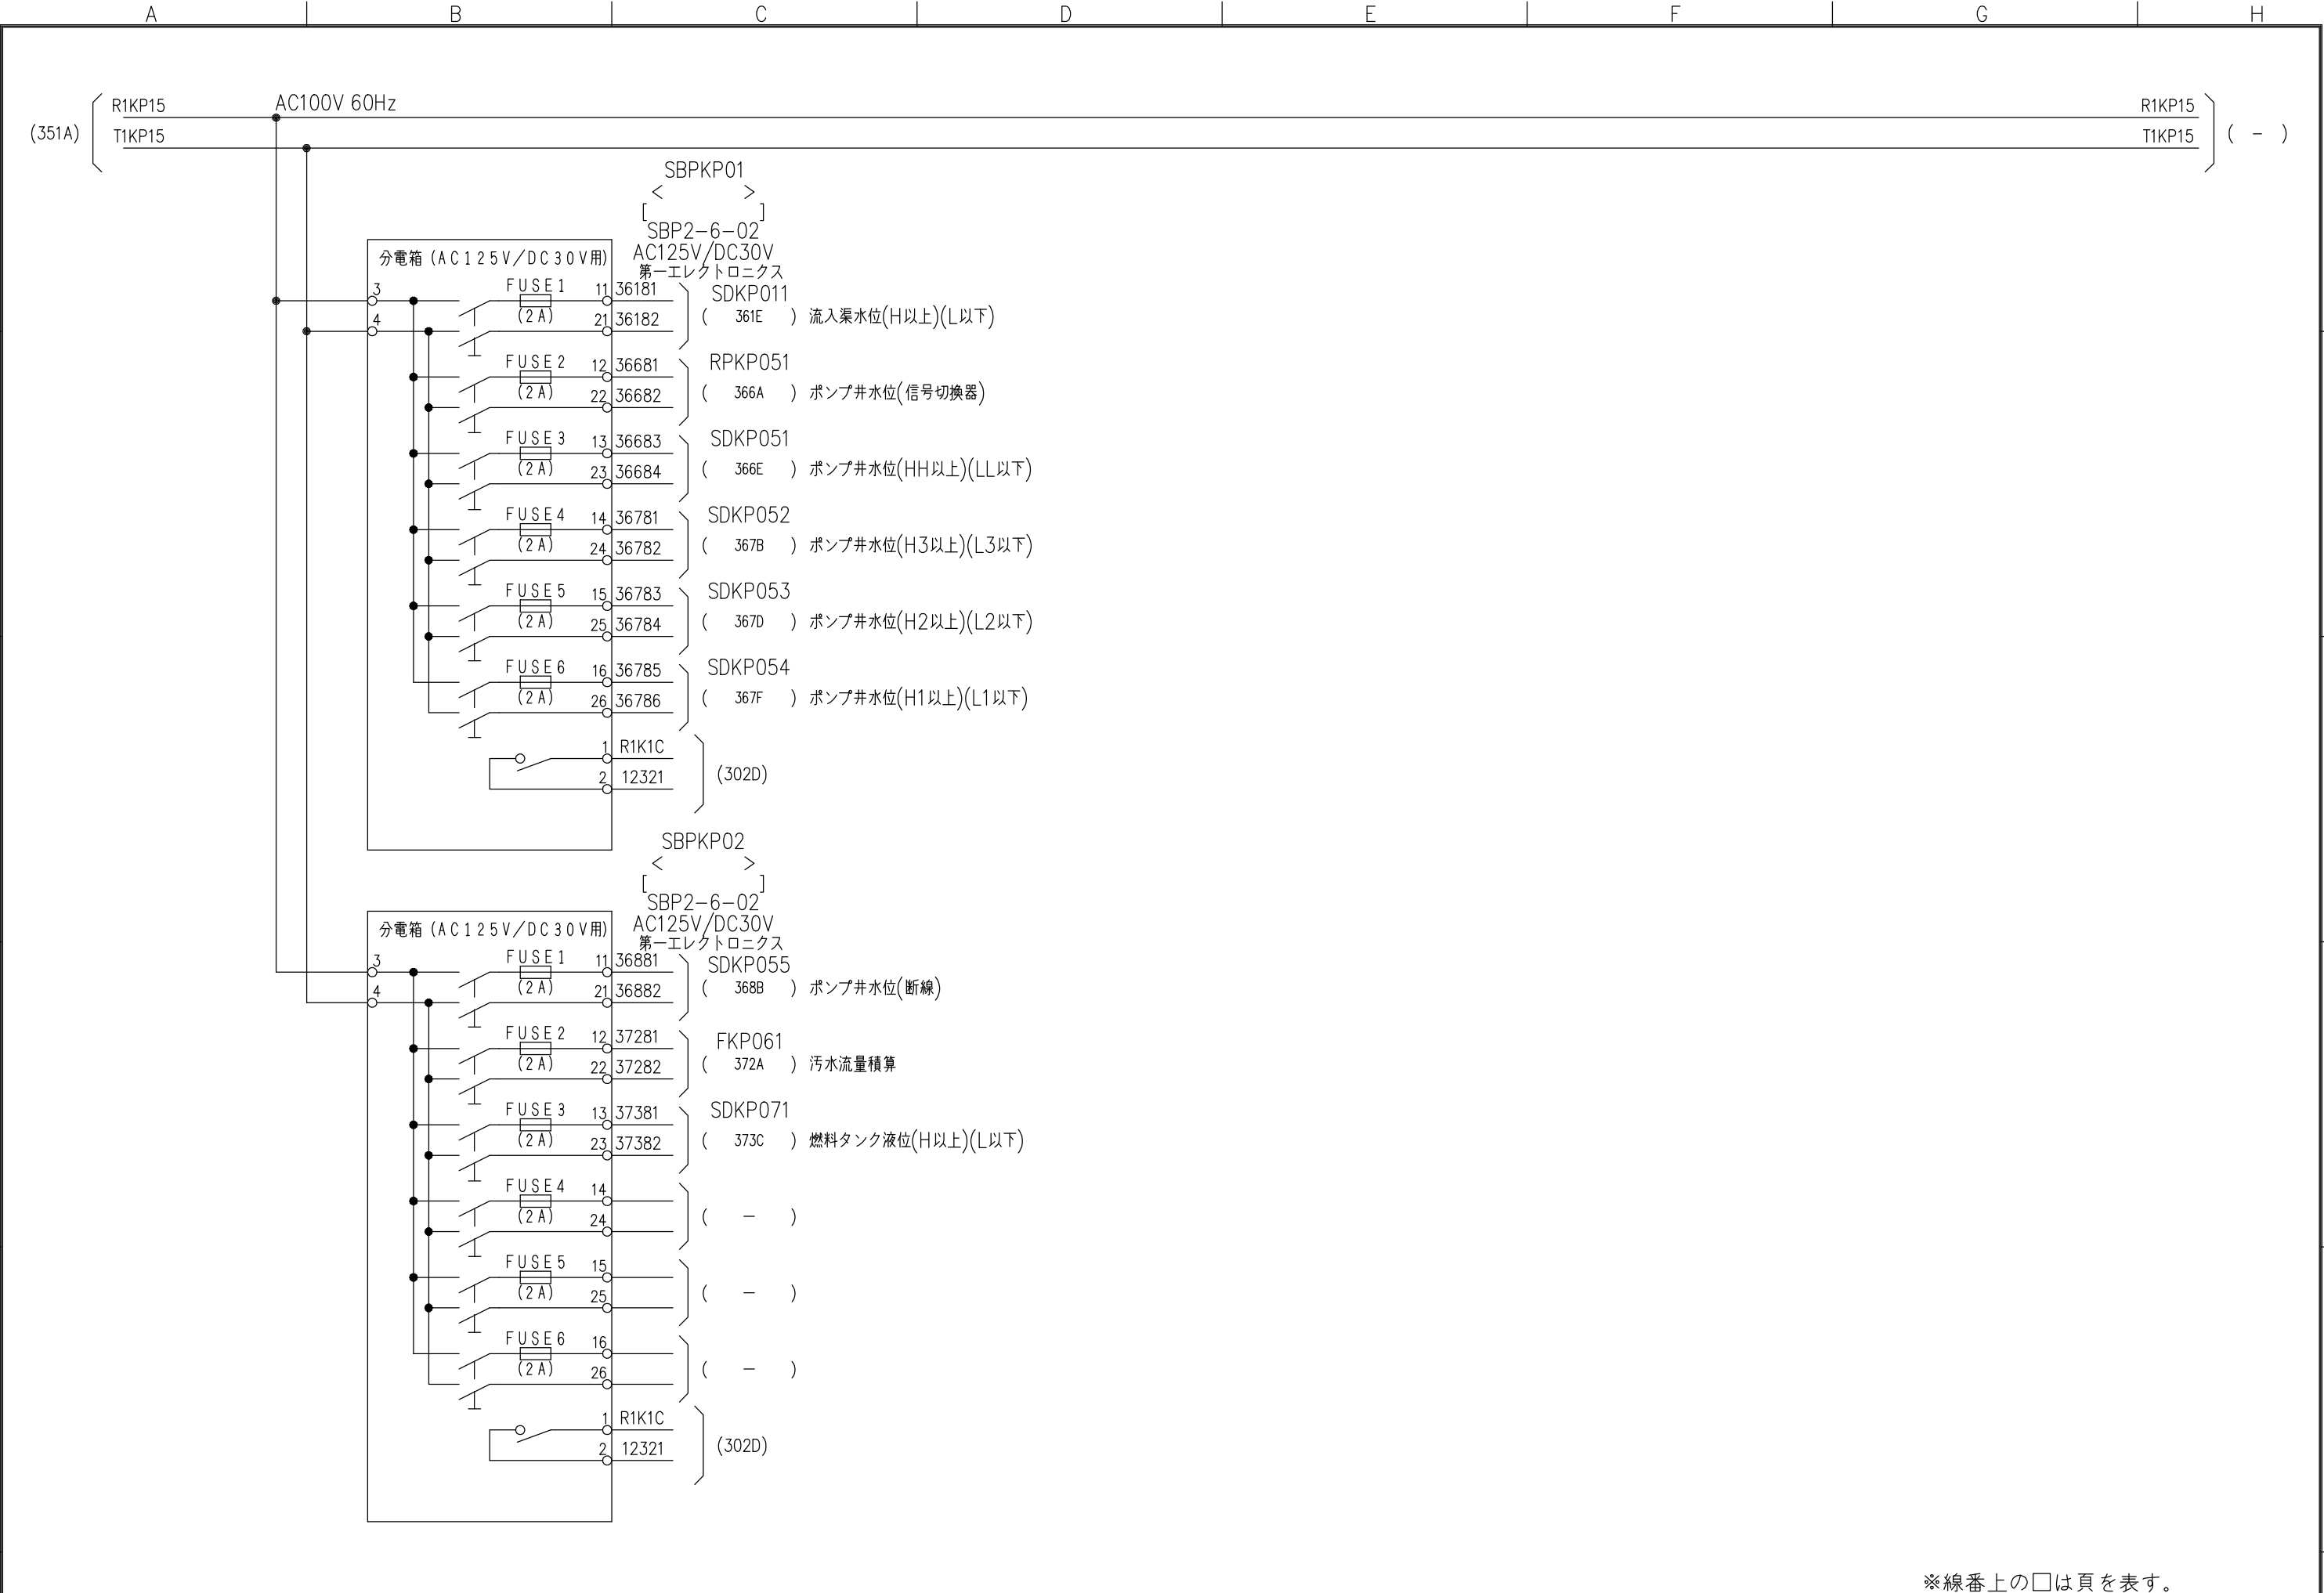


※線番上の□は頁を表す。

Revisions	)		Date	Name	メタウォーター株式会社 METAWATER Co., Ltd.	Title	計装テレメータ盤	Dwg.No.	MWA402712	352	b
	)	Drawn	2024-09-20	丸小野/阿多							
	)	Checked	2024-09-20	丹/淵邊			計装回路	Ref.	KW11_06_00	KP	
	b) 信号名称記載		2025-02-04	丸小野/阿多							

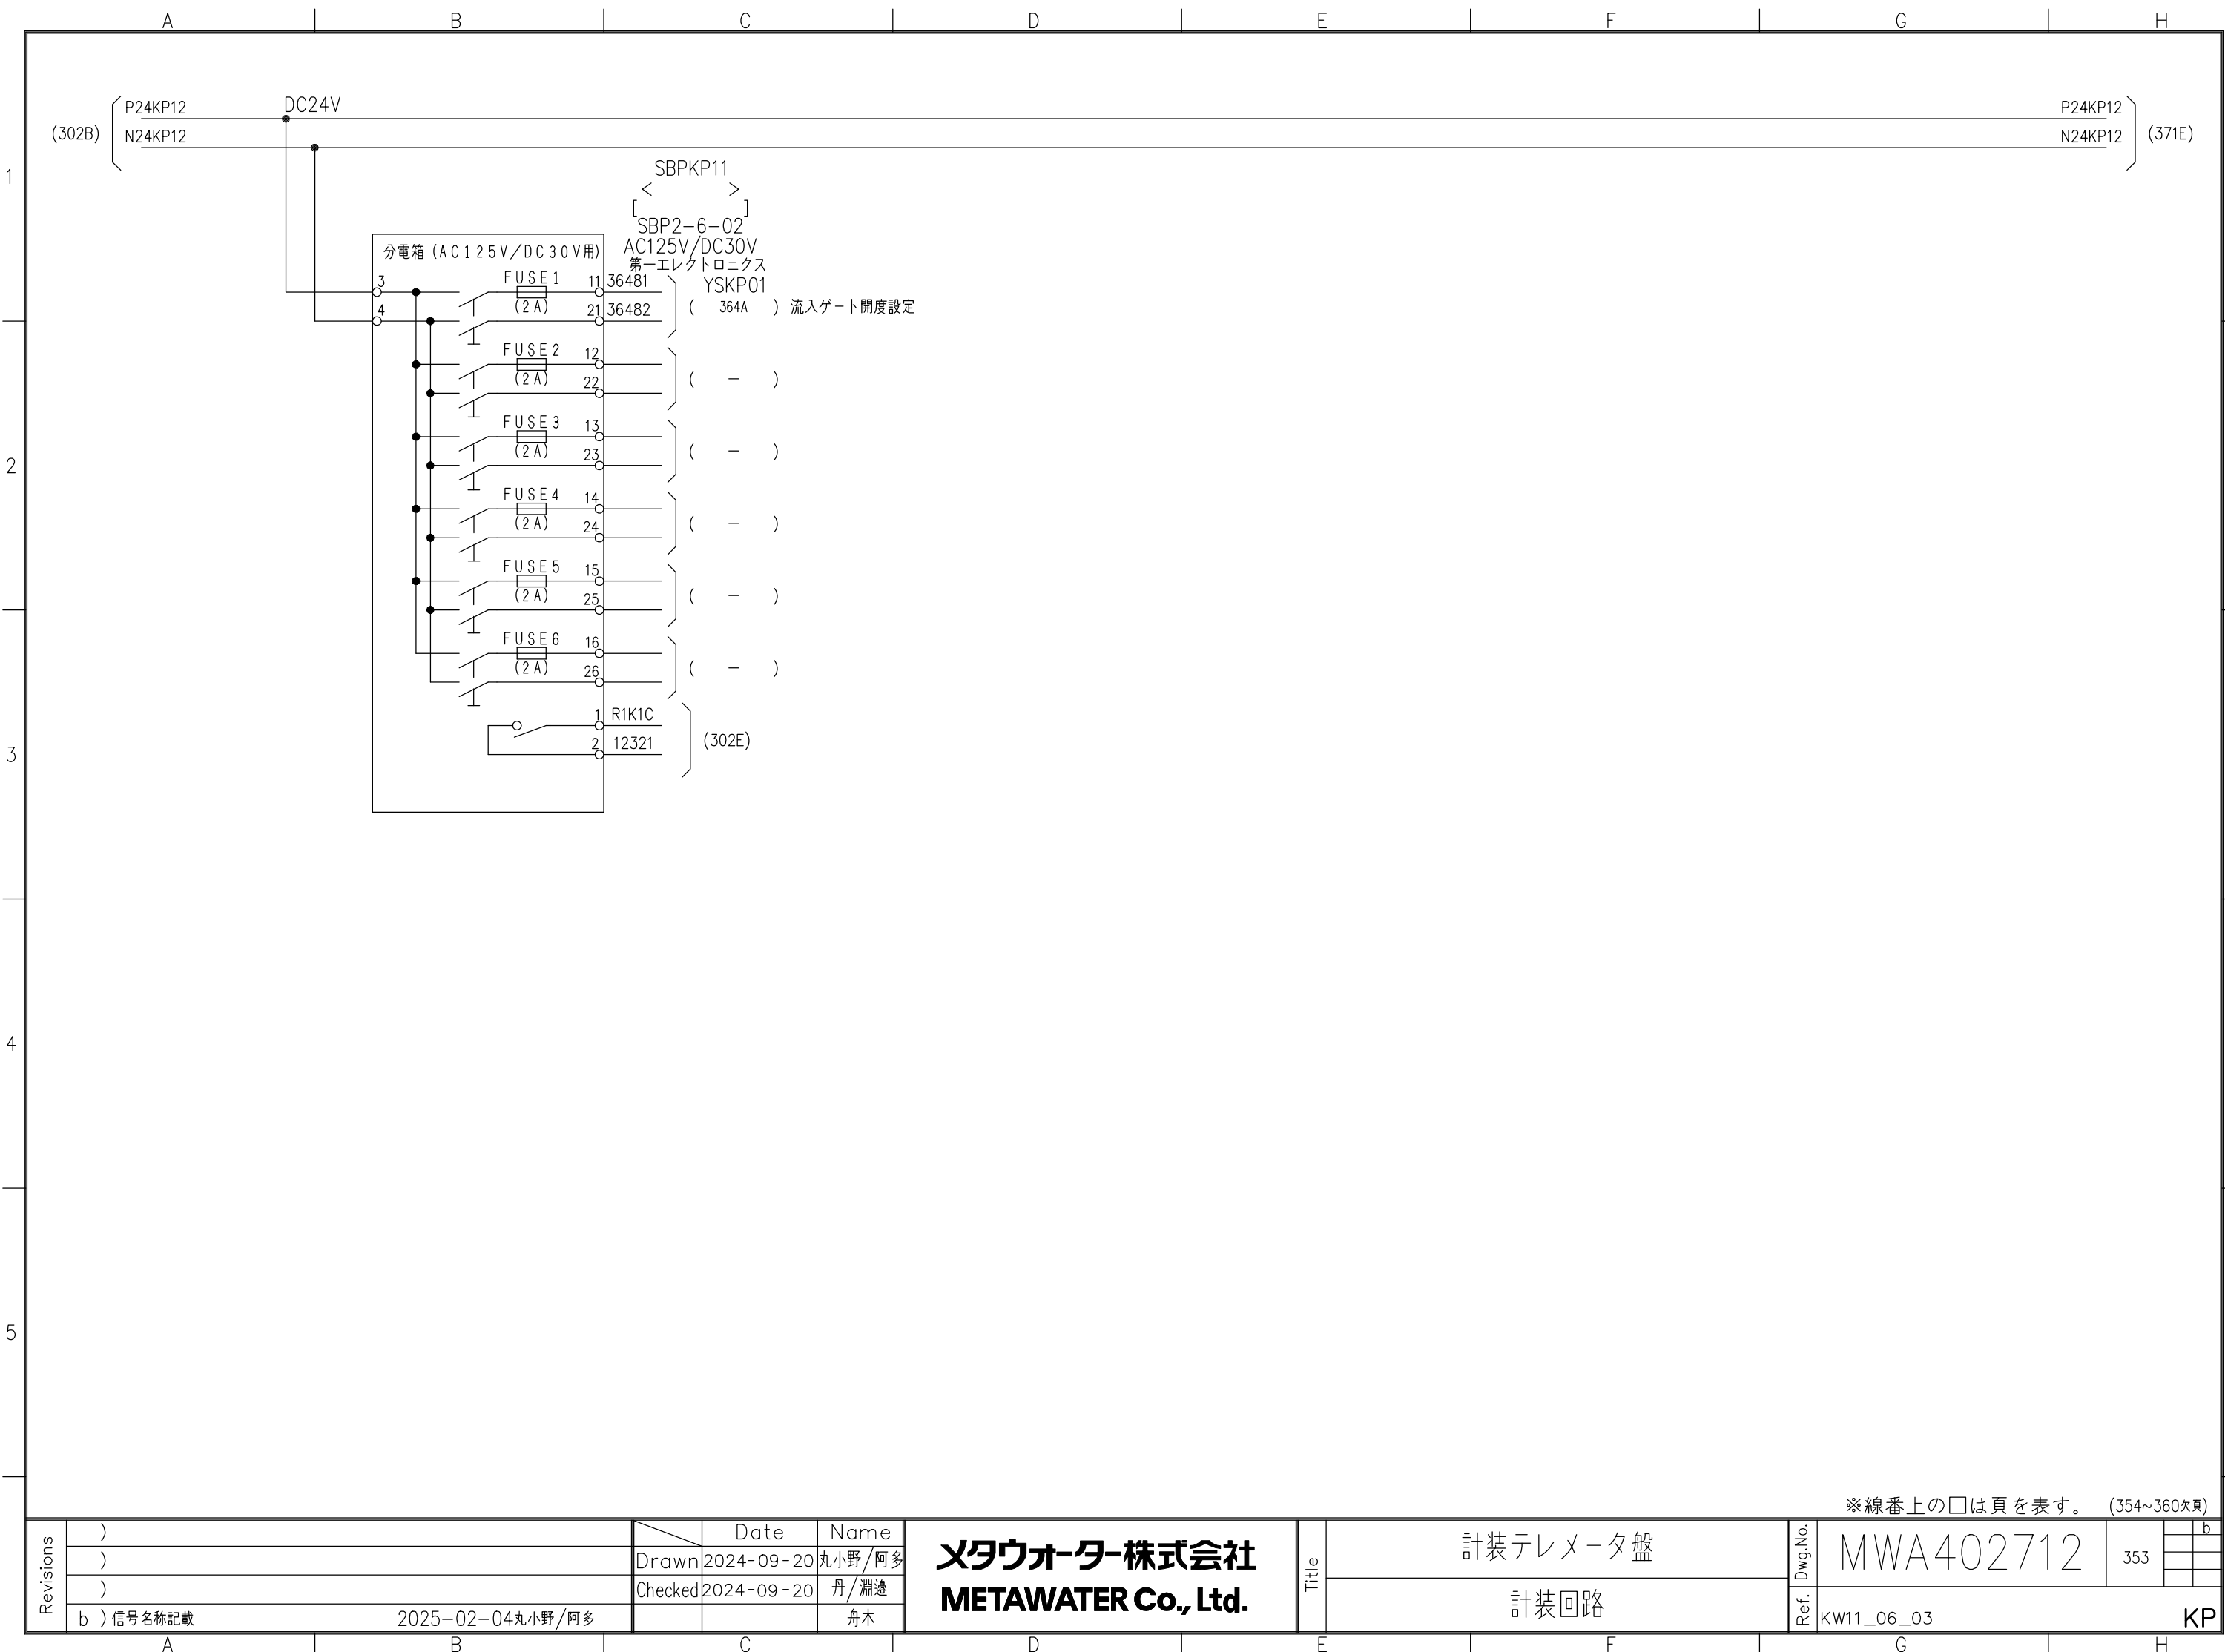

※線番上の□は頁を表す。(354~360欠頁)

Revisions	)		Date	Name	メタウォーター株式会社 METAWATER Co., Ltd.	Title	計装テレメータ盤	Dwg.No.	MWA402712	353		b
	)	Drawn	2024-09-20	丸小野/阿多								
	)	Checked	2024-09-20	丹/淵邊			計装回路	Ref.	KW11_06_03	KP		
	b) 信号名称記載			2025-02-04丸小野/阿多								

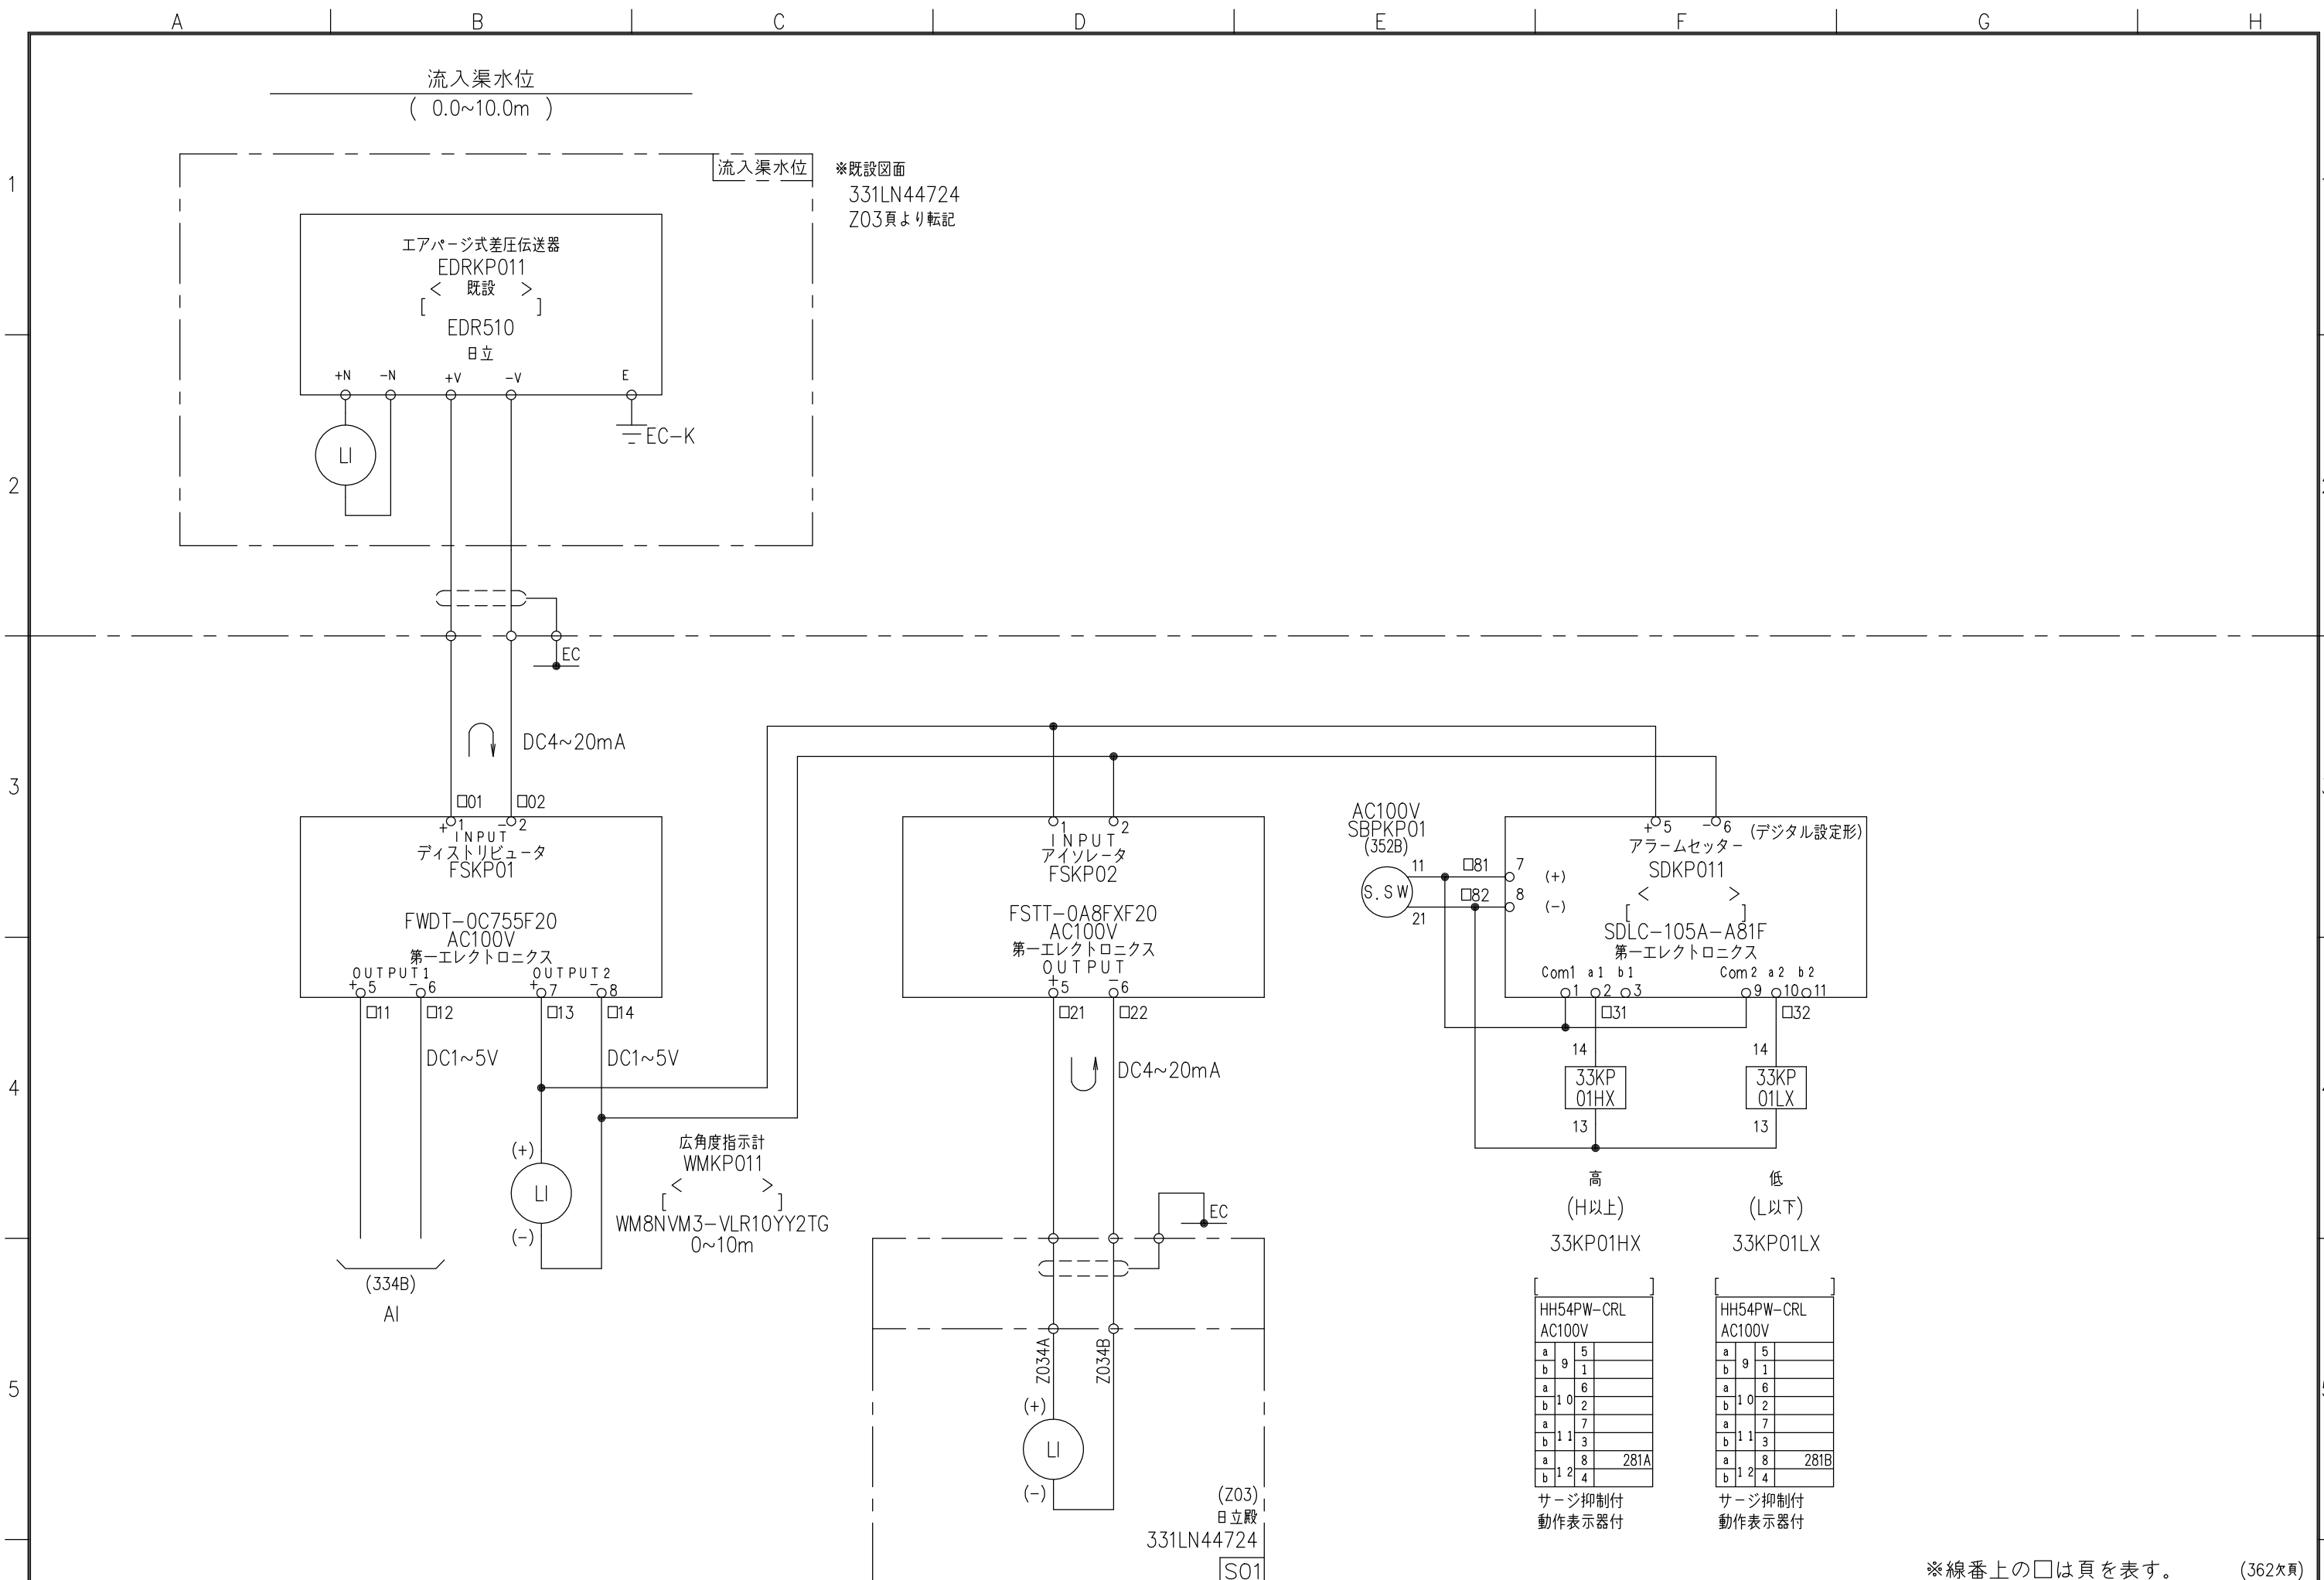



※既設図面
331LN44724
Z03頁より転記


(Z03)
日立殿
331LN44724
S01

※線番上の□は頁を表す。(362欠頁)


Revisions	)		Date	Name	メタウォーター株式会社 METAWATER Co., Ltd.	Title	計装テレメータ盤	Dwg.No.	MWA402712	361		a
	)	Drawn	2024-09-20	丸小野/阿多								
	)	Checked	2024-09-20	丹/淵邊								
	a) 図面修正フォロー			舟木								
	2024-11-11 丸小野/阿多											
							計装回路	Ref.	KW13_11_00			KP

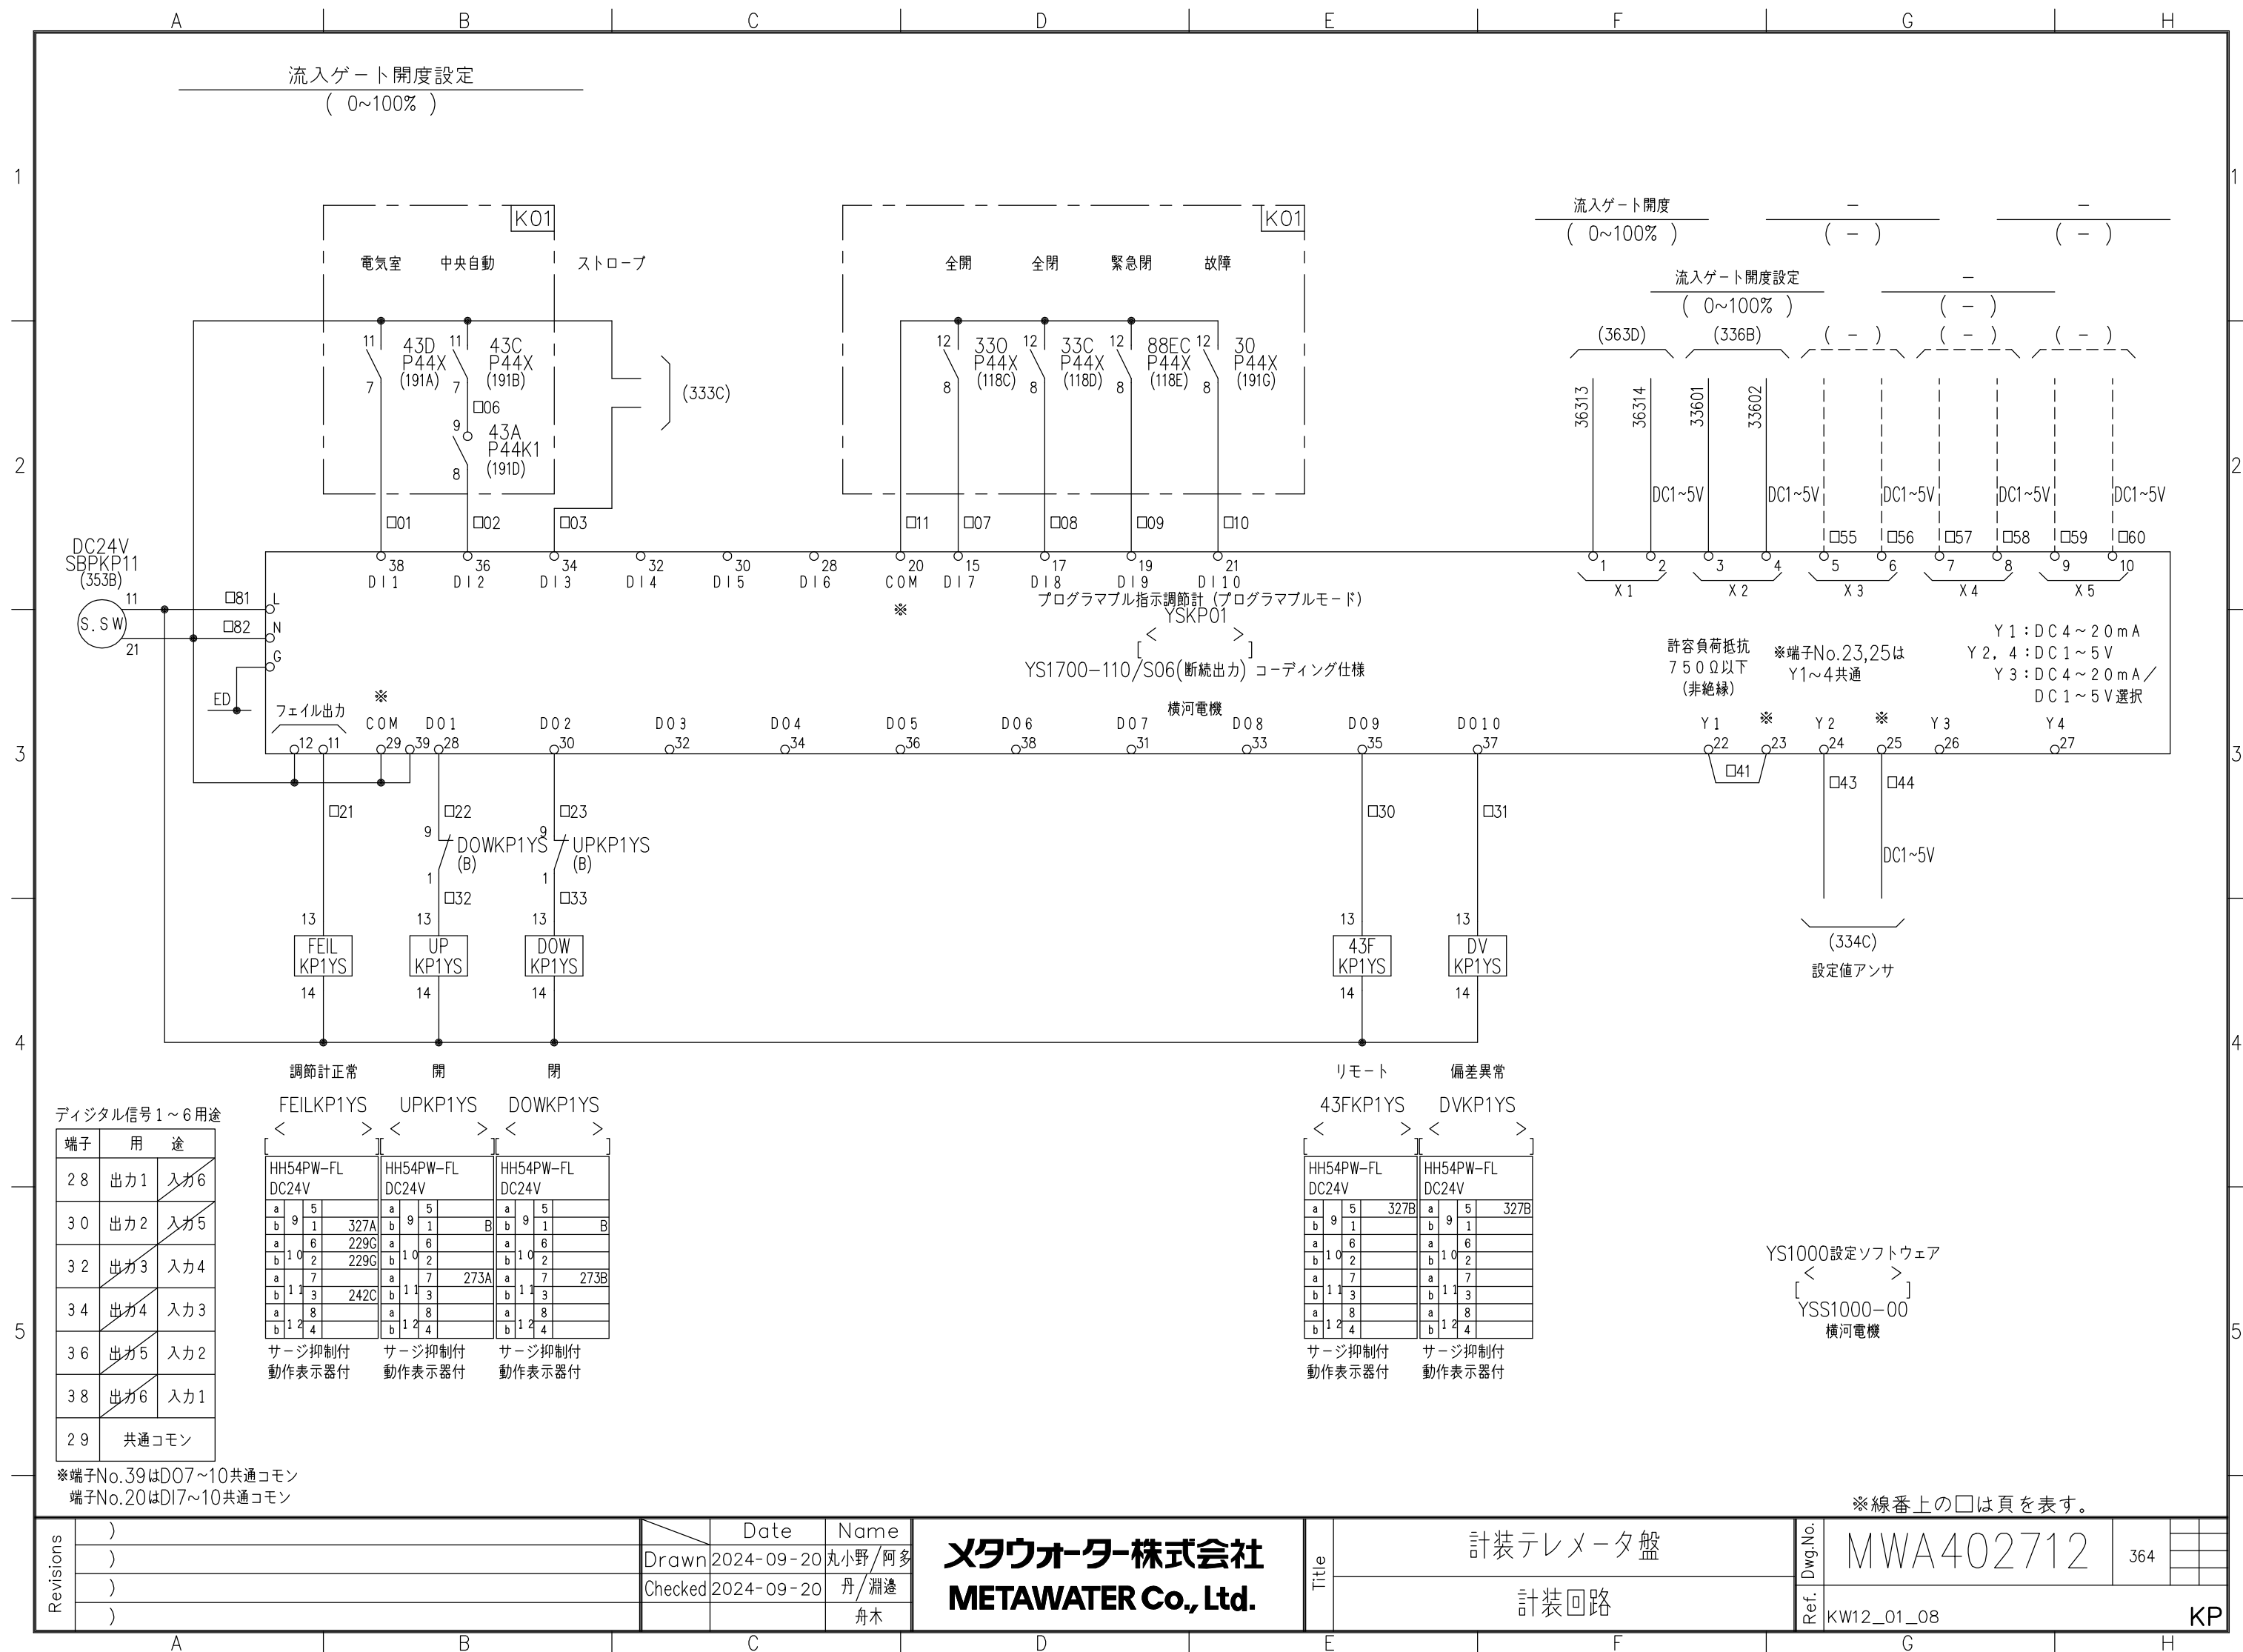


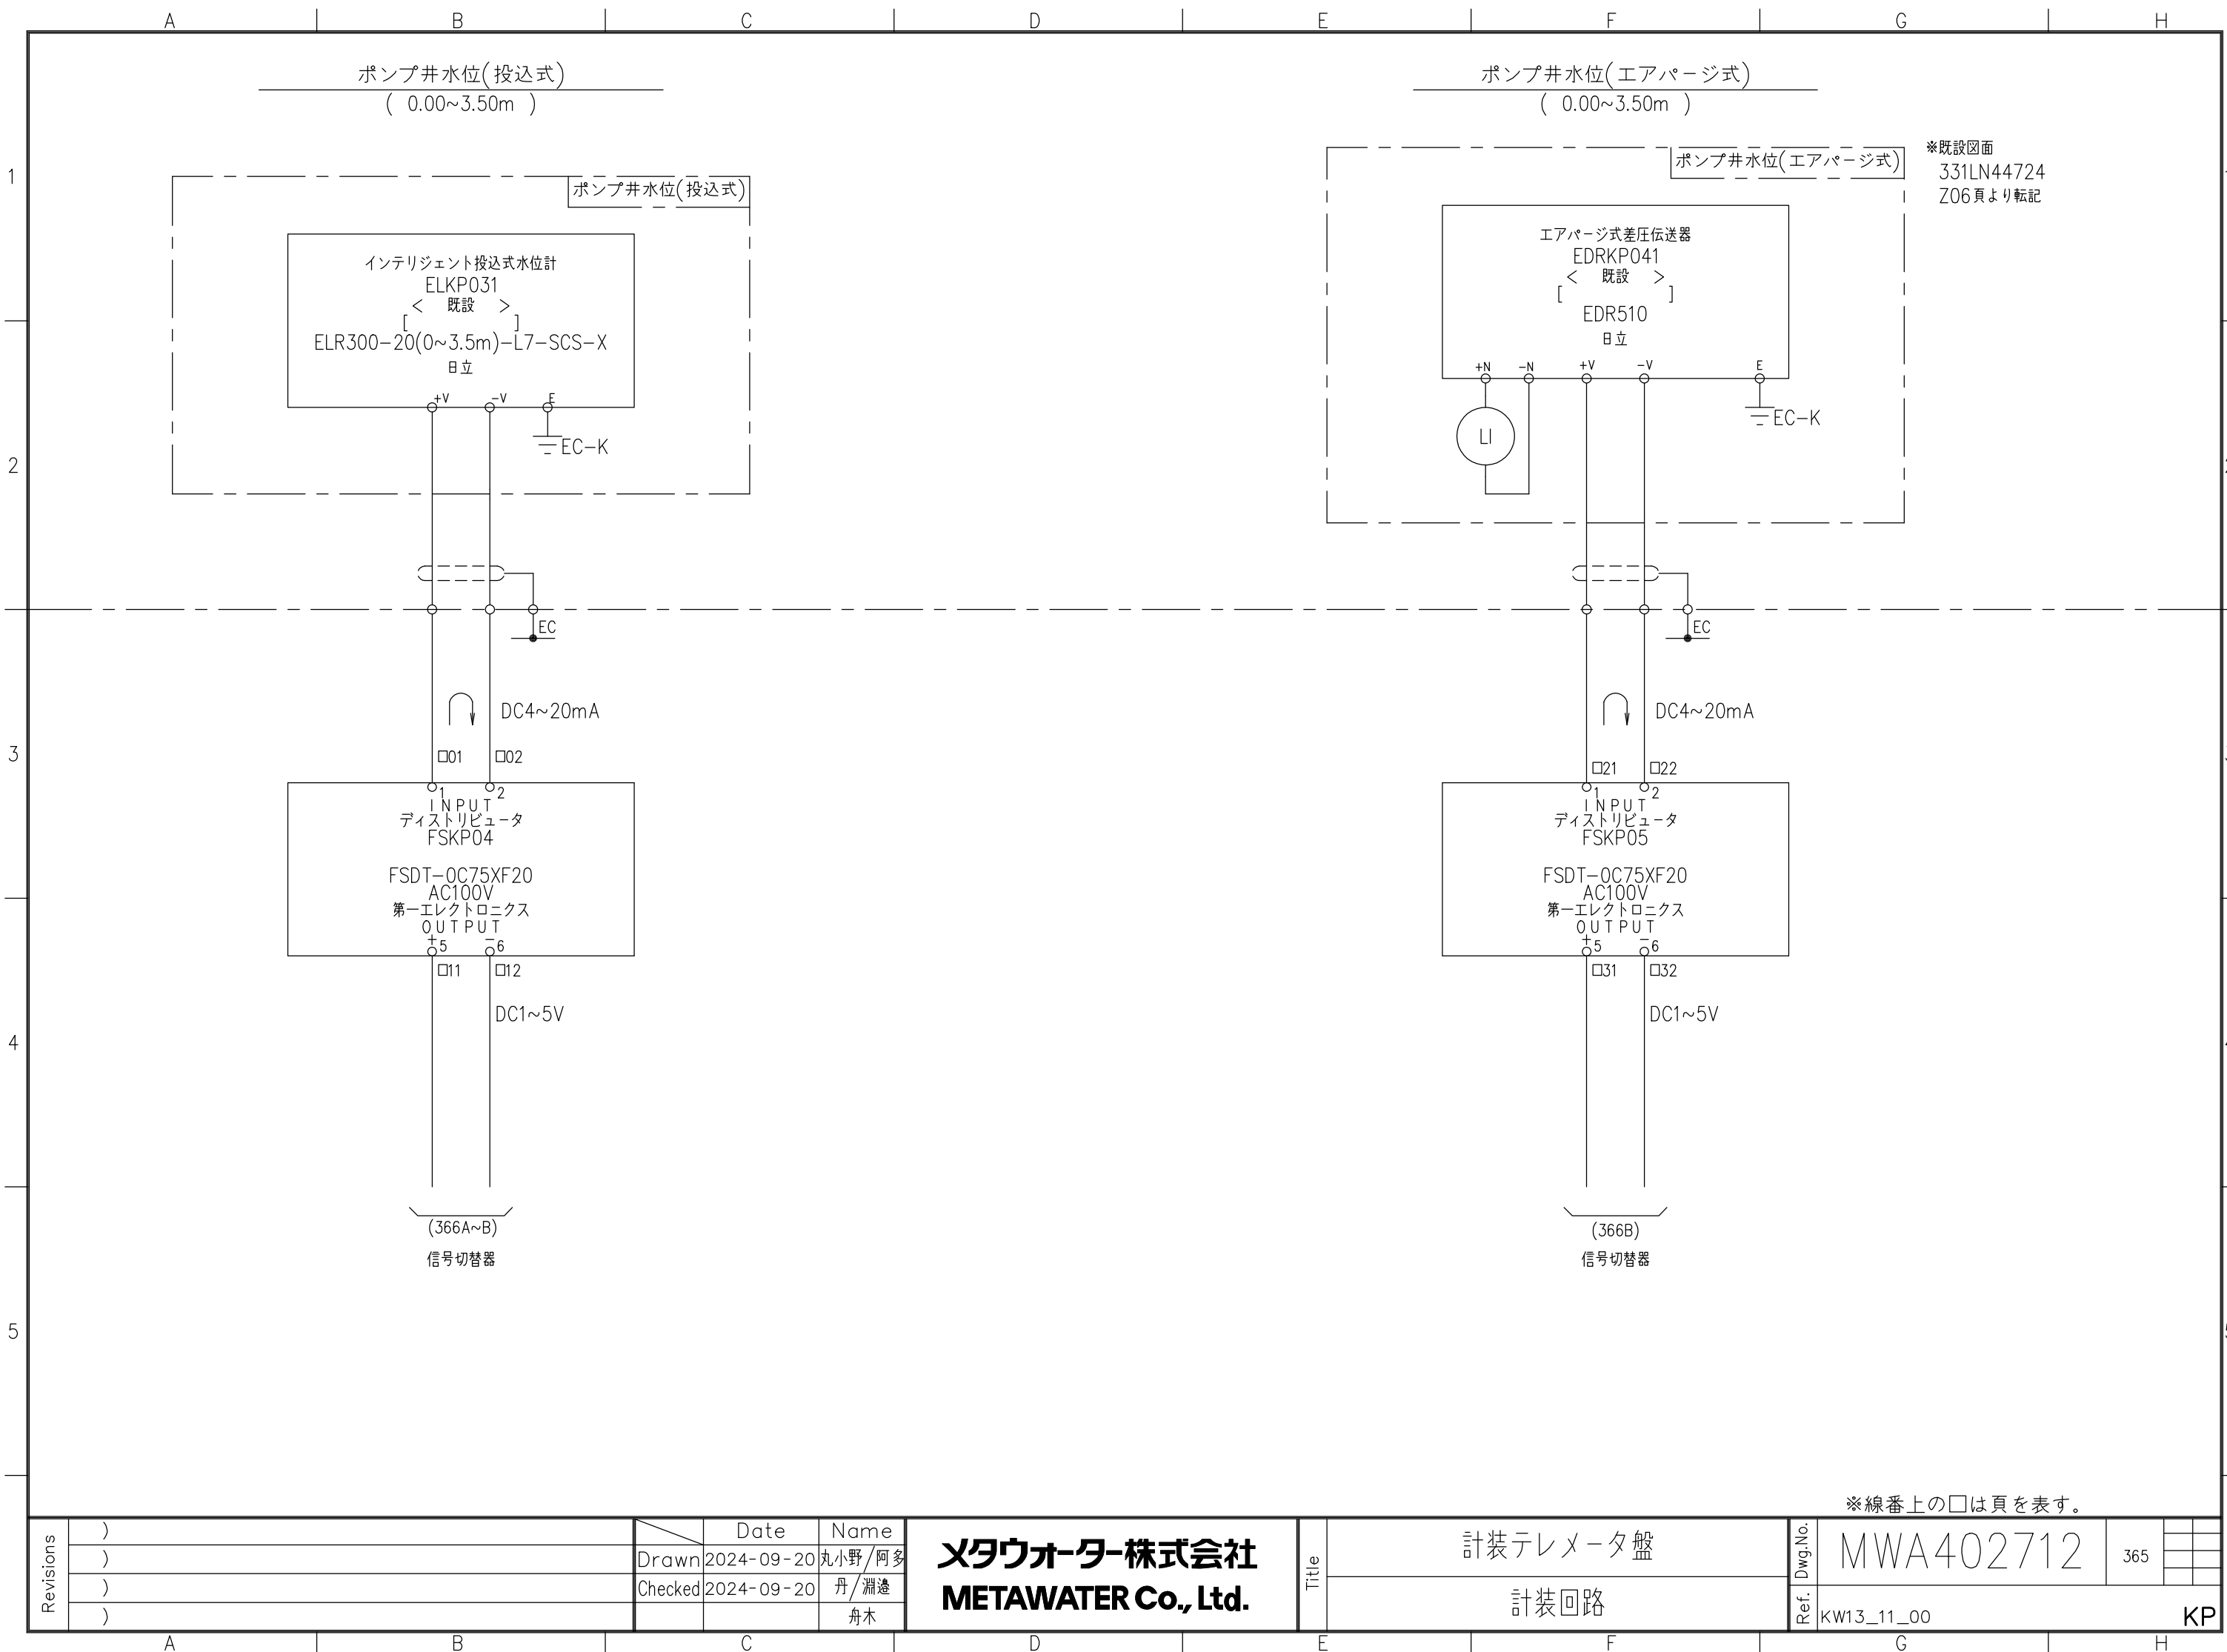


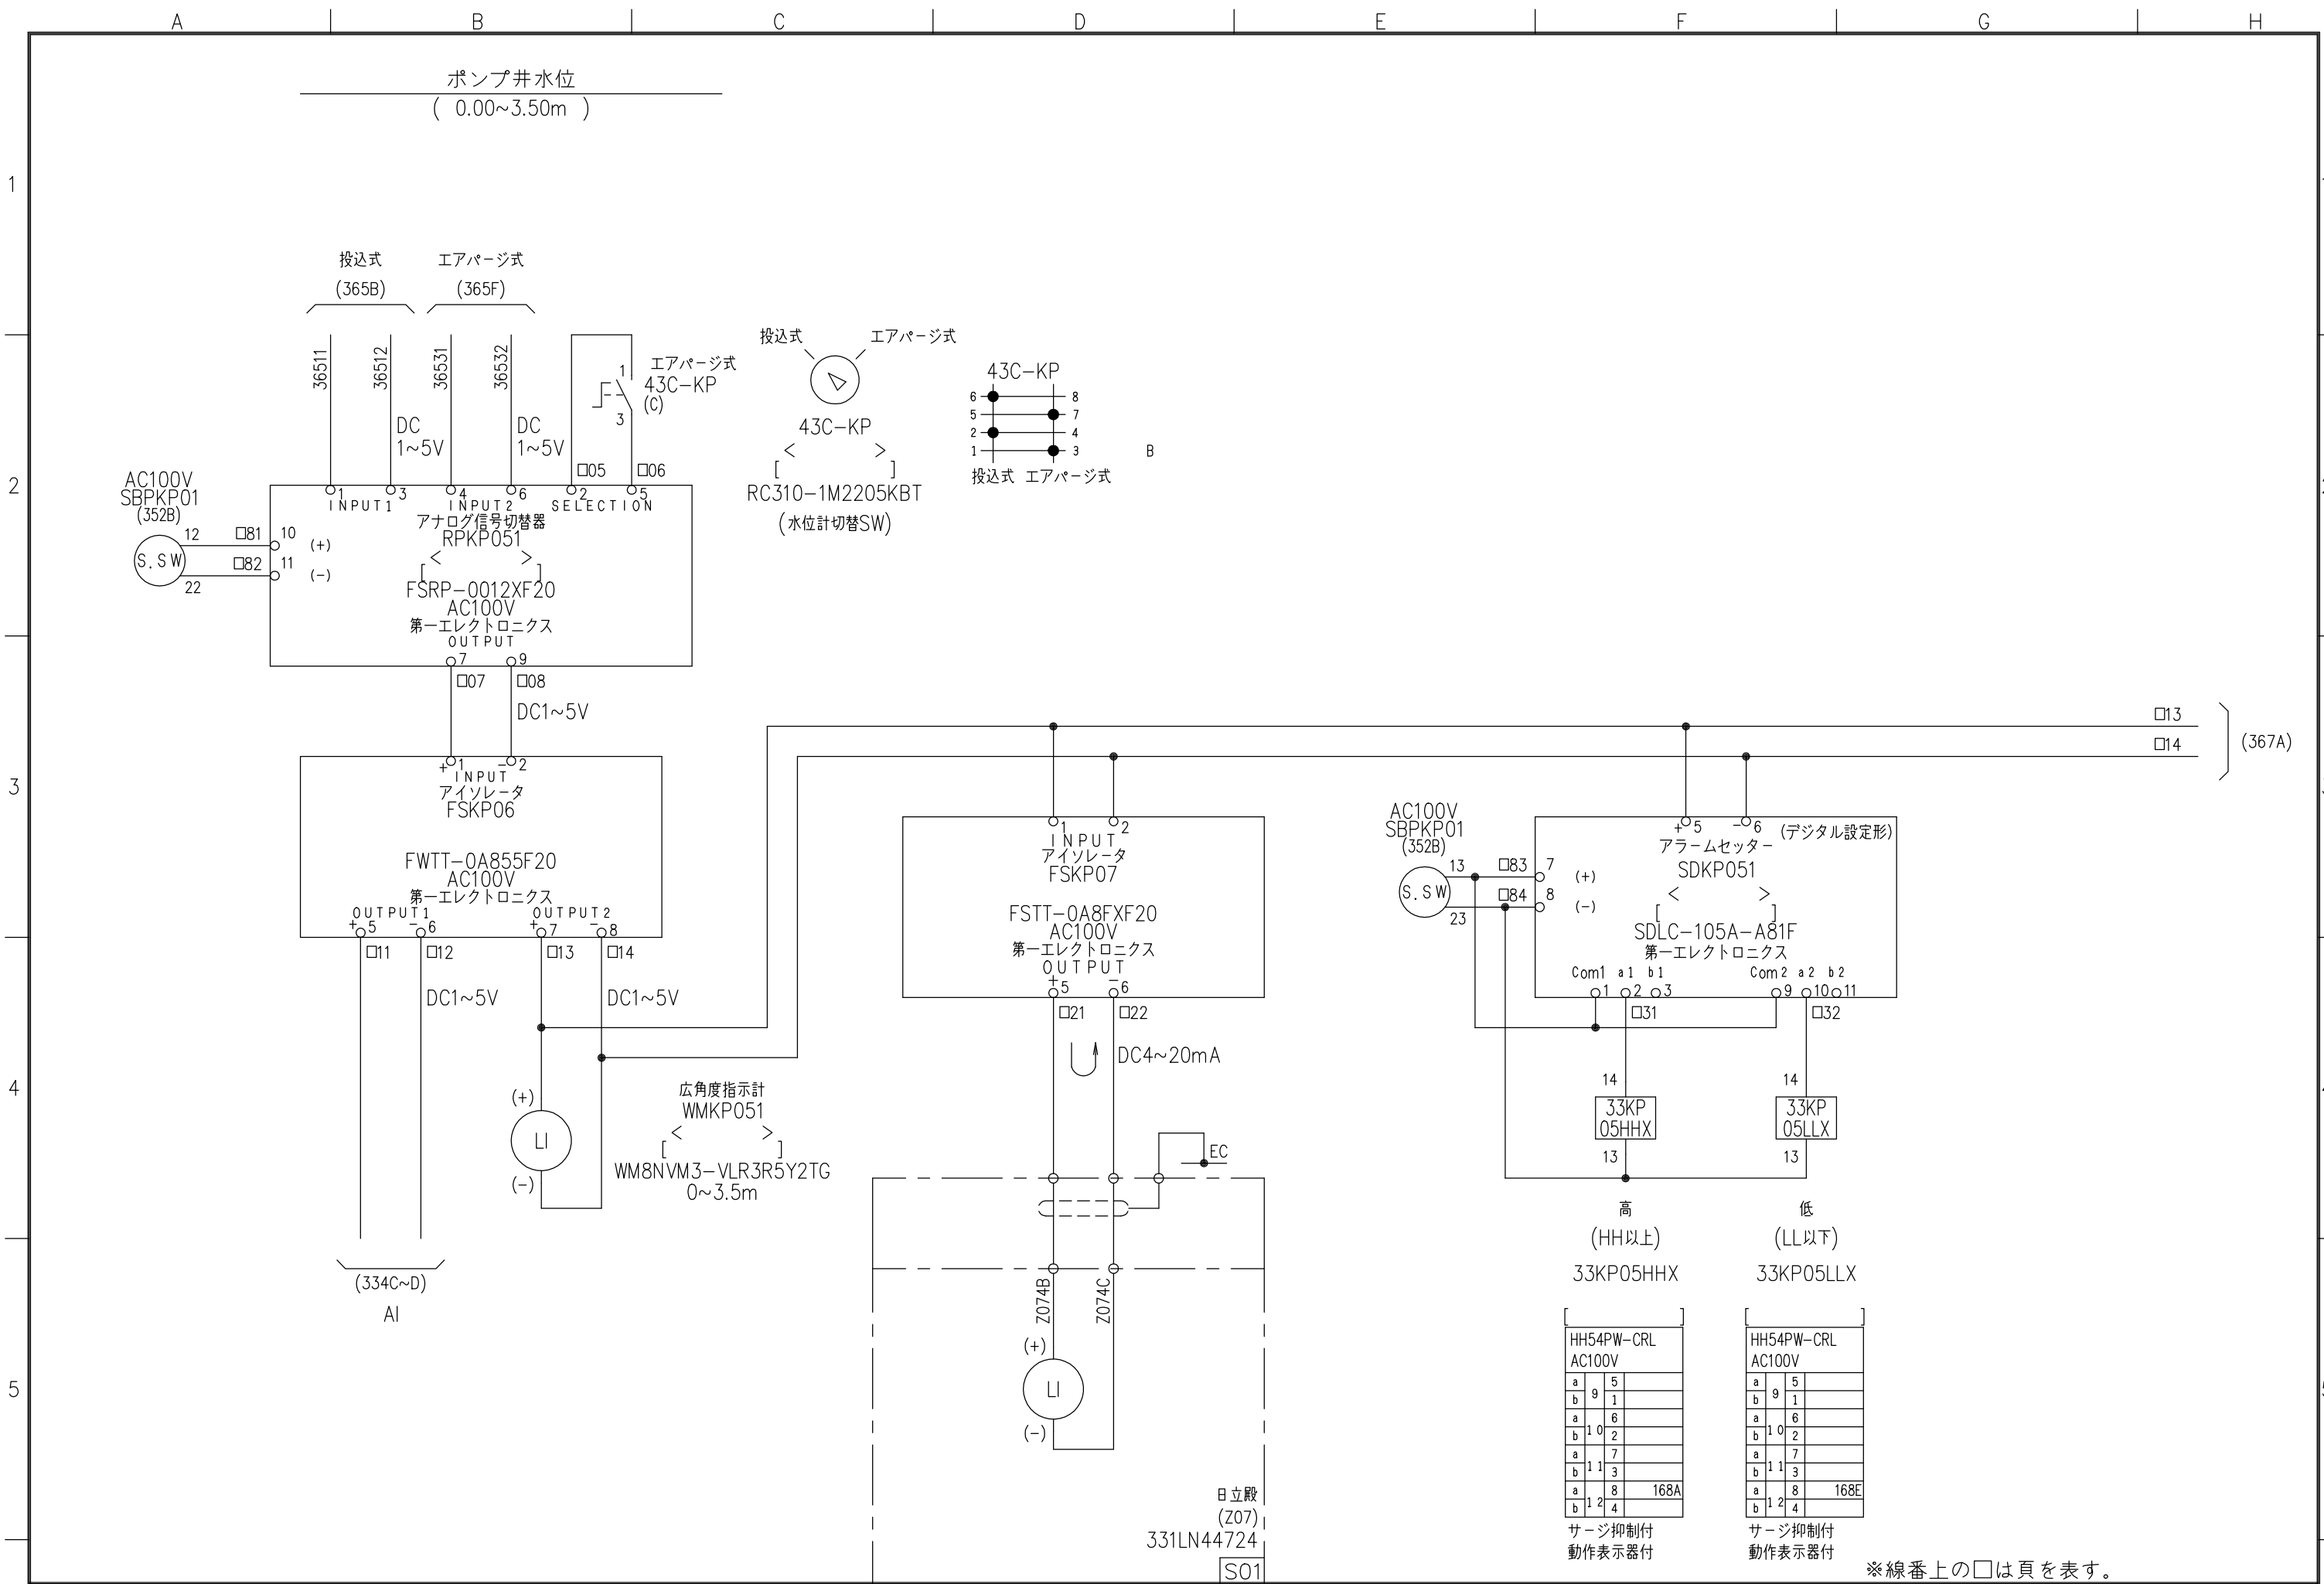


Revisions	)		Date	Name	メタウォーター株式会社 METAWATER Co., Ltd.	Title	計装テレメータ盤	Dwg.No.	MWA402712	366		a
	)	Drawn	2024-09-20	丸小野/阿多								
	)	Checked	2024-09-20	丹/淵邊			計装回路	Ref.	KW13_01_00c	KP		
	a) 図面修正フォロー			2024-11-11							丸小野/阿多	舟木

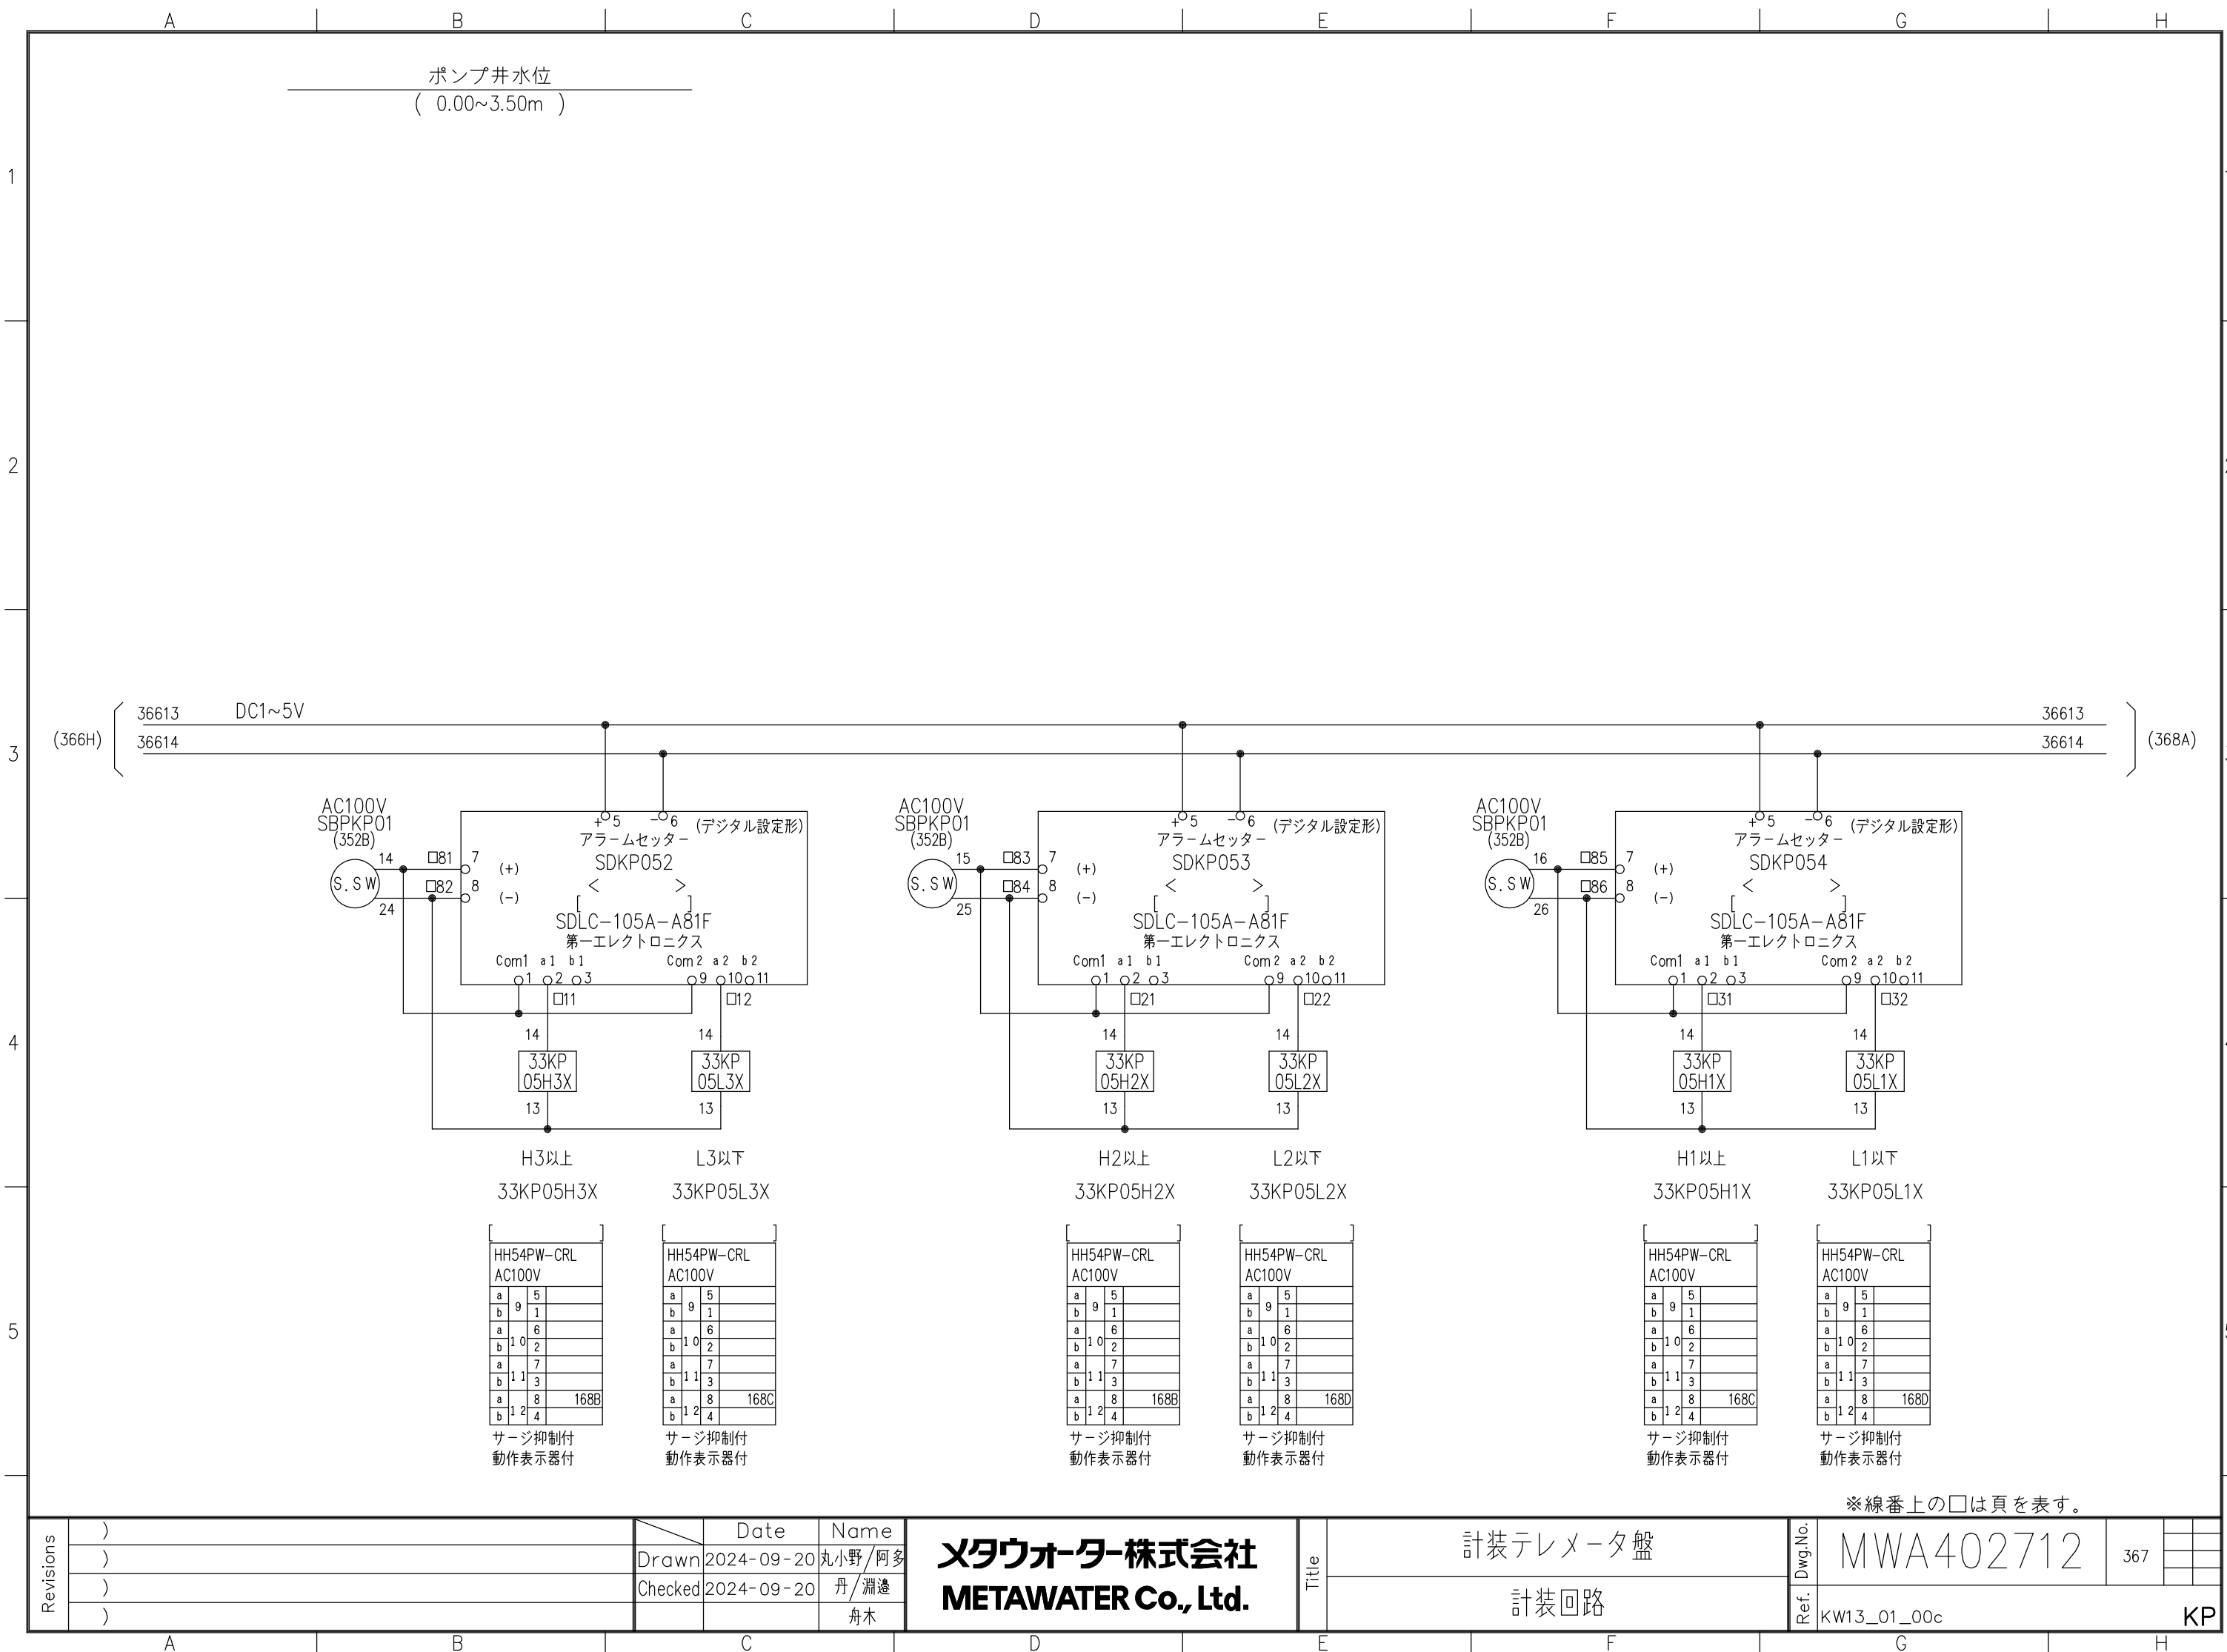

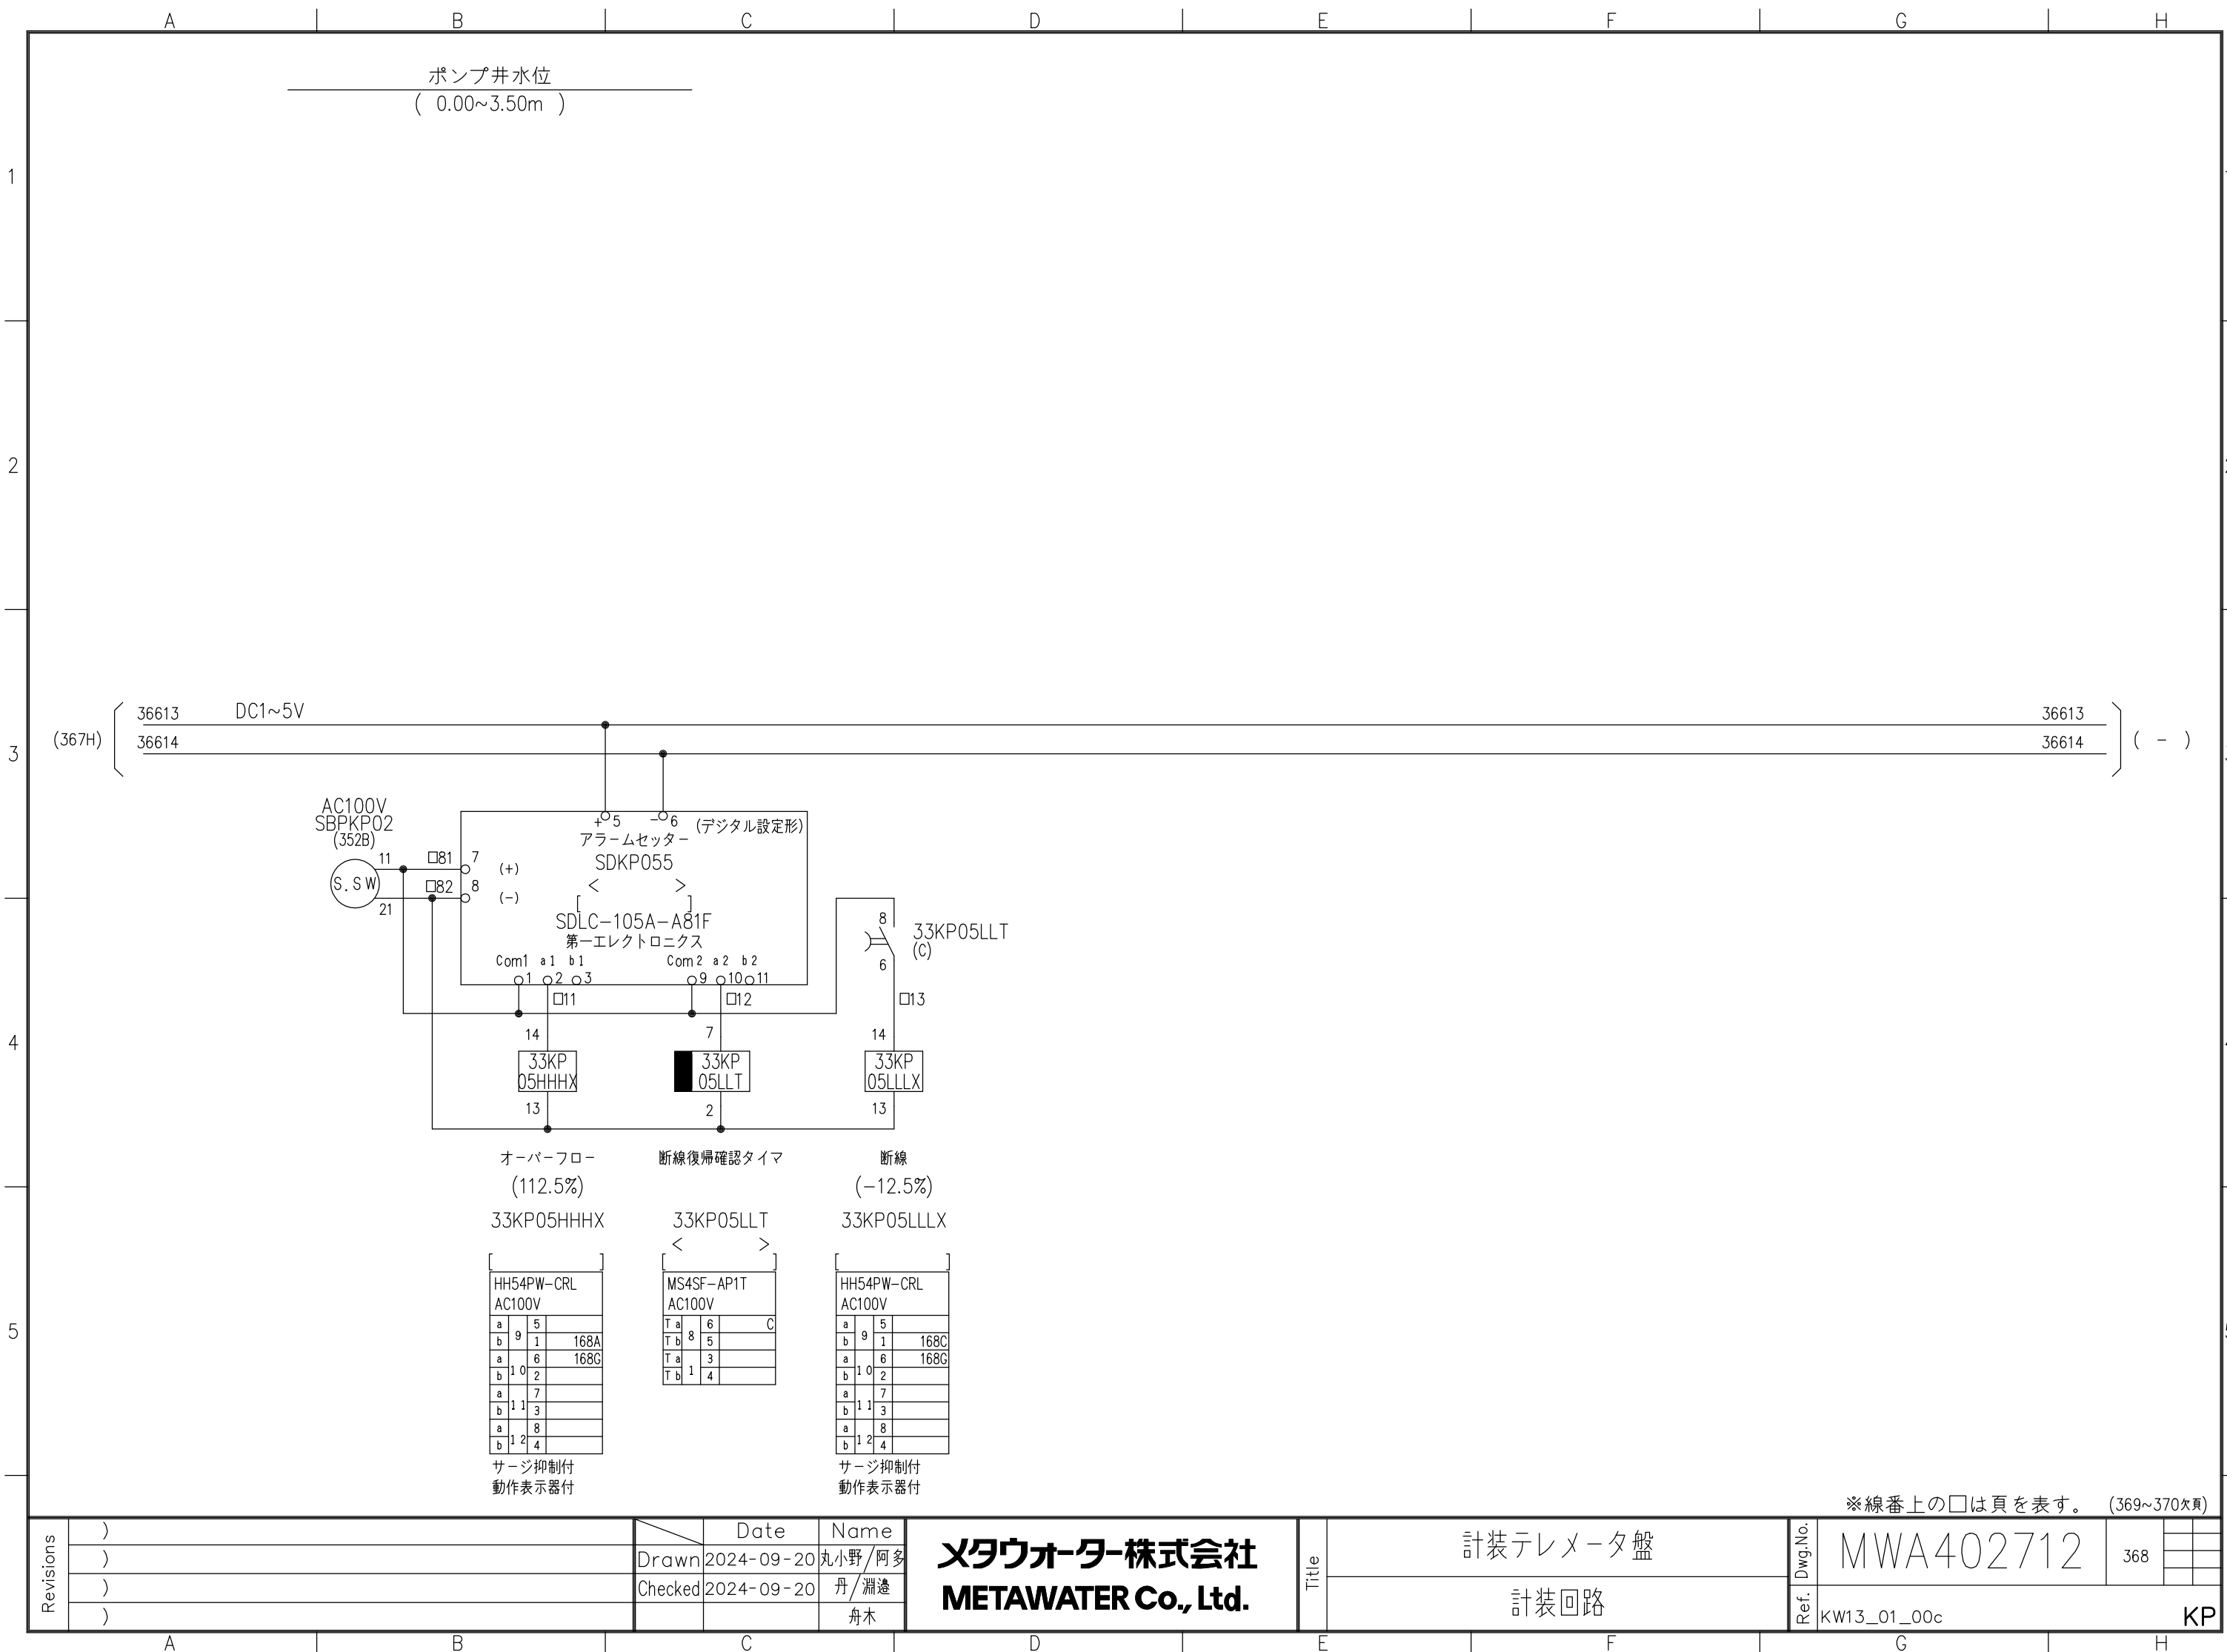


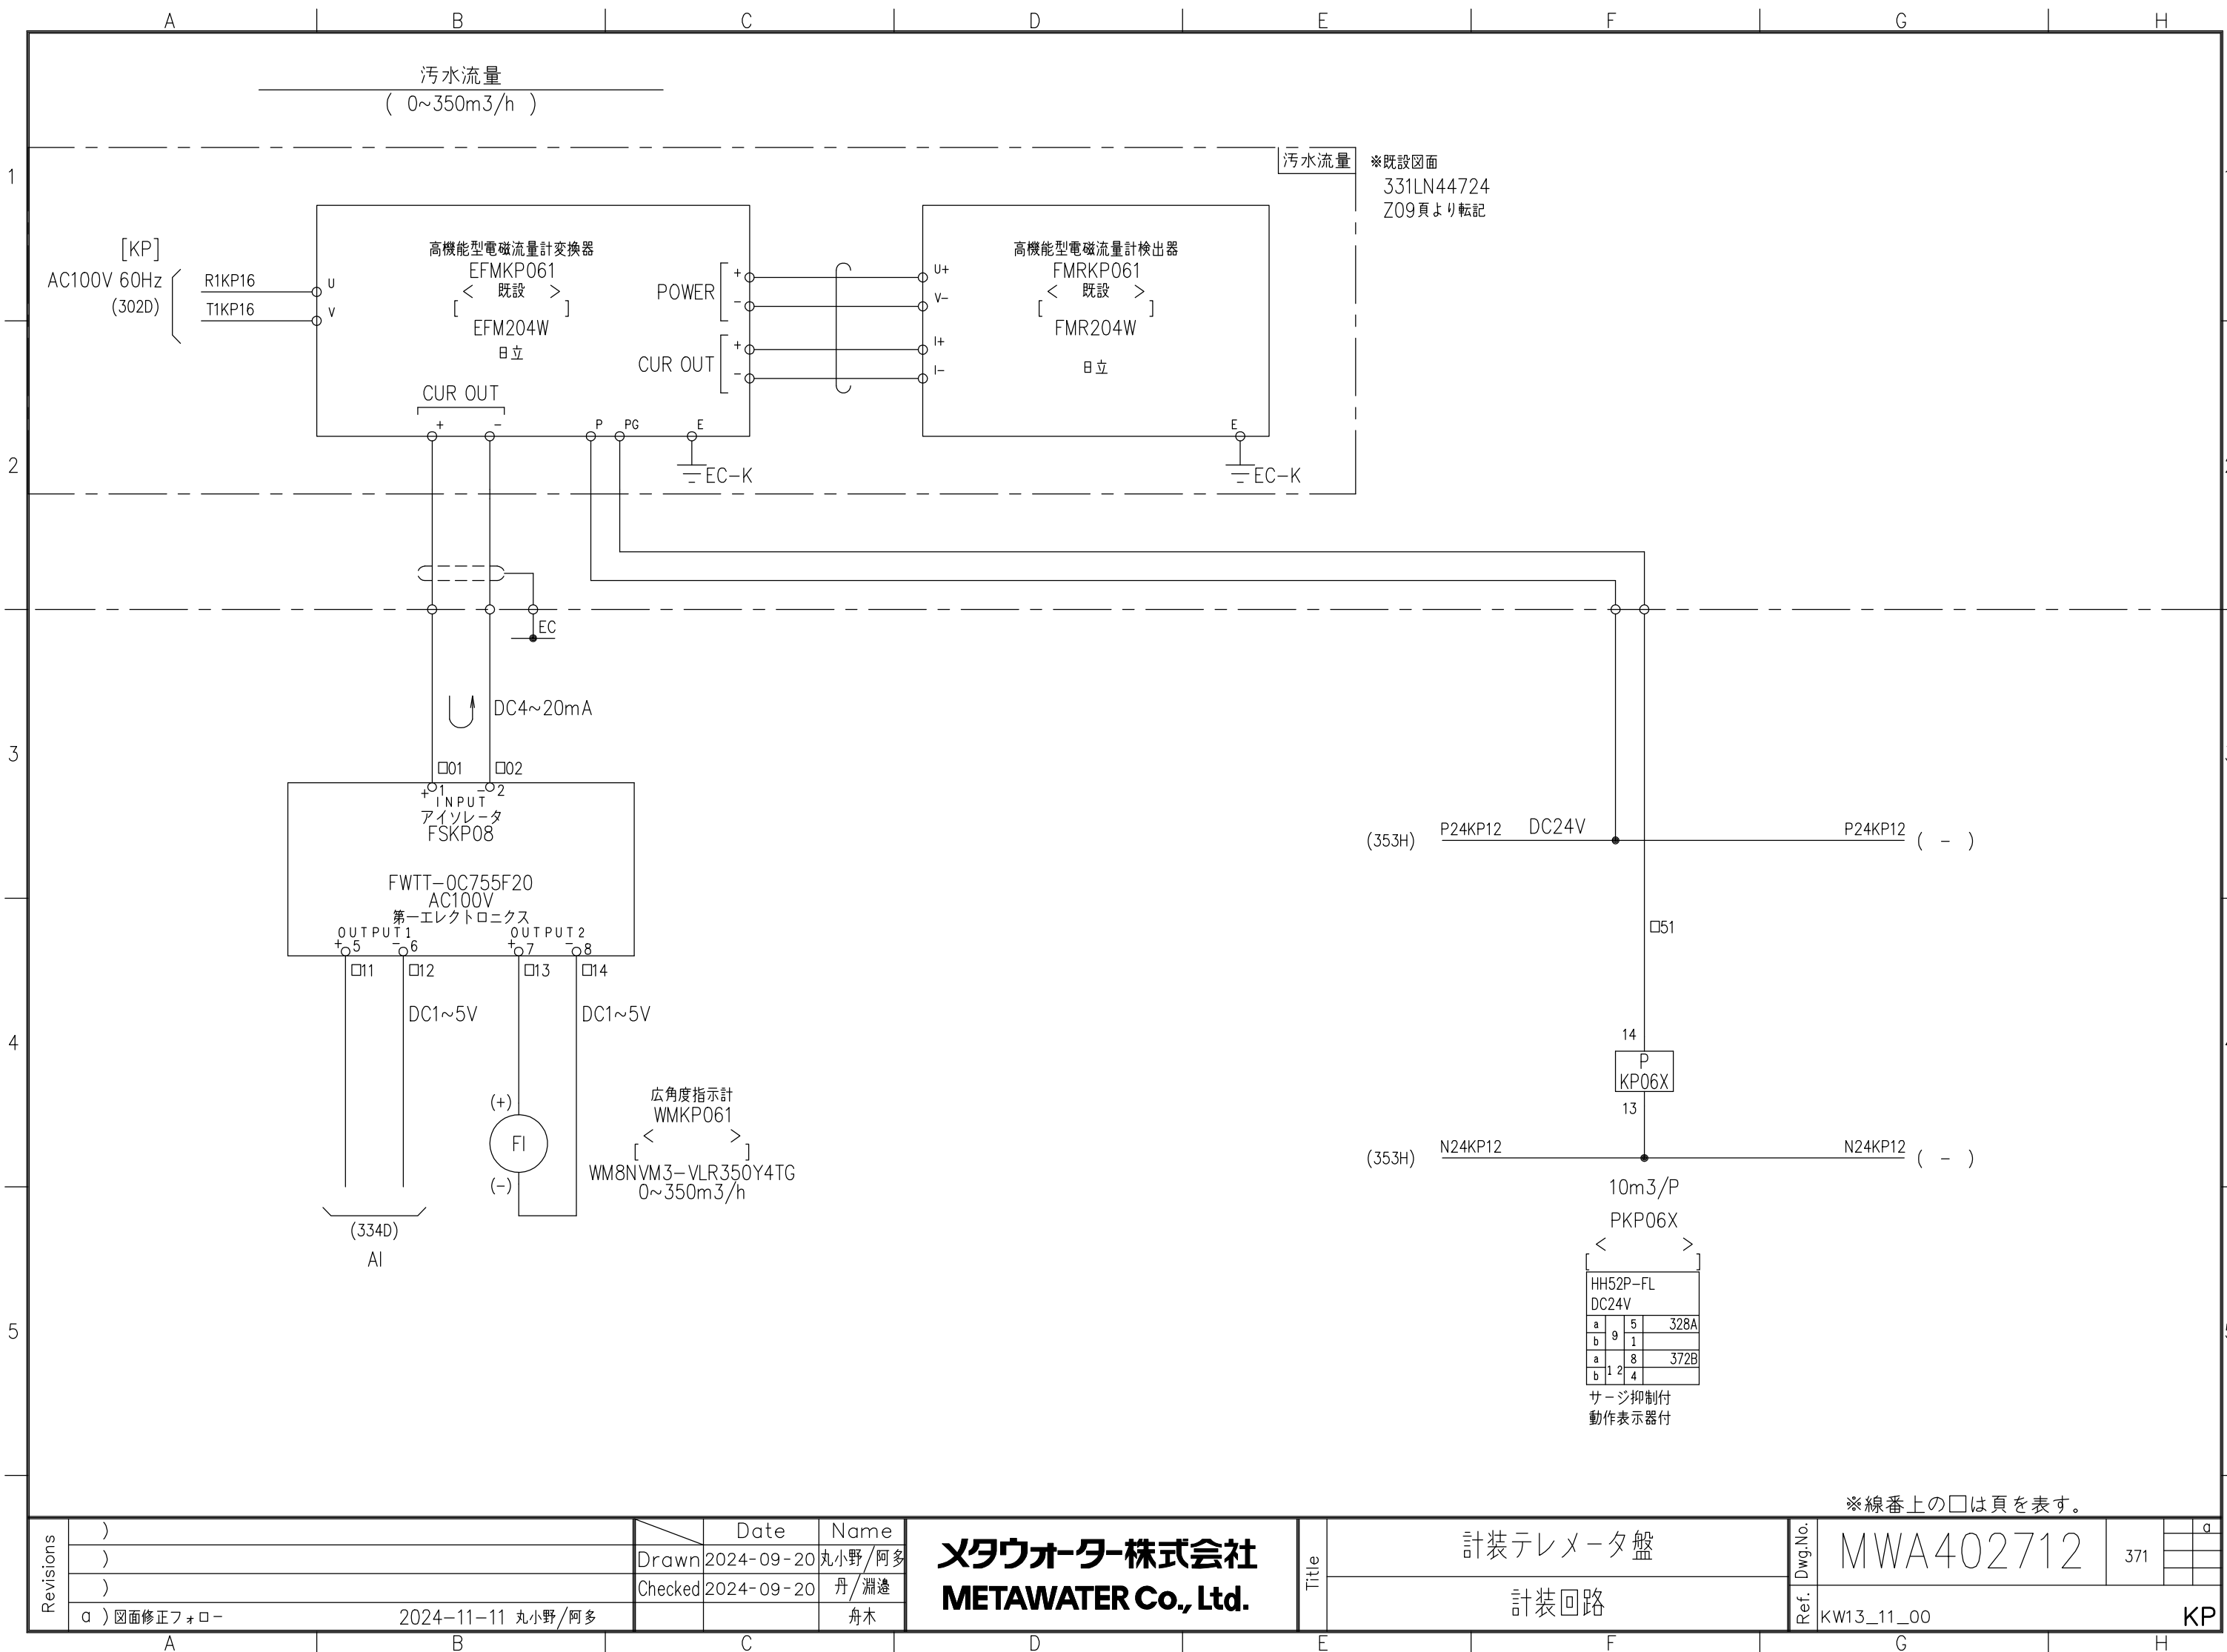

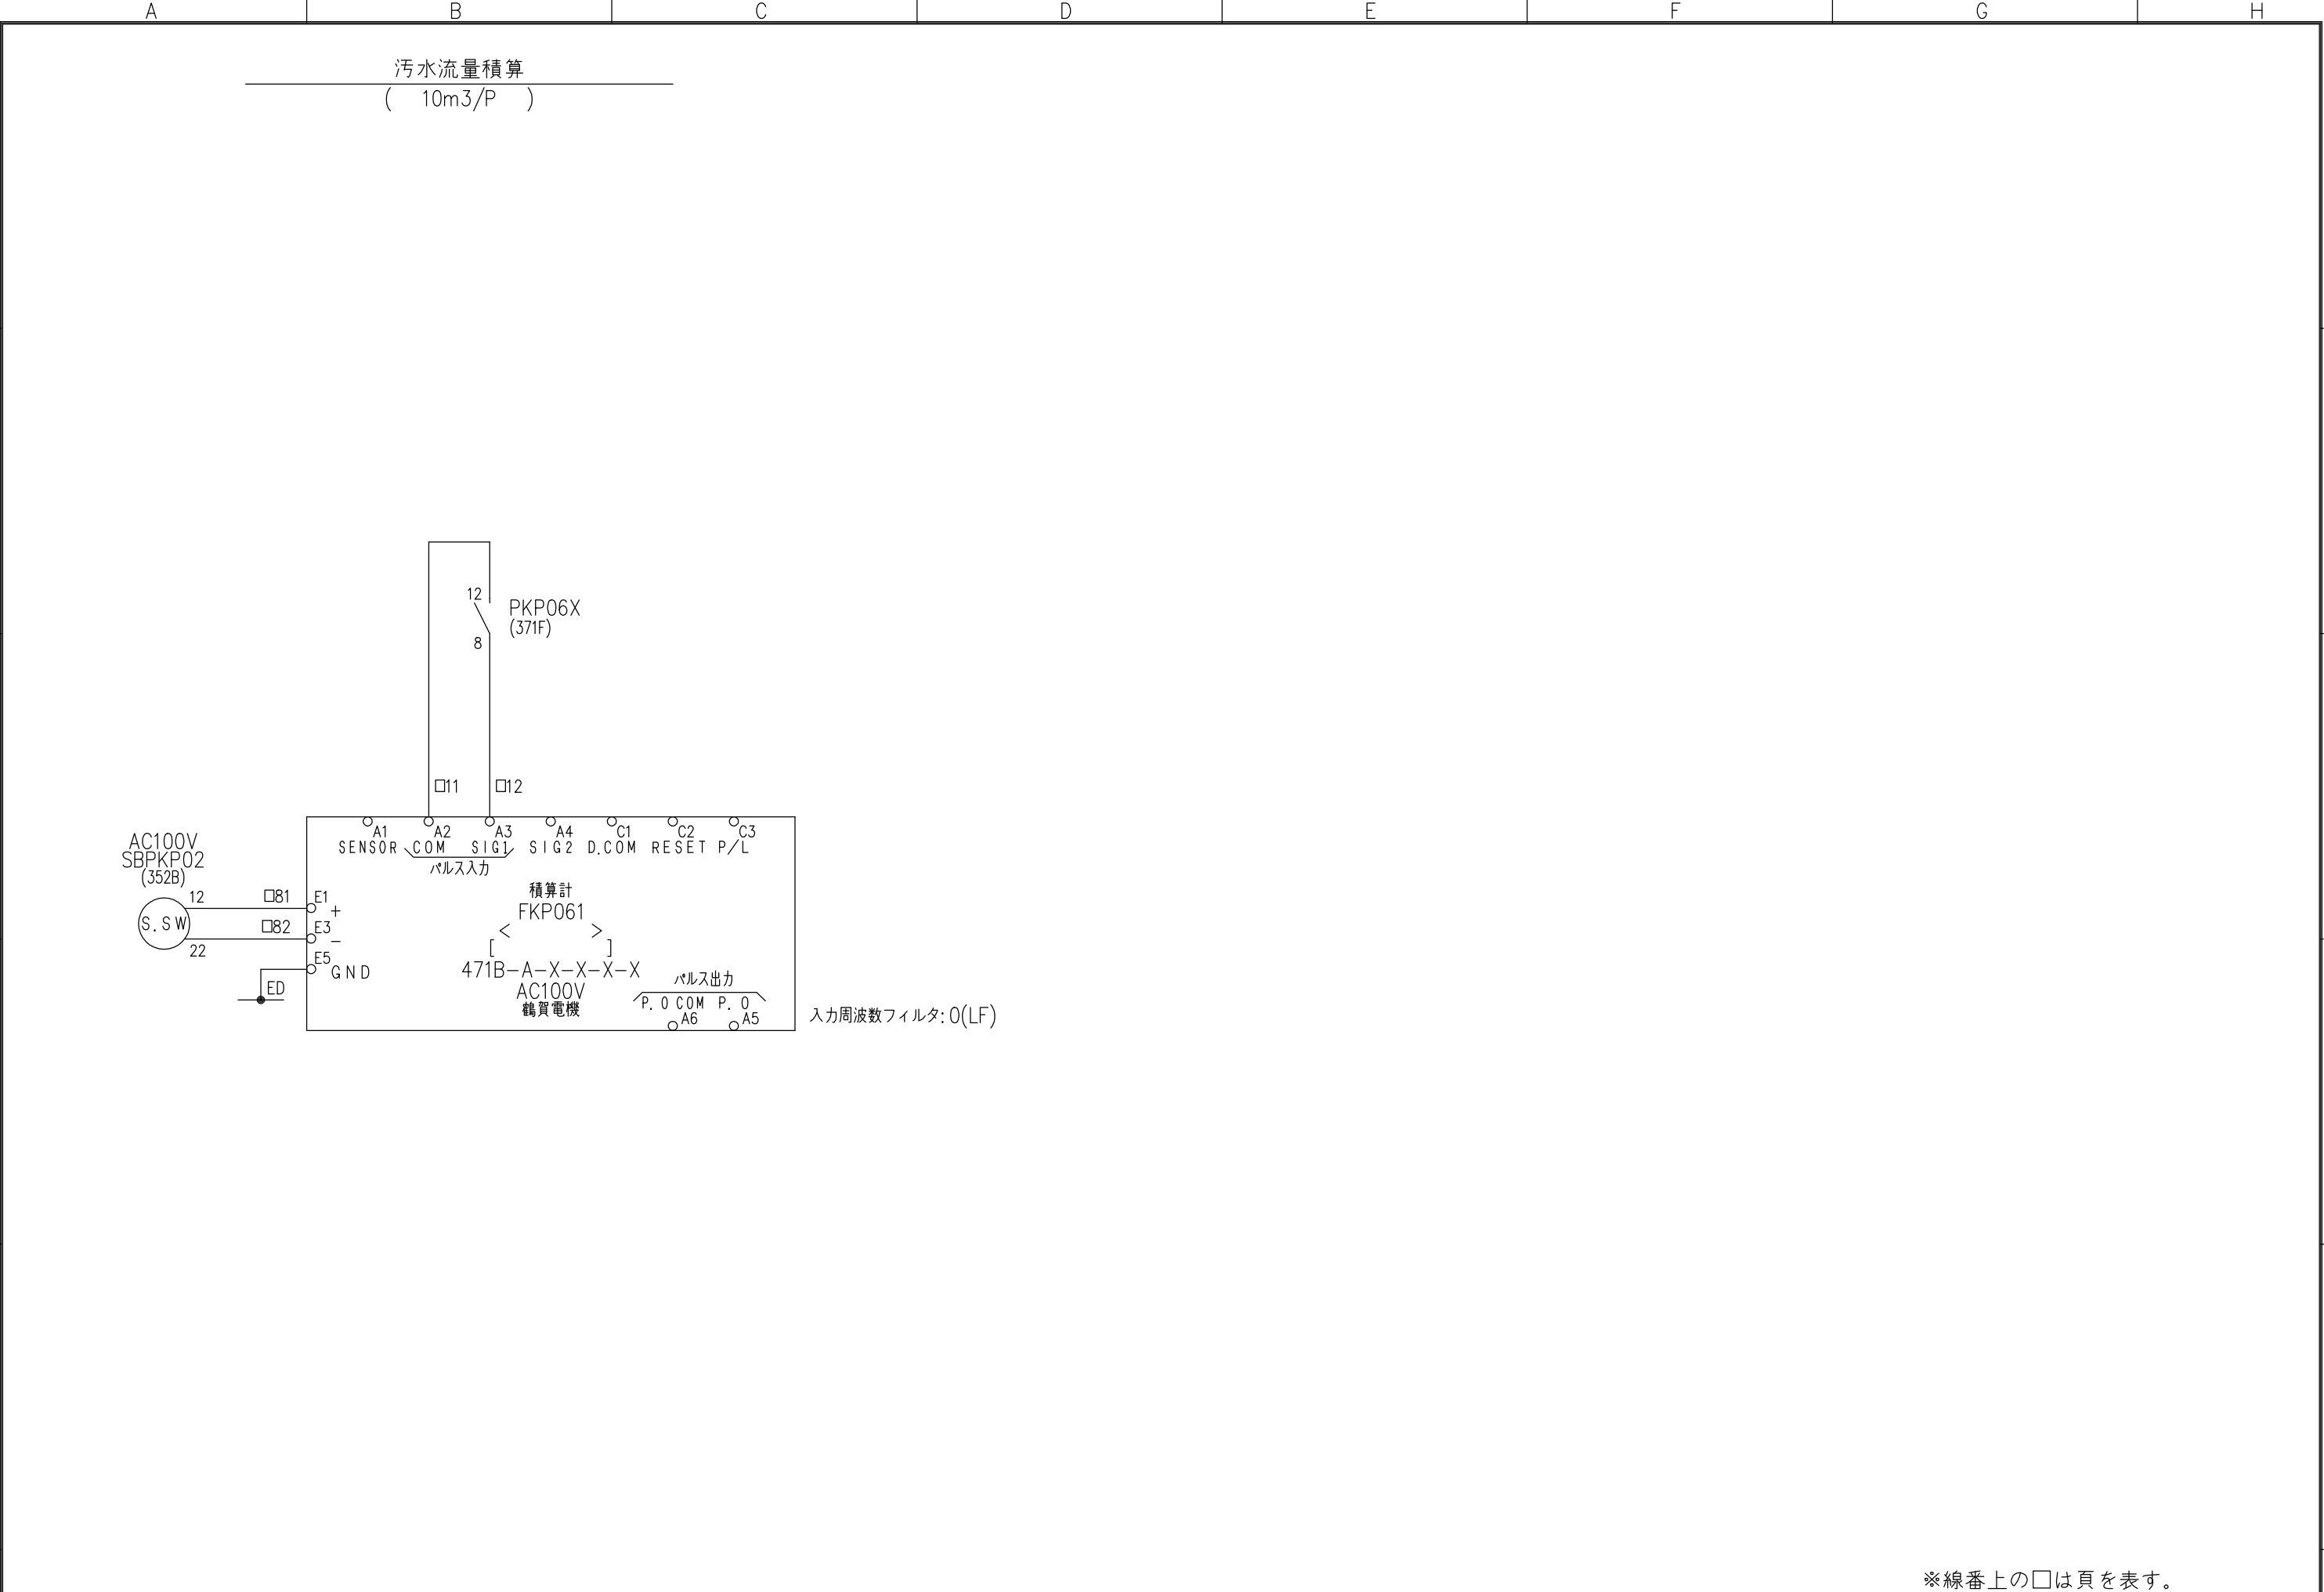


※線番上の□は頁を表す。


Revisions	)		Date	Name	メタウォーター株式会社 METAWATER Co., Ltd.	Title		Dwg.No.	MWA402712	372		
	)	Drawn	2024-09-20	丸小野/阿多			計装テレメータ盤					
	)	Checked	2024-09-20	丹/淵邊			計装回路	Ref.	KW13_11_05a	KP		
	)			舟木								

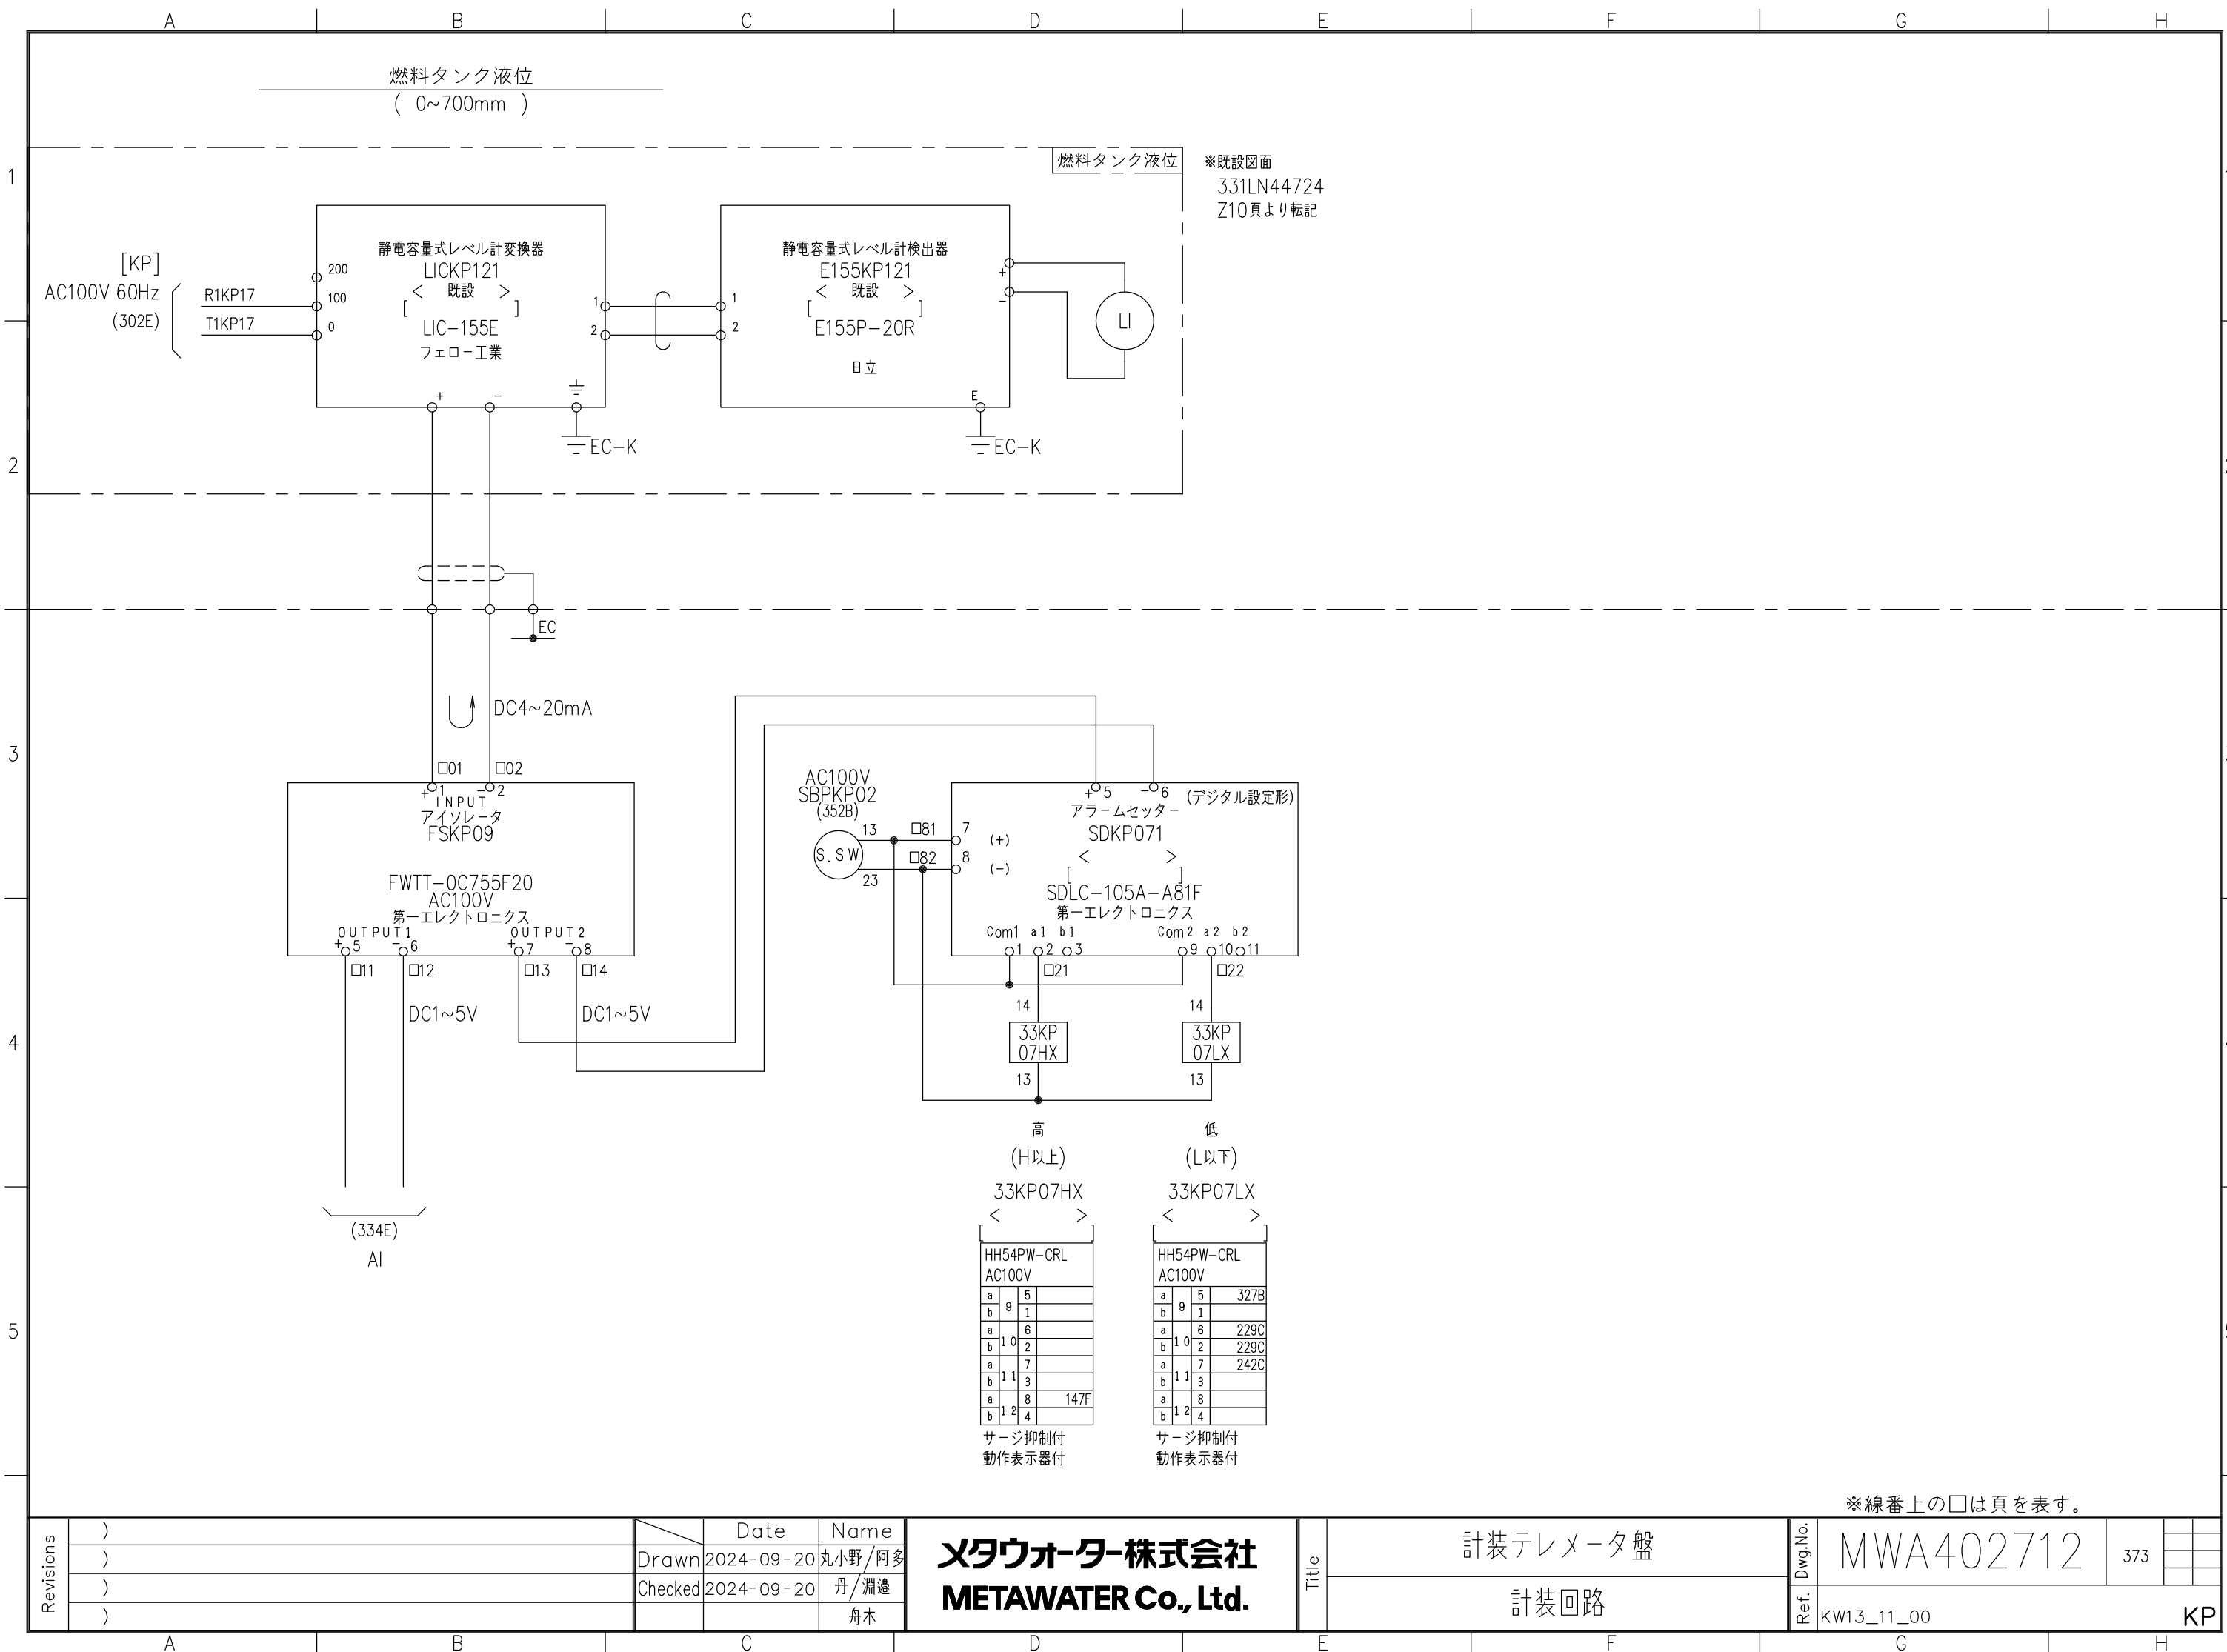

※線番上の□は頁を表す。

Revisions	)		Date	Name	メタウォーター株式会社 METAWATER Co., Ltd.	Title	計装テレメータ盤	Dwg.No.	MWA402712	373			
	)	Drawn	2024-09-20	丸小野/阿多			計装回路	Ref.	KW13_11_00	KP			
	)	Checked	2024-09-20	丹/淵邊									
	)			舟木									

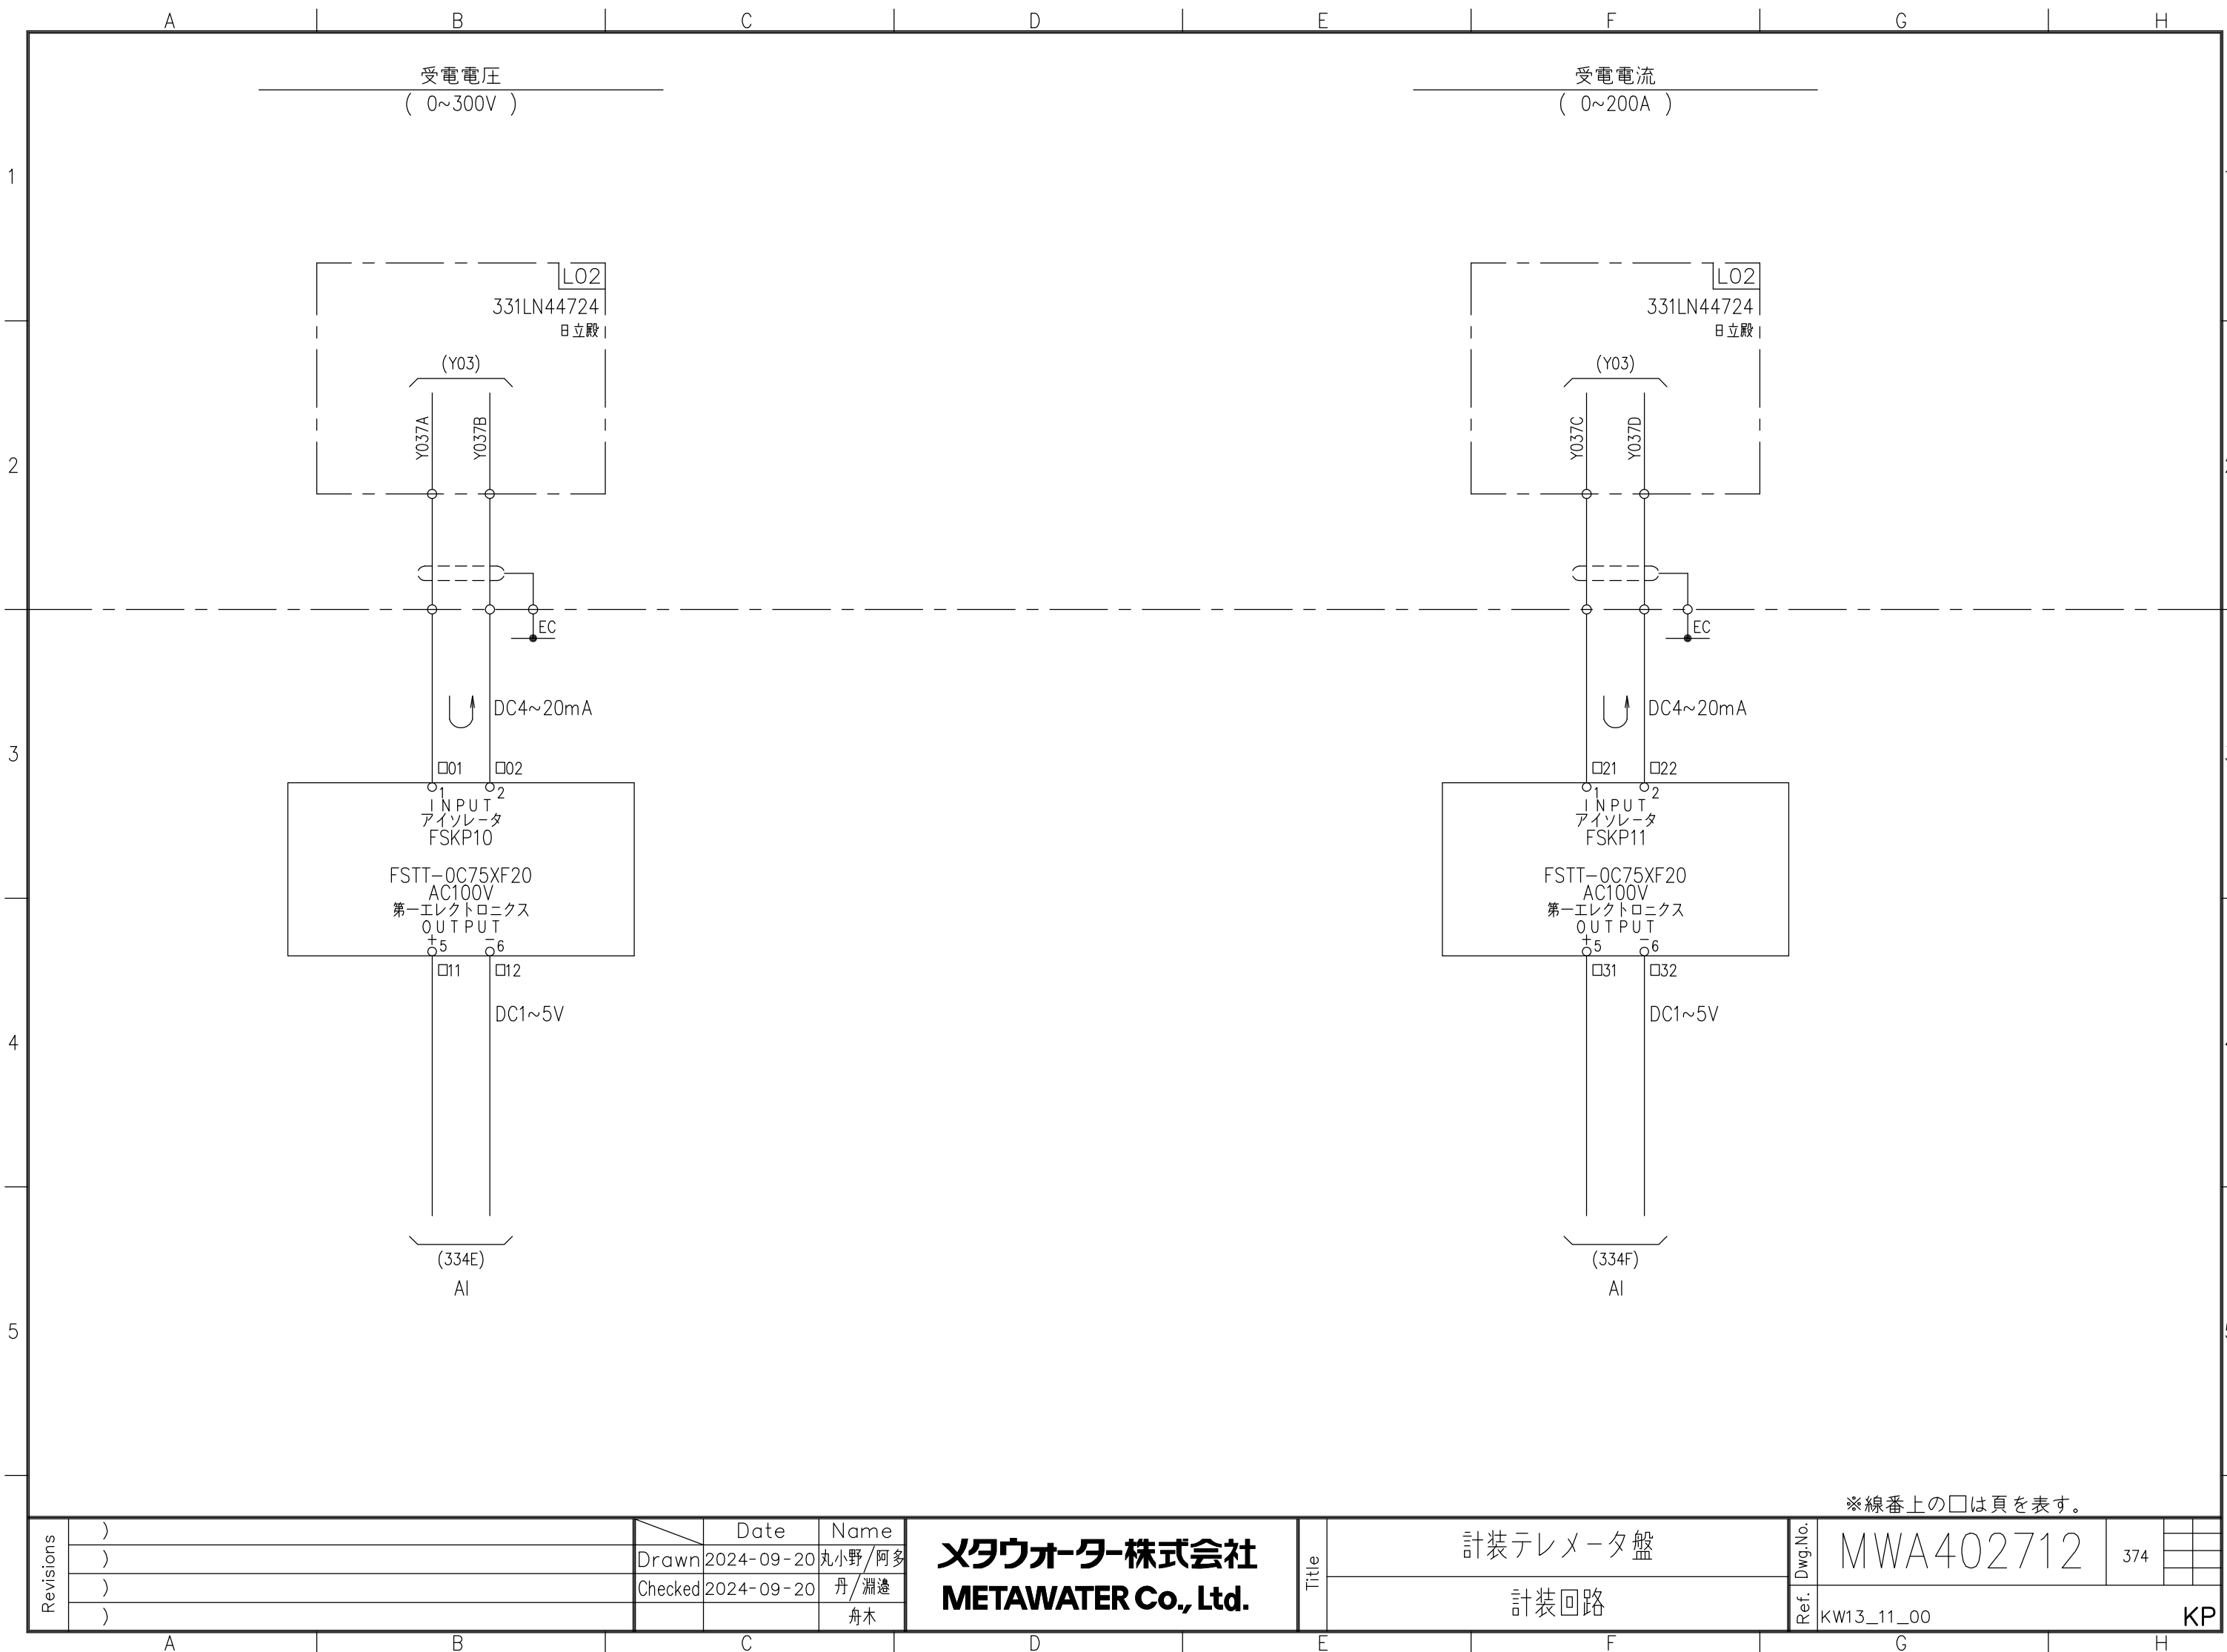

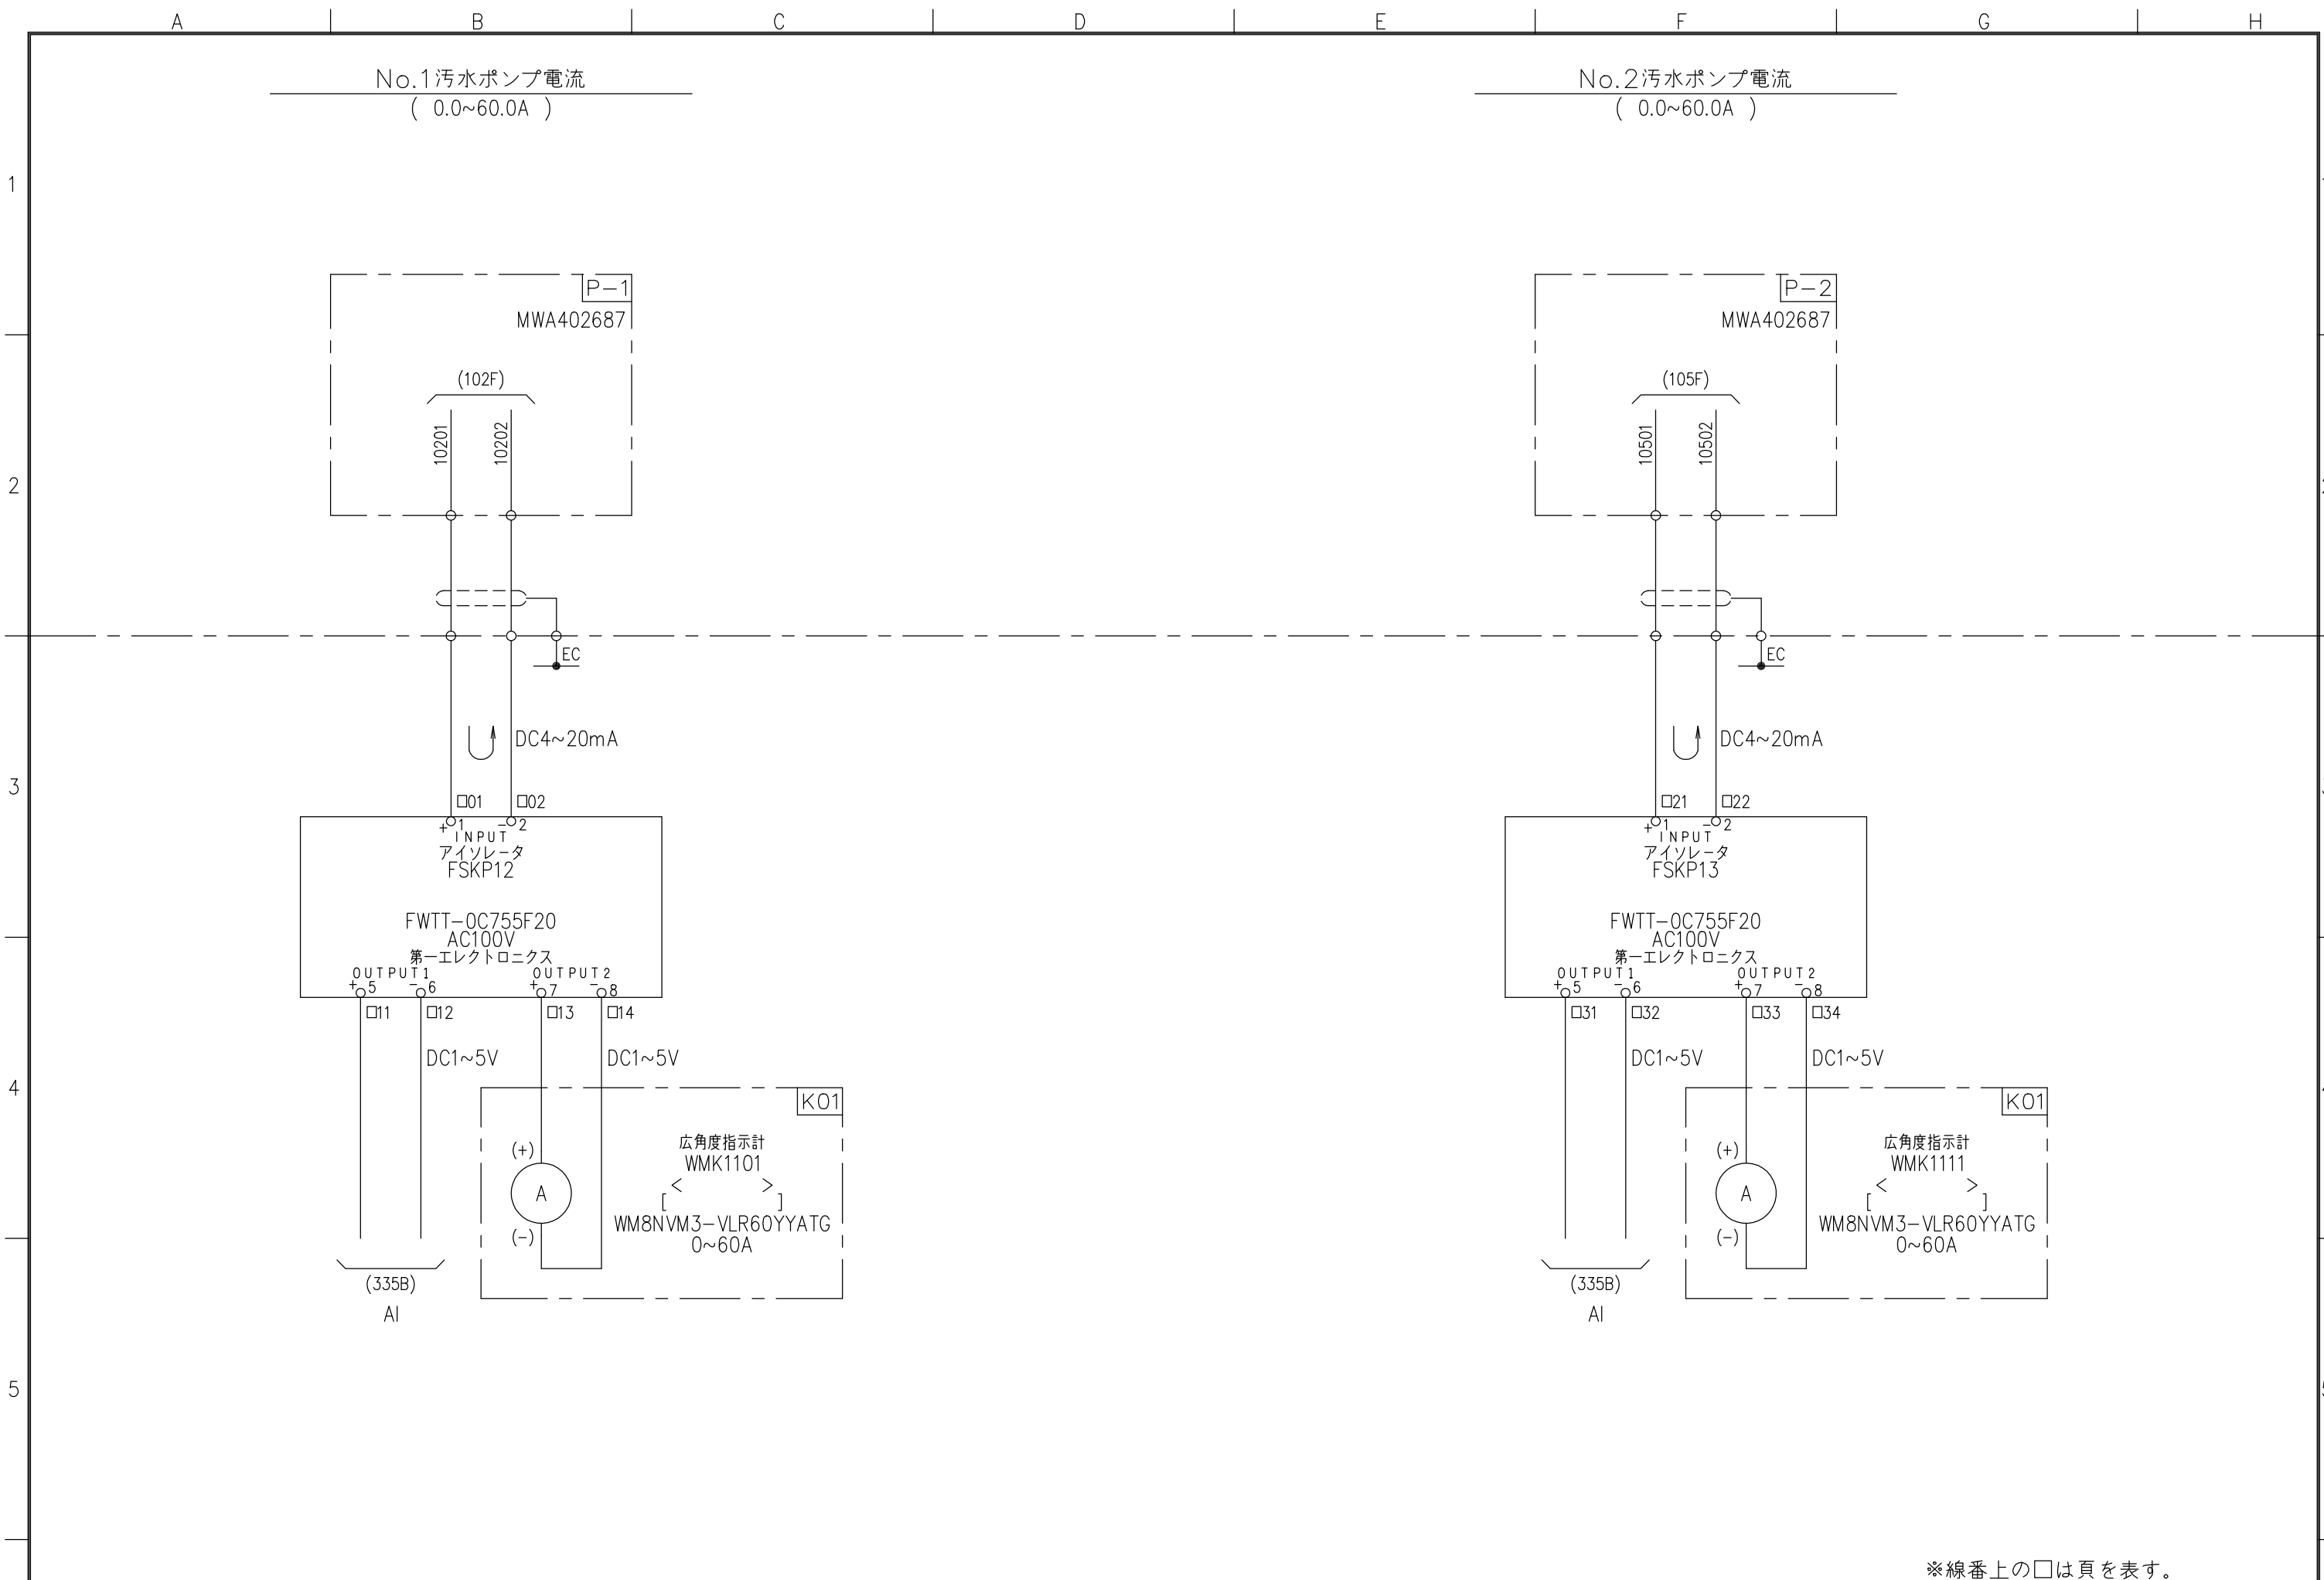

※線番上の□は頁を表す。

Revisions	)		Date	Name	メタウォーター株式会社 METAWATER Co., Ltd.	Title	計装テレメータ盤	Dwg.No.	MWA402712	375	a
	)	Drawn	2024-09-20	丸小野/阿多							
	)	Checked	2024-09-20	丹/淵邊			計装回路	Ref.	KW13_11_00	KP	
	a) 図面修正フォロー			舟木							

