

u | 2002-04-03
N33804
による現地試験フォロー
t | 2002-04-03
N33614
による現地試験フォロー
s | 2002-02-08
N33804
による取合フォロー
r | 2002-01-31
N33763
による取合フォロー
q | 2001-07-04
N33614
による取合フォロー
p | 2001-06-15
現地試験フォロー
o | 2001-05-09
アダプタ追加
n | 2001-03-21
ACS追加
m | 2000-11-09
一部変更
l | 2000-11-09
社内試験フォロー
k | 2000-09-20
一部変更
j | 2000-09-06
インターフェース変更
i | 2000-08-21
仕様変更及び
指摘事項による変更
h | 2000-06-08
アイソレータ追加
g | 2000-06-08
ケアレスミスフォロー
f | 2000-04-24
インターフェース見直し
e | 2000-03-01
M-F用ベースボード変更
d | 2000-02-18
入出力信号割付
c | 2000-02-18
分電盤盤略号変更
b | 2000-02-07
M-F収納ロッカー用
蛍光灯削除
a | 2000-01-13
M-F用ベースボード変更

変 更

v | 2003-02-07
Q33532
による取合フォロー

w | 2003-04-23
Q33532
による現地試験フォロー

x | 2004-01-19
Q33588
による取合フォロー

y | 2004-12-03
C18905による改造

z | 2005-11-07
C19378による改造

A | 2006-12-25
C48307
による改造

B | 2009-1-30
A0006550
による改造

以降の変更記号および
内容の詳細については、
変更履歴一覧表を参照

FUJIELECTRIC

展開接続図

御注文主 鹿児島市水道局 殿

納入場所 河頭浄水場

用途 河頭浄水場関連施設集中監視制御設備工事

A0006550
C48307
C19378
C18905
Q33588
製番 G33834
N33614
N33763
N33804

項目	内 容	ペ ー ジ	項目	内 容	ペ ー ジ
1	工事履歴一覧表, 変更履歴一覧表	001, 001-1	16		
2	展開接続図の見方	002	17	データロガー室CVCF分電盤(2)	101~131
3	制御器具番号表	003	18	データロガー室CVCF分電盤(1)	151~181
4	図記号一覧表	004~006	19		
5	接地基準	007~008	20		
6			21		
7	システム系統図	021~024	22		
8			23		
9			24		
10			25		
11			26		
12			27		
13			28		
14			29		
15			30		

製 図	調 査	検 認
河野、折茂 1999・12・29	宮腰 1999・12・29	山内 1999・12・29

図番 W426297

富士電機株式会社



A		B		C		D		E		F		G		H		
1																1
項目		内 容			ペ ー ジ		項目		内 容			ペ ー ジ				
31		—— 河頭管轄入出力制御装置 ——					61		—— 浄水場間入出力制御装置 ——							
32		電源回路			301		62		電源回路			601				
33		雑電源回路			311		63		雑電源回路			611				
34							64		ACS実装図			616				
35		F150S接続図、イーサネット接続図			321~325		65		F150S接続図、イーサネット接続図			621~623				
36							66									
37							67									
38		Tリンク接続図			331~335		68									
39		インターフェース回路			351~389-3		69		インターフェース回路			651~652				
40							70									
41		計装回路			391~392		71									
42							72									
43							73									
44							74									
45							75									
46		—— 管理管轄入出力制御装置 ——					76		—— 場外系中継端子盤 ——							
47		電源回路			401~403		77									
48		雑電源回路			411		78		雑電源回路			711				
49							79		計装回路			721				
50		F150S接続図、イーサネット接続図(1)			421~424		80									
51		F150S接続図、イーサネット接続図(2)			431~434		81									
52		F120S接続図、イーサネット接続図(武之橋下用)			441~442		82		—— 甲系ろ過池操作室中継端子盤 ——							
53		計装回路			491		83									
54							84		雑電源回路			761				
55		Tリンク接続図(1)			501~502		85		インターフェース回路			771~773				
56		インターフェース回路			511~531		86									
57							87									
58		Tリンク接続図(2)			551~553		88									
59		インターフェース回路			561~595		89									
60							90									
Revisions	○				Date	Name		Fuji Electric Co.,Ltd.	Title	目 次	Ref. Dwg. No.	W426297	000-1	g n		
	○				Drawn	河野										
	㊦	ACS追加	01-03-21	折茂	Checked											
	㊧	ページ変更	00-06-08	河野												
A		B		C		D		E		F		G		H		

工 事 履 歴 一 覧 表

変更記号	製 番	年 月 日	工 事 名 称	備 考
オリジナル	G33834	’99-12-27		POS< >
q	N33614	’01-07-04	中迫ポンプ所外電気計装設備工事	
r	N33763	’02-01-31	宇宿ポンプ所電気計装設備工事	
s	N33804	’02-02-08	田上ポンプ所関連電気計装設備工事	
v	Q33532	’03-02-07	河頭浄水場計装設備工事	小野ポンプ所・脇田水源地・TM更新
x	Q33588	’04-01-19	河頭排水処理場電気設備工事	健康の森ポンプ所・鍋ヶ宇都配水池・田上台配水池
y	C18905	’04-12-03	若葉台配水池他計装設備工事	
z	C19378	’05-11-07	大峯ポンプ所電気計装設備ほか工事	
A	C48307	’06-12-25	伊敷台ポンプ所電気計装設備工事	
B	A0006550	’09-01-30	中山ポンプ所電気計装設備ほか工事	
C	A0208990	’10-02-22	星ヶ峯第二配水池ほか電気計装設備工事	
E	A0324990	’11-07-29	皇徳寺ポンプ所電気計装設備工事	
G	A0441080	2013-02-15	清泉寺水源地電気計装設備工事	
J	J1037400	2019-05-15	花野口ポンプ所ほか電気計装設備工事	
J	J1041559	2020-01-31	河頭浄水場ほか監視制御設備工事	
N	J1046896	2020-11-09	河頭浄水場ほか監視制御設備機能増設工事	

Revisions	)		Date	Name	メタウォーター株式会社 METAWATER Co., Ltd.	Title	工事履歴一覧表	Dwg.No.	W426297	001		
	)	Drawn	-	-							河野	
	)	Checked	-	-								
	)											
Ref.								CW00_02				

1

25

展開接続図の見方

1. 展開接続図は下記の規格を基準としてE.C.W.D (Elementary control Wiring Diagram) 方式で記入されています。

- (1) JIS C0301

(2) JIS C0401

(3) JEM 1090~1094
- 電気用図記号

制御用展開接続図

制御器具番号

2. 展開接続図のシート番号は最大4桁 (1~4桁) としています。4桁の場合、先頭は必ずアルファベットとなります。尚、変更により分割された場合前頁のシート番号-1、-2としています。 (例2-1, 2-2)

3. 外部端子および線番号は下記により表しています。

(1) 一般

□□□□

○○

シート番号に対応した英文字・数字

同一シート内での追番号 (原則2桁)


(左より右へ、かつ上から下への順 (01~99))

4. 使用器具型式の表示


各機器のシンボルの近傍に項番 (弊社手配No.) 型式、仕様を記入してあります。
タイマーについては、整定範囲を記入します。
整定値を指定する場合は、コイル右下に記入してあります。

5. 接点の来先, 行先表示

- a) 来先はコイルが記入されたシート番号とコイル位置アドレス (横座区分A~H) で示しています。
また同一シート内のは位置アドレスのみ記入し、シート番号は省略します。

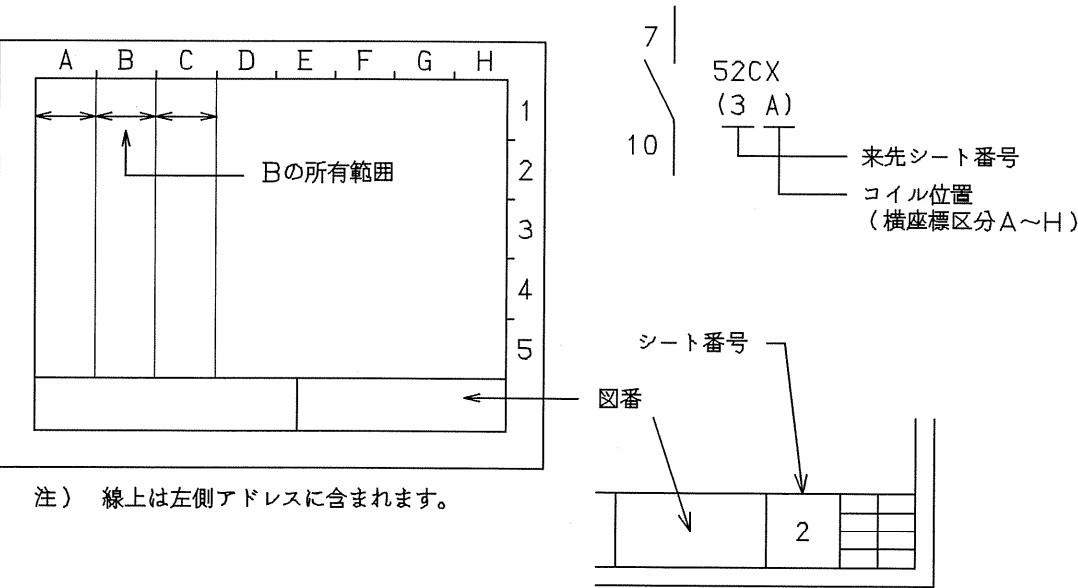

- b) 行先は展開接続図中のリレーコイルの下に接点構成図を表示し、来先と同様に記入してあります。

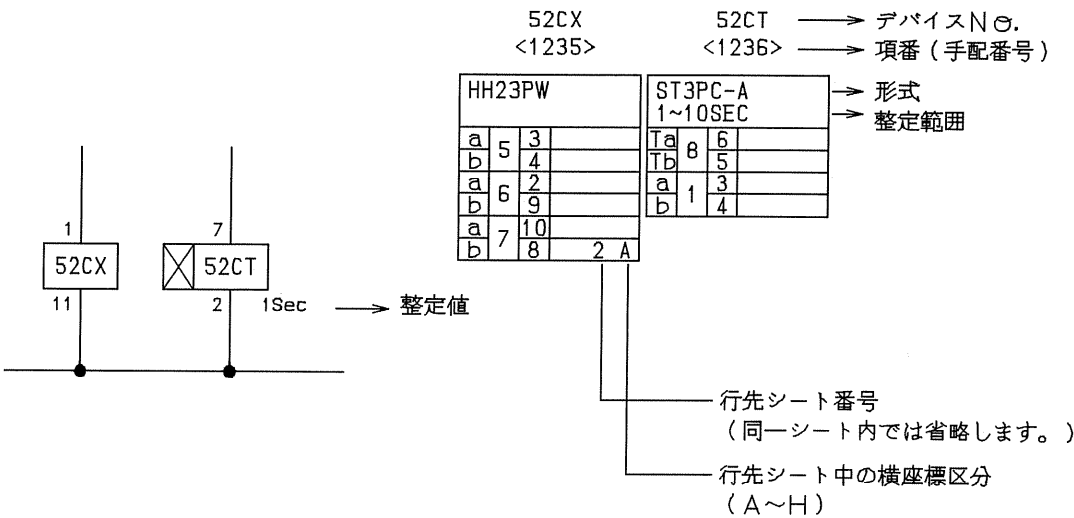

6. 制御電源又は信号線が、前後のシート以外におよぶ場合は来先, 行先を記入してあります。

(例) ——— R1C ——— 線番記号
(28B) ——— 行先シートNo. 或は、行先ユニットページ No.

7. 盤外の計測信号線についてはシールド線の表現を省略してあるが、原則としてすべてシールド線を使用するものとする。

以上

A		B		C		D		E		F		G		H		
器具 番号	器 具 名 称			器具 番号	器 具 名 称			器具 番号	器 具 名 称			器具 番号	器 具 名 称			
1	1	主幹制御器又はスイッチ			26	静止器温度スイッチ又は継電器			50	短絡選択継電器又は地絡選択継電器			74	調 整 弁		
	2	始動若しくは閉路限時継電器又は 始動若しくは閉路遅延継電器			27	交流不足電圧継電器			51	交流過電流継電器又は地絡過電流継電器			75	制動装置		
	3	操作スイッチ			28	警報装置			52	交流遮断器又は接触器			76	直流過電流継電器		
	4	主制御回路用接触器又は継電器			29	消火装置			53	励磁継電器又は励弧継電器			77	負荷調整装置		
	5	停止スイッチ又は継電器			30	機器の状態又は故障表示装置			54	高速度遮断器			78	搬送保護位相比較継電器		
2	6	始動遮断器，スイッチ， 接触器又は継電器			31	界磁変更遮断器，スイッチ， 接触器又は継電器			55	自動力率調整器又は力率継電器			79	交流再閉路継電器		
	7	調整スイッチ			32	直流逆流継電器			56	すべり検出器又は脱調継電器			80	直流不足電圧継電器		
	8	制御電源スイッチ			33	位置検出スイッチ又は装置			57	自動電流調整器又は電流継電器			81	調速機駆動装置		
	9	界磁転極スイッチ，接触器又は継電器			34	電動順序制御器			58	（予備番号）			82	直流再閉路継電器		
	10	順序スイッチ又はプログラム制御器			35	ブラシ操作装置又はスリップリング			59	交流過電圧継電器			83	選択スイッチ，接触器又は継電器		
3	11	試験スイッチ又は継電器			36	短絡装置			60	自動電圧平衡調整器又は 電圧平衡継電器			84	電圧継電器		
	12	過速度スイッチ又は継電器			37	極性継電器			61	自動電流平衡調整器又は 電流平衡継電器			85	信号継電器		
	13	同期速度スイッチ又は継電器			38	不足電流継電器			62	停止若しくは開路限時継電器又は 停止若しくは開路遅延継電器			86	ロックアウト継電器		
	14	低速度スイッチ又は継電器			39	軸受温度スイッチ又は継電器			63	圧力スイッチ又は継電器			87	差動継電器		
	15	速度調整装置			40	機械的異常監視装置又は検出スイッチ			64	地絡過電圧継電器			88	補機用遮断器，スイッチ， 接触器又は継電器		
4	16	表示線監視継電器			41	界磁電流継電器又は界磁喪失継電器			65	調速装置			89	断路器又は負荷開閉器		
	17	表示線継電器			42	界磁遮断器，スイッチ又は接触器			66	断続継電器			90	自動電圧調整器又は 自動電圧調整継電器		
	18	加速若しくは減速接触器又は 加速若しくは減速継電器			43	運転遮断器，スイッチ又は接触器			67	交流電力方向継電器又は 地絡方向継電器			91	自動電力調整器又は電力継電器		
	19	始動，運転切換接触器又は継電器			44	制御回路切換スイッチ， 接触器又は継電器			68	混入検出器			92	屏又はダンパ		
	20	補 機 弁			45	距離継電器			69	流量スイッチ又は継電器			93	（予備番号）		
5	21	主 機 弁			46	直流過電圧継電器			70	加減抵抗器			94	引外し自由接触器又は継電器		
	22	漏電遮断器，接触器又は継電器			47	逆相又は相不平衡電流継電器			71	整流素子故障検出装置			95	自動周波数調整器又は周波数継電器		
	23	温度調整装置又は継電器			48	欠相又は逆相電圧継電器			72	直流遮断器又は接触器			96	静止器内部故障検出装置		
	24	タップ切換装置			49	渋滞検出継電器			73	直流遮断器又は接触器			97	ラ ン ナ		
	25	同期検出装置				回転機温度スイッチ若しくは継電器 又は過負荷継電器				短絡用遮断器又は接触器			98	連結装置		
													99	自動記録装置		

Revisions	○			Date	Name	Fuji Electric Co.,Ltd.	Title	JEM 1090(1978) 制御器具番号表	Ref. Dwg. No.	W 4 2 6 2 9 7	003				
	○		Drawn		河野										
	○		Checked												
	○														
A		B		C		D		E		F		G		H	

A		B		C	D	E	F	G	H		
名称		図記号		備考	名称	図記号		備考	名称	図記号	備考
		a接点	b接点			a接点	b接点				
1	継電器接点又は 補助スイッチ接点			C接点の場合	手動操作自動 復帰接点 (ひねり形)				コンデンサ		
	手動復帰接点				端子				ヒューズ (包装形)		警報接点付
	L接点 (無遮断接点)			C接点の場合	継電器(一般)				ヒューズ (開放形)		
2	スイッチ残留接点				キープリレー コイル				ランプ		
	押しボタン スイッチ接点				遅延動作形 継電器 (オンディレイタイマー)				蛍光灯		JIS C 0303 より抜粋。
	引きボタン スイッチ接点				遅延復旧形 継電器 (オフディレイタイマー)				電源用 コンセント		3極 接地極付 3P E
3	接点(一般)又は 手動接点				遅延動作・遅延 復旧形継電器 (オンオフディレイタイマー)				プラグ ジャック		
	電磁接触器接点				整流器				ブザー		
	機械的接点			リミットスイッチのように 接点の開閉が電氣的以外の 原因により行われるもの。	ダイオード				ベル		
4	限時動作接点 (オンディレイタイマー)				バリスタ				切り換え スイッチ	COS	
	限時復帰接点 (オフディレイタイマー)				サイリスタ				押しボタン スイッチ	PBS	
	限時動作・ 限時復帰接点 (オンオフディレイタイマー)				抵抗器			スペースヒータ含む。			
5											
Revisions		Date		Name	Fuji Electric Co., Ltd.		Title		Ref. Dwg. No.		
○		Drawn		河野			図記号一覧表(1/2)		W426297		004
○		Checked					JIS C 0301(1982)		STENKA13		
○											
○											

A			B			C			D			E			F			G			H								
名称			図記号			備考			名称			図記号			備考			名称			図記号			備考					
C B									試験用 電流端子									光コード及び プラグアダプタ											
気中遮断器（一般）						1. 配線用遮断器（MCB） も含む。 2. 図は2極の場合			機器又は装置																				
ナイフスイッチ						図は2極の場合			熱電対						極性は省略しても可														
断路器									変換装置 （一般）						交流／直流														
負荷開閉器															直流／直流														
避雷器									導線																				
変圧器（一般）									導線分岐																				
計器用変圧器									接地																				
変流器									同軸ケーブル						シールドのある場合は、 下記の様に表す。														
零相変流器																													
計器用切換 開閉器 電圧，電流									ケーブル						シールド線の場合は、下図の 様に表す。														
試験用 電圧端子									パラレル通信路						必要によっては、心線（情報線）数 を下図の様に記入する。														
Revisions			○			Date			Name			Fuji Electric Co., Ltd.			Title			図記号一覧表（2/2）			Ref. Dwg. No.			W426297			005		
			○			Drawn			河野																				
			○			Checked																							
			○																										
A			B			C			D			E			F			G			H								

A

B

C

D

E

F

G

H

1

No.

本PJ
対象

本図番
変更記号

取 り 合 い 先

取 り 合 い 先 情 報

備 考

0 1

O

Q

展開接続図

MWA401002

9

メタウォーター

-

-

-

O

分電盤完了

0 2

0 3

0 4

0 5

0 6

0 7

0 8

0 9

1 0

1 1

1 2

1 3

1 4

1 5

1 6

1 7

自家発設備

-

-

-

-

1 8

無停電電源装置

-

-

-

-

1 9

直流電源装置

-

-

-

-

2 0

機械資料

-

-

-

-

2 1

計装機器資料

-

-

-

-

本ページには原図通則の管理対象外とする。

➡ 本図番の変更がなくても取り合いを確認したら変更記号を記入・更新する。

本ページには変更記号を付けない。取り合い確認で本ページのみ修正した場合は発行しない。

Revisions

)
)
)
)

Date
Name

Drawn
Checked

2023-12-07
2023-12-07

春成／阿多
丹
舟木

メタウォーター株式会社
METAWATER Co., Ltd.

Title

取り付け図面一覧表

Dwg.No.
Ref.

W426297
CW00_06a

009

A

B

C


D

E

F

G


H

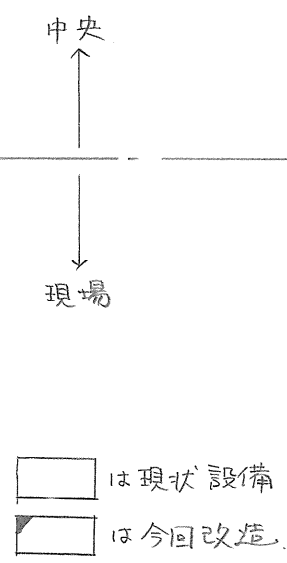


☐ は現状設備


☒ は今回改造

Revisions			Date	Name	メタウォーター株式会社 METAWATER Co., Ltd.	Title	場外系集中監視制御装置	Ref.	Dwg.No.	W426297	022 -1	B
		Drawn	2007-1-30	河野								
		Checked										
	⑧ 本頁追加	2007-1-30	河野									
A	B	▲	C	◇	△	E	F	G	H			

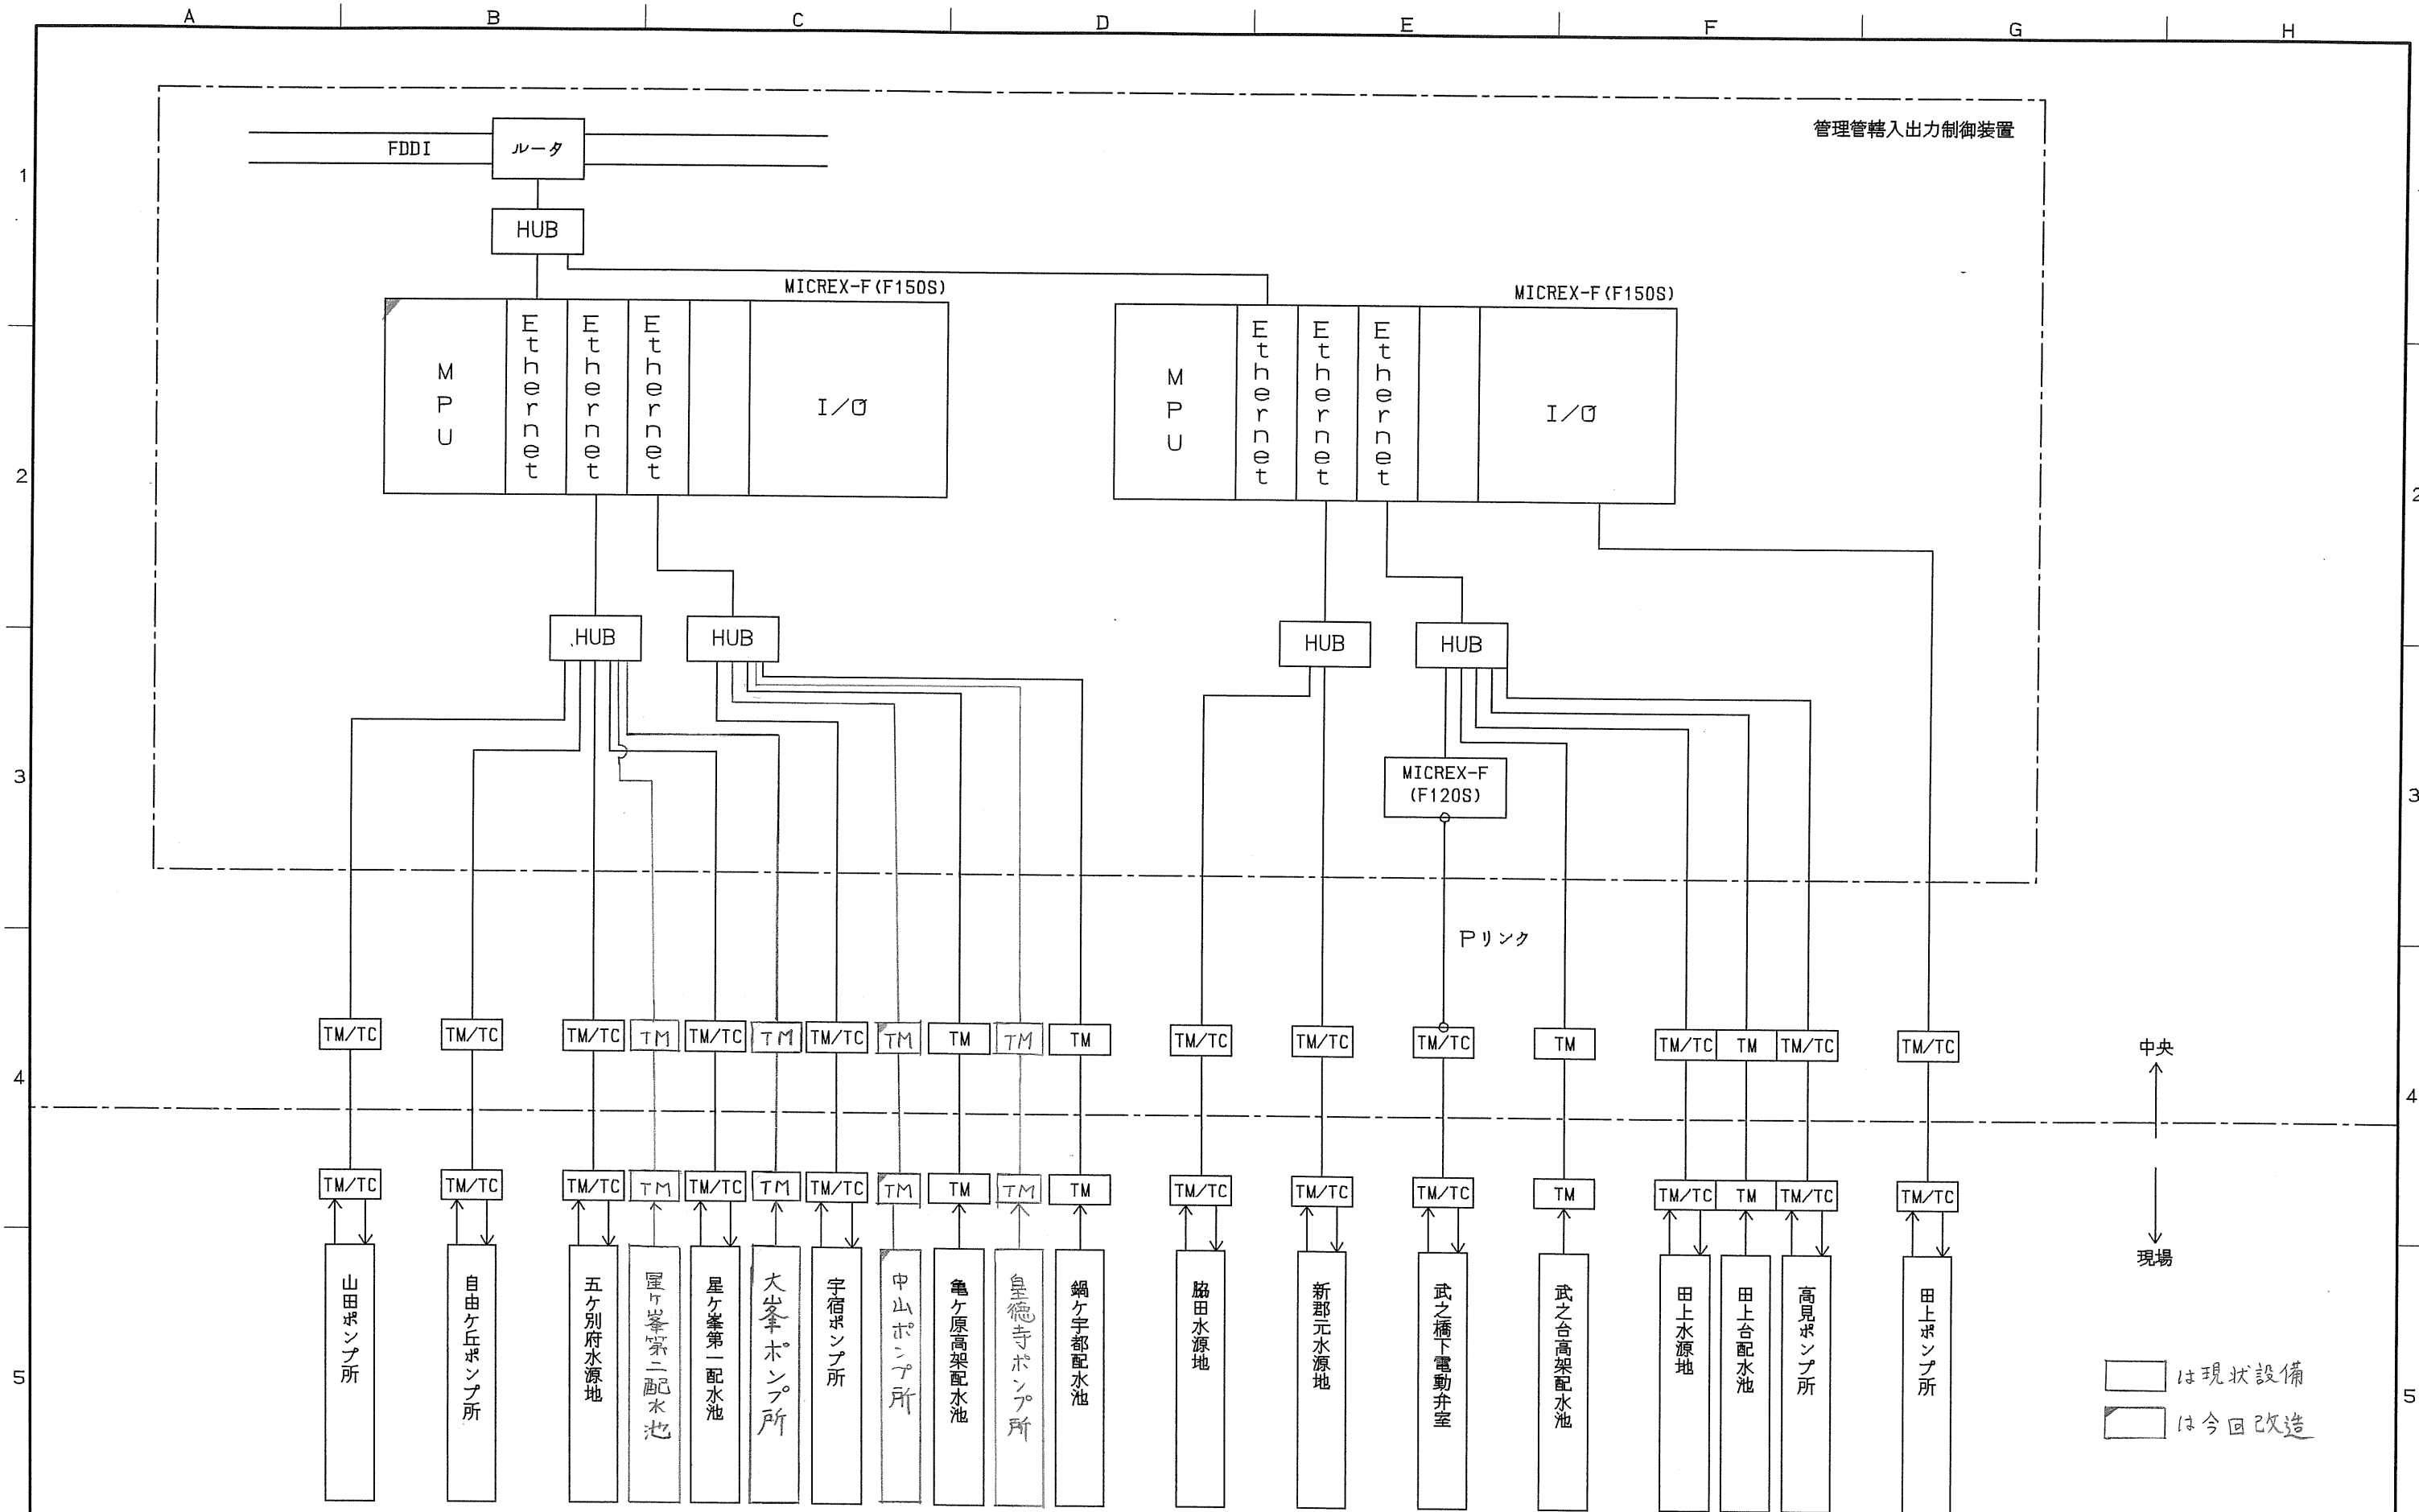
[illegible]

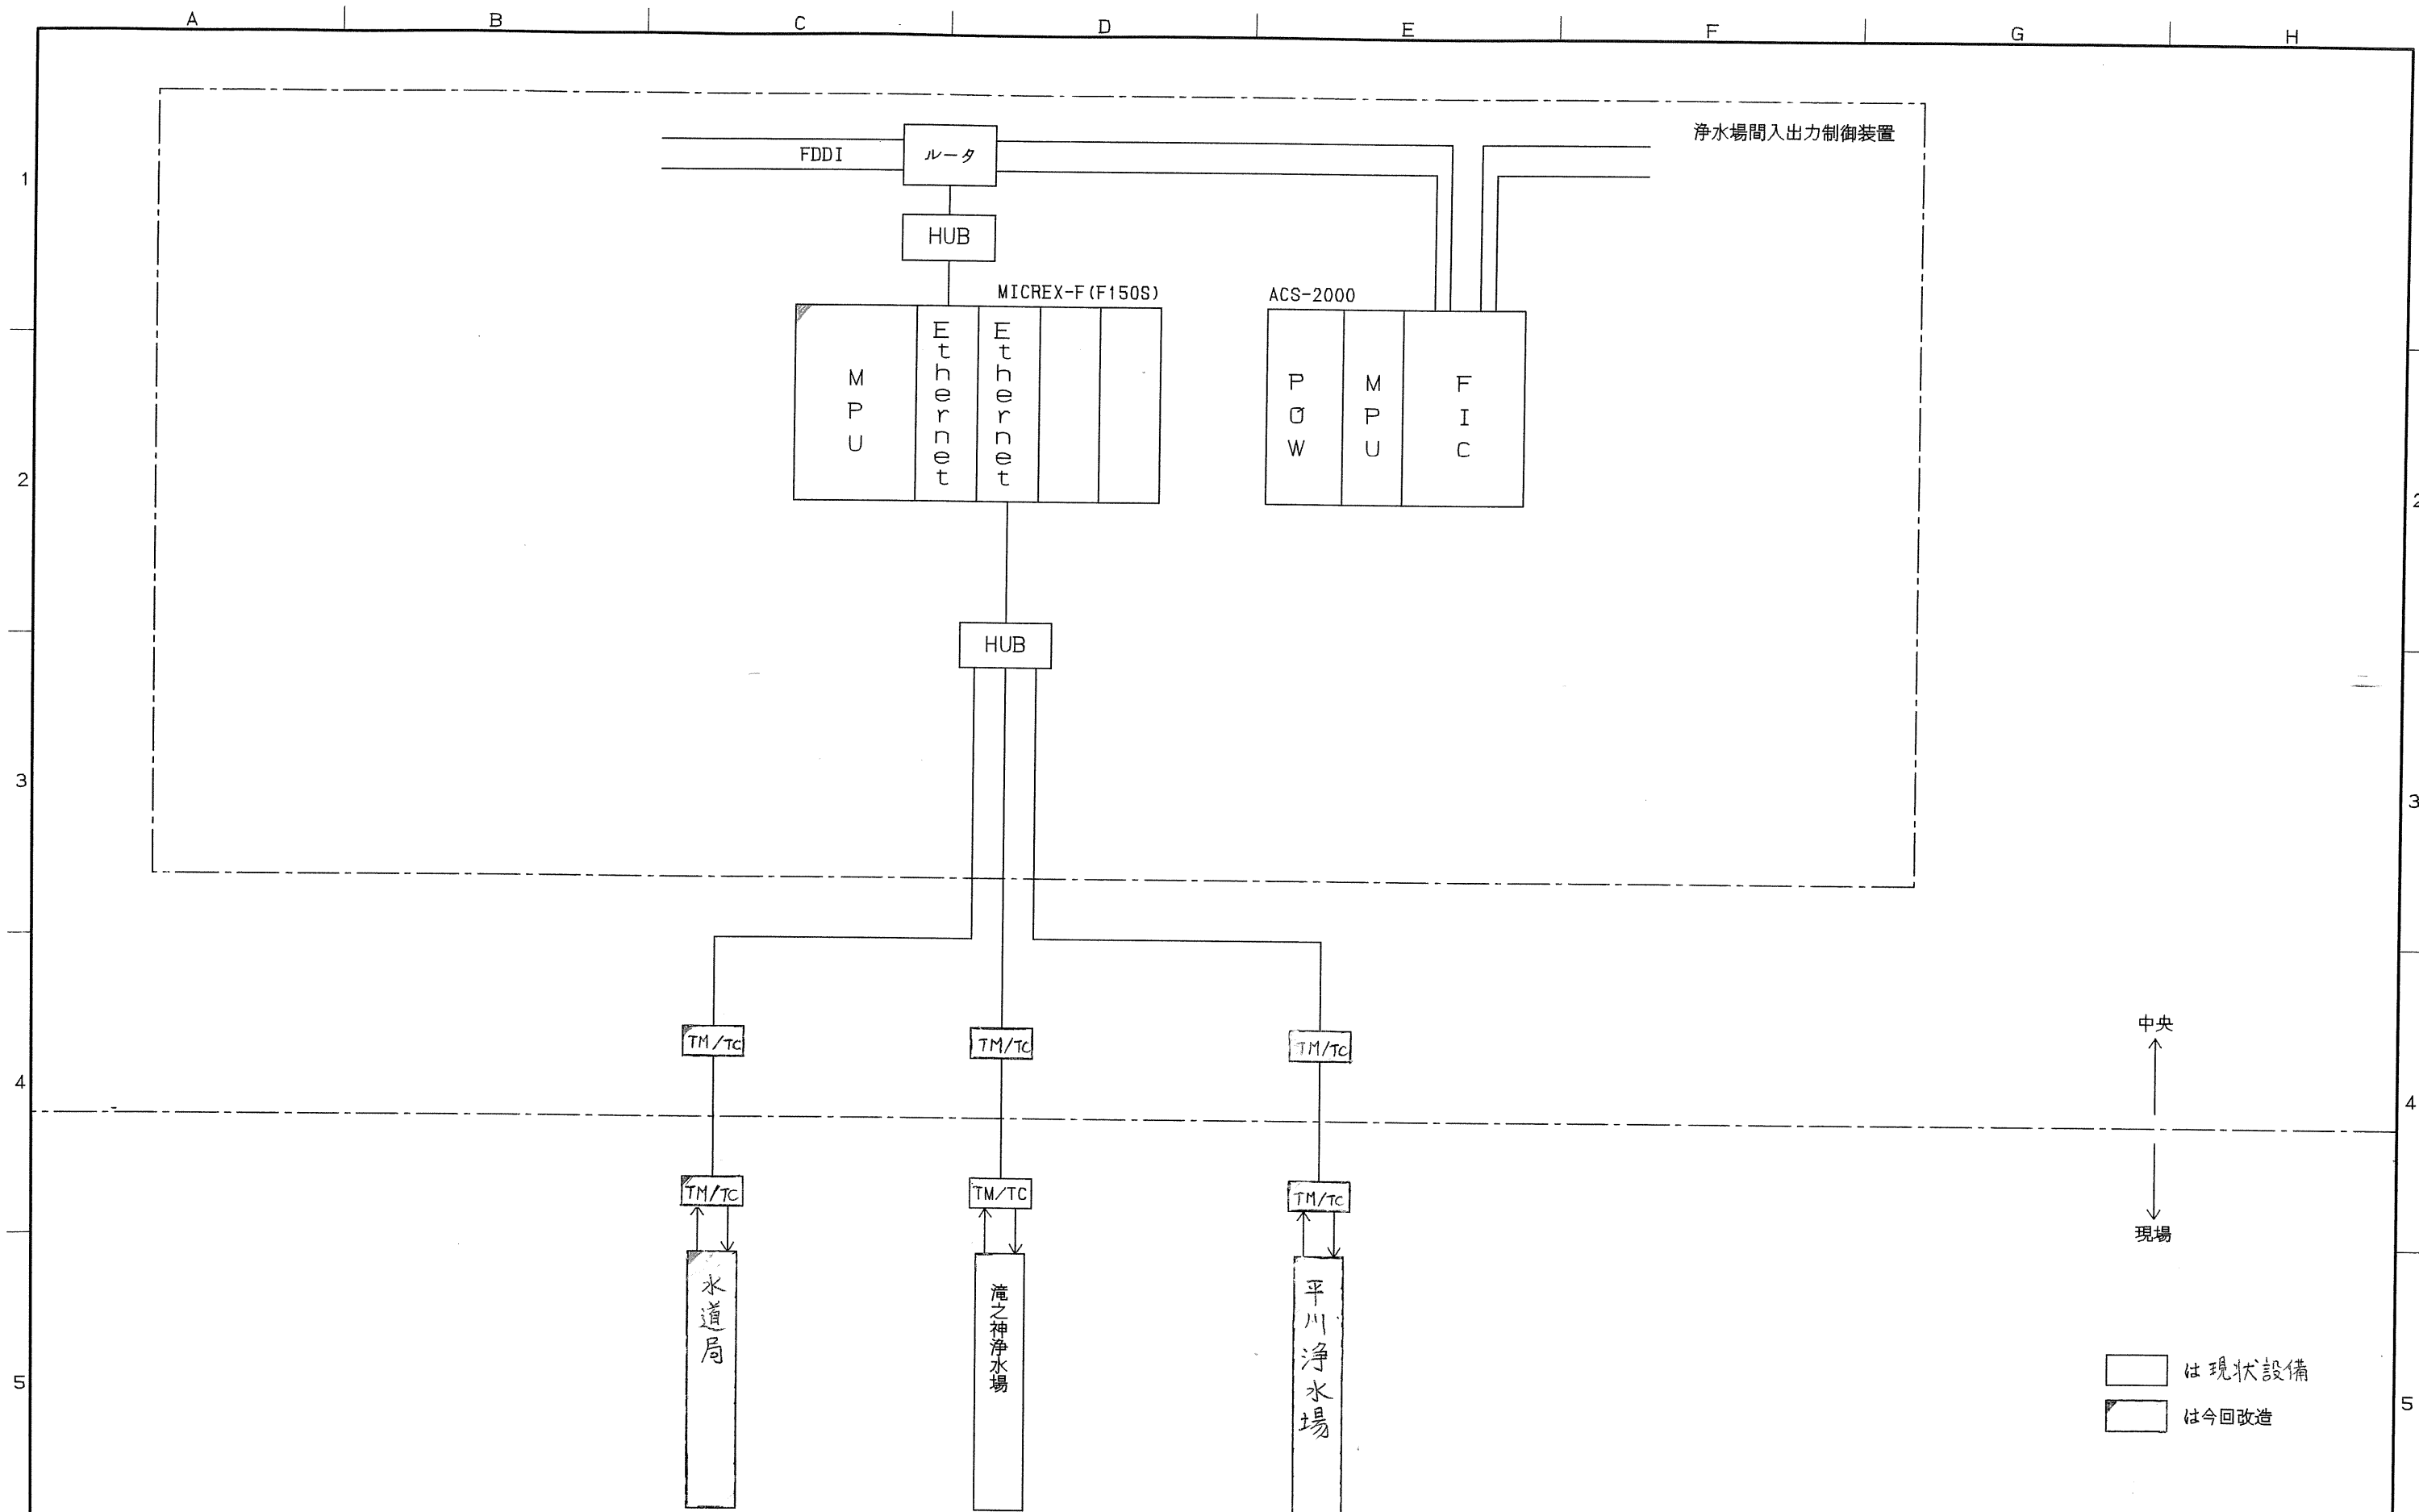



Revisions	③「今回改造」を「現状設備」に変更	'05-11-07	大城	Date	Name	Fuji Electric Co., Ltd.	Title 場外系集中監視制御設備 システム構成（４／４）	Ref. Dwg. No. W426297	024			
	㊦ ACS追加	'01-03-21	折茂	Drawn	河野							
	㊧ 本頁全面書換	'00-09-20	折茂	Checked								
	㊨ 書換原図	'00-06-08	河野									

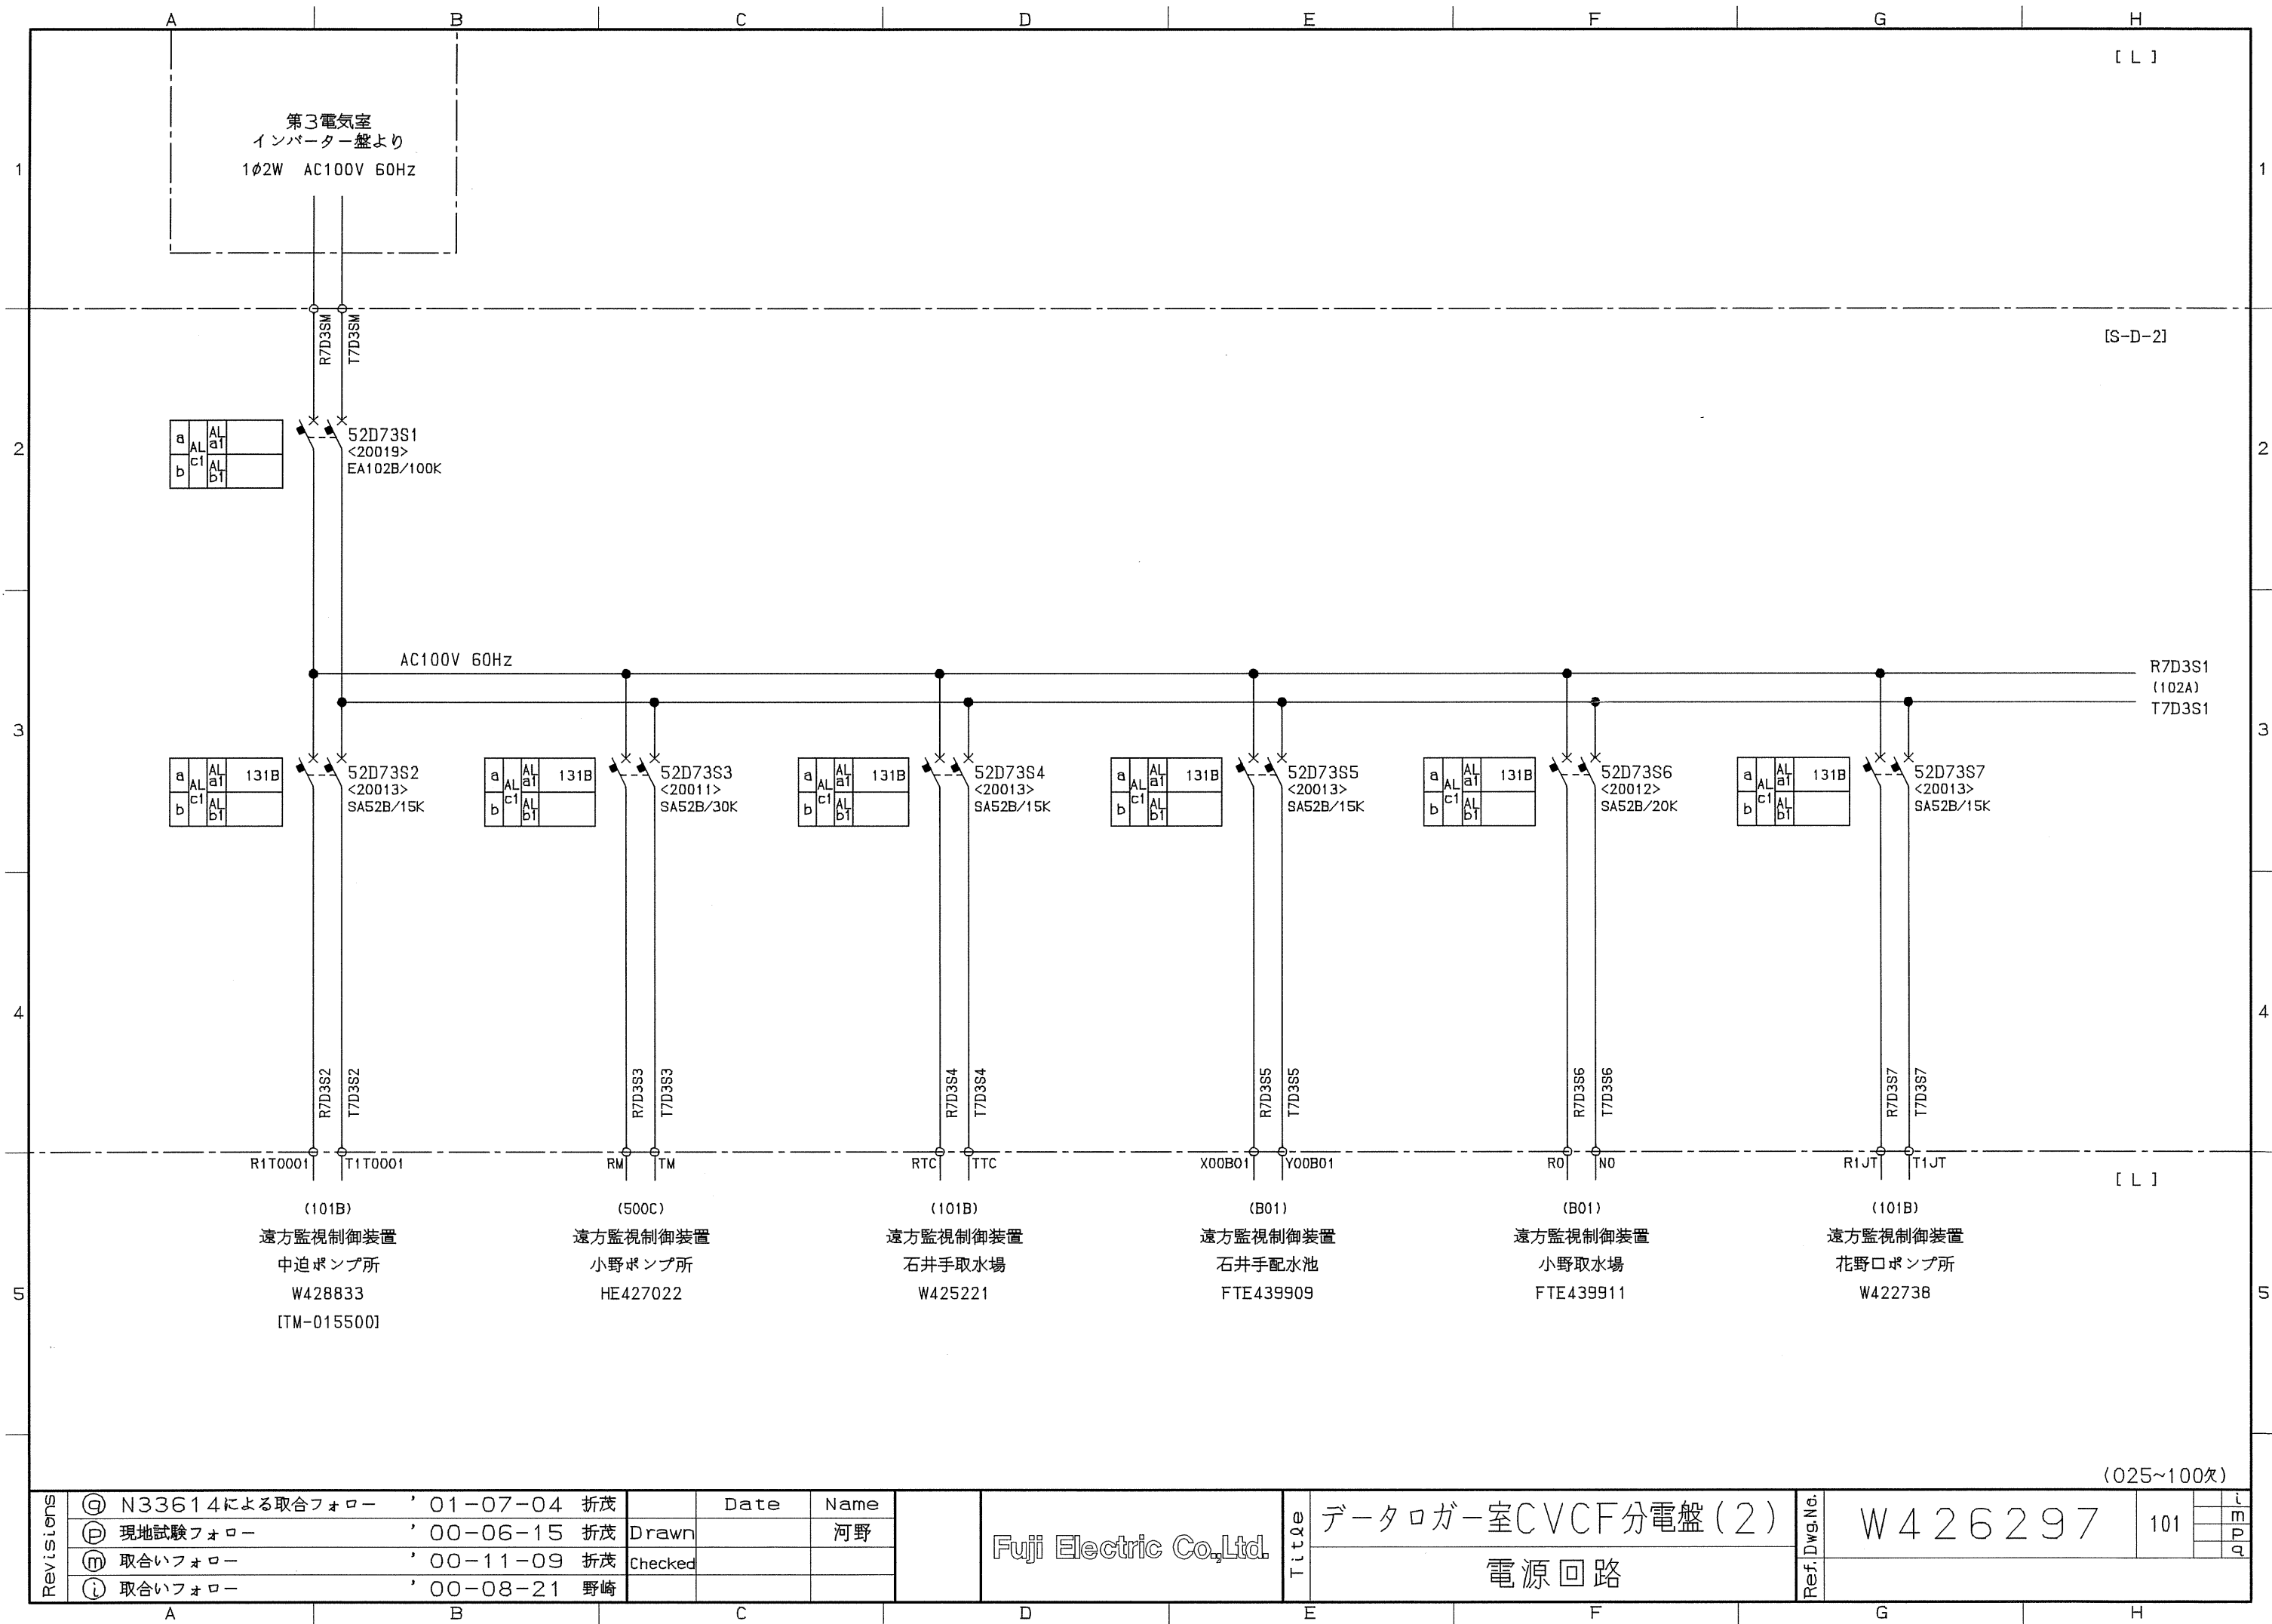



Revisions	①	N33614による取合フォロー	' 01-07-04	折茂		Date	Name	Fuji Electric Co., Ltd.	Title データロガー室CVCF分電盤(2) 電源回路	Ref. Dwg. No. W426297	101	i
	②	現地試験フォロー	' 00-06-15	折茂	Drawn		河野					m
	③	取合いフォロー	' 00-11-09	折茂	Checked							p
	④	取合いフォロー	' 00-08-21	野崎								q

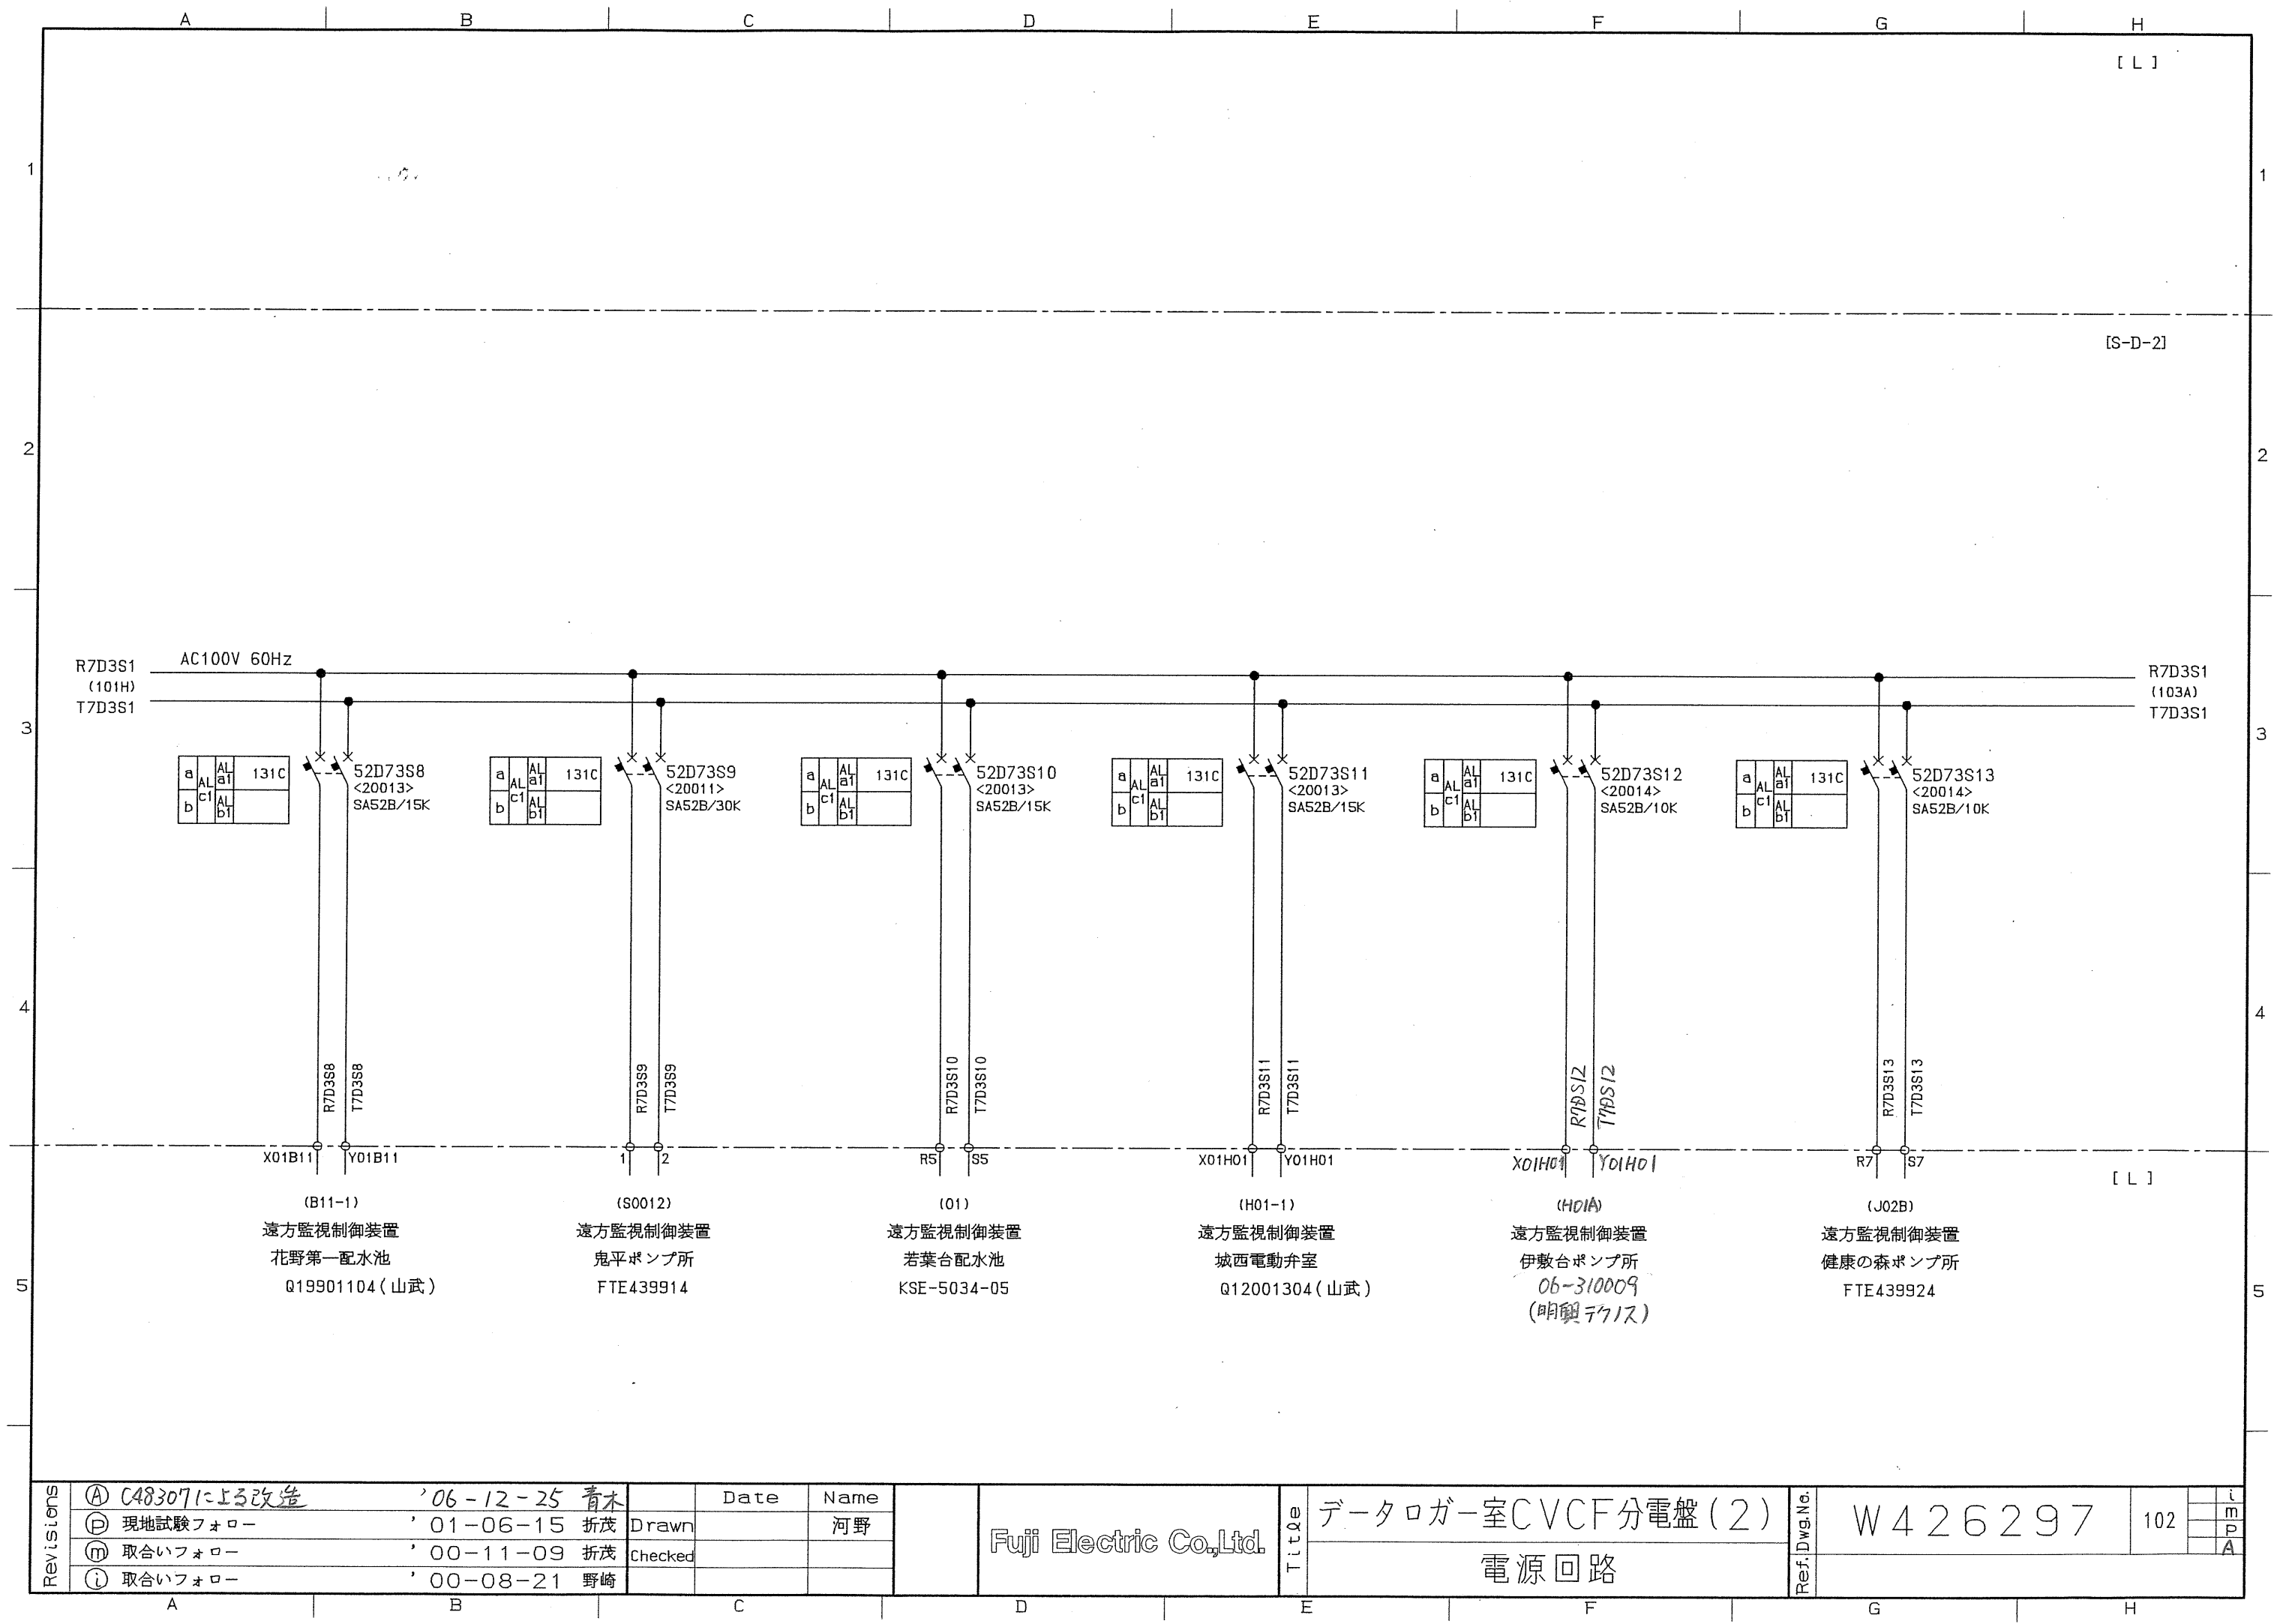


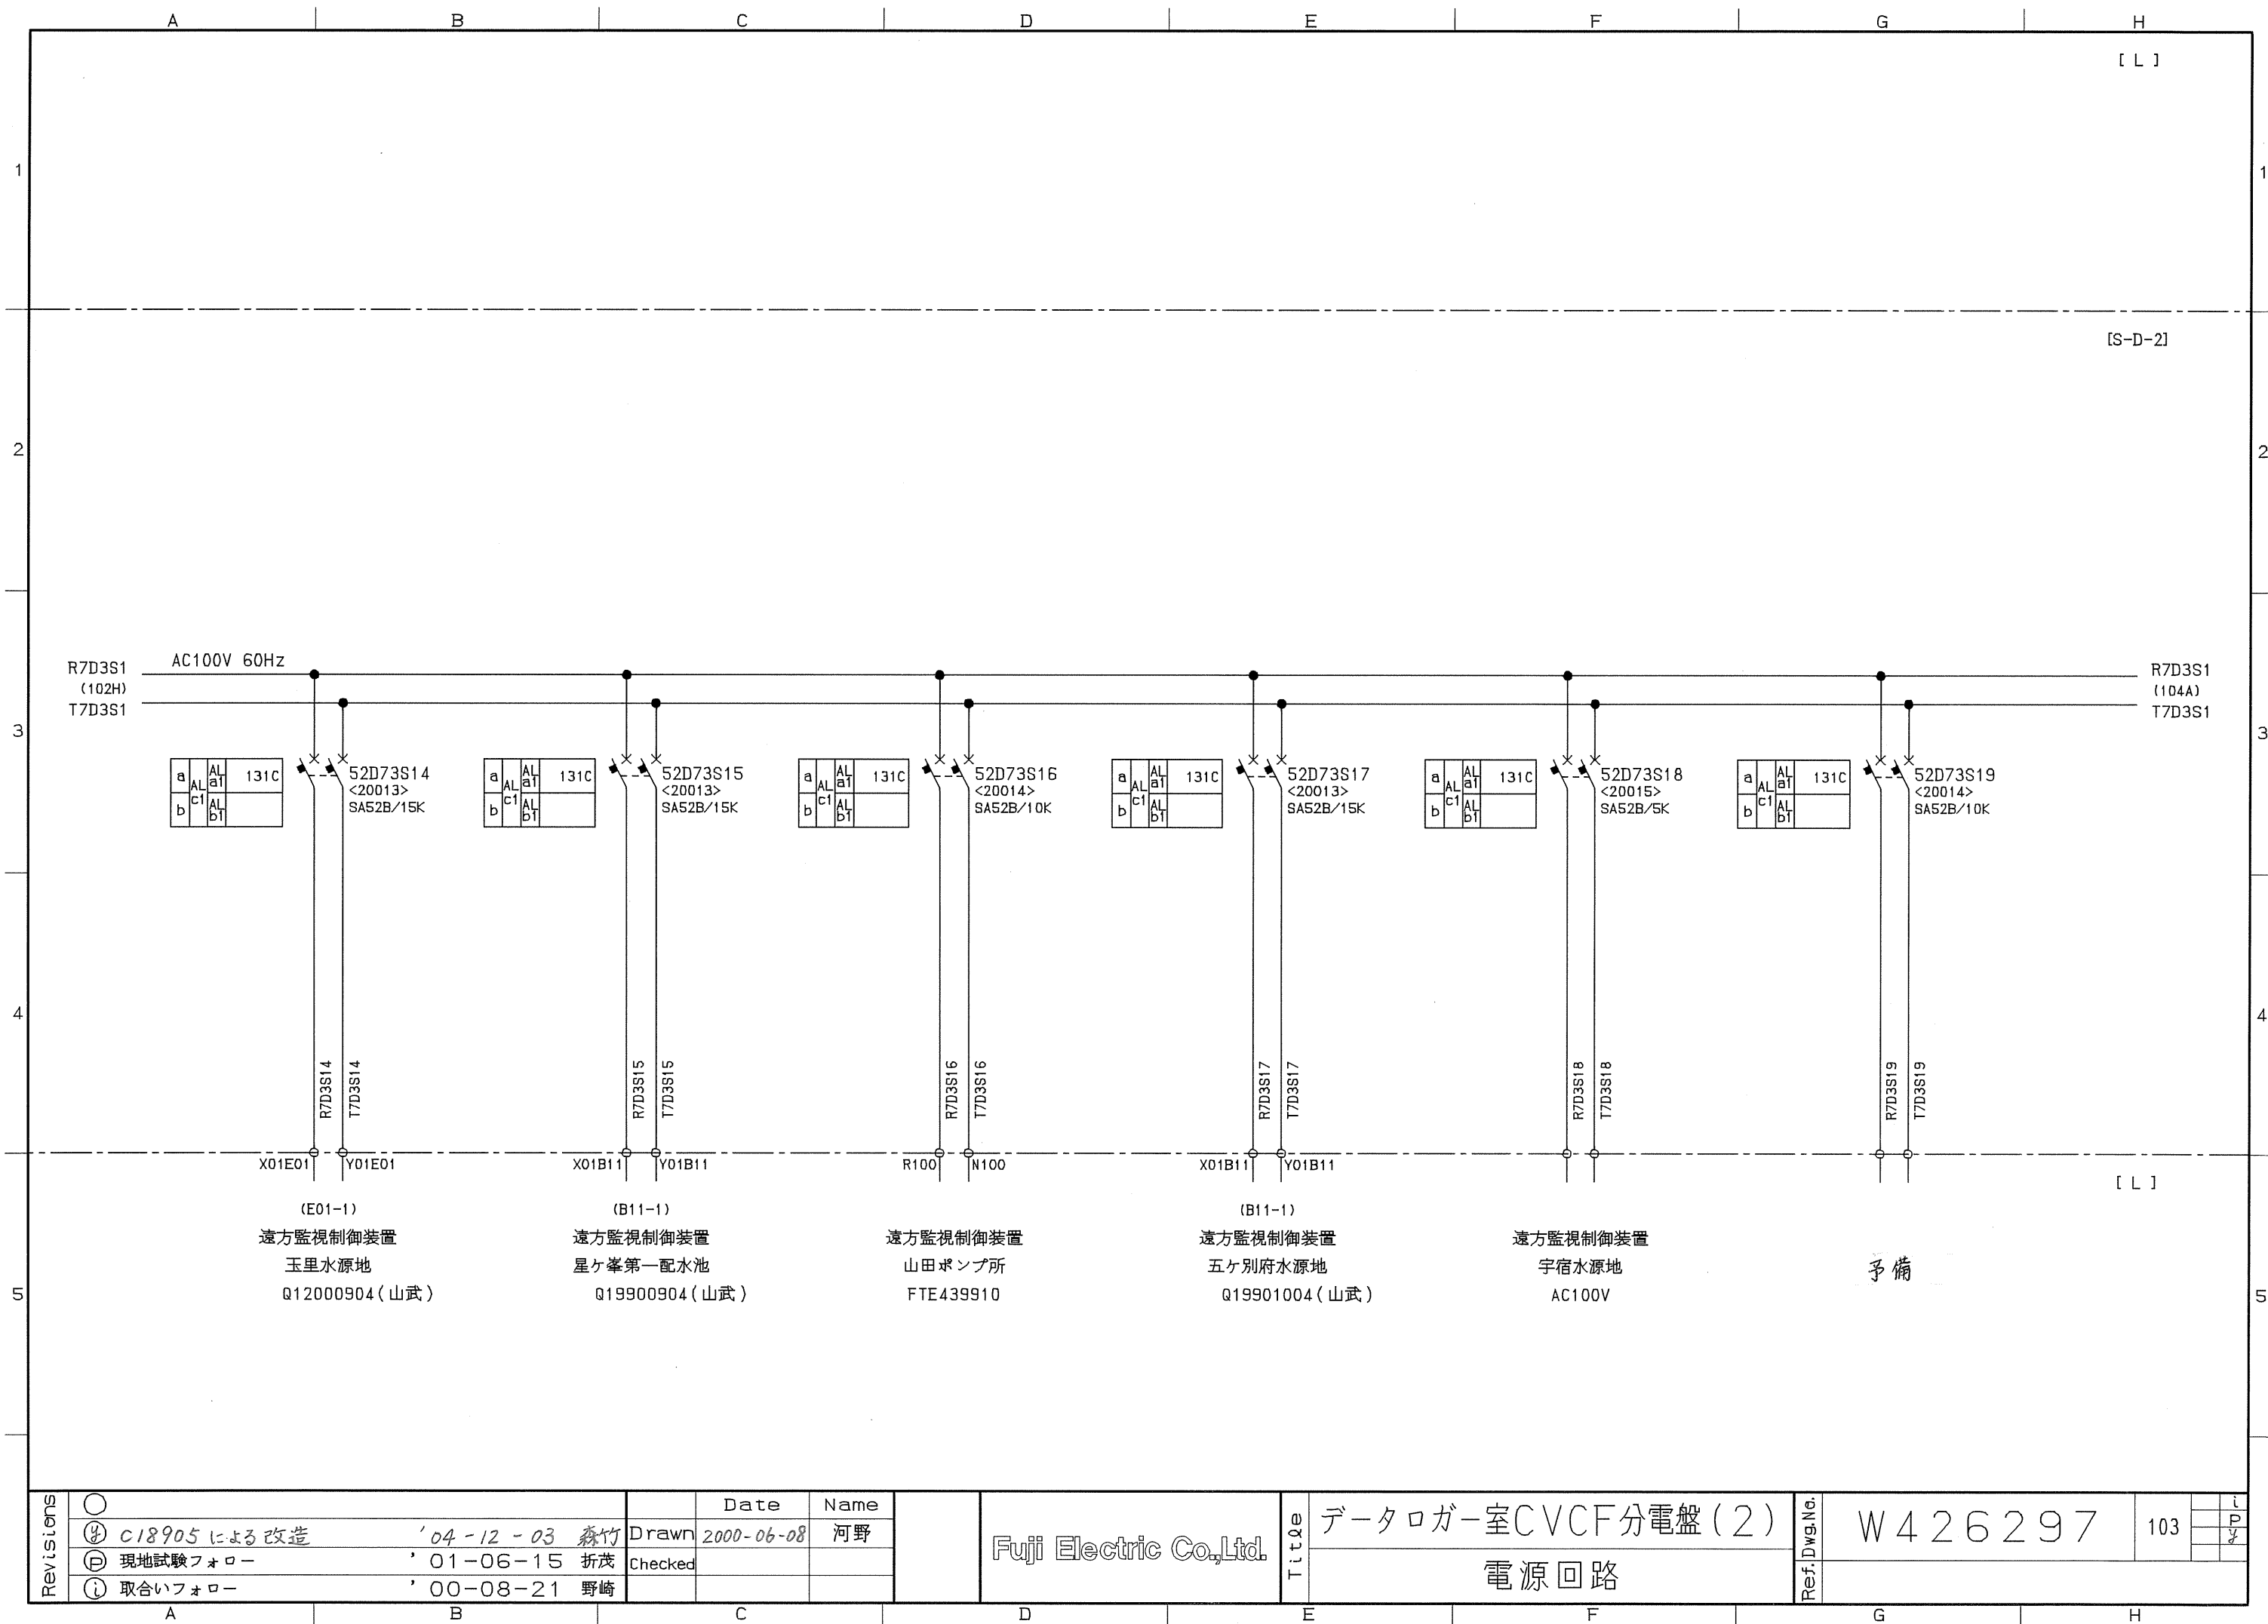


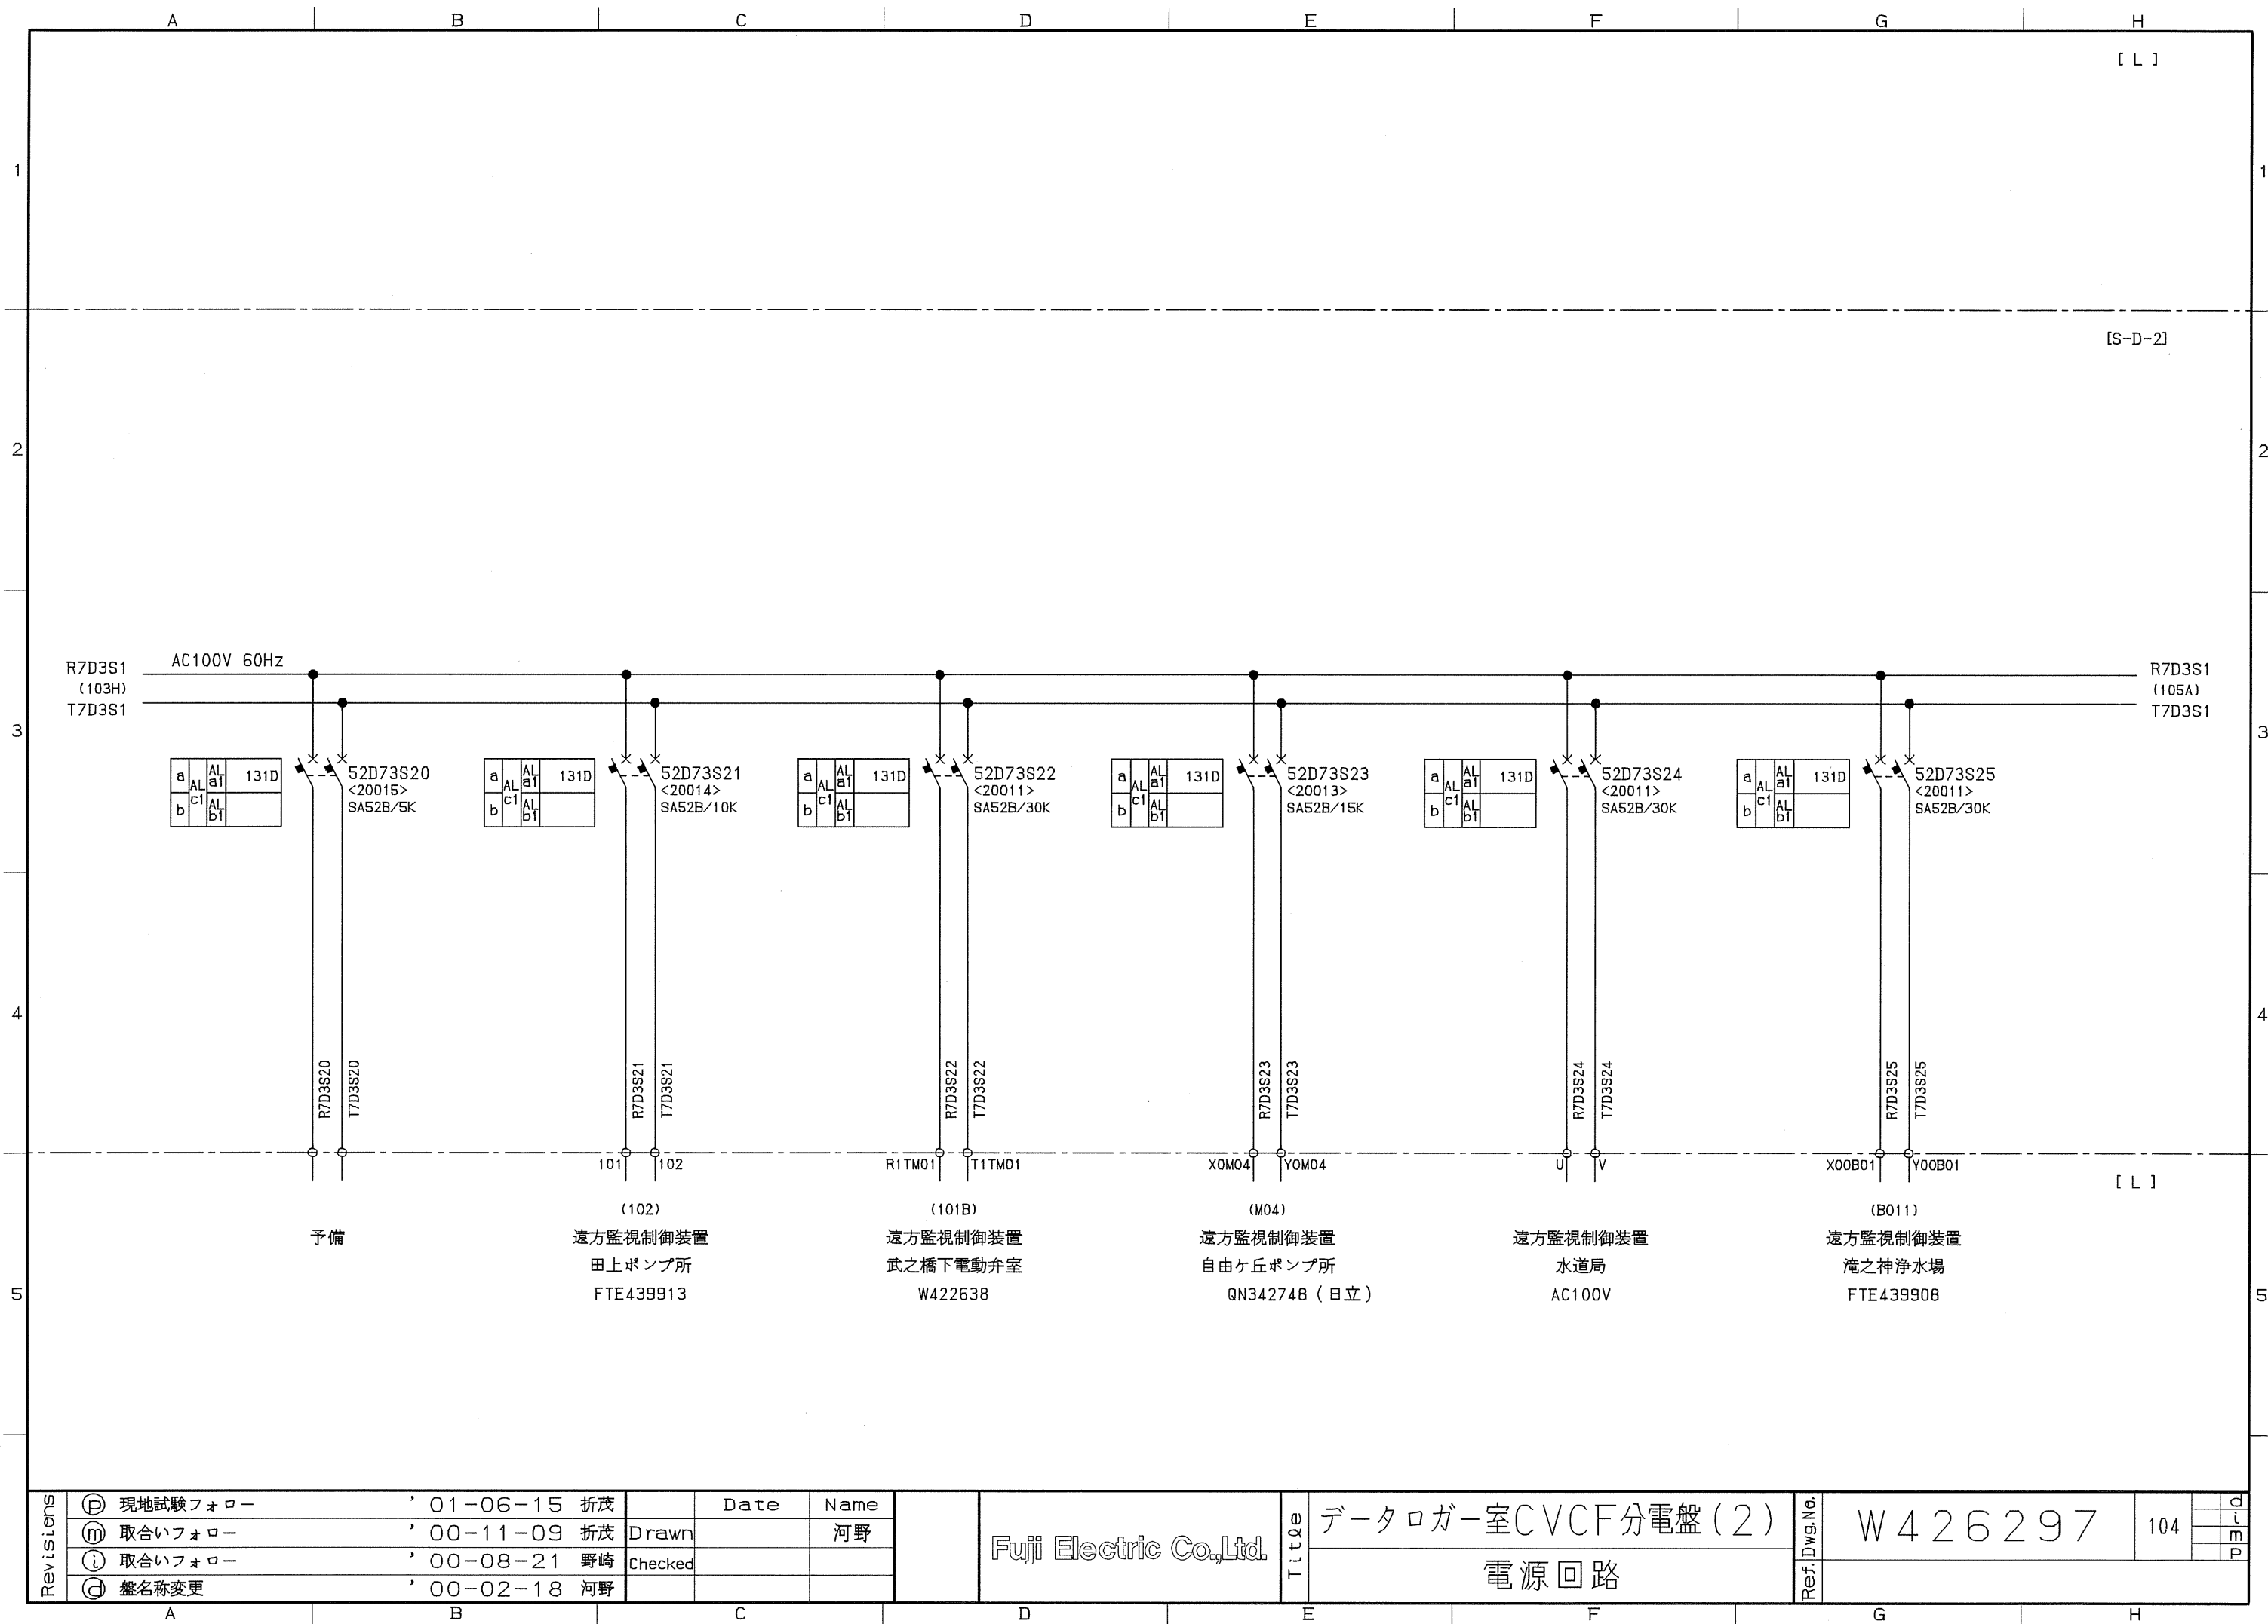


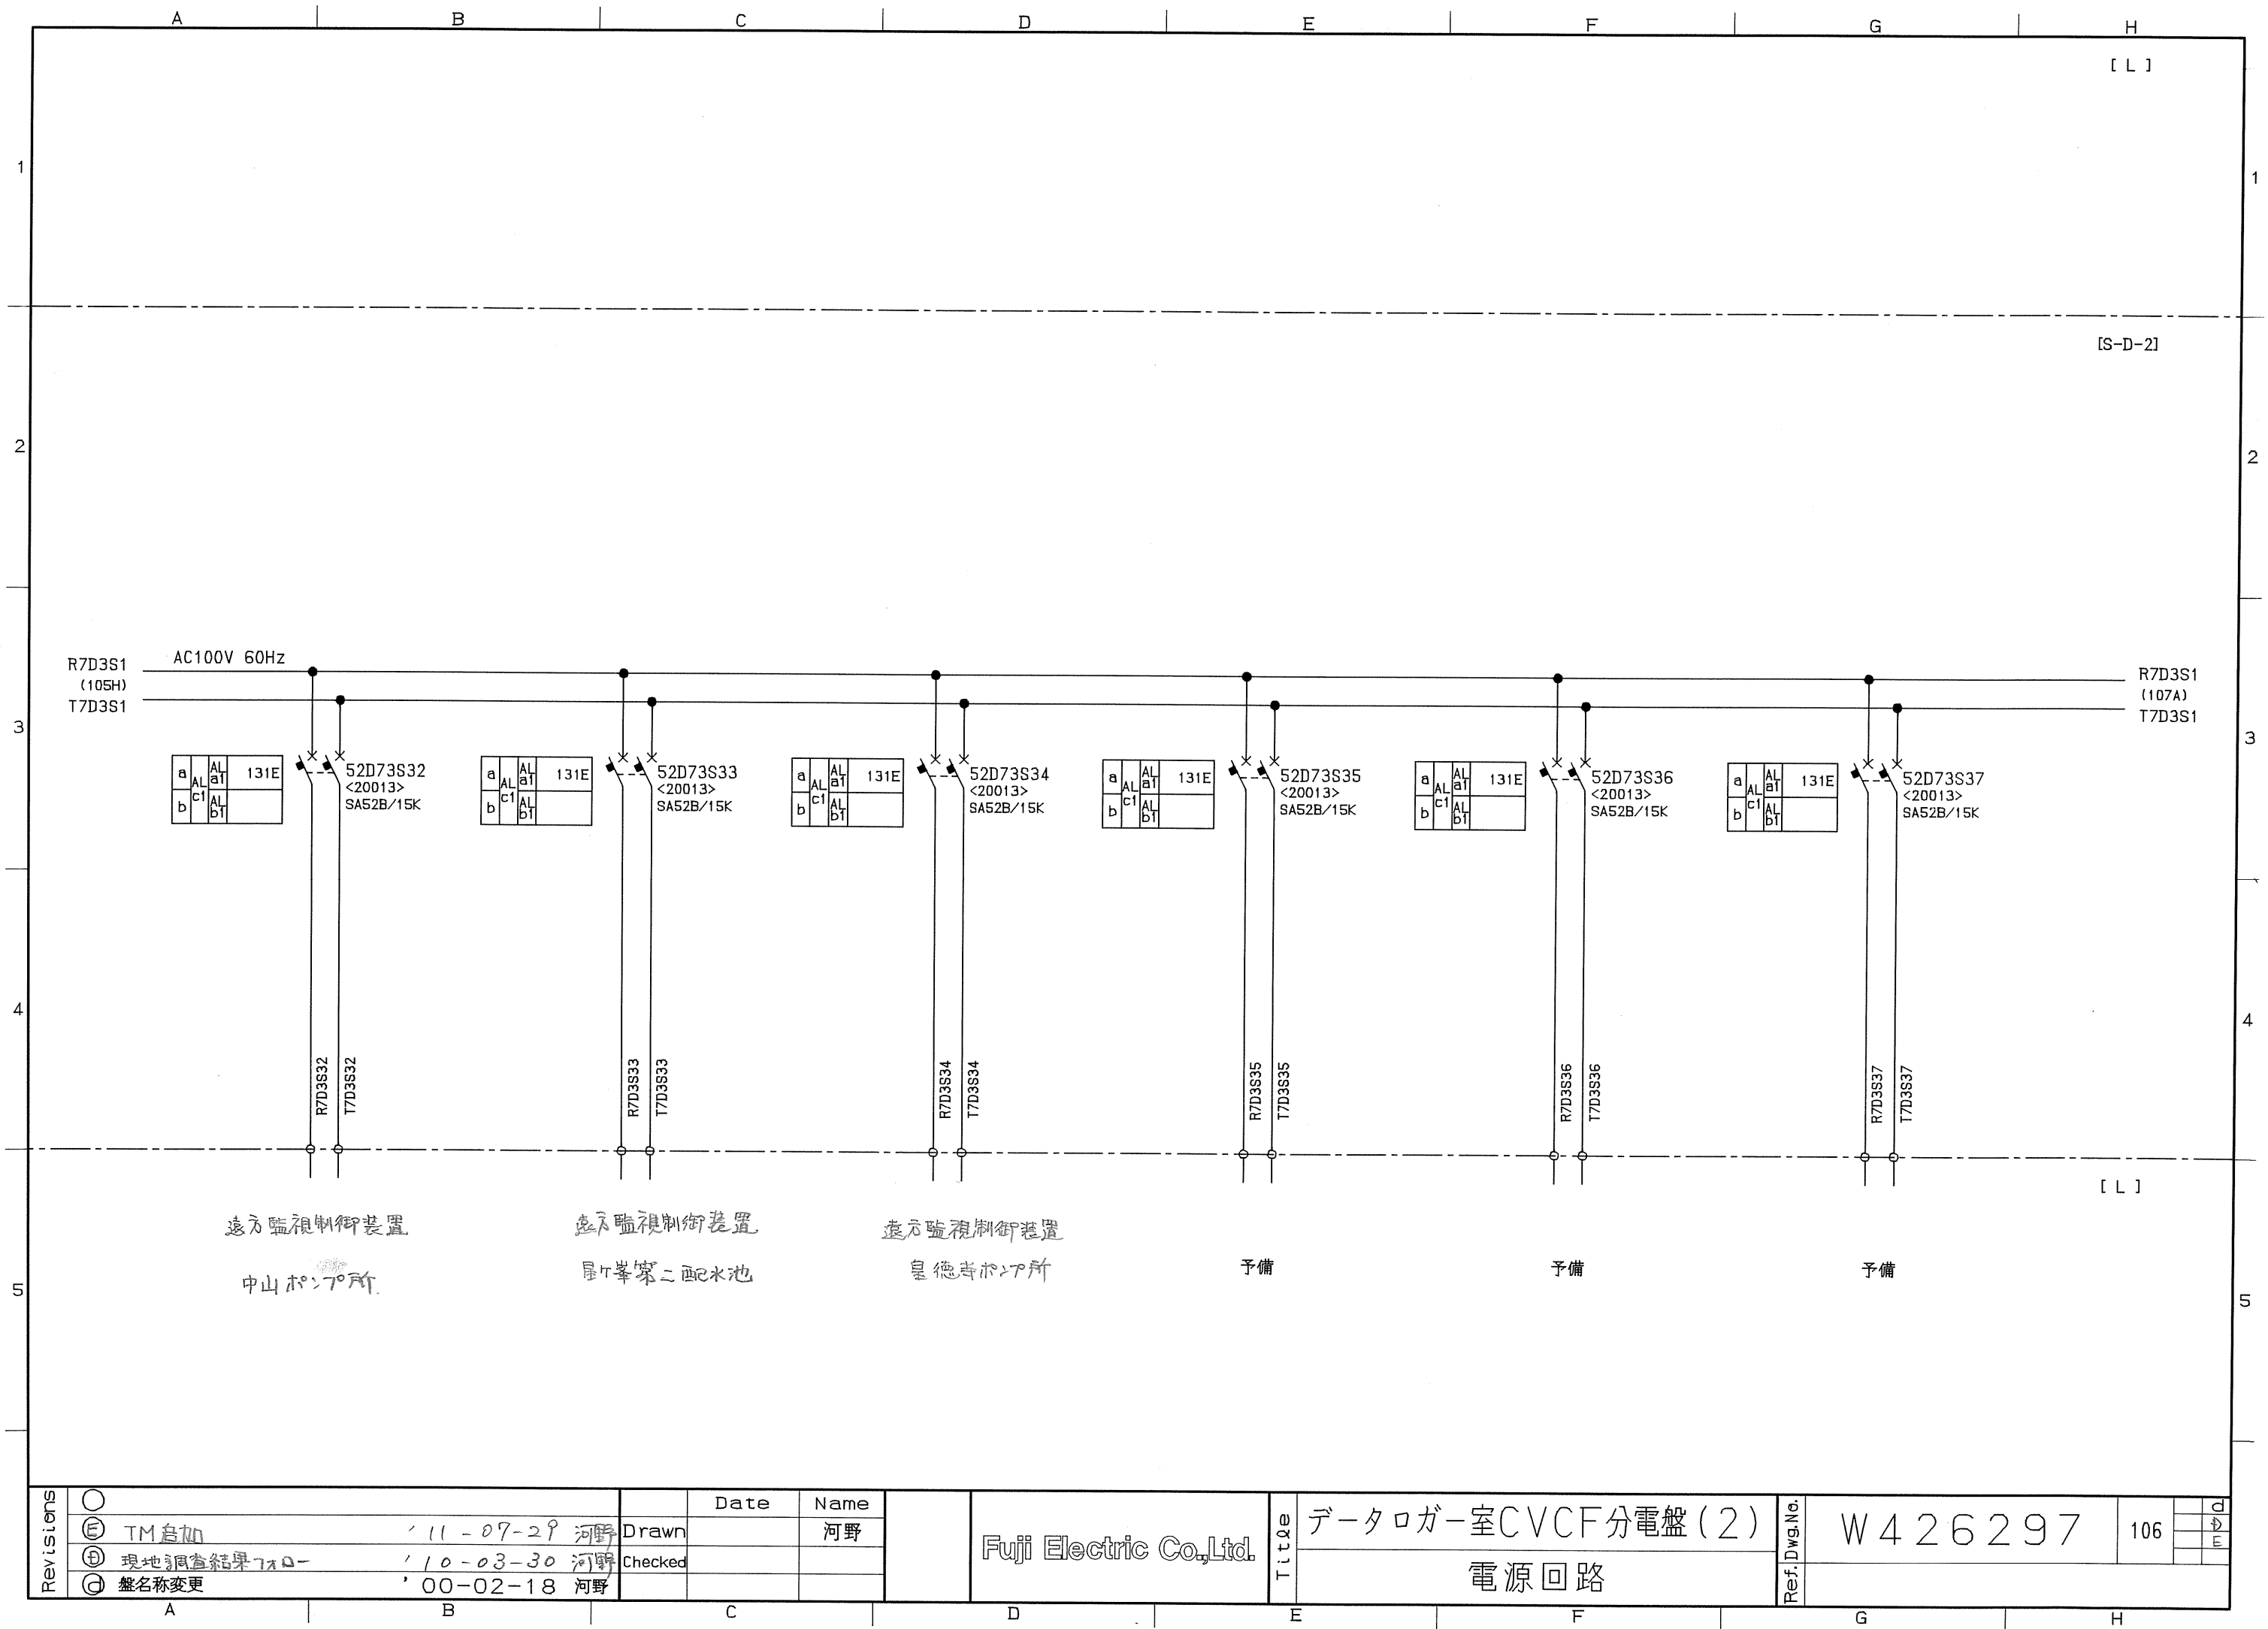

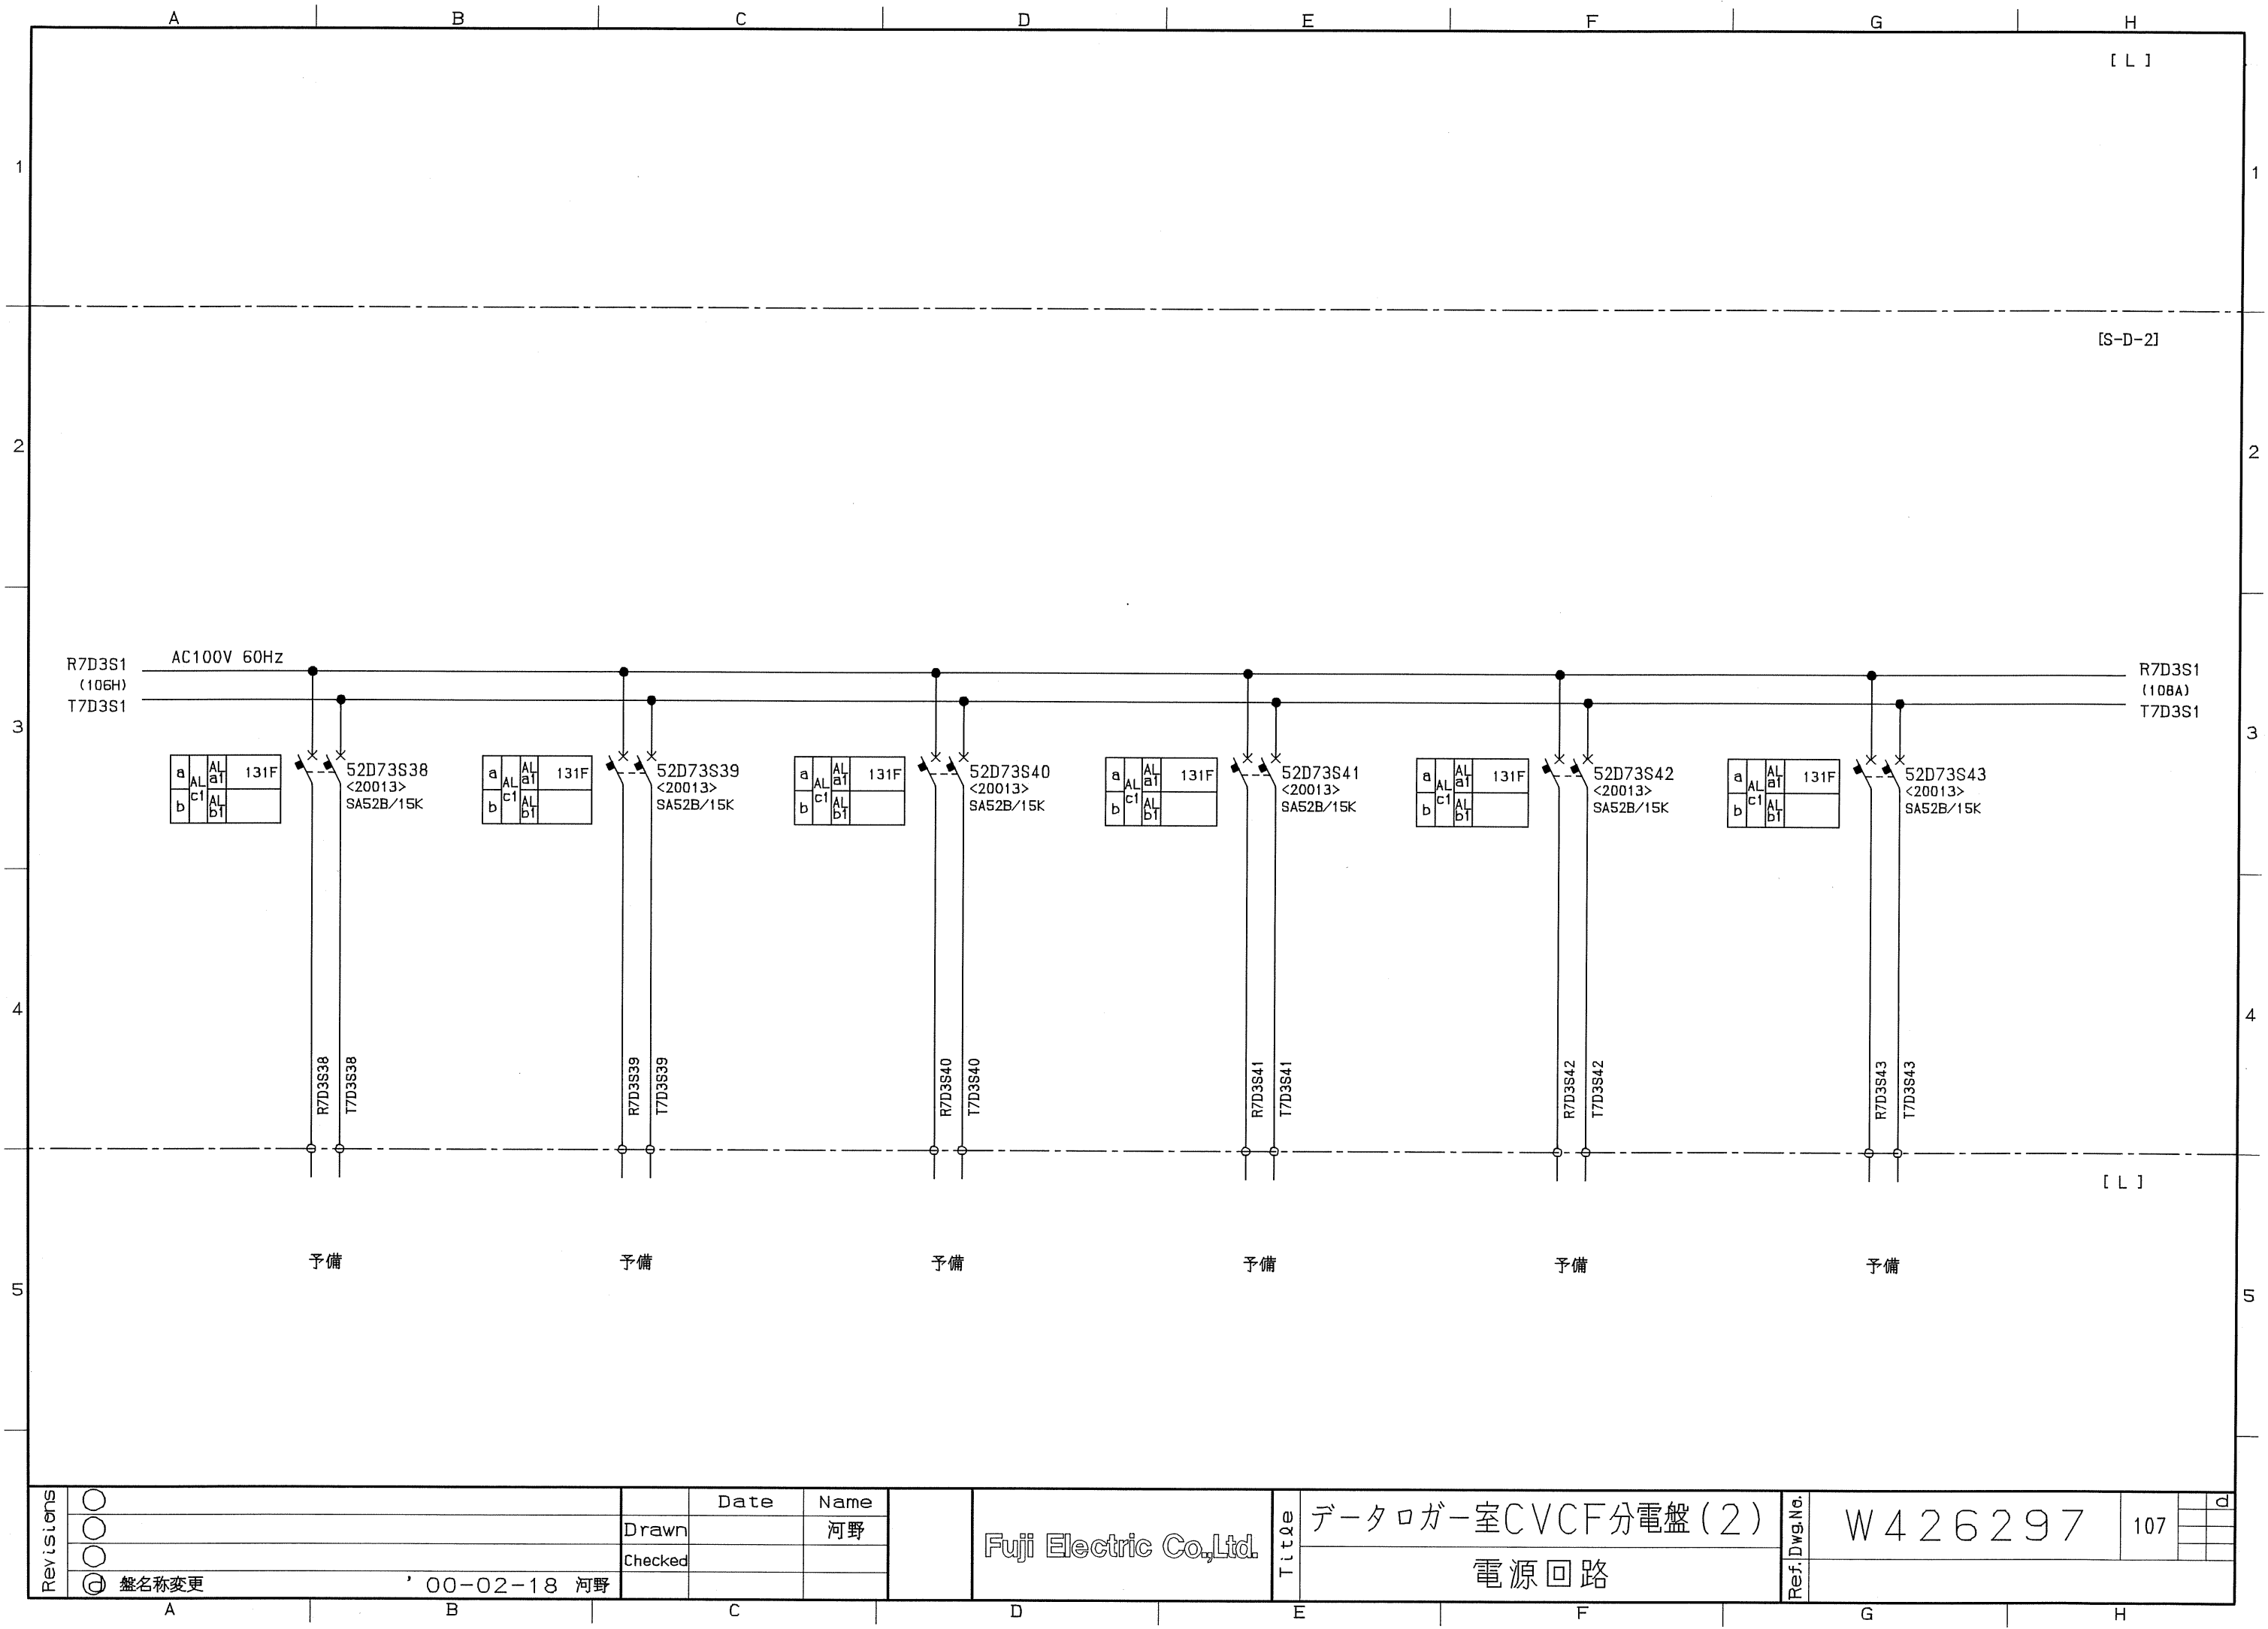


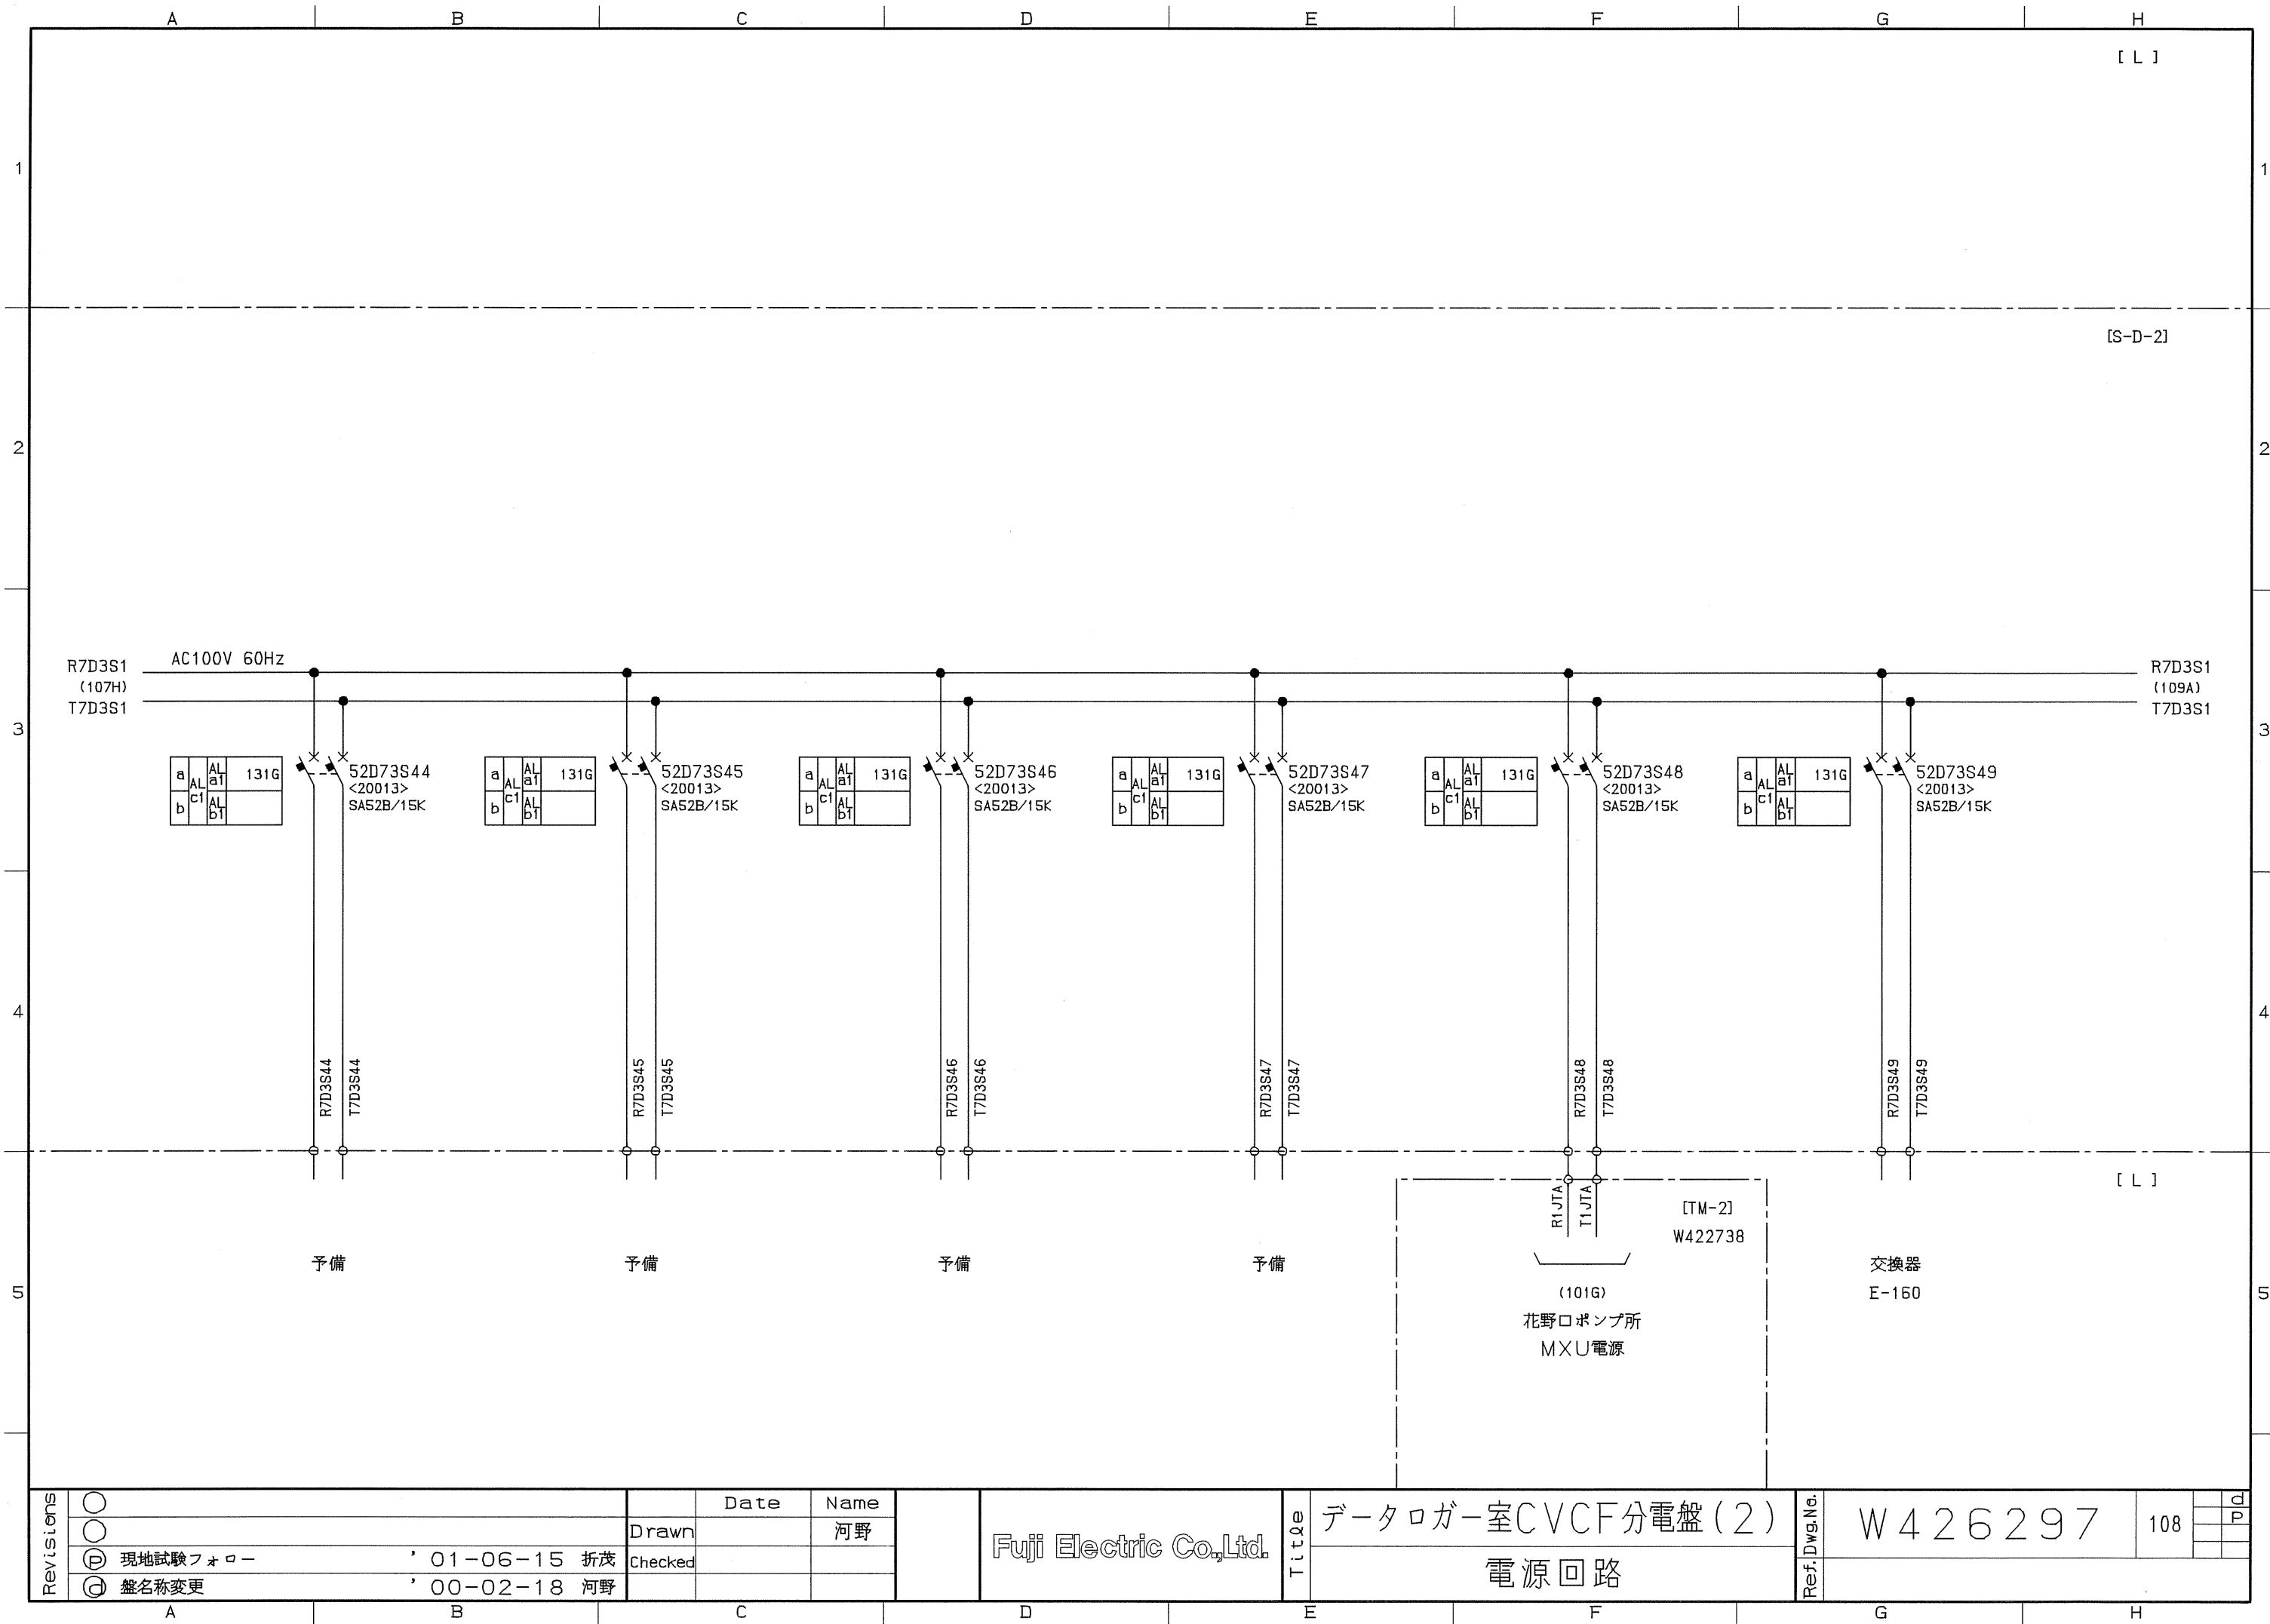


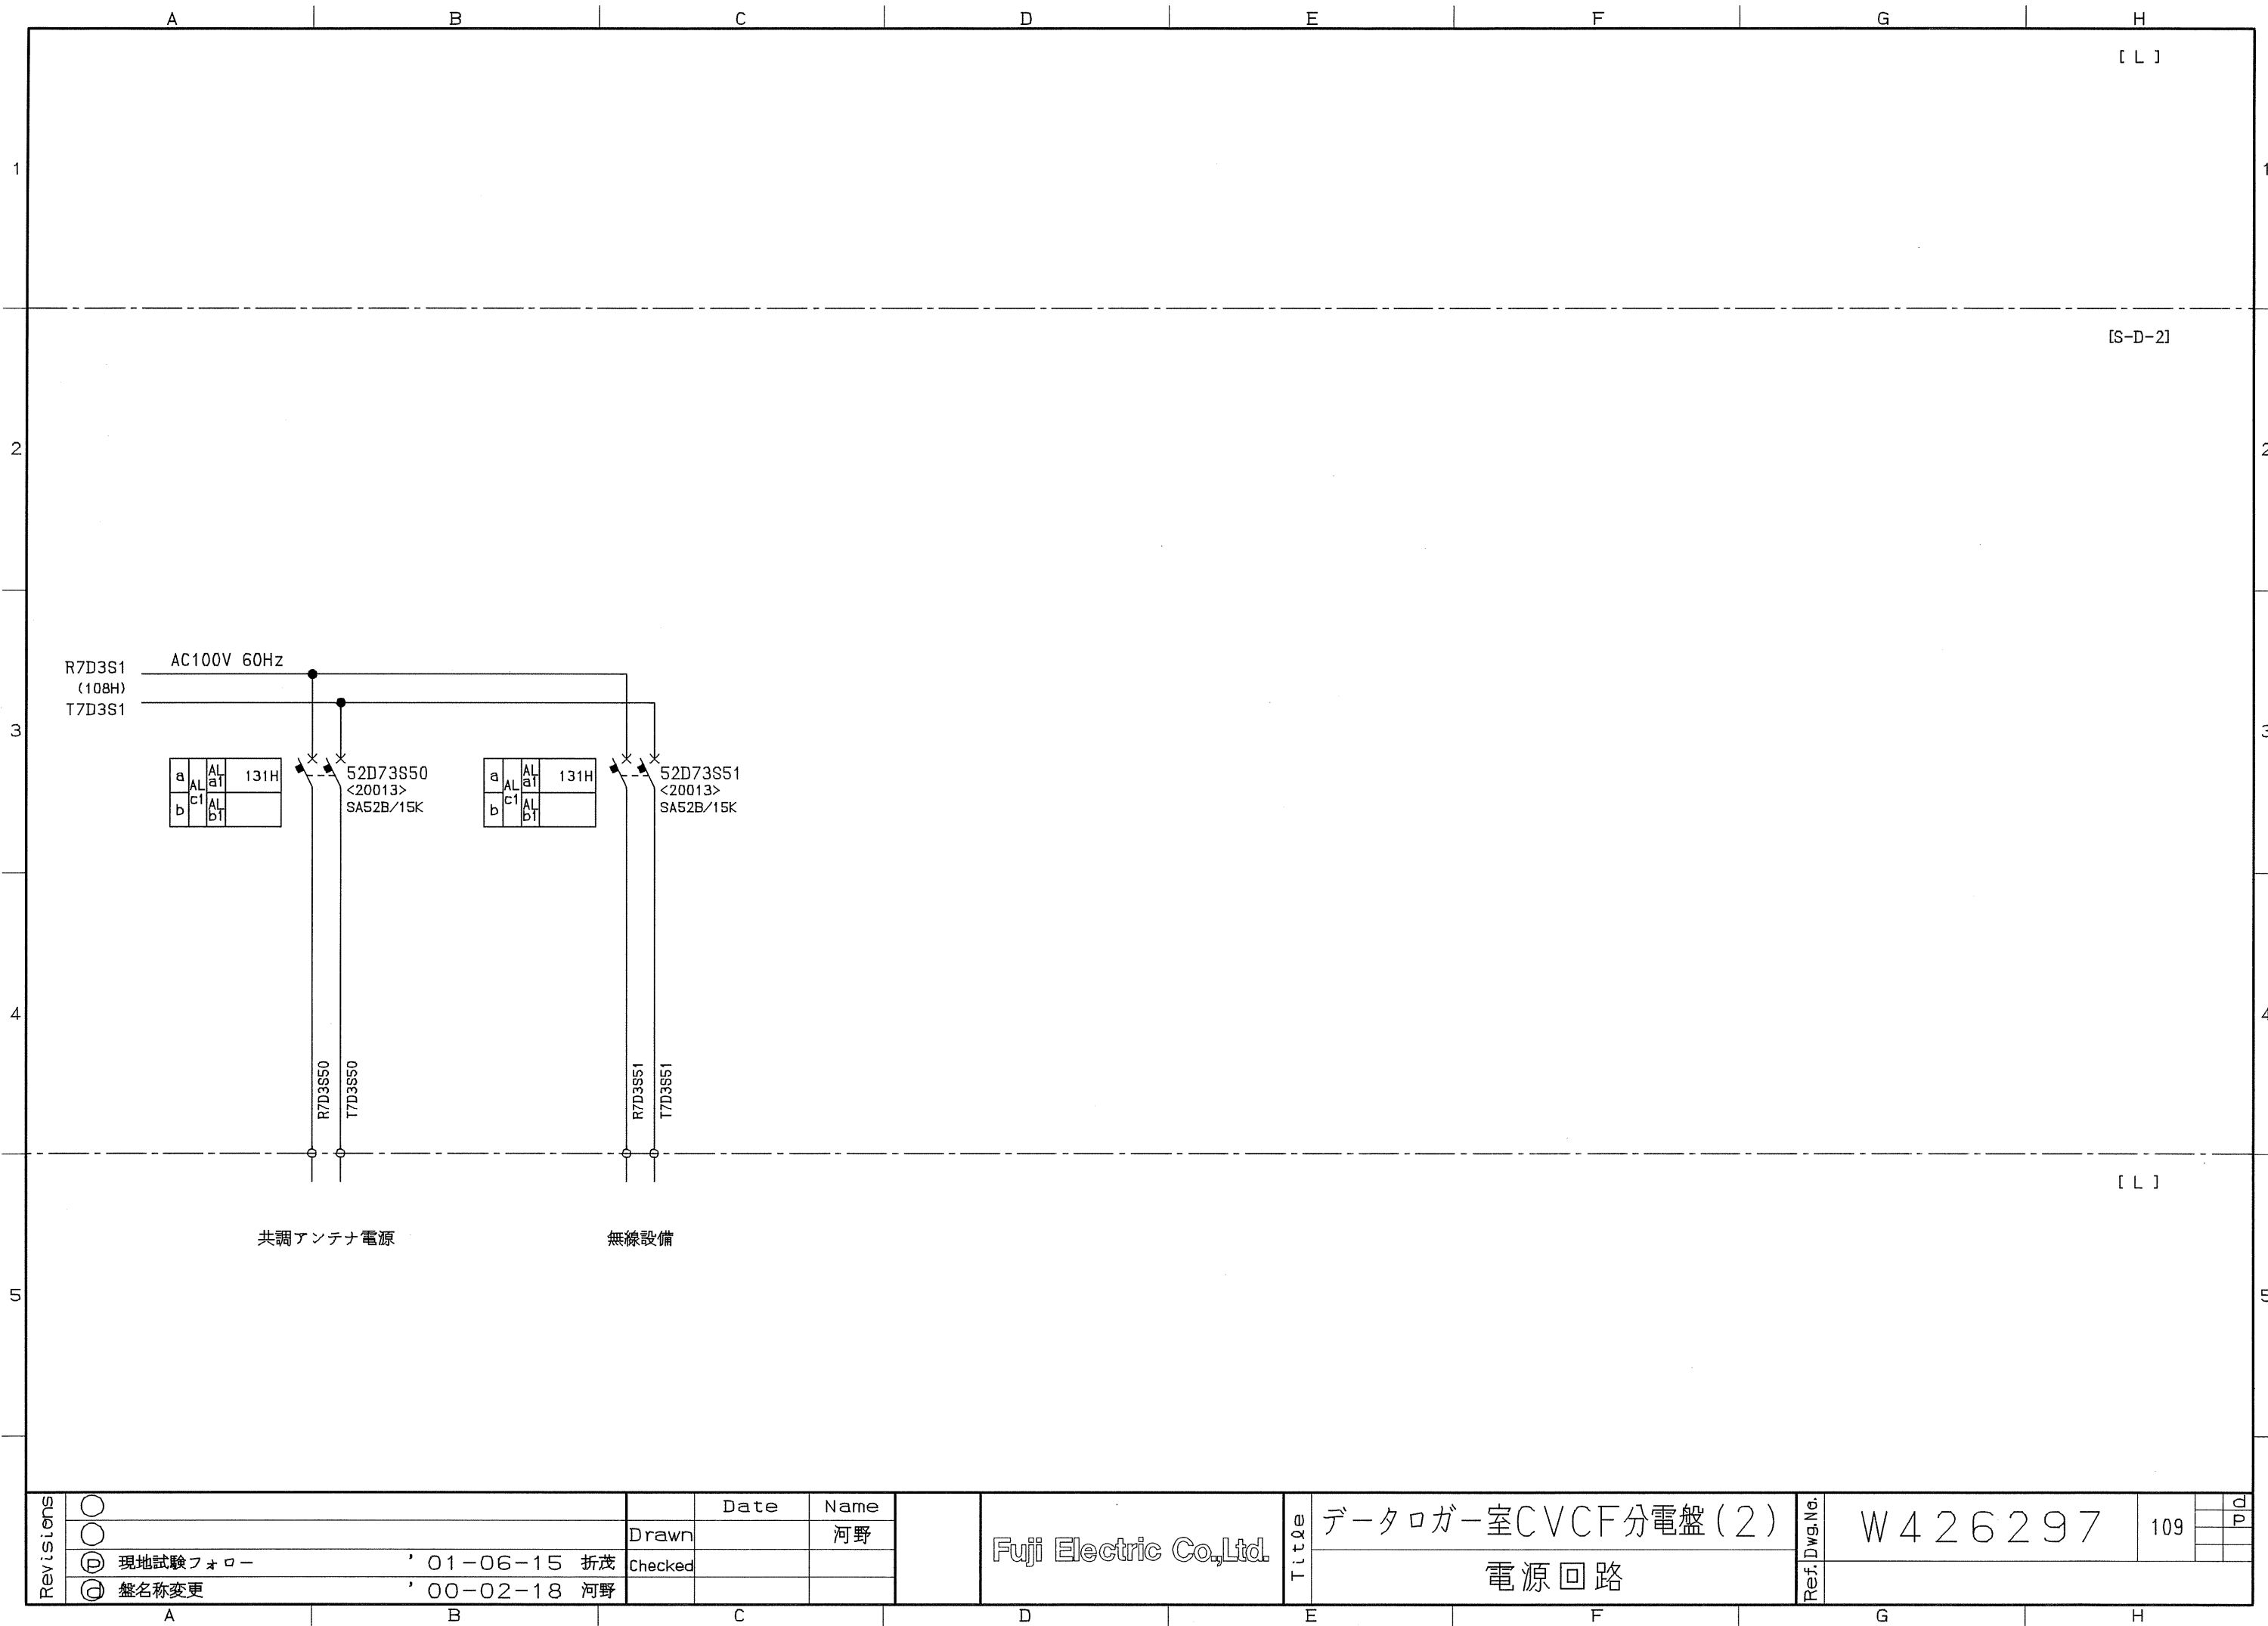


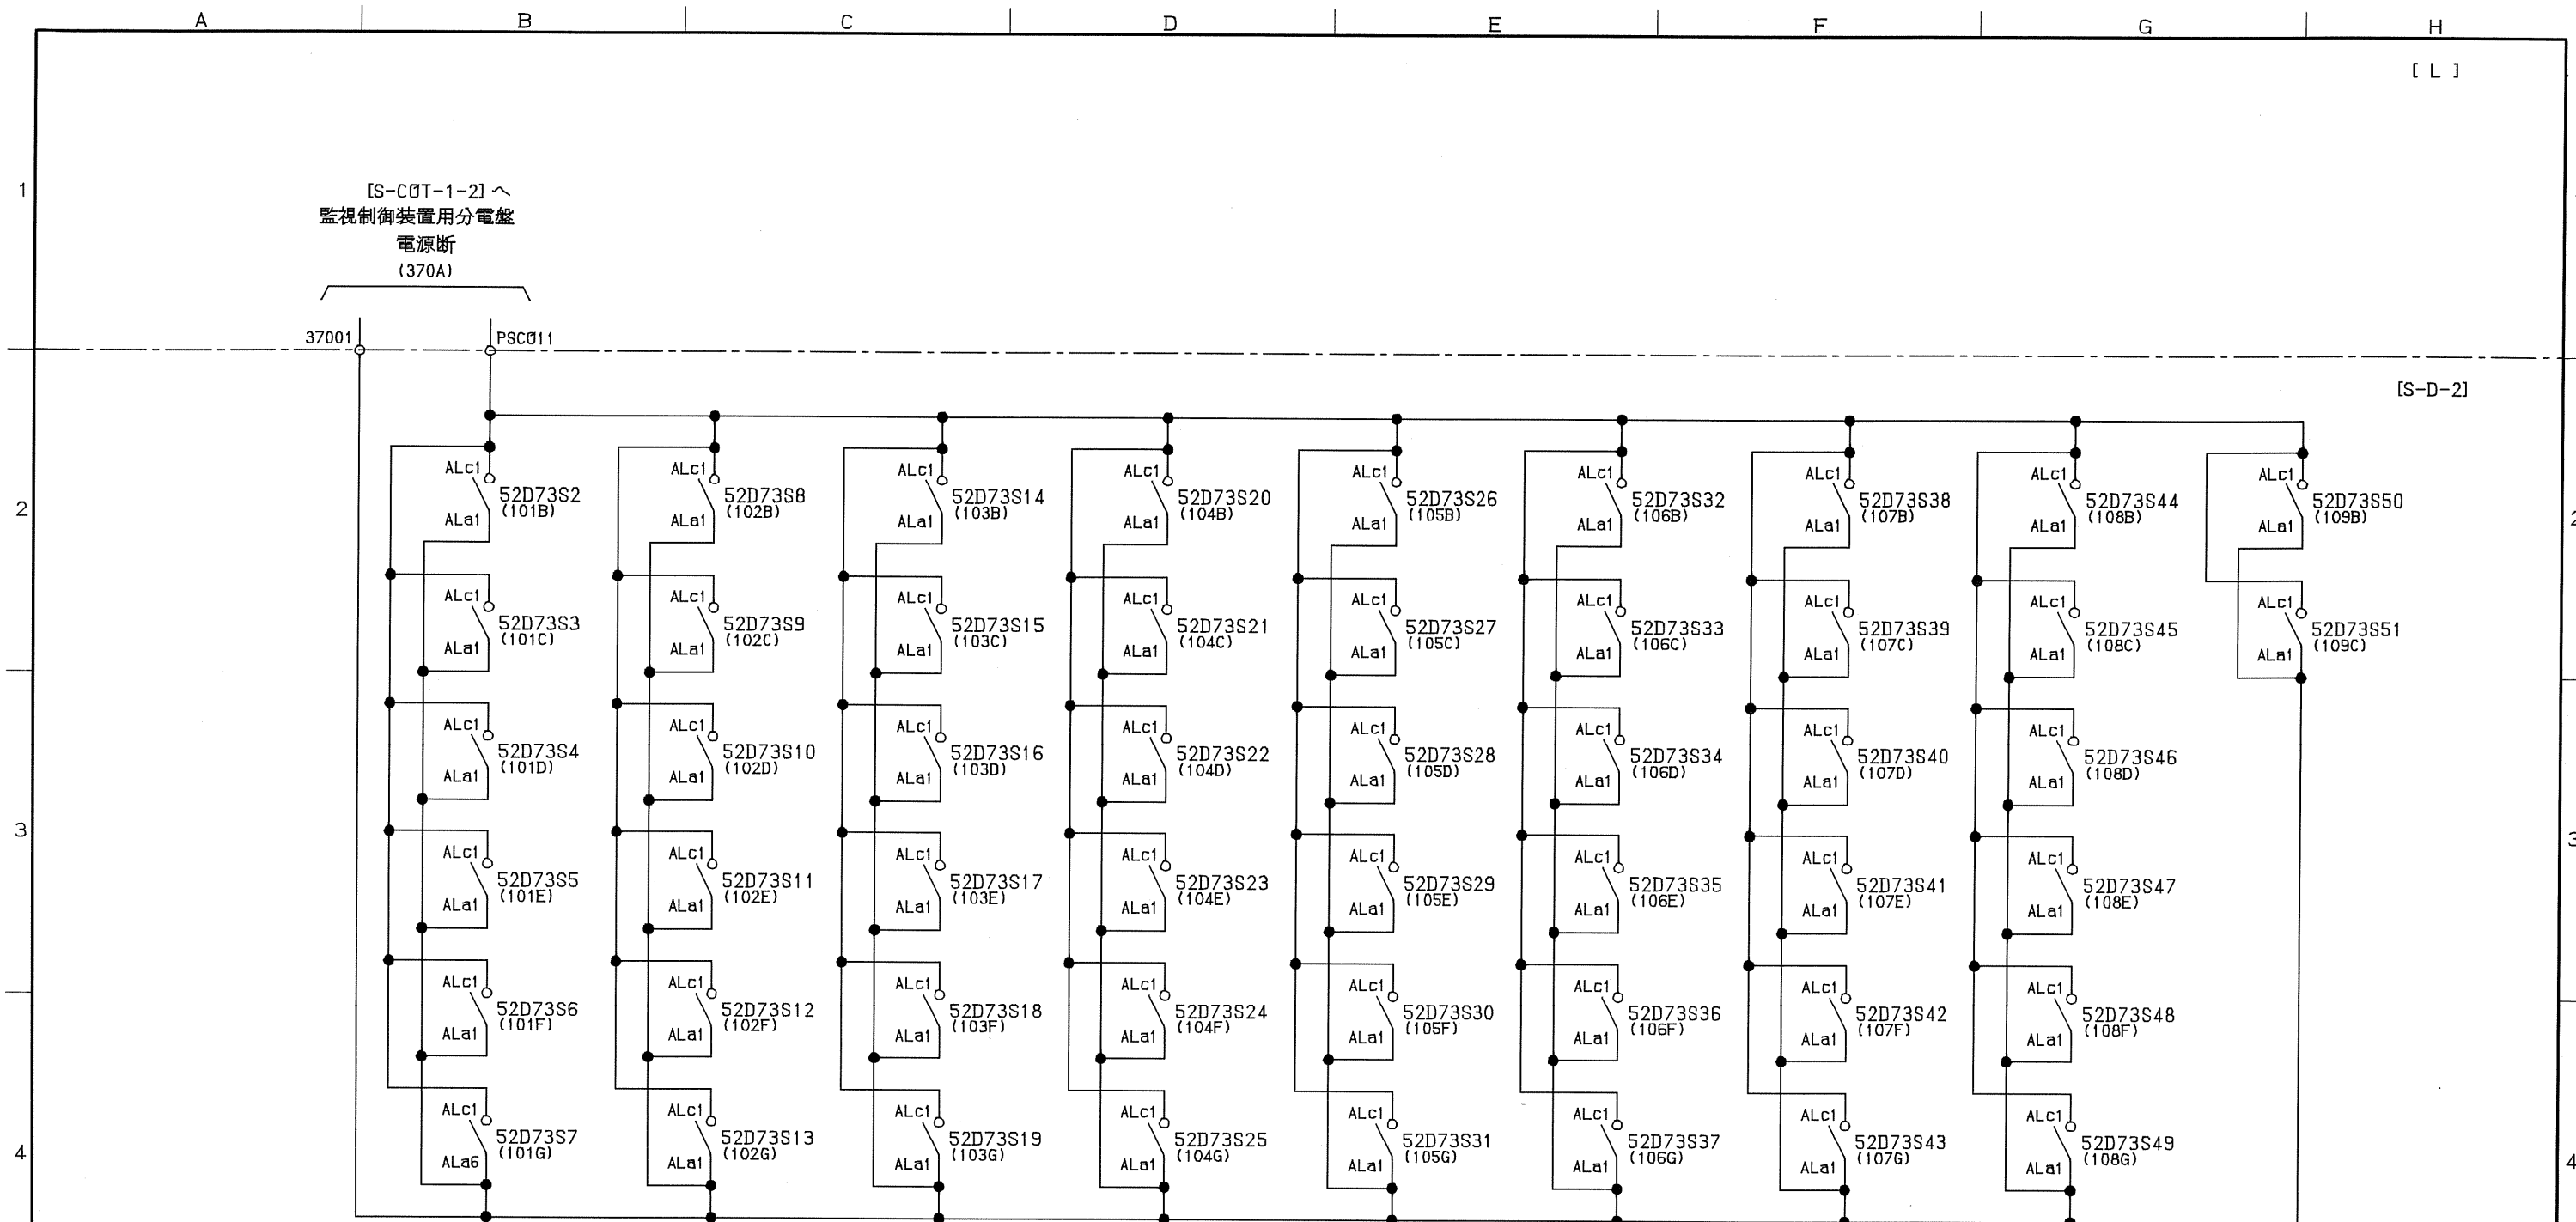



Revisions	○			Date	Name	Fuji Electric Co.,Ltd.	Title	データロガー室CVCF分電盤(2) 電源回路	Ref. Dwg. No.	W426297	131	(122~130x)
	○		Drawn		河野							
	①	取合いフォロー	' 00-08-21	野崎	Checked							
	②	盤名称変更	' 00-02-18	河野								

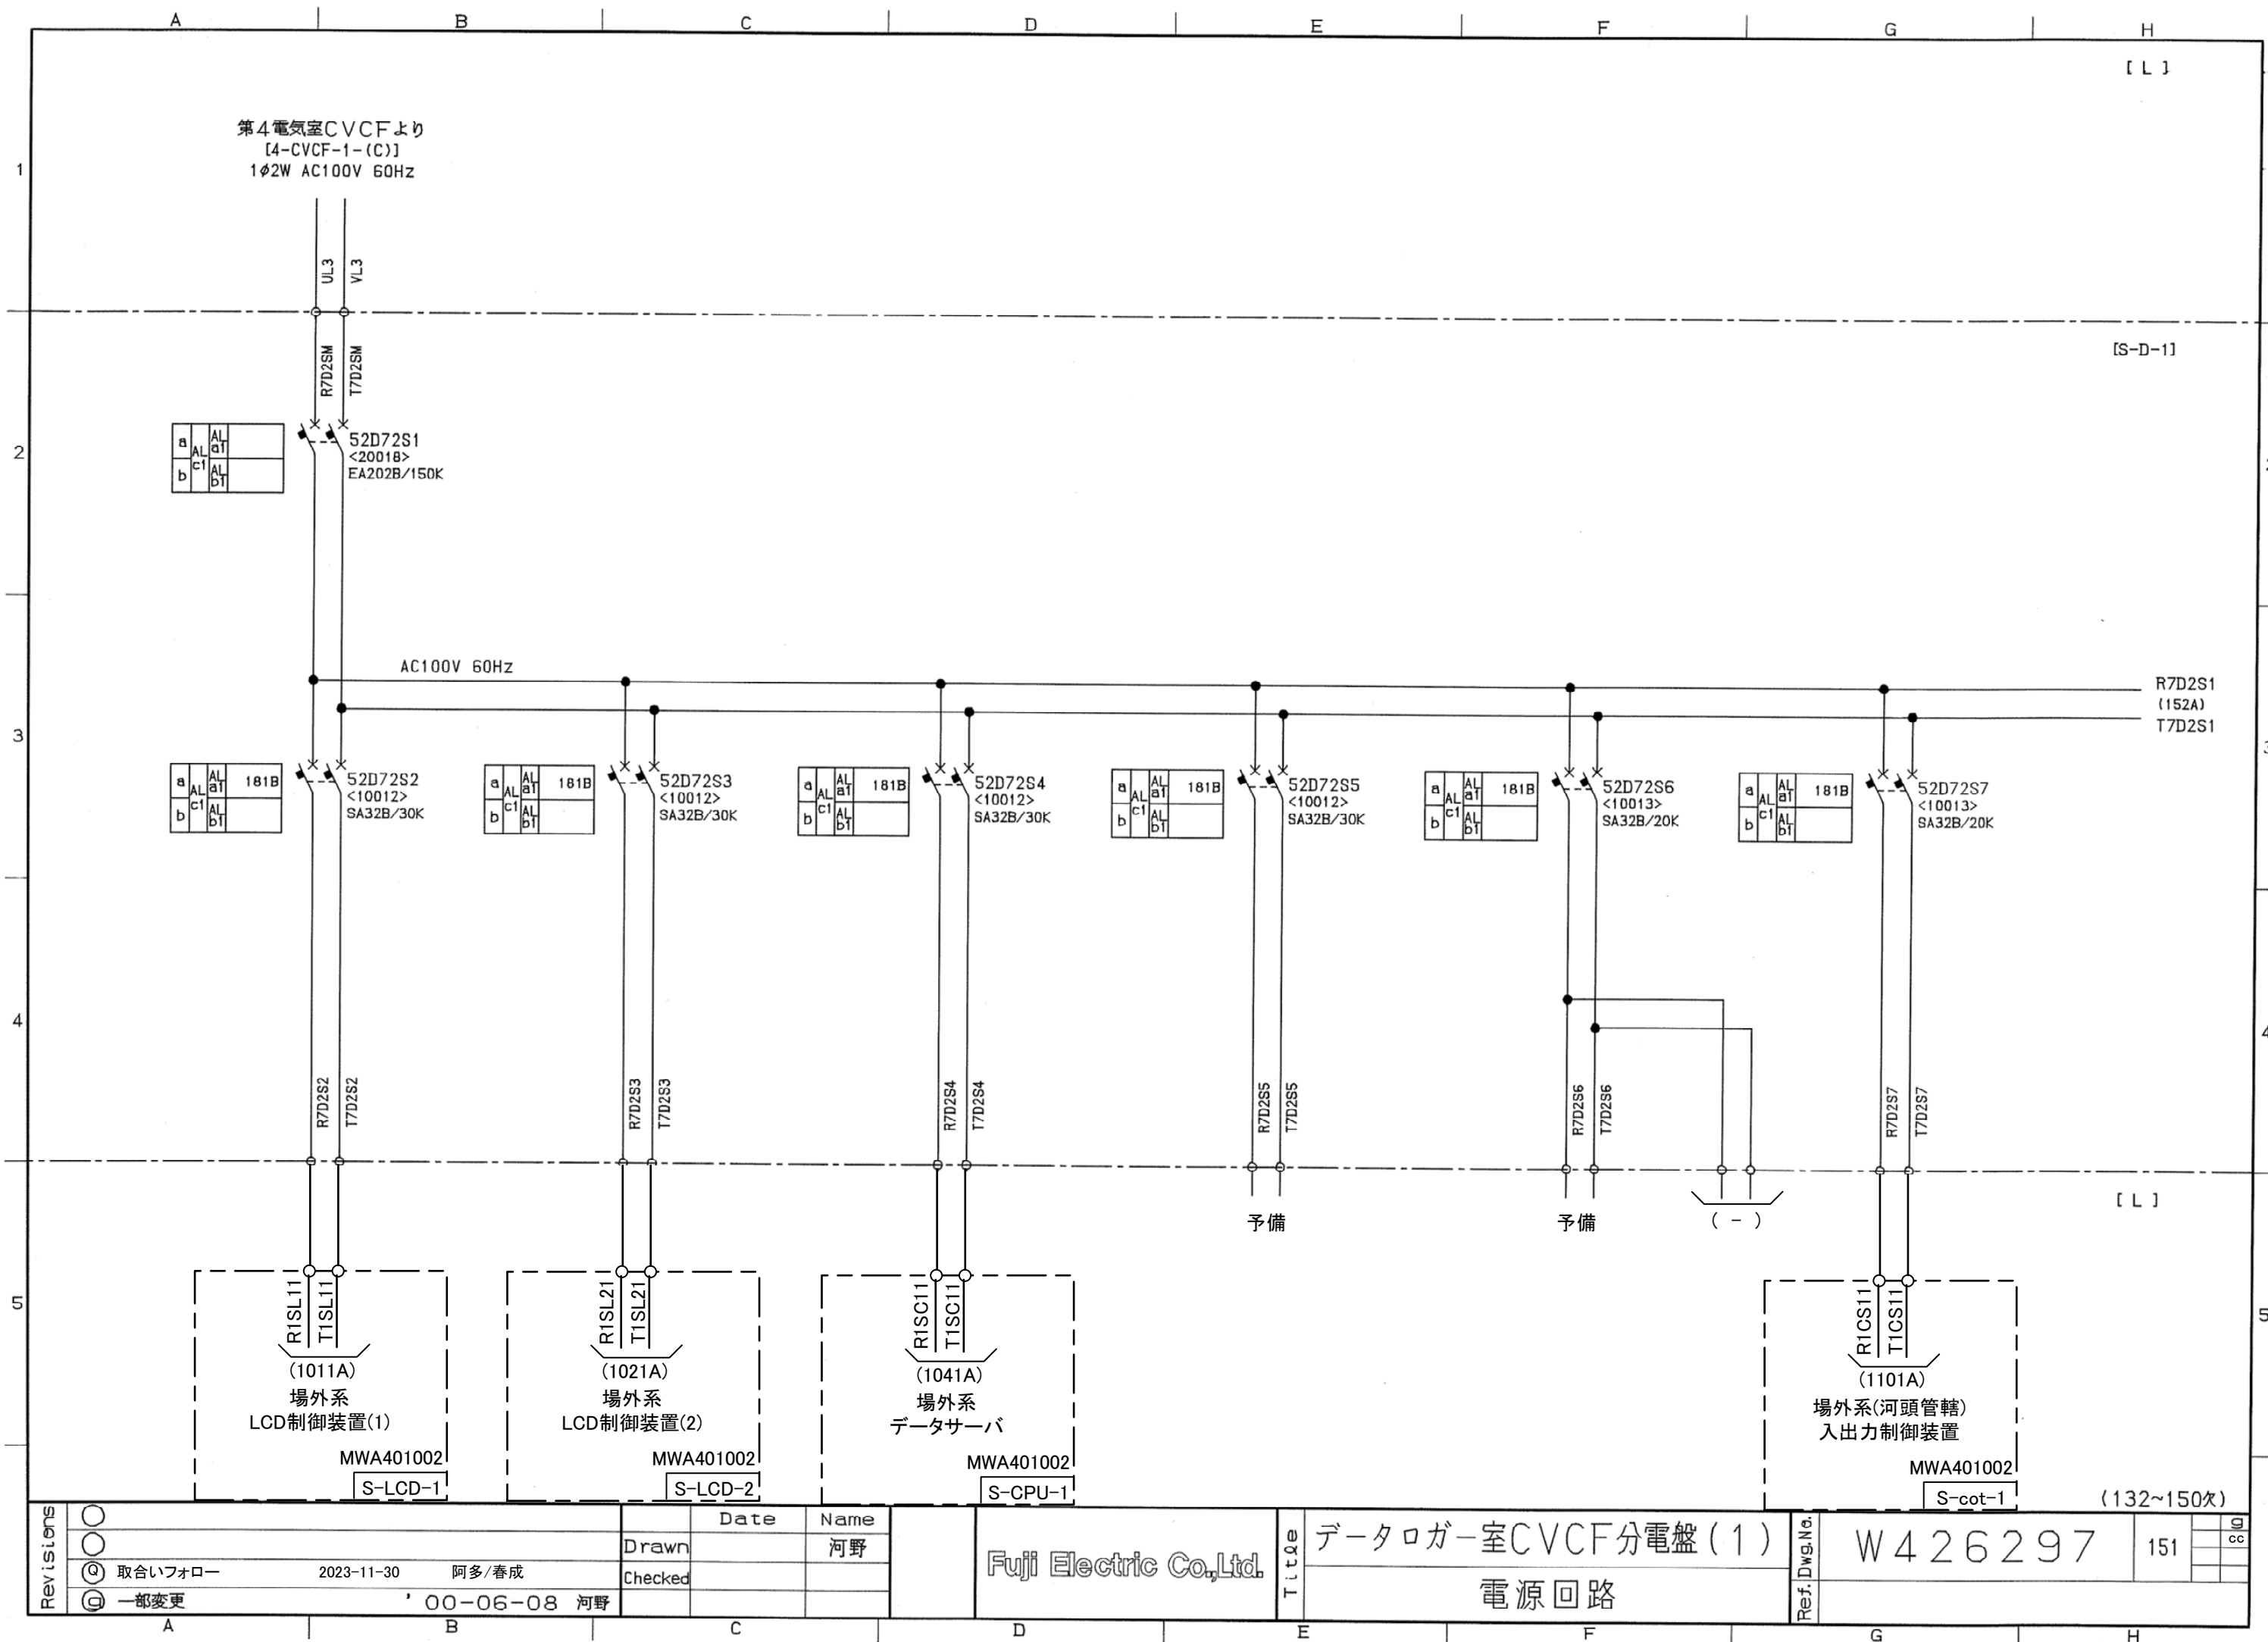

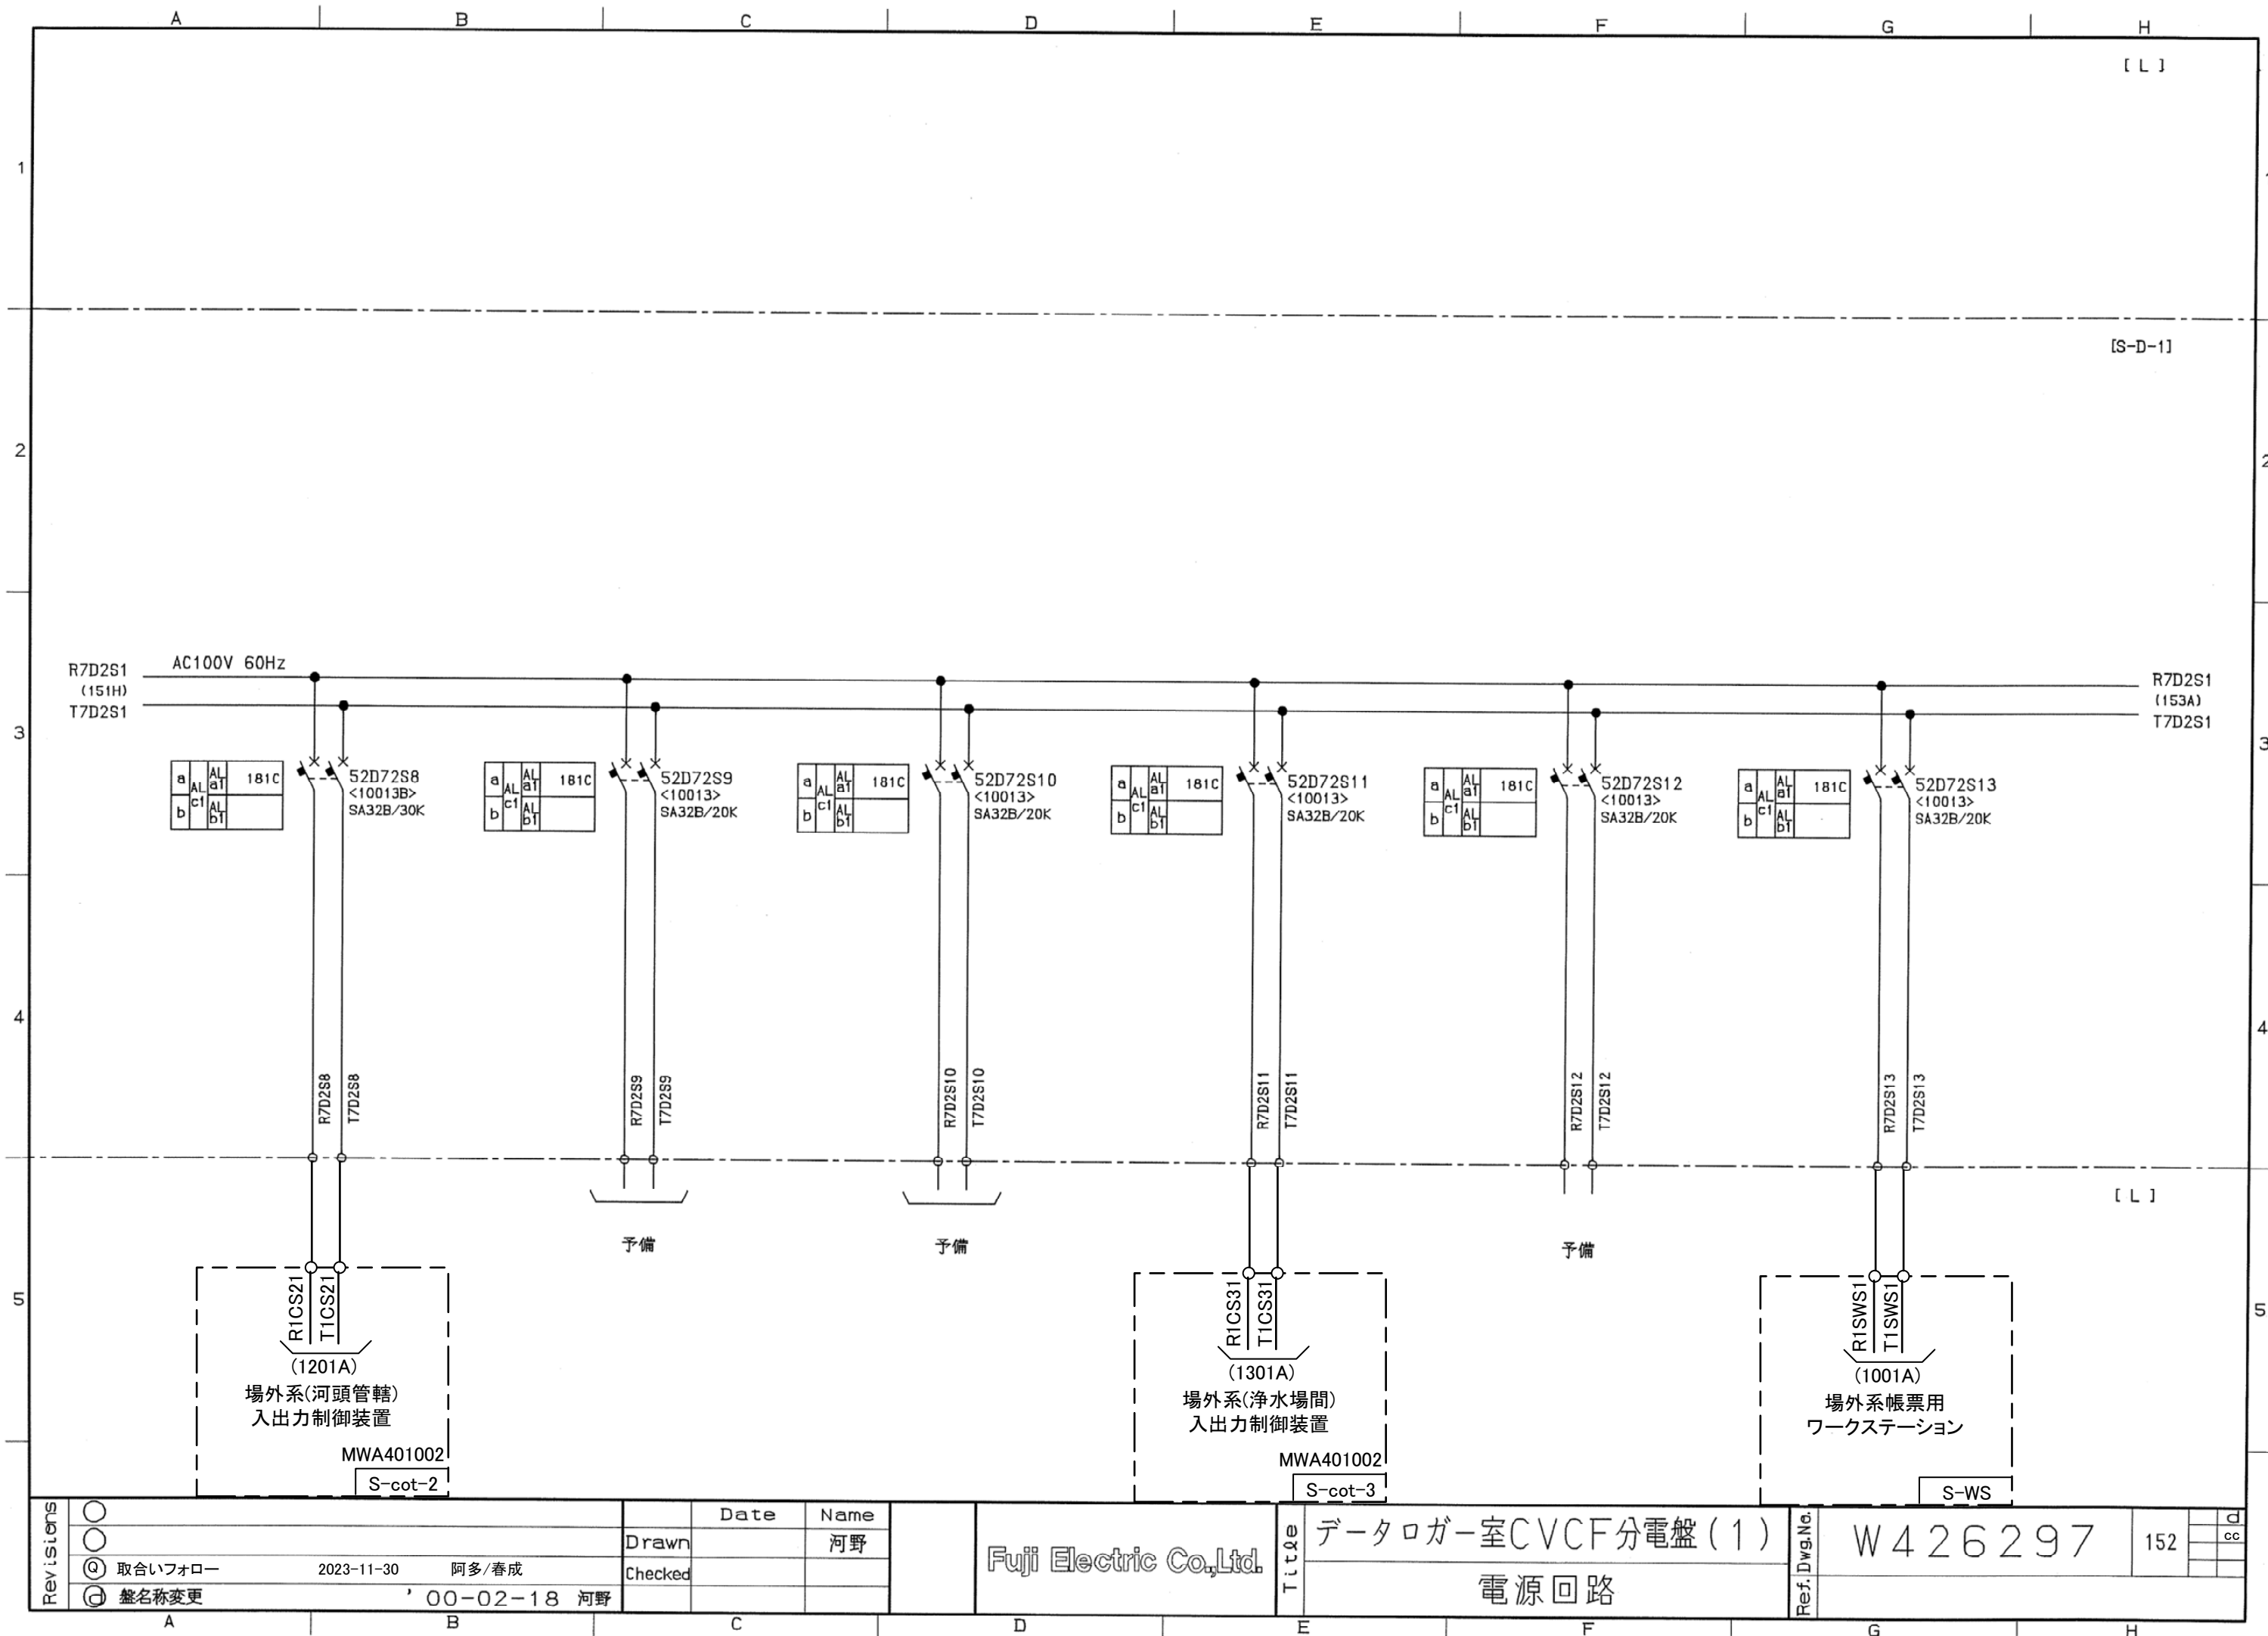


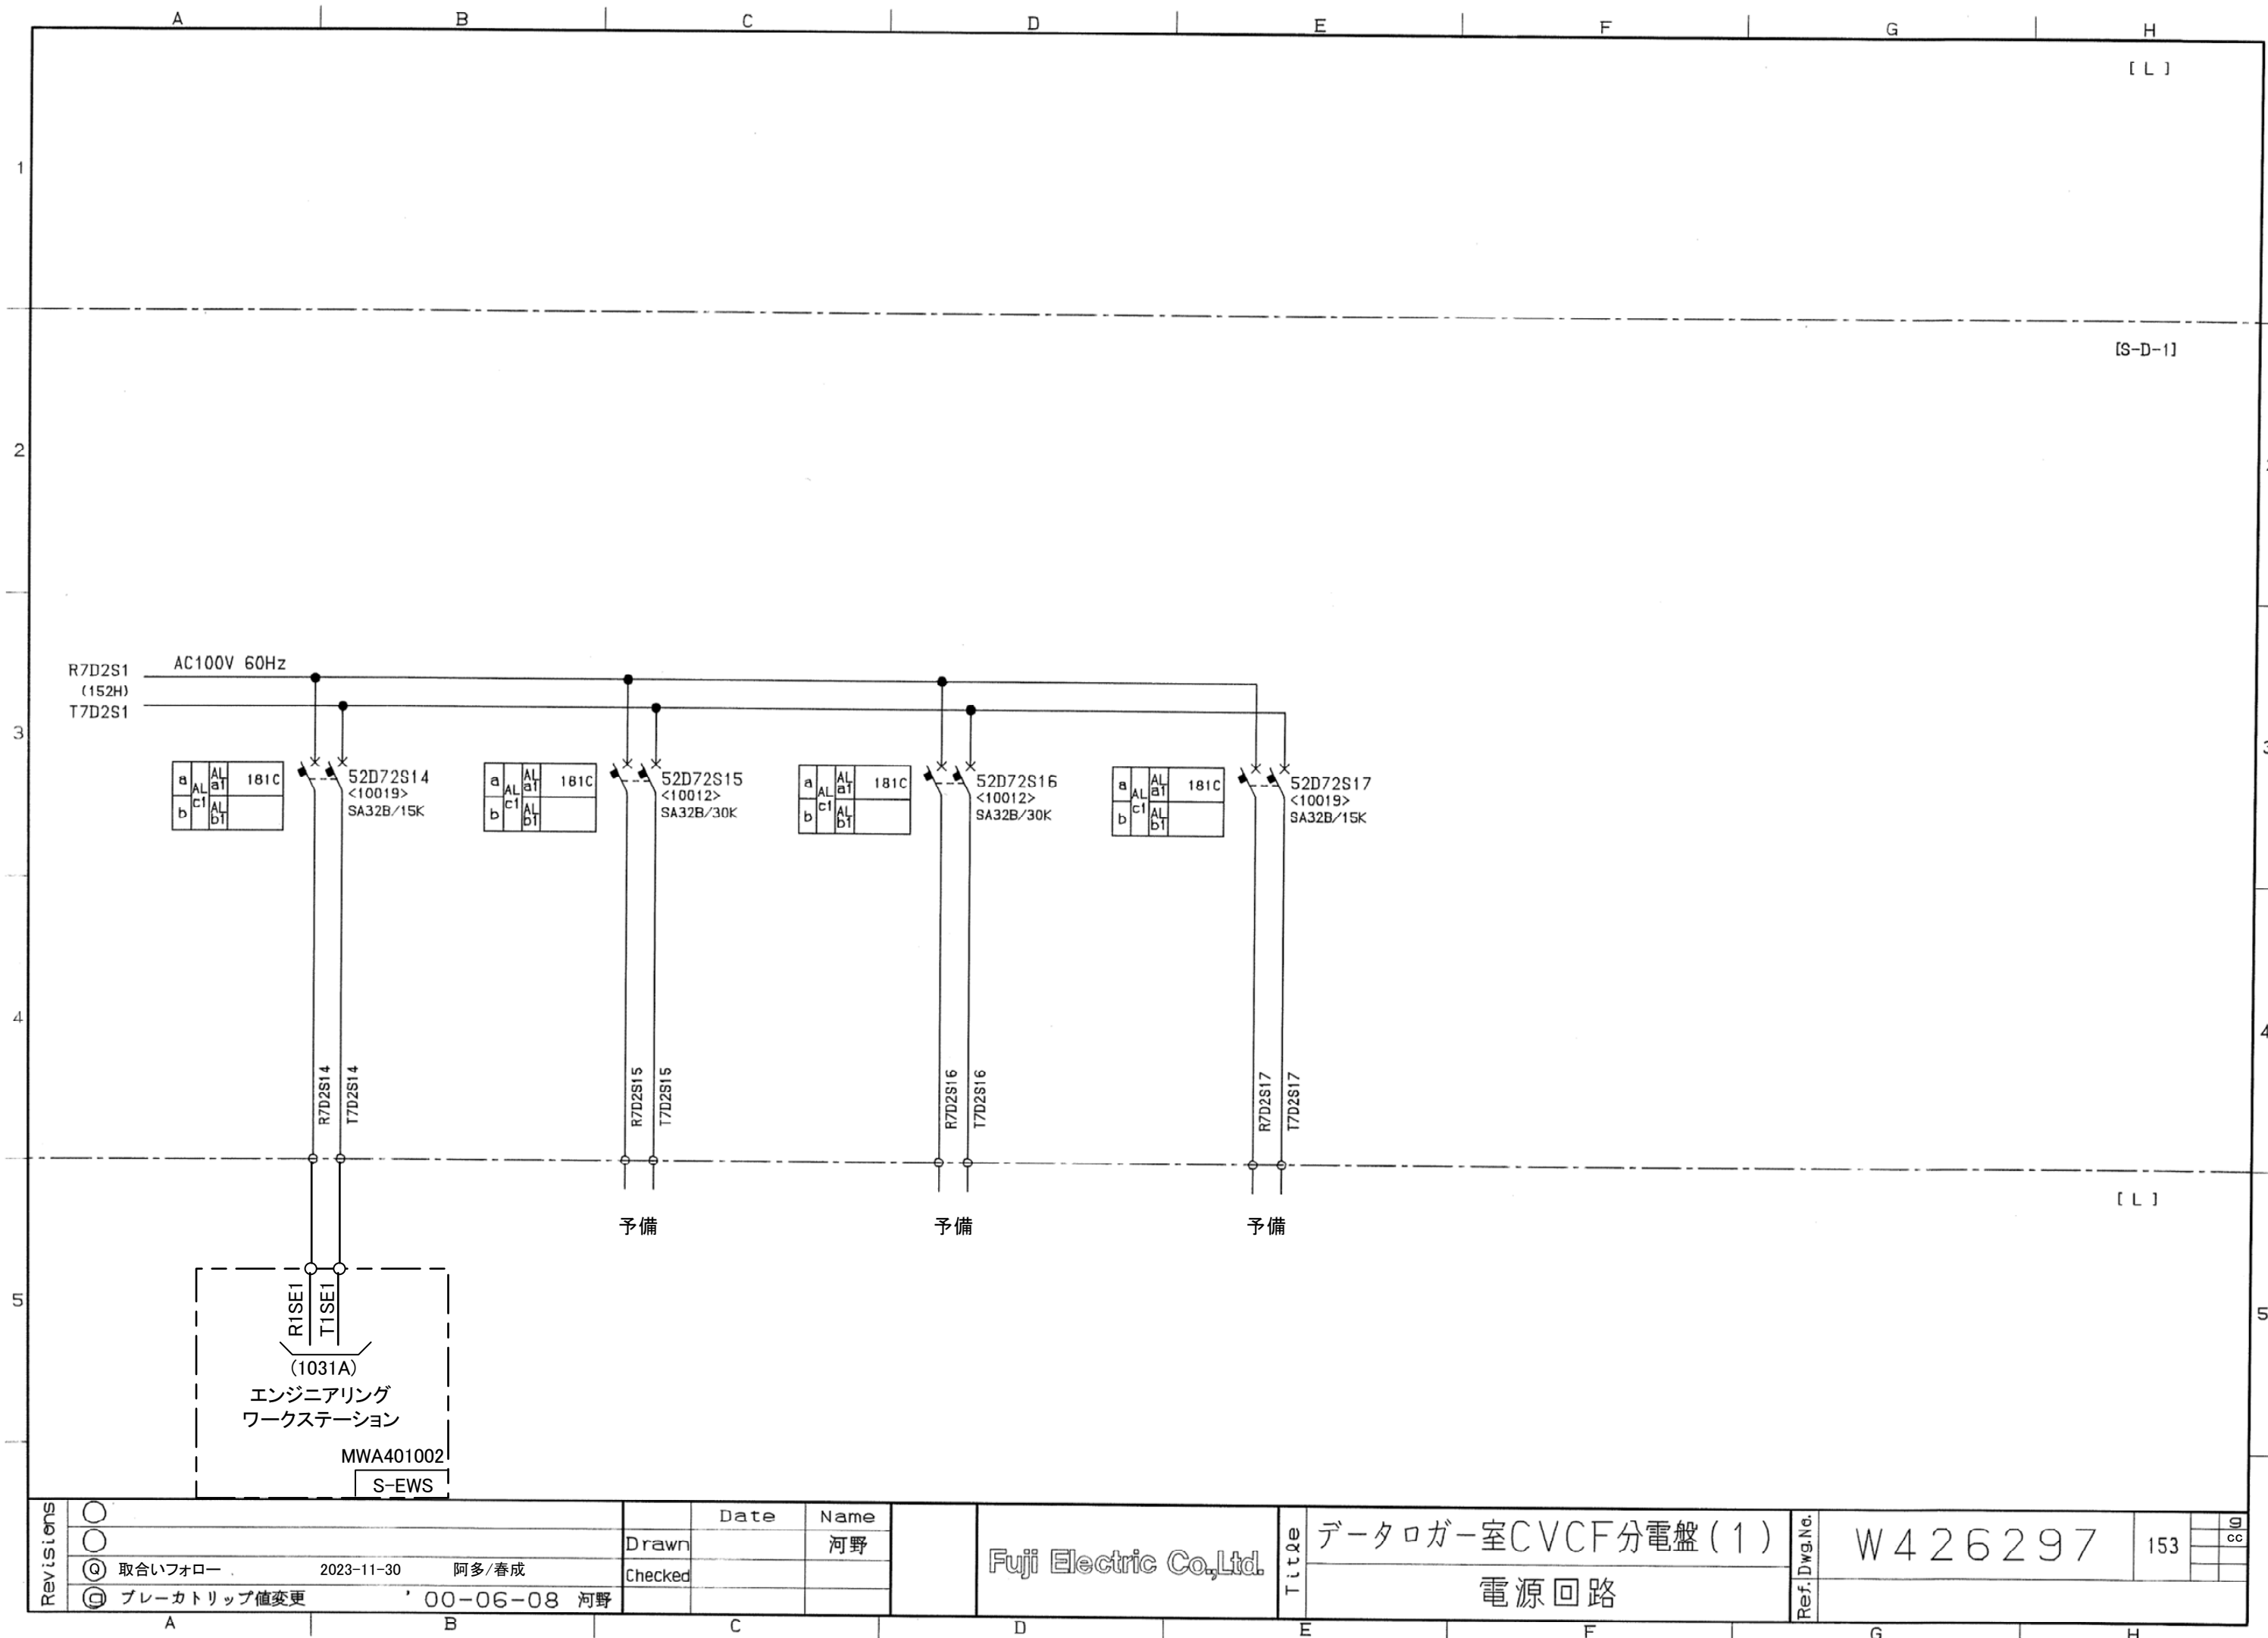

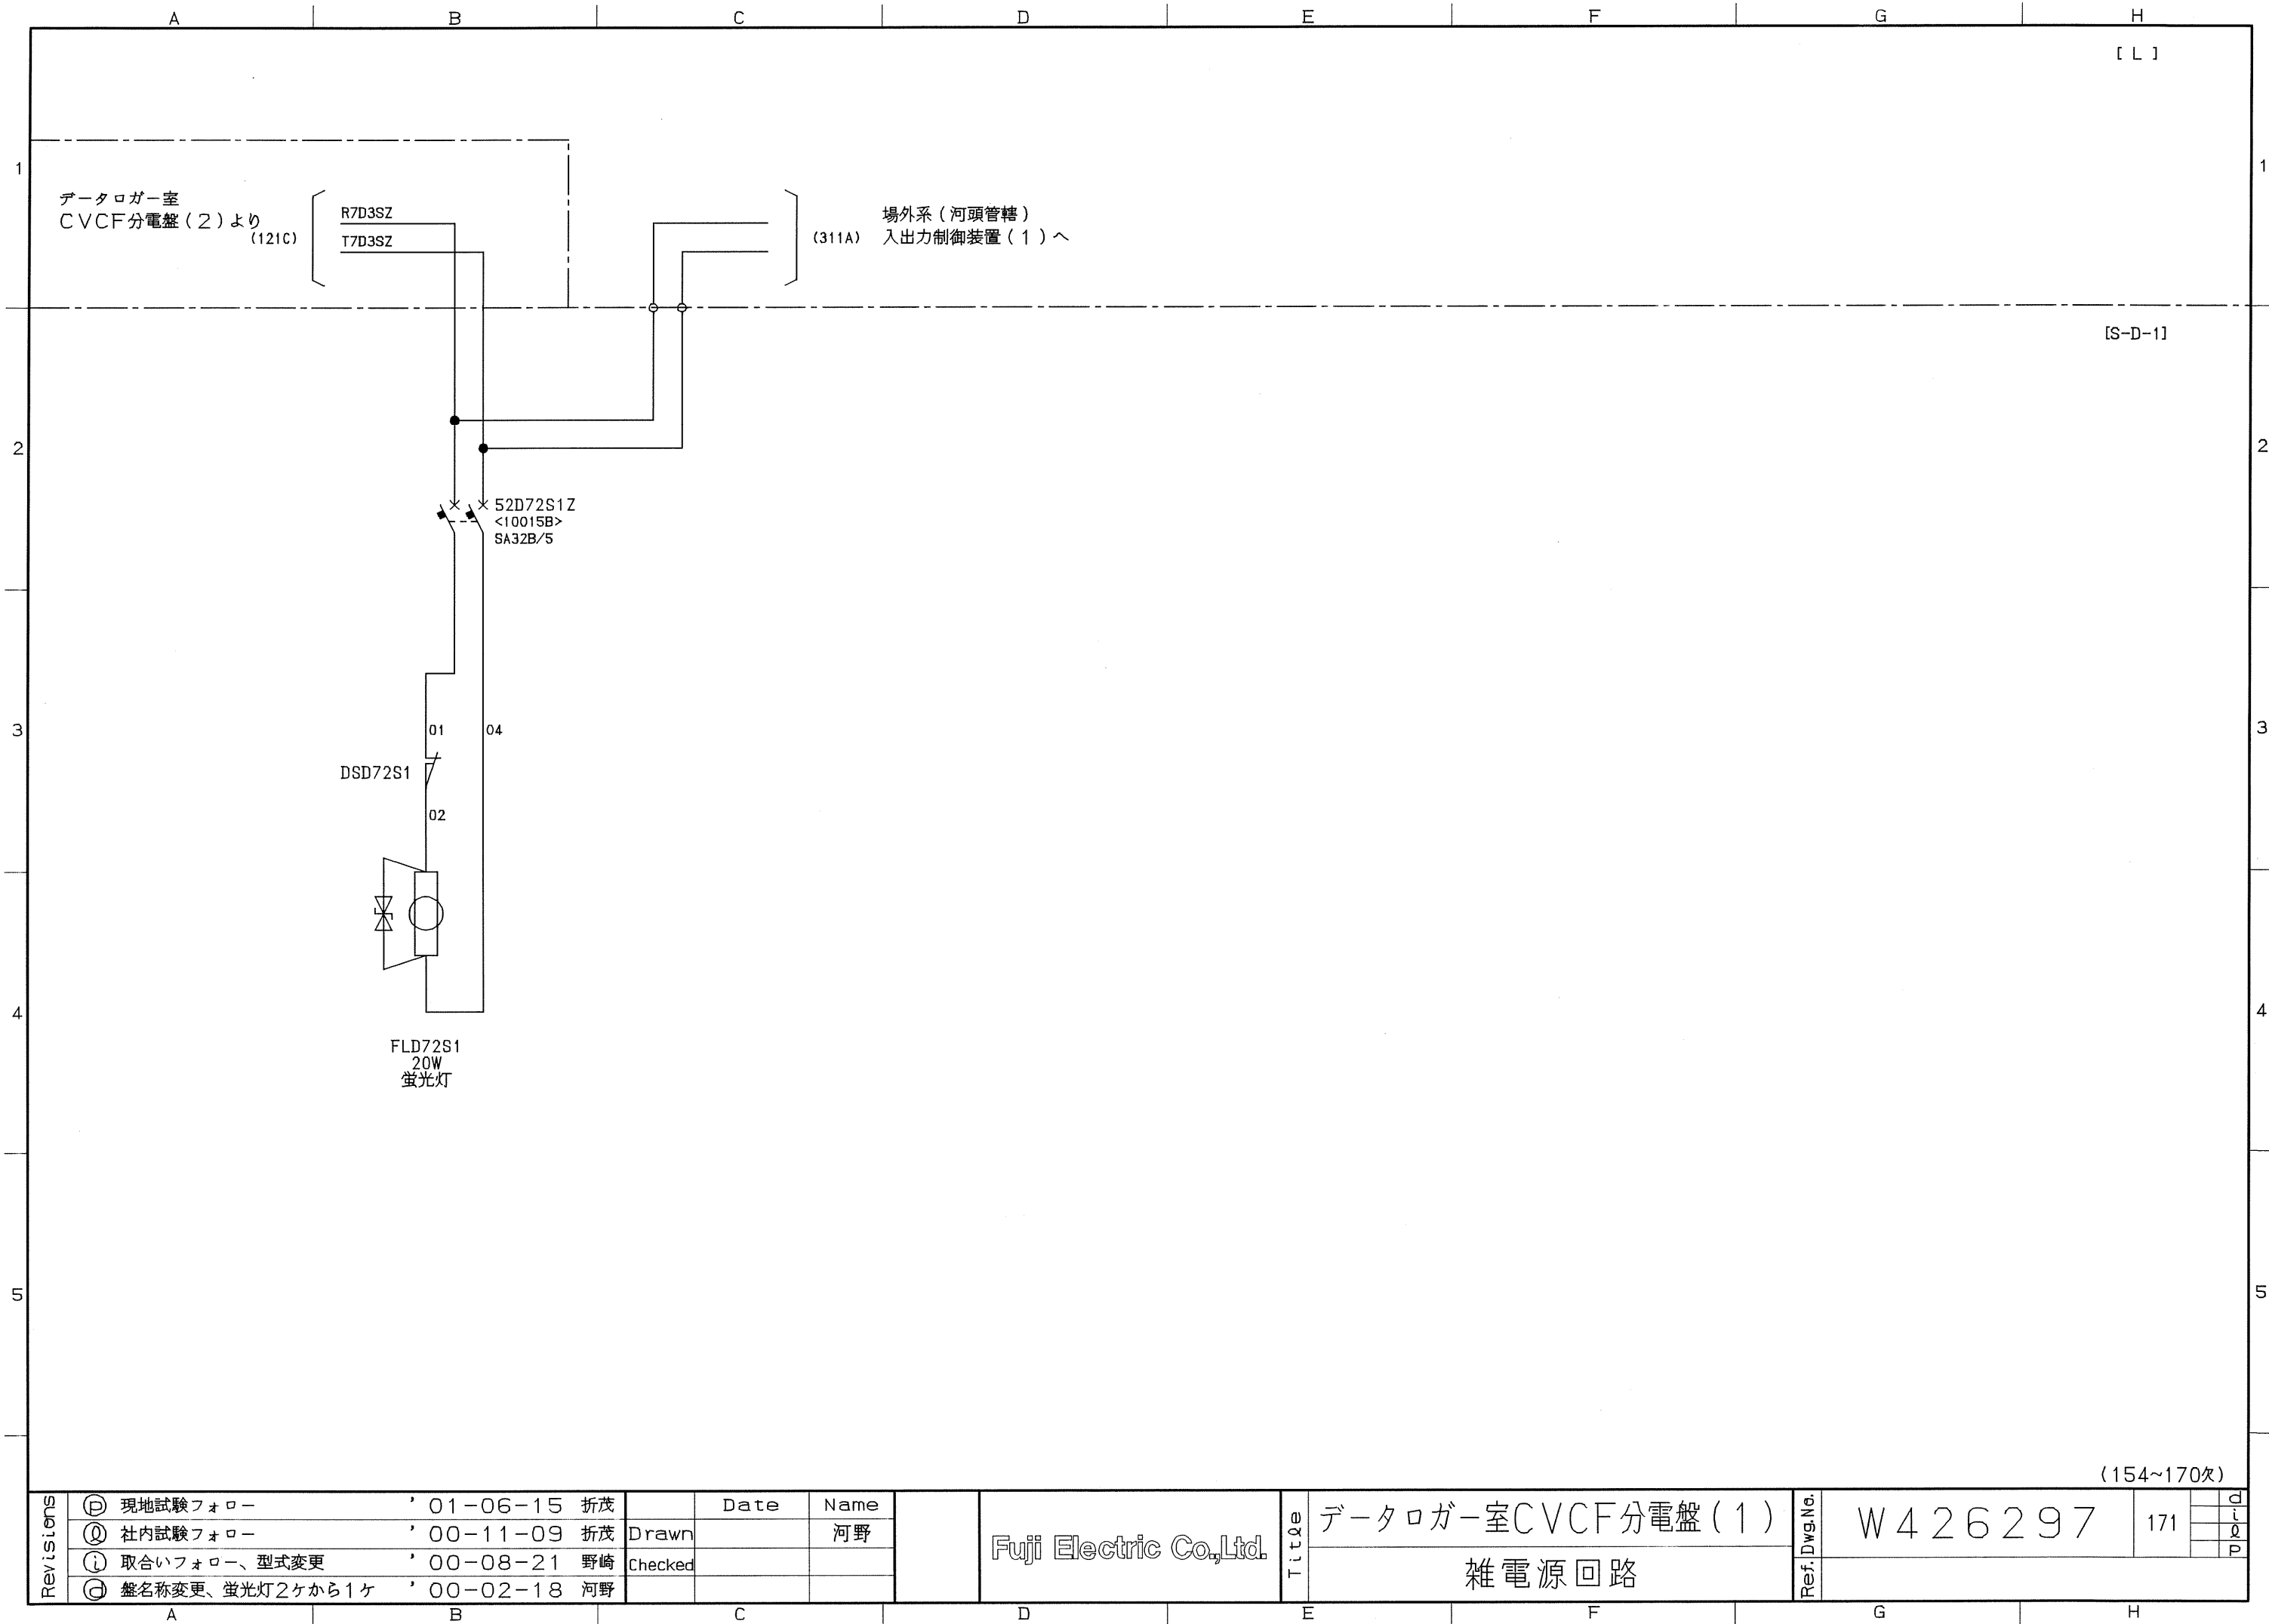


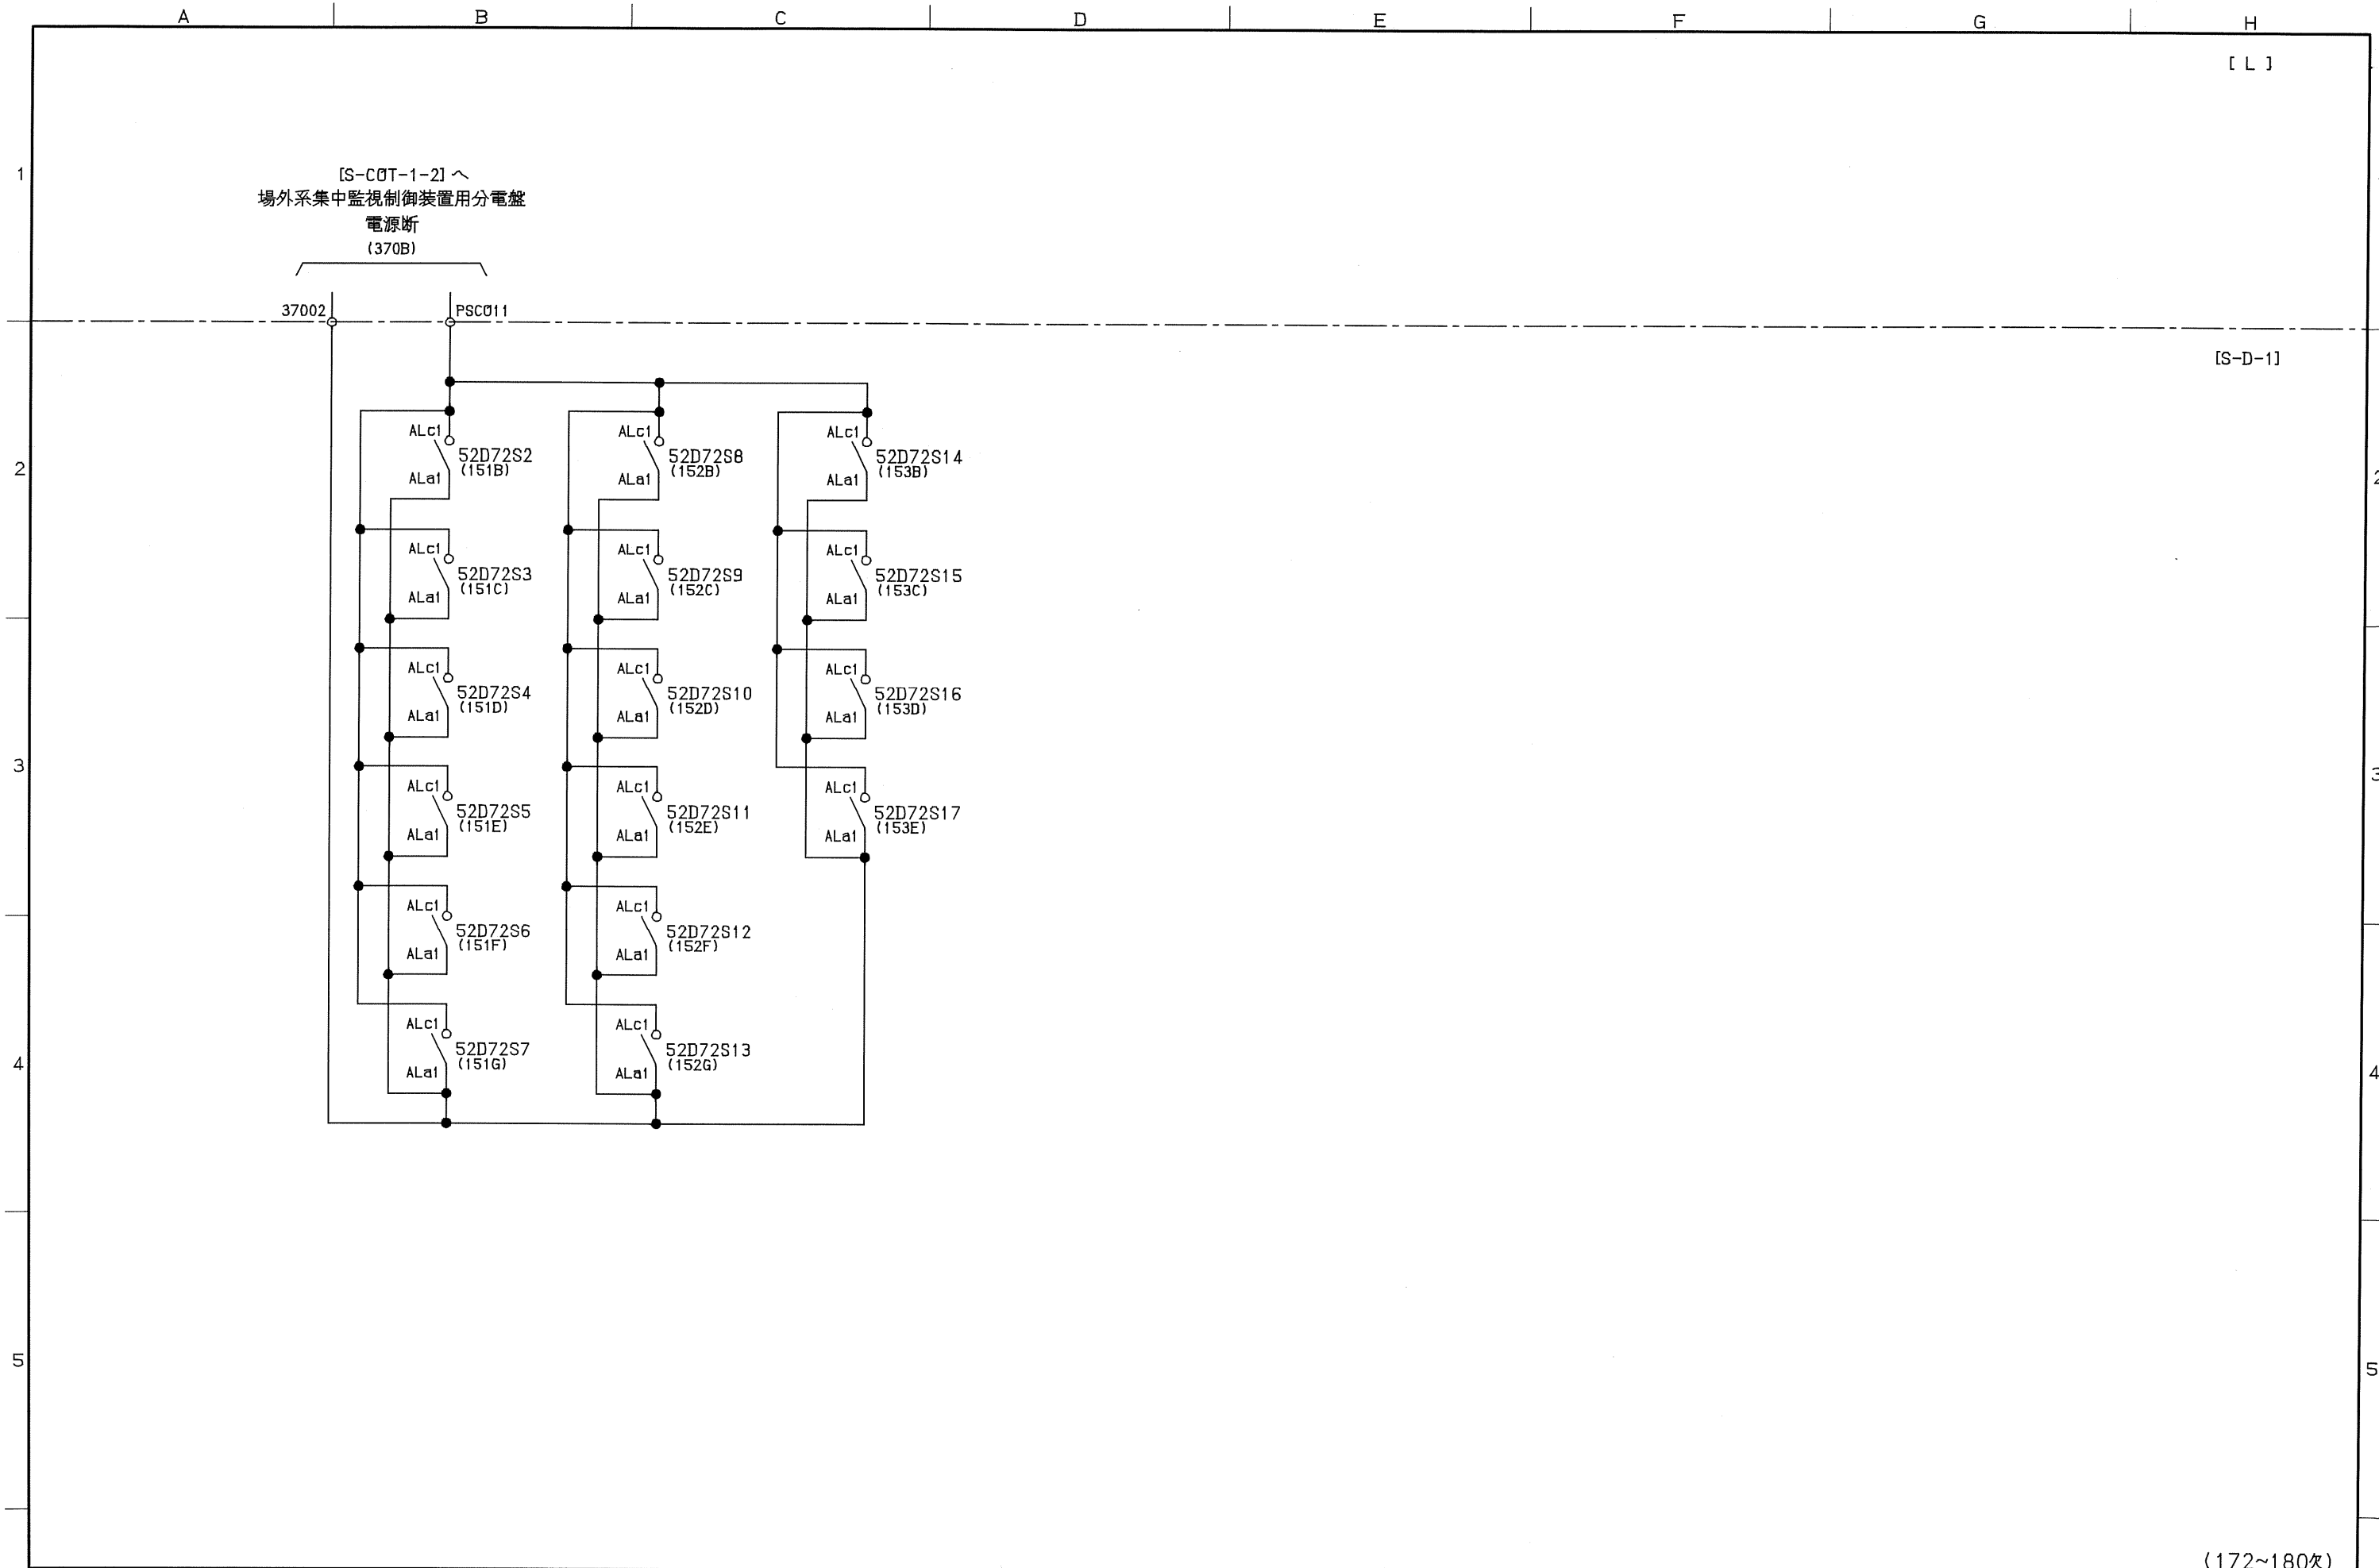

Revisions	○			Date	Name	Fuji Electric Co., Ltd.	Title	データロガー室CVCF分電盤(1) 電源回路	Ref. Dwg. No.	W426297	181	(172~180欠)
	○		Drawn	河野								
	① 取合いフォロー		' 00-08-21	野崎								
	② 盤名称変更		' 00-02-18	河野								
A			B		C	D	E	F	G	H		

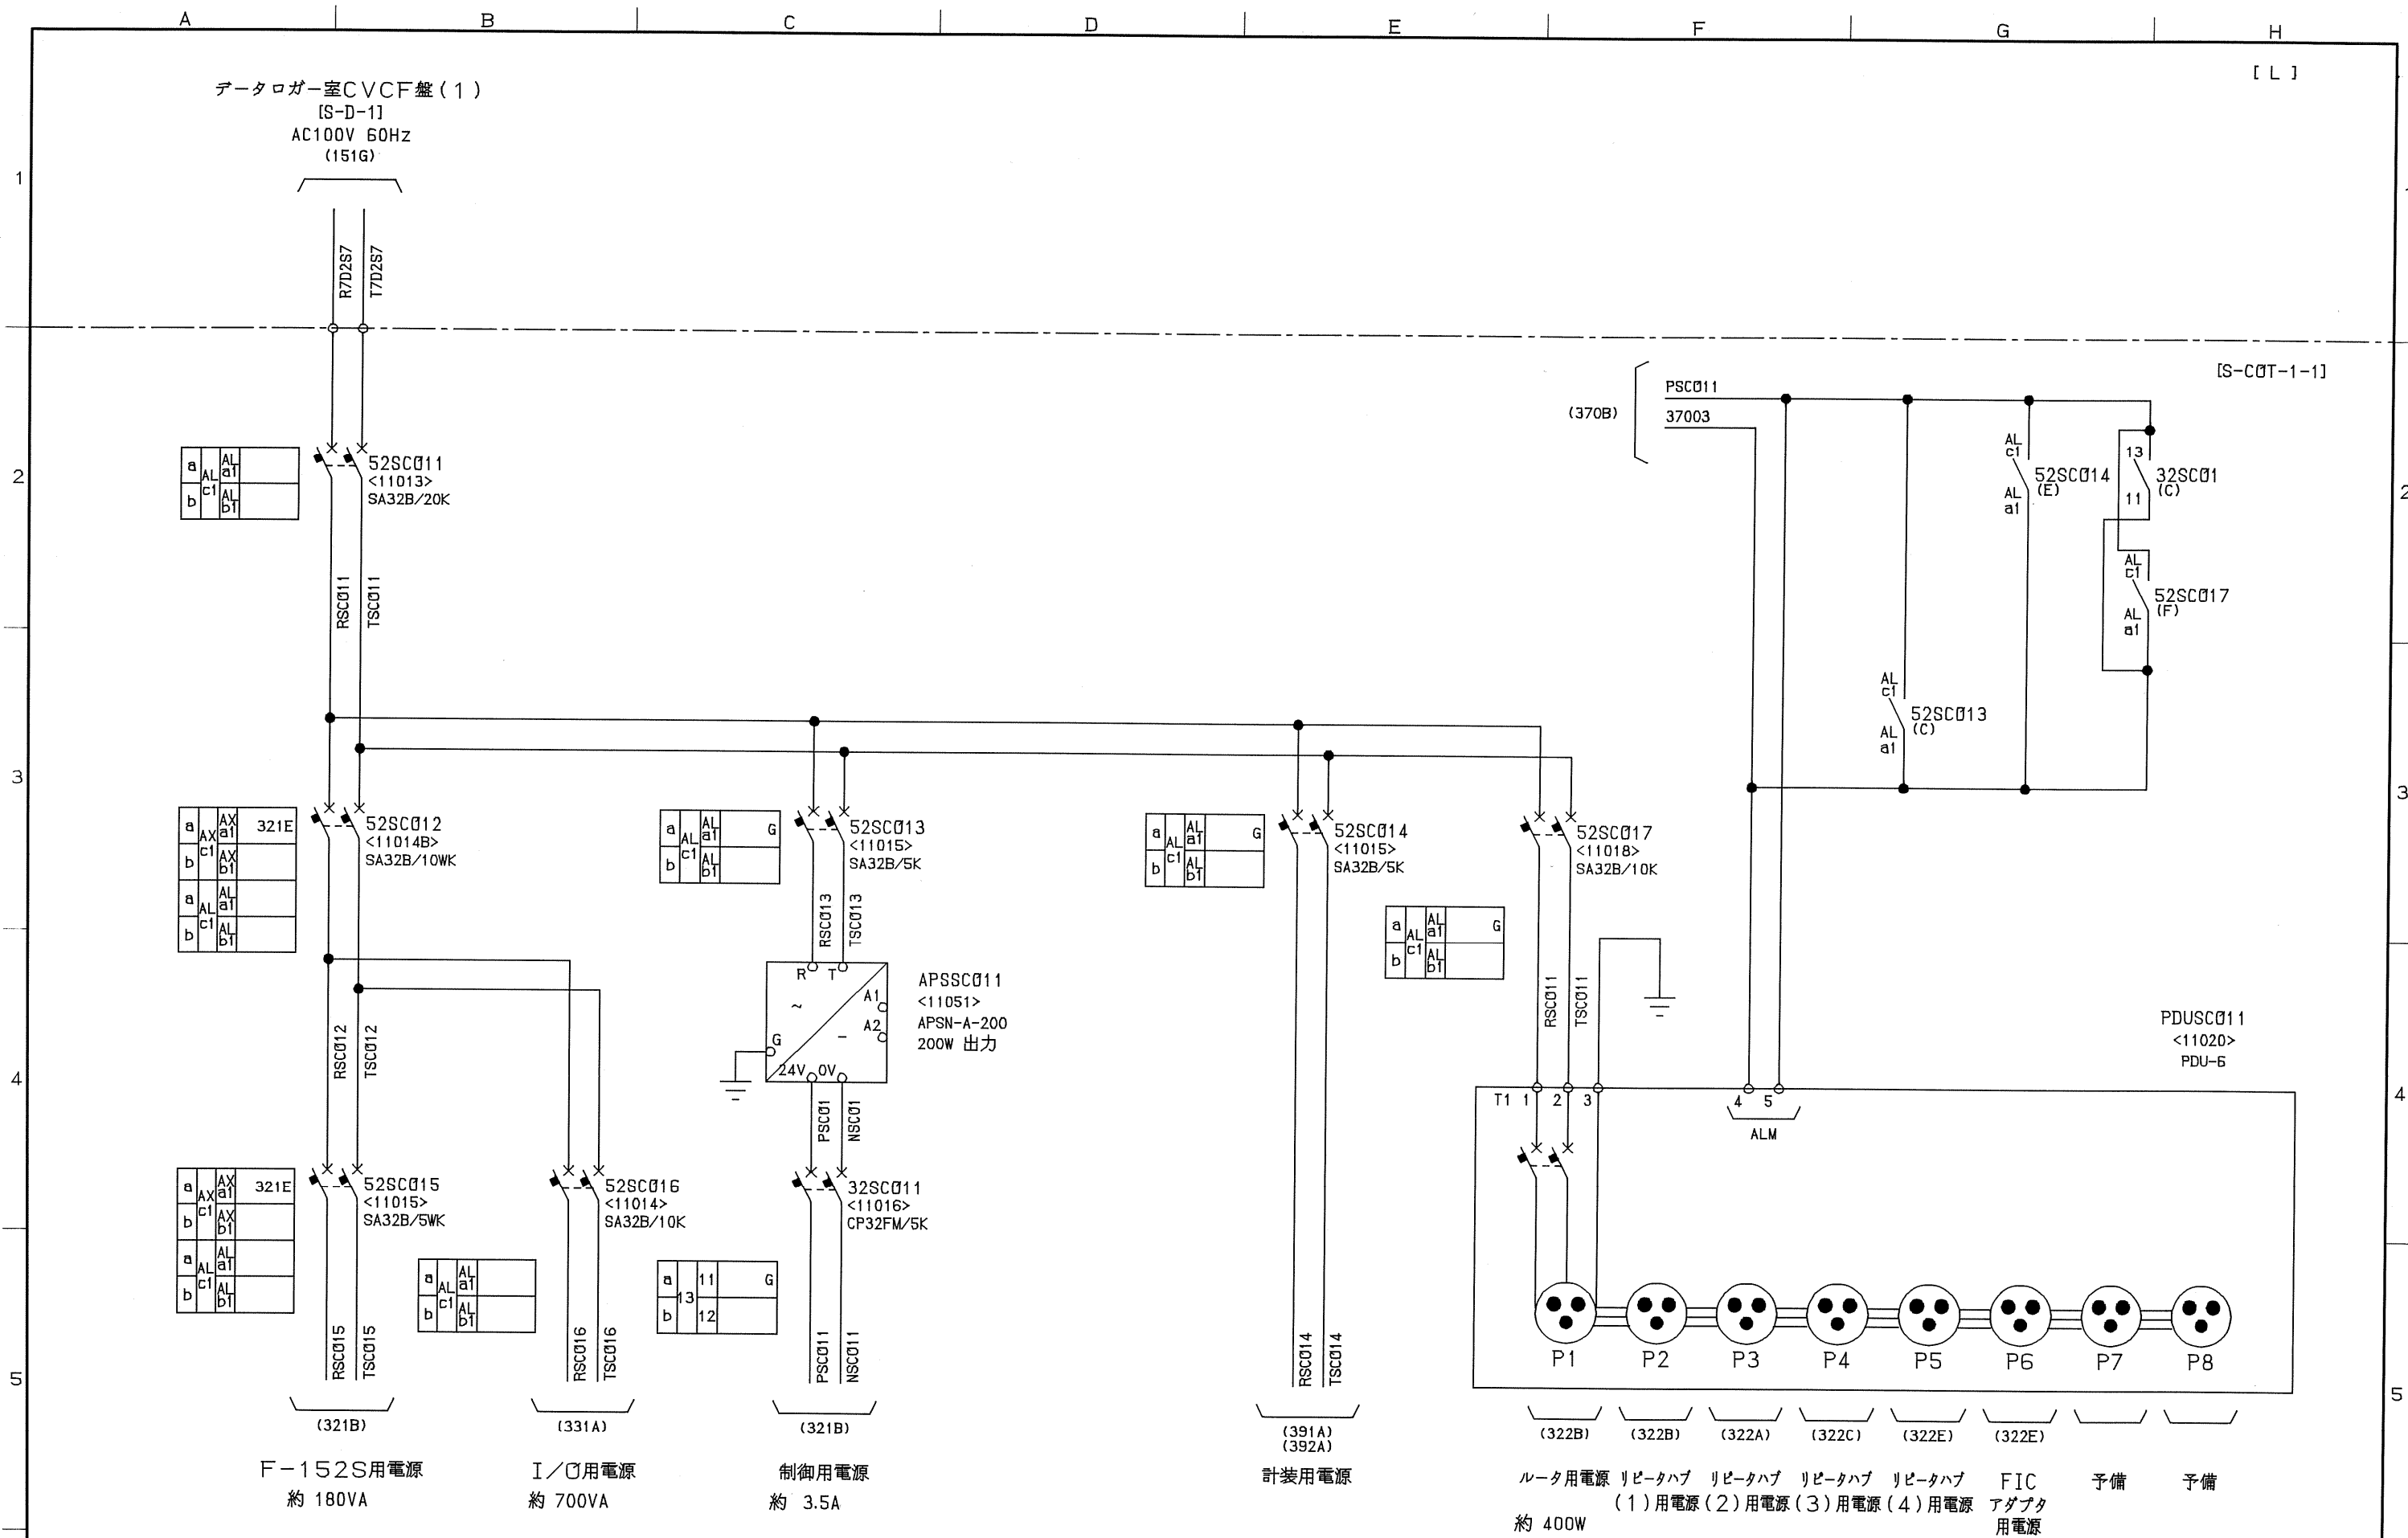

Revisions	○			Date	Name	Fuji Electric Co.,Ltd.	Title	河頭管轄入出力制御装置 電源回路	Ref. Dwg. No.	W 4 2 6 2 9 7	301			g		
	◎	取合い追加	' 01-05-09	折茂	Drawn										1999-12-29	原田
	①	ブレーカ追加、取合い変更	' 00-08-21	野崎	Checked											
	◎	ブレーカトリップ値変更	' 00-06-08	河野												
A		B		C		D		E		F		G		H		

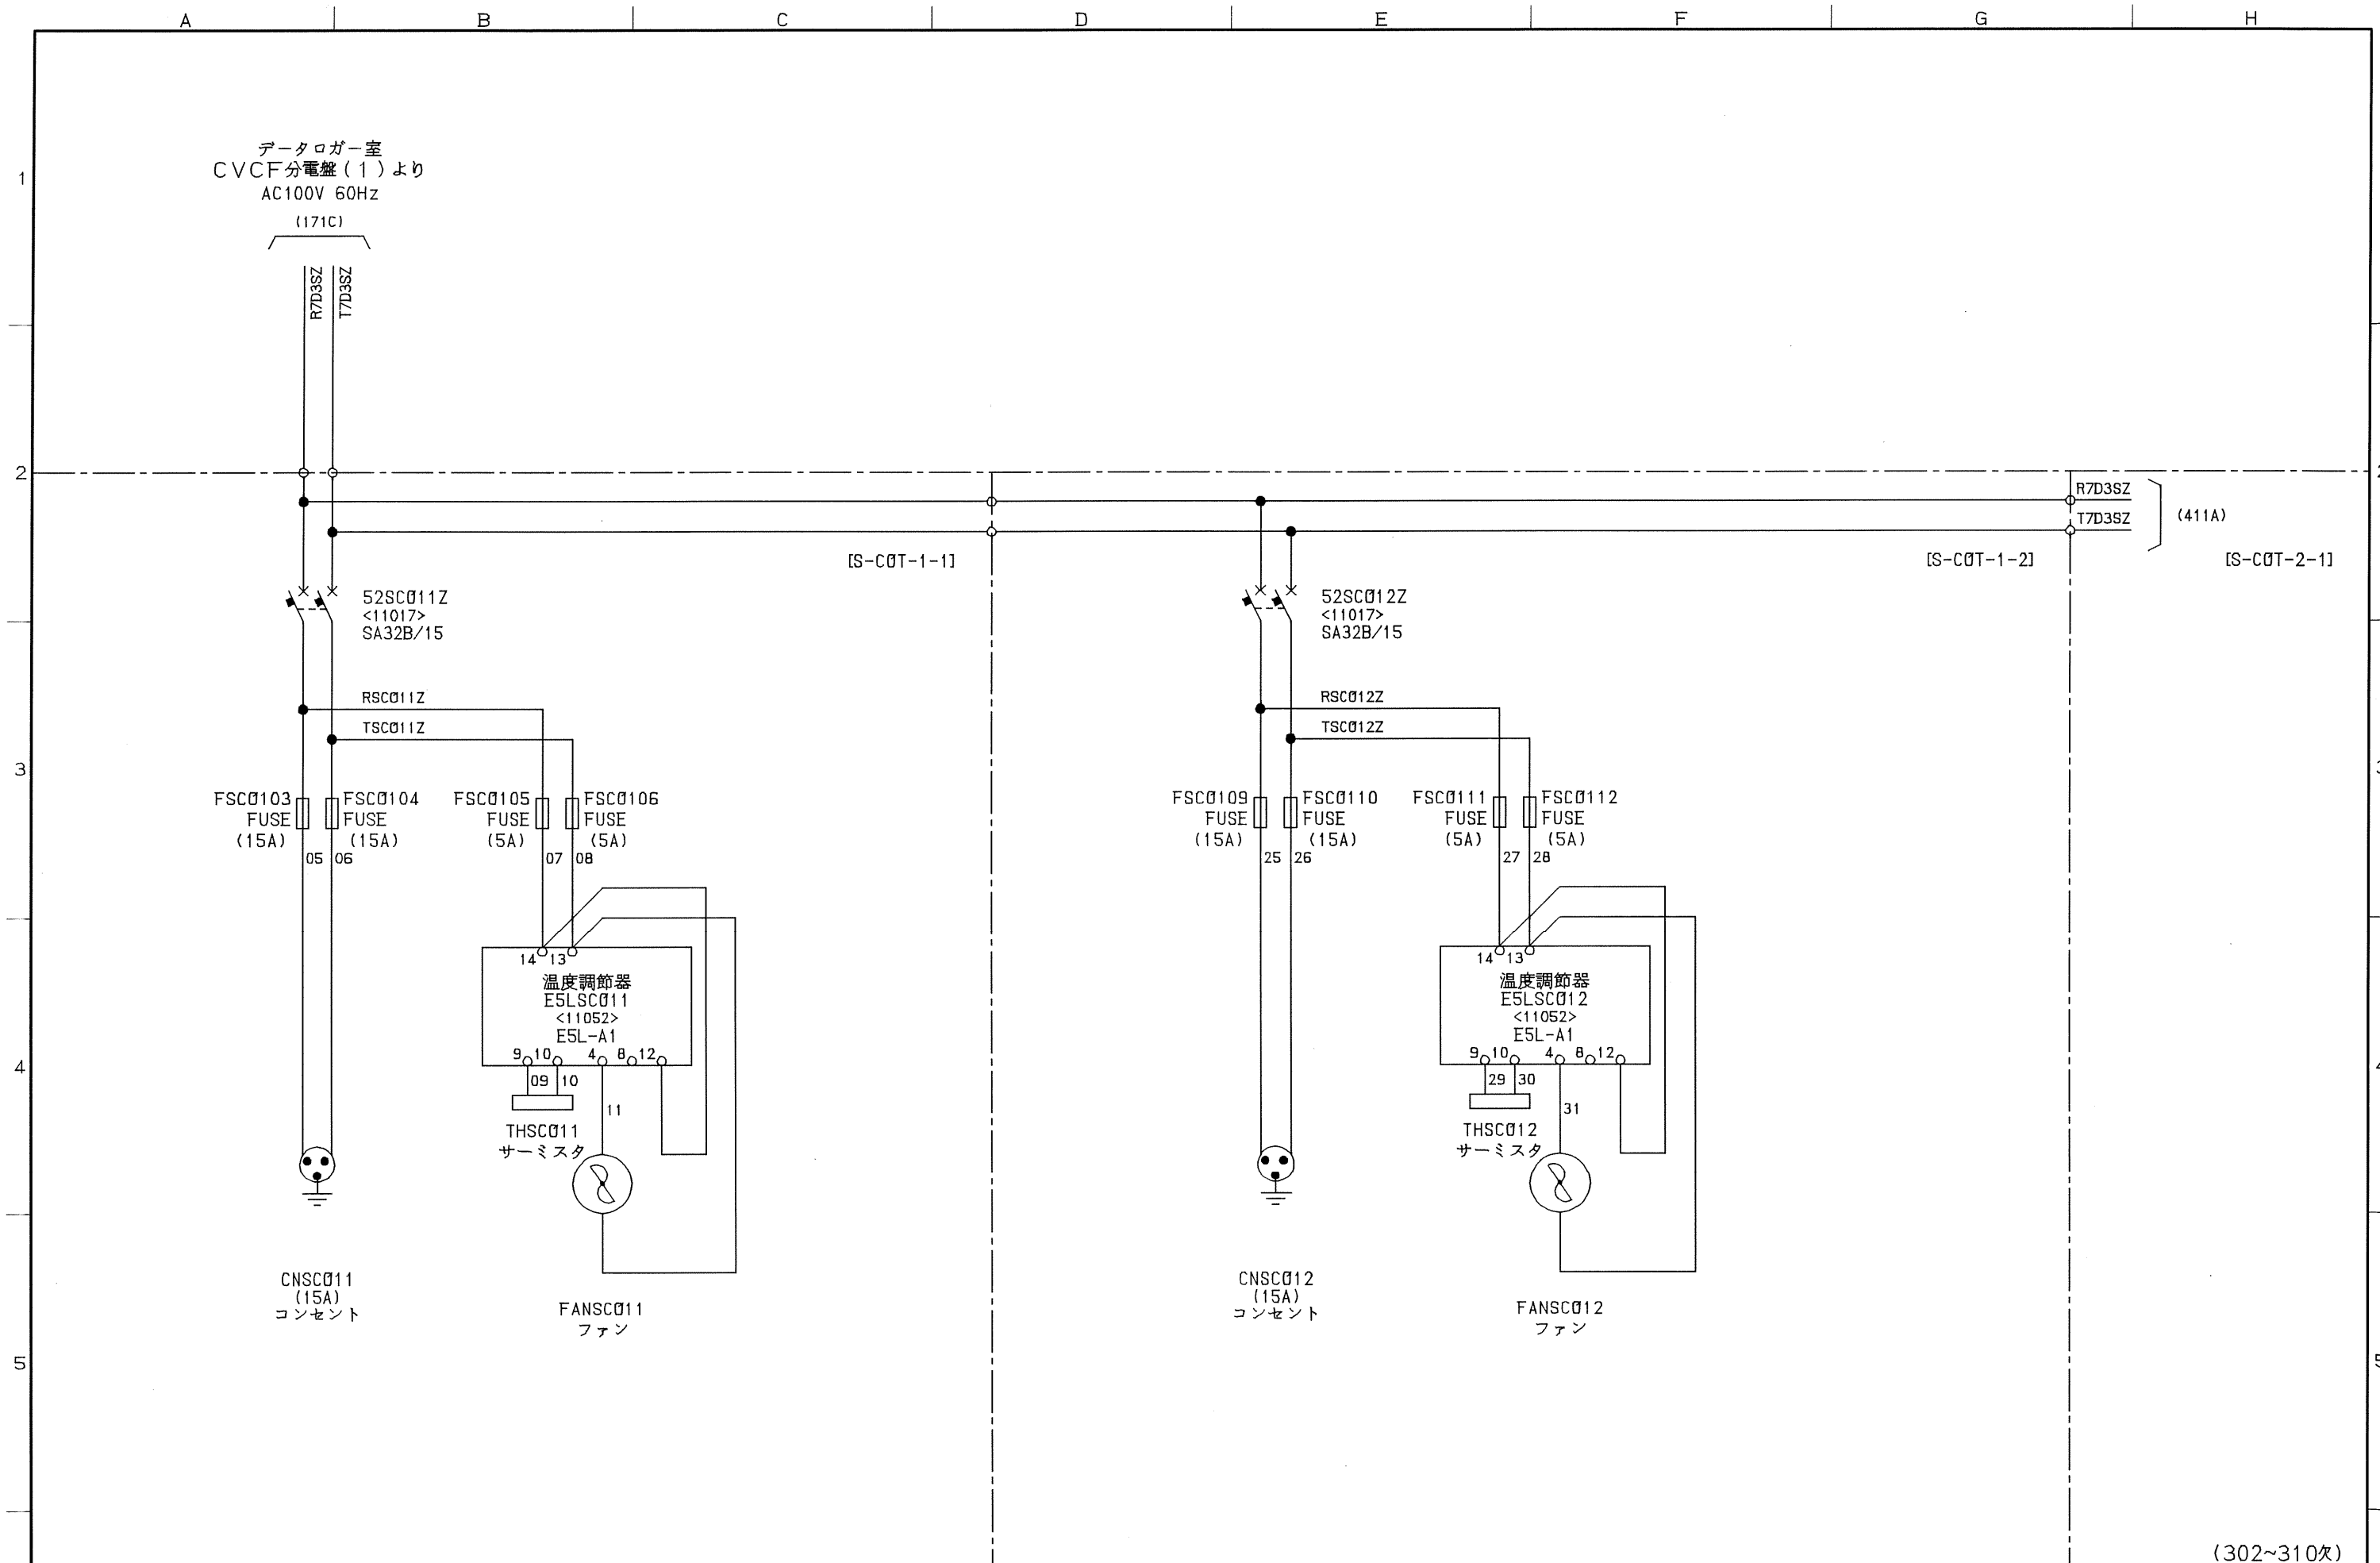

Revisions	⑤	現地試験フォロー	' 01-06-15	折茂		Date	Name	Fuji Electric Co.,Ltd.	Title	河頭管轄入出力制御装置 雑電源回路	Ref. Dwg. No.	W 4 2 6 2 9 7	311	Q P	
	④	社内試験フォロー	' 00-11-09	折茂	Drawn	原田									
	③	取合いフォロー	' 00-08-21	野崎	Checked										
	②	ケアレスミス修正	' 00-06-08	河野											
A		B		C		D		E		F		G		H	


D


Title


Ref. Dwg. No.	
---------------	--


4


準構成図

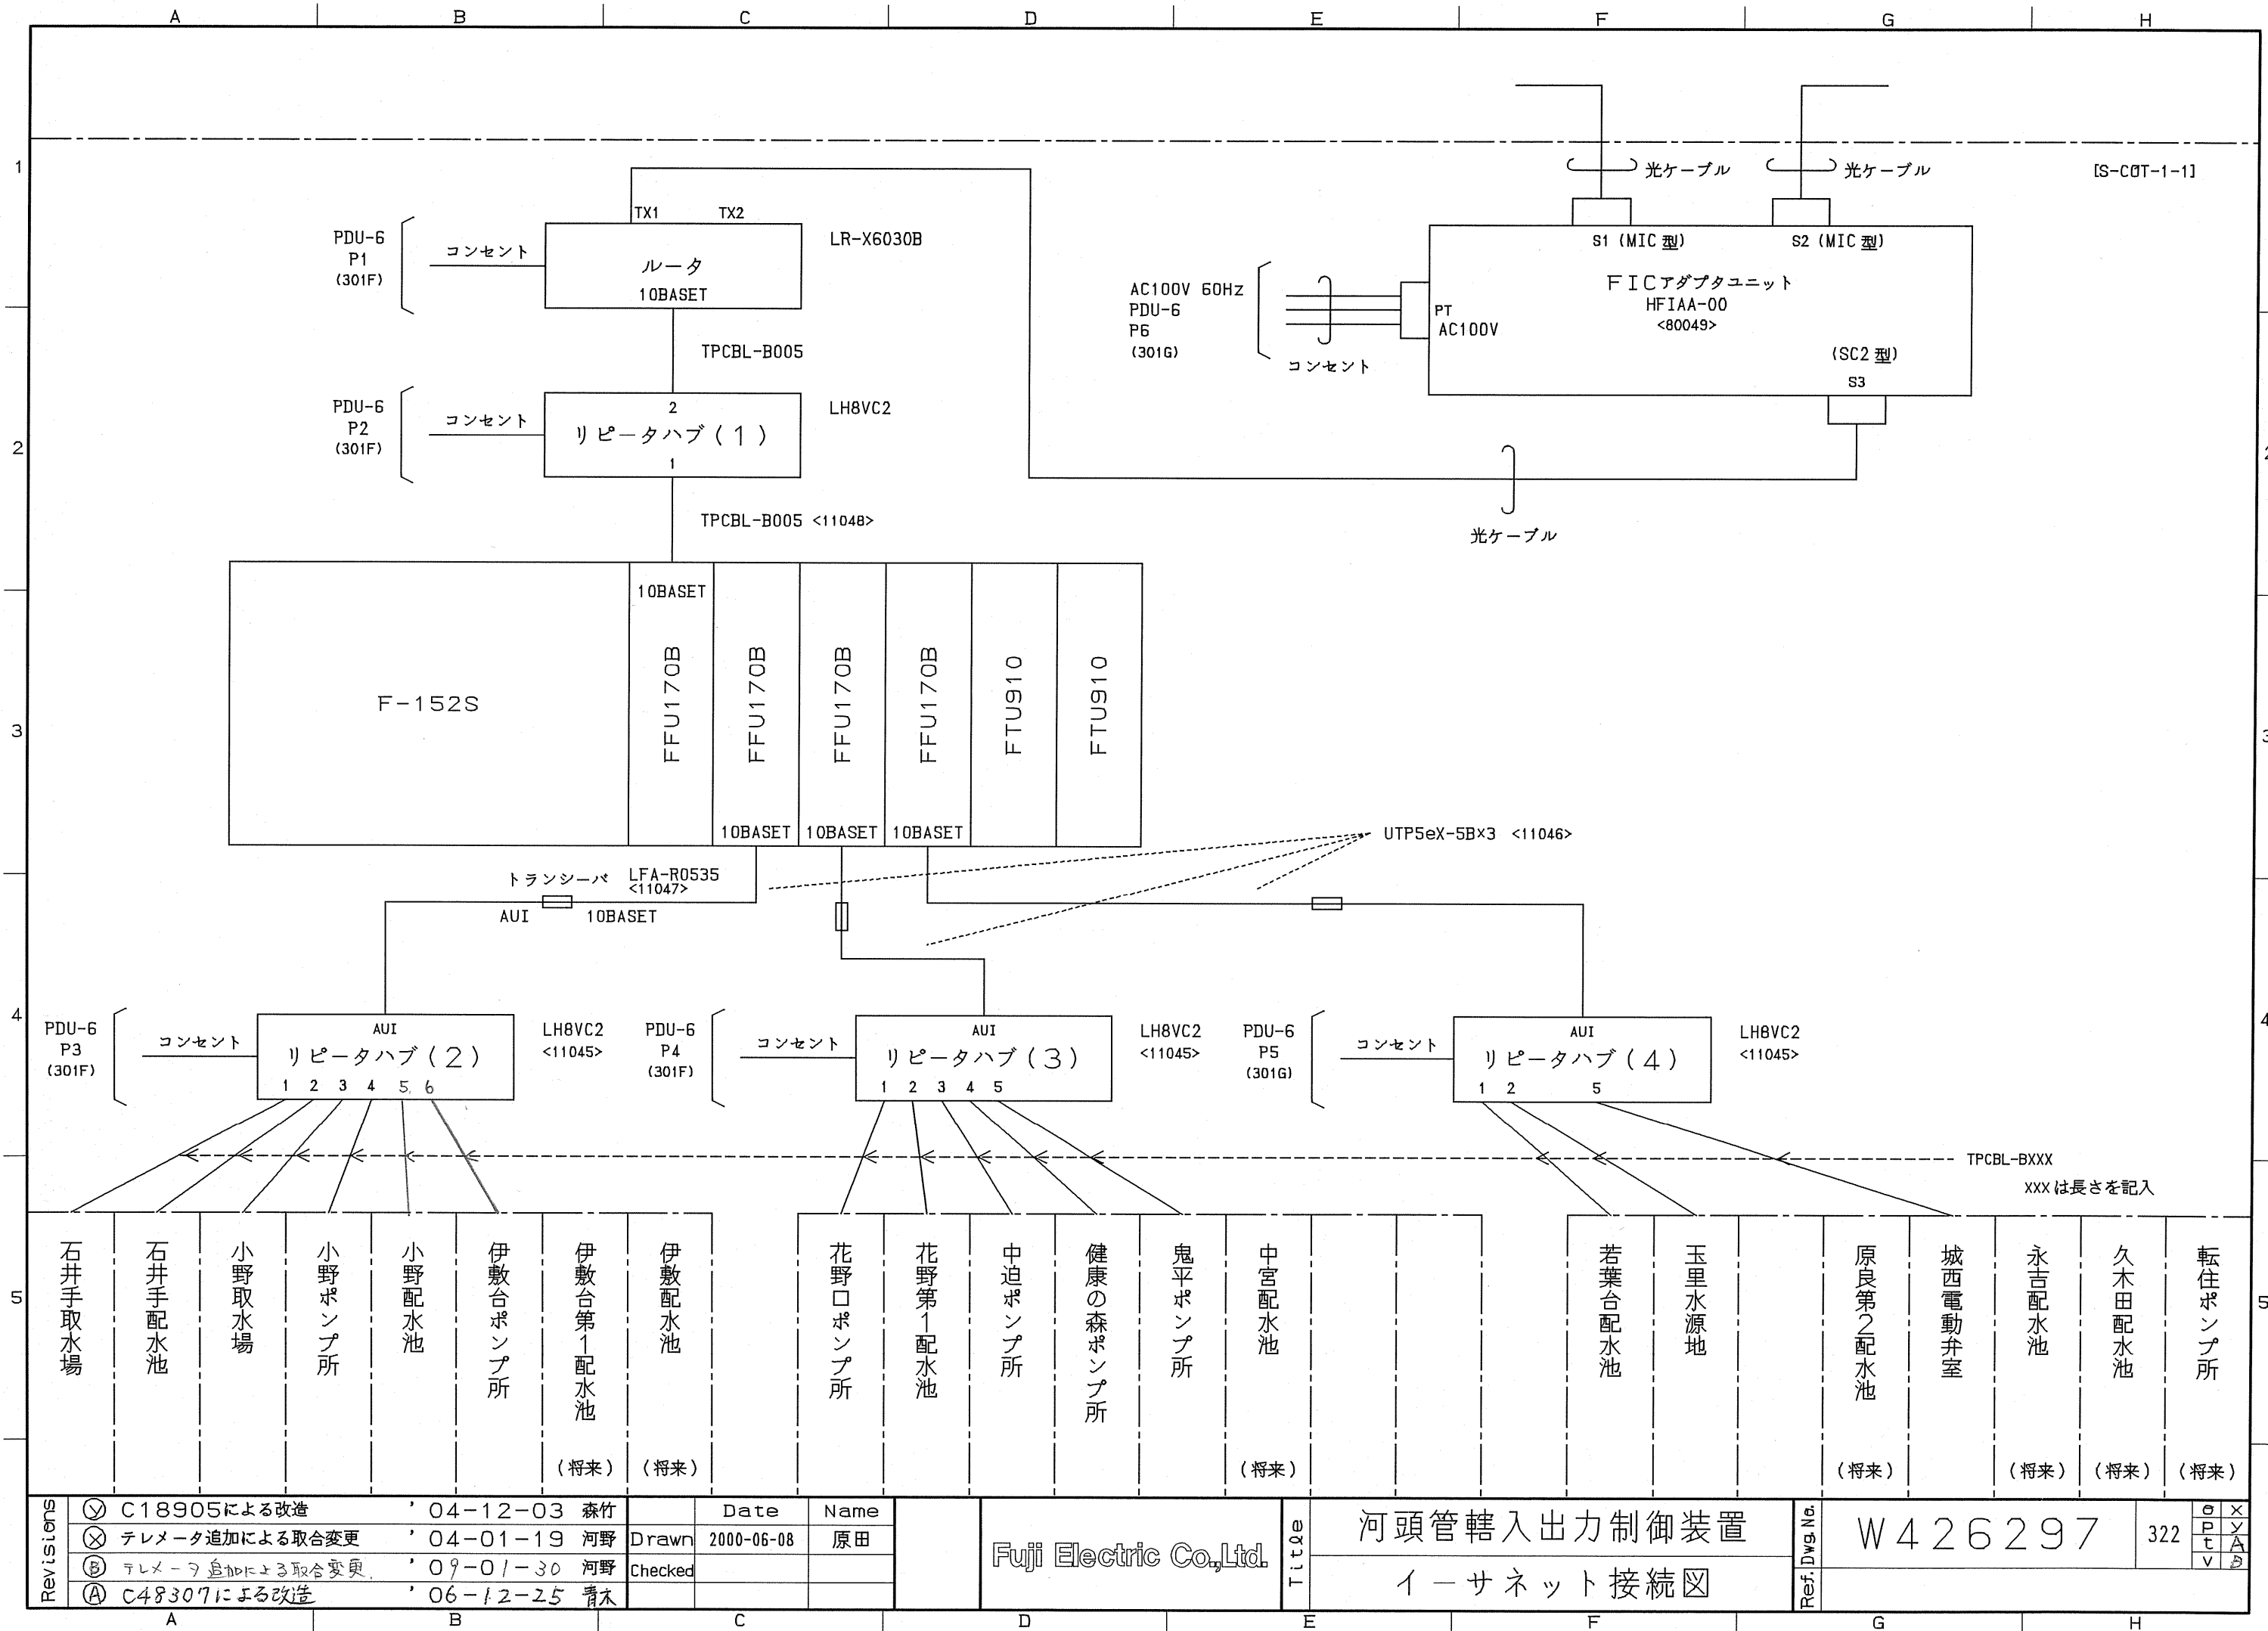


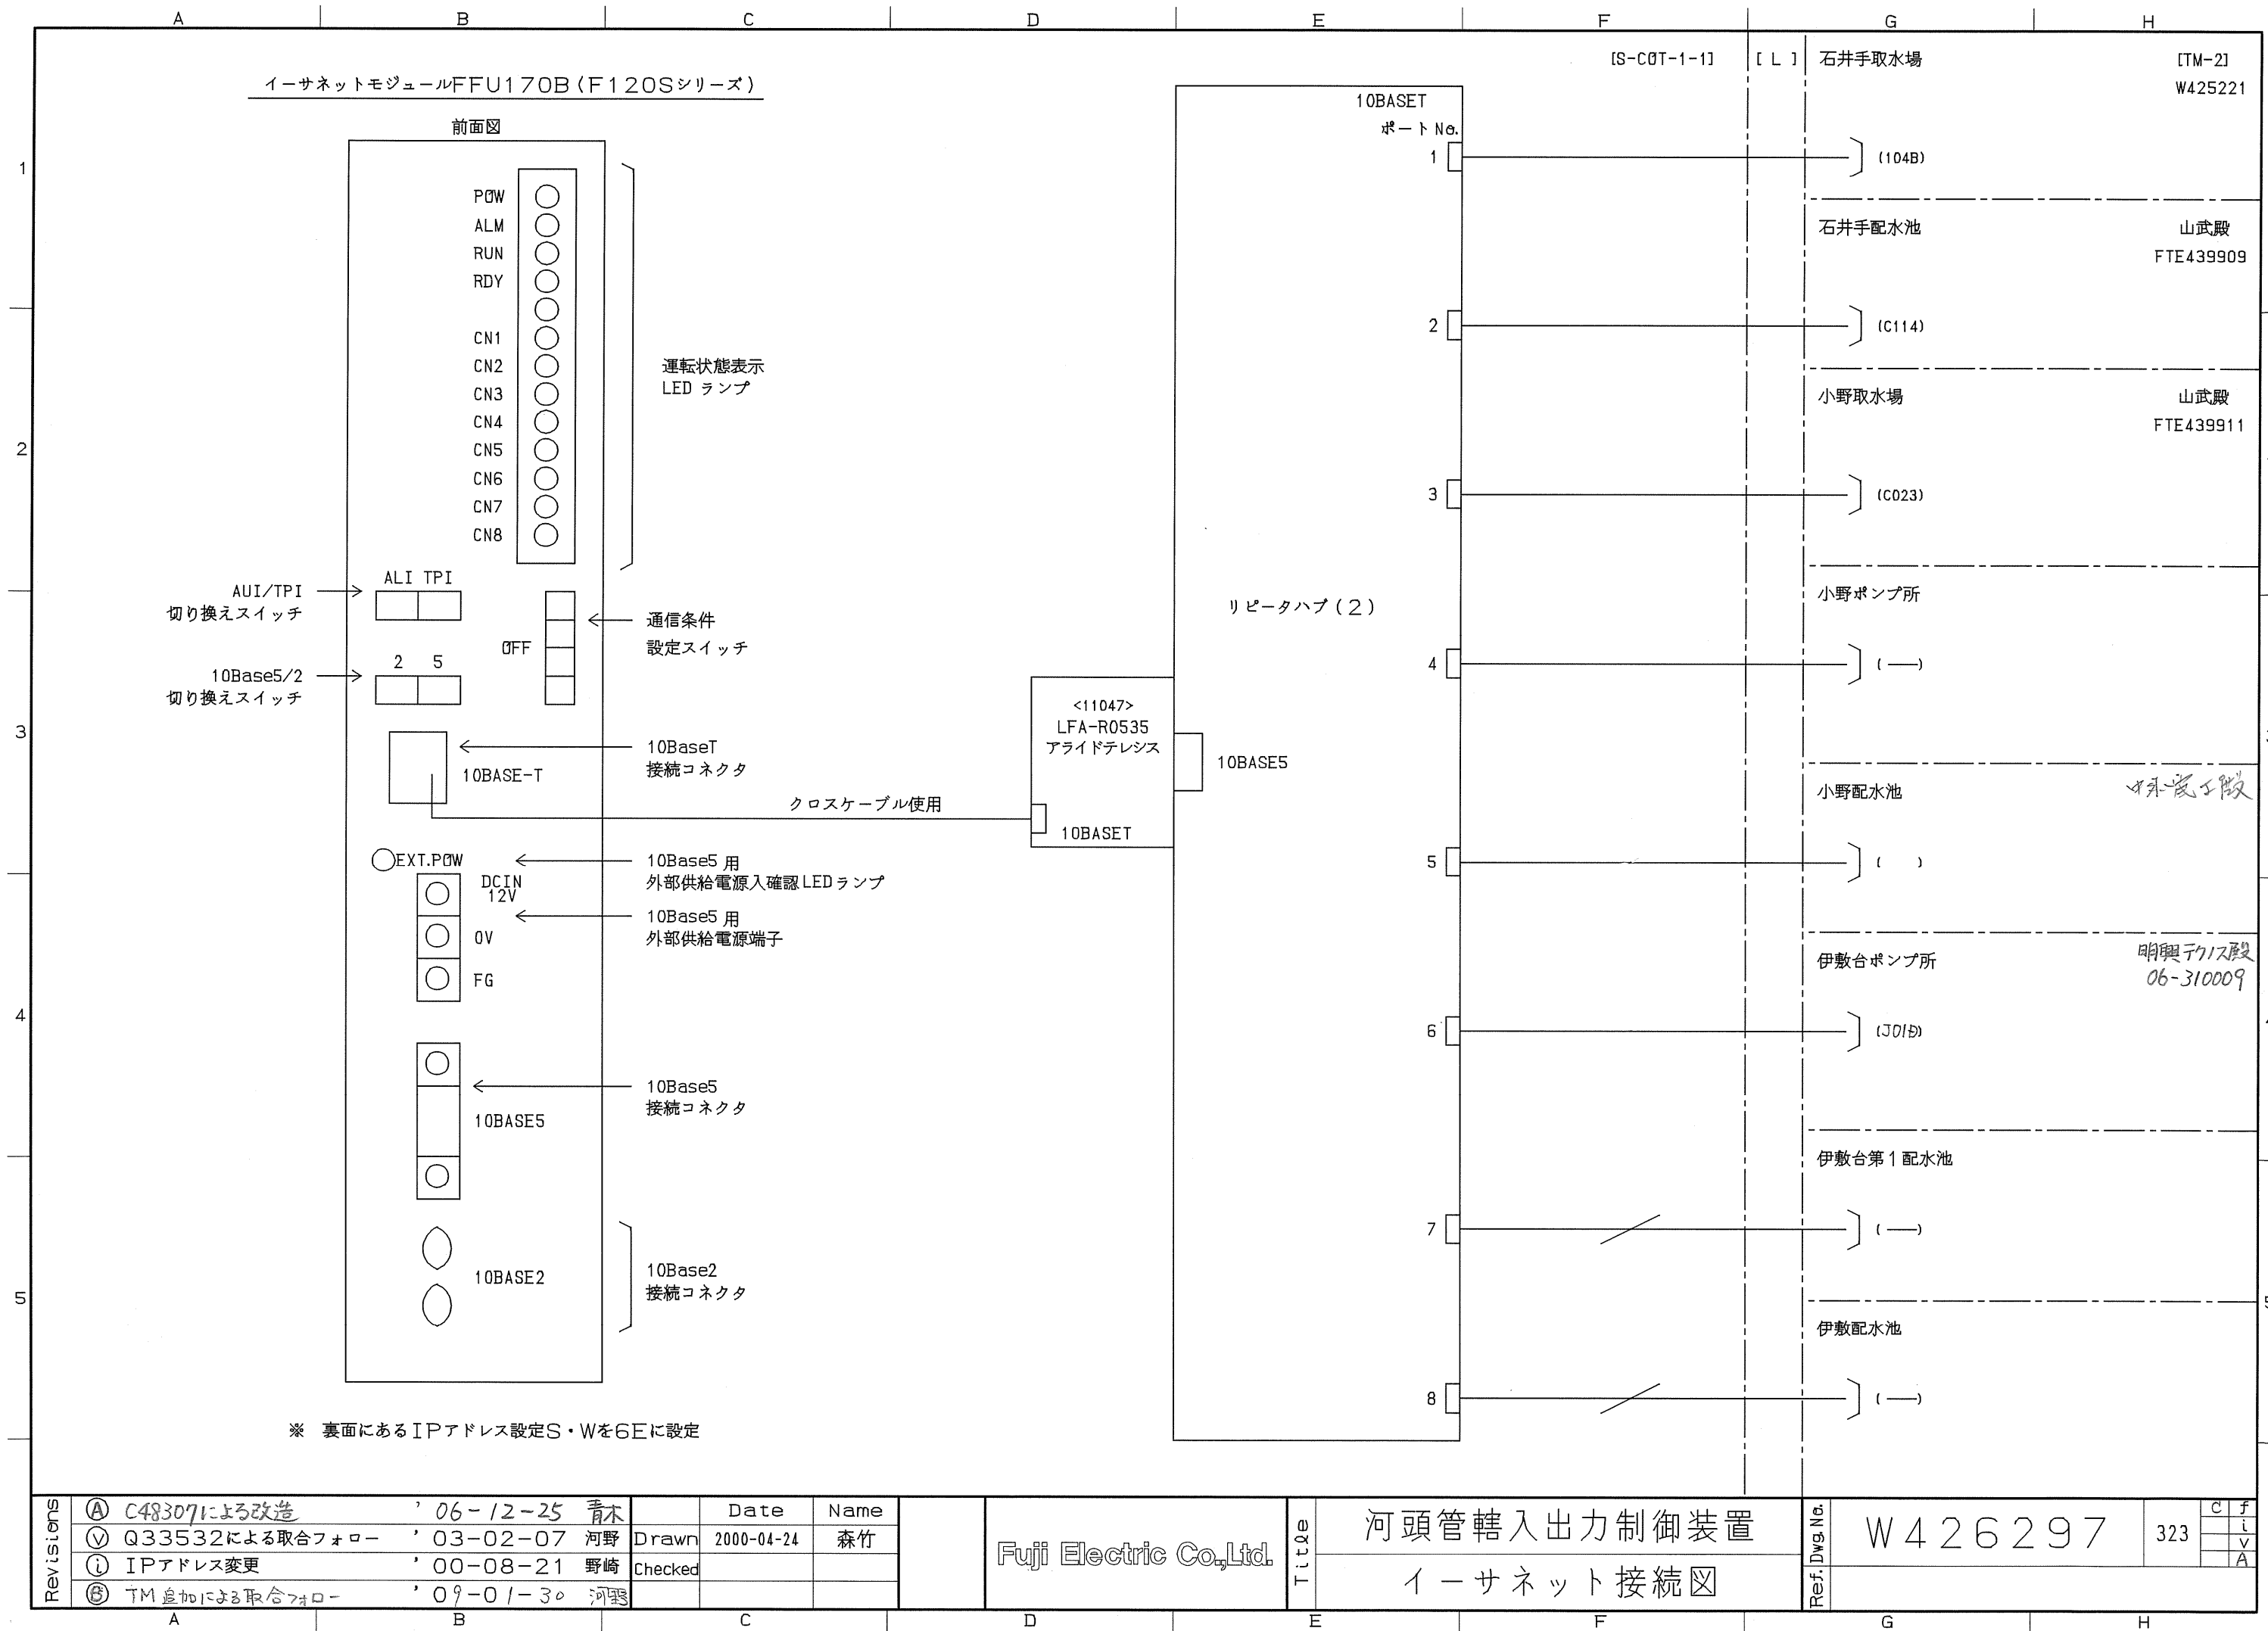


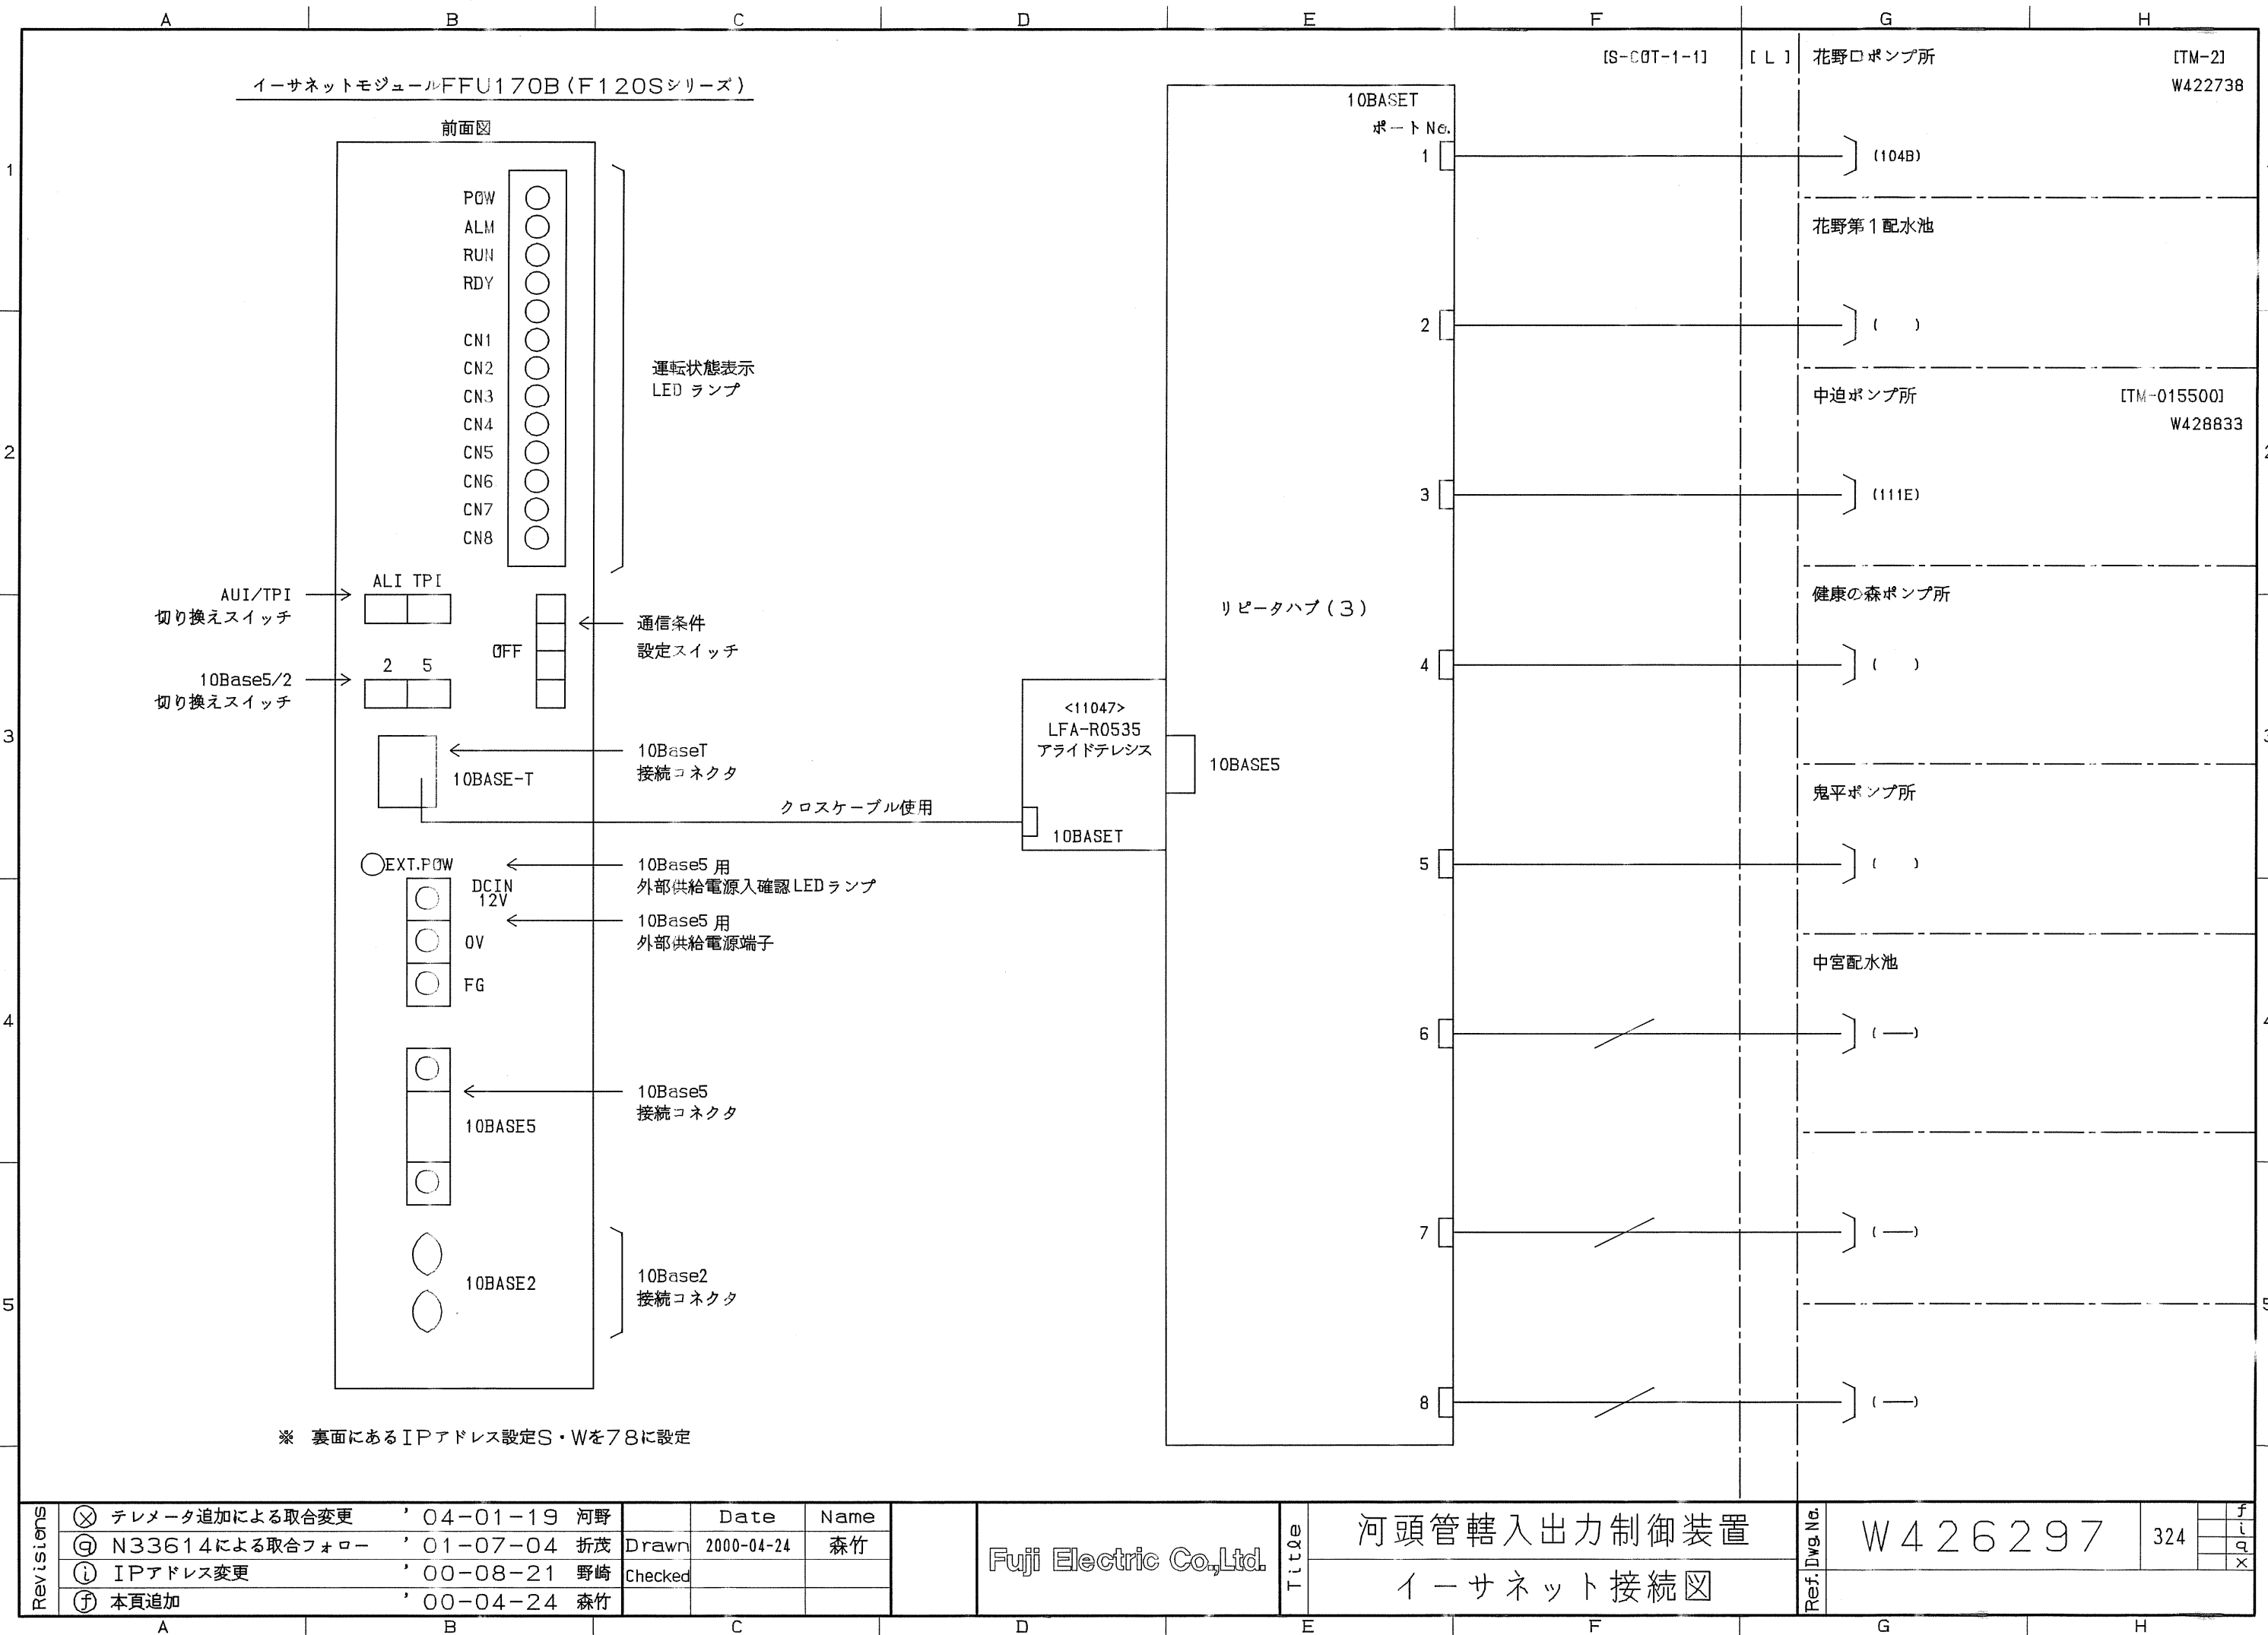


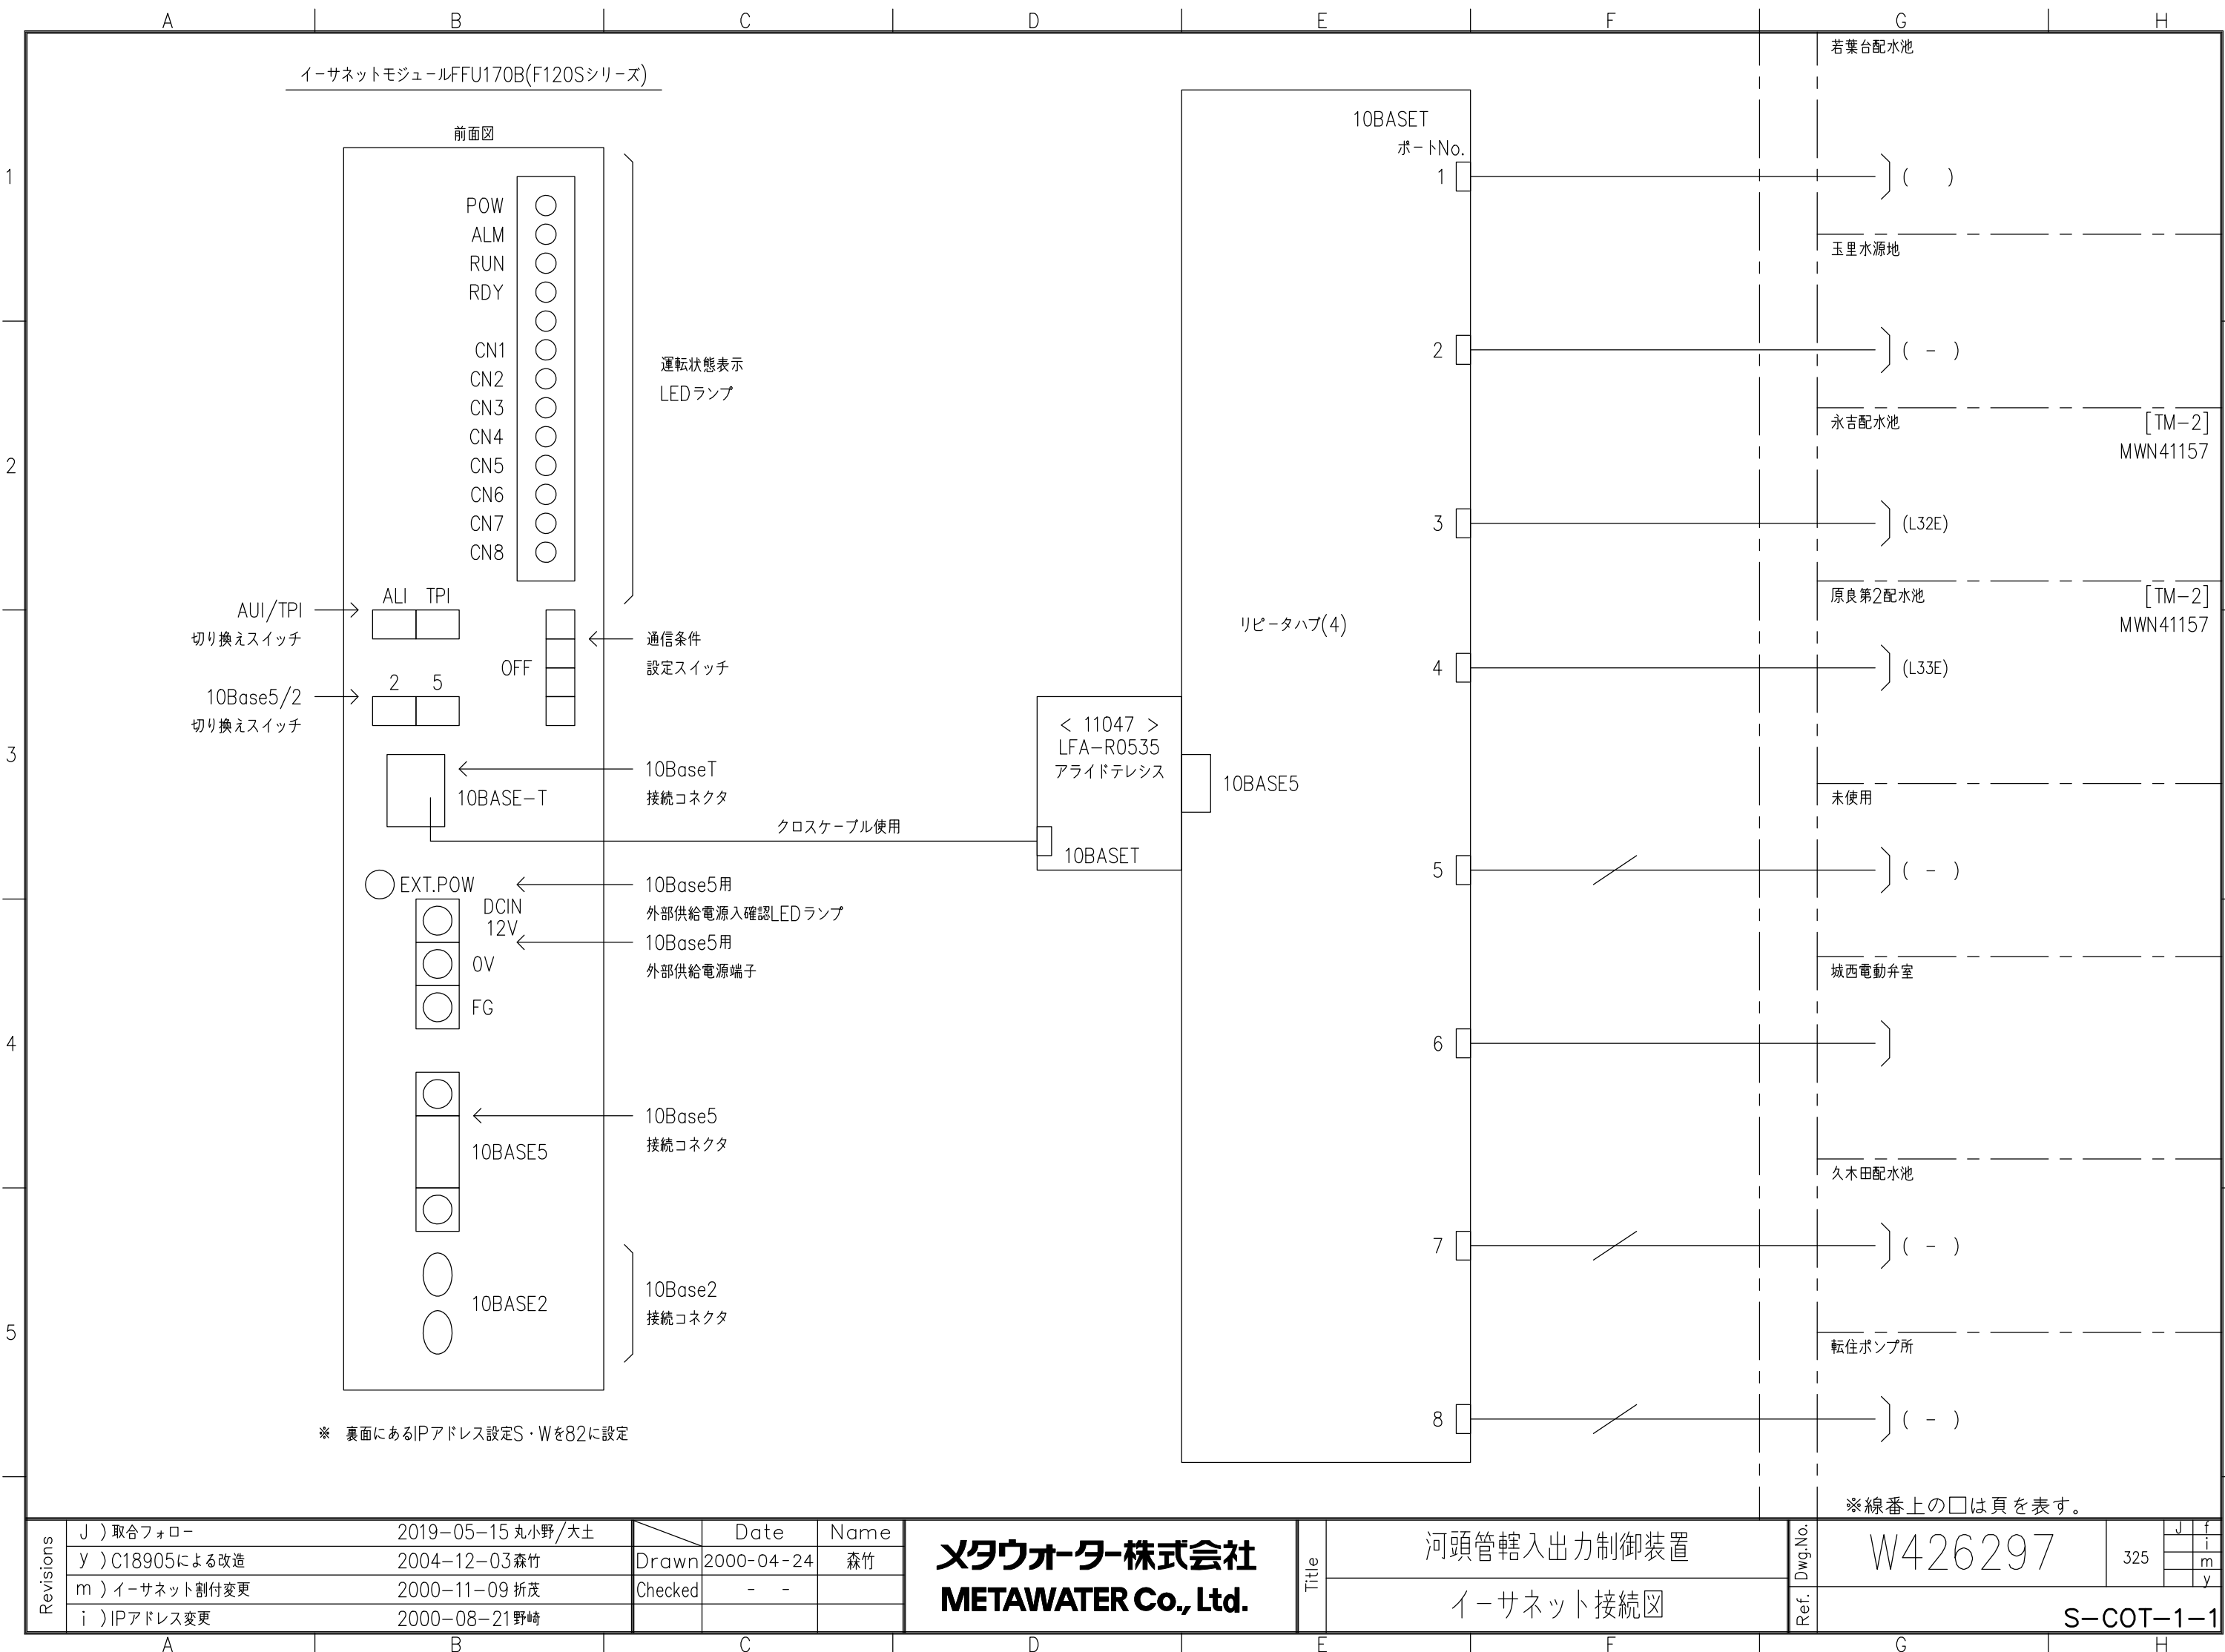



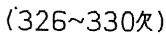



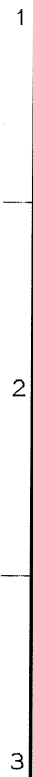


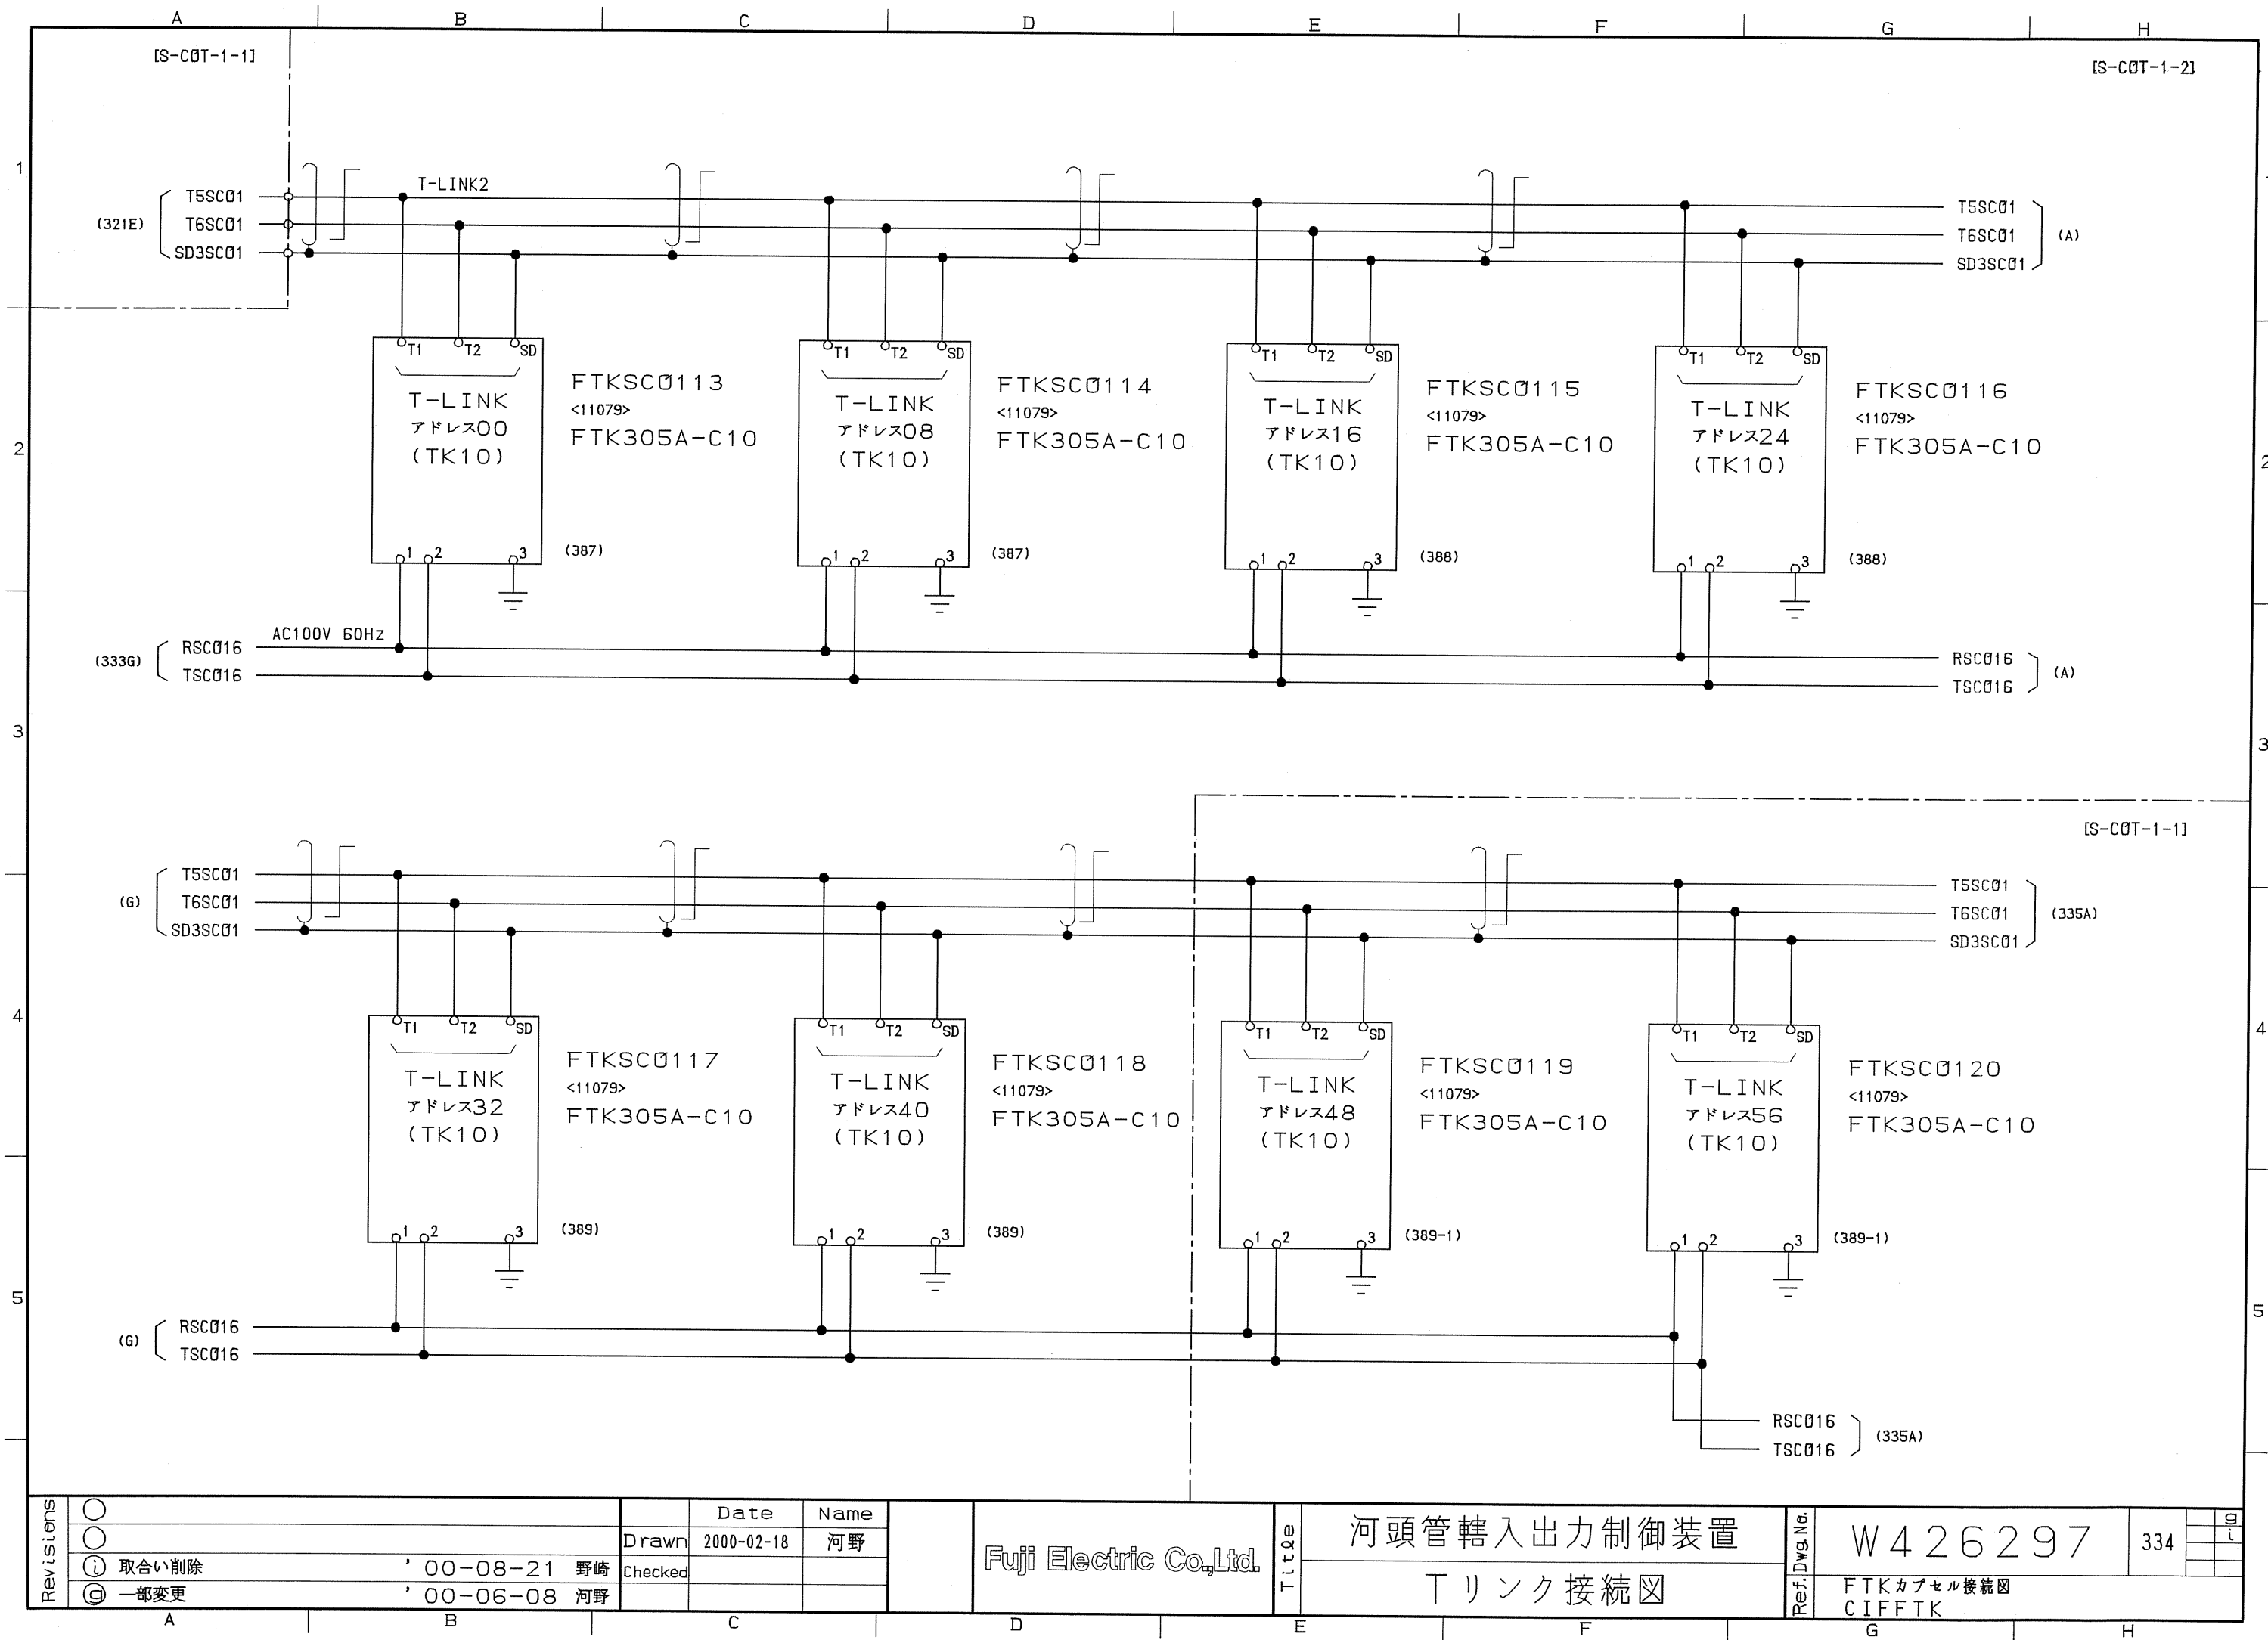


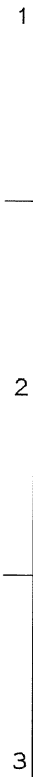




4	5
---	---

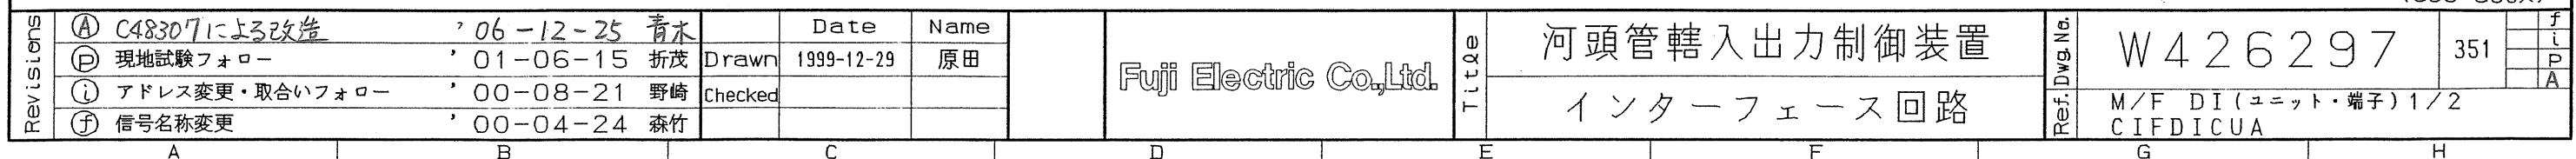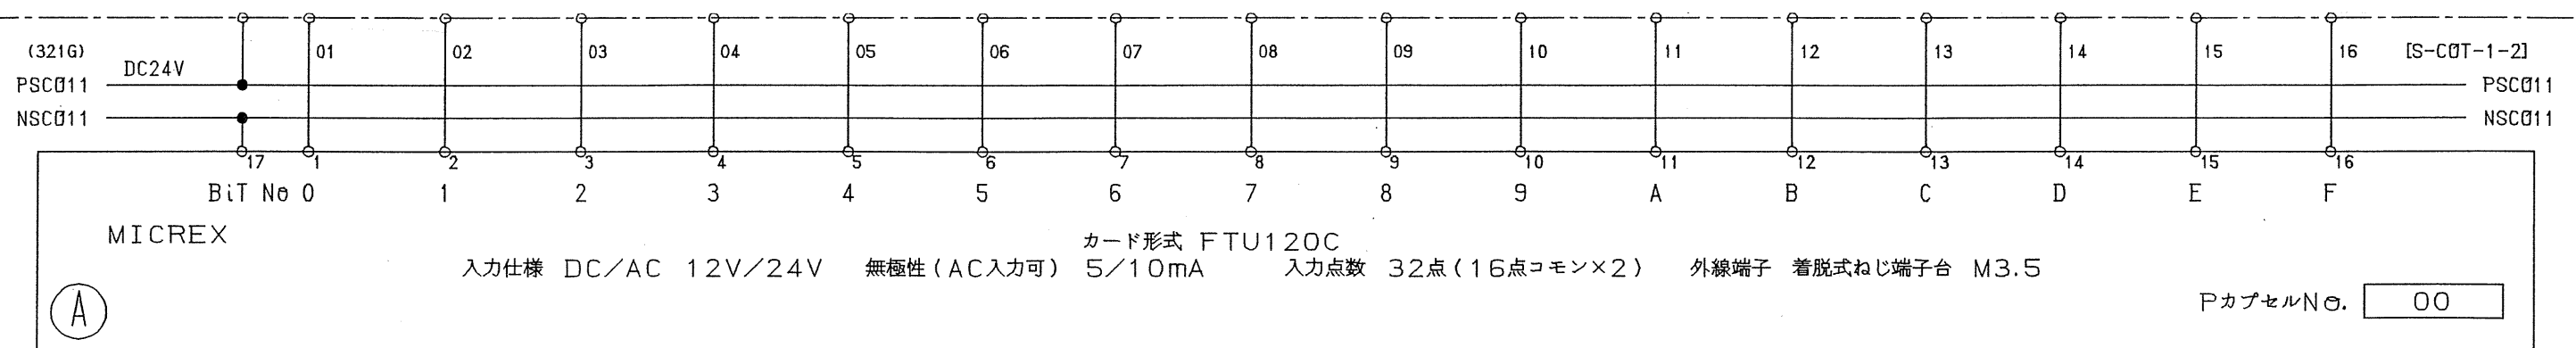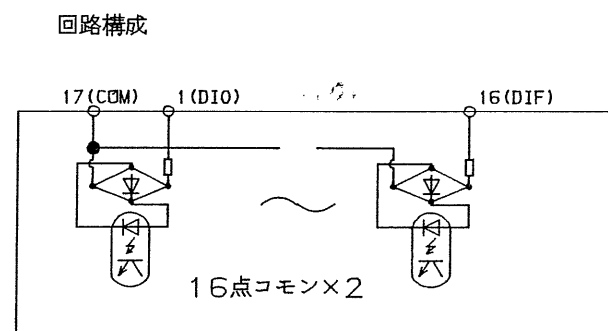

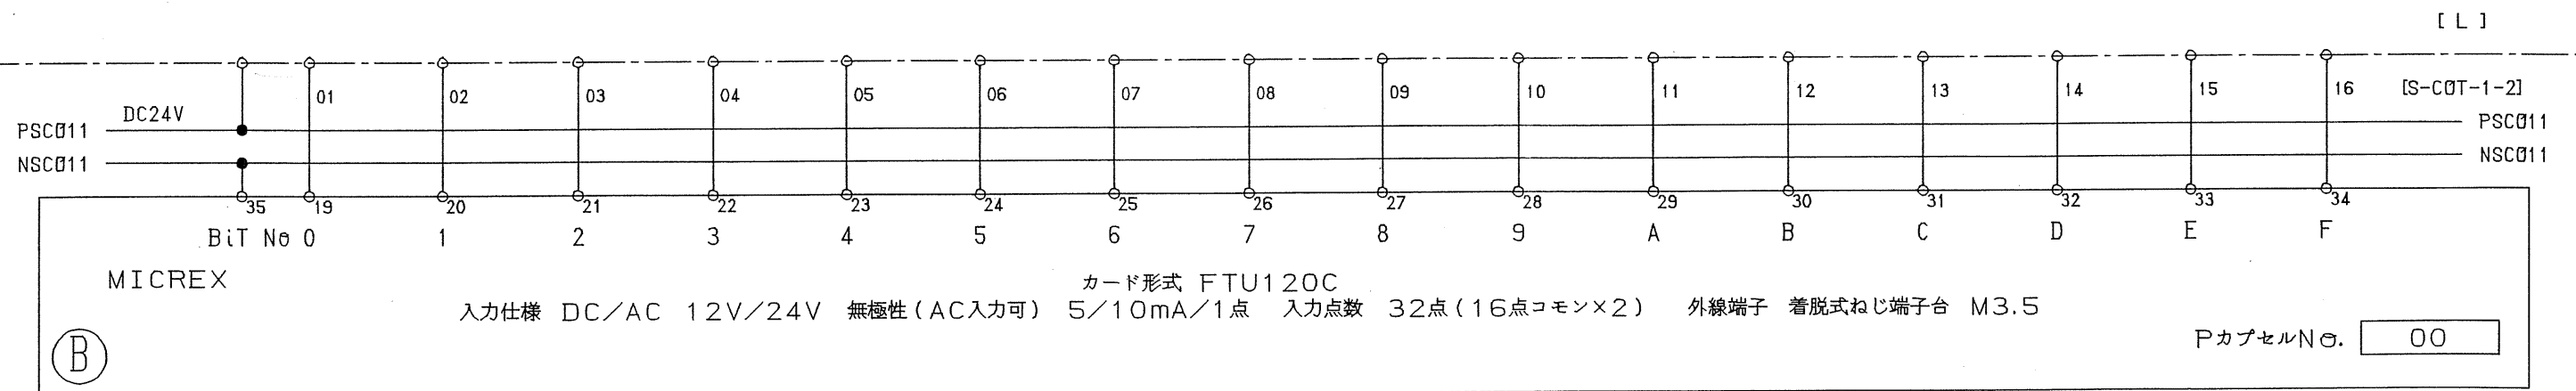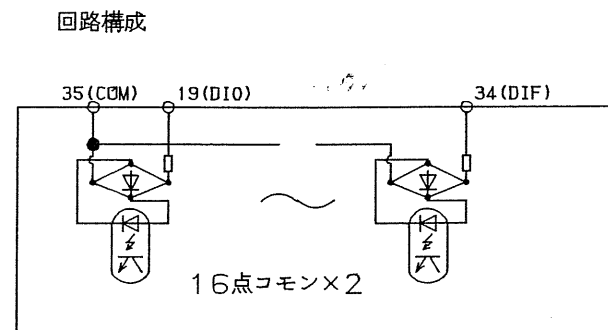


Revisions	④	C483071による改造	'06-12-25	青木	Date	Name	Fuji Electric Co.,Ltd.	Title	河頭管轄入出力制御装置 インターフェース回路	Ref. Dwg. No.	W426297	352	P i A		
	⑤	現地試験フォロー	'01-06-15	折茂	Drawn	原田									
	⑥	アドレス変更・信号削除	'00-08-21	野崎	Checked										
	⑦	信号名称変更	'00-04-24	森竹											
A		B		C		D		E		F		G		H	

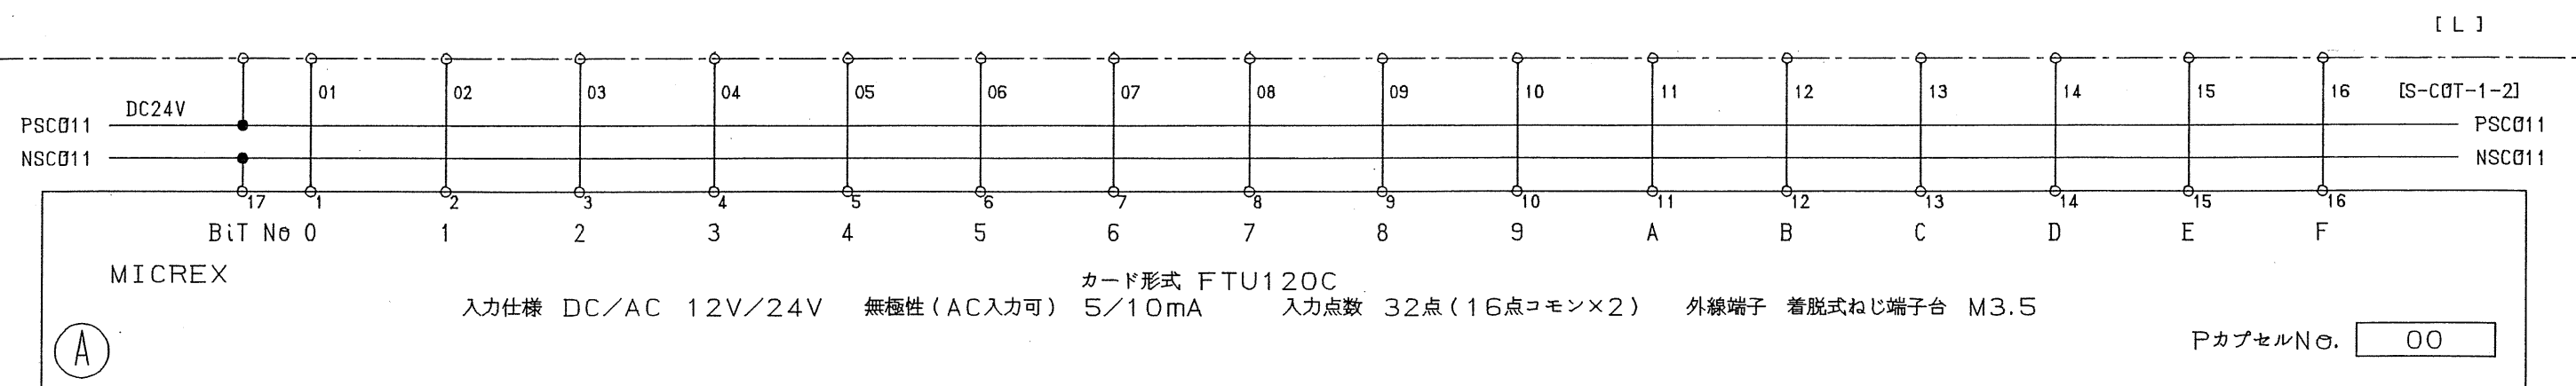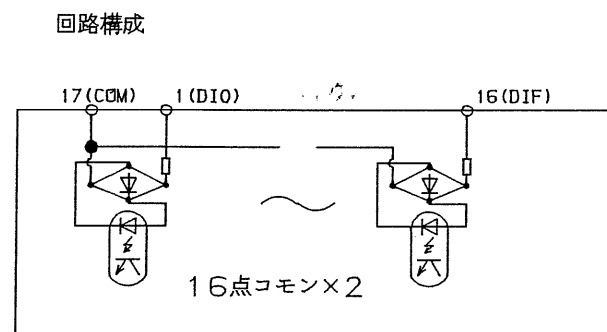

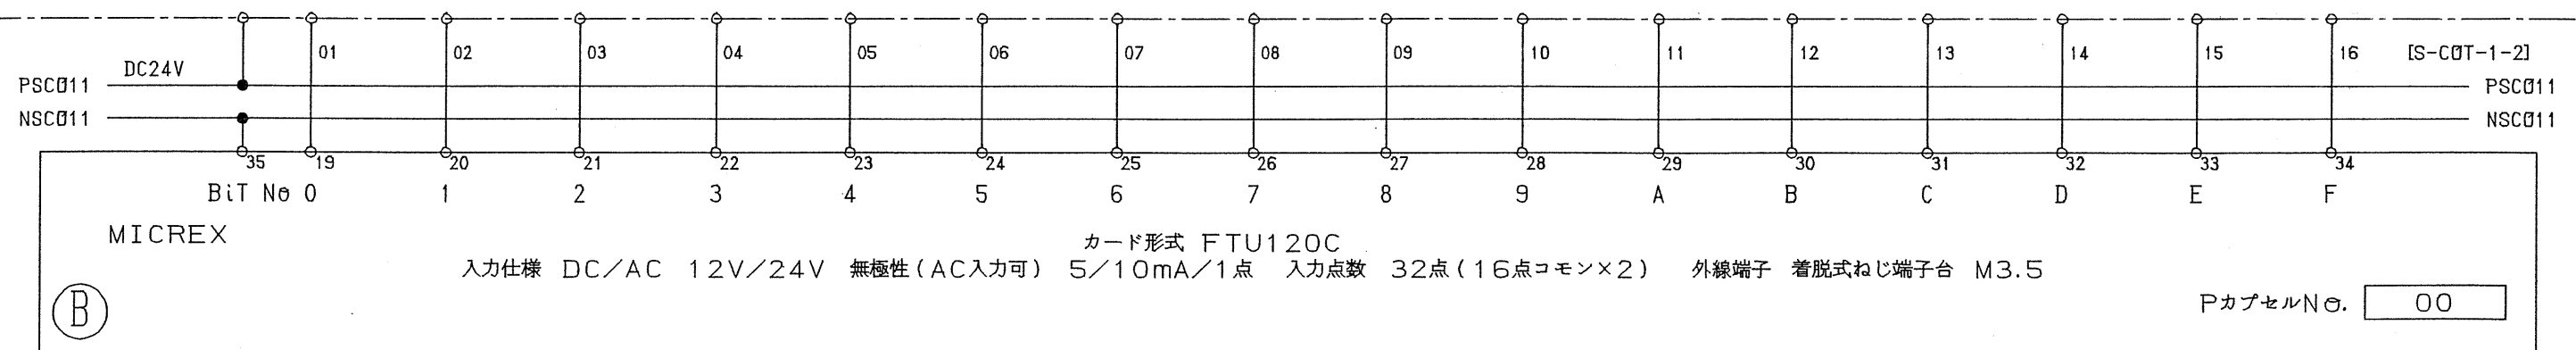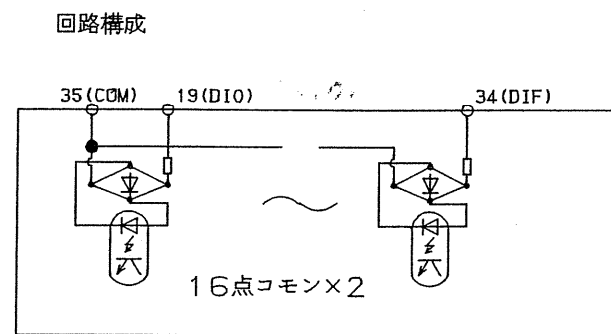


	P)現地試験フォロー	'01-06-15	折茂		Date	Name		Fuji Electric Co.,Ltd.	Title	河頭管轄入出力制御装置 インターフェース回路	Dwg.No.	W426297	354	P A K M
Revisions	(m)取合いフォロー	'00-11-09	折茂		Drawn	1999-12-29	原田							
	(K)信号追加	'00-09-20	折茂											
	(i)アドレス変更・信号名称変更	'00-08-21	野崎		Checked							M/F DI(ユニット・端子)2/2		
	(A)C48307による改造	'06-12-25	青木								CIFDICUB			
	A	B	C	D	E	F	G	H	I	J	K	L	M	N



回路構成

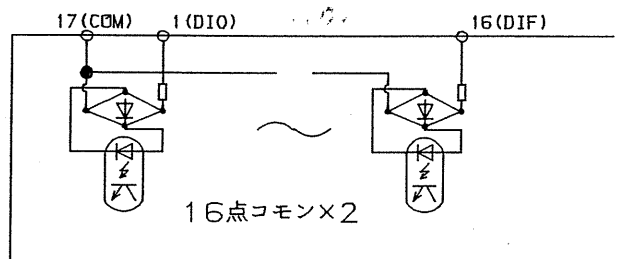


アドレス	項目名称	備考
I.0400	予備	
I.0401		
I.0402		
I.0403		
I.0404		
I.0405		
I.0406		
I.0407		
I.0408		
I.0409		
I.040A		
I.040B		
I.040C		
I.040D		
I.040E		
I.040F	↓	

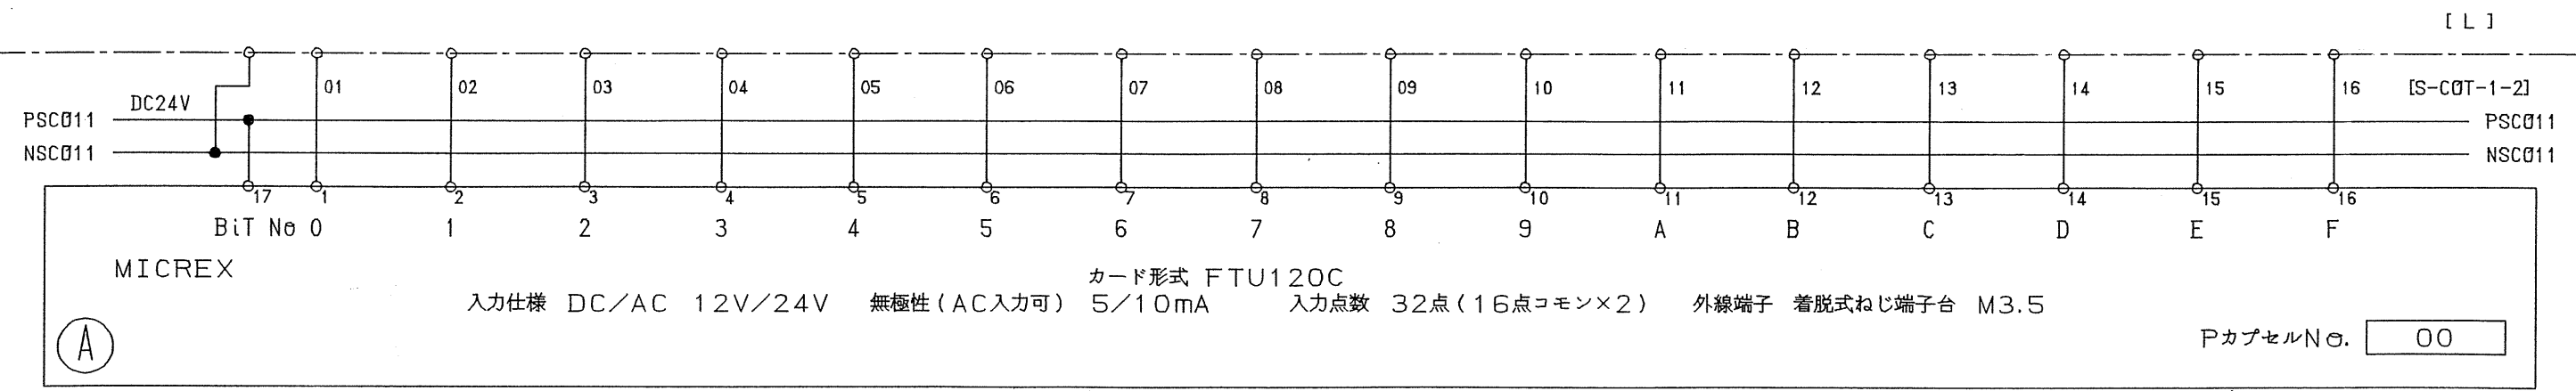


Revisions	① 現地試験フォロー	01-06-15	折茂		Date	Name	Fuji Electric Co., Ltd.	河頭管轄入出力制御装置 インターフェース回路	Ref. Dwg. No. W426297	355	M/F DI (ユニット・端子) 1/2 CIFDICUA
	② コモン変更	00-09-06	折茂	Drawn		原田					
	③ アドレス変更・取合いフォロー	00-08-21	野崎	Checked							
	④ C48307による改造	06-12-25	青木								

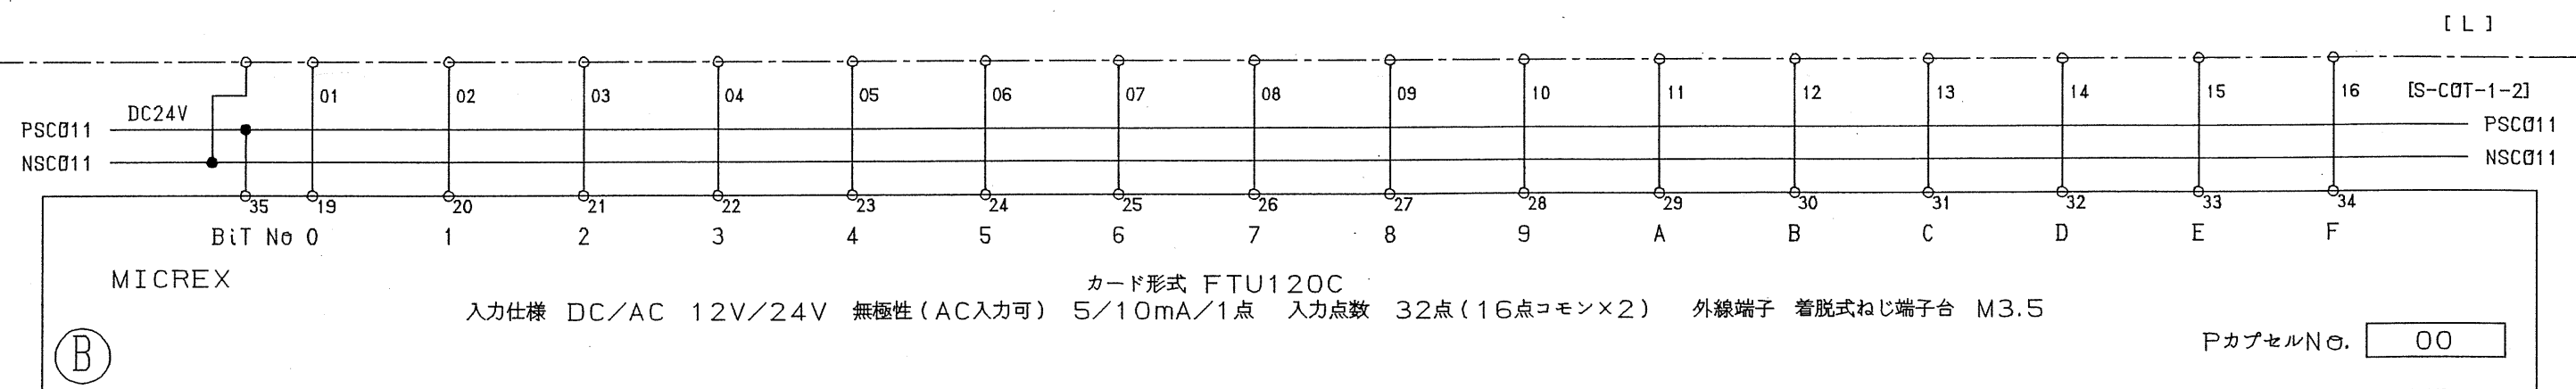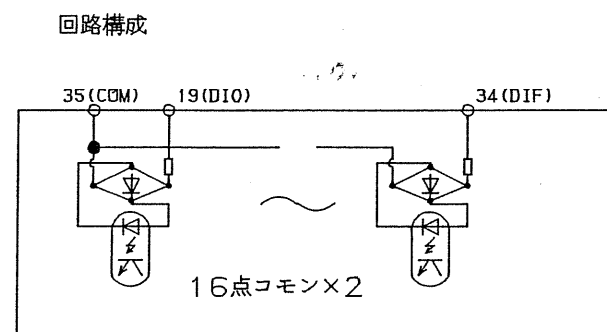

回路構成

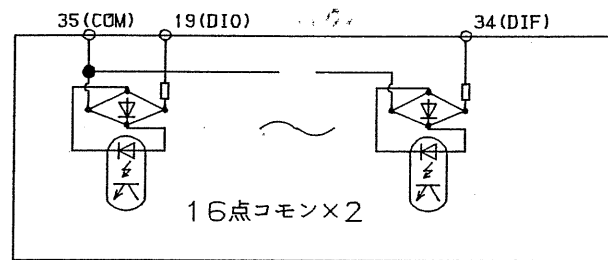


アドレス	項目名称	備考
I.0430	予備	
I.0431		
I.0432		
I.0433		
I.0434		
I.0435		
I.0436		
I.0437		
I.0438		
I.0439		
I.043A		
I.043B		
I.043C		
I.043D		
I.043E		
I.043F	↓	

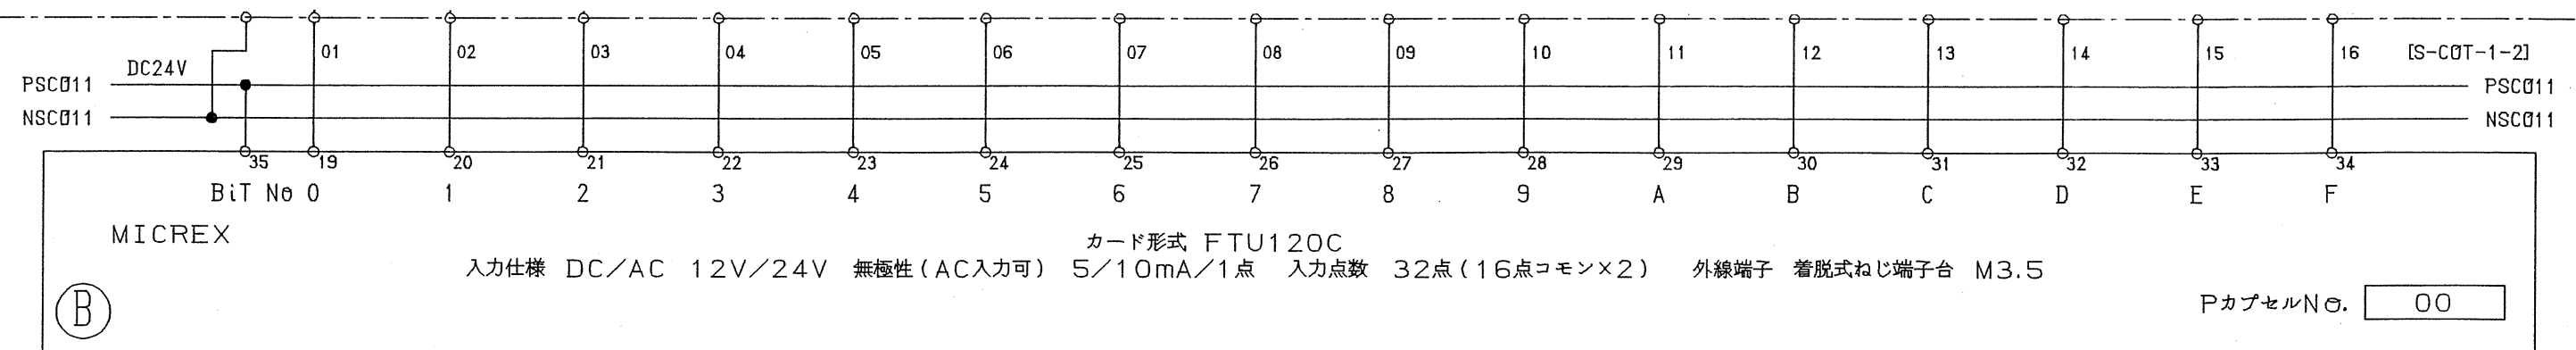


Revisions	②	現地試験フォロー	' 01-06-15	折茂		Date	Name	Fuji Electric Co.,Ltd.	Title	河頭管轄入出力制御装置	Ref. Dwg. No.	W426297	358	A d i j P
	③	コモン変更	' 00-09-06	折茂	Drawn	原田								
	④	アドレス変更・取合いフォロー	' 00-08-21	野崎	Checked									
	⑤	C48307による改造	' 06-12-25	青木										




回路構成

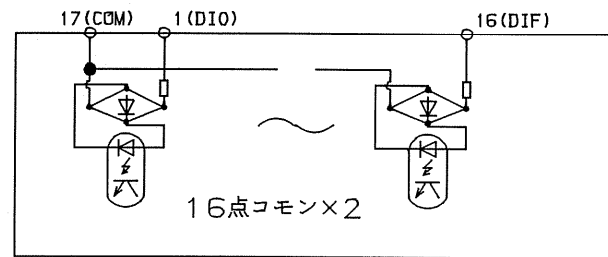


アドレス	項目名称	備考
I.0440	予備	
I.0441	予備	
I.0442	予備	
I.0443	予備	
I.0444	予備	
I.0445	予備	
I.0446	予備	
I.0447	予備	
I.0448	予備	
I.0449	予備	
I.044A	予備	
I.044B	予備	
I.044C	予備	
I.044D	予備	
I.044E	予備	
I.044F	予備	

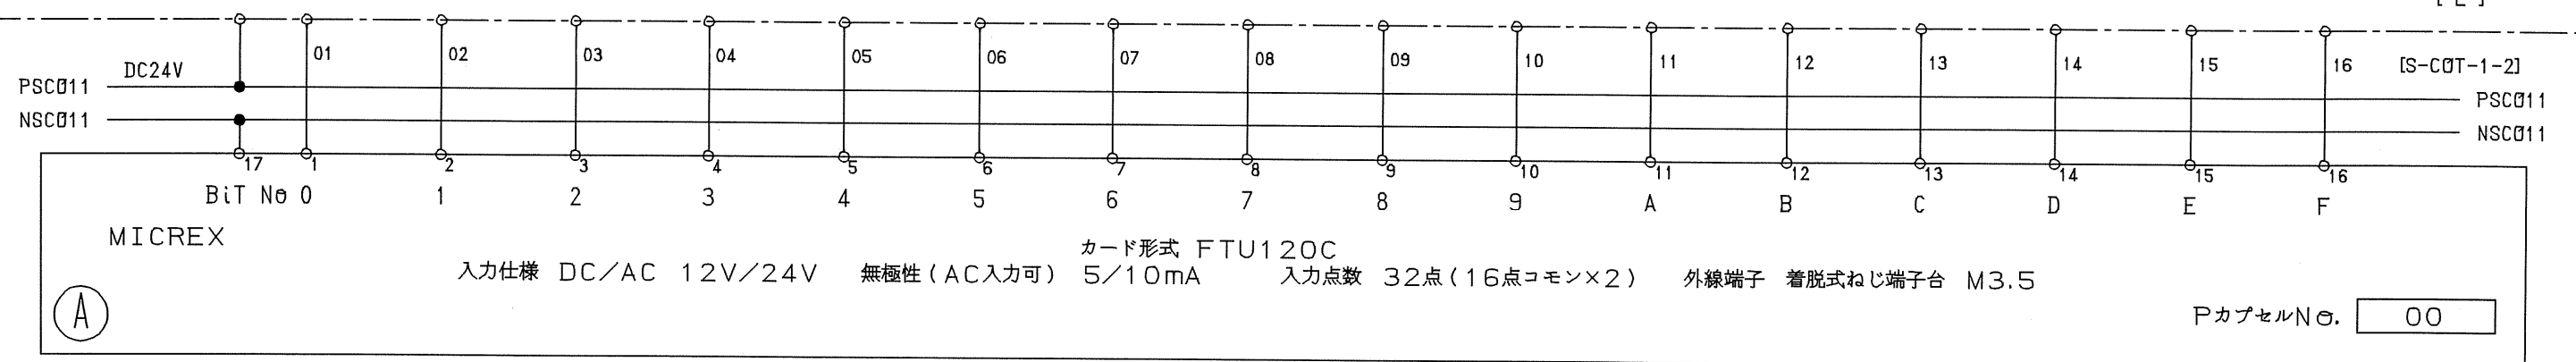

Revisions	○		Date	Name	Fuji Electric Co., Ltd.	河頭管轄入出力制御装置 インターフェース回路	Ref. Dwg. No. W426297	359	M/F DI (ユニット・端子) 1/2 CIFD/CUA
	○		Drawn	1999-12-29 原田					
	①	アドレス変更・信号削除	00-08-21 野崎	Checked					
	②	信号名称変更	00-04-24 森竹						

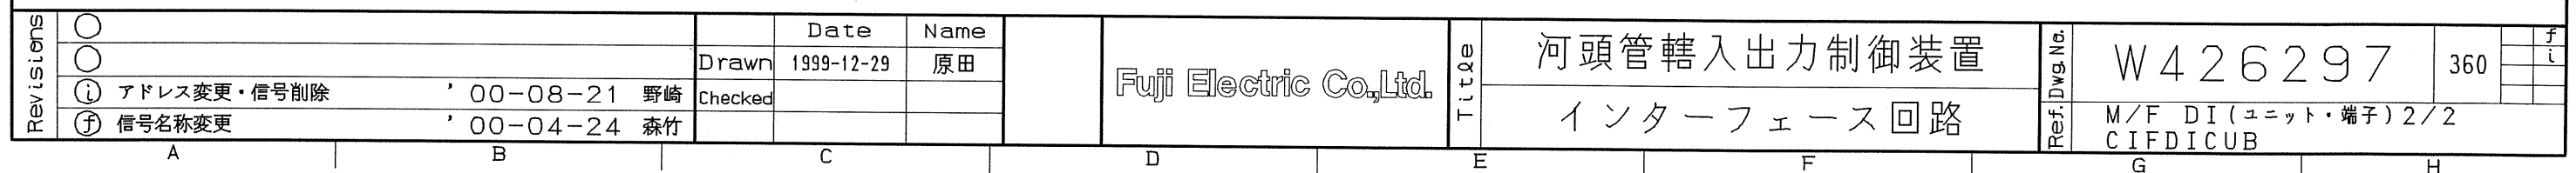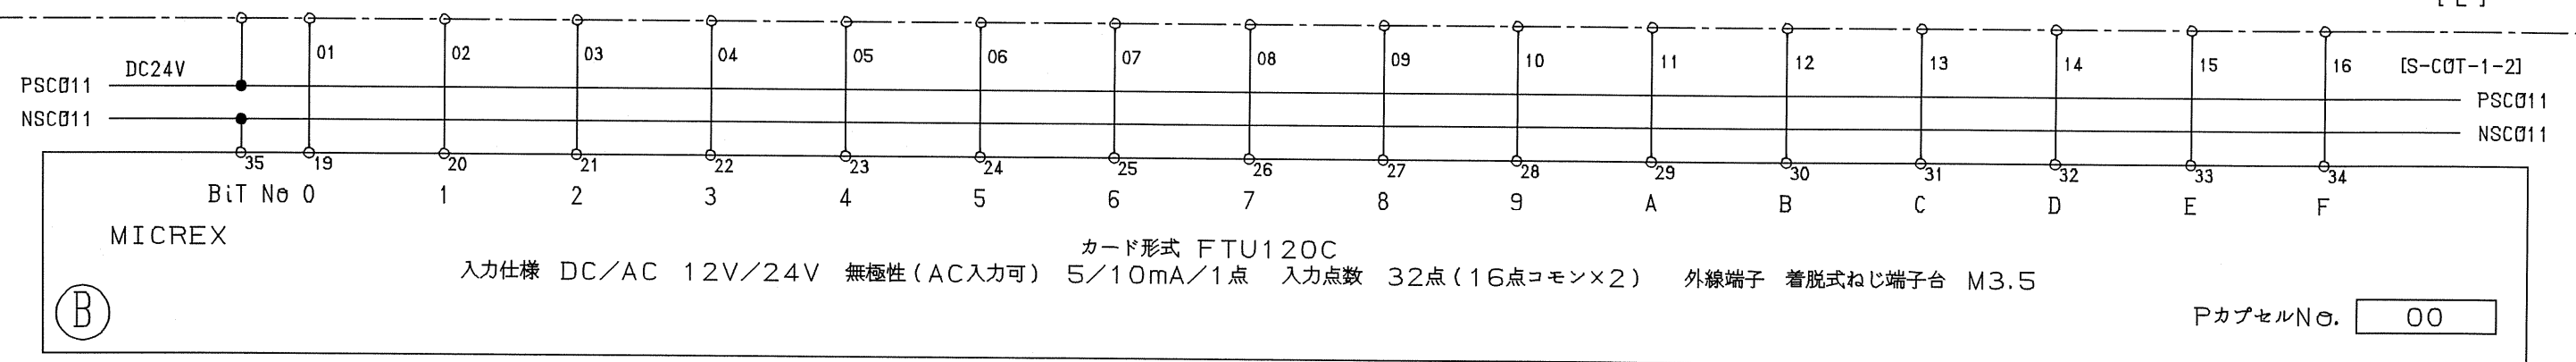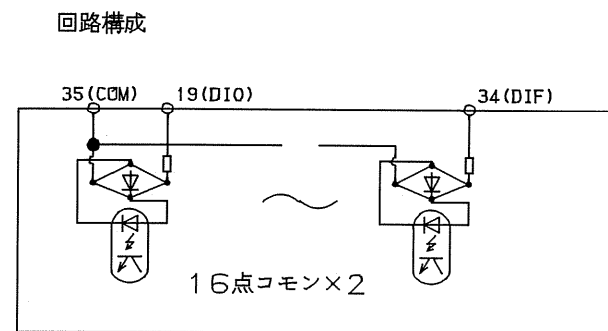

回路構成

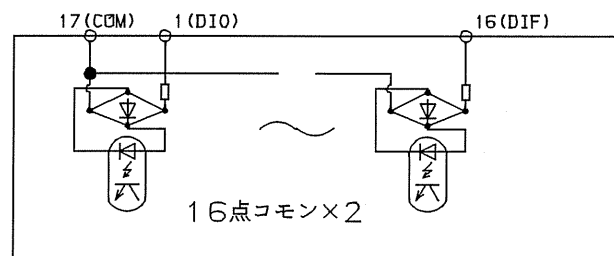

アドレス	項目名称	備考
I.0460	小野ポンプ所 テレメータ異常	-括故障
I.0461	予備	
I.0462	予備	
I.0463	予備	
I.0464	予備	
I.0465	予備	
I.0466	予備	
I.0467	予備	
I.0468	小野配水池 シーメンタ異常	-括故障
I.0469	予備	
I.046A	予備	
I.046B	予備	
I.046C	予備	
I.046D	予備	
I.046E	予備	
I.046F	予備	

[遠方監視制御装置盤 (小野ポンプ所)]

[遠方監視制御装置盤 (小野配水池)]

52151

PSC011
NSC011


MICREX

入力仕様 DC/AC 12V/24V 無極性 (AC入力可) 5/10mA 入力点数 32点 (16点コモン×2) 外線端子 着脱式ねじ端子台 M3.5

PカプセルNo. 00


Revisions	① 現地試験フォロー	01-06-15	折茂	Date	Name	Fuji Electric Co., Ltd.	0011	河頭管轄入出力制御装置 インターフェース回路	Ref. Dwg. No.	W426297	361	V B K P
	② 信号追加	00-09-20	折茂	Drawn	原田							
	③ 信号追加	09-01-30	河野	Checked								
	④ Q33532による取合フォロー	03-02-07	河野									

A B C D E F G H

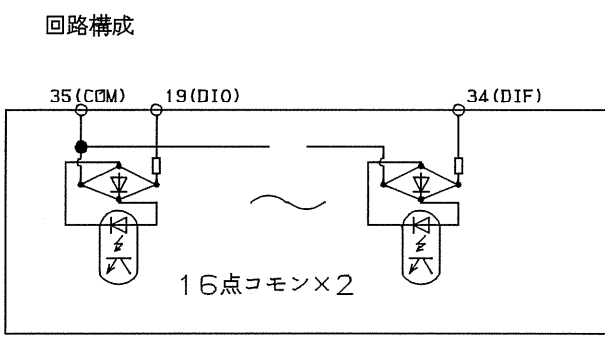

アドレス	項目名称		備考
I.0470	中迫ポンプ所	予備	
I.0471	中迫ポンプ所	予備	
I.0472	中迫ポンプ所	予備	
I.0473	中迫ポンプ所	予備	
I.0474	中迫ポンプ所	予備	
I.0475	中迫ポンプ所	予備	
I.0476	中迫ポンプ所	予備	
I.0477	中迫ポンプ所	予備	
I.0478	中迫ポンプ所	予備	
I.0479	中迫ポンプ所	予備	
I.047A	中迫ポンプ所	予備	
I.047B	中迫ポンプ所	予備	
I.047C	中迫ポンプ所	予備	
I.047D	中迫ポンプ所	予備	
I.047E	中迫ポンプ所	予備	
I.047F	中迫ポンプ所	TM故障	


[TM-015500] 遠方監視制御装置盤（中迫ポンプ所）より W428833

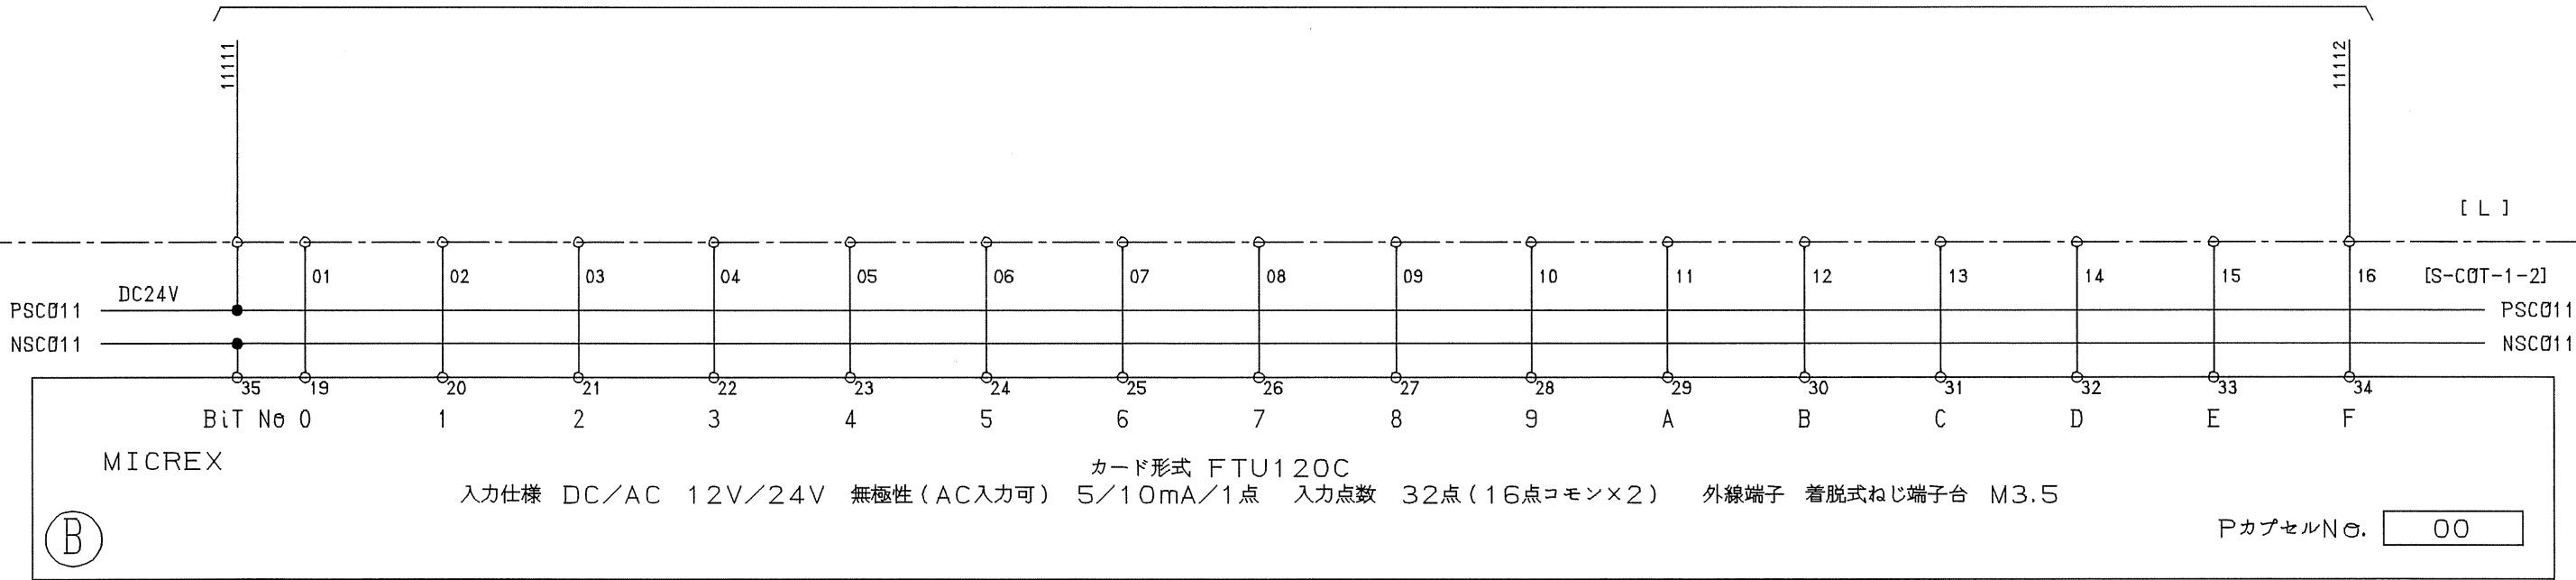

Revisions	⑨	N33614による取合フォロー	'	01-07-04	折茂		Date	Name	Fuji Electric Co.,Ltd.	Title	河頭管轄入出力制御装置 インターフェース回路	Ref. Dwg. No.	W426297	362	M/F DI (ユニット・端子) 2/2 CIFDICUB	f i k q
	Ⓚ	信号追加	'	00-09-20	折茂	Drawn	1999-12-29	原田								
	①	アドレス変更・信号削除	'	00-08-21	野崎	Checked										
	⑦	信号名称変更	'	00-04-24	森竹											


A B C D E F G H

回路構成

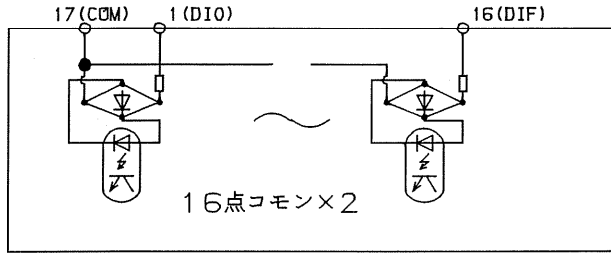


アドレス	項目名称	備考
I.0480	城西電動弁室 予備	
I.0481	城西電動弁室 予備	
I.0482	城西電動弁室 予備	
I.0483	城西電動弁室 予備	
I.0484	城西電動弁室 予備	
I.0485	城西電動弁室 予備	
I.0486	城西電動弁室 予備	
I.0487	城西電動弁室 予備	
I.0488	城西電動弁室 予備	
I.0489	城西電動弁室 予備	
I.048A	城西電動弁室 予備	
I.048B	城西電動弁室 予備	
I.048C	城西電動弁室 予備	
I.048D	城西電動弁室 予備	
I.048E	城西電動弁室 予備	
I.048F	城西電動弁室 TM故障	

[遠方監視制御装置盤 (城西電動弁室)] より (J12)Q12001304 (山武)

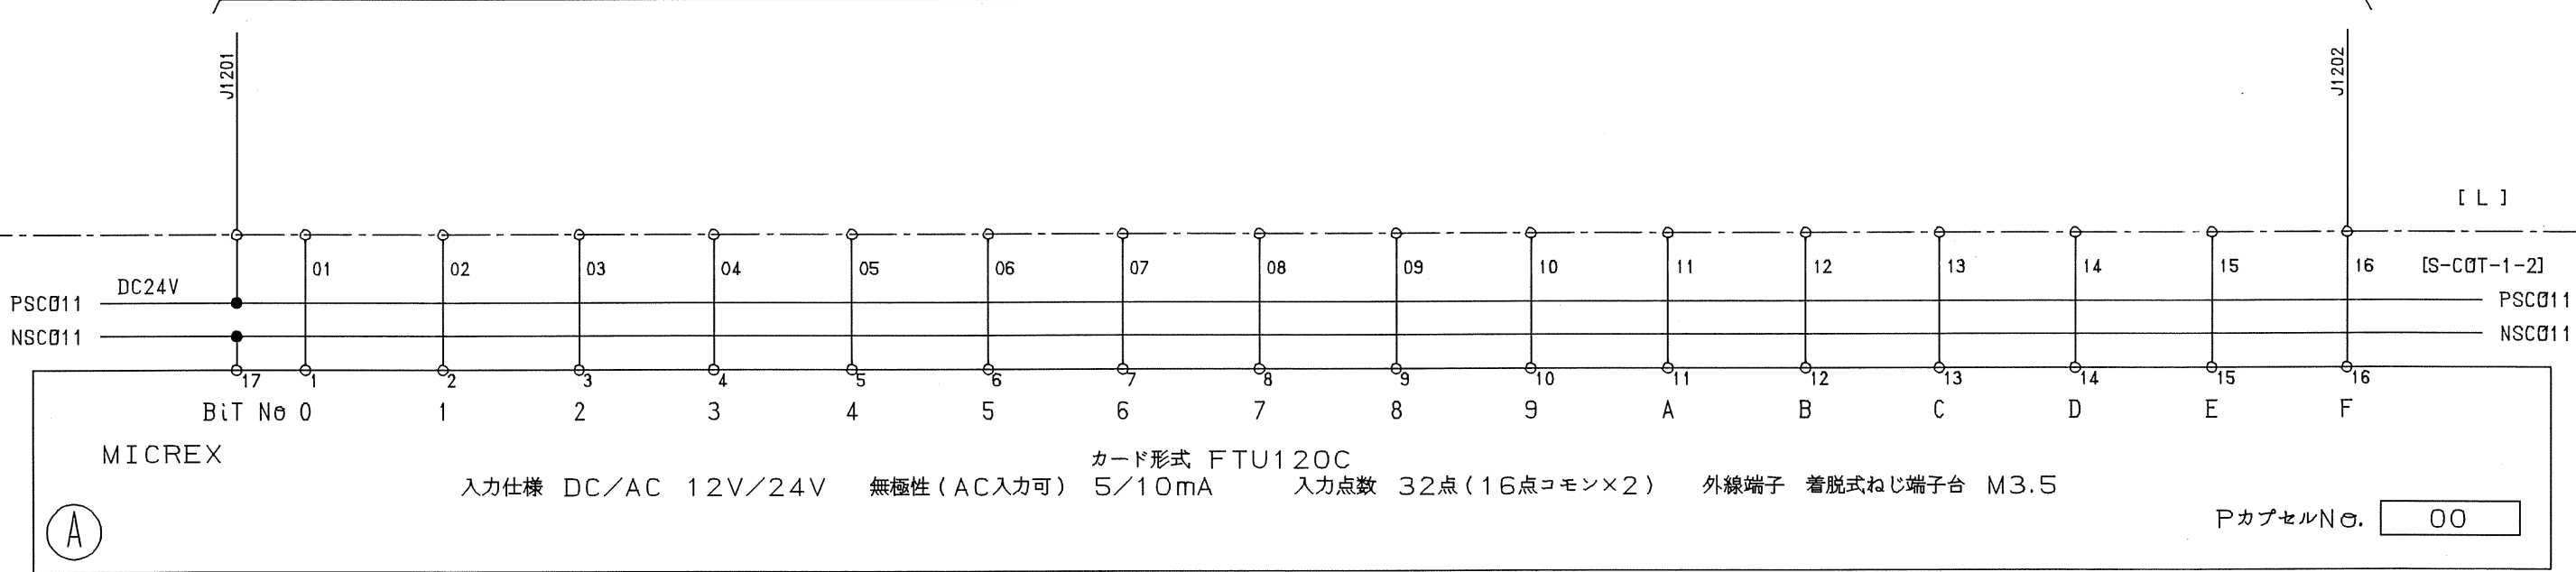


⑤	現地試験フォロー	' 01-06-15	折茂		Date	Name	Fuji Electric Co.,Ltd.	河頭管轄入出力制御装置 インターフェース回路	Ref. Dwg. No.	W426297	363	M/F DI (ユニット・端子) 1/2 CIFDICUA	P
⑥	信号追加	' 00-09-20	折茂	Drawn	1999-12-29	原田							
⑦	アドレス変更・信号削除	' 00-08-21	野崎	Checked									
⑧	信号名称変更	' 00-04-24	森竹										



回路構成

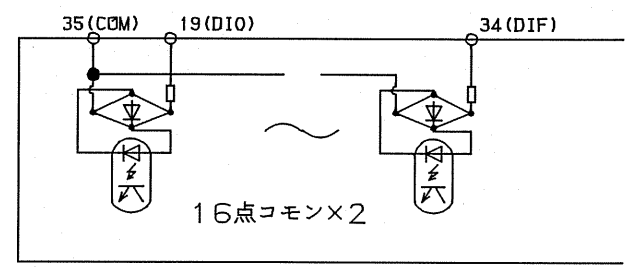


アドレス	項目名称	備考
I.0490	予備	
I.0491	予備	
I.0492	予備	
I.0493	予備	
I.0494	予備	
I.0495	予備	
I.0496	予備	
I.0497	予備	
I.0498	予備	
I.0499	予備	
I.049A	予備	
I.049B	予備	
I.049C	予備	
I.049D	予備	
I.049E	予備	
I.049F	若葉台配水池	TM故障

[遠方監視制御装置盤（若葉台配水池）]

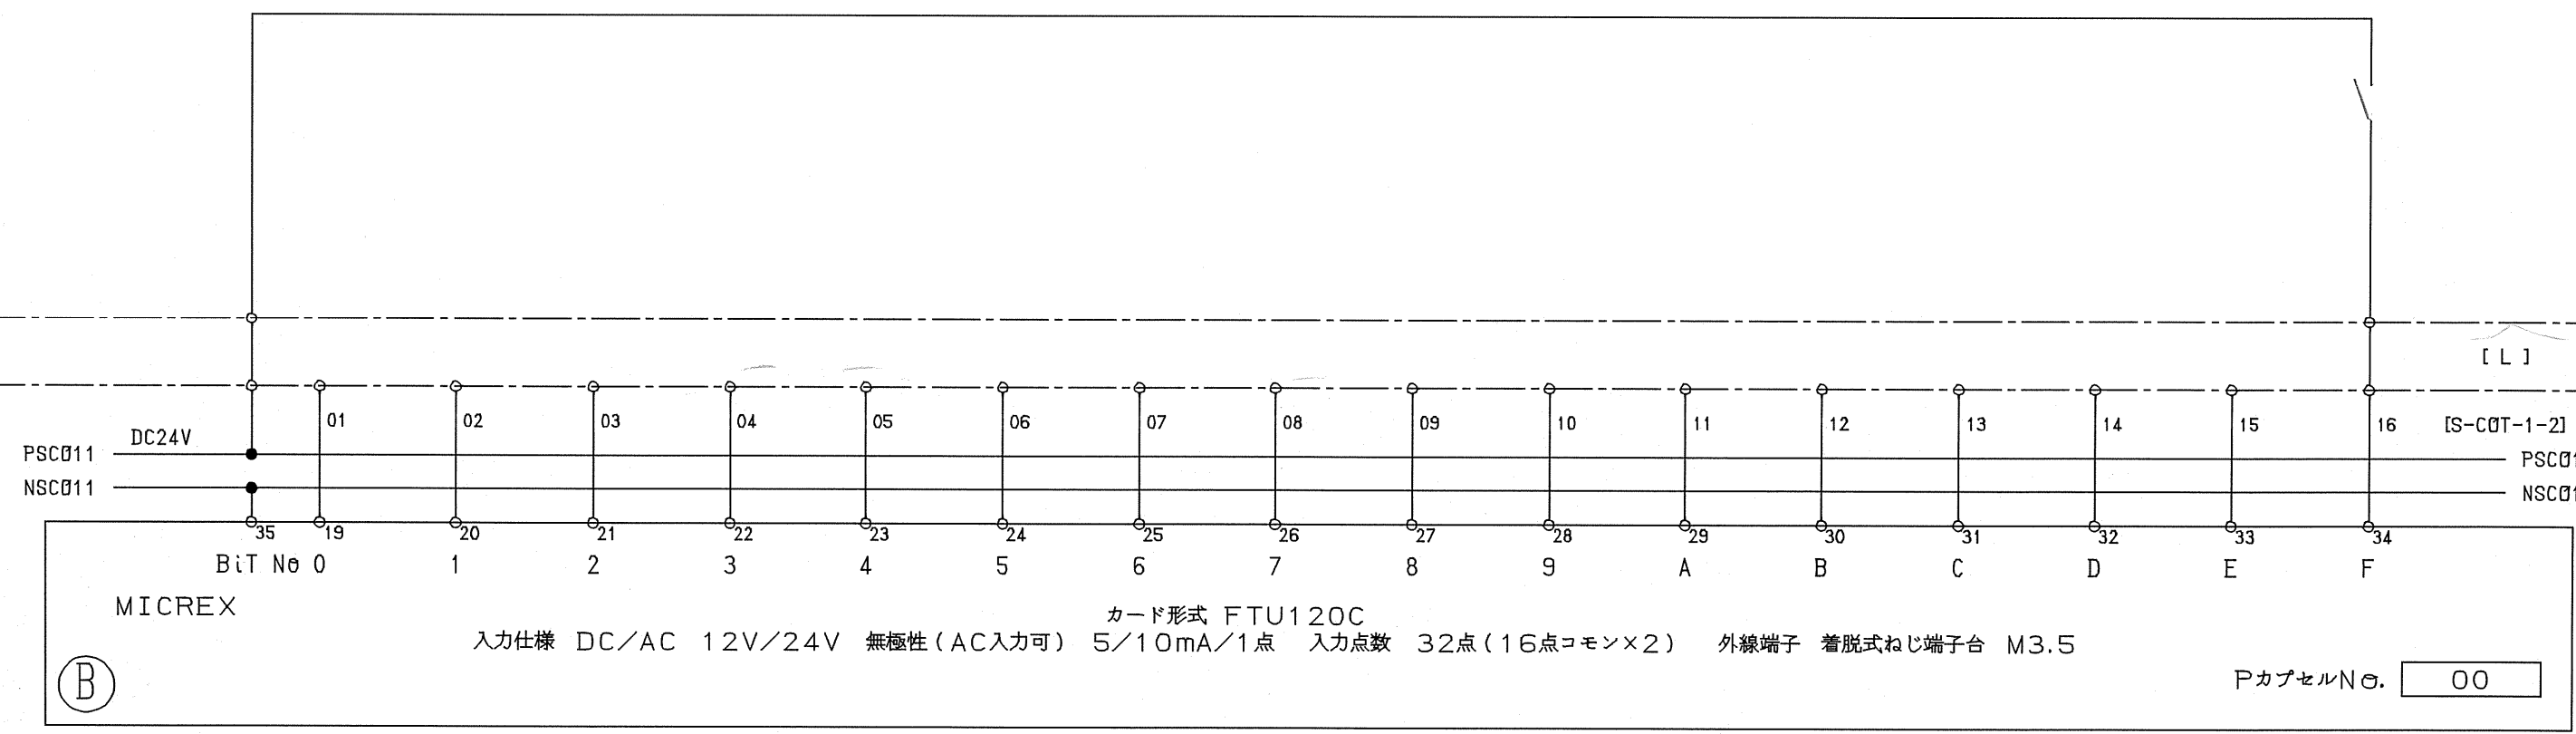


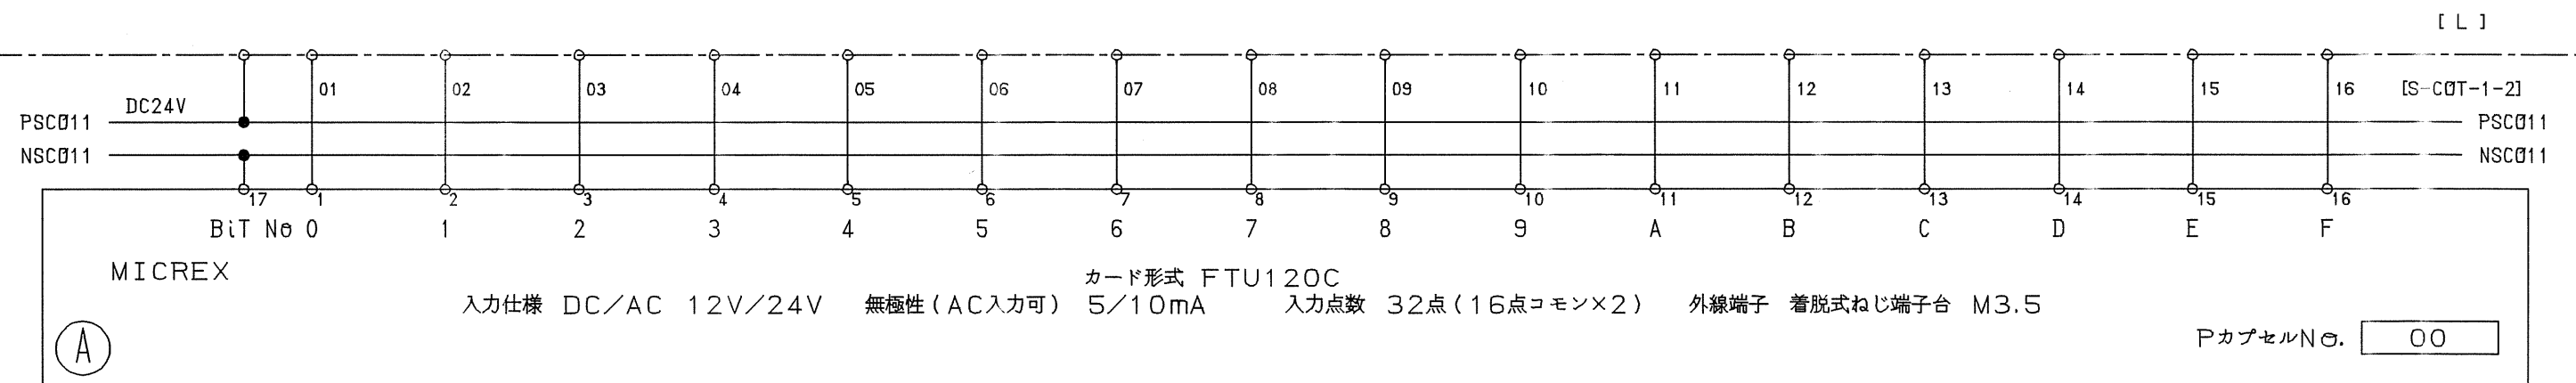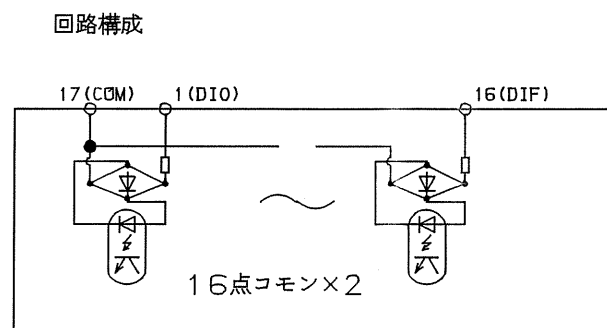

Revisions	⑤	現地試験フォロー	' 01-06-15	折茂		Date	Name	Fuji Electric Co., Ltd.	Title	河頭管轄入出力制御装置 インターフェース回路	Ref. Dwg. No.	W 4 2 6 2 9 7	365	☒ f ☐ i ☐ K ☐ P
	④	信号追加	' 00-09-20	折茂	Drawn	1999-12-29	原田							
	③	アドレス変更・取合いフォロー	' 00-08-21	野崎	Checked									
	②	テレメータ追加による取合変更	' 04-01-19	河野										

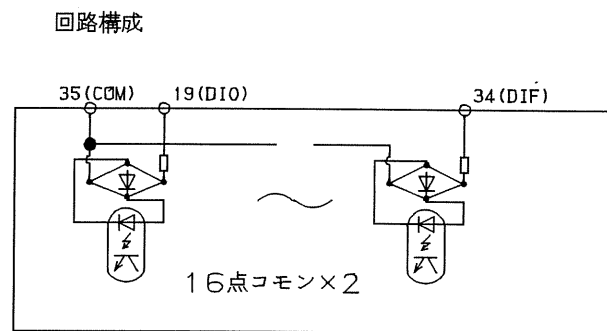


[遠方監視制御装置盤(伊敷台ポンプ所)]
06-310009(明興テクノス)

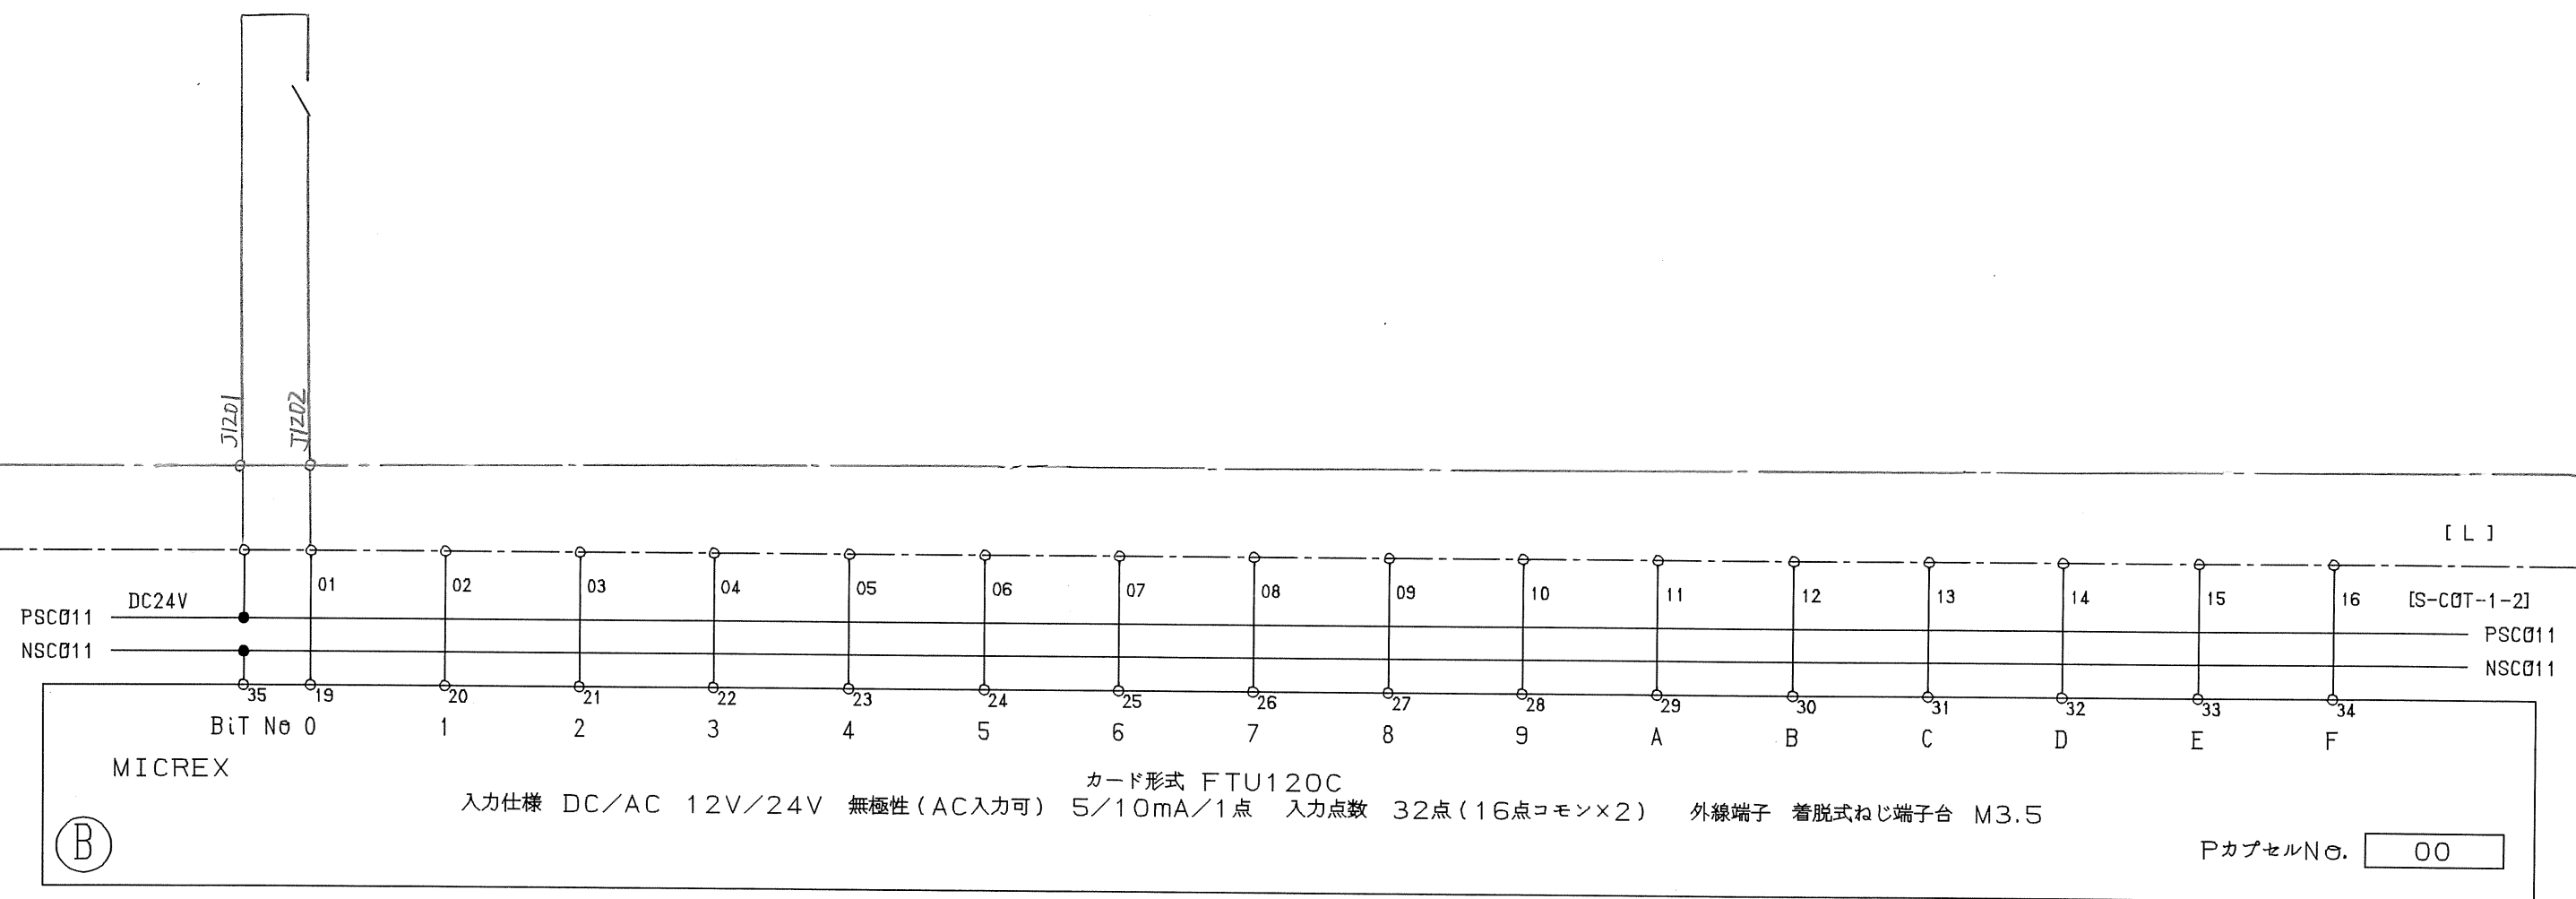

Revisions	○			Date	Name	Fuji Electric Co.,Ltd.	Title	河頭管轄入出力制御装置 インターフェース回路	Ref. Dwg. No.	W426297	366	A			
	④	C48307に53改造	'06-12-25	青木	Drawn								1999-12-29	原田	
	③	アドレス変更・信号削除	'00-08-21	野崎	Checked										
	②	信号名称変更	'00-04-24	森竹											
A		B		C		D		E		F		G		H	

A B C D E F G H

回路構成

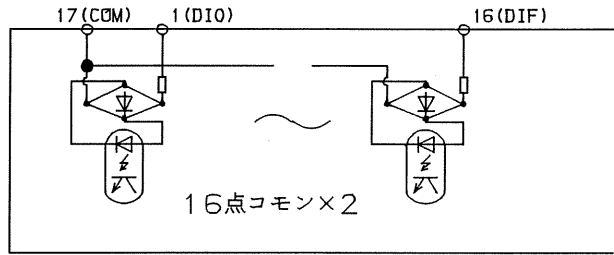

アドレス	項目名称	備考
I.0520	石井手配水池 テレメータ異常	一括故障
I.0521	予備	
I.0522	予備	
I.0523	予備	
I.0524	予備	
I.0525	小野取水場 テレメータ異常	一括故障
I.0526	予備	
I.0527	予備	
I.0528	予備	
I.0529	予備	
I.052A	花野第1配水池 テレメータ異常	一括故障
I.052B	予備	
I.052C	予備	
I.052D	予備	
I.052E	予備	
I.052F	予備	

[遠方監視制御装置 (石井手配水池)]

[遠方監視制御装置 (小野取水場)]

[遠方監視制御装置 (花野第1配水池)]

FTE439909

C1209

C1210

01

02

03

04

05

06

07

08

09

10

11

12

13

14

15

16

[L]

[S-COT-1-2]

PSC011

NSC011

PSC011

NSC011

Bit No 0

1

2

3

4

5

6

7

8

9

A

B

C

D

E

F

MICREX

入力仕様 DC/AC 12V/24V

無極性 (AC入力可)

カード形式 FTU120C

入力点数 32点 (16点コモン×2)

外線端子 着脱式ねじ端子台 M3.5

PカプセルNo.

00

A

Revisions	①	現地試験フォロー	' 01-06-15	折茂		Date	Name	Fuji Electric Co.,Ltd.	Title	河頭管轄入出力制御装置	Ref. Dwg. No.	W 4 2 6 2 9 7	367	子 i k P
	②	一部変更	' 00-09-20	折茂	Drawn	1999-12-29	原田							
	③	アドレス変更・信号削除	' 00-08-21	野崎	Checked									
	④	信号名称・取合い変更	' 00-04-24	森竹										

A

B

C


D

E


F



G

H

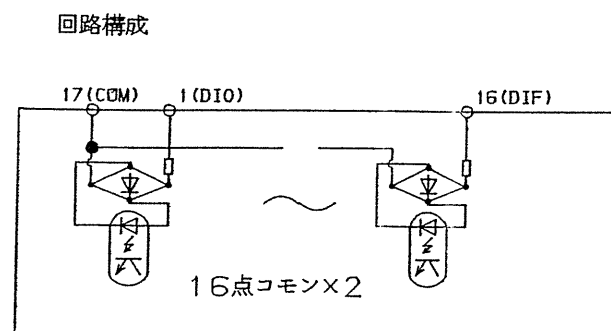

〔遠方監視制御装置盤（健康の森ポンプ所）〕

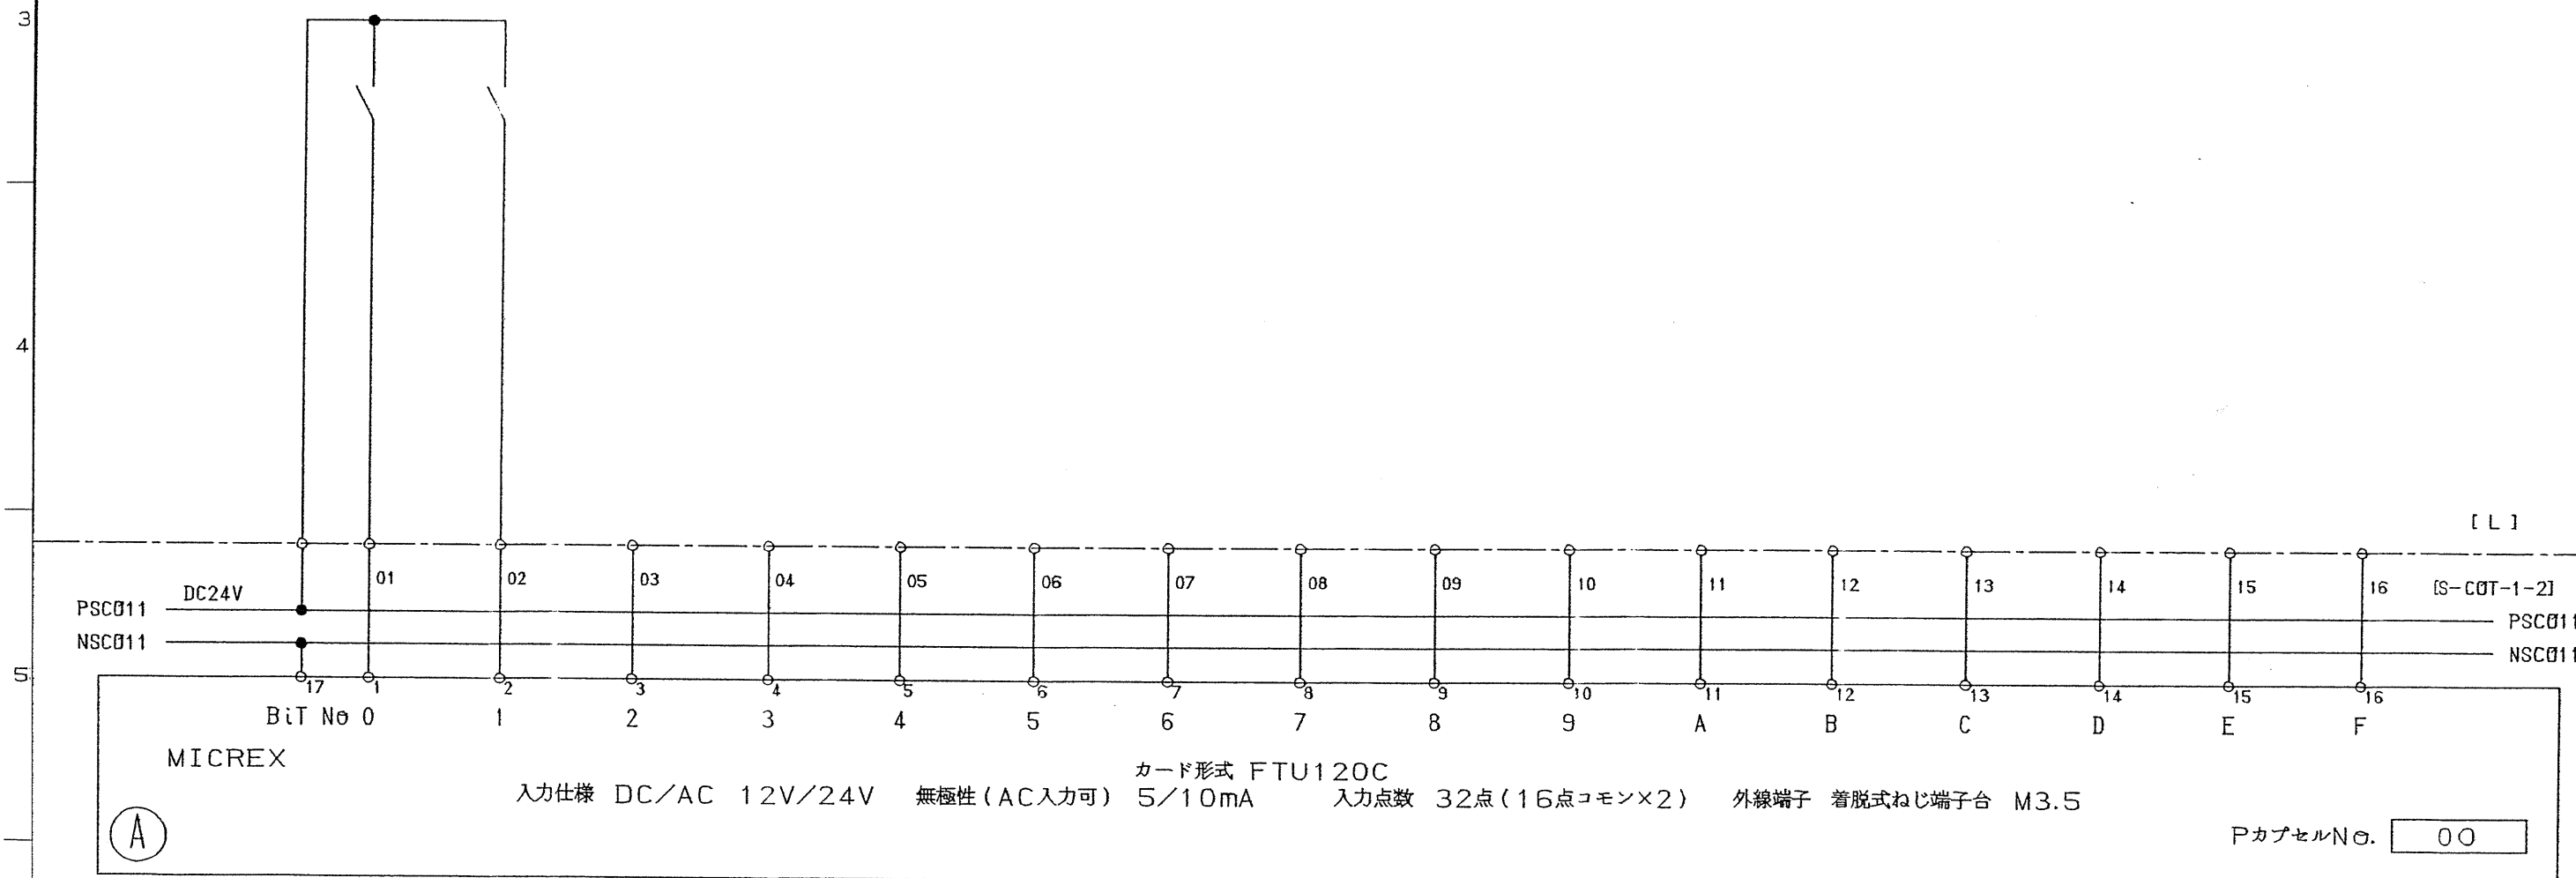
[illegible]

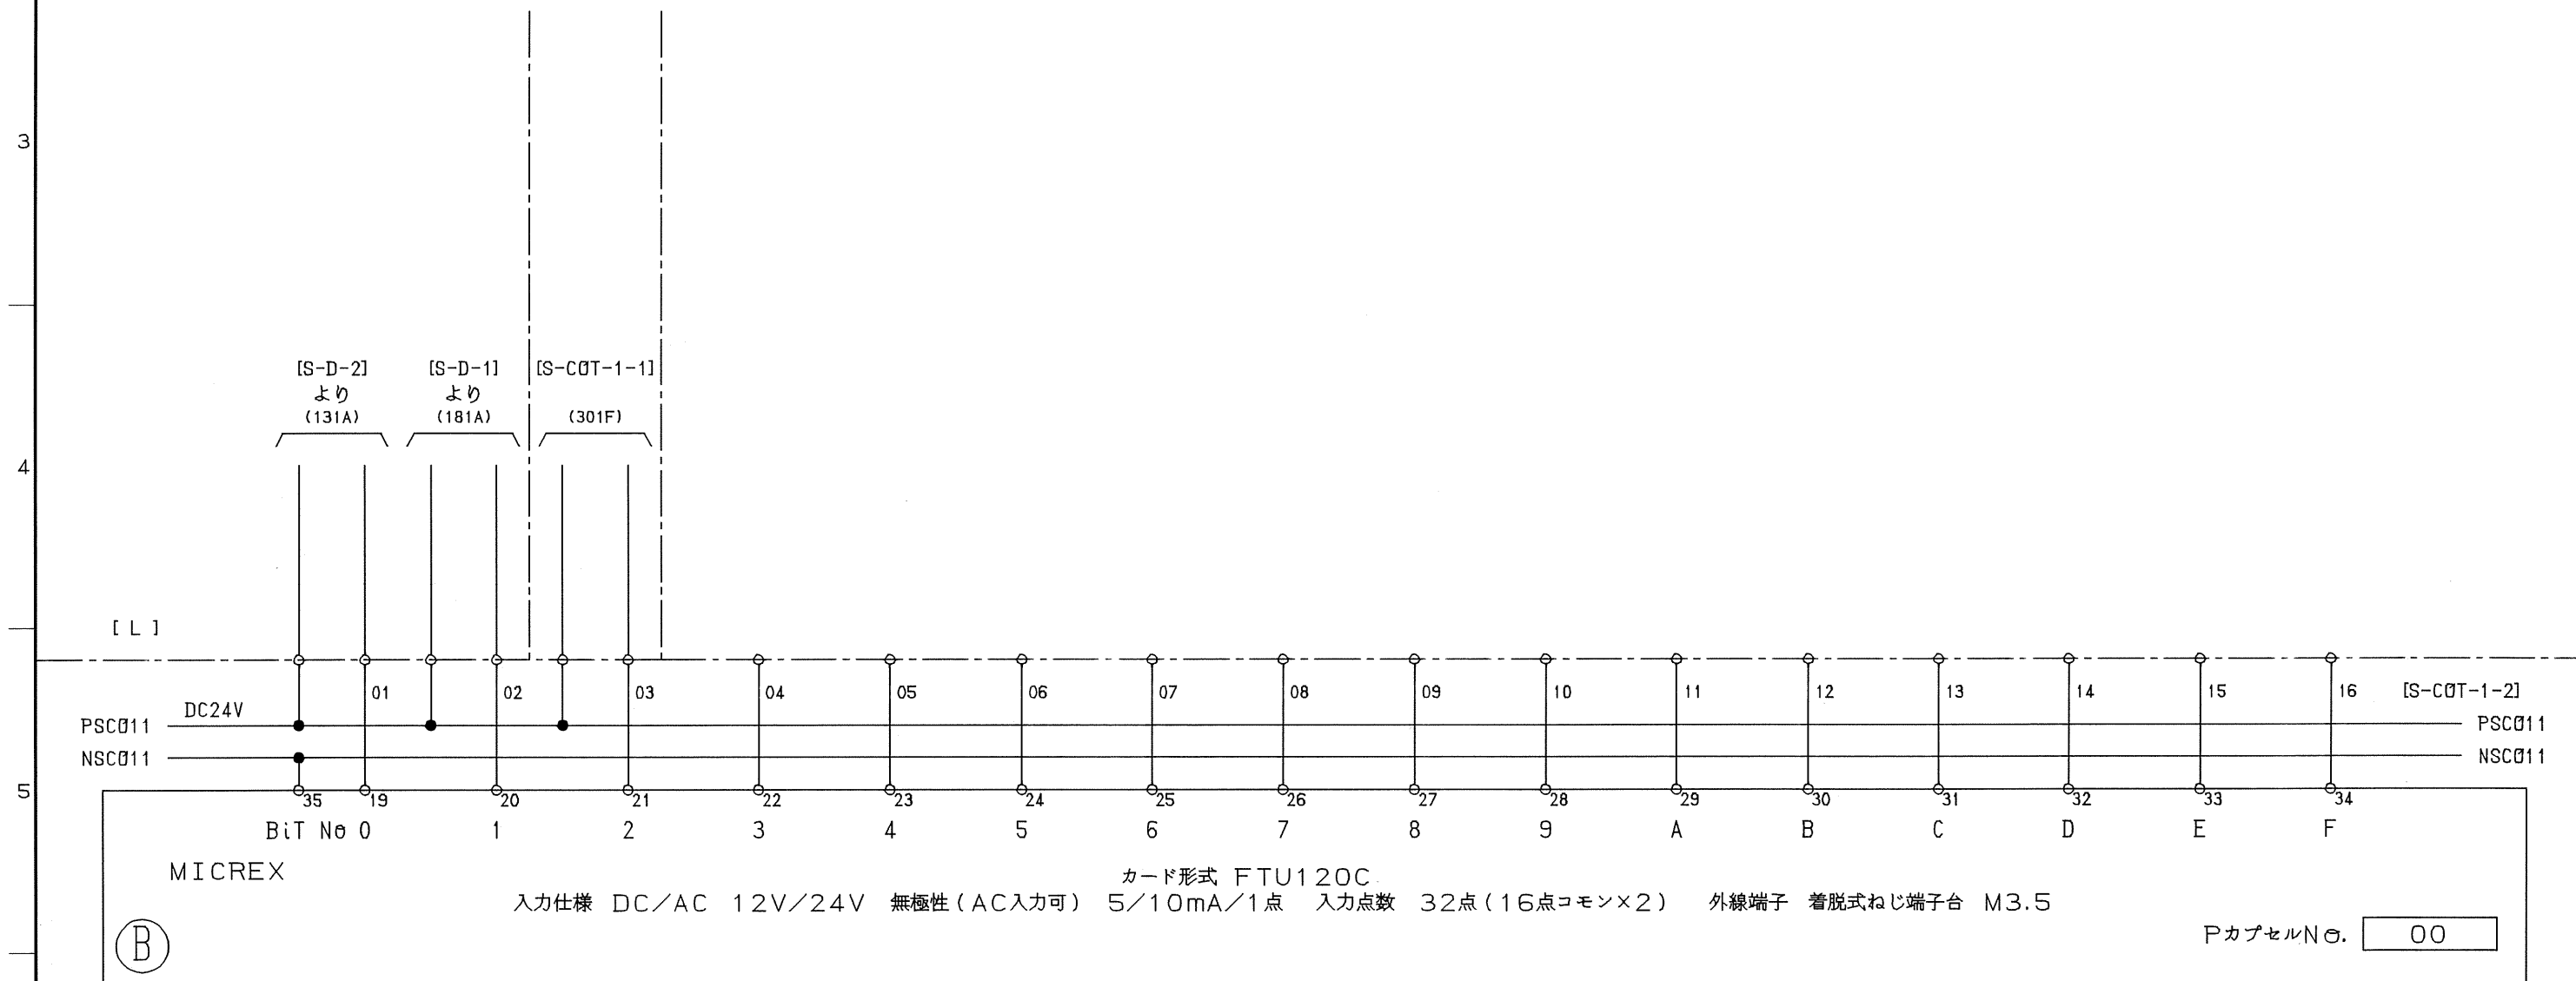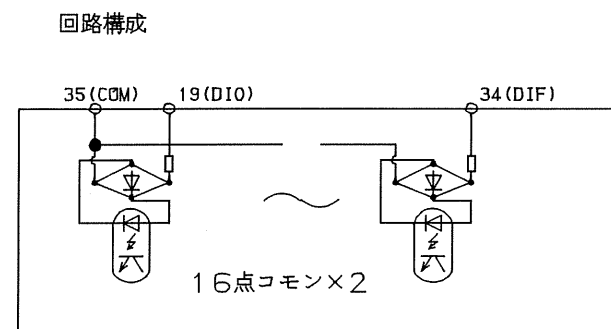

Revisions	○			Date	Name	Fuji Electric Co., Ltd.	Title	河頭管轄入出力制御装置 インターフェース回路	Ref. Dwg. No.	W 4 2 6 2 9 7	370	F I P			
	Ⓐ	現地試験フォロー	' 01-06-15 折茂	Drawn	1999-12-29								原田		
	Ⓘ	アドレス変更・信号追加	' 00-08-21 野崎	Checked											
	㊦	中端盤削除	' 00-04-24 森竹												
A		B		C		D		E		F		G		H	


全点独立×16

アドレス	項目名称	備考
0.0560	予備	
0.0561		
0.0562		
0.0563		
0.0564		
0.0565		
0.0566		
0.0567		
0.0568		
0.0569		
0.056A		
0.056B		
0.056C		
0.056D		
0.056E		
0.056F	√	

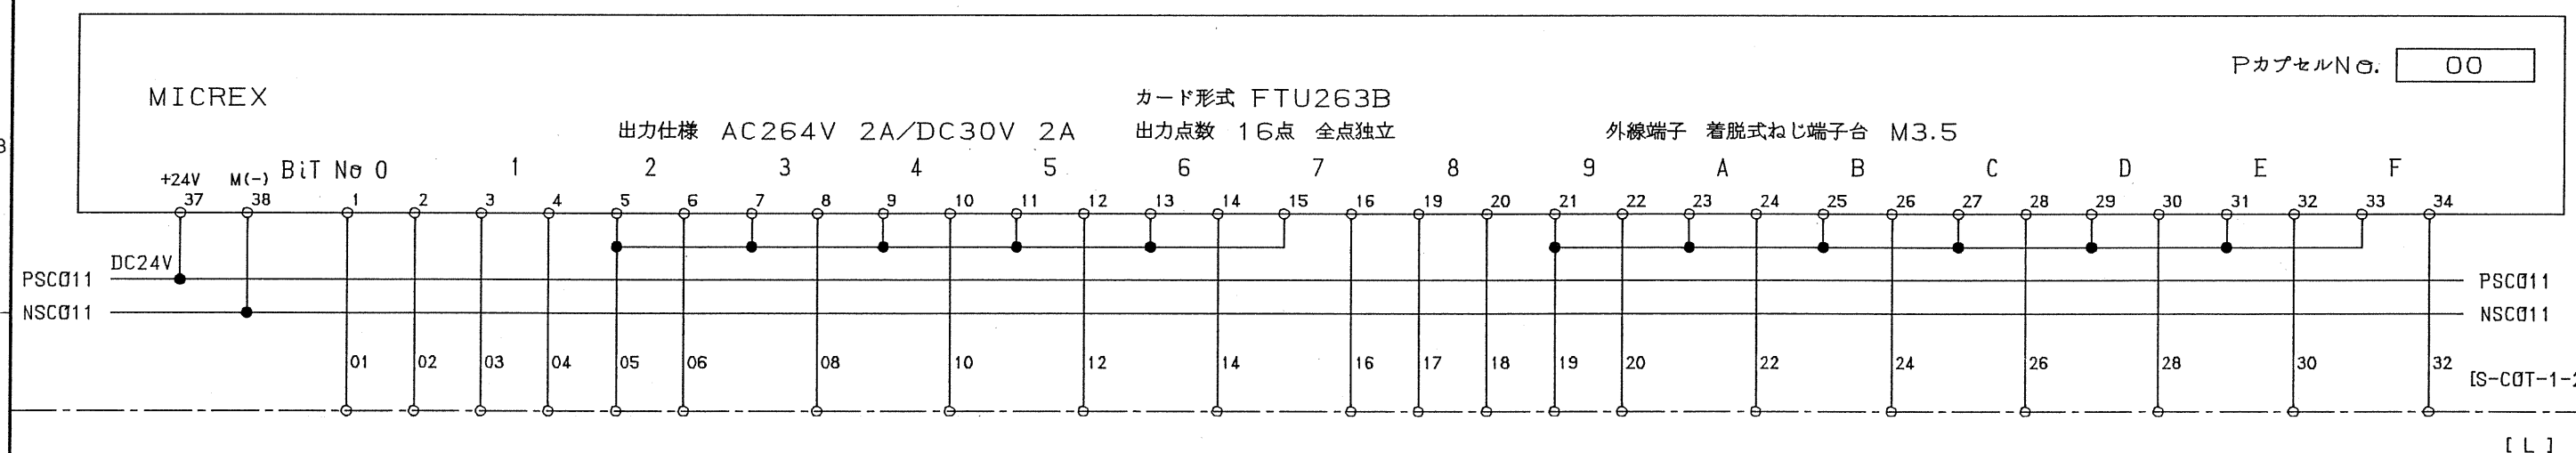

Revisions	④	C48307による改造	' 06-12-25	青木		Date	Name	Fuji Electric Co., Ltd.	Title	河頭管轄入出力制御装置 インターフェース回路	Ref. Dwg. No.	W 4 2 6 2 9 7 M/F D0 (RY・ユニット) 1/1 CIED00UA	371
	③	現地試験フォロー	' 01-06-15	折茂	Drawn		原田						
	②	アドレス変更・取合いフォロー	' 00-08-21	野崎	Checked								
	①	信号割付	' 00-02-18	河野									

回路構成

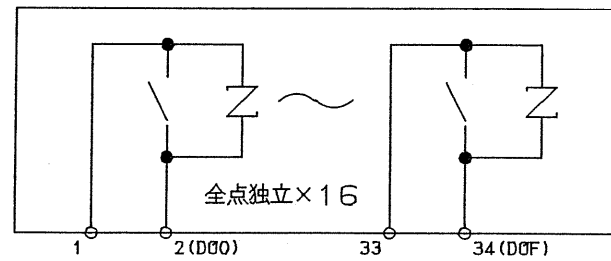

アドレス	項目名称	備考
0.0570	予備	
0.0571		
0.0572		
0.0573		
0.0574		
0.0575		
0.0576		
0.0577		
0.0578		
0.0579		
0.057A		
0.057B		
0.057C		
0.057D		
0.057E		
0.057F	↓	

MICREX


カード形式 FTU263B

PカプセルNo. 00

出力仕様 AC264V 2A/DC30V 2A

出力点数 16点 全点独立


外線端子 着脱式ねじ端子台 M3.5

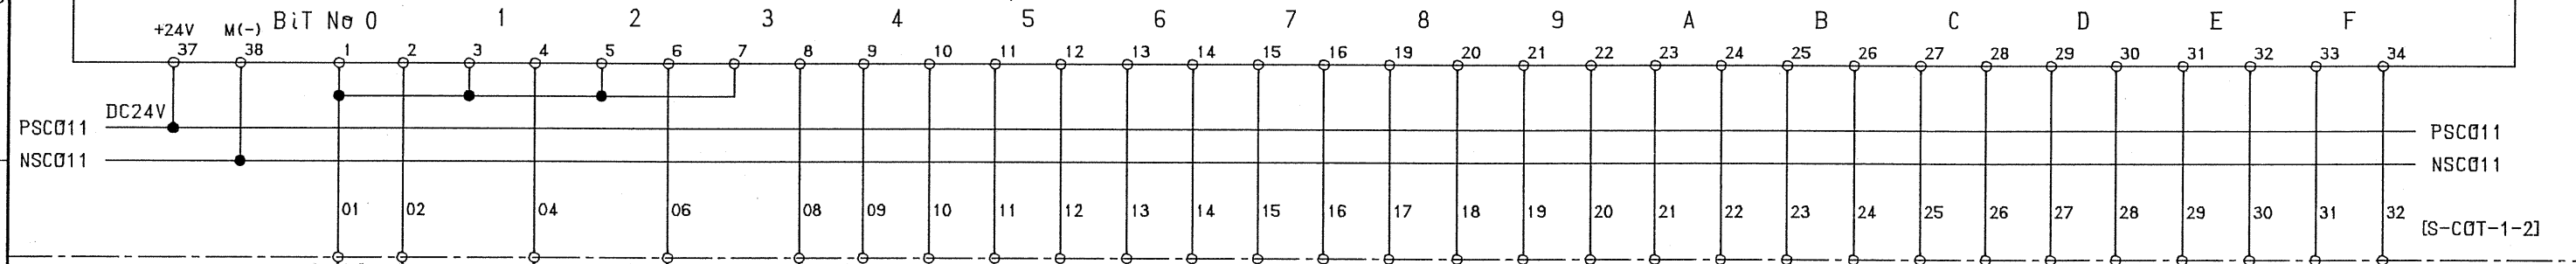

Revisions	① C4830'7による改造	'06-12-25 青木	Date	Name	Fuji Electric Co.,Ltd.	河頭管轄入出力制御装置 インターフェース回路	Ref. Dwg. No.	W426297	372	M/F D0 (RY・ユニット) 1/1 CIFD0RUA	d i p A
	② 現地試験フォロー	'01-06-15 折茂	Drawn	原田							
	③ アドレス変更・取合いフォロー	'00-08-21 野崎	Checked								
	④ 信号割付	'00-02-18 河野									

全点独立 $\times 16$


ア ド レ ス	項 目 名 称	備 考
0.0580	予備	
0.0581	予備	
0.0582	予備	
0.0583	予備	
0.0584	予備	
0.0585	予備	
0.0586	予備	
0.0587	予備	
0.0588	予備	
0.0589	予備	
0.058A	予備	
0.058B	予備	
0.058C	予備	
0.058D	予備	
0.058E	予備	
0.058F	予備	

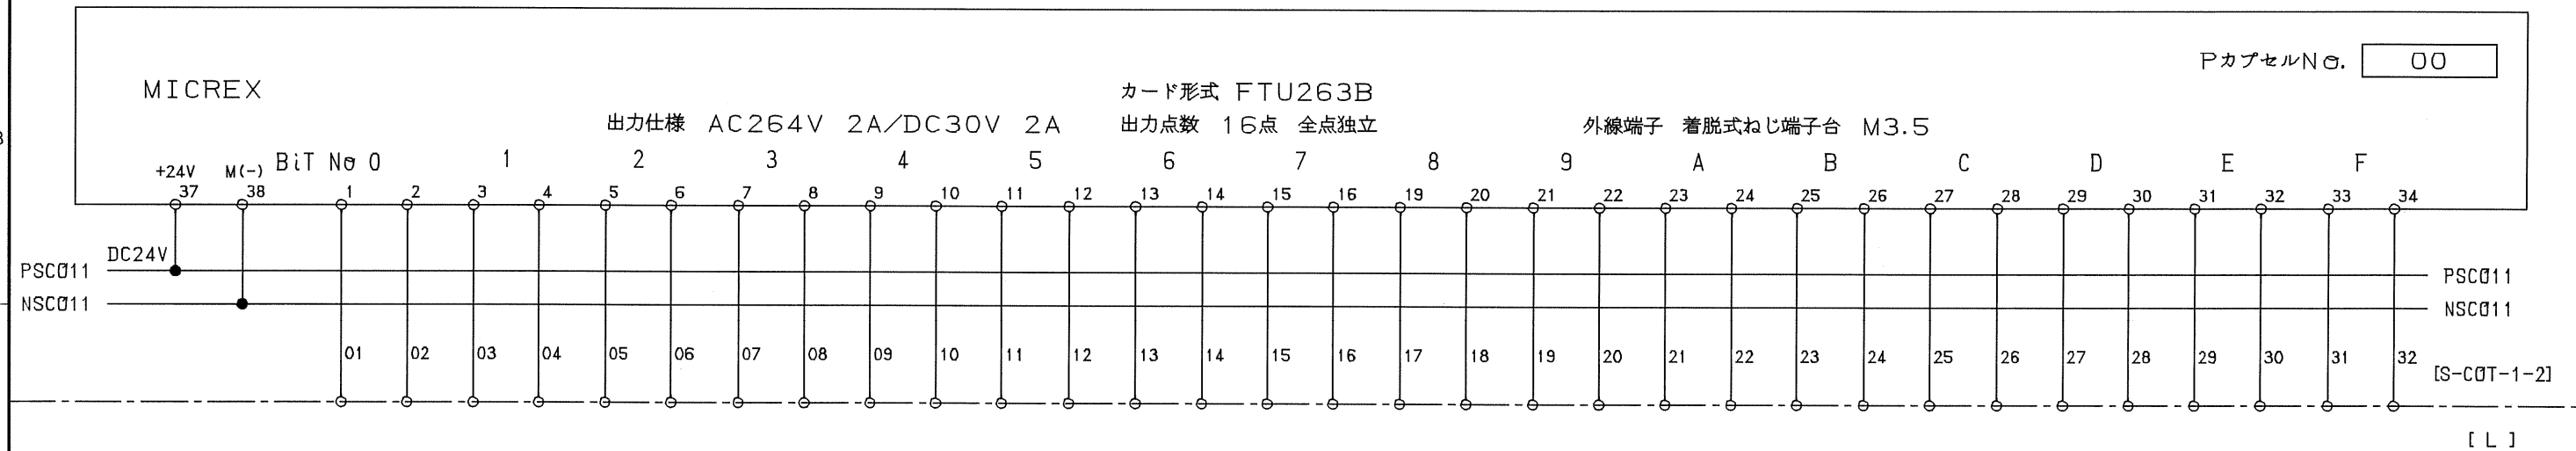

Revisions	○		Date	Name	Fuji Electric Co.,Ltd.	Title	河頭管轄入出力制御装置 インターフェース回路	Ref. Dwg. No.	W 4 2 6 2 9 7	373	M/F D0 (RY・ユニット) 1/1 CIFD0RUA				
	○		Drawn	1999-12-29								原田			
	①	アドレス変更・信号削除	' 00-08-21	野崎								Checked			
	②	信号名称変更	' 00-04-24	森竹											
A		B		C		D		E		F		G		H	

全点独立 x 16


ア ド レ ス	項 目 名 称	備 考
0.0590	予備	
0.0591	予備	
0.0592	予備	
0.0593	予備	
0.0594	予備	
0.0595	予備	
0.0596	予備	
0.0597	予備	
0.0598	予備	
0.0599	予備	
0.059A	予備	
0.059B	予備	
0.059C	予備	
0.059D	予備	
0.059E	予備	
0.059F	予備	

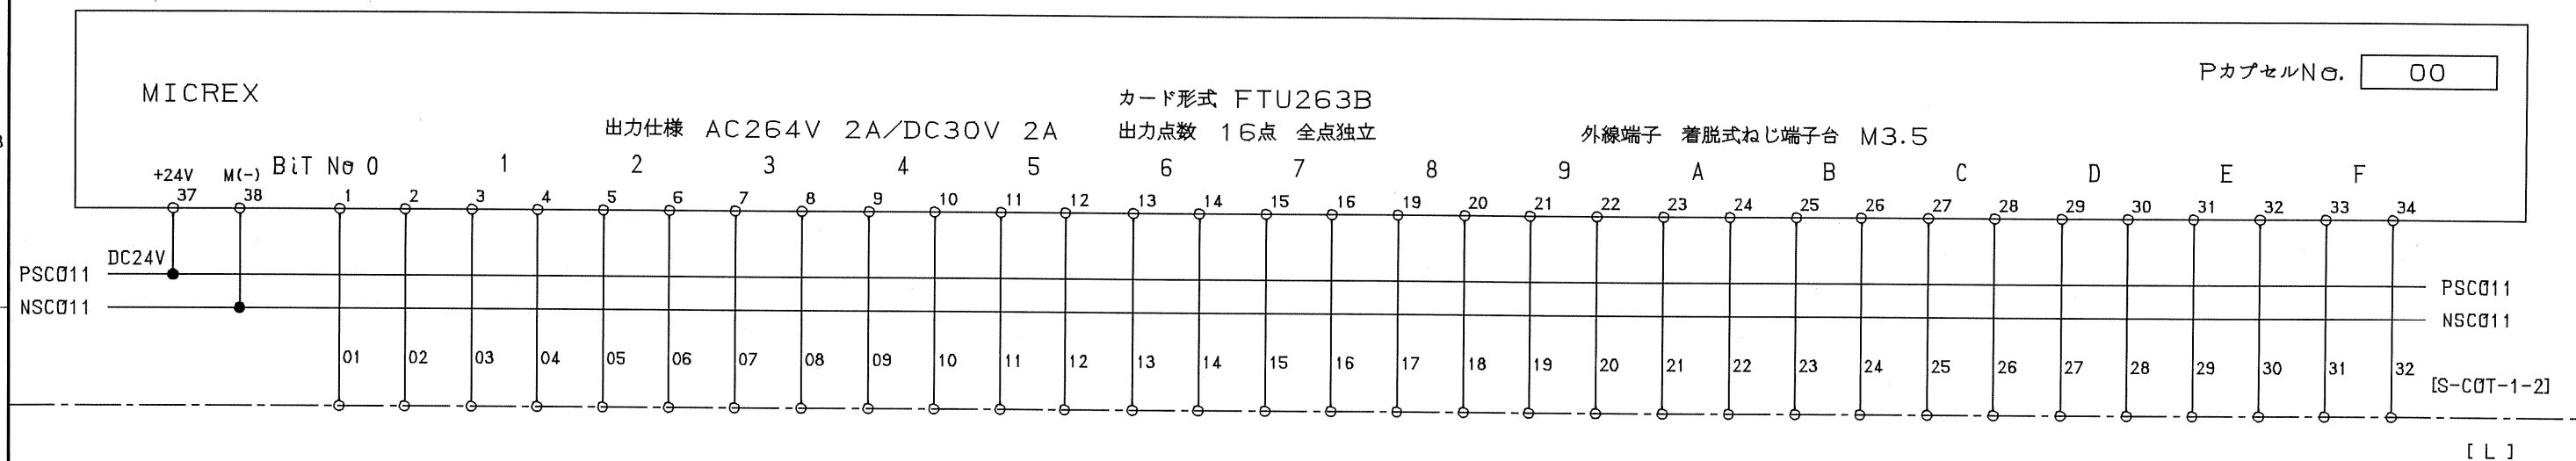


Revisions	○		Date	Name	Fuji Electric Co.,Ltd.	Title	河頭管轄入出力制御装置	Ref. Dwg. No.	W426297	374	シ イ			
	○		Drawn	2000-02-18								河野		
	①	アドレス変更・信号削除	' 00-08-21	野崎								Checked		
	②	信号名称変更	' 00-04-24	森竹										
A		B		C		D		E		F				

全点独立×16

ア ド レ ス	項 目 名 称	備 考
0.0600	予備	
0.0601	予備	
0.0602	予備	
0.0603	予備	
0.0604	予備	
0.0605	予備	
0.0606	予備	
0.0607	予備	
0.0608	予備	
0.0609	予備	
0.060A	予備	
0.060B	予備	
0.060C	予備	
0.060D	予備	
0.060E	予備	
0.060F	予備	

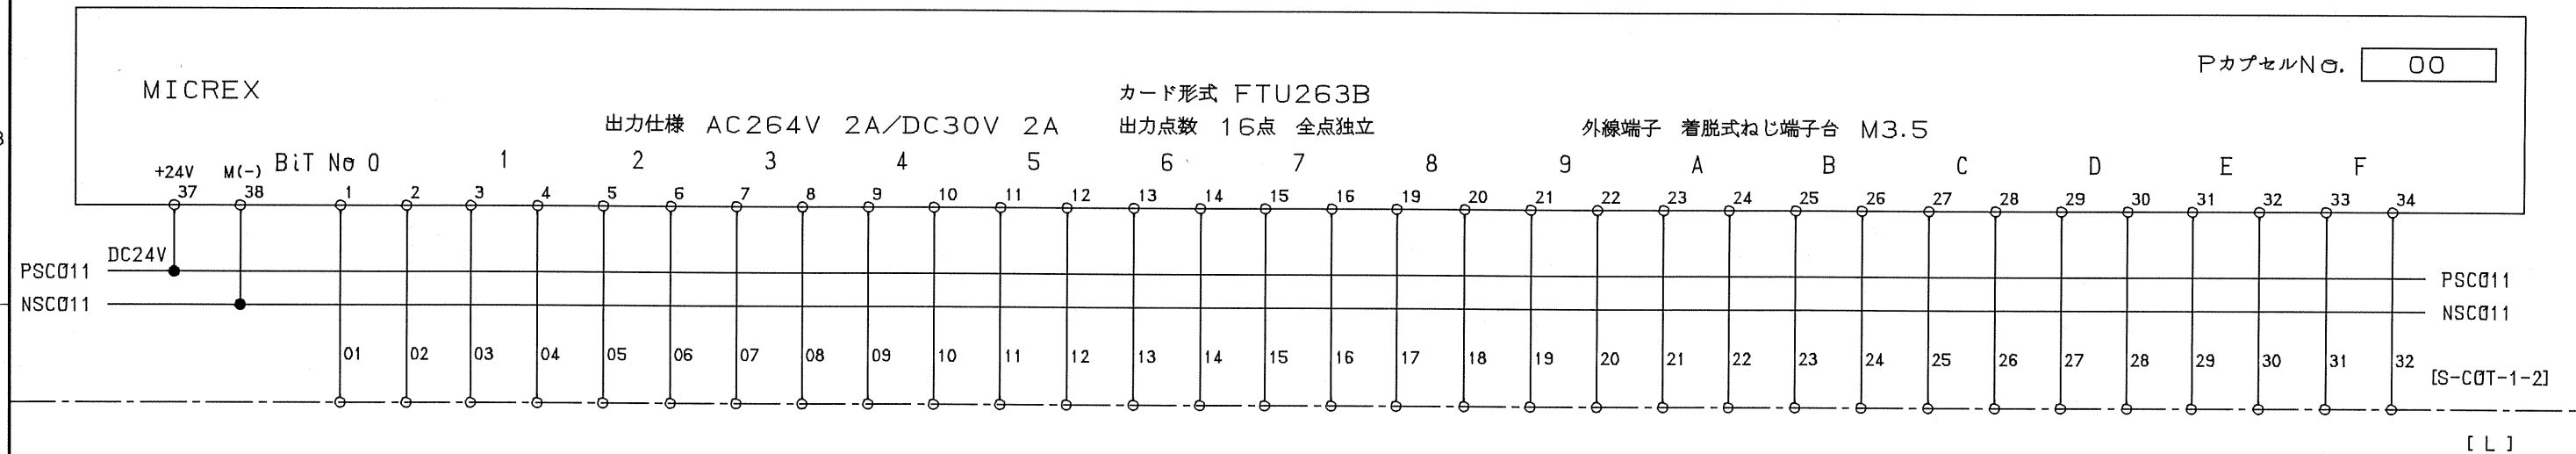

Revisions	○			Date	Name	Fuji Electric Co.,Ltd.	Title	河頭管轄入出力制御装置	Ref. Dwg. No.	W 4 2 6 2 9 7	375	チ イ			
	○			Drawn	2000-02-18								河野		
	①	アドレス変更・信号削除	' 00-08-21	野崎	Checked										
	②	信号名称変更	' 00-04-24	森竹											
A		B		C		D		E		F		G		H	

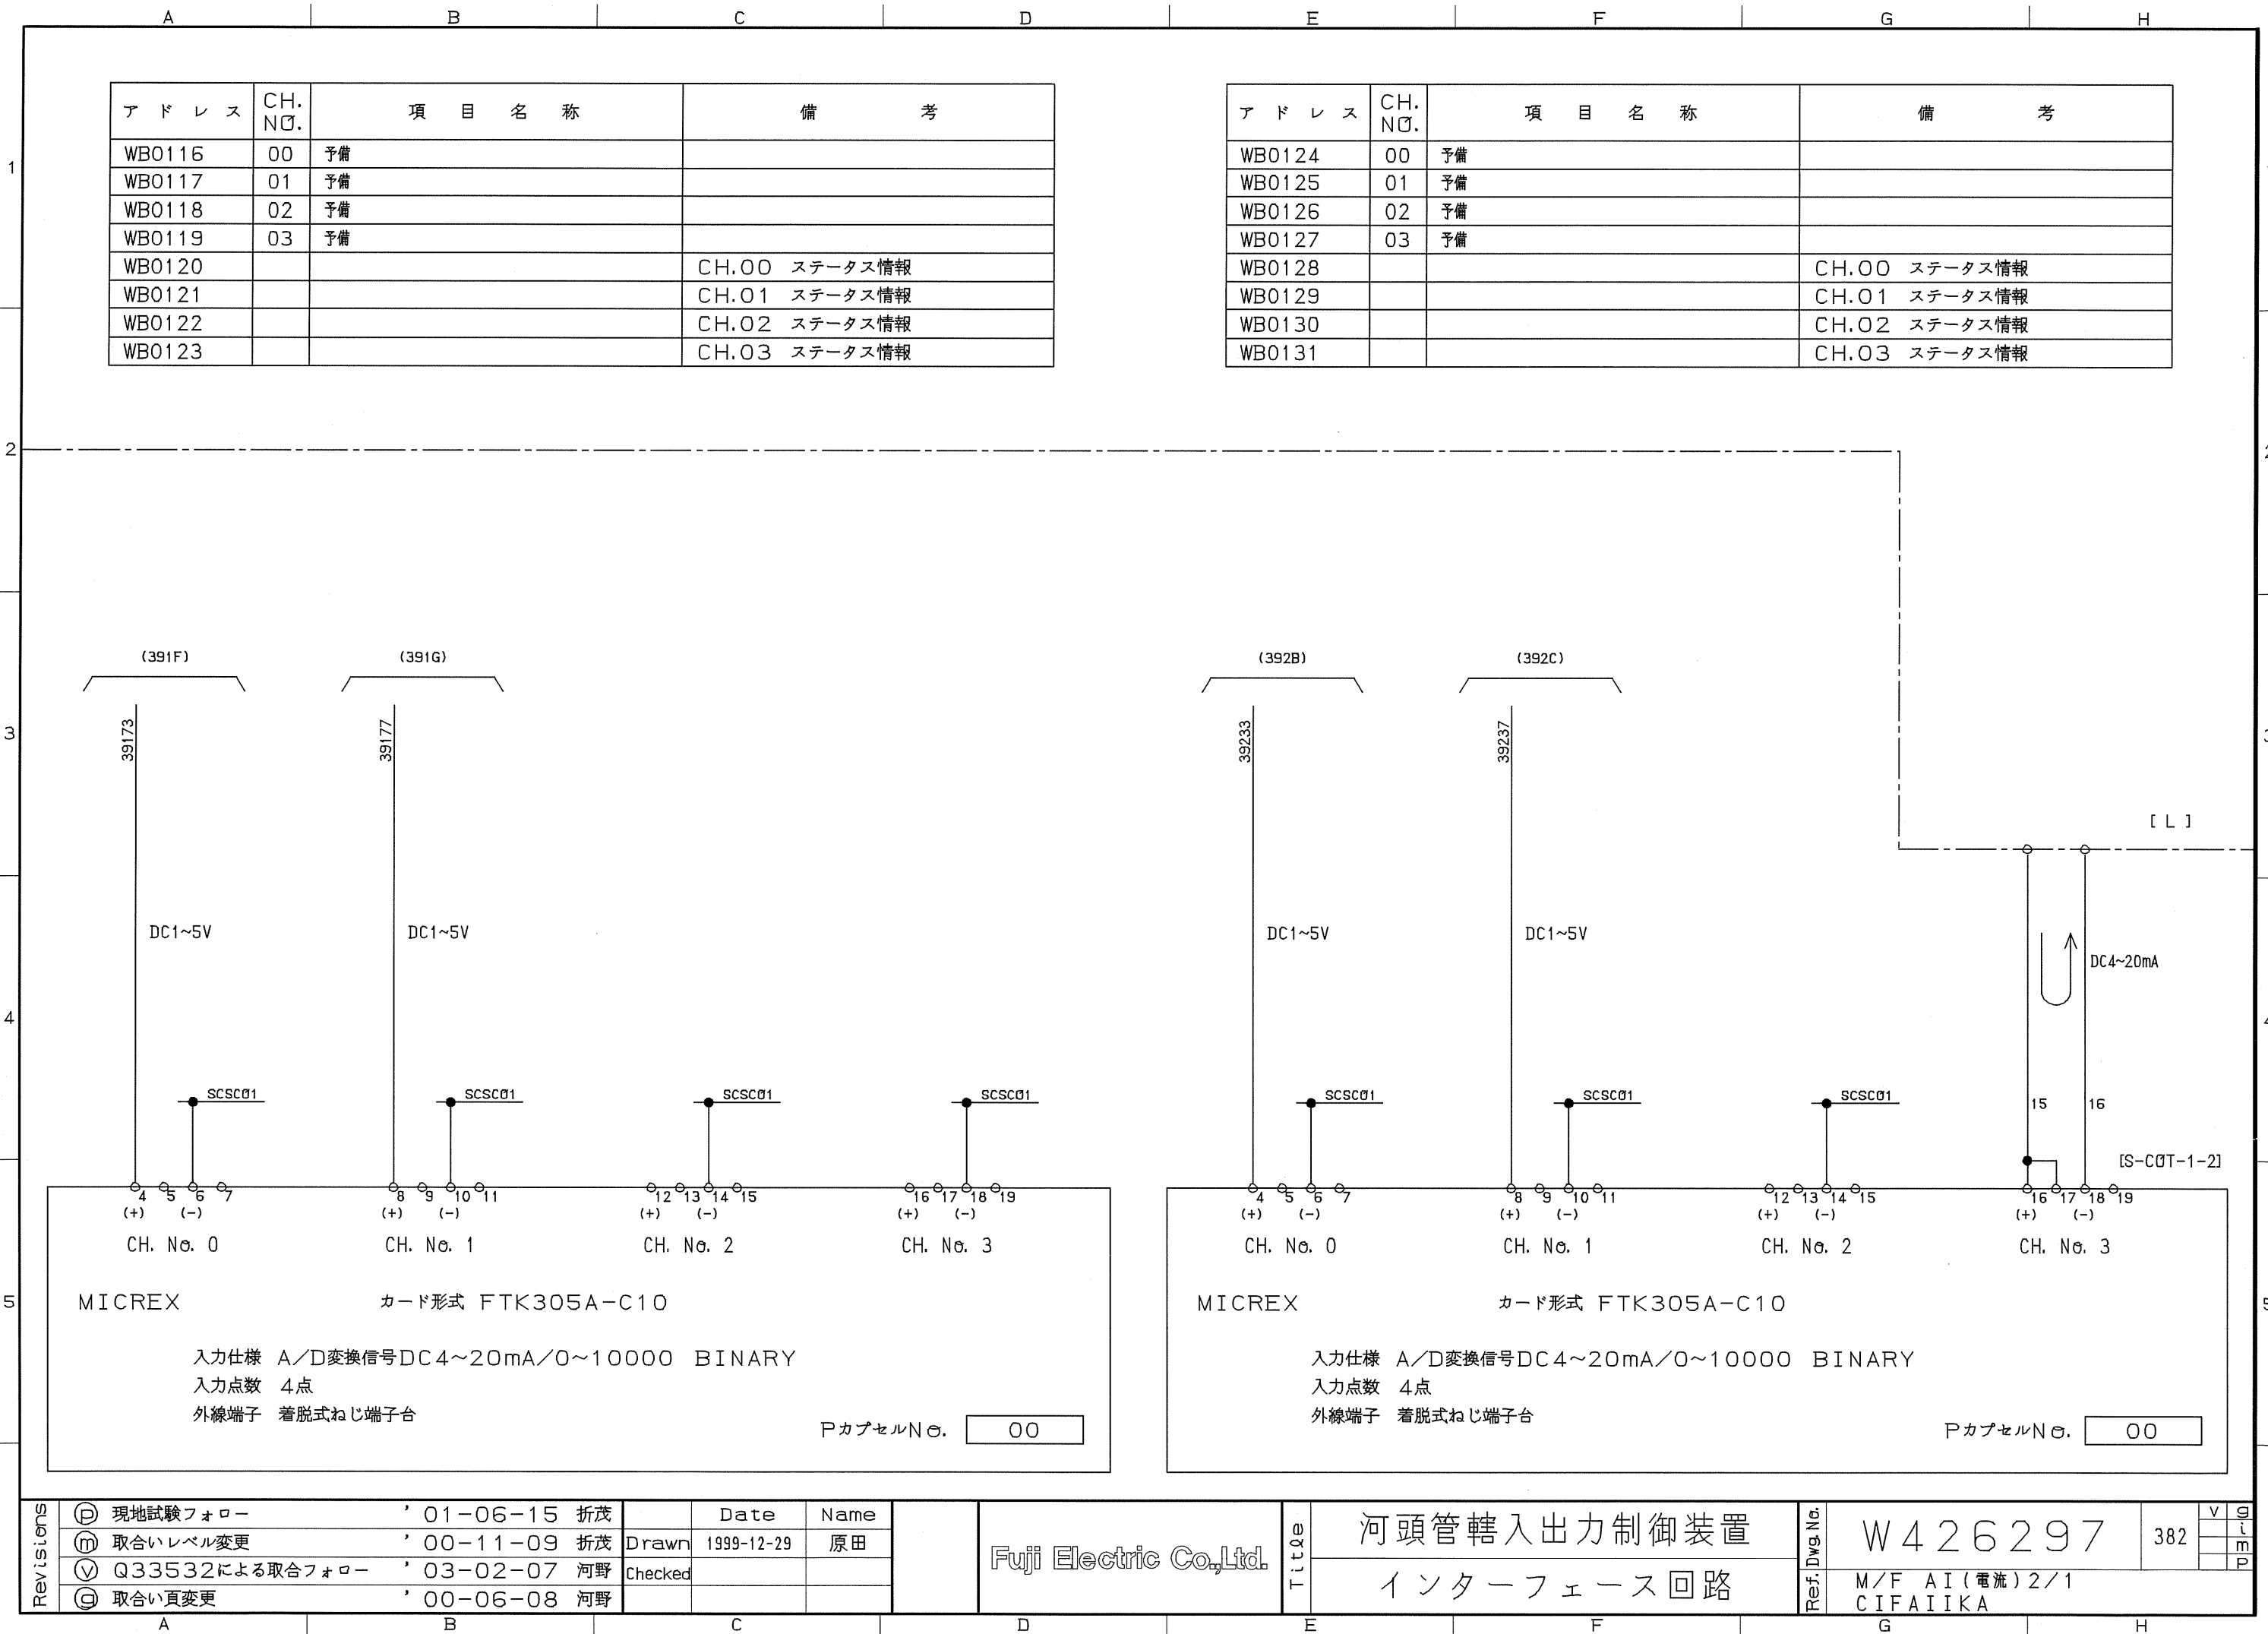

1

2

3

4

5

WB0124

WB0125

WB0126

WB0127

WB0128

WB0129

WB0130

WB0131

00

01

02

03

予備

予備

予備

予備

CH.00 ステータス情報

CH.01 ステータス情報

CH.02 ステータス情報

CH.03 ステータス情報

3

4

5

(392B)

(392C)

39233

39237

DC1~5V

DC1~5V

SCSC01

SCSC01

4 (+)

5 (-)

6 (+)

7 (-)

8 (+)

9 (-)

10 (+)

11 (-)

12 (+)

13 (-)

14 (+)

15 (-)

16 (+)

17 (-)

18 (+)

19 (-)

CH. No. 0

CH. No. 1

CH. No. 2

CH. No. 3

MICREX

カード形式 FTK305A-C10

入力仕様 A/D変換信号DC4~20mA/0~10000 BINARY

入力点数 4点

外線端子 着脱式ねじ端子台

PカプセルNo.

00

3

4

5

(392C)

39237

DC1~5V

SCSC01

4 (+)

5 (-)

6 (+)

7 (-)

8 (+)

9 (-)

10 (+)

11 (-)

12 (+)

13 (-)

14 (+)

15 (-)

16 (+)

17 (-)

18 (+)

19 (-)

CH. No. 3

[L]

DC4~20mA

IS-C0T-1-2]

Revisions

① 現地試験フォロー

② 取合いレベル変更

③ Q33532による取合フォロー

④ 取合い頁変更

01-06-15 折茂

00-11-09 折茂

03-02-07 河野

00-06-08 河野

Date

1999-12-29

Name

原田

Drawn

Checked

Fuji Electric Co.,Ltd.

河頭管轄入出力制御装置

インターフェース回路

Ret.Dwg.No.

W426297

M/F AI(電流)2/1

CIFAIIKA

382

V

g



l

m

P

アドレス	CH. NO.	項目名称	備考
WB0132	00	予備	
WB0133	01	予備	
WB0134	02	予備	
WB0135	03	予備	
WB0136			CH.00 ステータス情報
WB0137			CH.01 ステータス情報
WB0138			CH.02 ステータス情報
WB0139			CH.03 ステータス情報



アドレス	CH. NO.	項目名称	備考
WB0140	00	予備	
WB0141	01	予備	
WB0142	02	予備	
WB0143	03	予備	
WB0144			CH.00 ステータス情報
WB0145			CH.01 ステータス情報
WB0146			CH.02 ステータス情報
WB0147			CH.03 ステータス情報

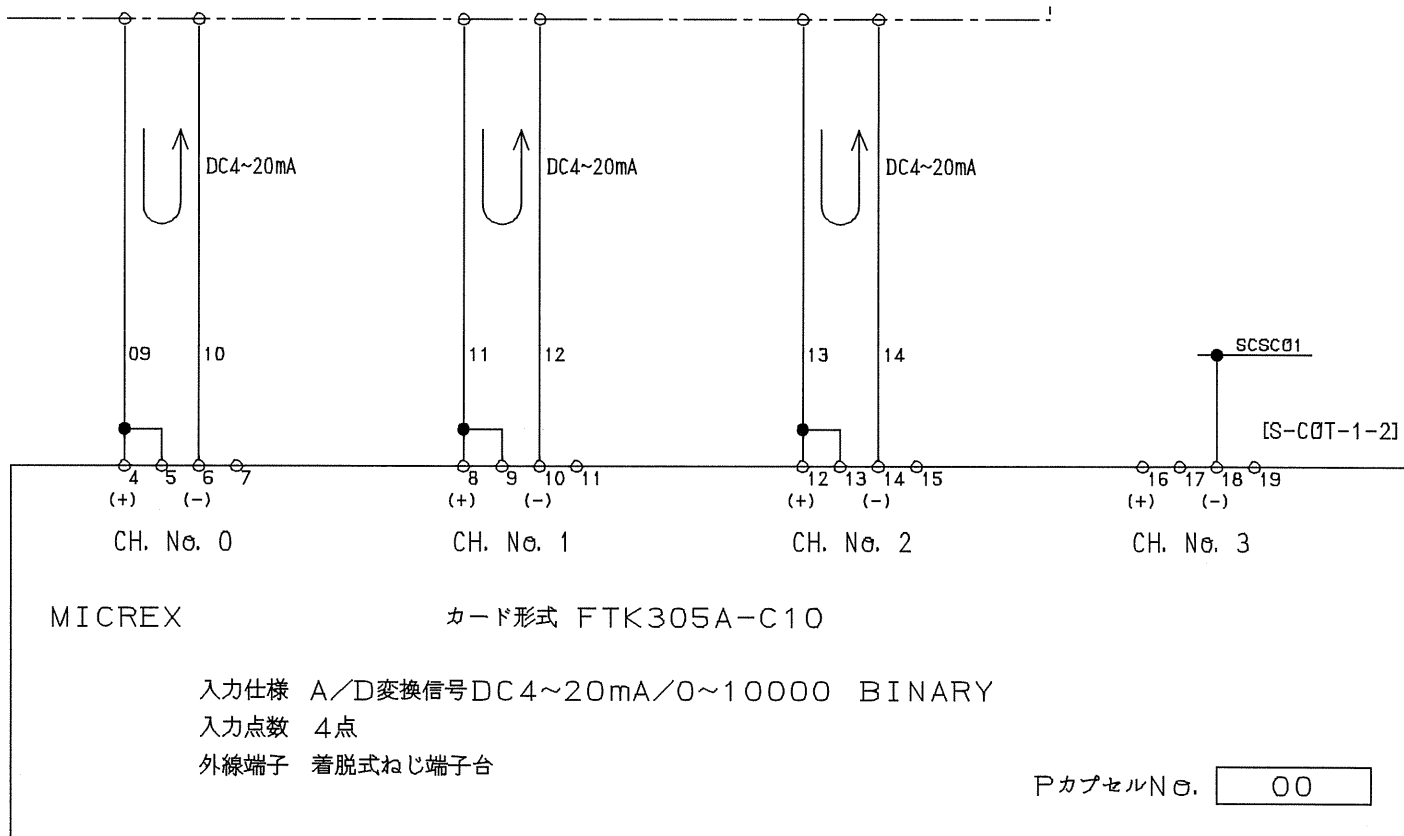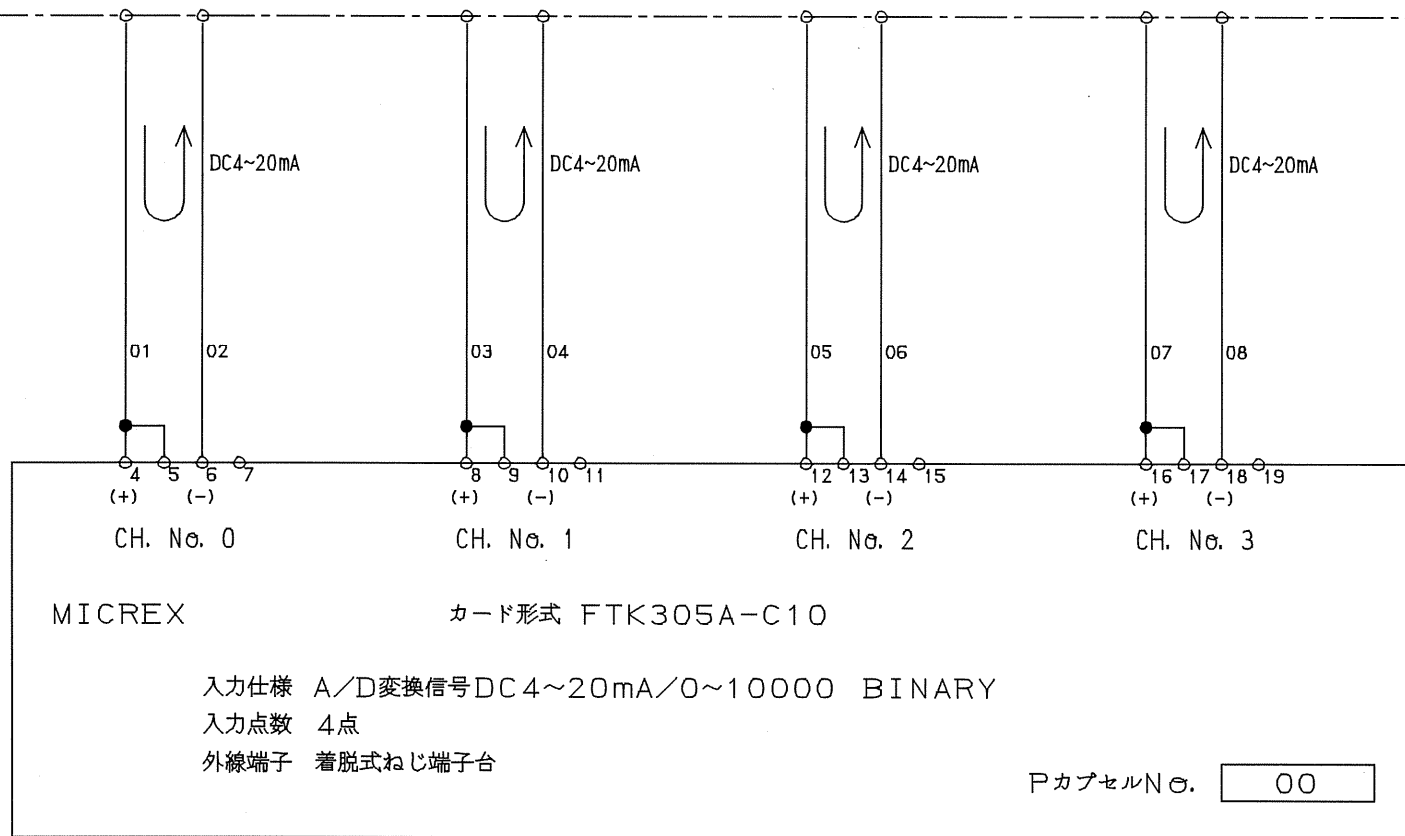

Revisions	①	現地試験フォロー	' 01-06-15	折茂		Date	Name	Fuji Electric Co., Ltd.	E	河頭管轄入出力制御装置 インターフェース回路	Ref. Dwg. No.	W426297	383	V g i m P
	②	取合いレベル変更	' 00-11-09	折茂	Drawn	1999-12-29	原田							
	③	信号削除・取合いフォロー	' 00-08-21	野崎	Checked									
	④	Q33532による取合フォロー	' 03-02-07	河野										



アドレス	CH. NO.	項目名称	備考
WB0148	00	予備	
WB0149	01	予備	
WB0150	02	予備	
WB0151	03	予備	
WB0152			CH.00 ステータス情報
WB0153			CH.01 ステータス情報
WB0154			CH.02 ステータス情報
WB0155			CH.03 ステータス情報

アドレス	CH. NO.	項目名称	備考
WB0156	00	予備	
WB0157	01	予備	
WB0158	02	予備	
WB0159	03	予備	
WB0160			CH.00 ステータス情報
WB0161			CH.01 ステータス情報
WB0162			CH.02 ステータス情報
WB0163			CH.03 ステータス情報

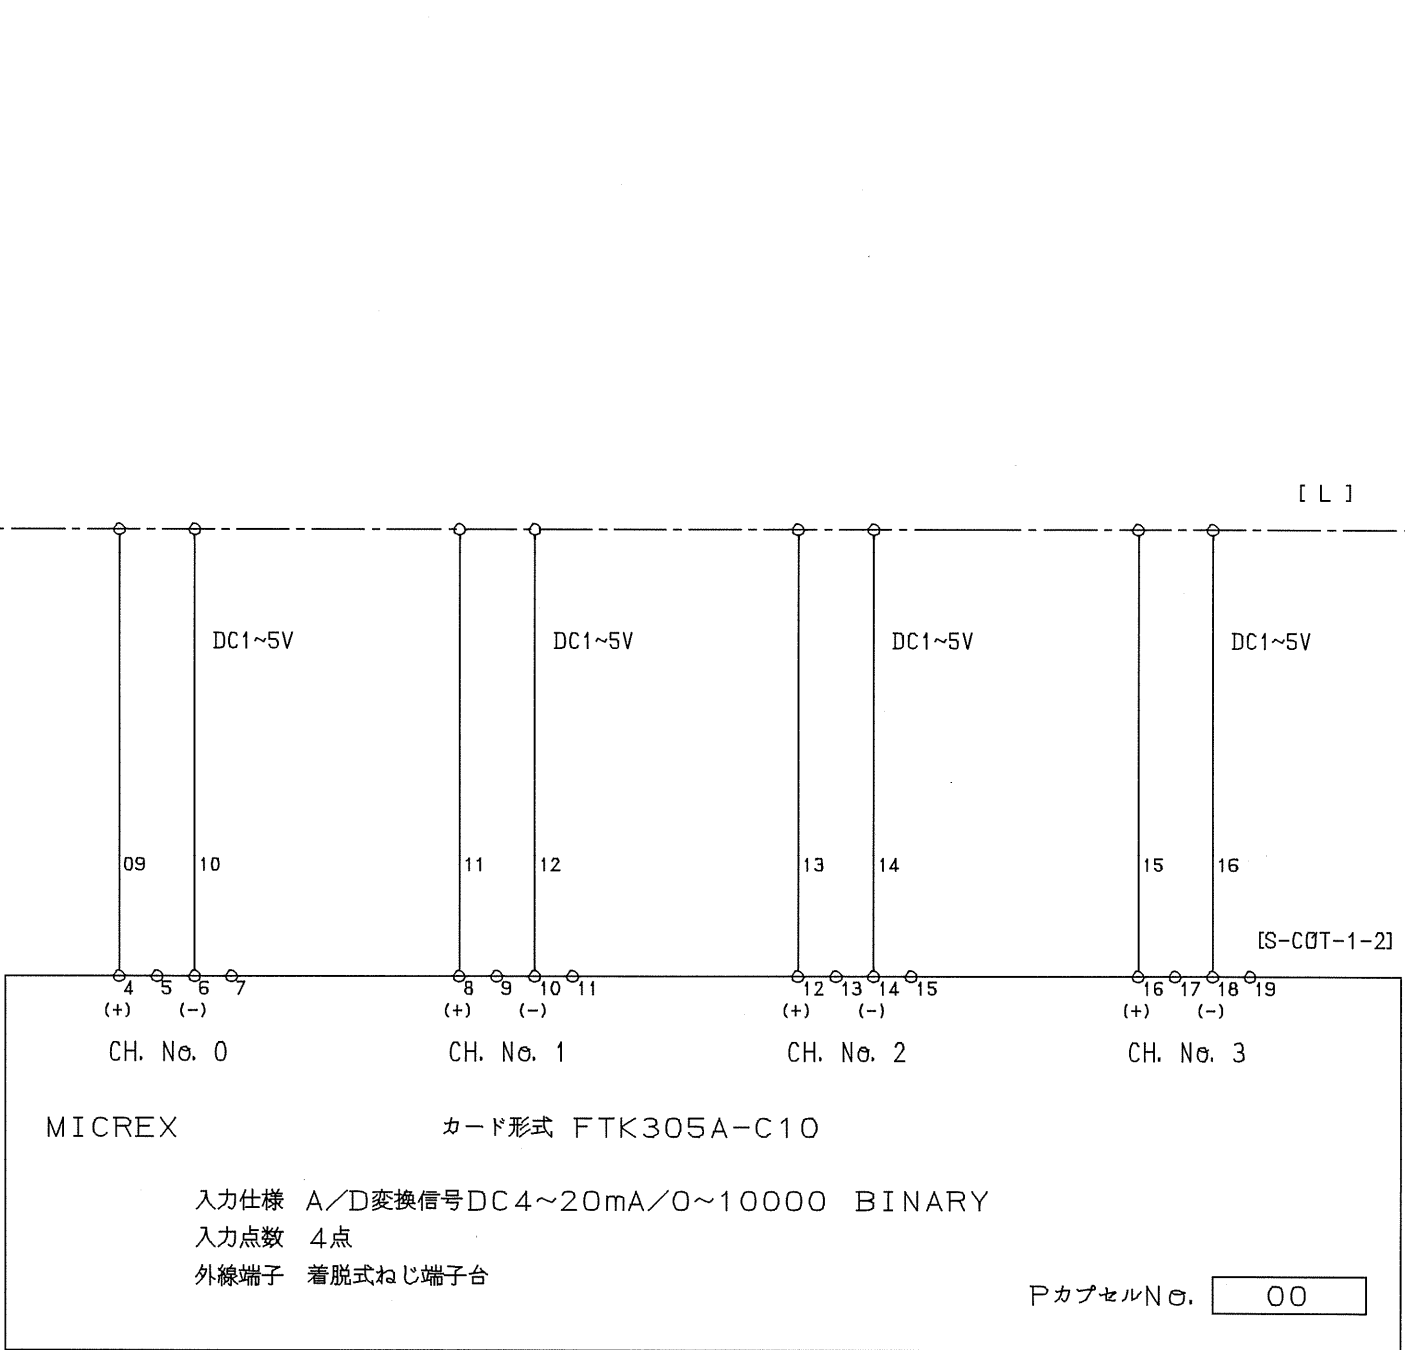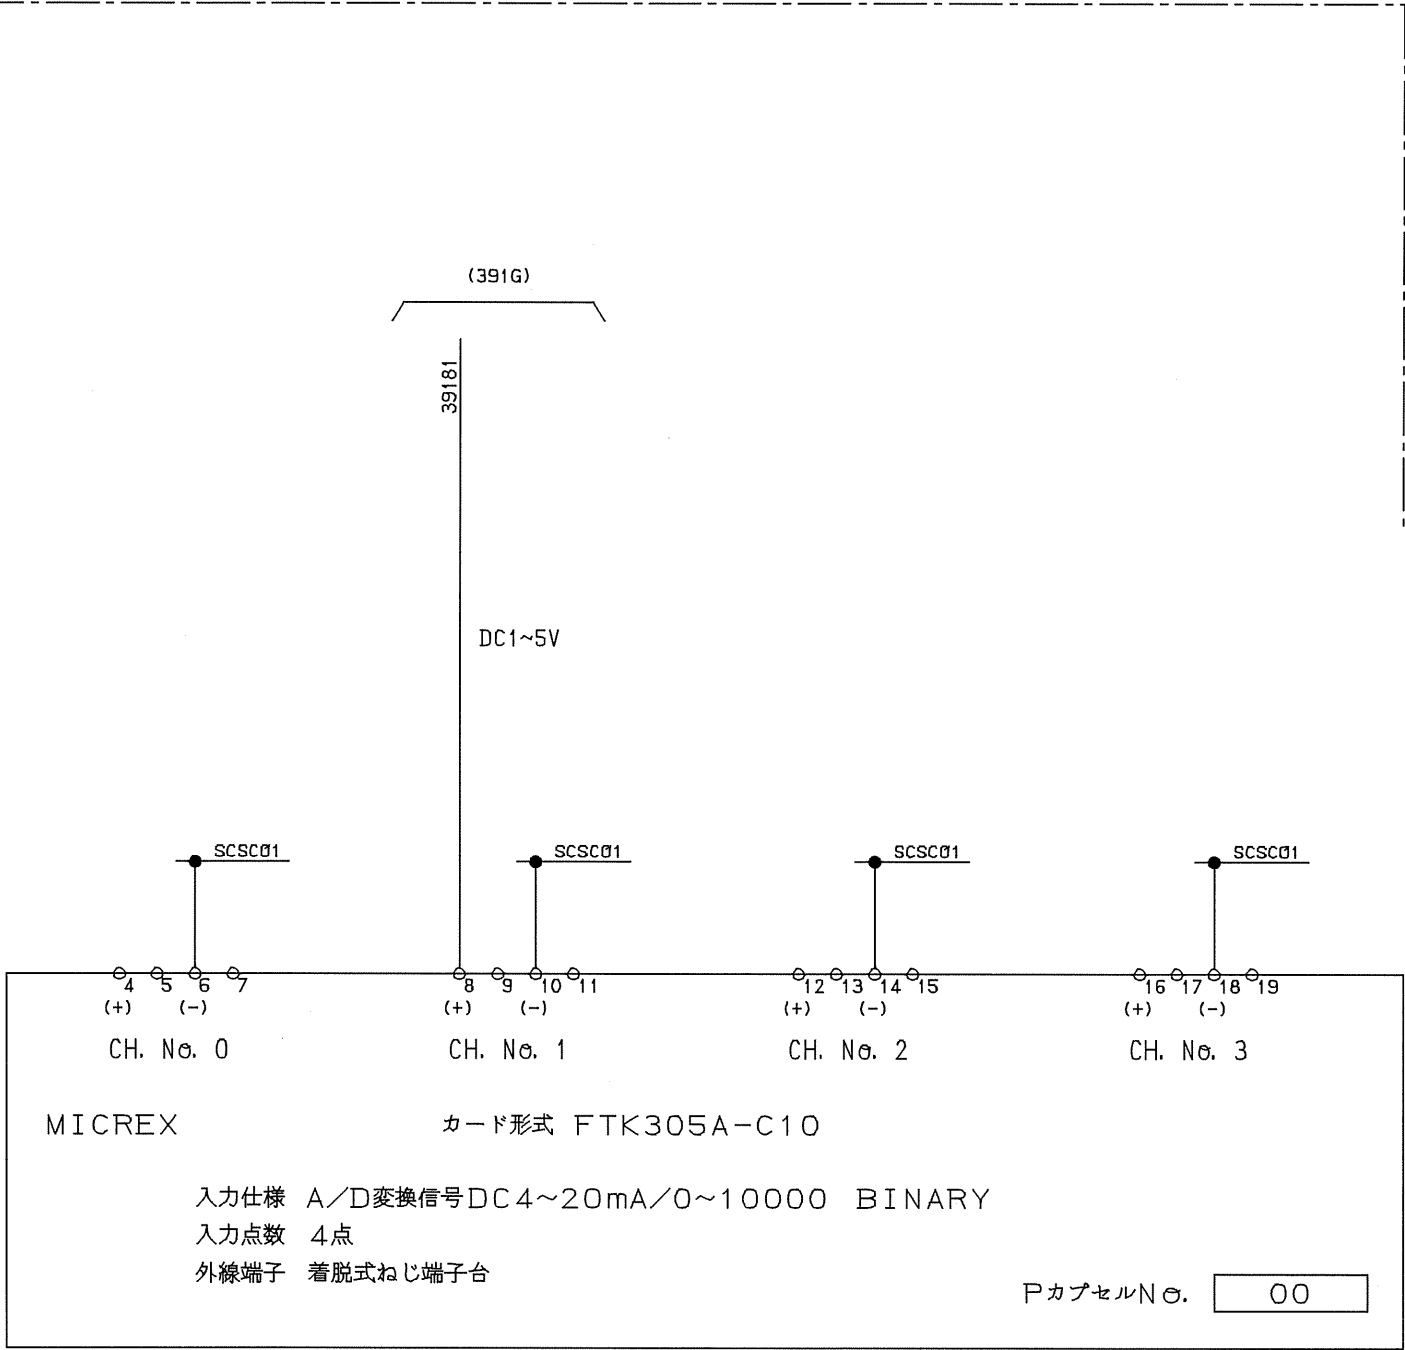

アドレス	CH. NO.	項目名称	備考
WB0200	00	予備	
WB0201	01		
WB0202	02		
WB0203	03		
WB0204			CH.00 ステータス情報
WB0205			CH.01 ステータス情報
WB0206			CH.02 ステータス情報
WB0207			CH.03 ステータス情報


アドレス	CH. NO.	項目名称	備考
WB0208	00		
WB0209	01		
WB0210	02		
WB0211	03		
WB0212			CH.00 ステータス情報
WB0213			CH.01 ステータス情報
WB0214			CH.02 ステータス情報
WB0215			CH.03 ステータス情報

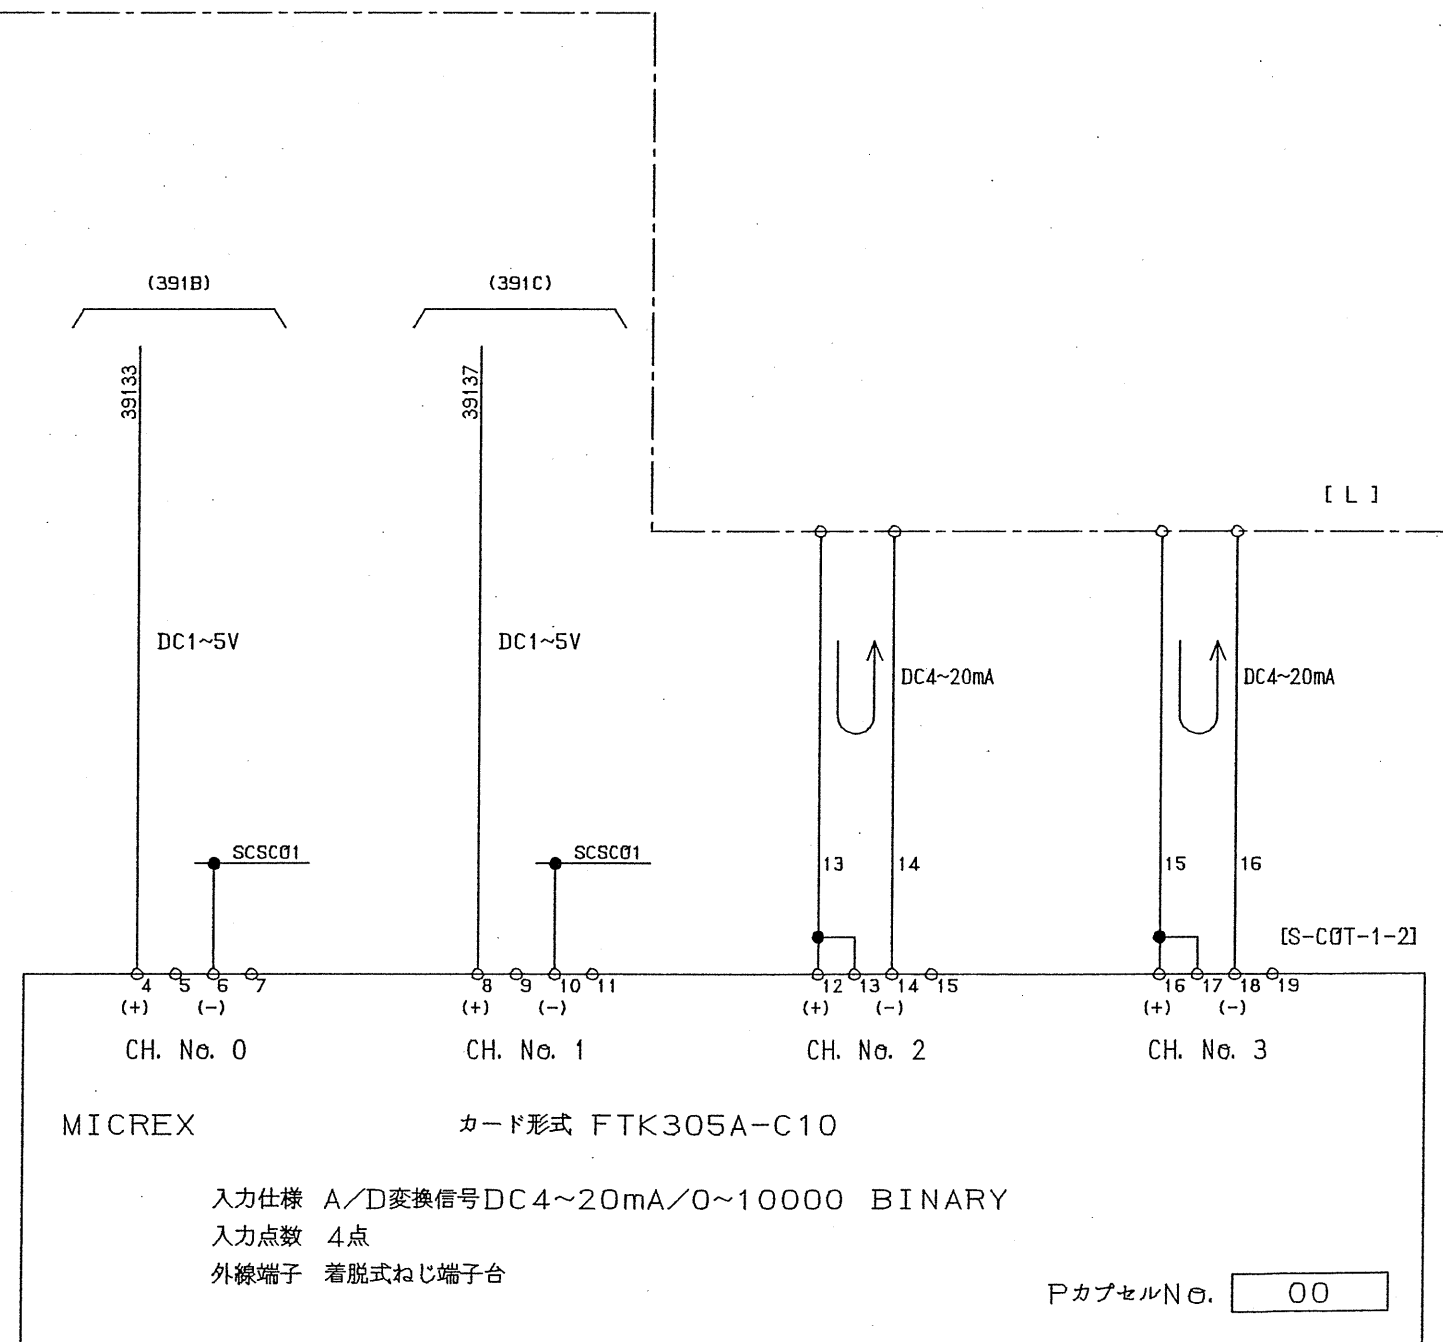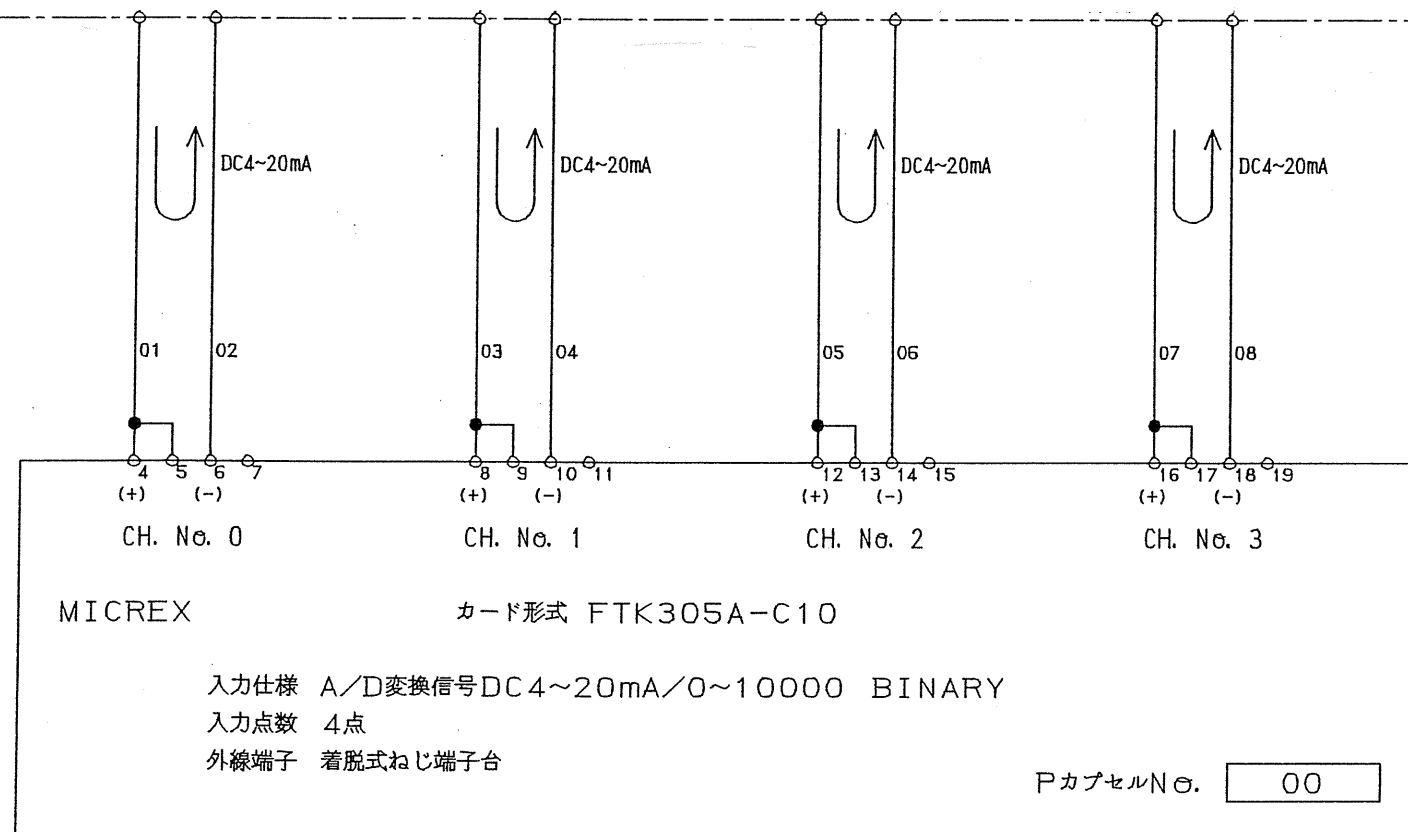

Revisions	① 現地試験フォロー	01-06-15 折茂	Date	Name	Fuji Electric Co., Ltd.	河頭管轄入出力制御装置 インターフェース回路	Rev. No.	W426297	387	A g l m P
	② ケアレスミスフォロー	00-11-09 折茂	Drawn	1999-12-29 原田						
	③ 取合いフォロー	00-08-21 野崎	Checked							
	④ C483071による改造	06-12-25 青木								

アドレス	CH. NO.	項目名称	備考
WB0216	00	予備	
WB0217	01	予備	
WB0218	02	予備	
WB0219	03	予備	
WB0220			CH.00 ステータス情報
WB0221			CH.01 ステータス情報
WB0222			CH.02 ステータス情報
WB0223			CH.03 ステータス情報



アドレス	CH. NO.	項目名称	備考
WB0224	00	予備	
WB0225	01	予備	
WB0226	02	予備	
WB0227	03	予備	
WB0228			CH.00 ステータス情報
WB0229			CH.01 ステータス情報
WB0230			CH.02 ステータス情報
WB0231			CH.03 ステータス情報

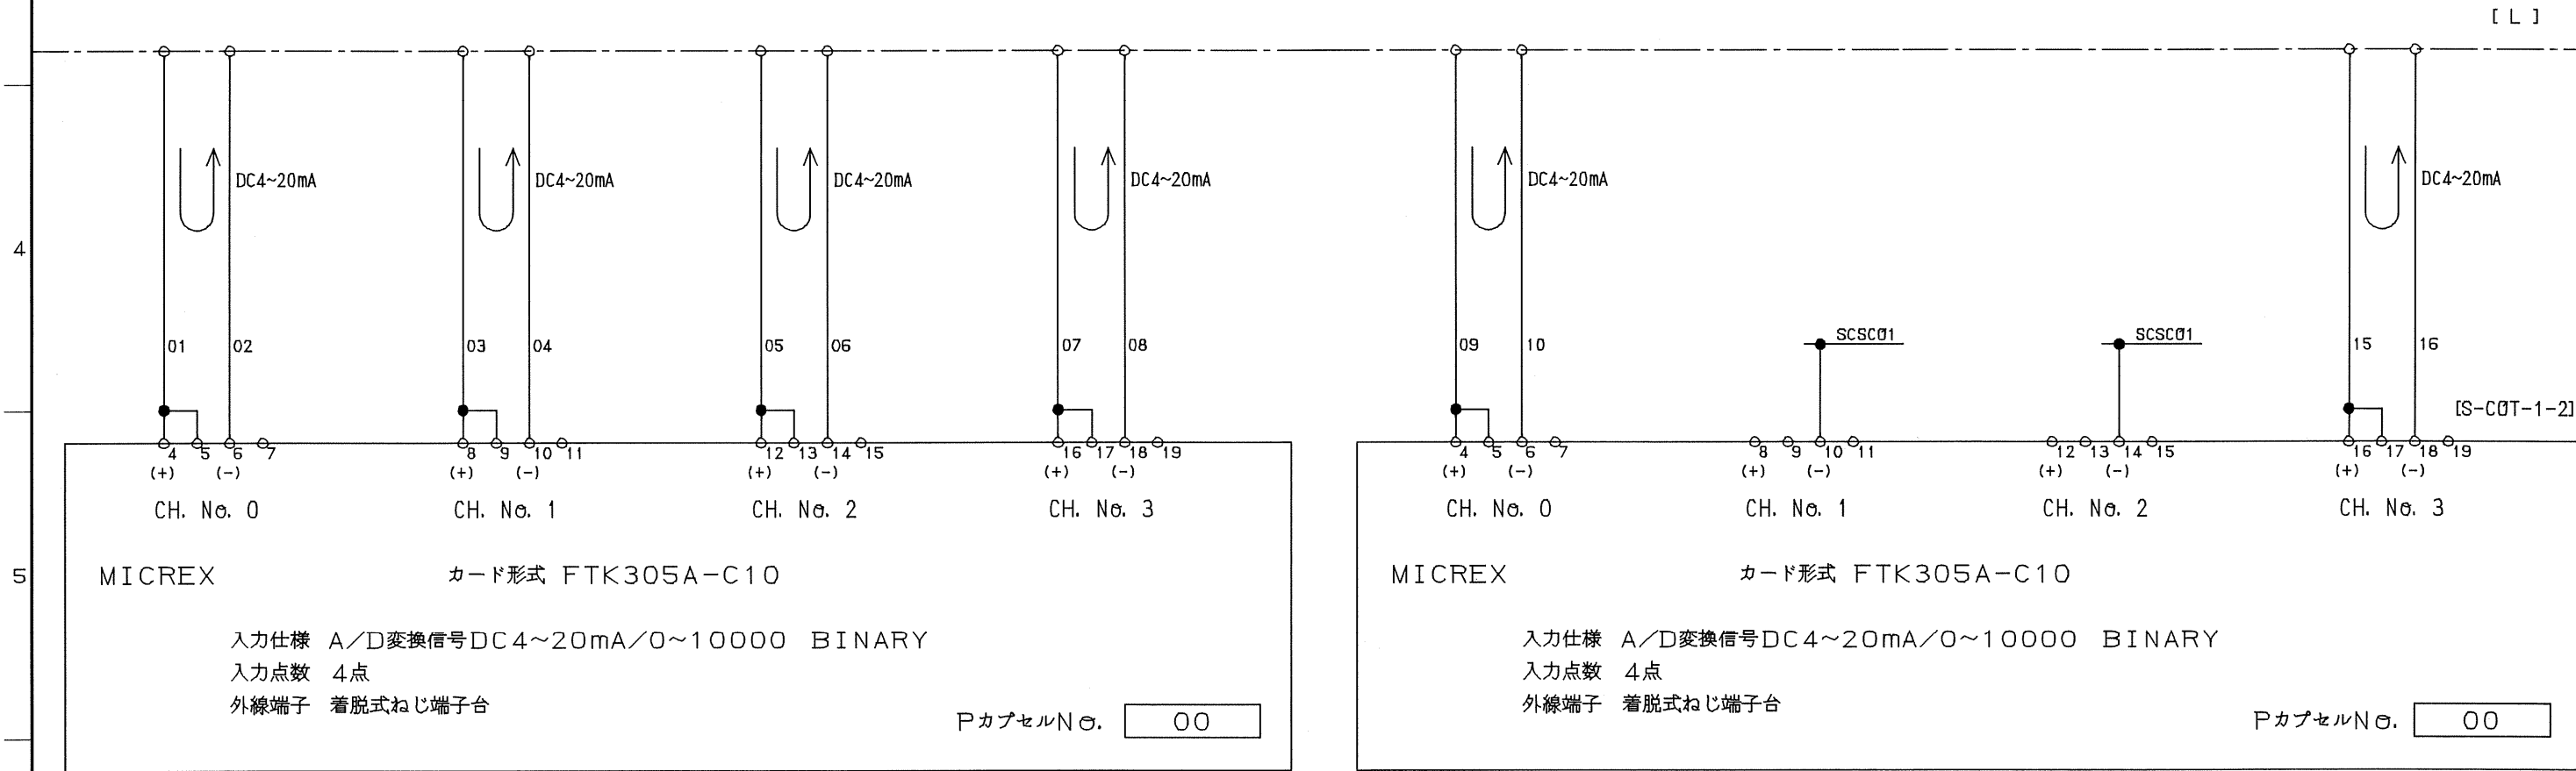

Revisions	○			Date	Name	Fuji Electric Co.,Ltd.	Title	河頭管轄入出力制御装置 インターフェース回路	Ref. Dwg. No.	W426297	388	M/F AI(電流)2/1 CIFAIKA			
	②	現地試験フォロー	' 01-06-15	折茂	Drawn								1999-12-29	原田	
	①	信号削除・取合い削除	' 00-08-21	野崎	Checked										
	③	取合い頁変更	' 00-06-08	河野											
A		B		C		D		E		F		G		H	

アドレス	CH. NO.	項目名称	備考
WB0232	00	予備	
WB0233	01	予備	
WB0234	02	予備	
WB0235	03	予備	
WB0236			CH.00 ステータス情報
WB0237			CH.01 ステータス情報
WB0238			CH.02 ステータス情報
WB0239			CH.03 ステータス情報


アドレス	CH. NO.	項目名称	備考
WB0240	00	予備	
WB0241	01	予備	
WB0242	02	予備	
WB0243	03	予備	
WB0244			CH.00 ステータス情報
WB0245			CH.01 ステータス情報
WB0246			CH.02 ステータス情報
WB0247			CH.03 ステータス情報

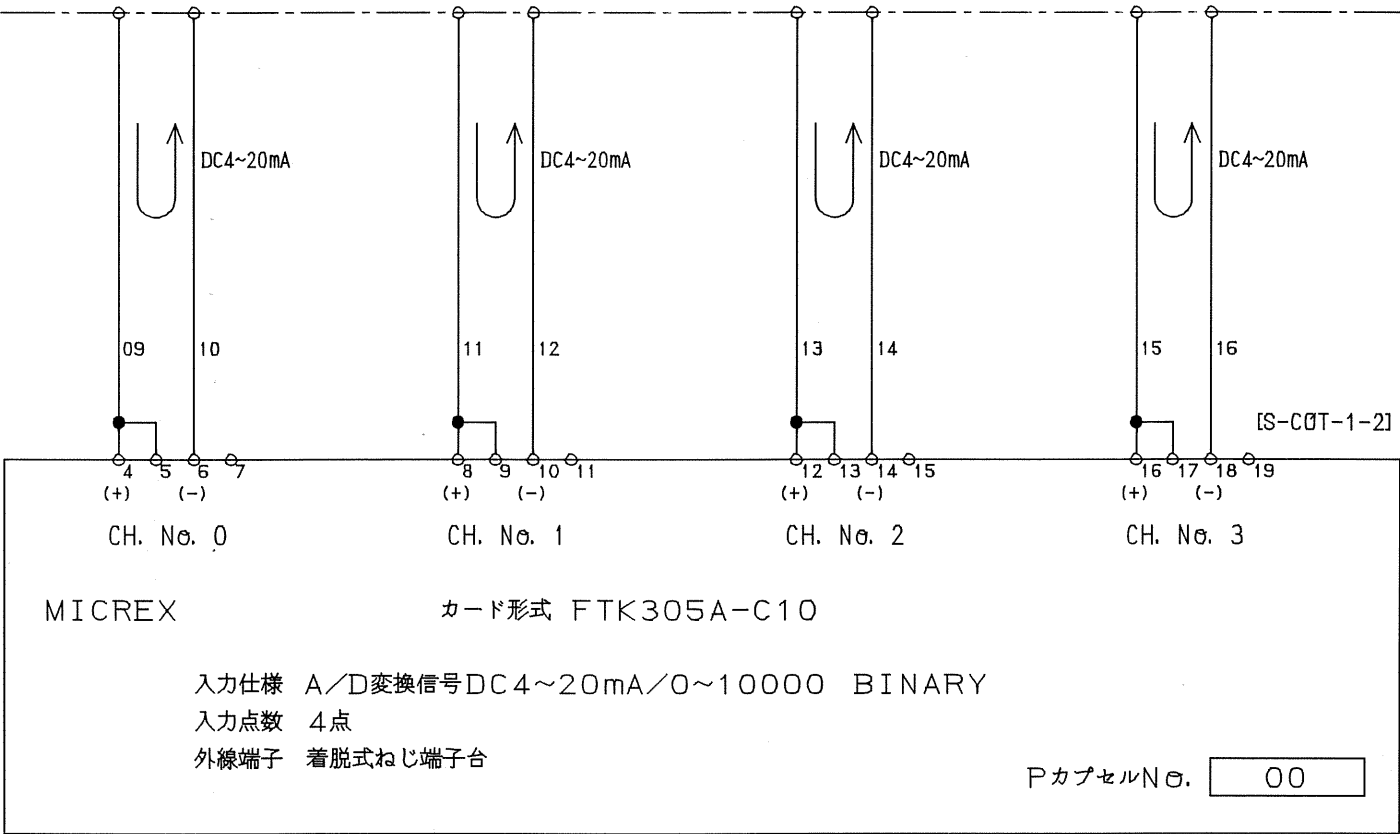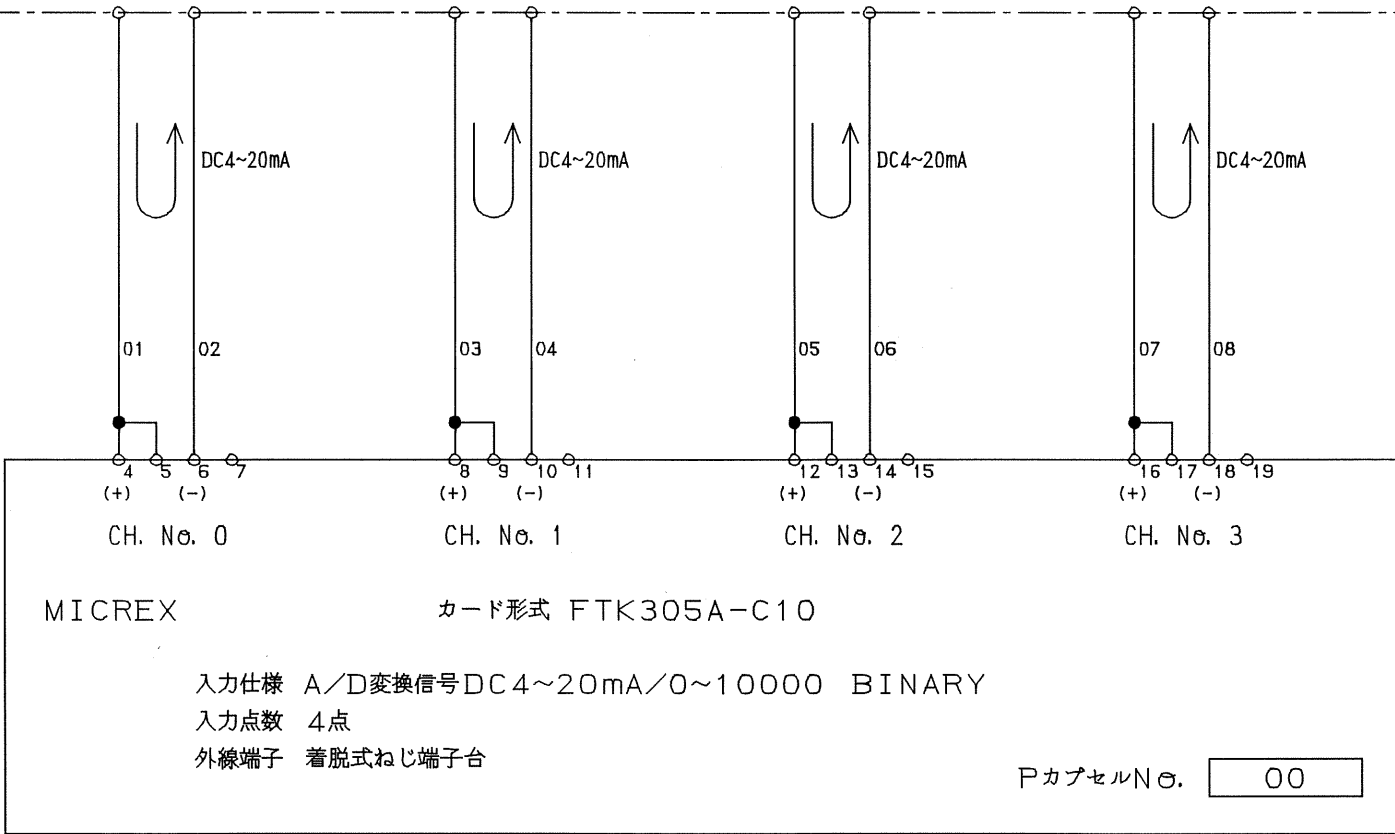

Revisions	○			Date	Name	Fuji Electric Co.,Ltd.	Title	河頭管轄入出力制御装置 インターフェース回路	Ref. Dwg. No.	W 4 2 6 2 9 7	389	f i P			
	Ⓐ	現地試験フォロー	' 01-06-15	折茂	Drawn								2000-02-18	河野	
	Ⓘ	信号削除	' 00-08-21	野崎	Checked										
	Ⓙ	信号名称・取合い信号変更	' 00-04-24	森竹											
A		B		C		D		E		F		G		H	

アドレス	CH. NO.	項目名称	備考
WB0248	00	予備	
WB0249	01	予備	
WB0250	02	予備	
WB0251	03	予備	
WB0252			CH.00 ステータス情報
WB0253			CH.01 ステータス情報
WB0254			CH.02 ステータス情報
WB0255			CH.03 ステータス情報



アドレス	CH. NO.	項目名称	備考
WB0256	00	予備	
WB0257	01	予備	
WB0258	02	予備	
WB0259	03	予備	
WB0260			CH.00 ステータス情報
WB0261			CH.01 ステータス情報
WB0262			CH.02 ステータス情報
WB0263			CH.03 ステータス情報

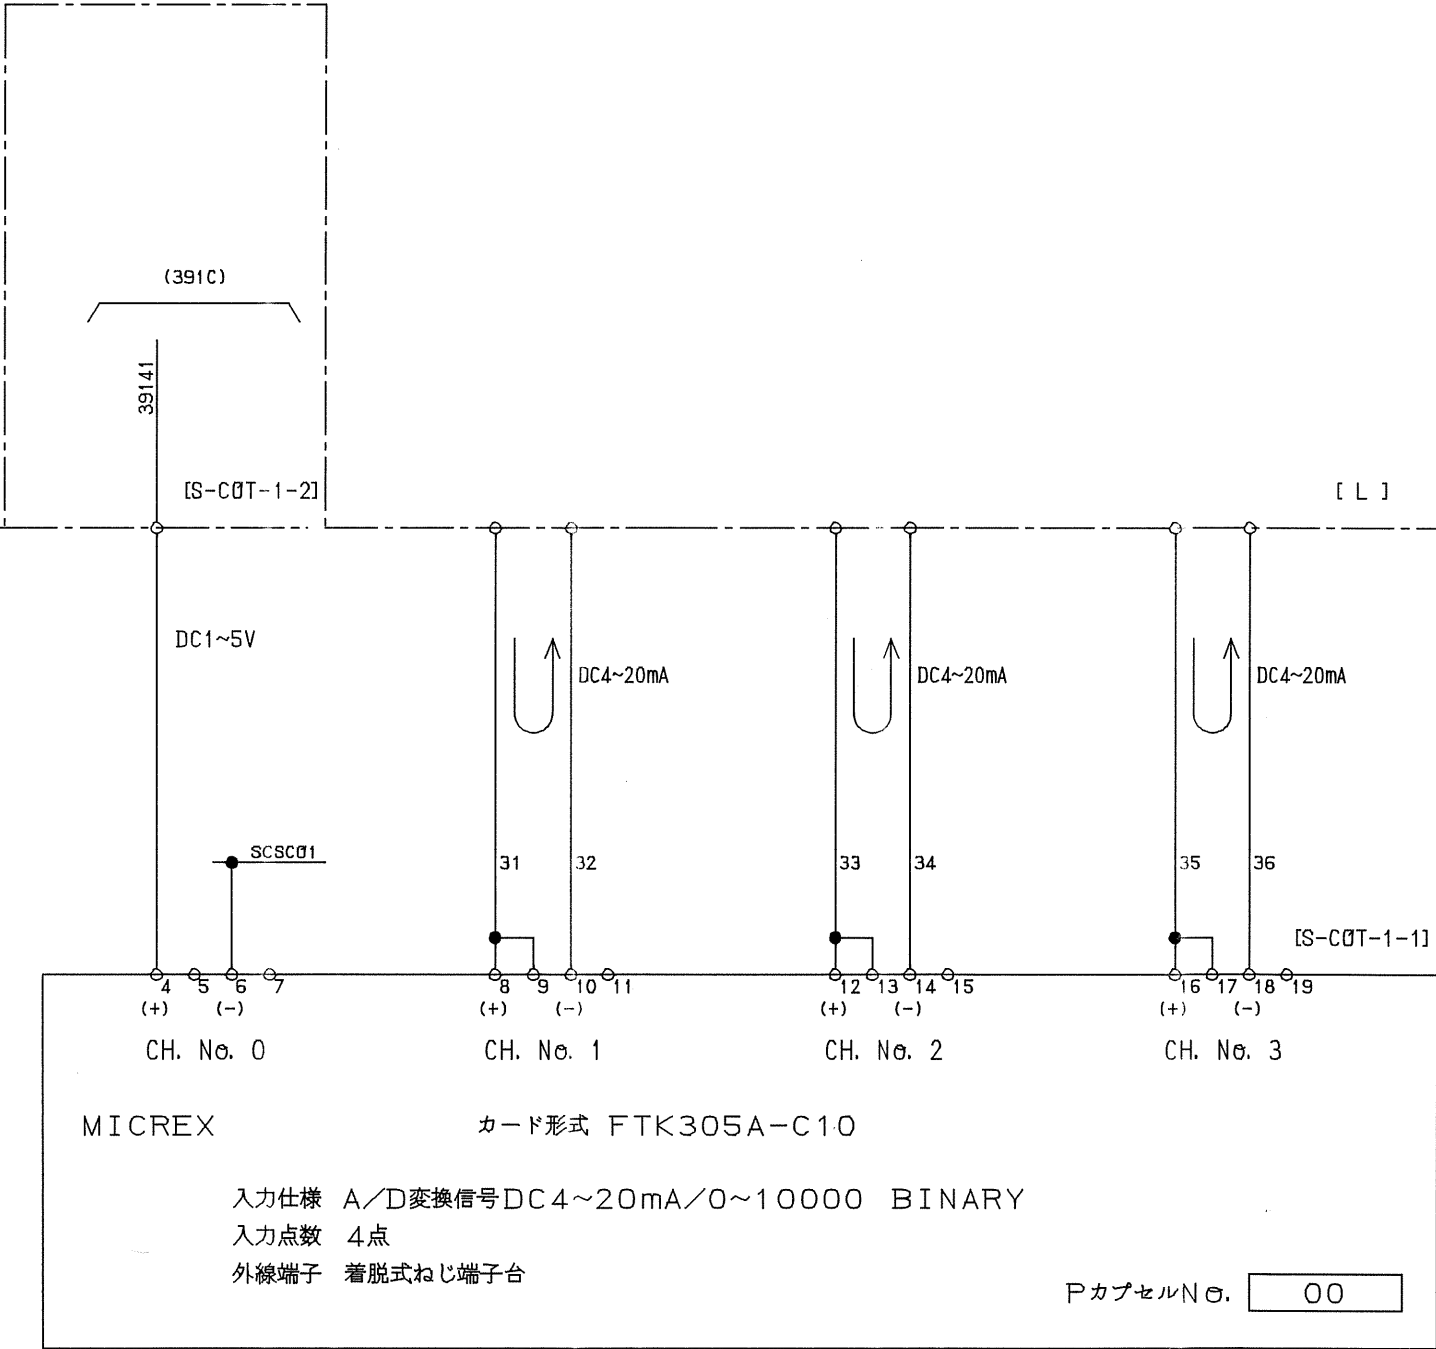

Revisions	①	現地試験フォロー	'	01-06-15	折茂		Date	Name	Fuji Electric Co., Ltd.	Title	河頭管轄入出力制御装置 インターフェース回路	Ref. Dwg. No.	W426297	389 -1	X L P	g t k P
	②	線番修正	'	00-09-20	折茂	Drawn	2000-06-08	河野								
	③	信号削除・取合いフォロー	'	00-08-21	野崎	Checked										
	④	テレメータ追加による取合変更	'	04-01-19	河野											

アドレス	CH. NO.	項目名称	備考
WB0264	00	予備	
WB0265	01	予備	
WB0266	02	予備	
WB0267	03	予備	
WB0268			CH.00 ステータス情報
WB0269			CH.01 ステータス情報
WB0270			CH.02 ステータス情報
WB0271			CH.03 ステータス情報

アドレス	CH. NO.	項目名称	備考
WB0272	00	予備	
WB0273	01	予備	
WB0274	02	予備	
WB0275	03	予備	
WB0276			CH.00 ステータス情報
WB0277			CH.01 ステータス情報
WB0278			CH.02 ステータス情報
WB0279			CH.03 ステータス情報

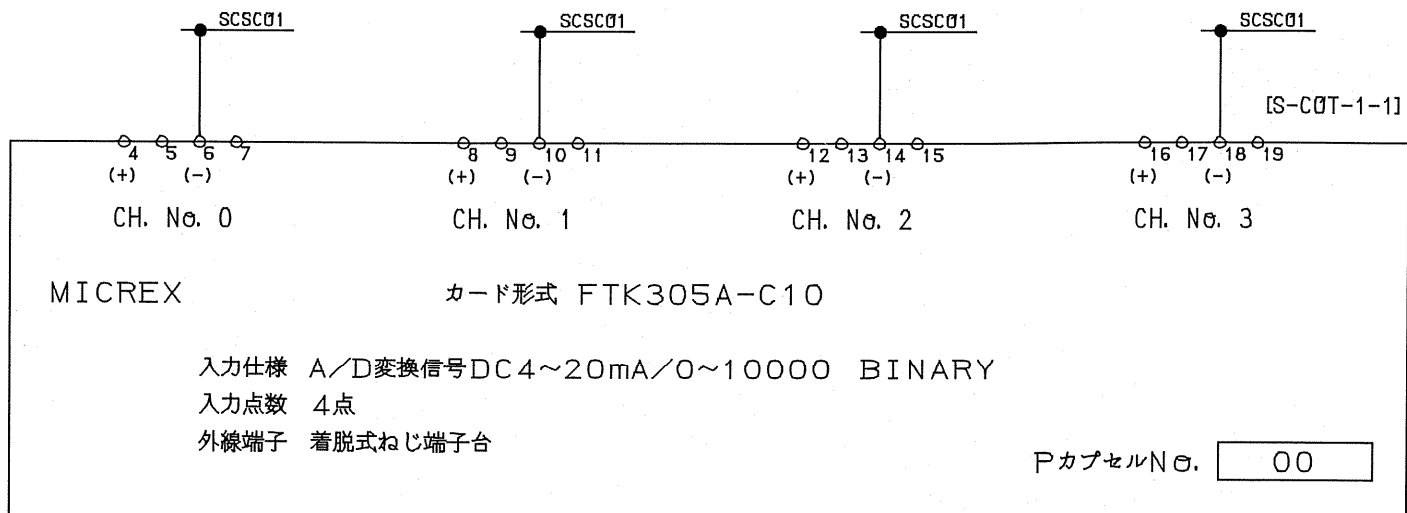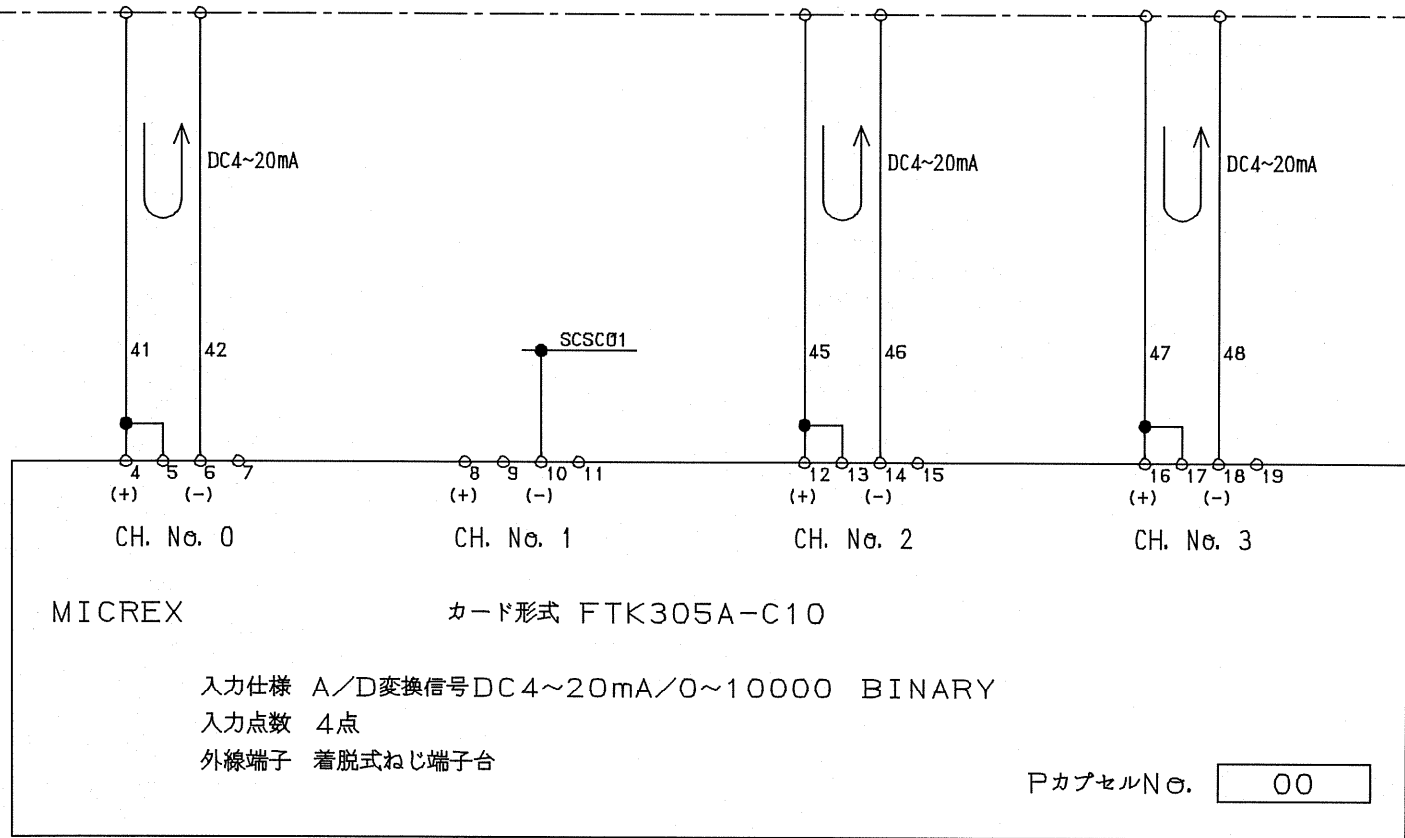

Revisions	⑤ 信号追加	' 02-02-08 河野	Date	Name	Fuji Electric Co., Ltd.	河頭管轄入出力制御装置 インターフェース回路	W426297	M/F AI(電流)2/1 CIFAI IKA	389 -2	t y p s
	⑥ 現地試験フォロー	' 01-06-15 折茂	Drawn	2000-06-08 河野						
	⑦ C18905による改造	' 04-12-03 森竹	Checked							
	⑧ 現地試験フォロー	' 02-04-03 河野								

遠方監視制御装置盤

[L]

[S-COT-1-2]

収納ケース
RSC011
<11056>
RS-19

AC100V 60Hz
(301E) RSC014
TSC014

電源ユニット
ZRSC011
<11055>
ZRS-10

E

アイソレータ
TRSC0101
<11057>
TRS-12

アイソレータ
TRSC0102
<11057>
TRS-12

アイソレータ
TRSC0103
<11057>
TRS-12

アイソレータ
TRSC0104
<11057>
TRS-12

アイソレータ
TRSC0105
<11057>
TRS-12

アイソレータ
TRSC0106
<11057>
TRS-12

アイソレータ
TRSC0107
<11057>
TRS-12

アイソレータ
TRSC0108
<11057>
TRS-12

アイソレータ
TRSC0109
<11057>
TRS-12

アイソレータ
TRSC0110
<11057>
TRS-12

アイソレータ
TRSC0111
<11057>
TRS-12

アイソレータ
TRSC0112
<11057>
TRS-12

アイソレータ
TRSC0113
<11057>
TRS-12

アイソレータ
TRSC0114
<11057>
TRS-12

第1出力 第2出力

4 5 6 7

33 34

37 38

41 42

73 74

77 78

81 82

86

SCSC01

CRSC01

CR接地ユニット

10K Ω 10 μ F

0V

G

E

(387E)

DC1~5V

(387F)

DC1~5V

(389-1E)

DC1~5V

(382A)

DC1~5V

(382B)


DC1~5V

(384B)

DC1~5V


(392A)

Revisions	Ⓐ 現地試験フォロー	01-06-15	折茂		Date	Name	Fuji Electric Co., Ltd.	Title	河頭管轄入出力制御装置 計装回路	Ref. Dwg. No.	W 4 2 6 2 9 7	391	(390x)	v x A	l m P
	Ⓐ C483071による改造	06-12-25	青木	Drawn	2000-06-08	河野									
	ⓧ テレメータ追加による取合変更	04-01-19	河野	Checked											
	ⓧ Q33532による取合変更	03-02-07	河野												

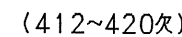


A	B	C	D	E	F	G	H
---	---	---	---	---	---	---	---

③ TMI追加
④ FICアダプタ追加
'05-11-07 大井成
'01-05-09 折茂

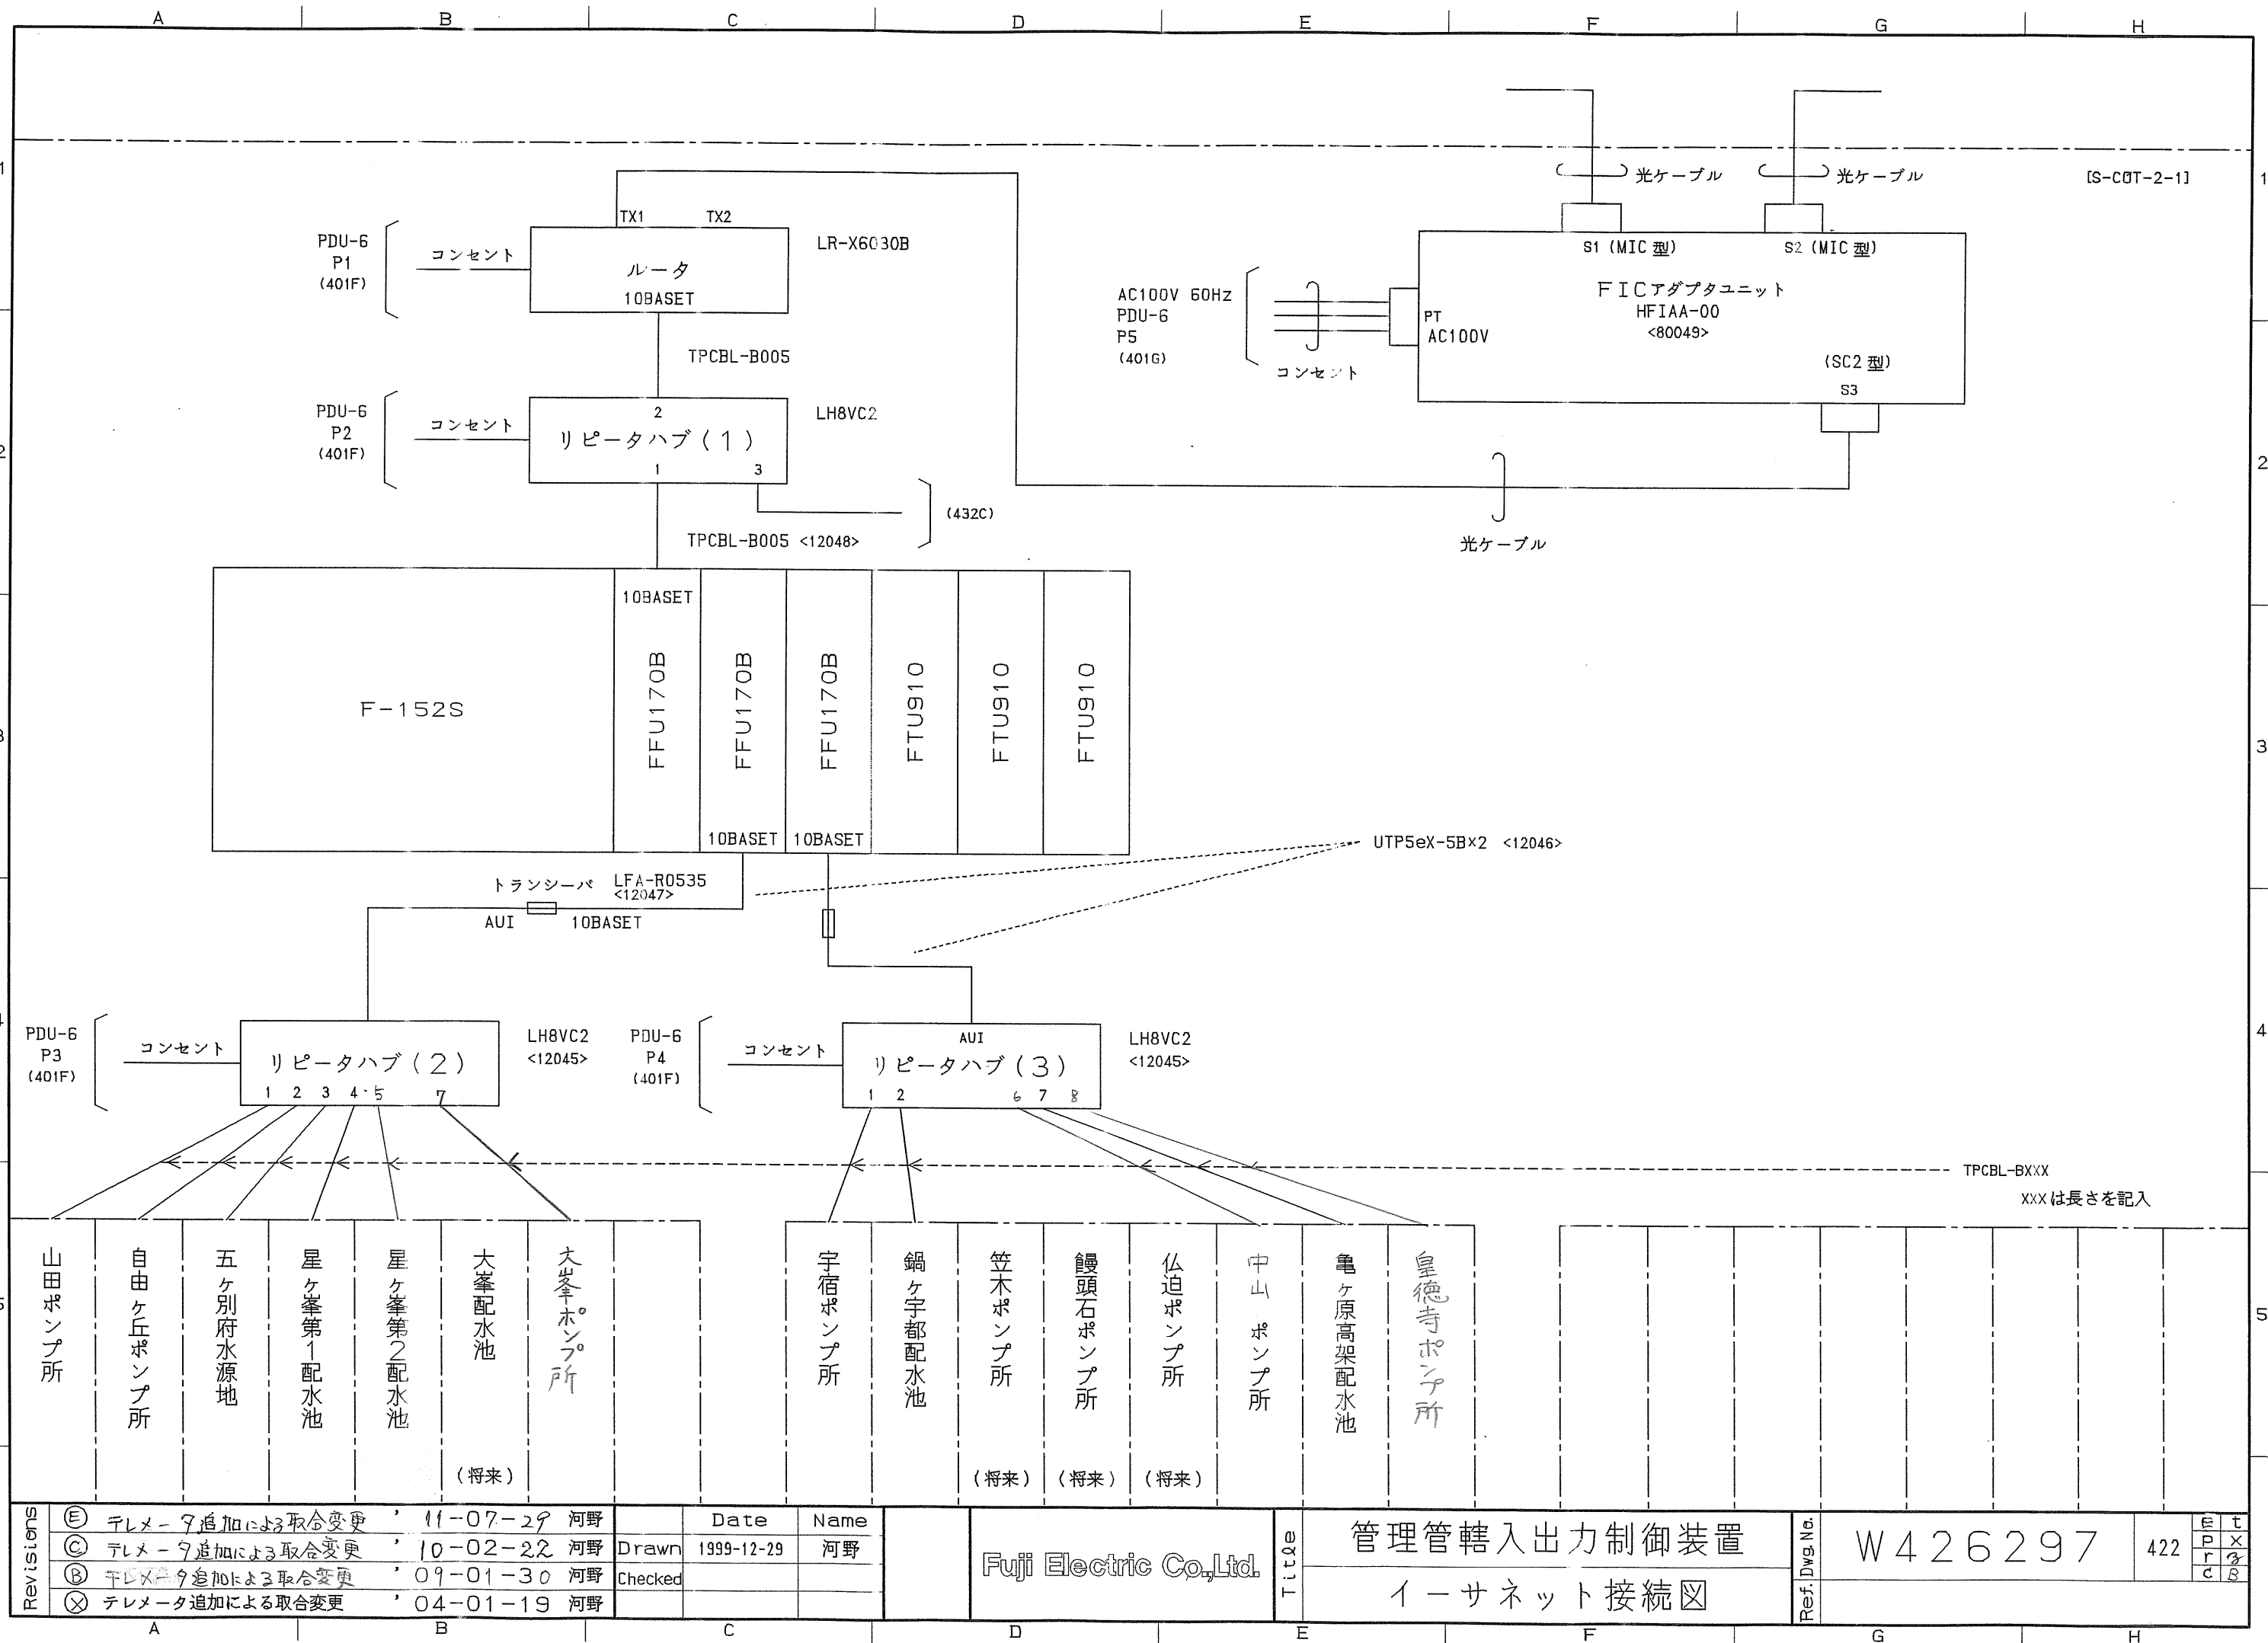

イーサネットモジュールFFU170B (F120Sシリーズ)

前面図

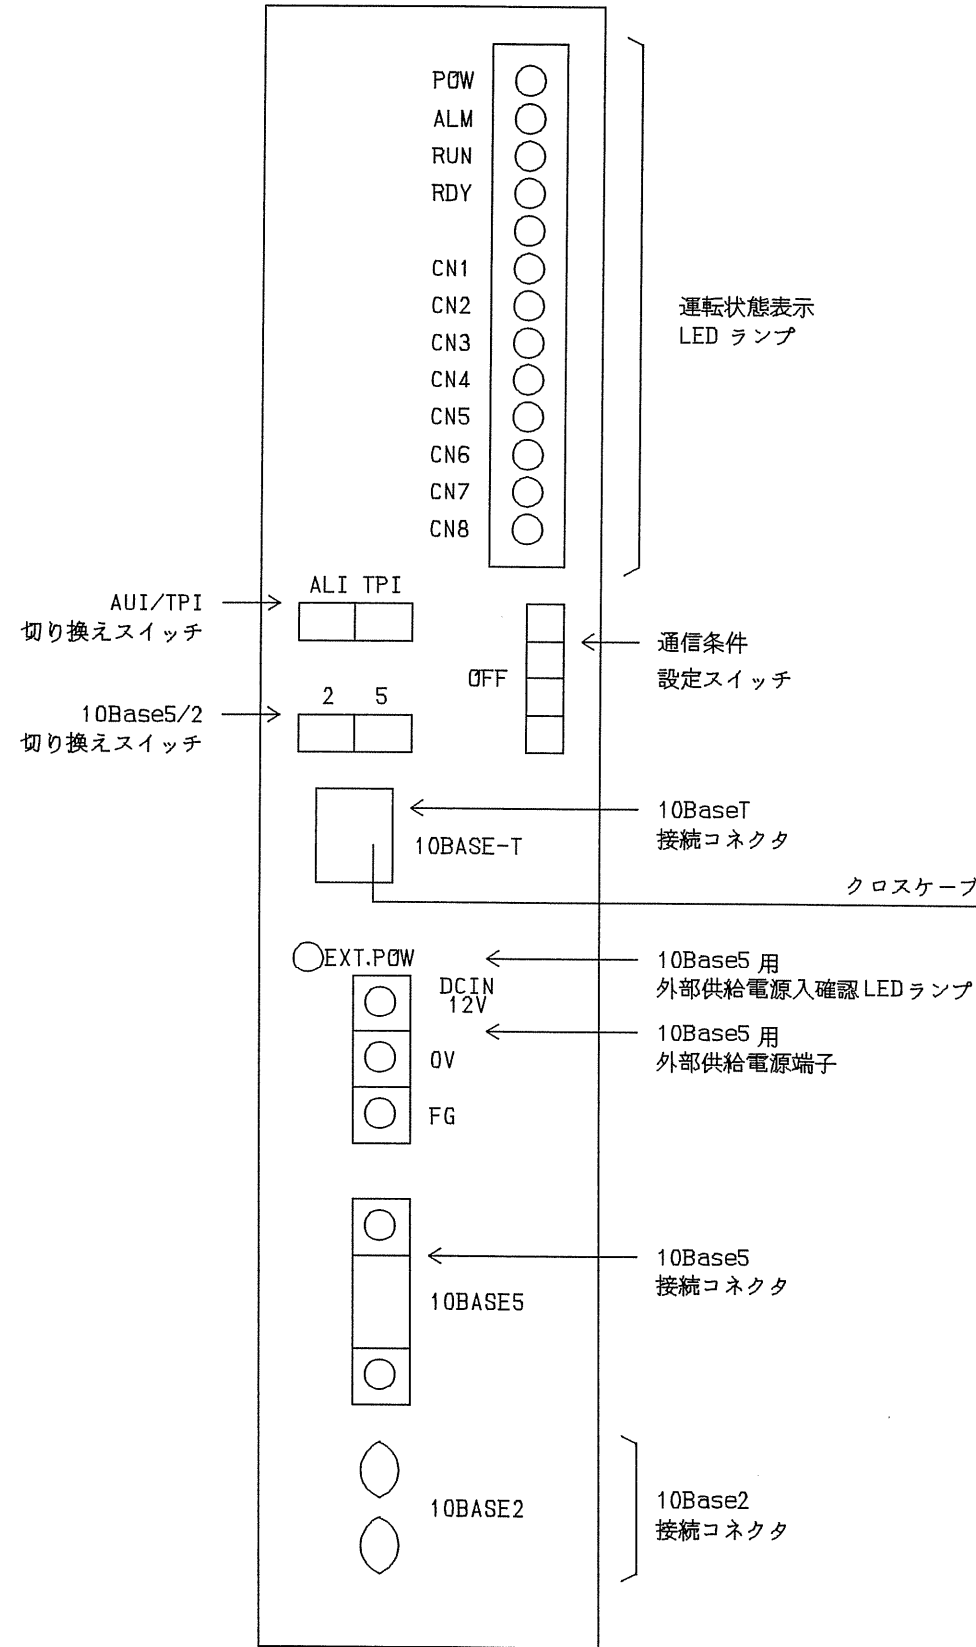

運転状態表示
LED ランプ

通信条件
設定スイッチ

10BaseT
接続コネクタ

クロスケーブル使用

10Base5 用
外部供給電源入確認 LED ランプ

10Base5 用
外部供給電源端子

10Base5
接続コネクタ

10Base2
接続コネクタ

※ 裏面にあるIPアドレス設定S・Wを8Cに設定

10BASET
ポート No.

リピータハブ (2)

10BASE5

<12047>
LFA-R0535
アライドテレシス

10BASET

[S-COT-2-1]

[L]

山田ポンプ所

FTE439910

(64BF)

自由ヶ丘ポンプ所

()

五ヶ別府水源池

()

星ヶ峯第1配水池

()

星ヶ峯第2配水池

()

大峯配水池

()

大峯ポンプ所

()

()

Revisions

②	TM追加	05-11-07	大城
①	イーサネット割付変更	00-11-09	折茂
①	IPアドレス変更	00-08-21	野崎
③	TM追加	10-02-22	河野

Date	Name
2000-04-24	森竹
Checked	

Fuji Electric Co., Ltd.

100011


管理管轄入出力制御装置
イーサネット接続図

Rev. No.


W426297


423


C
F
i
m
2

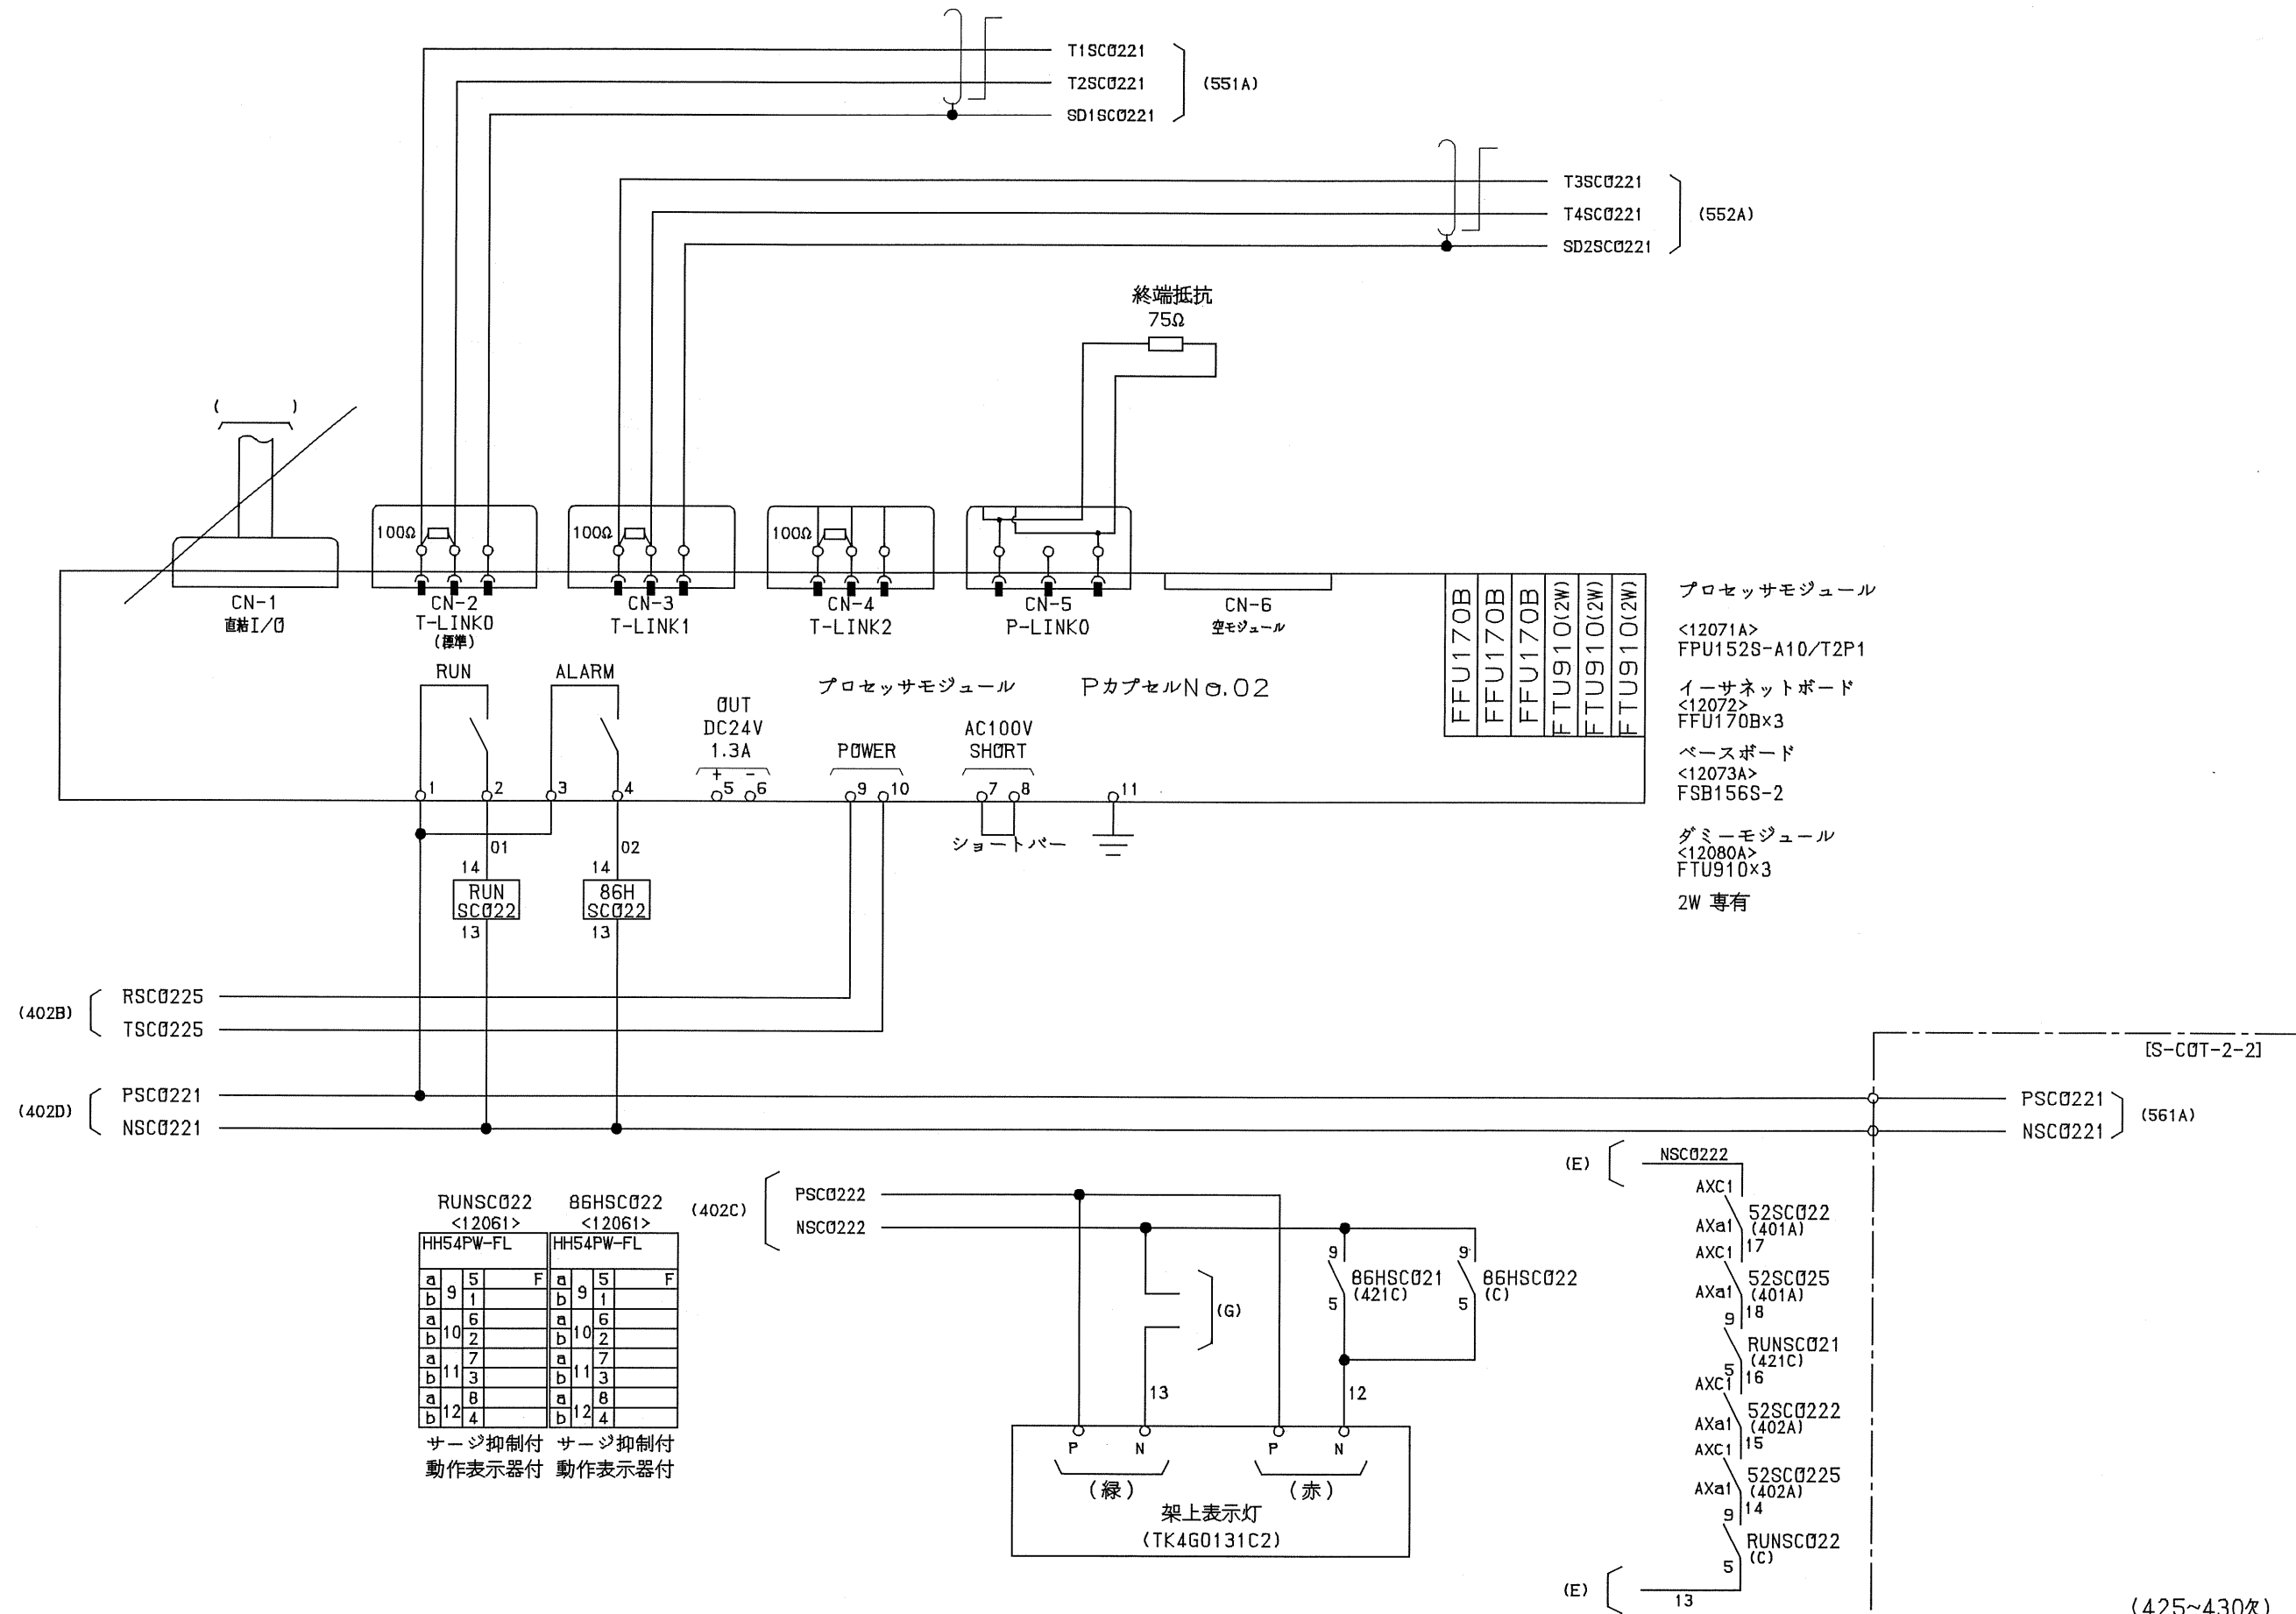


Revisions	Date	Name	Fuji Electric Co., Ltd.	管理管轄入出力制御装置	W426297	431	9
○							g
Ⓚ	00-09-20	折茂	Drawn				k
Ⓛ	00-08-21	野崎	Checked				
ⓐ	00-06-08	河野					
				F152S 接続図	MICREX-F120S 標準構成図		
					CIF120S		

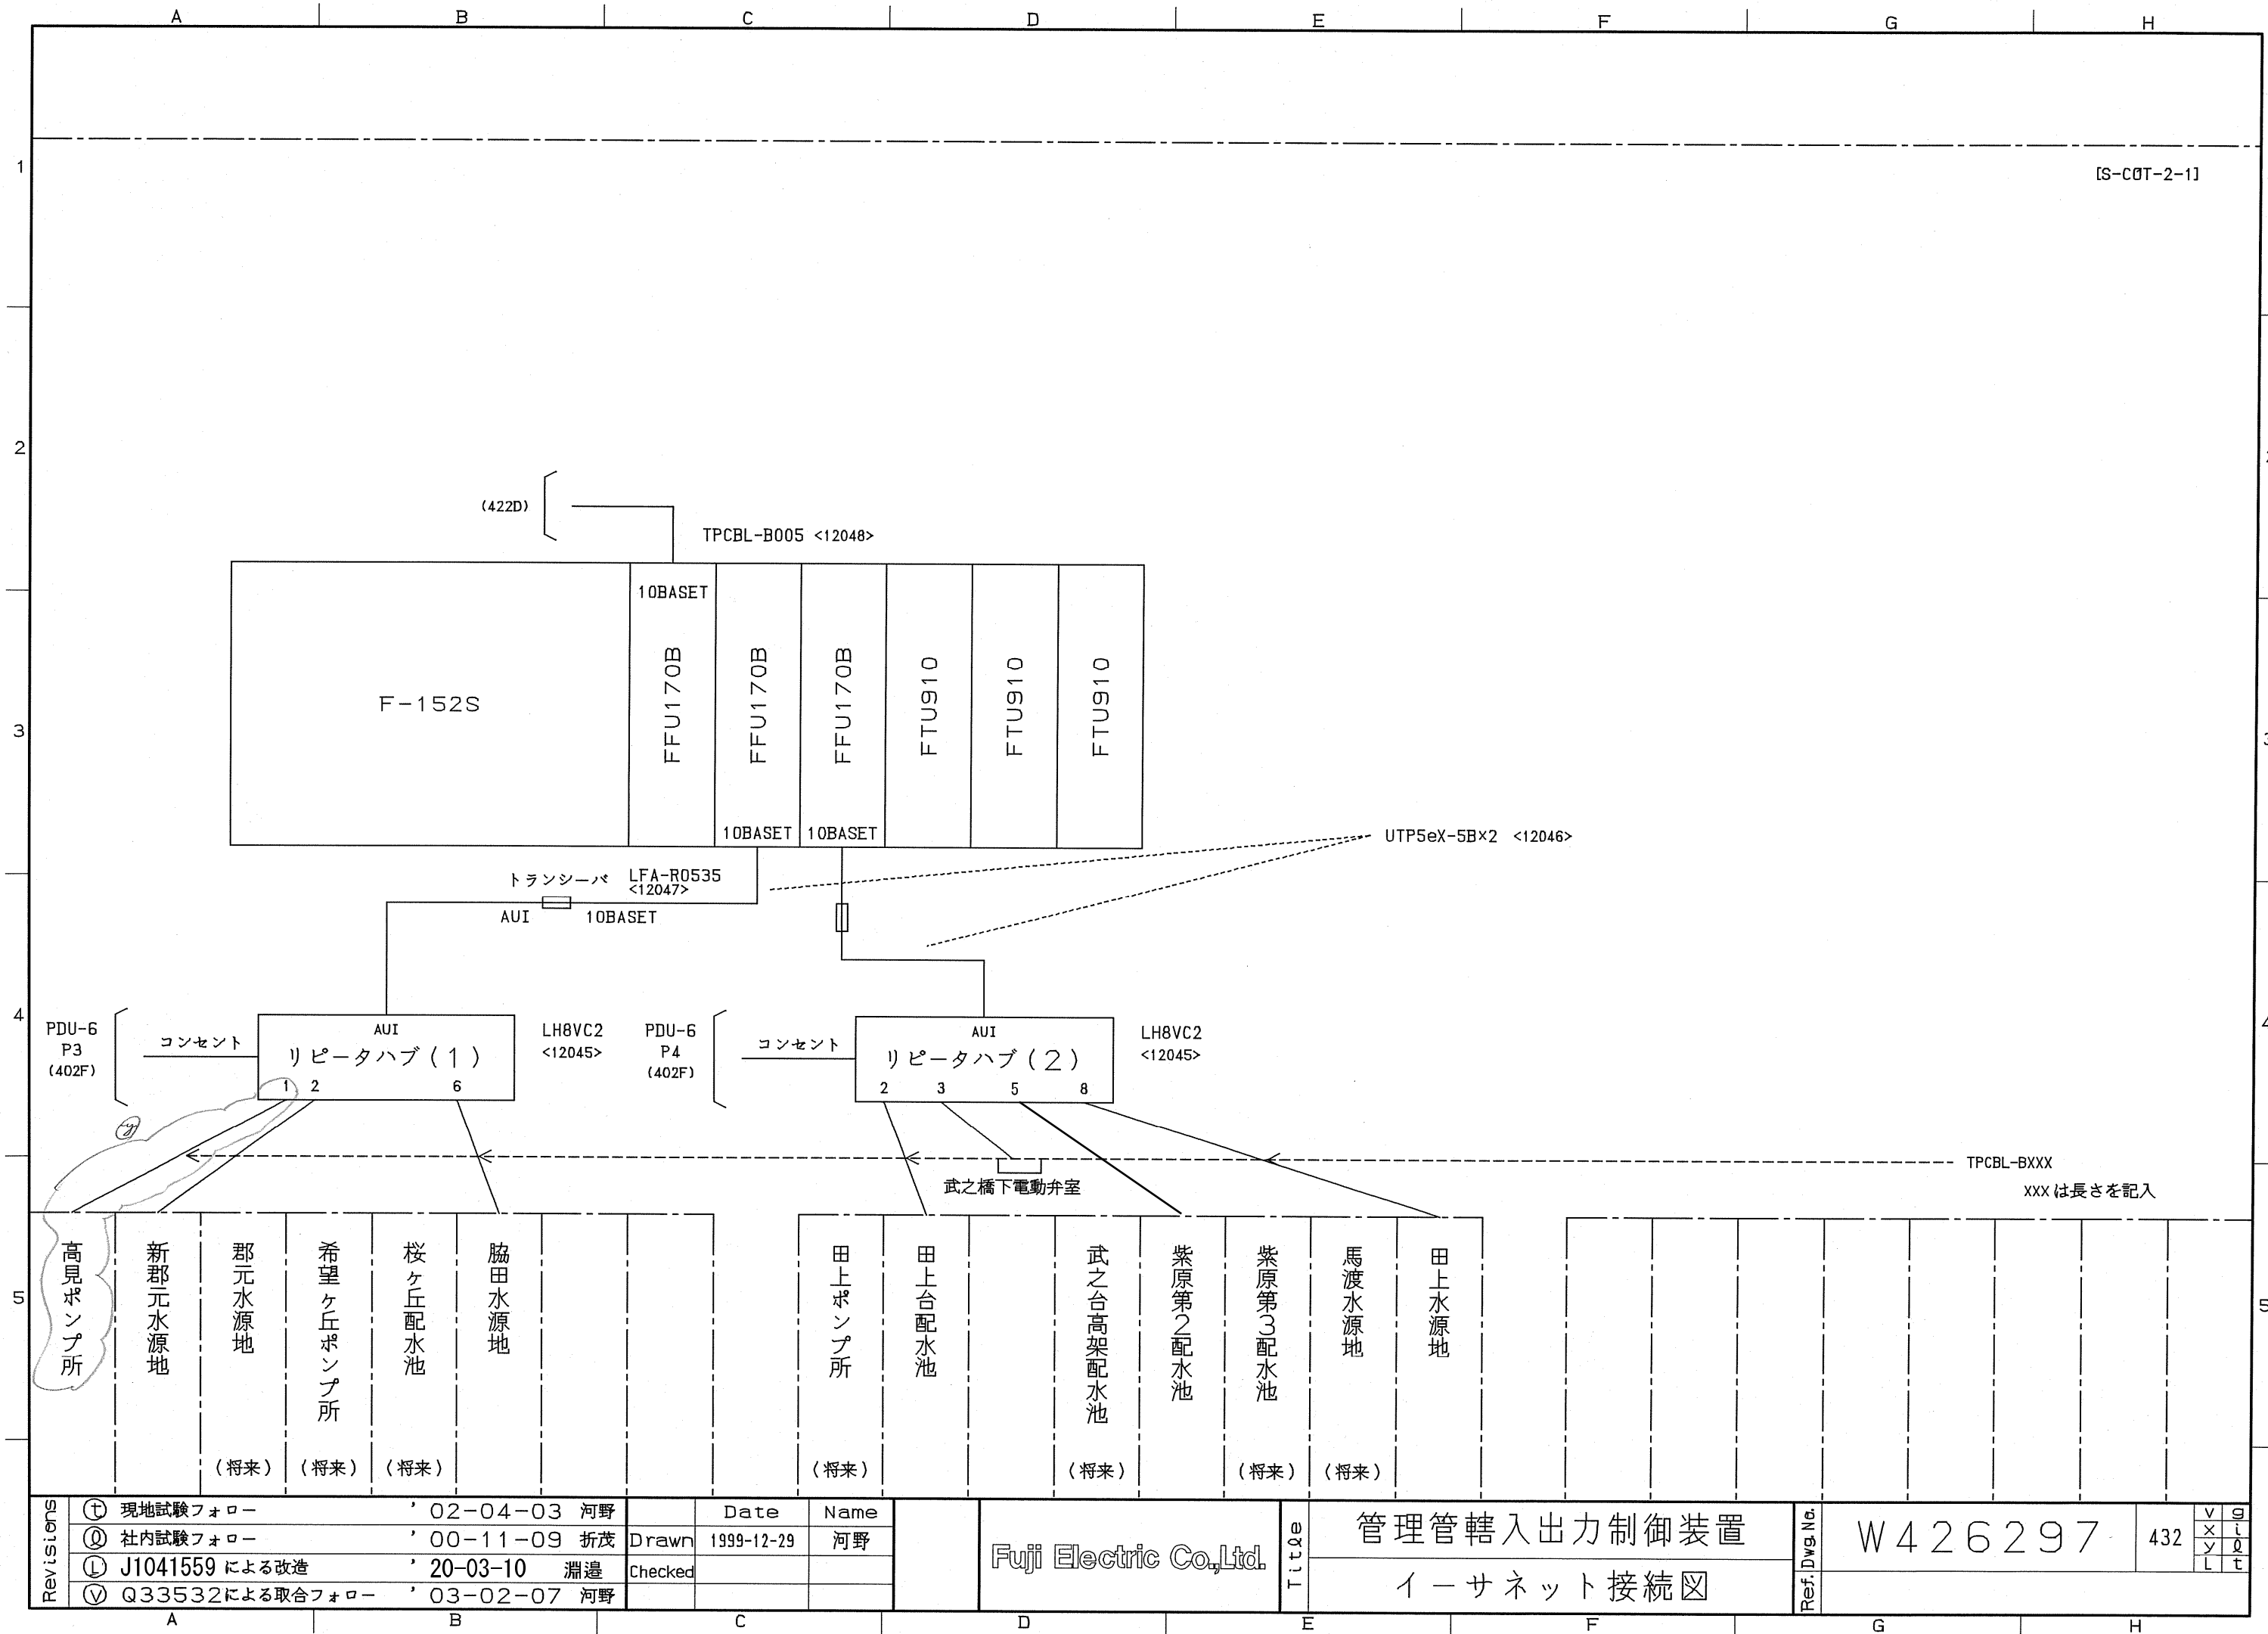

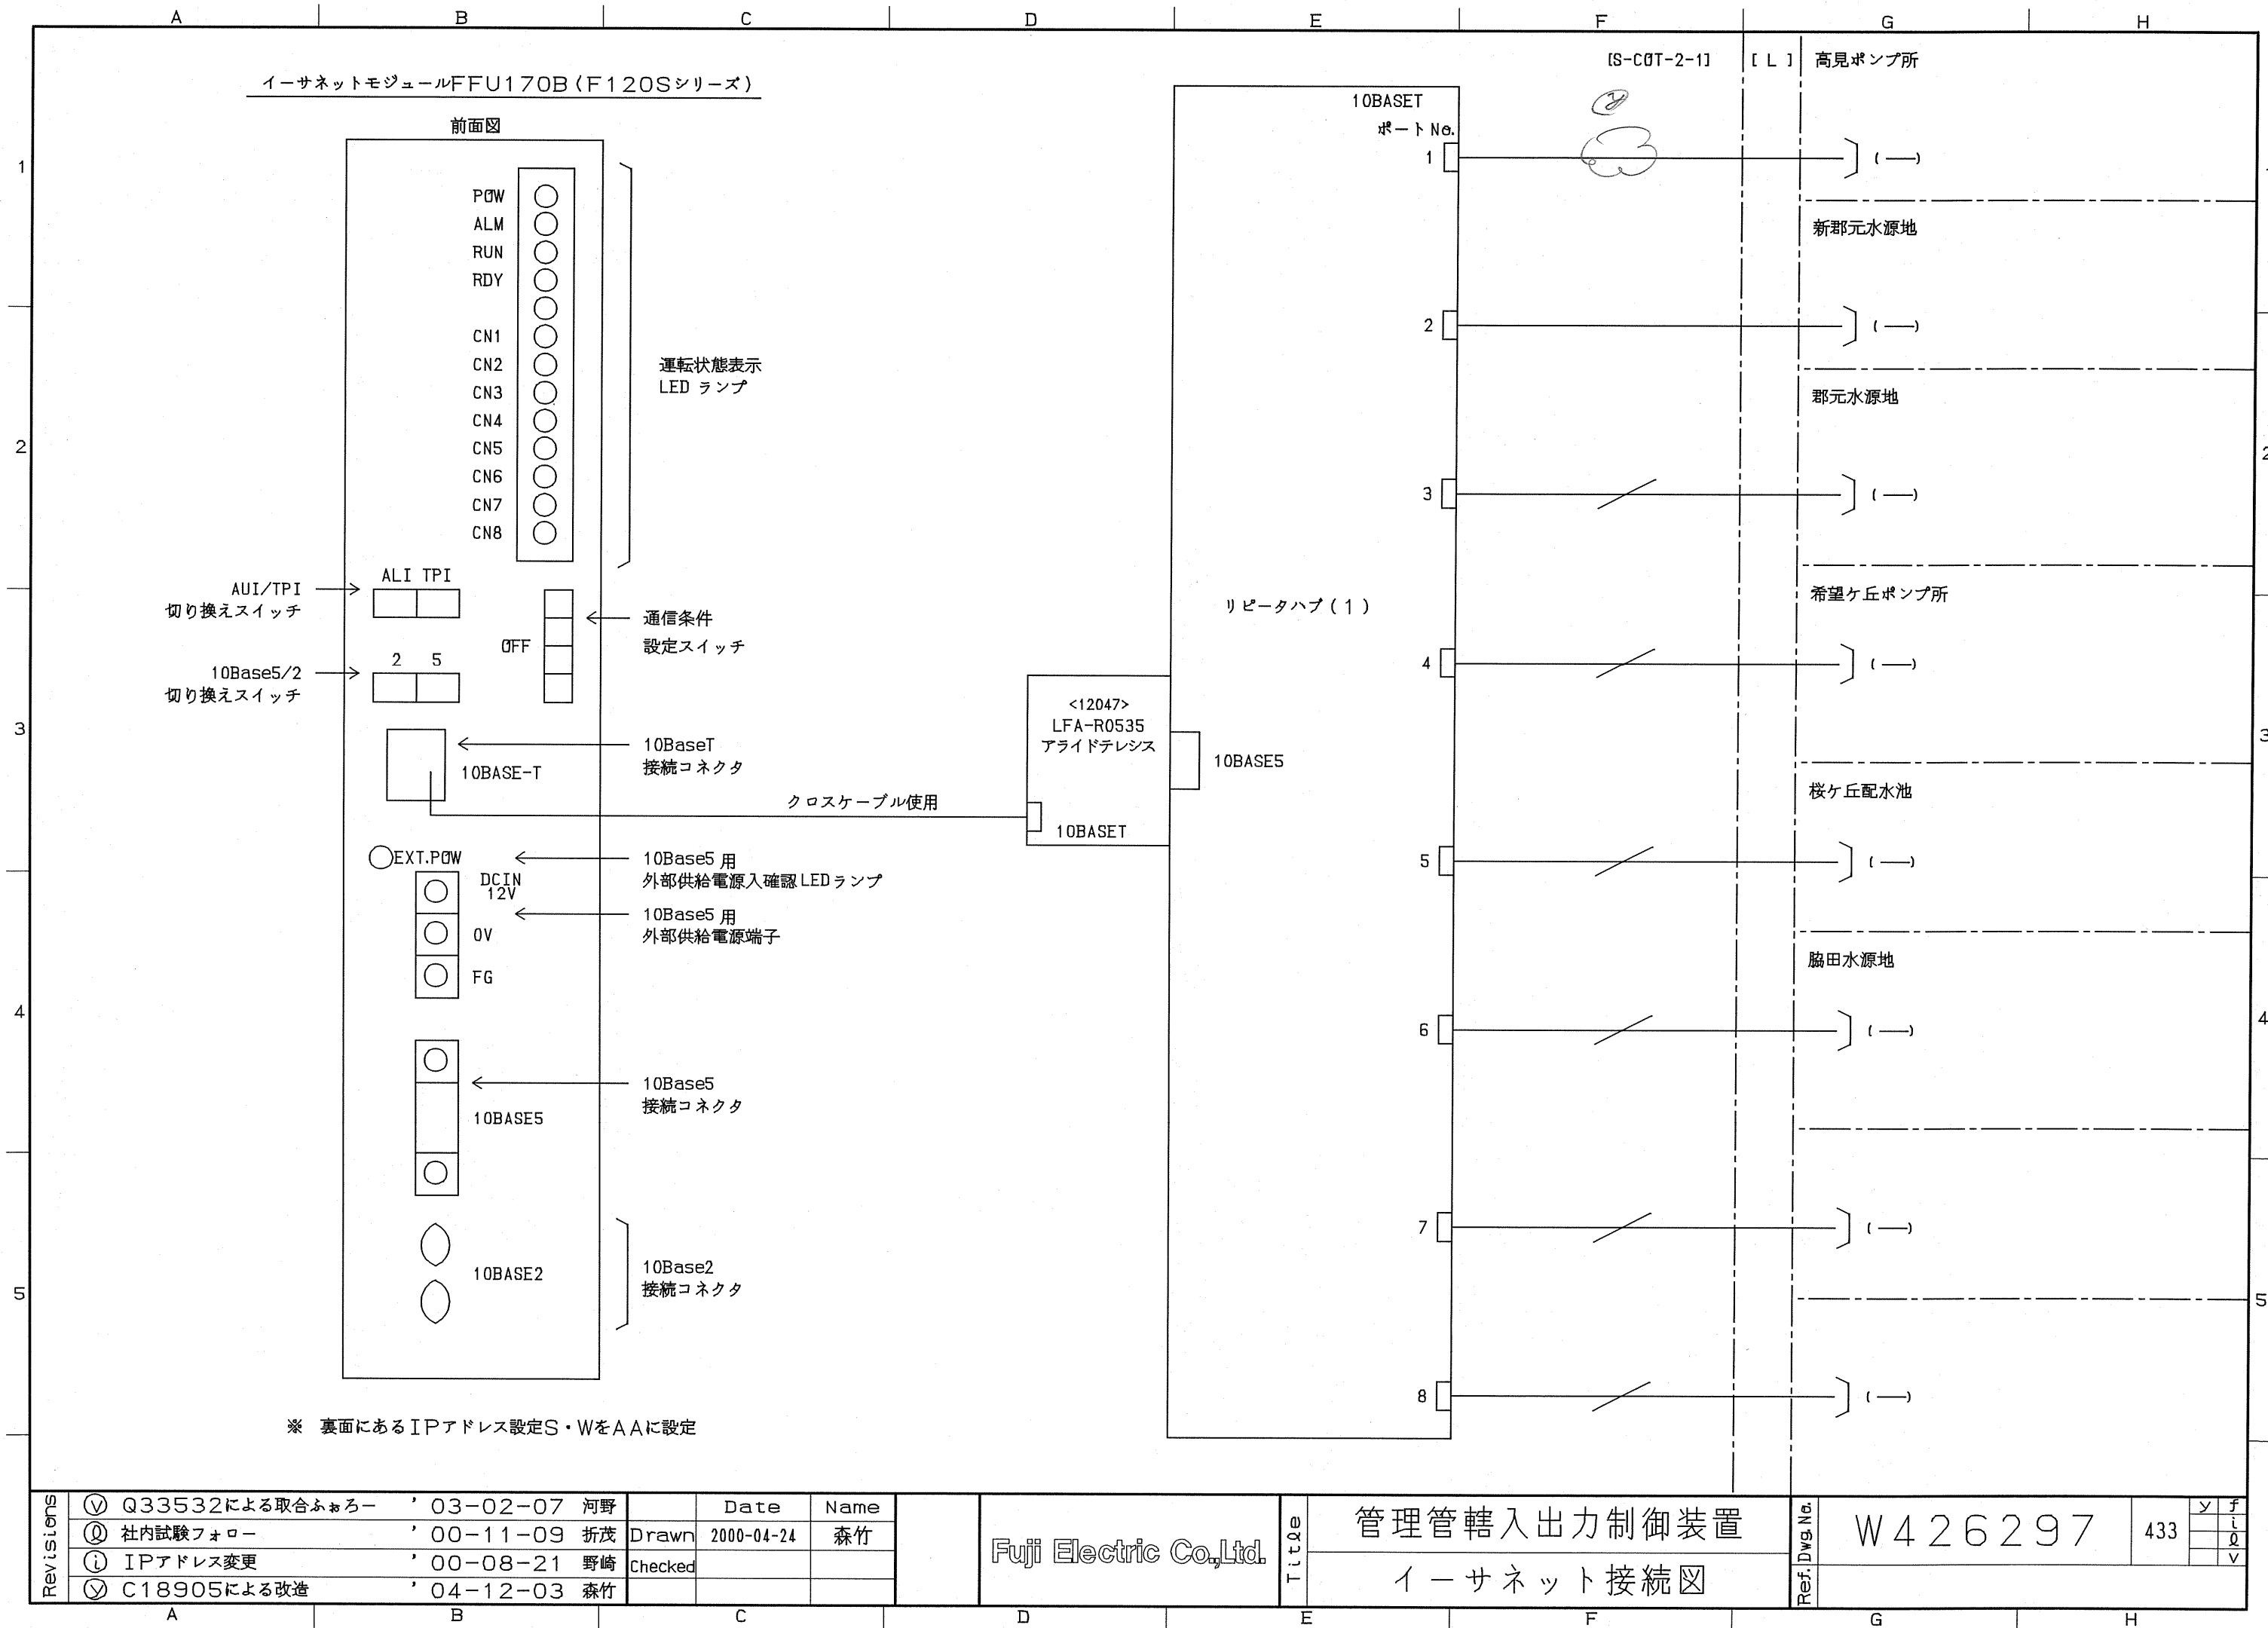


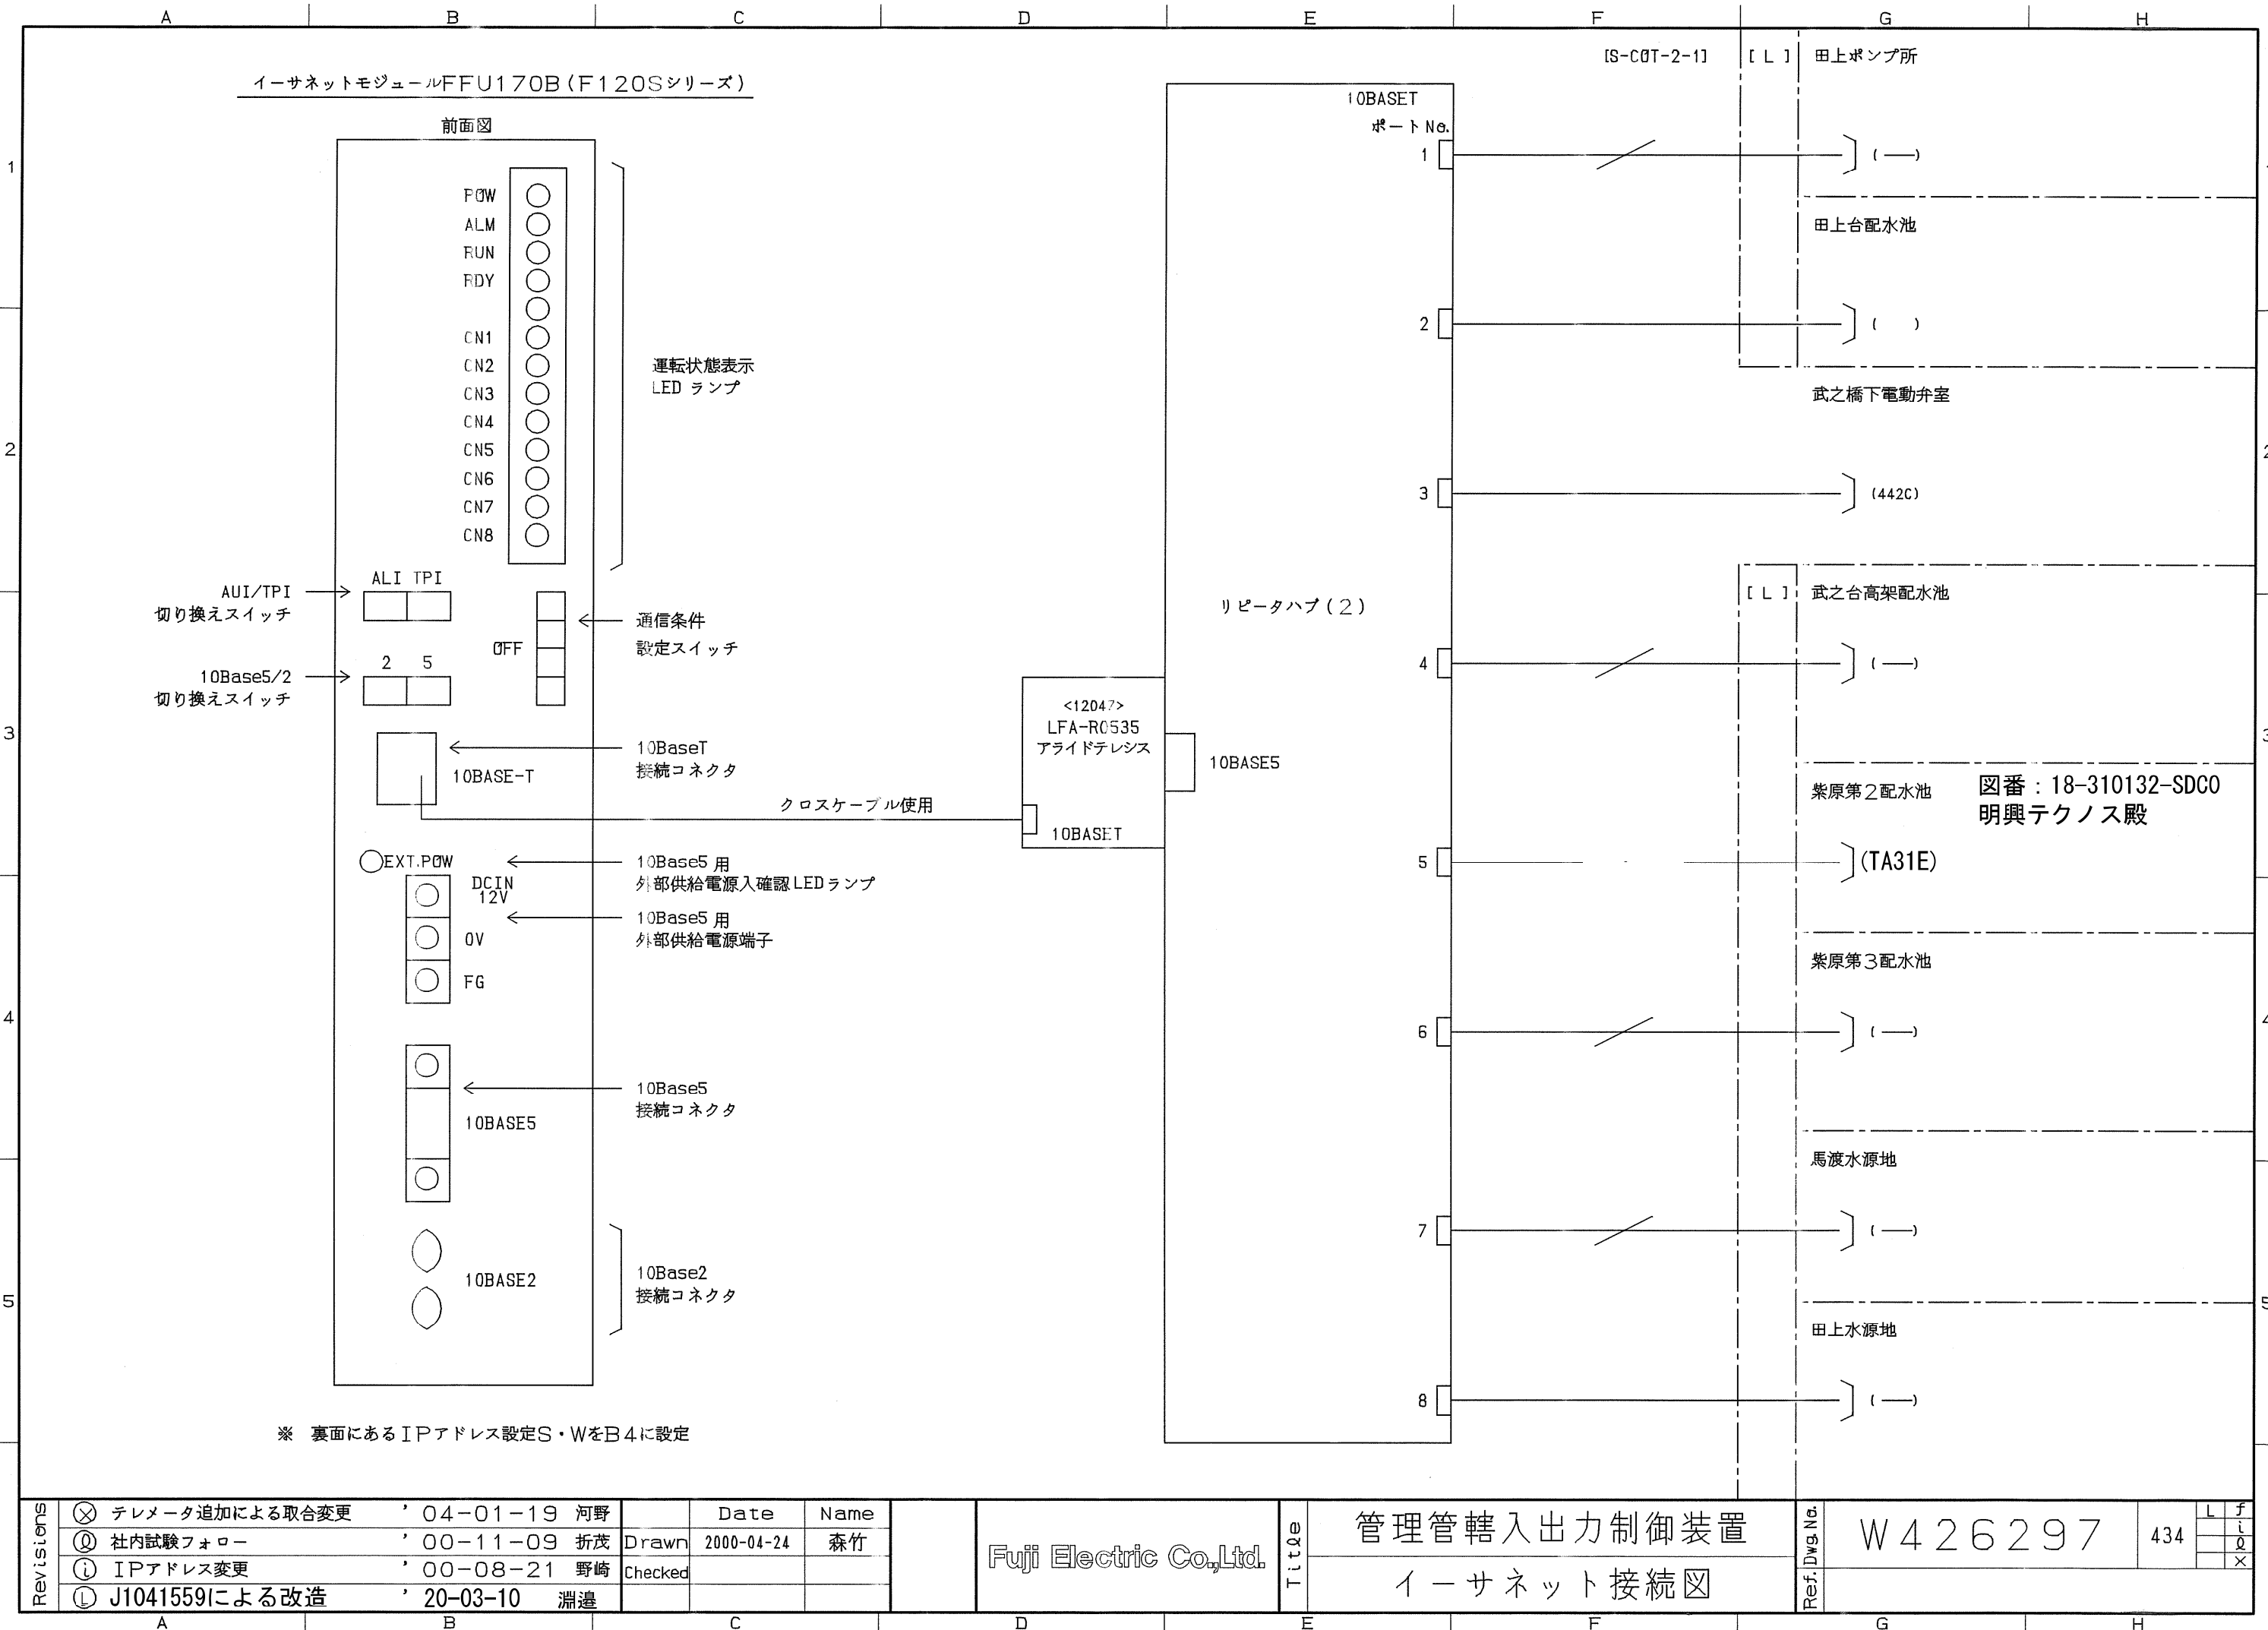



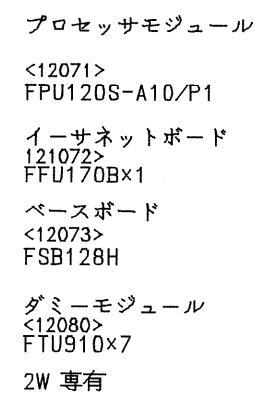





RUNSC023				86HSC023			
<12062>				<12062>			
HH54PW-CRL				HH54PW-CRL			
a	b	5		a	b	5	
	9	1			9	1	
a	b	6		a	b	6	
	10	2			10	2	
a	b	7		a	b	7	
	11	3			11	3	
a	b	8		a	b	8	
	12	4			12	4	

(435~440欠)

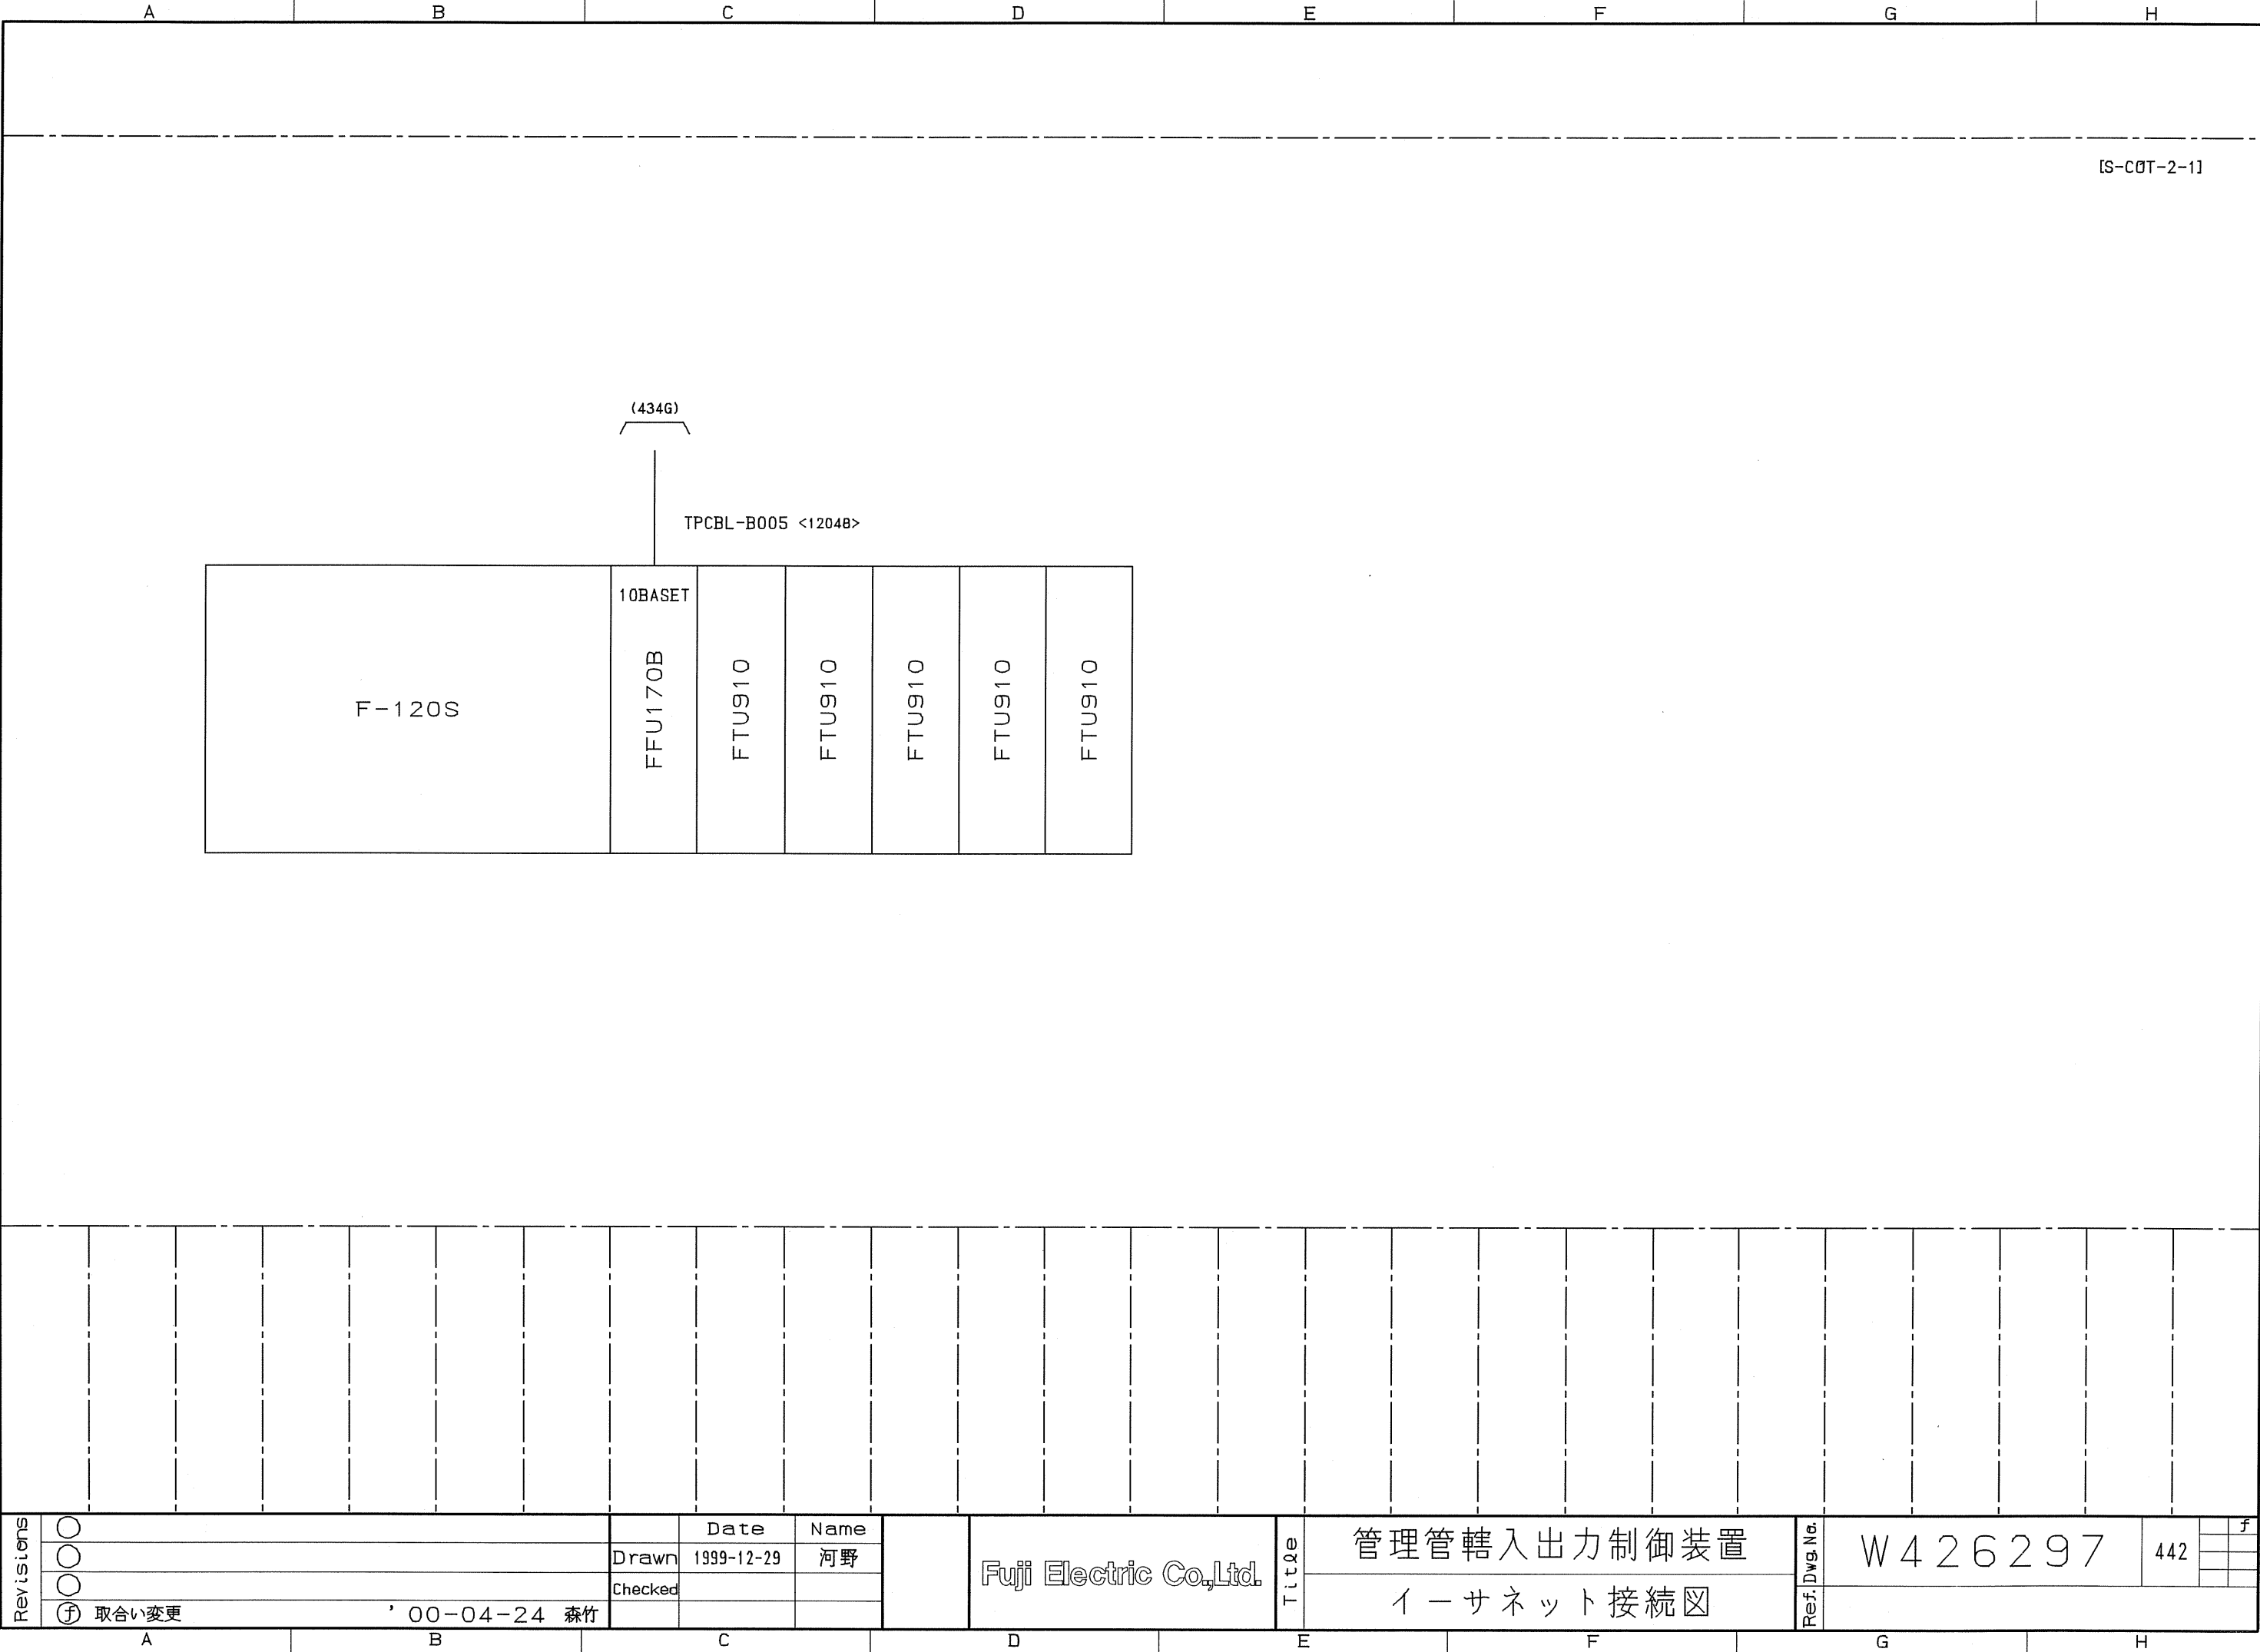

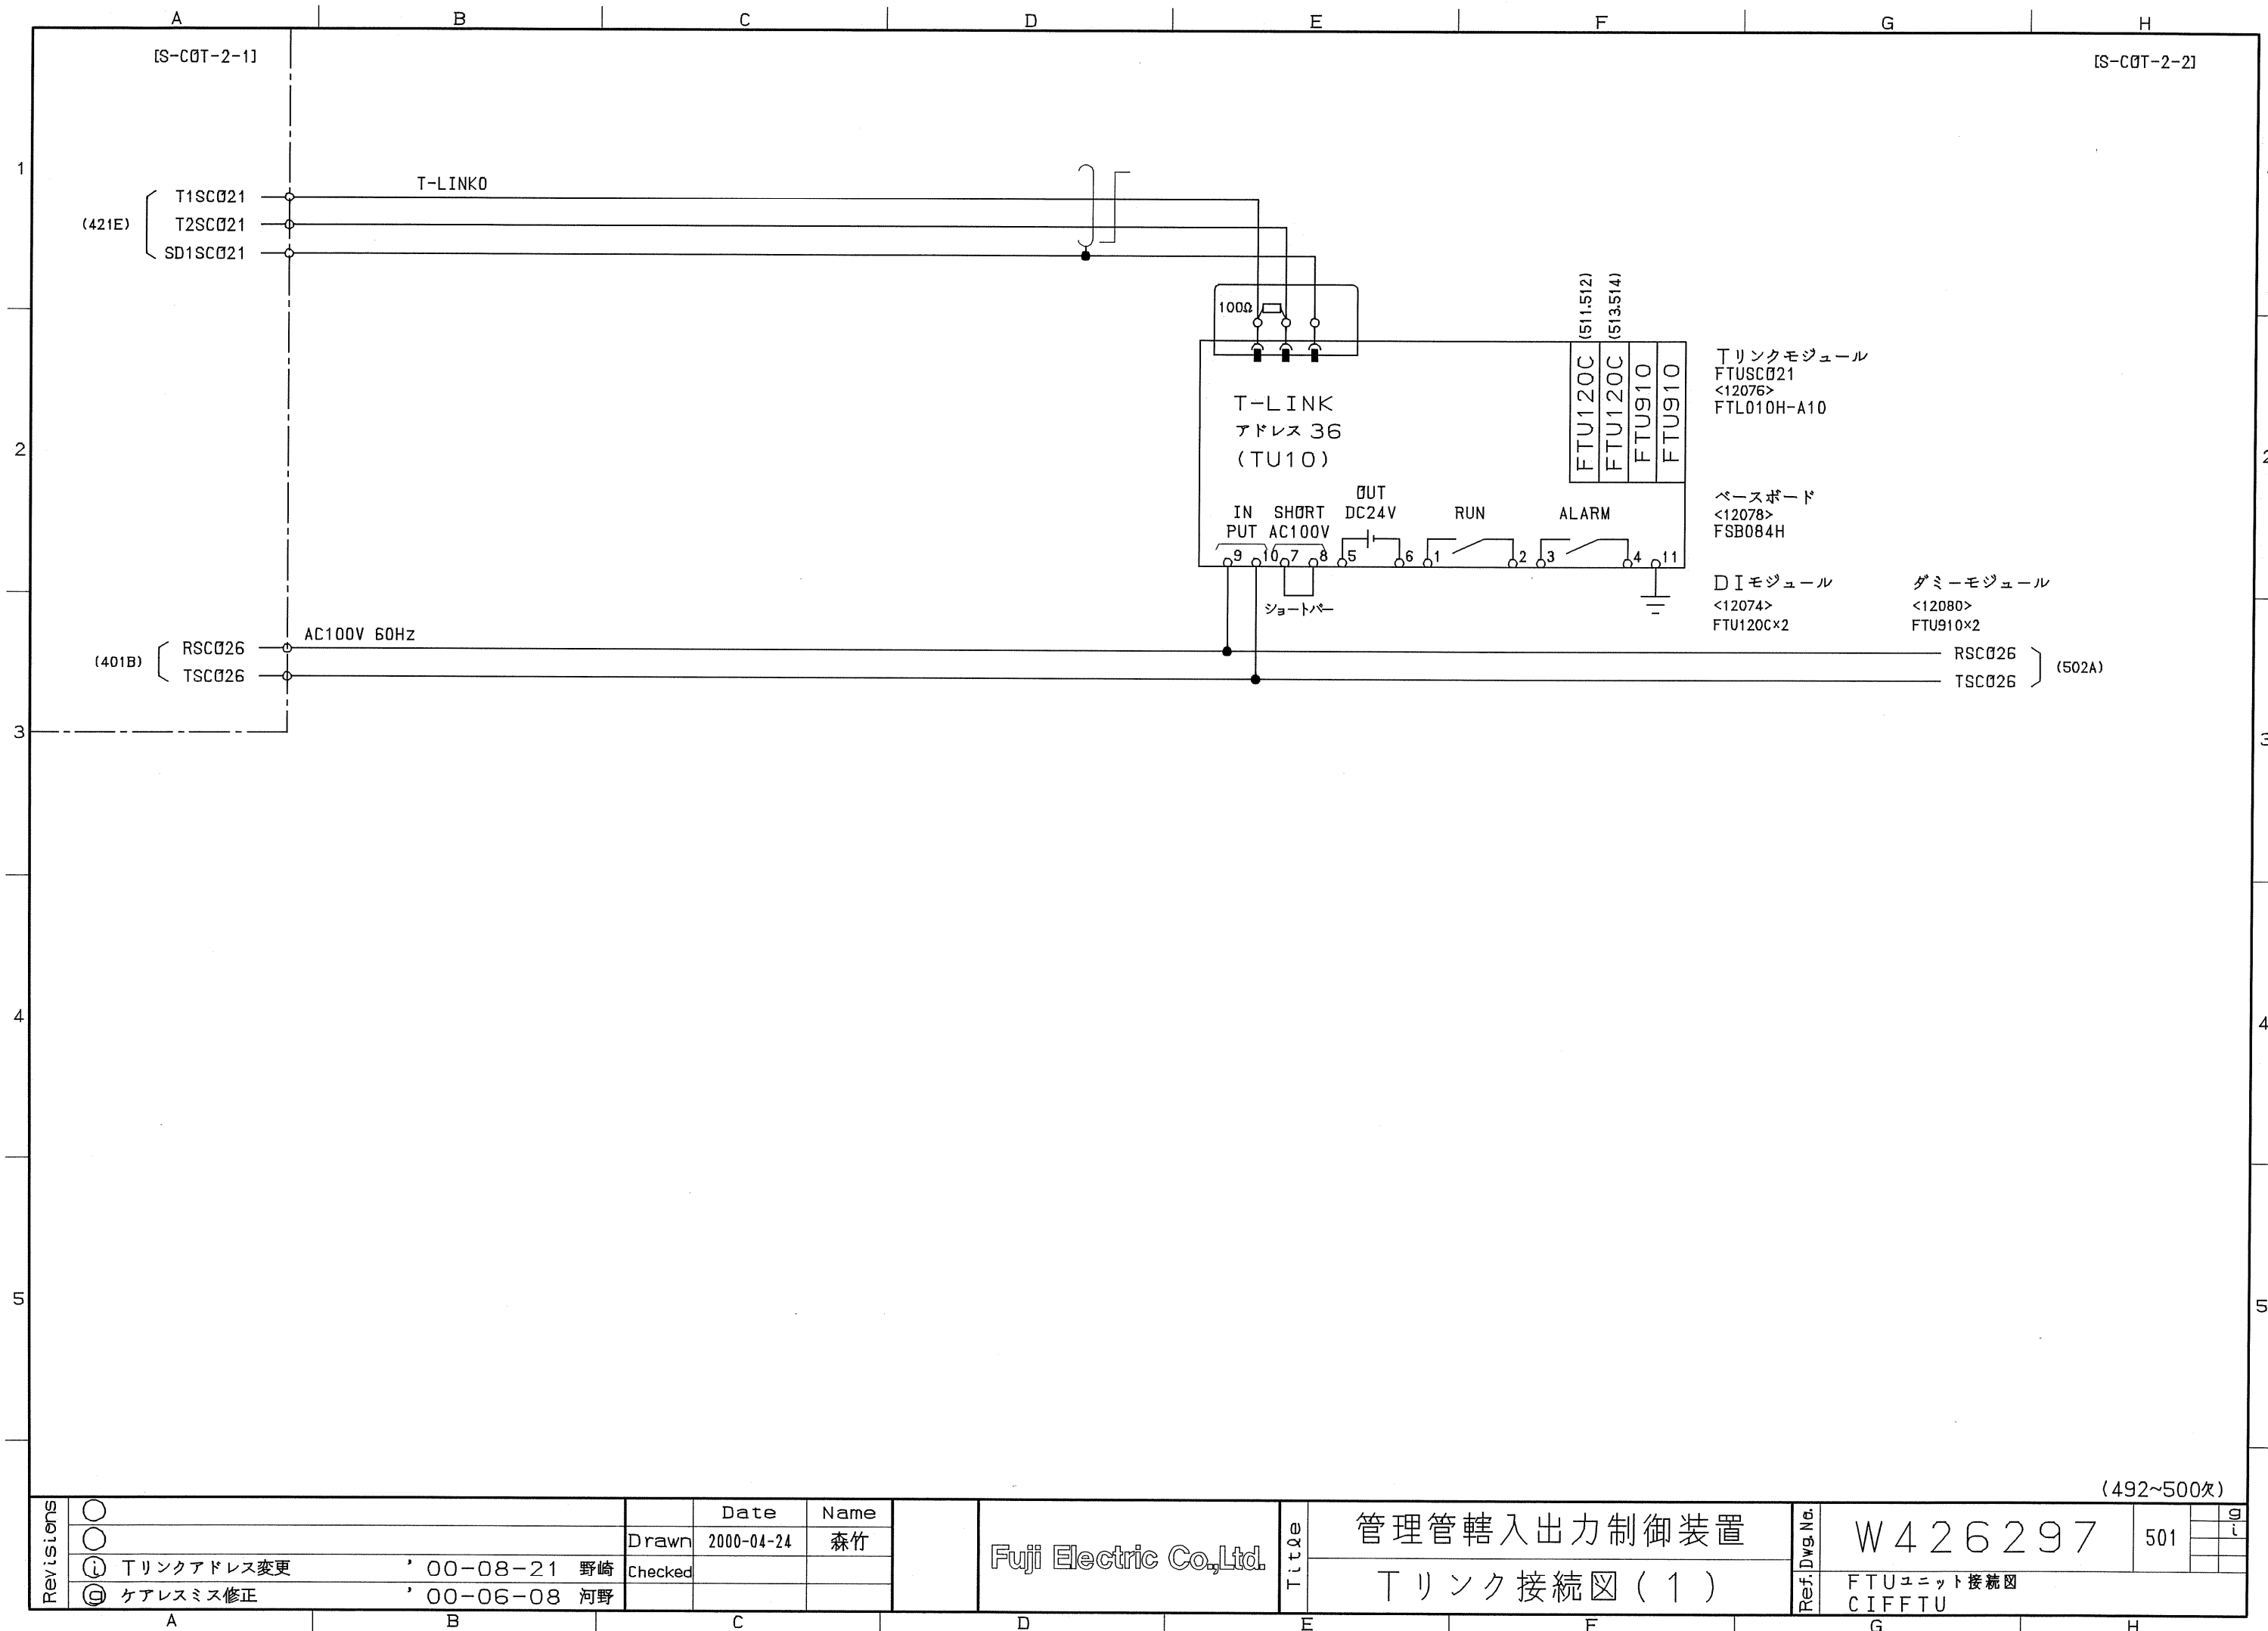

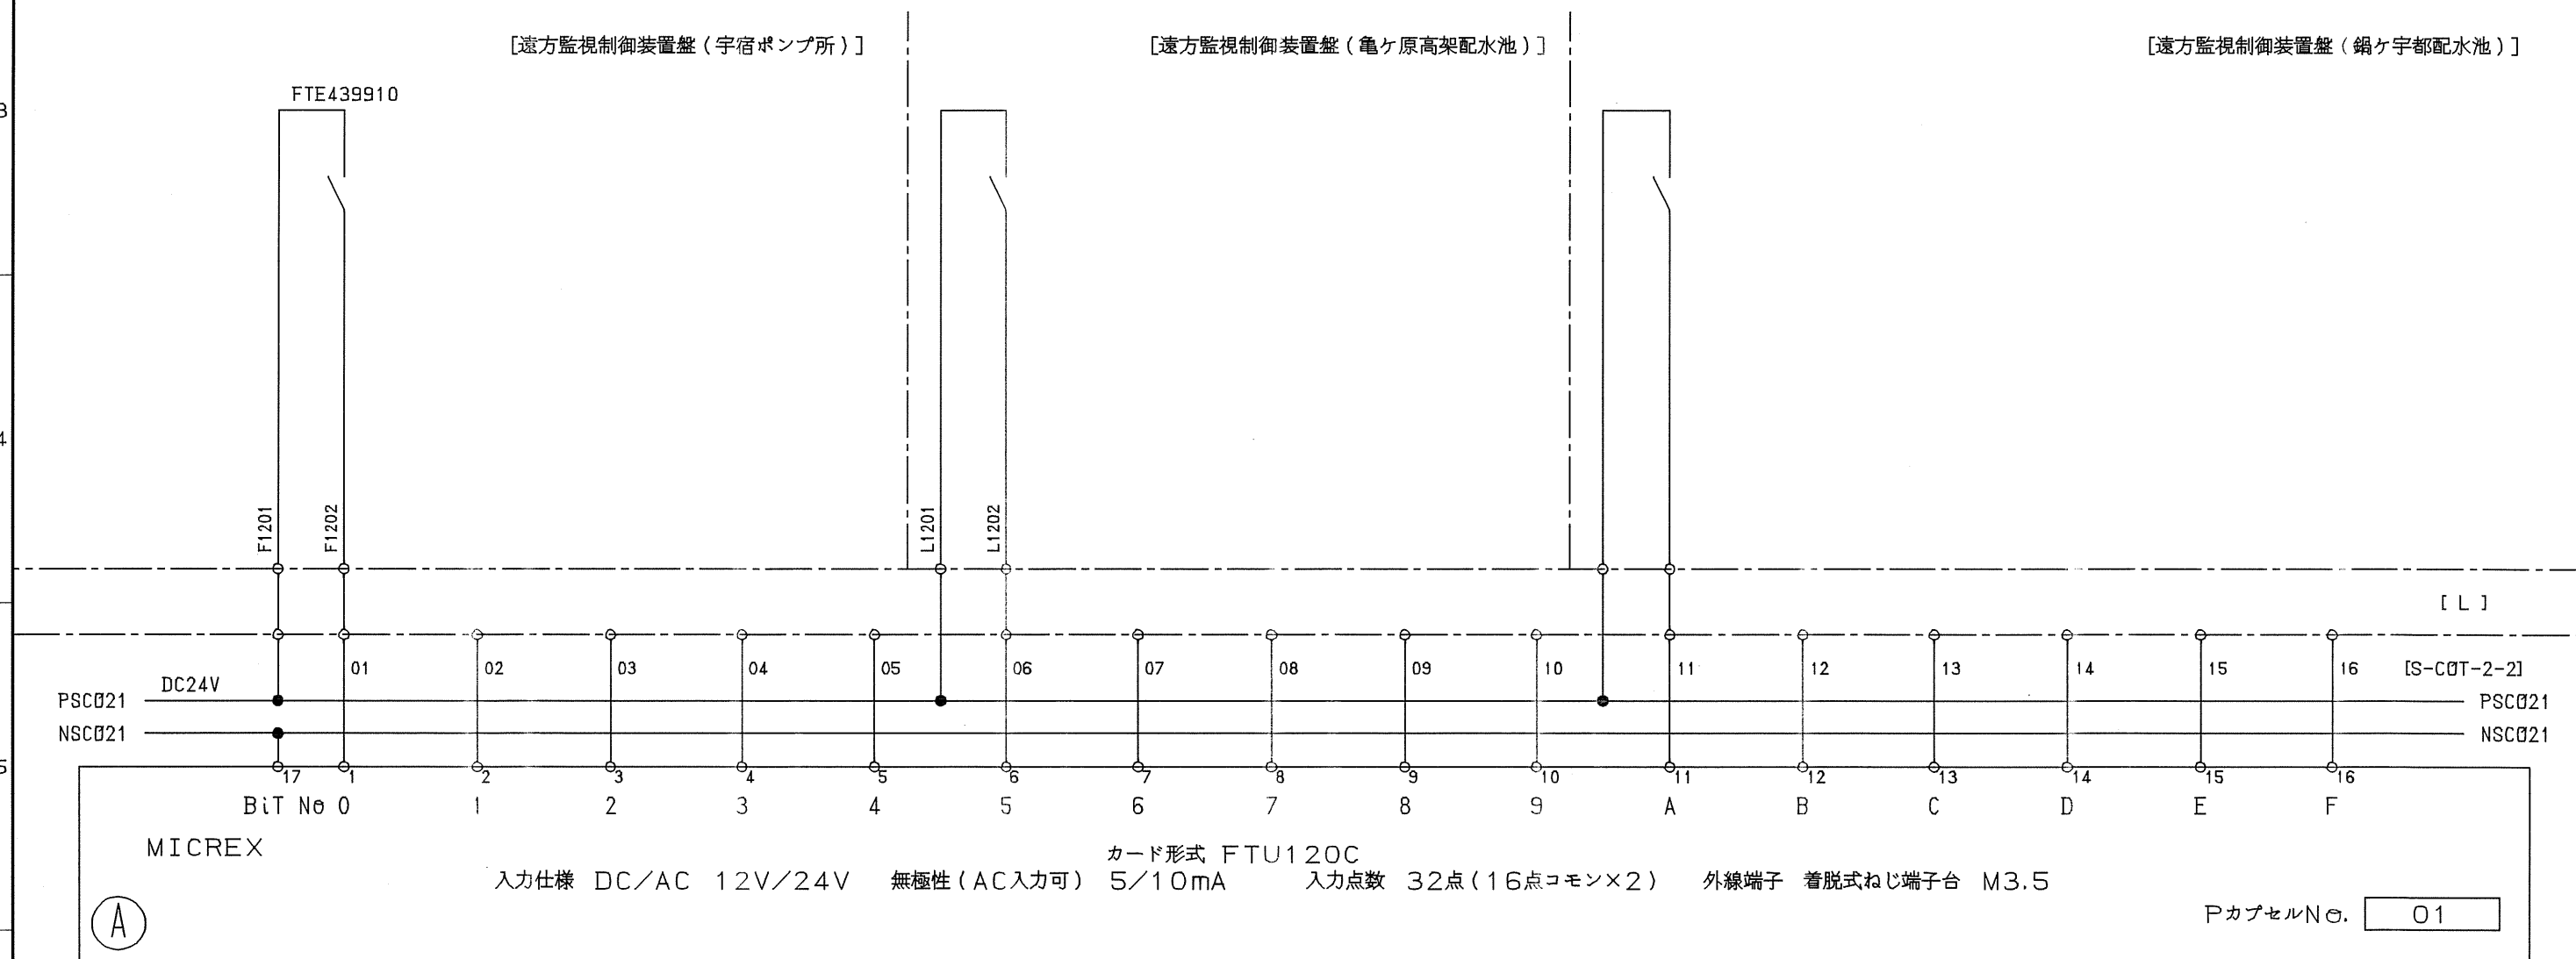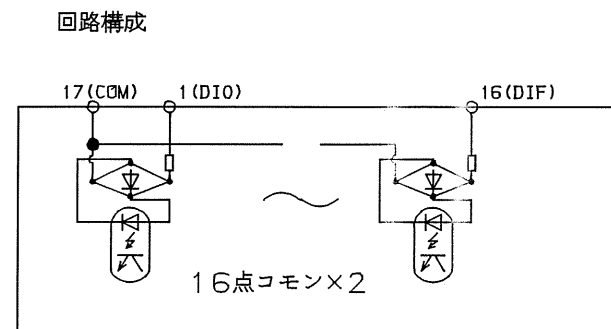


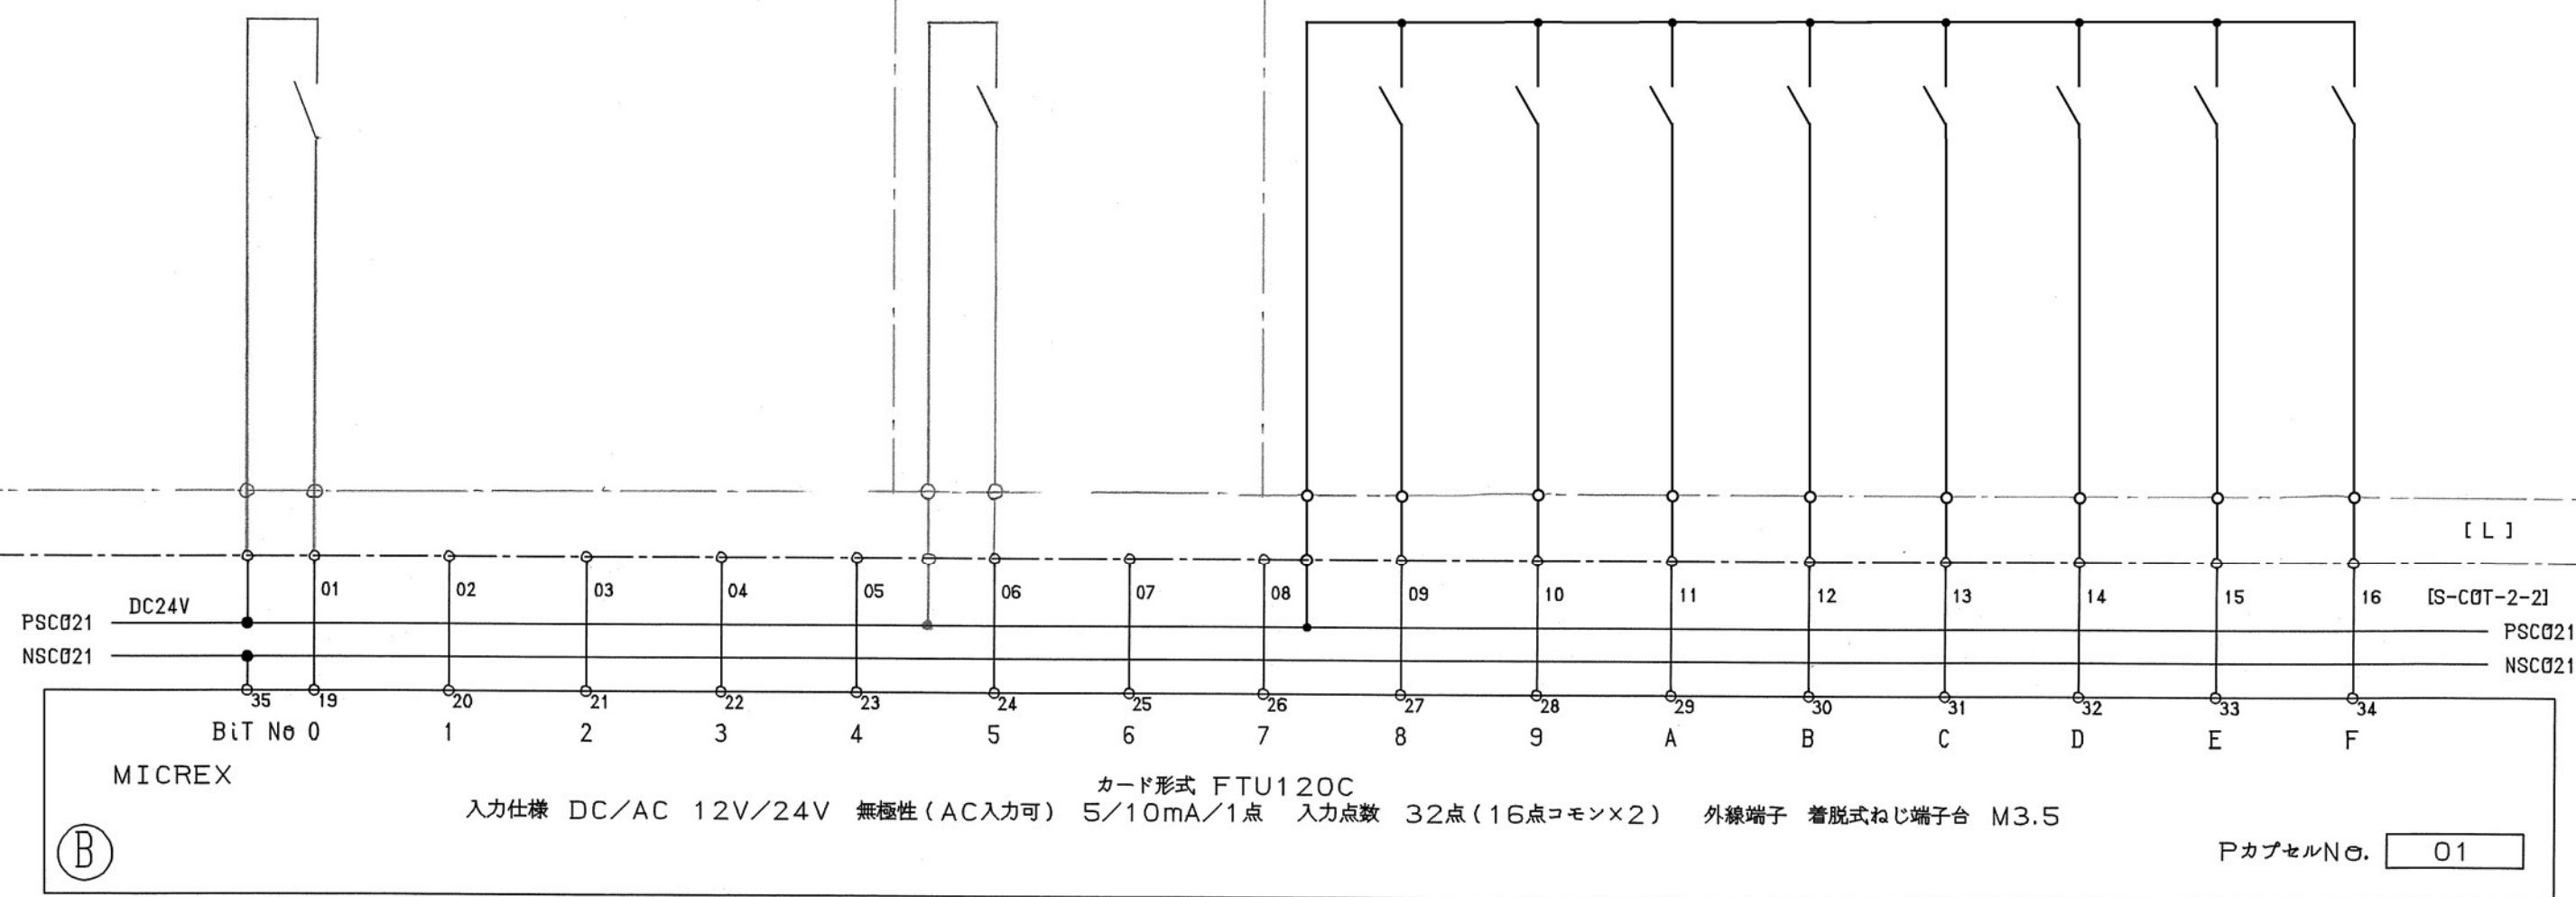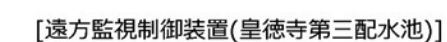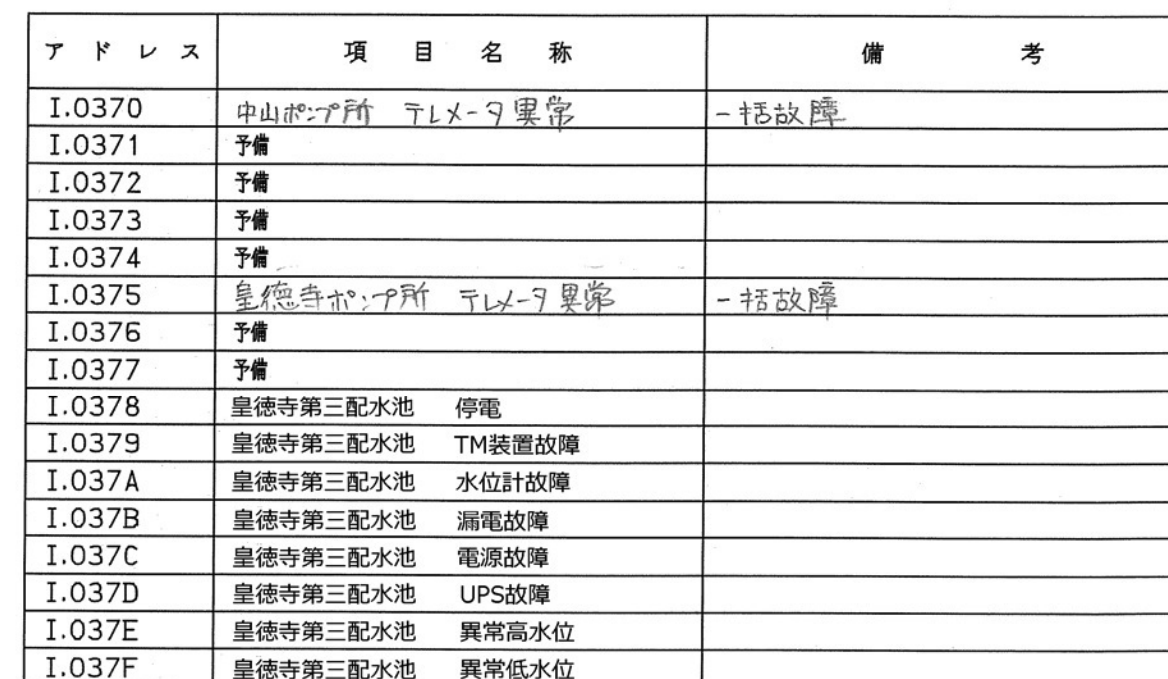

Revisions	(E) 信号追加	'11-07-29	河野		Date	Name	Fuji Electric Co.,Ltd.	Title	管理管轄入出力制御装置 インターフェース回路	Ref. Dwg. No.	W426297	512	JIS		
	(B) 信号追加	'09-01-30	河野	Drawn	2000-04-24	森竹									
	(C) アドレス変更	'00-08-21	野崎	Checked											
	(D) 取合追加	'20-01-31	八尋												
A		B		C		D		E		F		G		H	

A B C D E F G H

回路構成

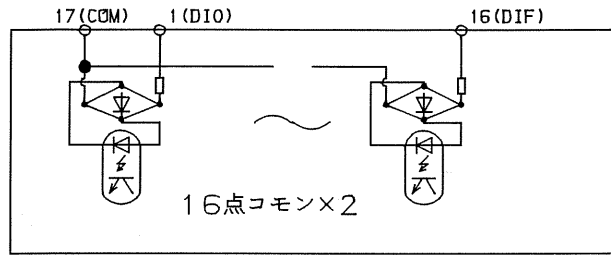

アドレス	項目名称	備考
I.0380	山田ポンプ所テレメータ異常	一括故障
I.0381	予備	
I.0382	予備	
I.0383	予備	
I.0384	予備	
I.0385	自由ヶ丘ポンプ所テレメータ異常	一括故障
I.0386	予備	
I.0387	予備	
I.0388	予備	
I.0389	予備	
I.038A	五ヶ別府水源地テレメータ異常	一括故障
I.038B	予備	
I.038C	予備	
I.038D	予備	
I.038E	予備	
I.038F	予備	

[遠方監視制御装置盤 (山田ポンプ所)]

[遠方監視制御装置盤 (自由ヶ丘ポンプ所)]

[遠方監視制御装置盤 (五ヶ別府水源地)]

FTE439910

80A17

80A18

COM3M13

SBM13

B4107

B4108

PSC021

NSC021

DC24V

01

02

03

04

05

06

07

08

09

10

11

12

13

14

15

16

[L]

[S-COT-2-2]

PSC021

NSC021

Bit No 0

1

2

3

4

5

6

7

8

9

A

B

C

D

E

F

MICREX

入力仕様 DC/AC 12V/24V 無極性 (AC入力可) 5/10mA 入力点数 32点 (16点コモン×2) 外線端子 着脱式ねじ端子台 M3.5

PカプセルNo. 01

Revisions	①	現地試験フォロー	'	01-06-15	折茂		Date	Name	Fuji Electric Co.,Ltd.	Title	管理管轄入出力制御装置 インターフェース回路	Ref. Dwg. No.	W426297	513	M/F DI (ユニット・端子) 1/2 CIFDICUA	f i k P
	②	取合い追記	'	00-09-20	折茂	Drawn	2000-04-24	森竹								
	③	信号削除	'	00-08-21	野崎	Checked										
	④	本頁追加	'	00-04-24	森竹											

A

B

C


D

E



F

G


H

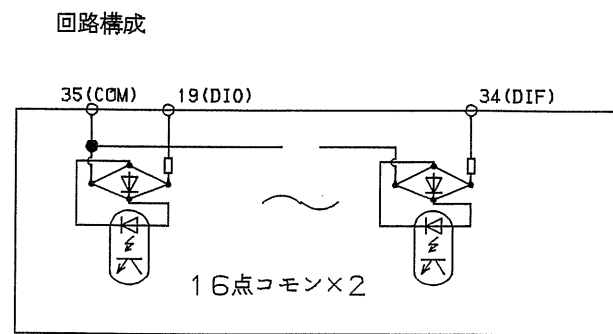


ア ド レ ス	項 目 名 称	備 考
I.0390	星ヶ峯第1配水池テレメータ異常	一括故障
I.0391	予備	
I.0392	予備	
I.0393	予備	
I.0394	予備	
I.0395	大峯ポンプ所テレメータ異常	一括故障
I.0396	予備	
I.0397	予備	
I.0398	予備	
I.0399	予備	
I.039A	星ヶ峯第2配水池テレメータ異常	一括故障
I.039B	予備	
I.039C	予備	
I.039D	予備	
I.039E	予備	
I.039F	予備	

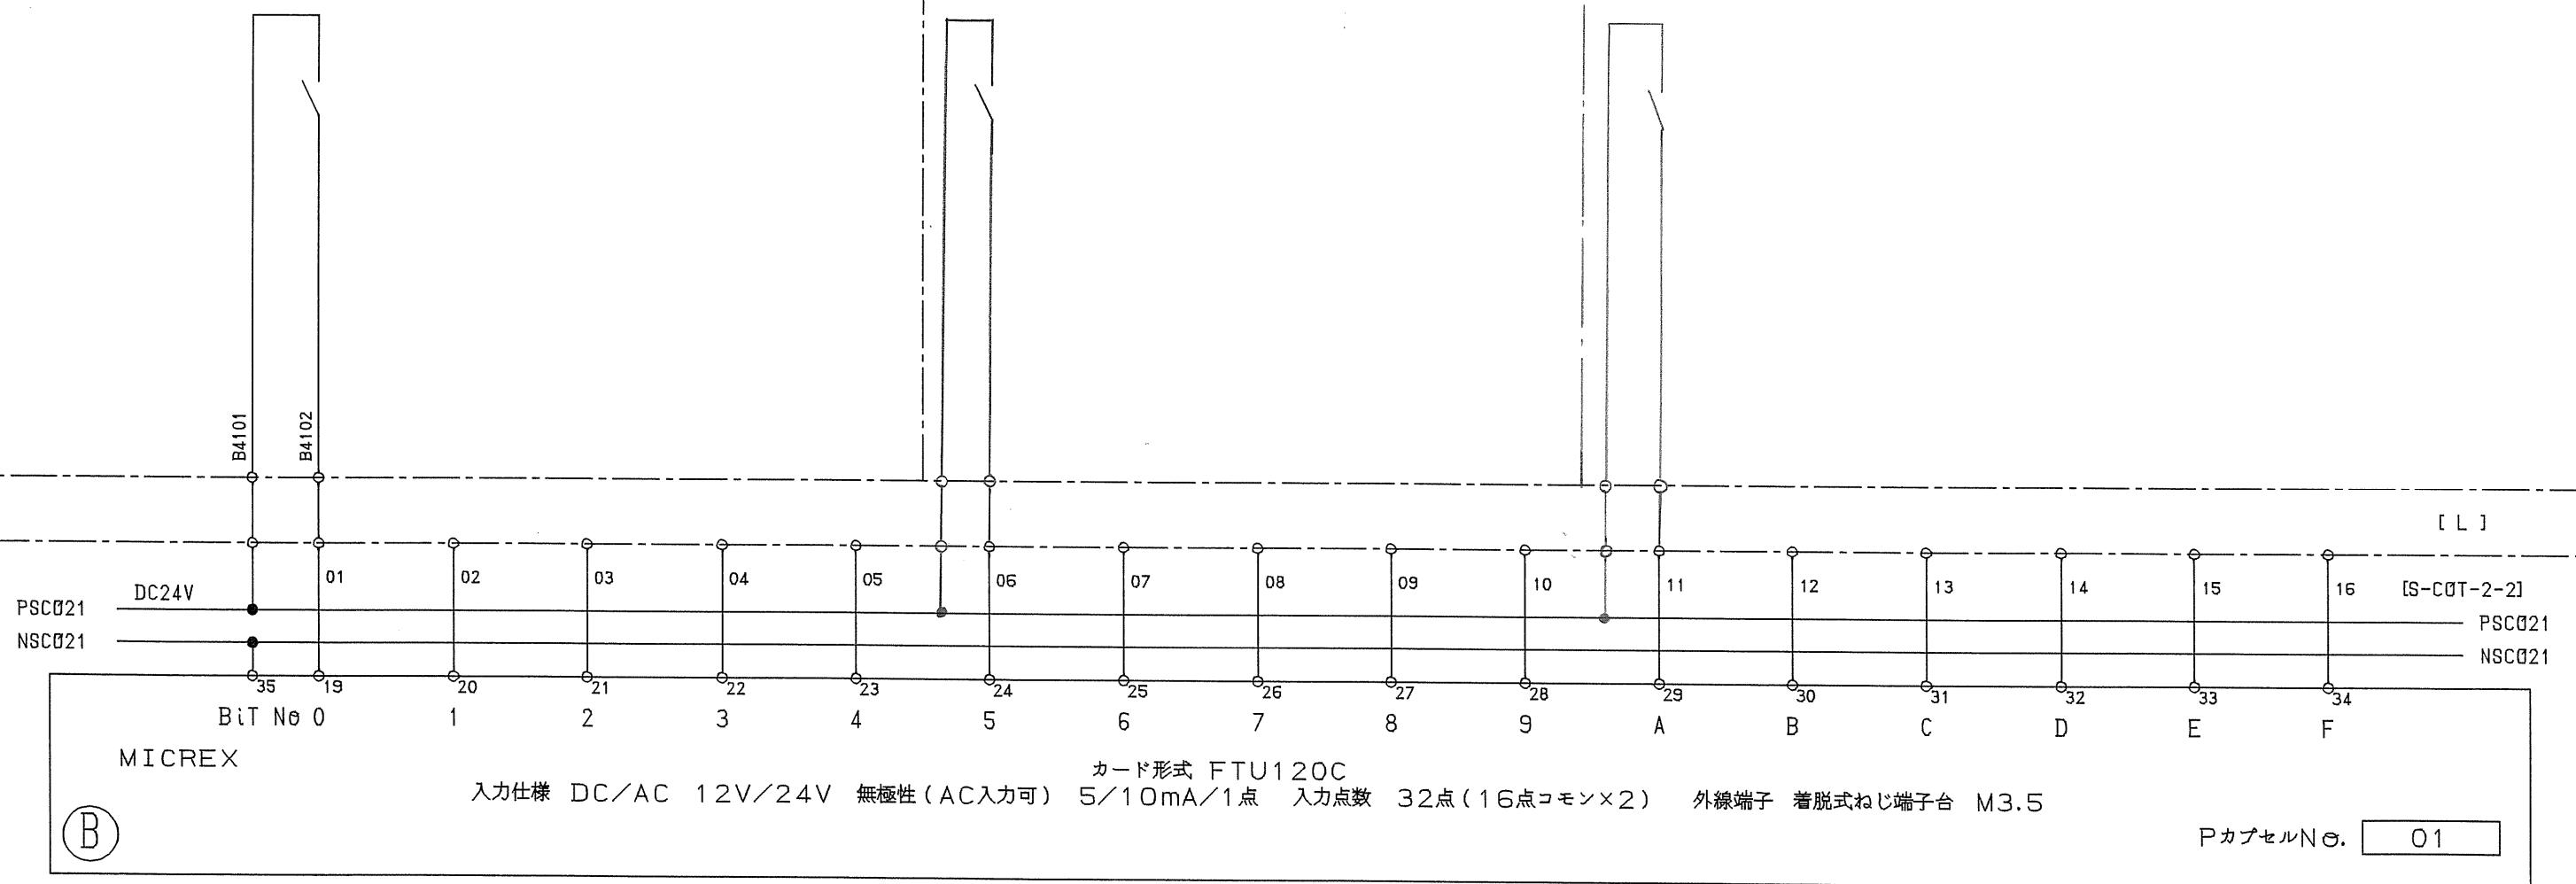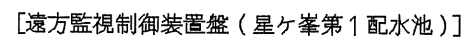

Revisions	⑤ 信号追加	' 02-02-08 河野		Date	Name	Fuji Electric Co., Ltd.	Title	管理管轄入出力制御装置	Ref. Dwg. No.	W 4 2 6 2 9 7	514	t	f
	④ 信号追加	' 10-02-22 河野	Drawn	2000-04-24	森竹							i	
	③ 信号追加	' 05-11-07 大城	Checked									p	
	① 現地試験フォロー	' 02-04-03 河野										s	
インターフェース回路													

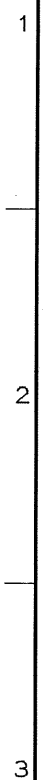
5

回路構成

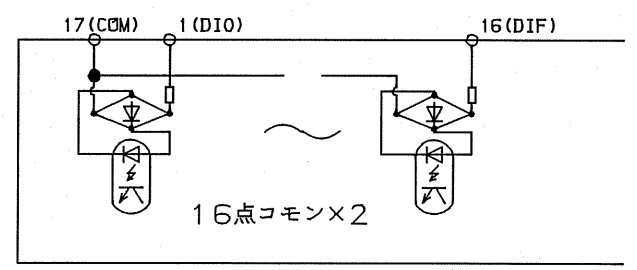


アドレス	項目名称	備考
I.0360	予備	
I.0361	予備	
I.0362	予備	
I.0363	予備	
I.0364	予備	
I.0365	予備	
I.0366	予備	
I.0367	予備	
I.0368	予備	
I.0369	予備	
I.036A	予備	
I.036B	予備	
I.036C	予備	
I.036D	予備	
I.036E	予備	
I.036F	高見水源地	TM故障

[遠方監視制御装置（高見ポンプ所）] より

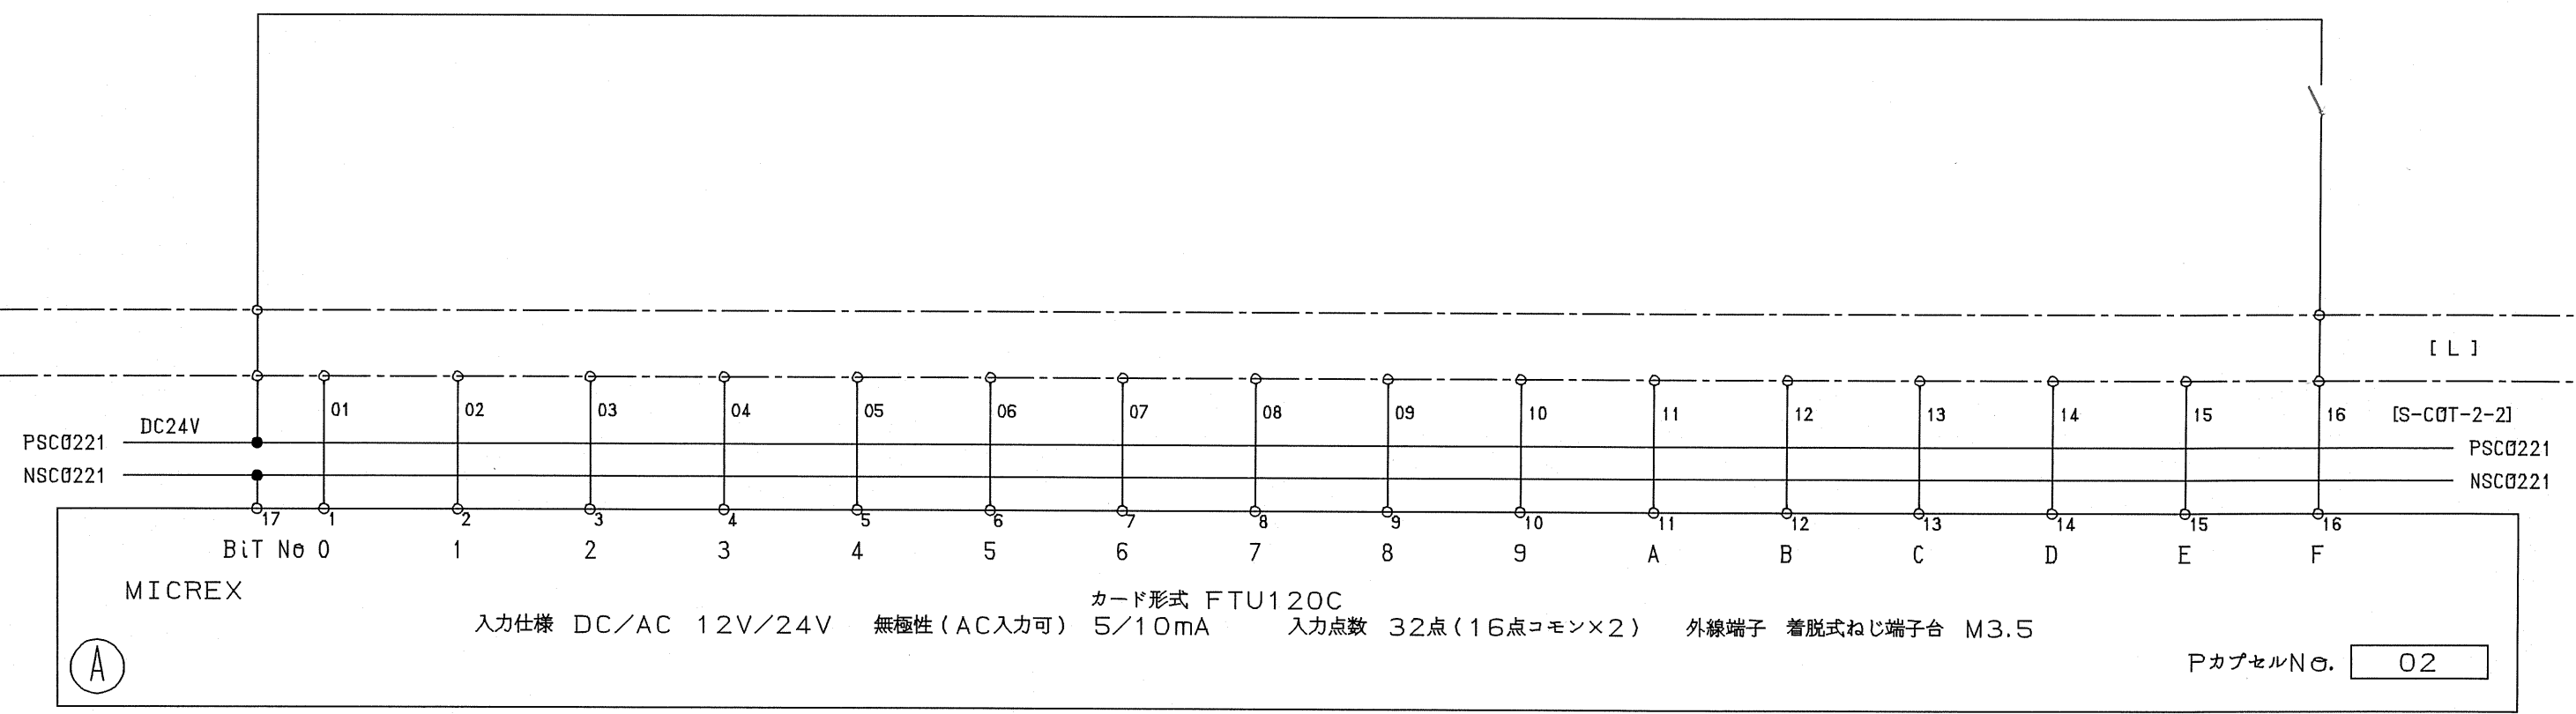


Revisions	①	信号追加	' 00-11-09	折茂		Date	Name	Fuji Electric Co., Ltd.	Title	管理管轄入出力制御装置 インターフェース回路	Rev. No.	W426297	561	P Y L K m
	②	信号追加	' 00-09-21	折茂	Drawn	2000-04-24	森竹							
	③	C18905による改造	' 04-12-03	森竹	Checked									
	④	現地試験フォロー	' 01-06-15	折茂										

回路構成

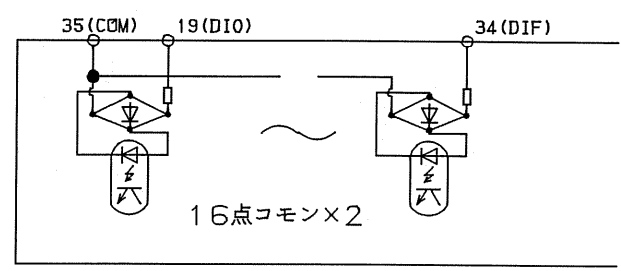

アドレス	項目名称	備考
I.0370	予備	
I.0371	予備	
I.0372	予備	
I.0373	予備	
I.0374	予備	
I.0375	予備	
I.0376	予備	
I.0377	予備	
I.0378	予備	
I.0379	予備	
I.037A	予備	
I.037B	予備	
I.037C	予備	
I.037D	予備	
I.037E	予備	
I.037F	予備	

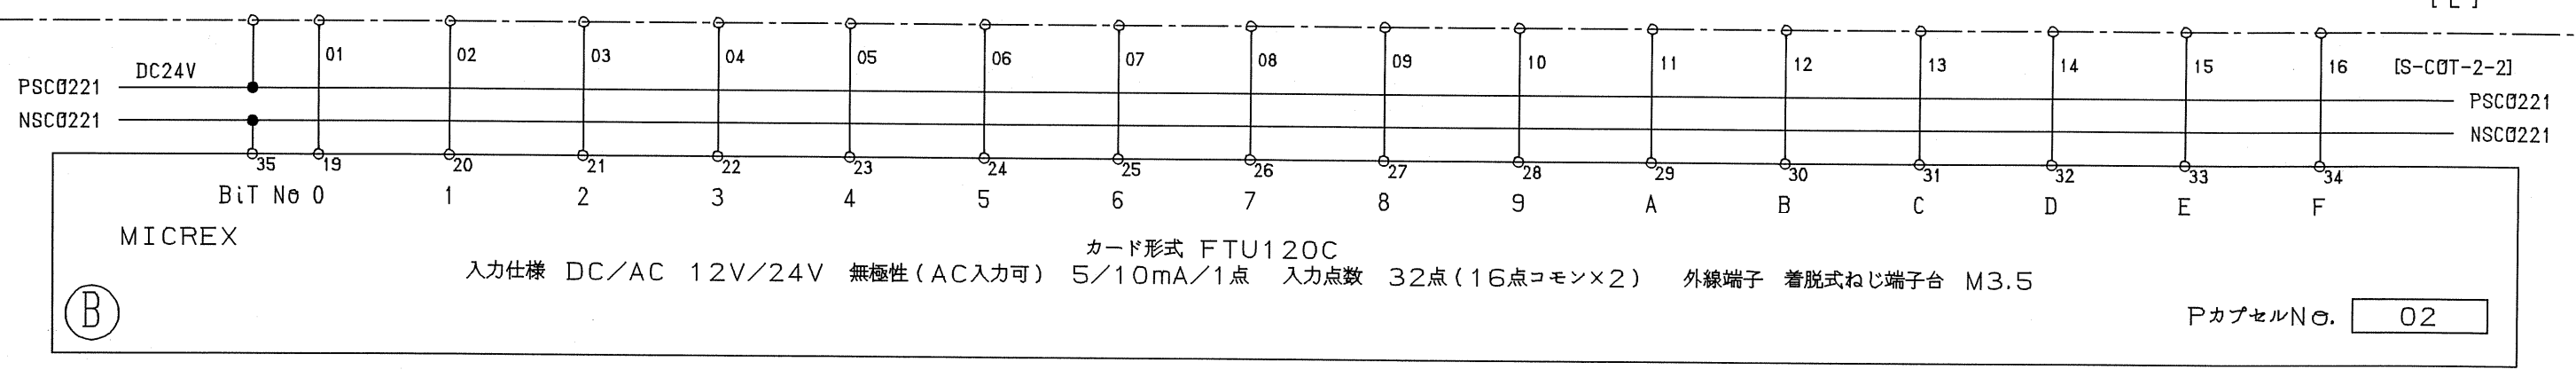

Revisions

○			
○			
①	アドレス変更、信号削除	00-08-21	野崎
②	本頁追加 (P.503を書換え)	00-04-24	森竹

	Date	Name
Drawn	2000-04-24	森竹
Checked		

Fuji Electric Co., Ltd.

管理管轄入出力制御装置
インターフェース回路

Ref. Dwg. No.



W426297

562

M/F DI (ユニット・端子) 2/2
CIFDICUB


①

②

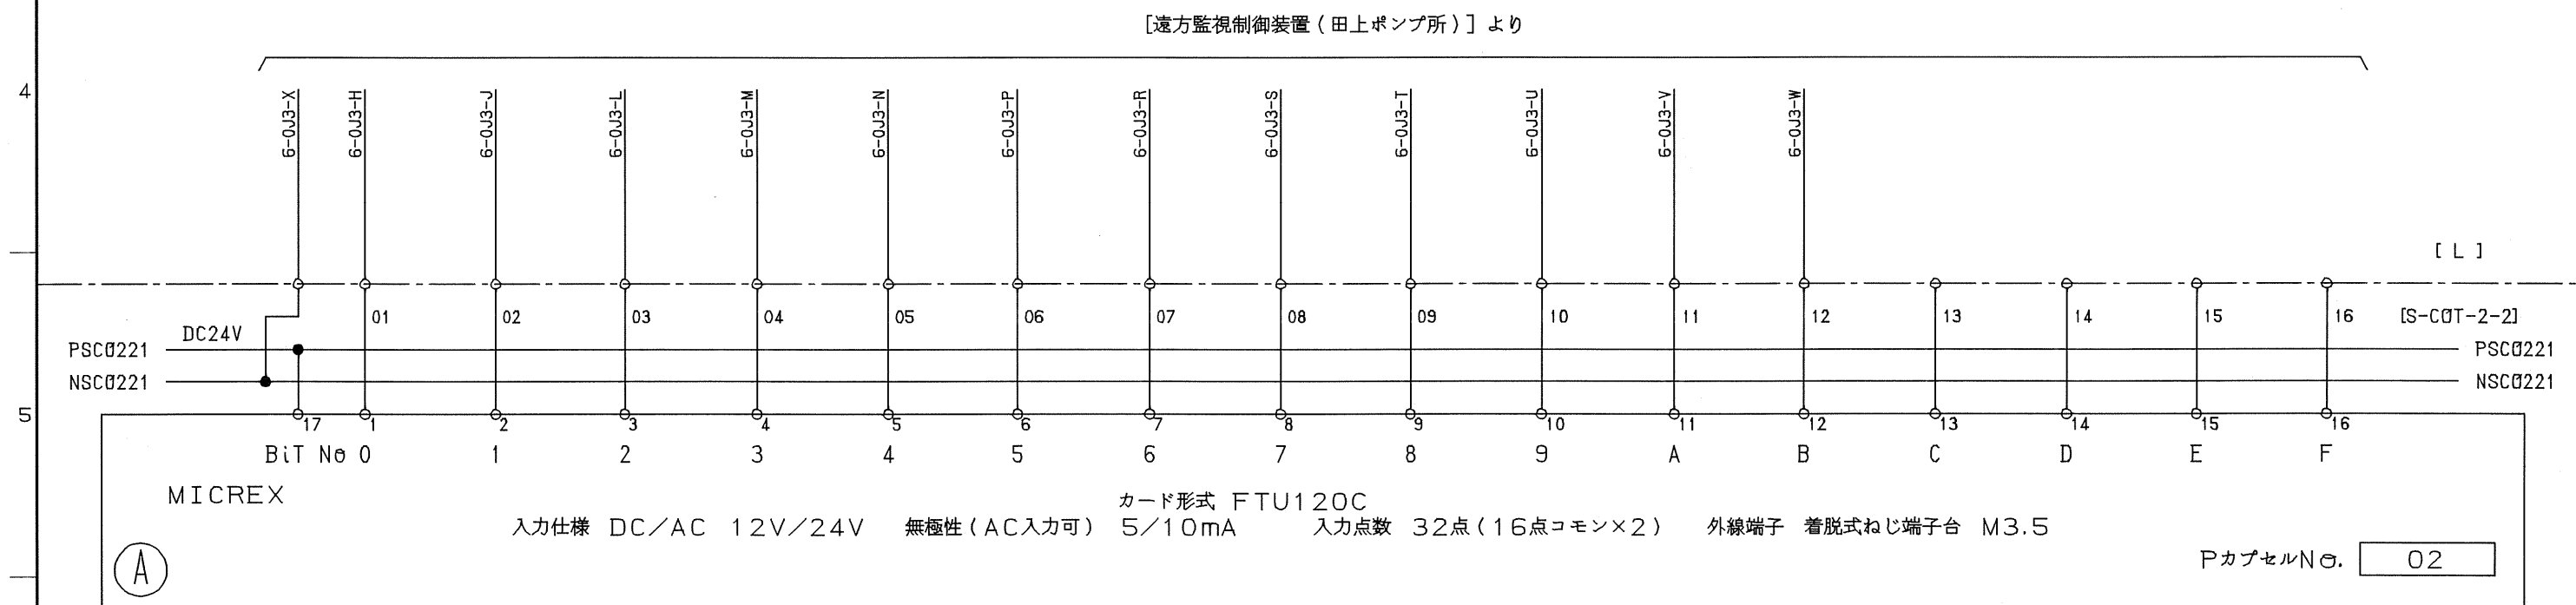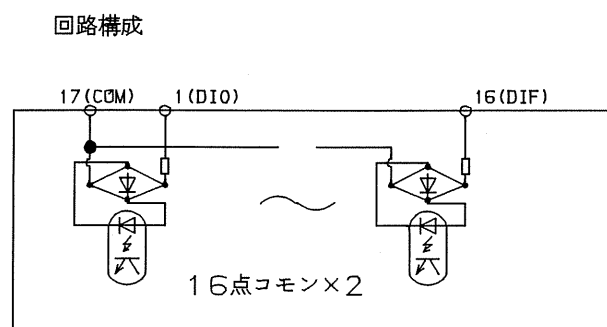


Revisions	⑤	現地試験フォロー	' 01-06-15	折茂		Date	Name	Fuji Electric Co.,Ltd.	Title	管理管轄入出力制御装置 インターフェース回路	Ref. Dwg. No.	W426297	563	M/F DI (ユニット・端子) 1/2 CIEDICUA
	④	コモン変更	' 00-11-09	折茂	Drawn	2000-04-24	森竹							
	③	アドレス変更、信号名称変更	' 00-08-21	野崎	Checked									
	②	本頁追加 (P.504を書換え)	' 00-04-24	森竹										

回路構成

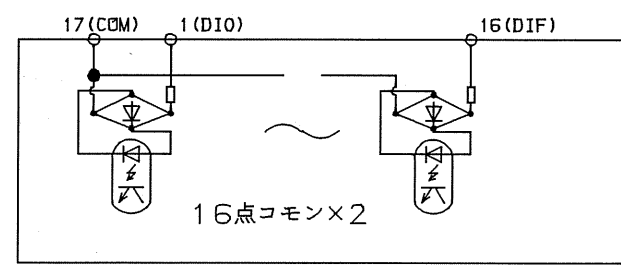

アドレス	項目名称		備考
I.0400	田上ポンプ所	自家発運転	
I.0401	田上ポンプ所	自家発故障	
I.0402	田上ポンプ所	受電停電	
I.0403	田上ポンプ所	受電故障	
I.0404	田上ポンプ所	浸水	
I.0405	田上ポンプ所	火災	
I.0406	田上ポンプ所	扉開	
I.0407	田上ポンプ所無停電電源装置	故障	
I.0408	田上ポンプ所	自家発燃料油面低下	
I.0409	田上ポンプ所	受電しゃ断器入	
I.040A	田上ポンプ所送水元弁	故障	
I.040B	田上ポンプ所送水元弁	全開	
I.040C	田上ポンプ所		
I.040D	田上ポンプ所		
I.040E	田上ポンプ所		
I.040F	田上ポンプ所		

[遠方監視制御装置 (田上ポンプ所)] より (62~3)FTE439913

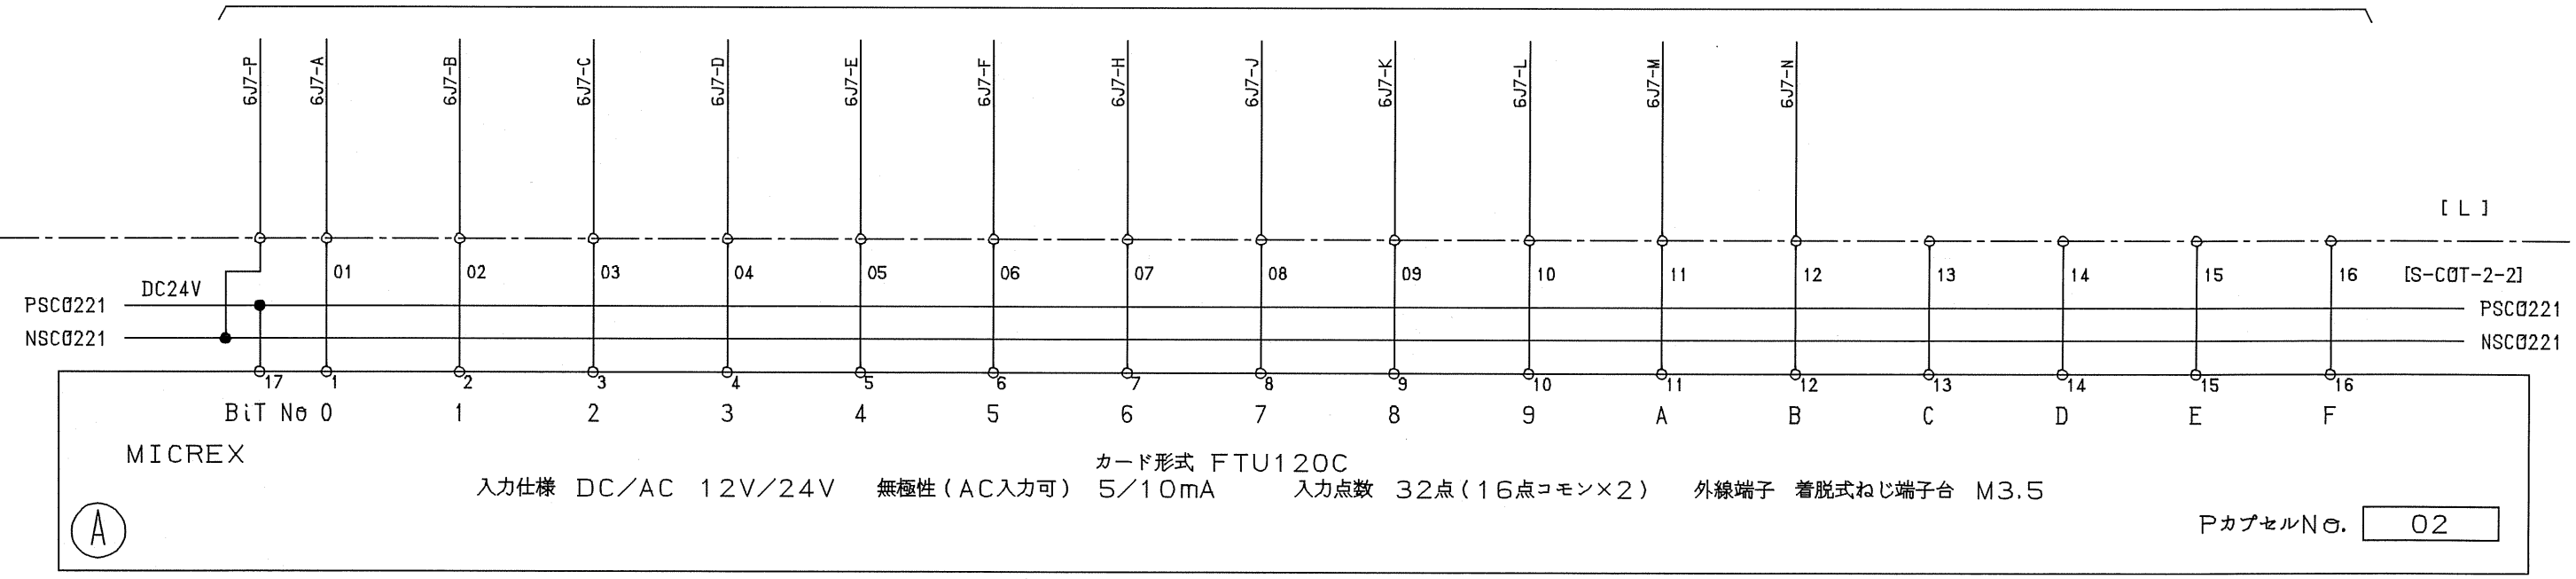

Revisions

○				Date	Name	
①	コモン変更	' 00-11-09	折茂	Drawn	2000-04-24	森竹
②	アドレス変更、信号名称変更	' 00-08-21	野崎	Checked		
③	本頁追加 (P.506を書換え)	' 00-04-24	森竹			

Fuji Electric Co.,Ltd.

管理管轄入出力制御装置
インターフェース回路


W426297

M/F DI (ユニット・端子) 1/2
CIFDICUA

565


565

回路構成

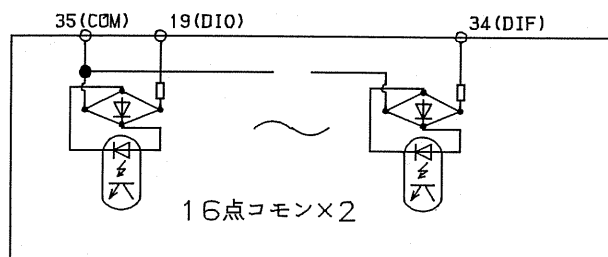


アドレス	項目名称	備考
I.0410	田上ポンプ所送水元弁 全閉	
I.0411	田上ポンプ所1号送水ポンプ 運転	
I.0412	田上ポンプ所2号送水ポンプ 運転	
I.0413	田上ポンプ所3号送水ポンプ 運転	
I.0414	田上ポンプ所1号送水ポンプ 故障	
I.0415	田上ポンプ所2号送水ポンプ 故障	
I.0416	田上ポンプ所3号送水ポンプ 故障	
I.0417	田上ポンプ所1号送水ポンプ 起動待機	
I.0418	田上ポンプ所2号送水ポンプ 起動待機	
I.0419	田上ポンプ所3号送水ポンプ 起動待機	
I.041A	田上ポンプ所 電源故障	
I.041B	田上ポンプ所 一括故障	
I.041C	田上ポンプ所	
I.041D	田上ポンプ所	
I.041E	田上ポンプ所	
I.041F	田上ポンプ所	

[遠方監視制御装置 (田上ポンプ所)] より (63~4)FTE439913

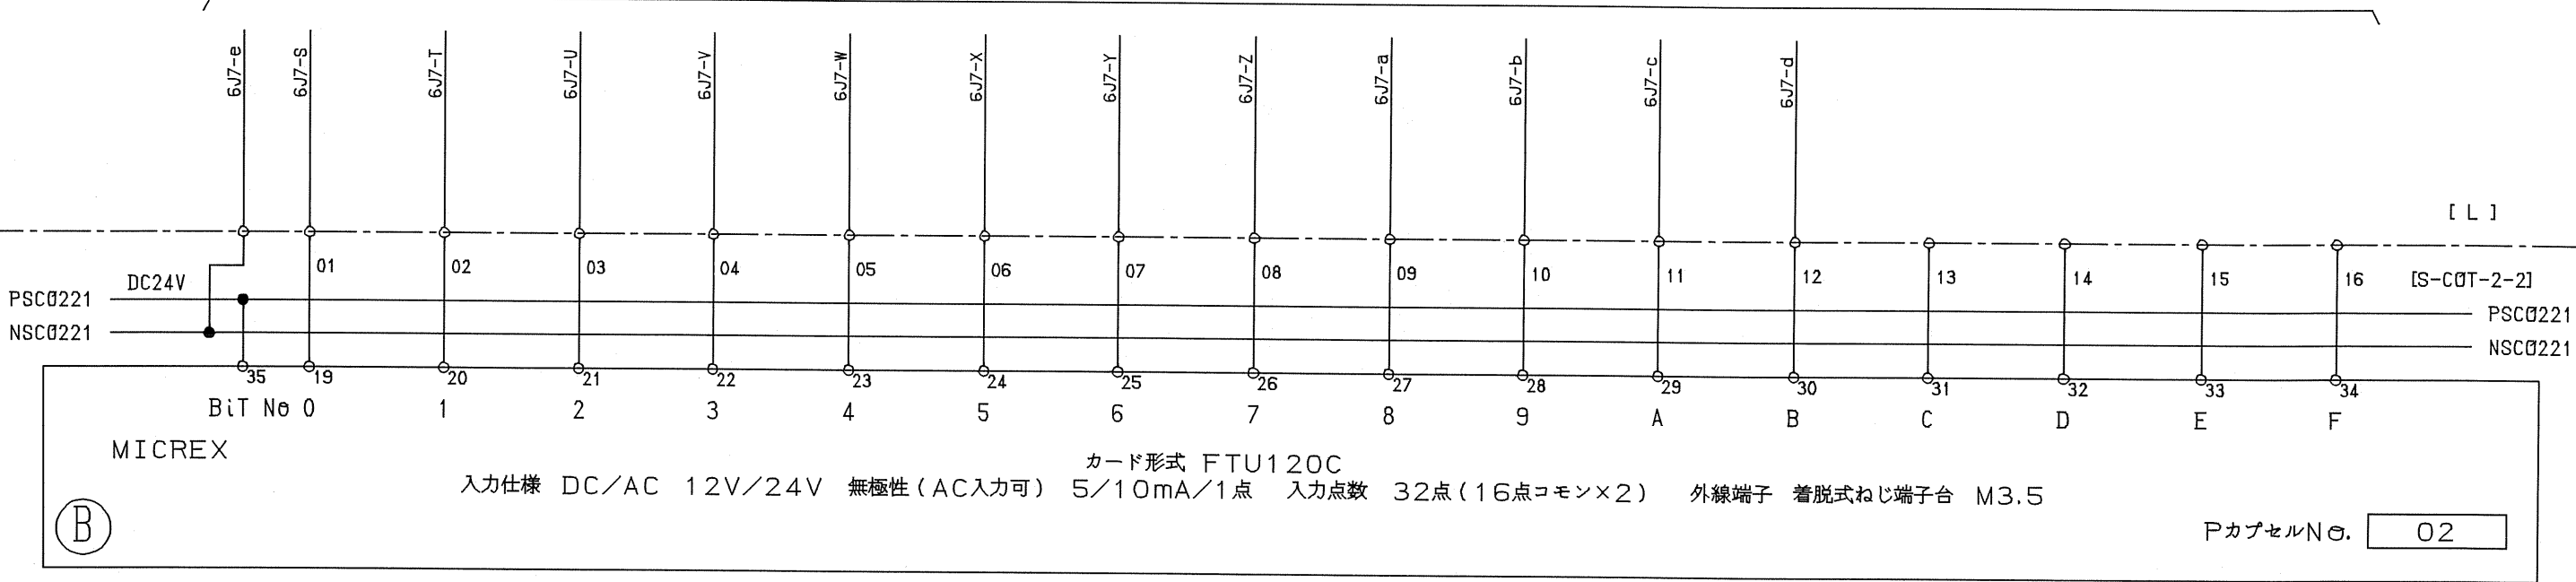


Revisions	○ コモン変更	00-11-09	折茂	Drawn	2000-04-24	森竹	Fuji Electric Co., Ltd.	Title	管理管轄入出力制御装置 インターフェース回路	Ref. Dwg. No.	W426297	566	f i m
	① アドレス変更、取合いフォロー	00-08-21	野崎	Checked									
	② 本頁追加 (P.507を書換え)	00-04-24	森竹										

回路構成

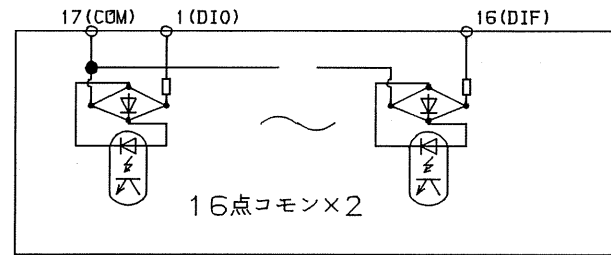







アドレス	項目名称	備考
I.0420	田上ポンプ所田上水源地 停電	
I.0421	田上ポンプ所田上水源地 TM故障	
I.0422	田上ポンプ所田上水源地 一括故障	
I.0423	田上ポンプ所柴ヶ原第3配水池 停電	
I.0424	田上ポンプ所柴ヶ原第3配水池 故障	
I.0425	田上ポンプ所武田ヶ瀬戸ポンプ所 停電	
I.0426	田上ポンプ所武田ヶ瀬戸ポンプ所 故障	
I.0427	田上ポンプ所武之台高架配水池 水位低	
I.0428	田上ポンプ所武之台高架配水池 水位高	
I.0429	田上ポンプ所 シーケンス故障	
I.042A	田上ポンプ所 柴ヶ原第3配水池 計装故障	
I.042B	田上ポンプ所 柴ヶ原第3配水池 漏開	
I.042C	田上ポンプ所	
I.042D	田上ポンプ所	
I.042E	田上ポンプ所	
I.042F	田上ポンプ所 TM故障	

[遠方監視制御装置(田上ポンプ所)]より (65~6)FTE439913

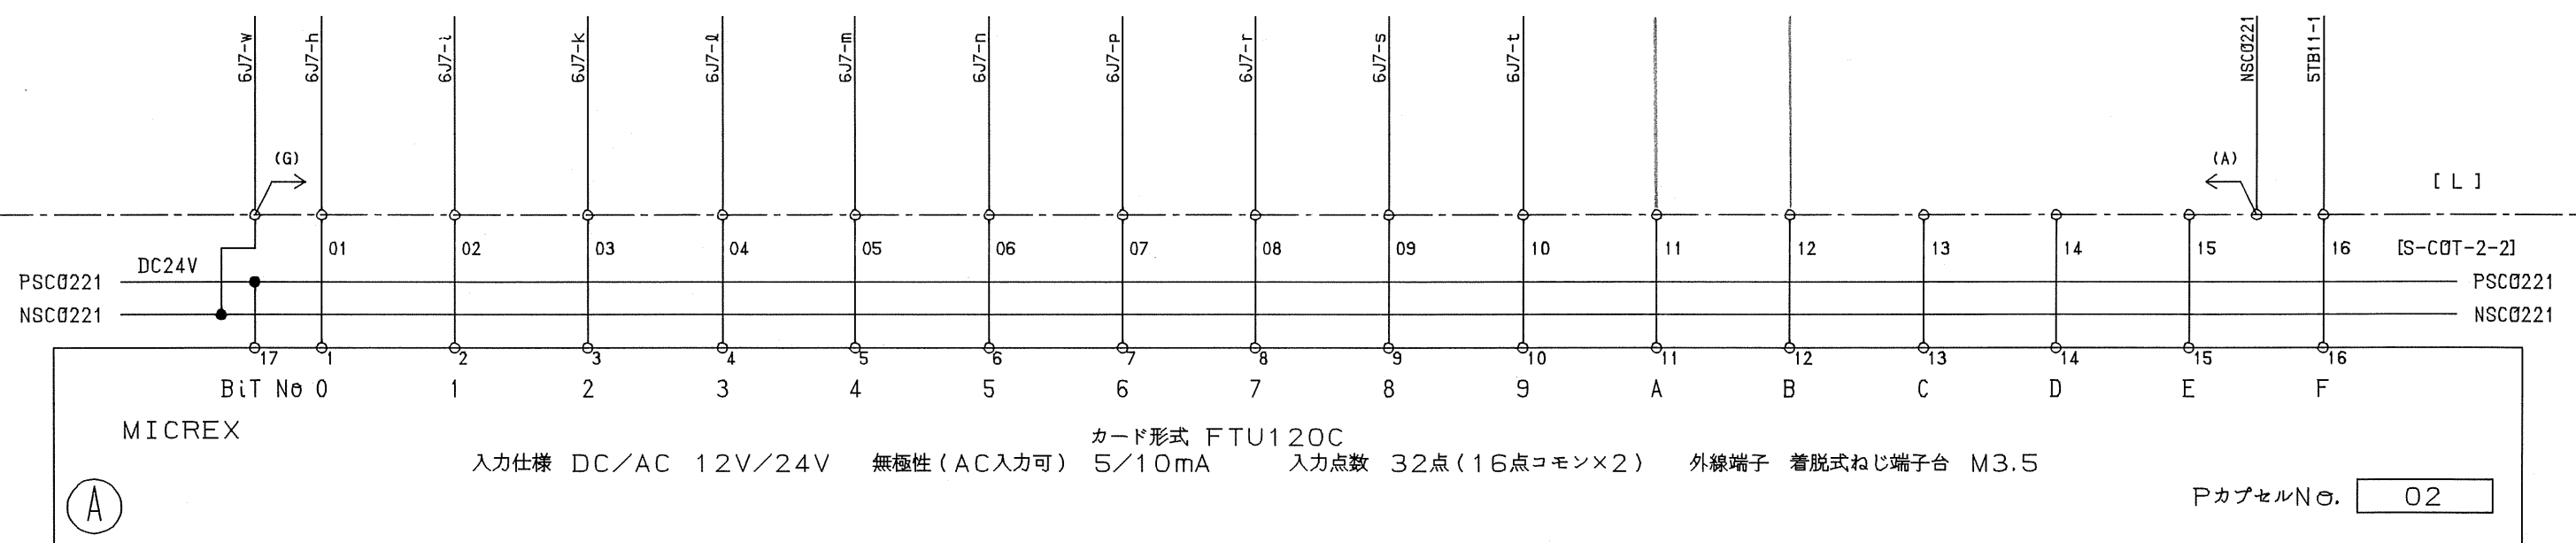

P) 現地試験フォロー ' 01-06-15 折茂 G) 清泉寺水源地電計装設備工事に伴う変更 2013-02-15 黒沼


Revisions	③	コモン変更	' 00-11-09	折茂		Date	Name	Fuji Electric Co., Ltd.	Title	管理管轄入出力制御装置	Ref. Dwg. No.	W426297	567	P G K M
	④	信号追加	' 00-09-20	折茂	Drawn	2000-04-24	森竹							
	⑤	アドレス変更、取合いフォロー	' 00-08-21	野崎	Checked									
	⑥	本頁追加 (P.508を書換え)	' 00-04-24	森竹										

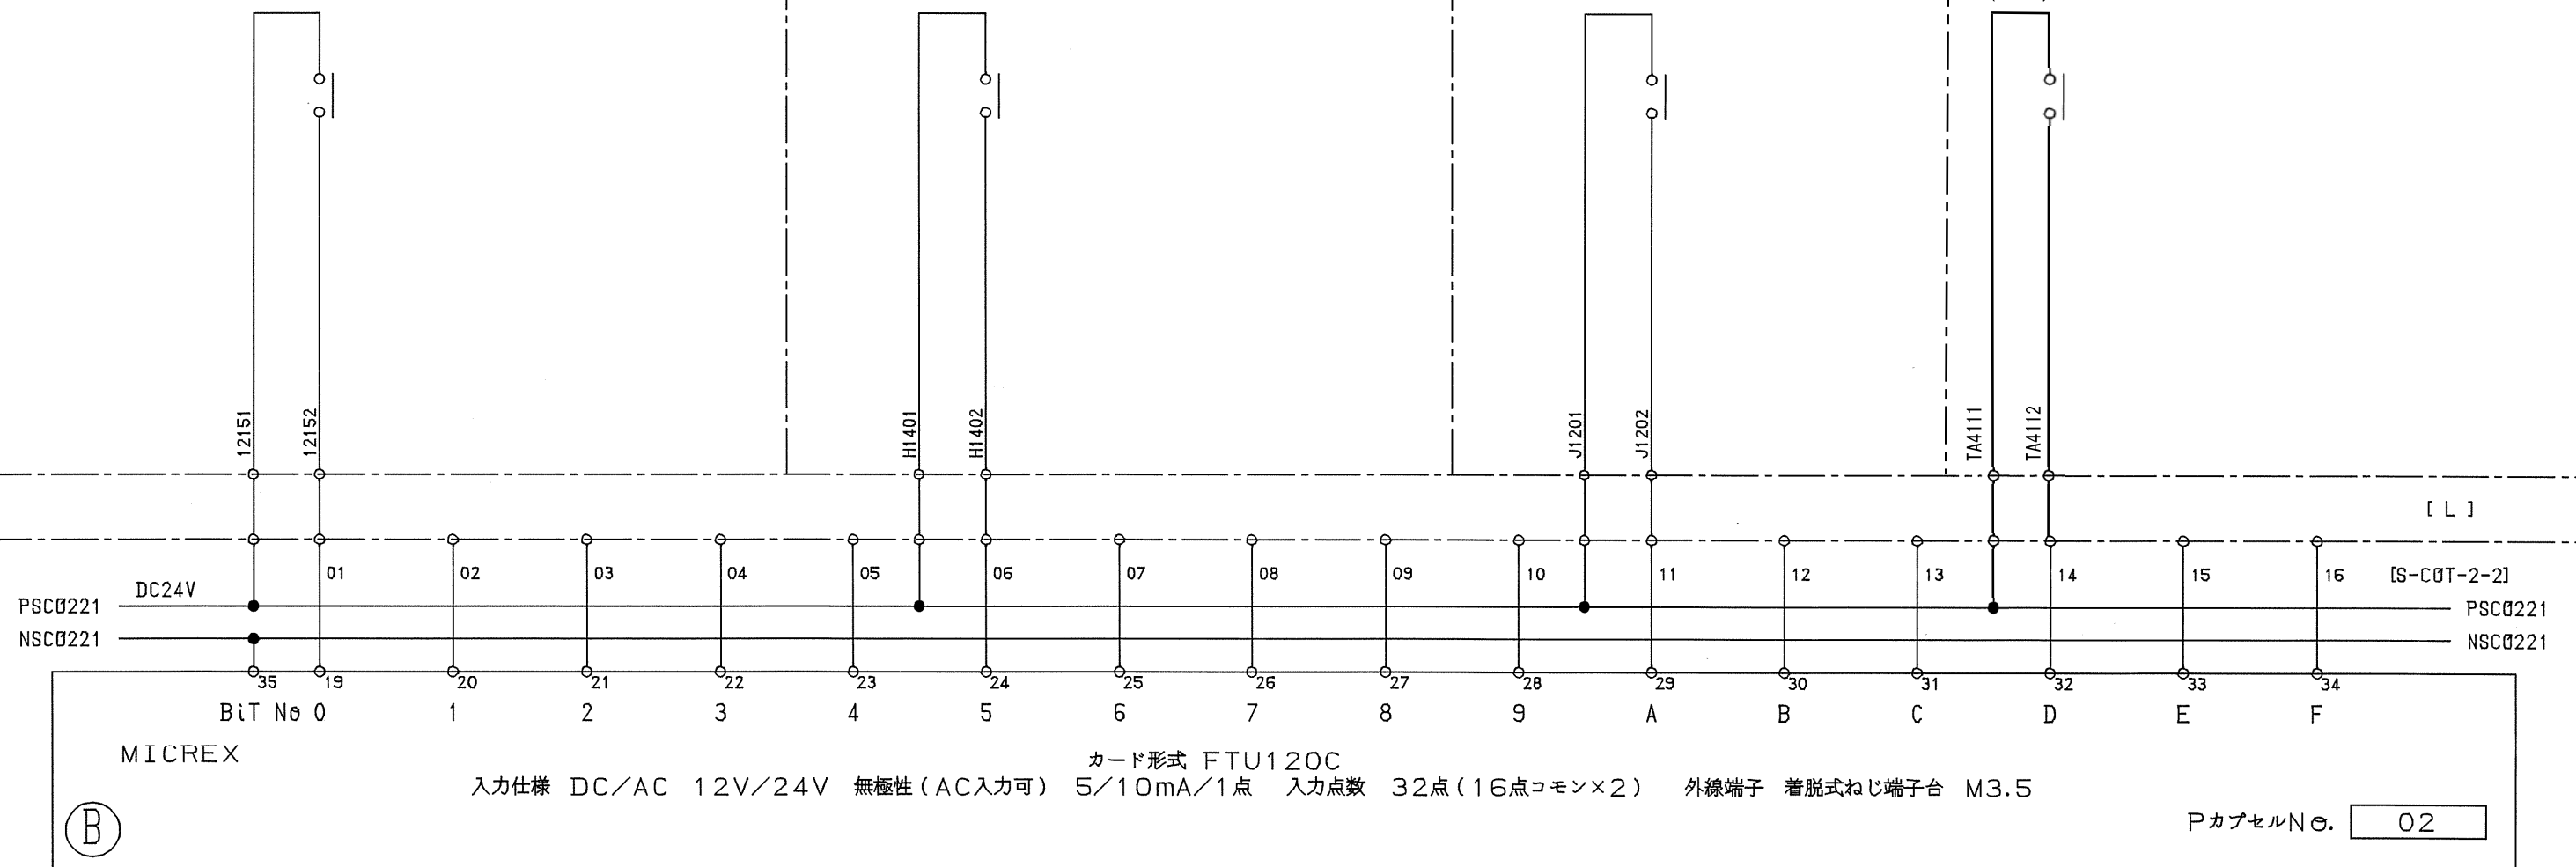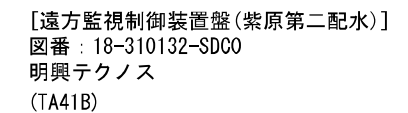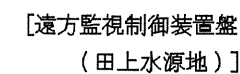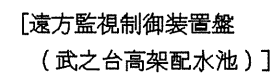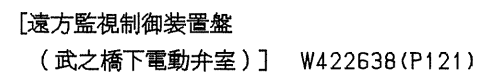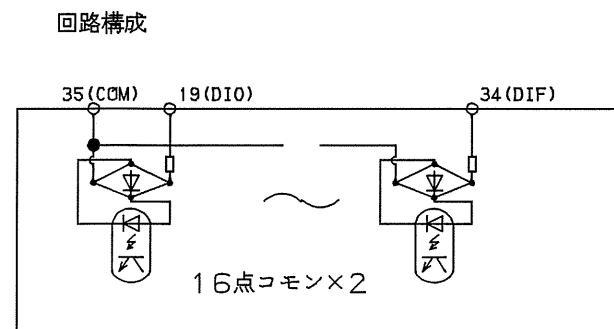

Revisions	①	取合い変更	' 00-11-09	折茂		Date	Name	Fuji Electric Co.,Ltd.	Title	管理管轄入出力制御装置 インターフェース回路	Ref. Dwg. No.	W426297	568	P t i c l e	E
	②	一部変更	' 00-09-20	折茂	Drawn	2000-04-24	森竹								
	③	J1041559による改造	' 20-03-10	淵邊	Checked										
	④	現地試験フォロー	' 02-04-03	河野											

A B C D E F G H

回路構成

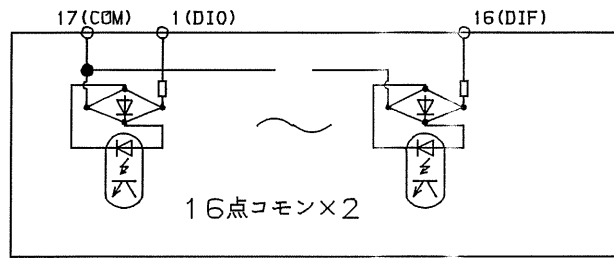

アドレス	項目名称	備考
I.0440	管理管轄入出力制御装置(1)	電源断
I.0441	管理管轄入出力制御装置(2)	電源断
I.0442	予備	
I.0443	予備	
I.0444	予備	
I.0445	脇田水源地 テレメータ異常	一括故障
I.0446	予備	
I.0447	予備	
I.0448	予備	
I.0449	予備	
I.044A	田上台配水池 テレメータ異常	
I.044B	予備	
I.044C	予備	
I.044D	予備	
I.044E	予備	
I.044F	予備	

[遠方監視制御装置盤(脇田水源地)]


[遠方監視制御装置盤(田上台配水池)]

[S-COT-2-1]より

(401F)

(402F)

[L]

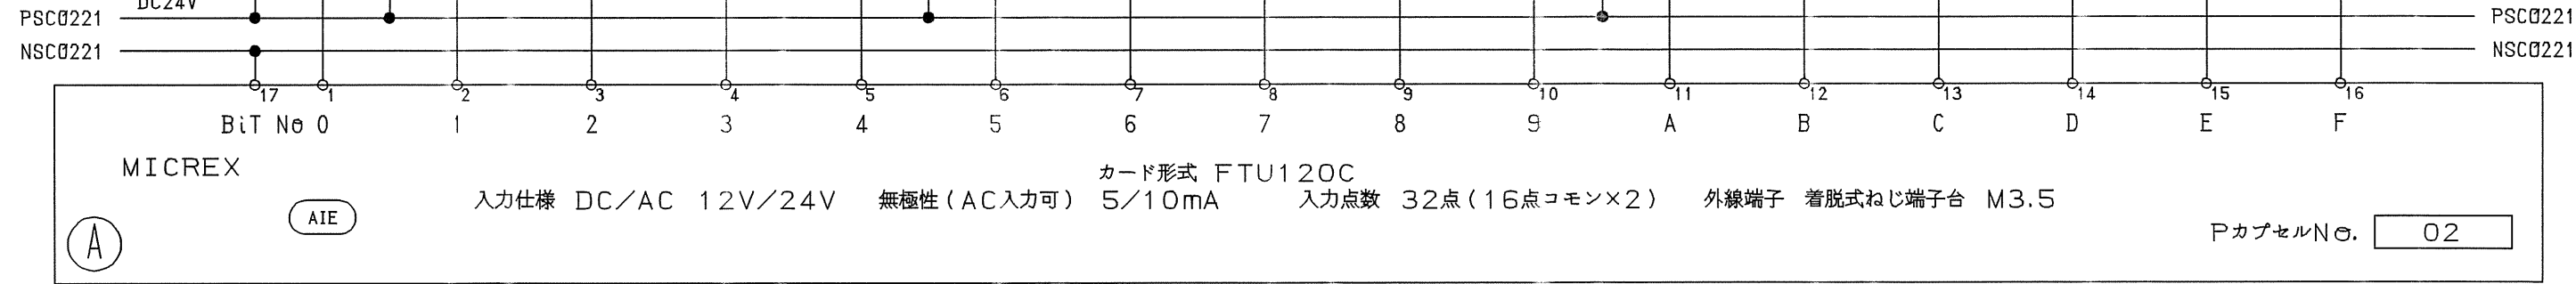

入力仕様 DC/AC 12V/24V 無極性(AC入力可) 5/10mA 入力点数 32点(16点コモン×2) 外線端子 着脱式ねじ端子台 M3.5


PケーブルNo. 02

Revisions	① Q33532による取合フォロー	03-02-07	河野	Date	Name	Fuji Electric Co.,Ltd.	管理管轄入出力制御装置 インターフェース回路	Ret.Dwg.No.	W426297	569	× P V
	② 現地試験フォロー	01-06-15	折茂	Drawn	森竹						
	③ アドレス変更、信号取合い追加	00-08-21	野崎	Checked							
	④ テレメータ追加による取合変更	04-01-19	河野								

A B C D E F G H


A B C D E F G H

回路構成

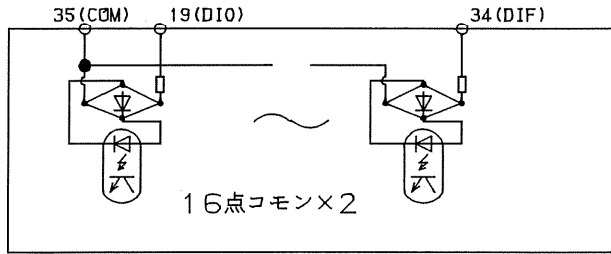

アドレス	項目名称	備考
I.0450	新郡元水源地	予備
I.0451	新郡元水源地	予備
I.0452	新郡元水源地	予備
I.0453	新郡元水源地	予備
I.0454	新郡元水源地	予備
I.0455	新郡元水源地	予備
I.0456	新郡元水源地	予備
I.0457	新郡元水源地	予備
I.0458	新郡元水源地	予備
I.0459	新郡元水源地	予備
I.045A	新郡元水源地	予備
I.045B	新郡元水源地	予備
I.045C	新郡元水源地	予備
I.045D	新郡元水源地	予備
I.045E	新郡元水源地	予備
I.045F	新郡元水源地	TM故障


[遠方監視制御装置(新郡元水源地)]より 図番: 18-310132-SDC0 明興テクノス殿 (TA41B)

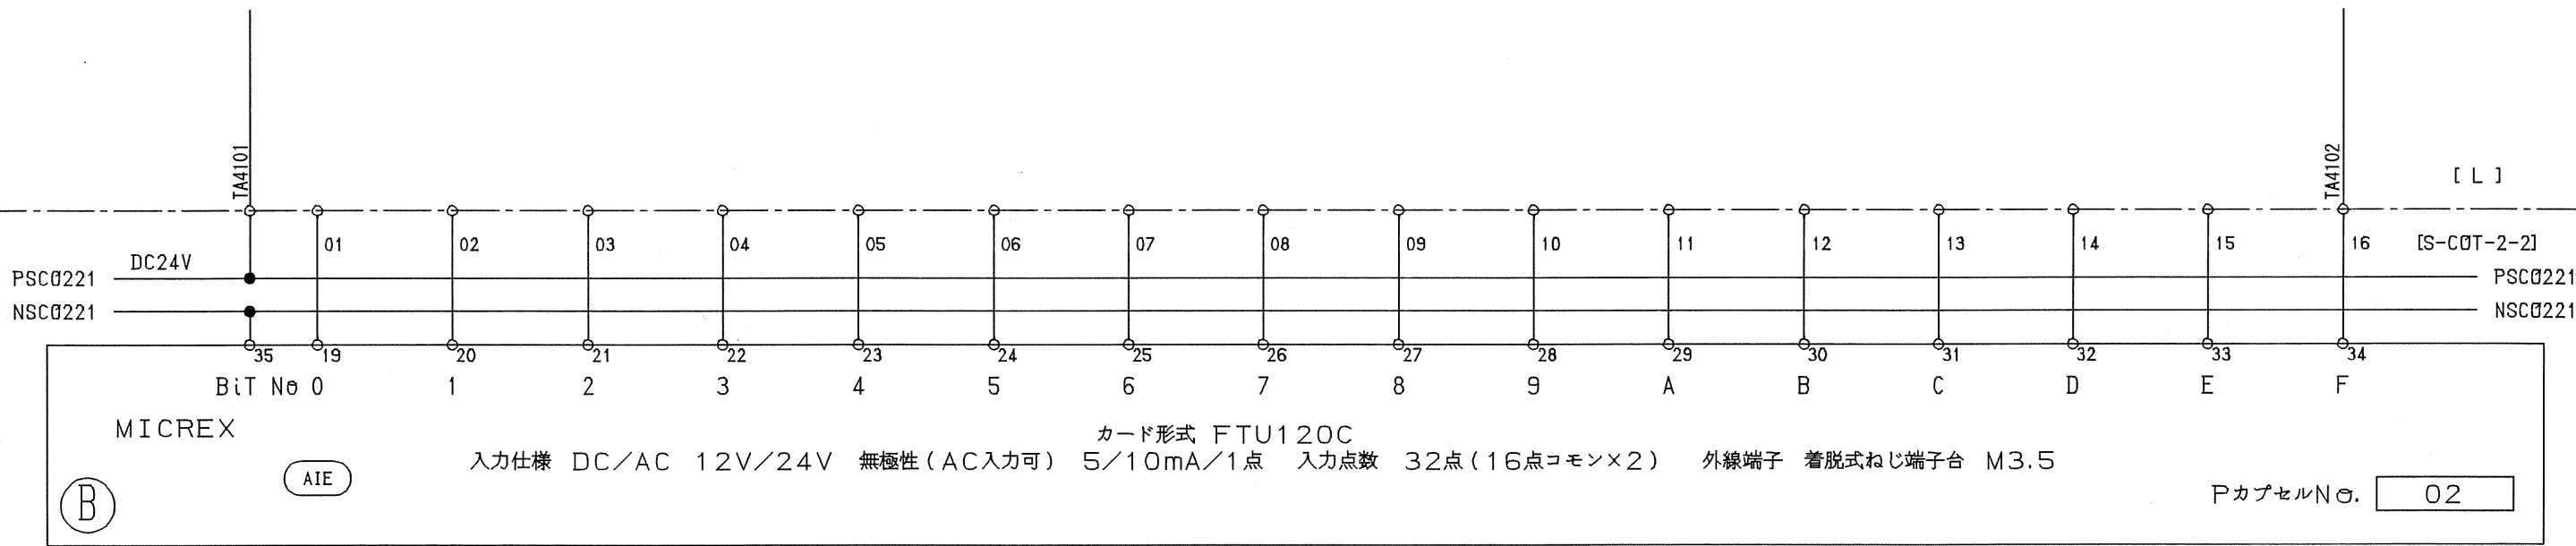

Revisions	①	現地試験フォロー	' 01-06-15	折茂		Date	Name	Fuji Electric Co.,Ltd.	Title	管理管轄入出力制御装置 インターフェース回路	Ref. Dwg. No.	W426297	570	L f i k P
	②	信号追加	' 00-09-20	折茂	Drawn	2000-04-24	森竹							
	③	アドレス変更	' 00-08-21	野崎	Checked									
	④	J1041559による改造	' 20-03-10	淵邊										

全点独立×16

ア ド レ ス	項 目 名 称	備 考
0.0460	田上ポンプ所送水元弁 開指令	
0.0461	田上ポンプ所送水元弁 予備	
0.0462	田上ポンプ所送水元弁 閉指令	
0.0463	田上ポンプ所送水元弁 選択	
0.0464	田上ポンプ所受電しゃ断器 選択	
0.0465	田上ポンプ所 切指令	
0.0466	田上ポンプ所 入指令	
0.0467	田上ポンプ所 手動選択	
0.0468	田上ポンプ所 自動選択	
0.0469	田上ポンプ所 1号選択	
0.046A	田上ポンプ所 2号選択	
0.046B	田上ポンプ所 3号選択	
0.046C	田上ポンプ所 自家発停止	
0.046D	田上ポンプ所 自家発起動	
0.046E	田上ポンプ所 自家発連動	
0.046F	田上ポンプ所 自家発自動	

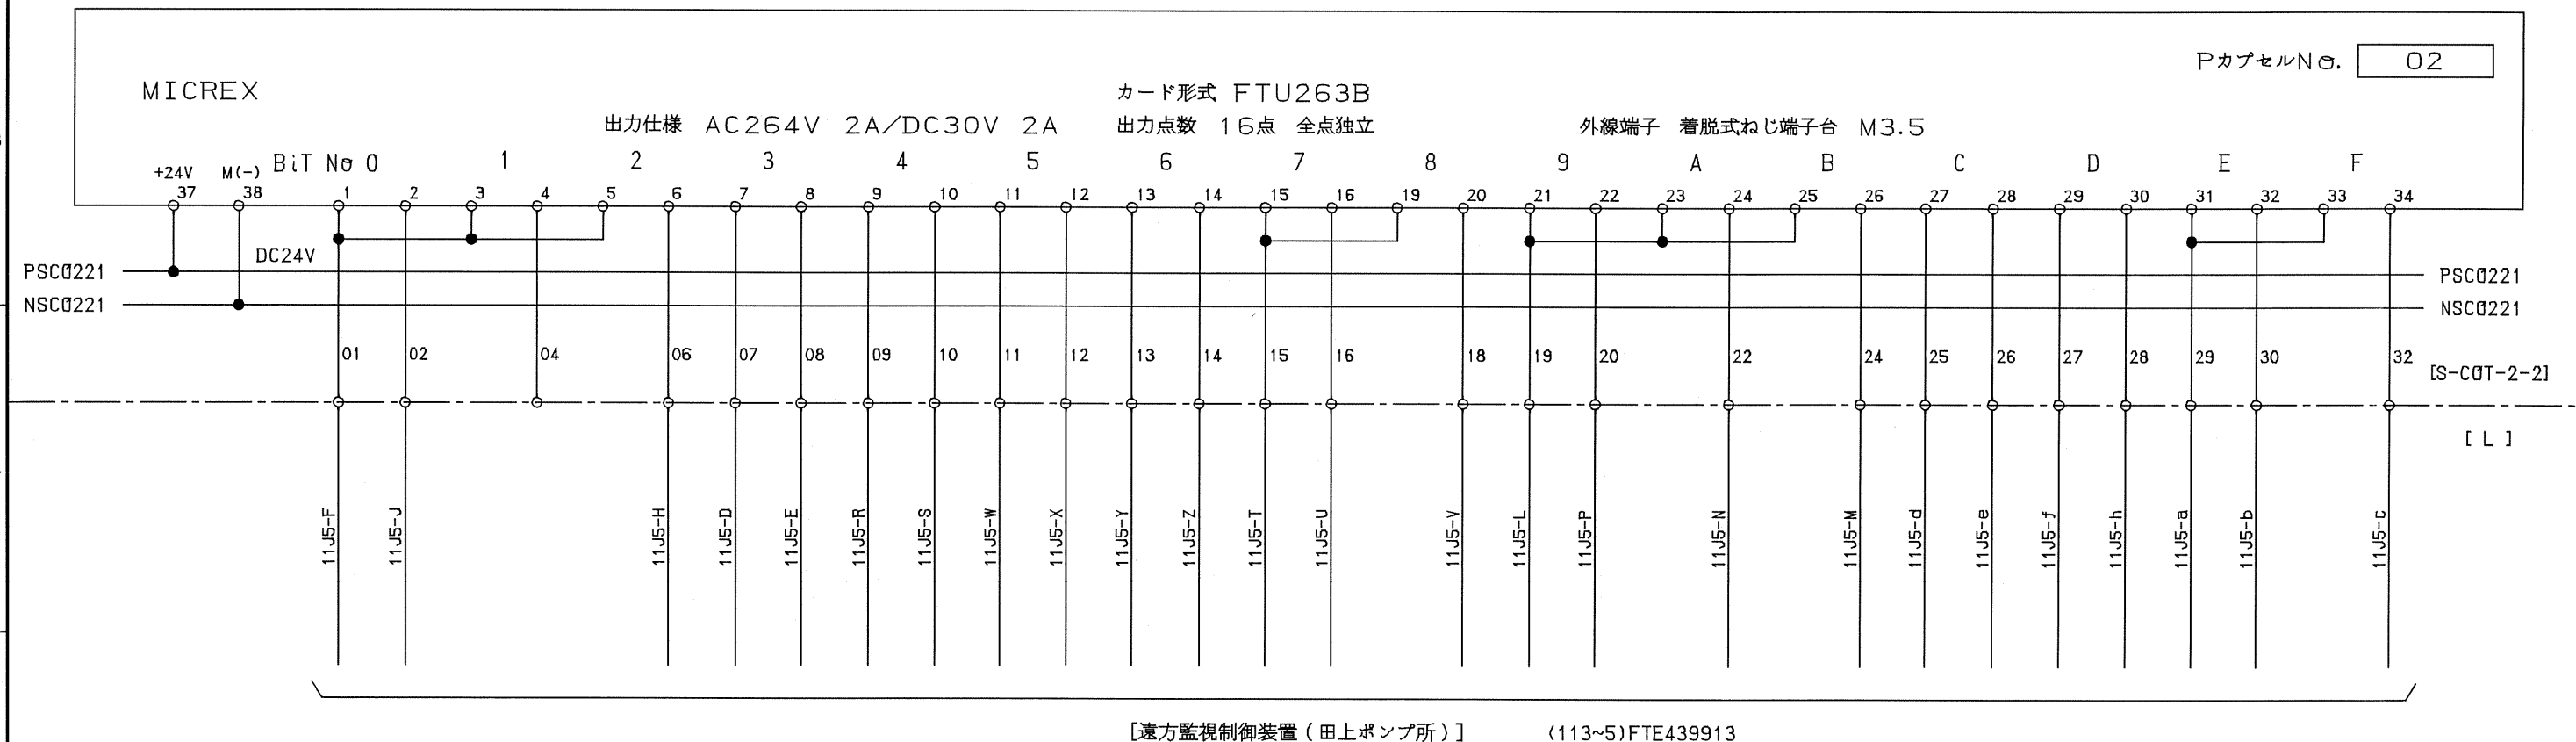


(113~5)FTE439913

Revisions	○			Date	Name	Fuji Electric Co.,Ltd.	Title	管理管轄入出力制御装置 インターフェース回路	Ref.Dwg.No.	(371-376X)					
	②	現地試験フォロー	' 01-06-15	折茂	Drawn					2000-04-24	森竹	W 4 2 6 2 9 7	577	フ ィ ー ド バ ック	
	③	アドレス変更、信号名称変更	' 00-08-21	野崎	Checked										
	④	本頁追加 (P.517を書換え)	' 00-04-24	森竹											
A		B		C		D		E		F		G		H	

全点独立×16

アドレス	項目名称	備考
0.0470	田上ポンプ所 選択	常ON
0.0471	田上ポンプ所 リセット	常OFF
0.0472	田上ポンプ所 予備	
0.0473	田上ポンプ所 予備	
0.0474	田上ポンプ所 予備	
0.0475	田上ポンプ所 予備	
0.0476	田上ポンプ所 予備	
0.0477	田上ポンプ所 予備	
0.0478	田上ポンプ所 予備	
0.0479	田上ポンプ所 予備	
0.047A	田上ポンプ所 予備	
0.047B	田上ポンプ所 予備	
0.047C	田上ポンプ所 予備	
0.047D	田上ポンプ所 予備	
0.047E	田上ポンプ所 予備	
0.047F	田上ポンプ所 予備	

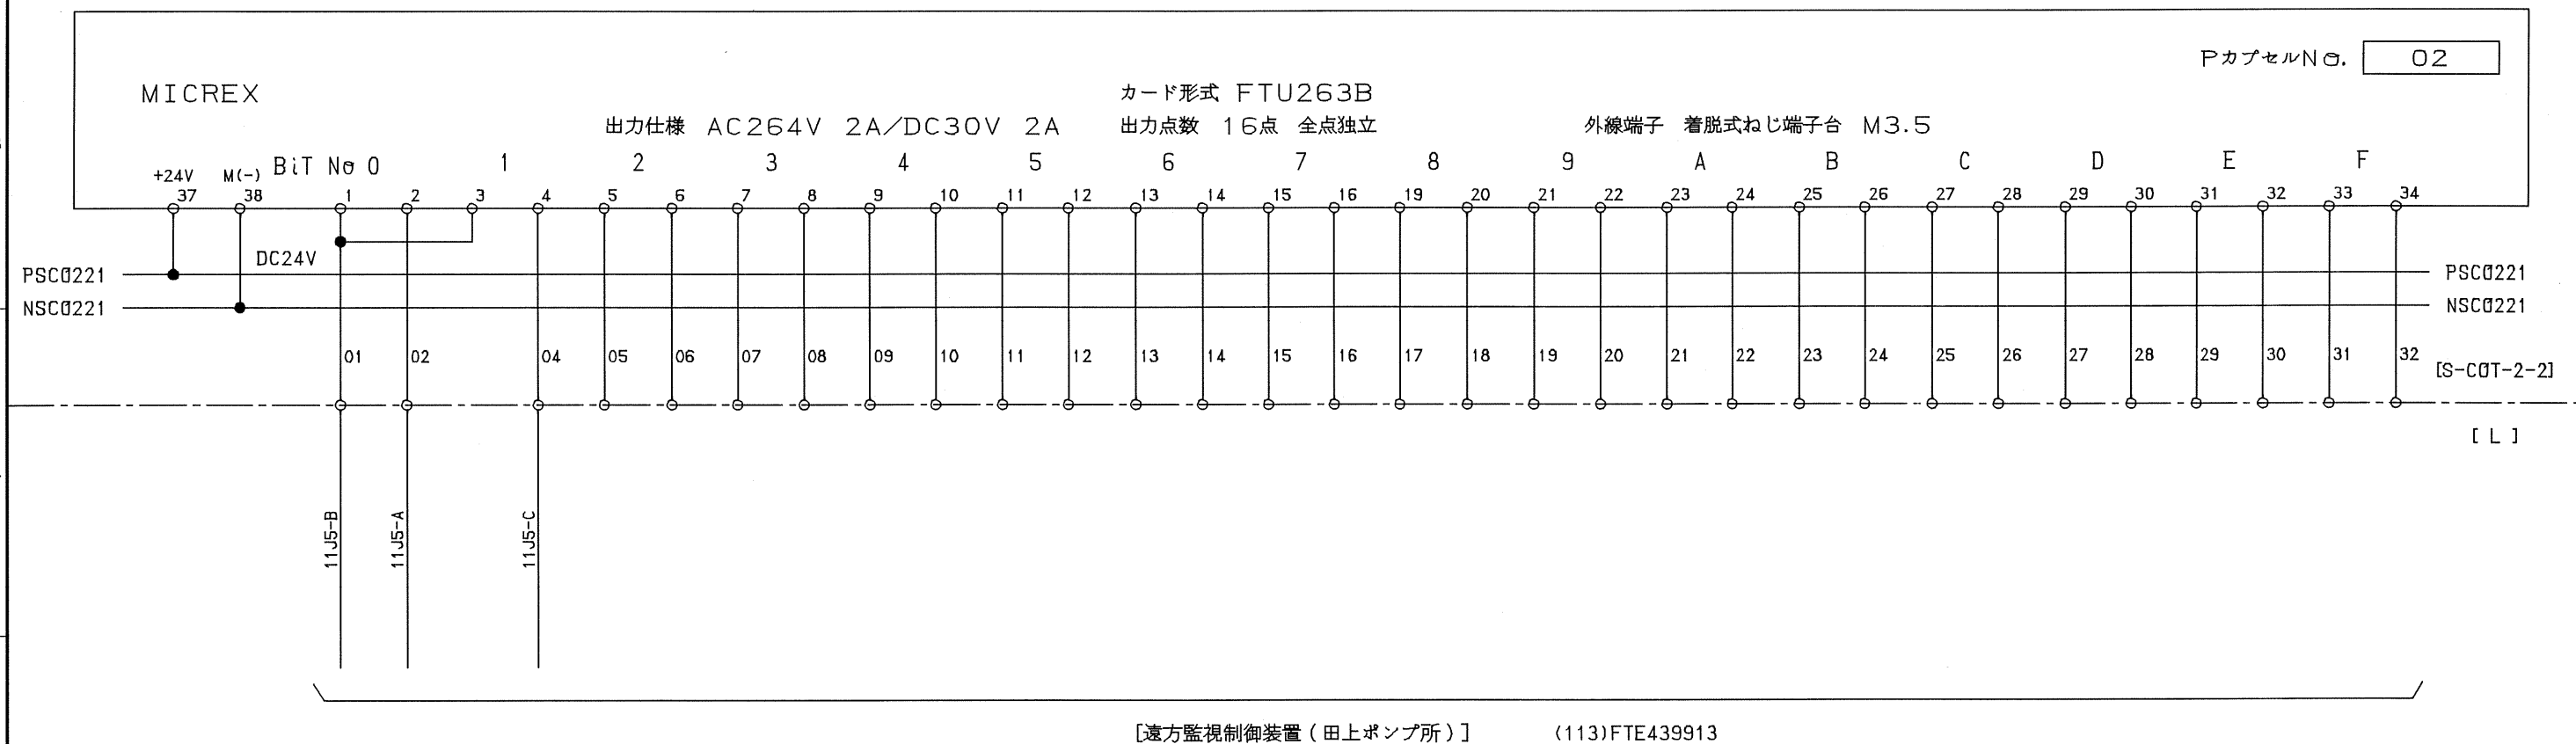


(113)FTE439913

Revisions	⑤	現地試験フォロー	' 01-06-15	折茂		Date	Name	Fuji Electric Co., Ltd.	Title	管理管轄入出力制御装置 インターフェース回路	Ref. Dwg. No.	W 4 2 6 2 9 7	578	M/F D0 (RY・ユニット) 1 / 1 CIFDGRUA	P
	④	ケアレスミスフォロー	' 00-11-09	折茂	Drawn	2000-04-24	森竹								
	③	アドレス変更、取合いフォロー	' 00-08-21	野崎	Checked										
	②	本頁追加 (P.518を書換え)	' 00-04-24	森竹											

アドレス	CH. NO.	項目名称	備考
WB0100	00	予備	
WB0101	01	予備	
WB0102	02	予備	
WB0103	03	予備	
WB0104			CH.00 ステータス情報
WB0105			CH.01 ステータス情報
WB0106			CH.02 ステータス情報
WB0107			CH.03 ステータス情報



アドレス	CH. NO.	項目名称	備考
WB0108	00	予備	
WB0109	01	予備	
WB0110	02	予備	
WB0111	03	予備	
WB0112			CH.00 ステータス情報
WB0113			CH.01 ステータス情報
WB0114			CH.02 ステータス情報
WB0115			CH.03 ステータス情報

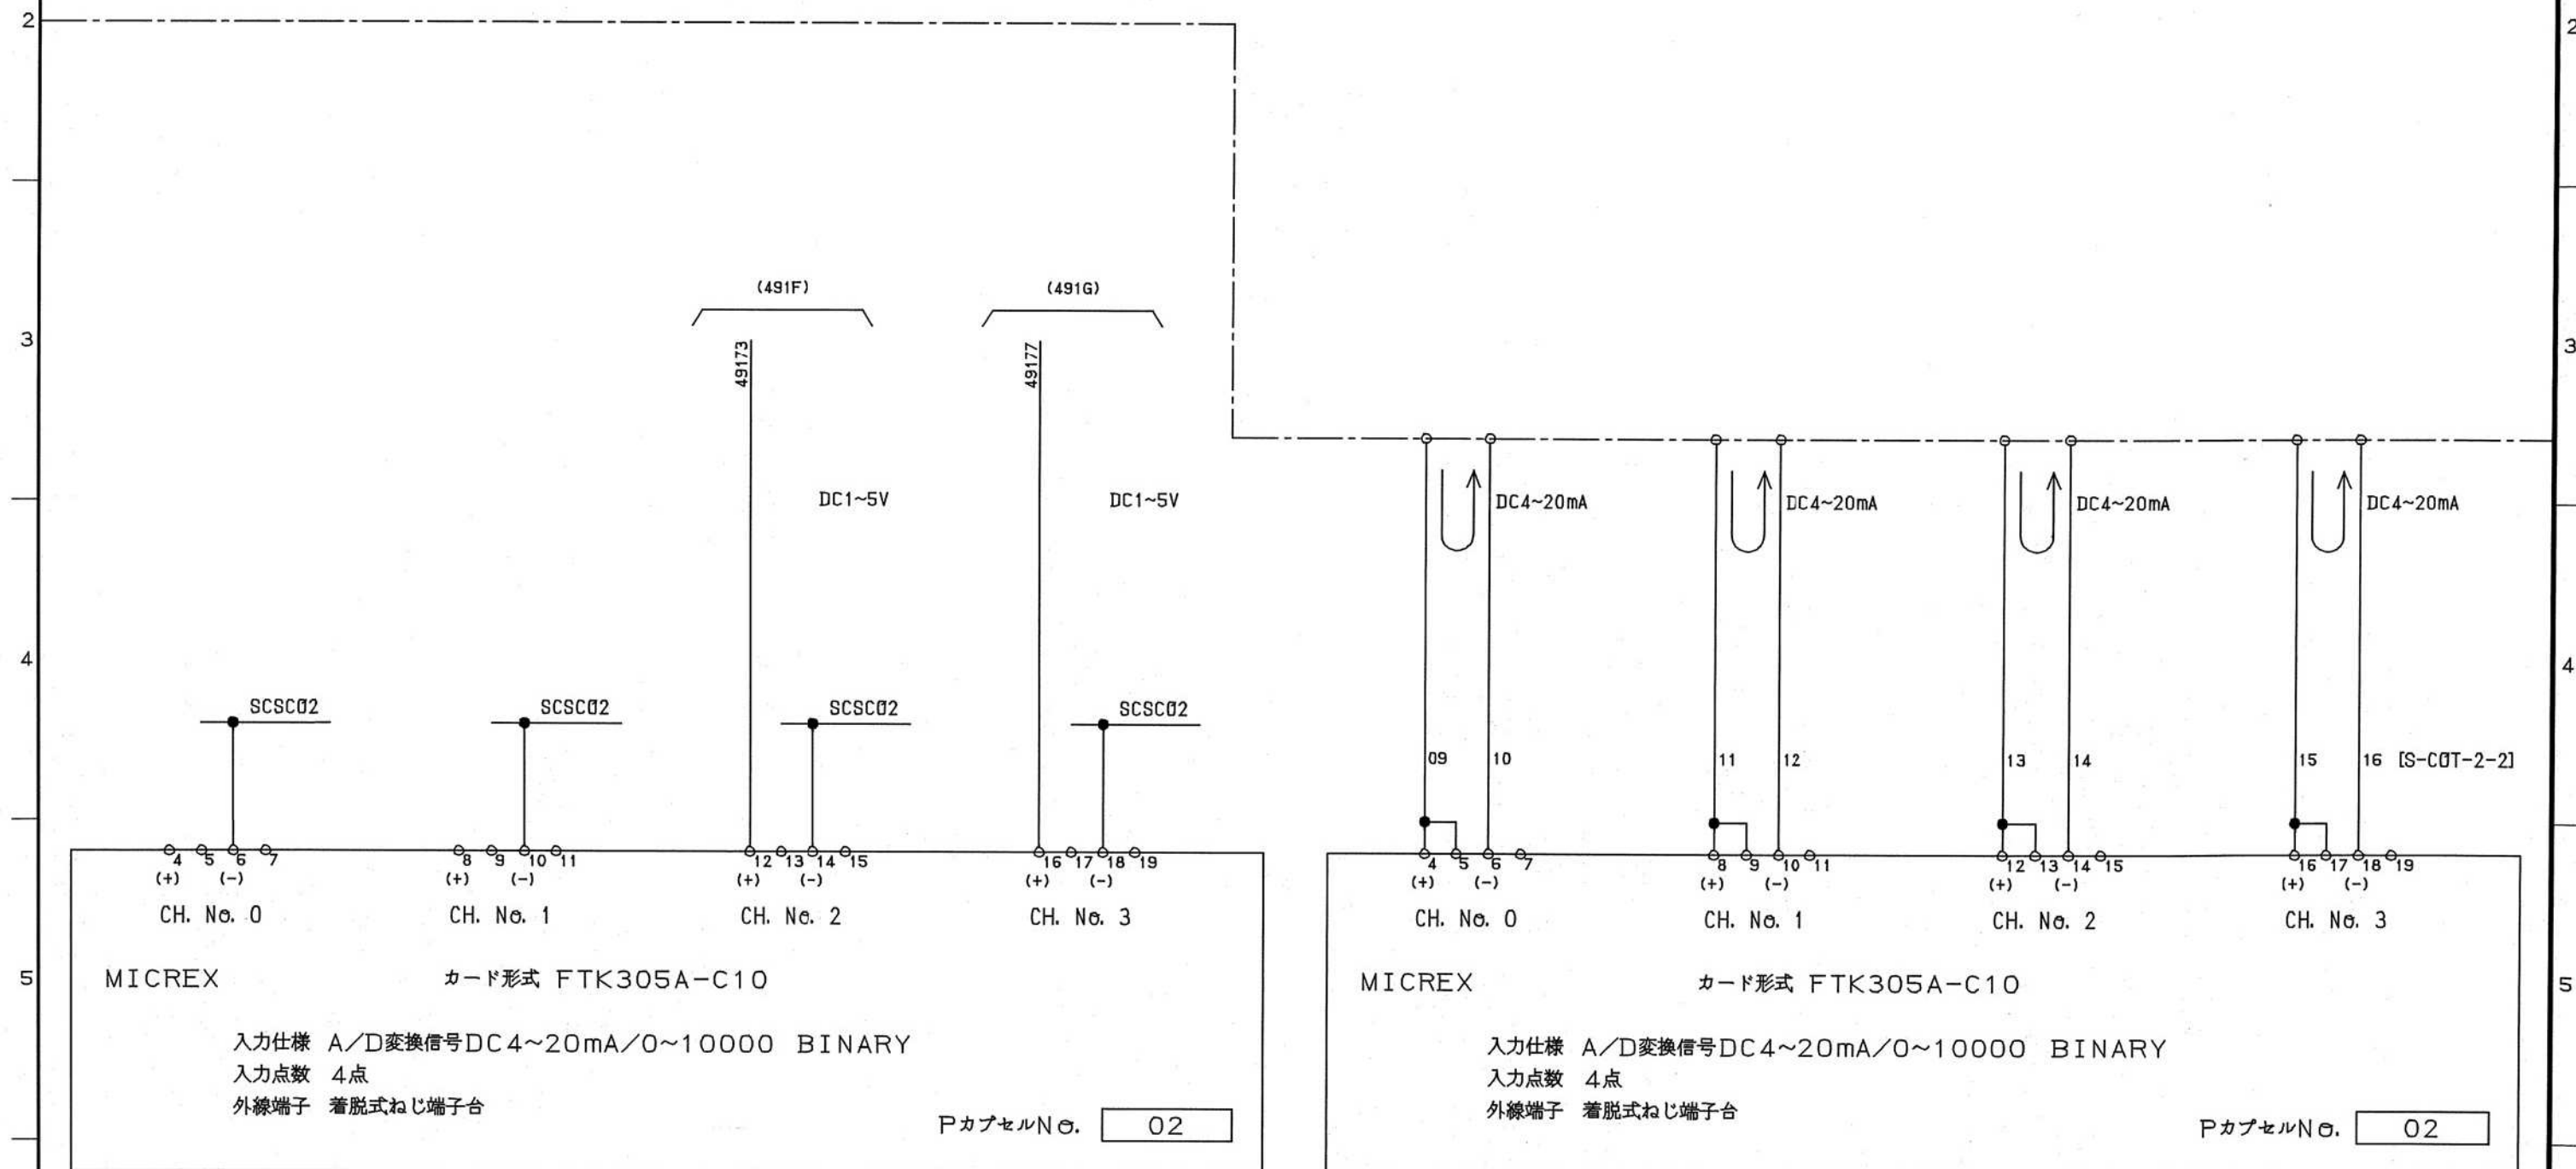

① 取合追加		'20-01-31 八尋		M)現地試験フォロー '20-06-05 八尋		(579~590欠)									
Revisions	② 現地試験フォロー	'01-06-15 折茂	Date	Name	Fuji Electric Co.,Ltd.	管理管轄入出力制御装置	W426297	591	シ ジ ミ P						
	③ 信号追加	'00-11-09 折茂	Drawn	2000-04-24 森竹											
	④ 信号削除	'00-08-21 野崎	Checked												
	⑤ C18905による改造	'04-12-03 森竹													
A		B		C		D		E		F		G		H	

アドレス	CH. NO.	項目名称	備考
WB0116	00	予備	
WB0117	01	予備	
WB0118	02	予備	
WB0119	03	予備	
WB0120			CH.00 ステータス情報
WB0121			CH.01 ステータス情報
WB0122			CH.02 ステータス情報
WB0123			CH.03 ステータス情報



アドレス	CH. NO.	項目名称	備考
WB0124	00	予備	
WB0125	01	予備	
WB0126	02	予備	
WB0127	03	予備	
WB0128			CH.00 ステータス情報
WB0129			CH.01 ステータス情報
WB0130			CH.02 ステータス情報
WB0131			CH.03 ステータス情報

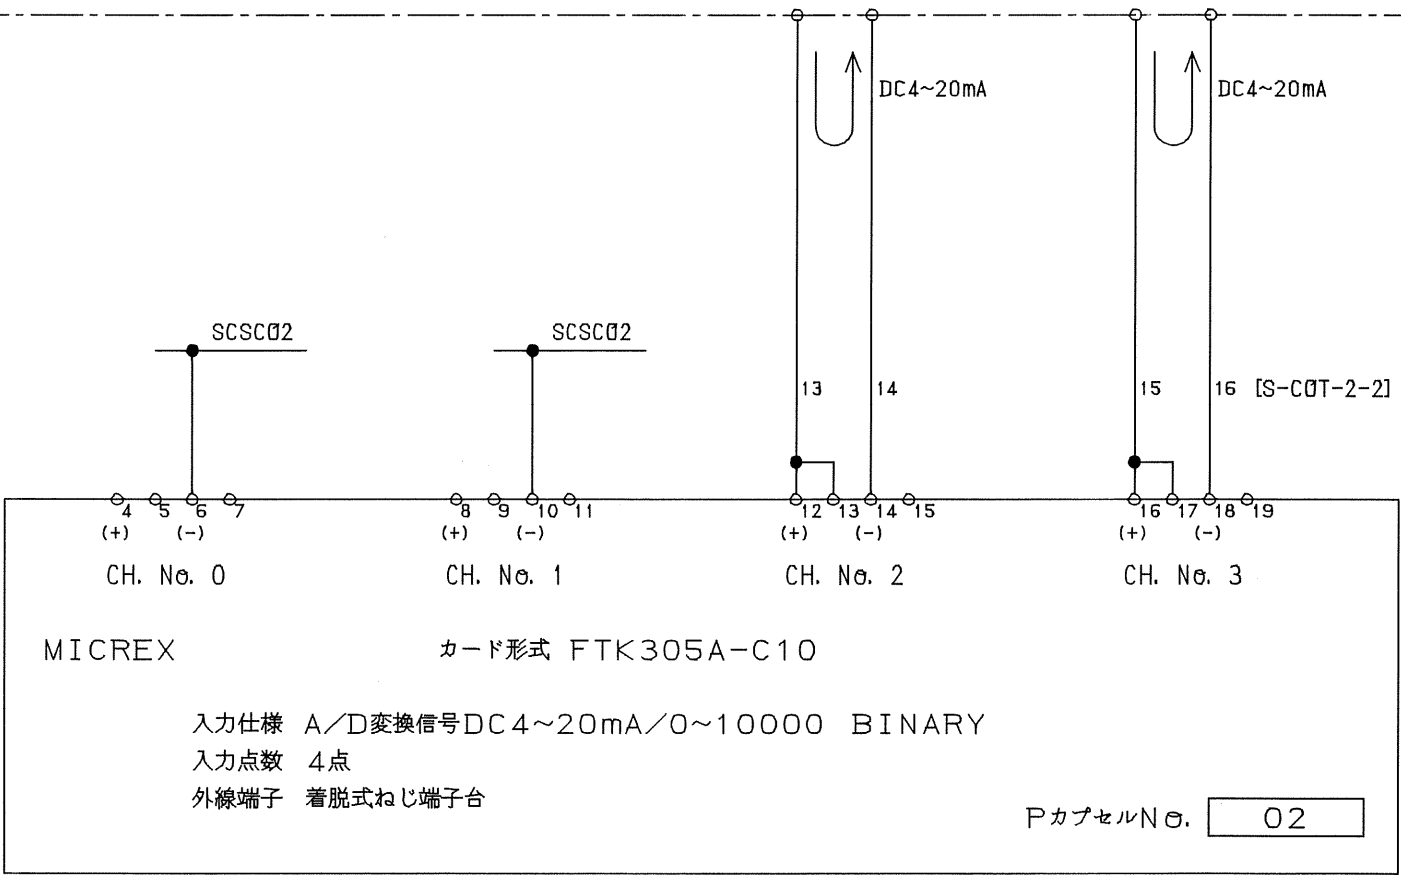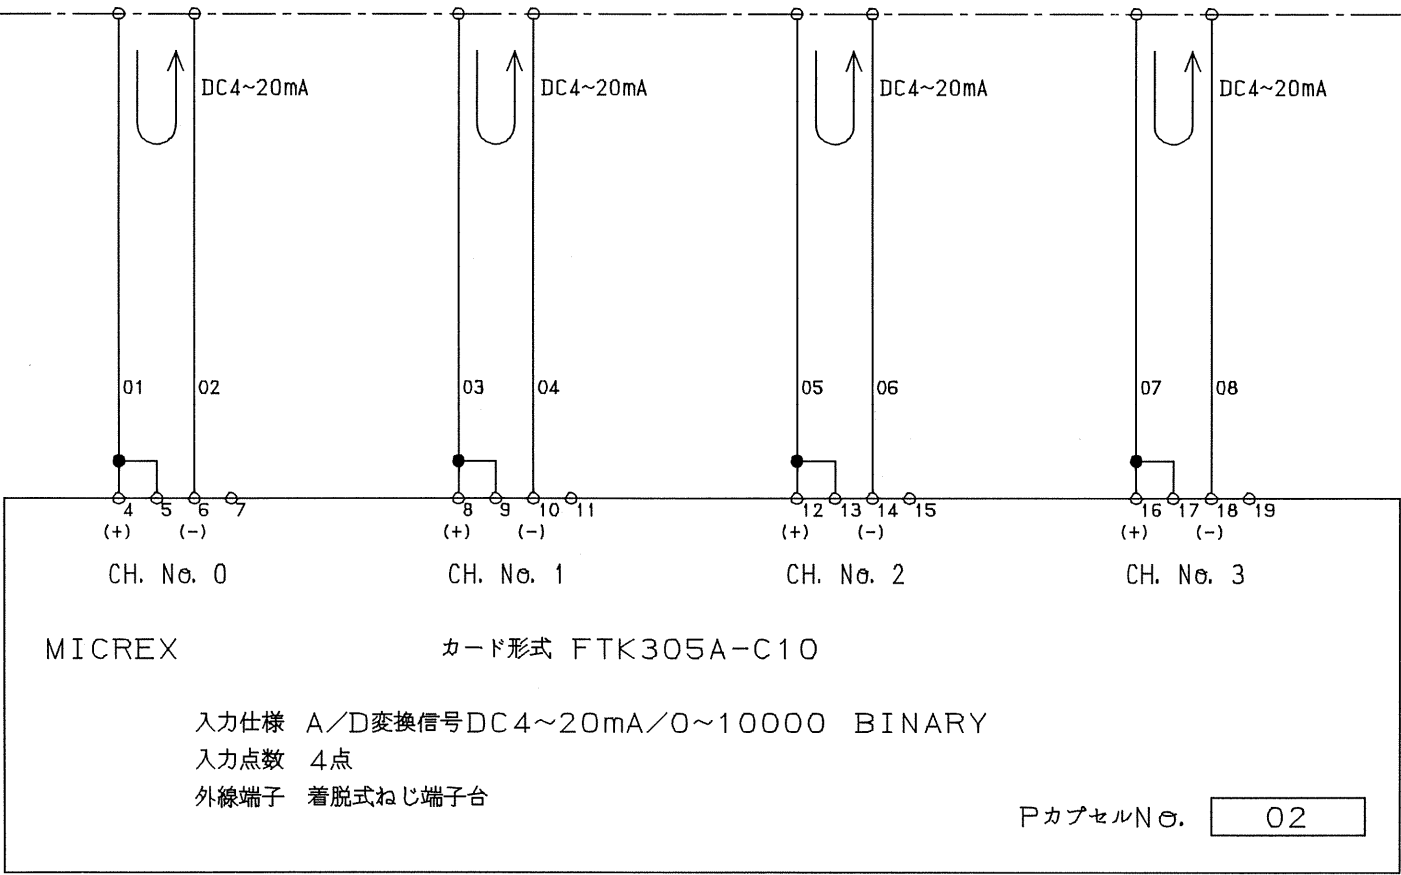

Revisions	①	現地試験フォロー	' 01-06-15	折茂		Date	Name	Fuji Electric Co.,Ltd.	Title	管理管轄入出力制御装置 インターフェース回路	Ref. Dwg No.	W426297	592	M/F AI(電流)2/1 CIFAI1KA	P
	②	信号削除	' 00-11-09	折茂	Drawn	2000-04-24	森竹								
	③	信号削除	' 00-08-21	野崎	Checked										
	④	本頁追加(P.533を書換え)	' 00-04-24	森竹											
A		B		C		D		E		F		G		H	

アドレス	CH. NO.	項目名称	備考
WB0132	00	予備	
WB0133	01	予備	
WB0134	02	予備	
WB0135	03	予備	
WB0136			CH.00 ステータス情報
WB0137			CH.01 ステータス情報
WB0138			CH.02 ステータス情報
WB0139			CH.03 ステータス情報

アドレス	CH. NO.	項目名称	備考
WB0140	00	予備	
WB0141	01	予備	
WB0142	02	予備	
WB0143	03	予備	
WB0144			CH.00 ステータス情報
WB0145			CH.01 ステータス情報
WB0146			CH.02 ステータス情報
WB0147			CH.03 ステータス情報

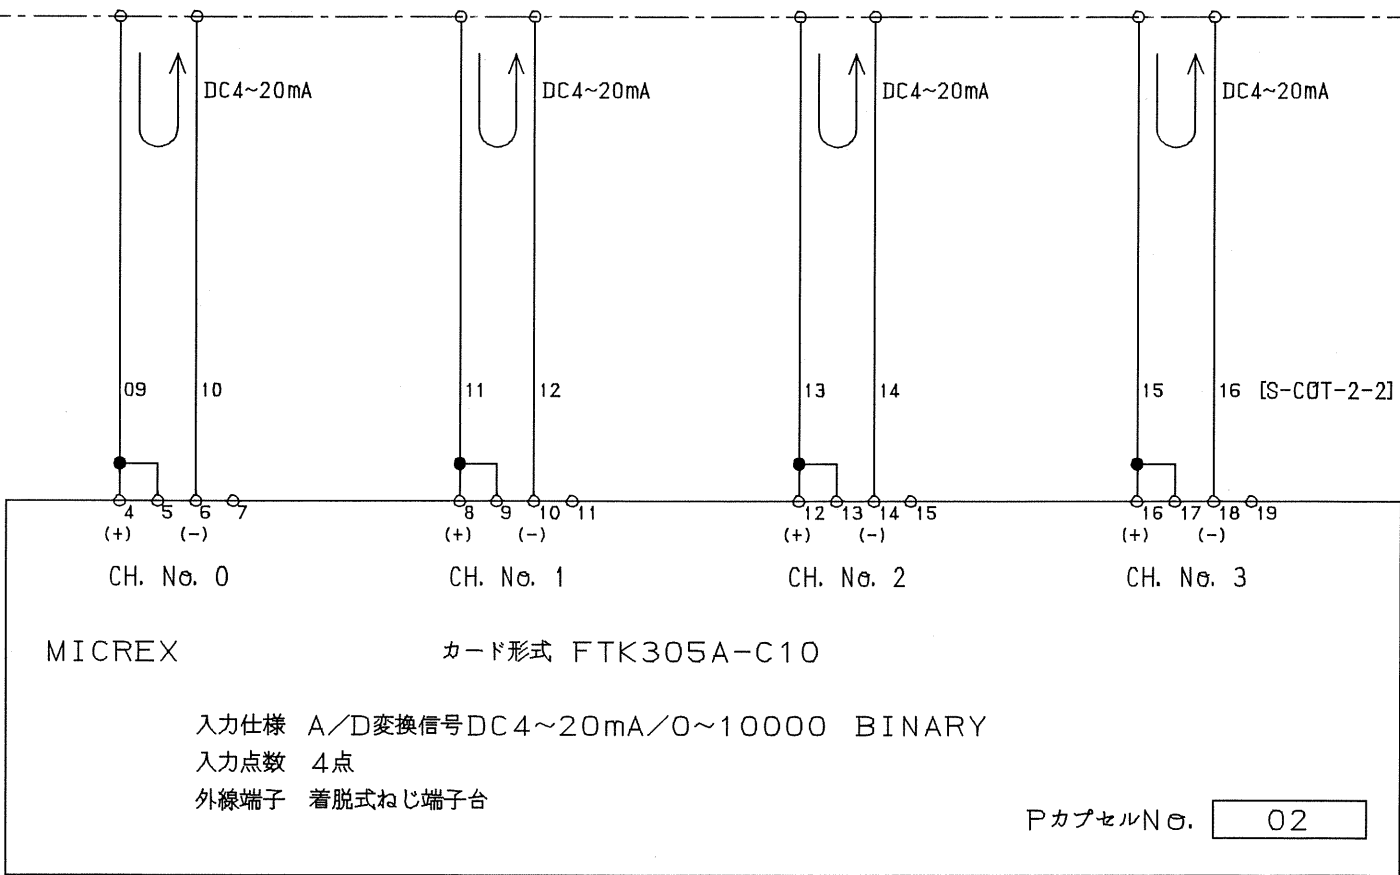
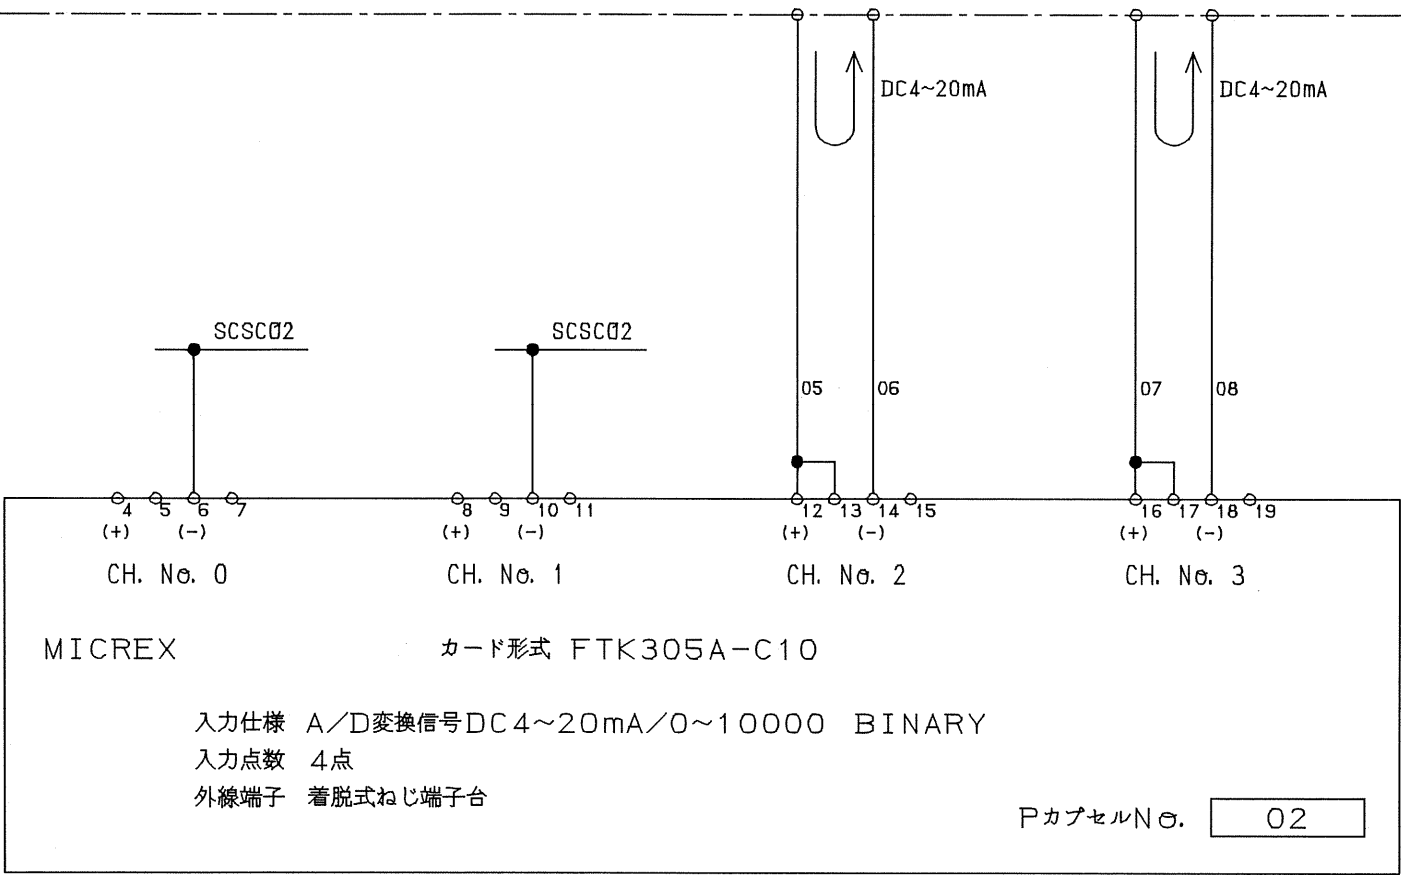


Revisions	○			Date	Name	Fuji Electric Co.,Ltd.	Title	管理管轄入出力制御装置 インターフェース回路	Rev. Dwg. No.	W426297	593	M/F AI(電流)2/1 CIFAI IKA	P		
	Ⓐ	現地試験フォロー	' 01-06-15	折茂	Drawn									2000-04-24	森竹
	Ⓘ	信号削除	' 00-08-21	野崎	Checked										
	Ⓕ	本頁追加(P.534を書換え)	' 00-04-24	森竹											
A		B		C		D		E		F		G		H	

アドレス	CH. NO.	項目名称	備考
WB0148	00	予備	
WB0149	01	予備	
WB0150	02	予備	
WB0151	03	予備	
WB0152			CH.00 ステータス情報
WB0153			CH.01 ステータス情報
WB0154			CH.02 ステータス情報
WB0155			CH.03 ステータス情報

アドレス	CH. NO.	項目名称	備考
WB0156	00	田上ポンプ所 受電電圧	
WB0157	01	田上ポンプ所 受電電流	
WB0158	02	田上ポンプ所 送水圧力	
WB0159	03	田上ポンプ所 吸込圧力	
WB0160			CH.00 ステータス情報
WB0161			CH.01 ステータス情報
WB0162			CH.02 ステータス情報
WB0163			CH.03 ステータス情報

[遠方監視制御装置盤(田上ポンプ所)] FTE439913

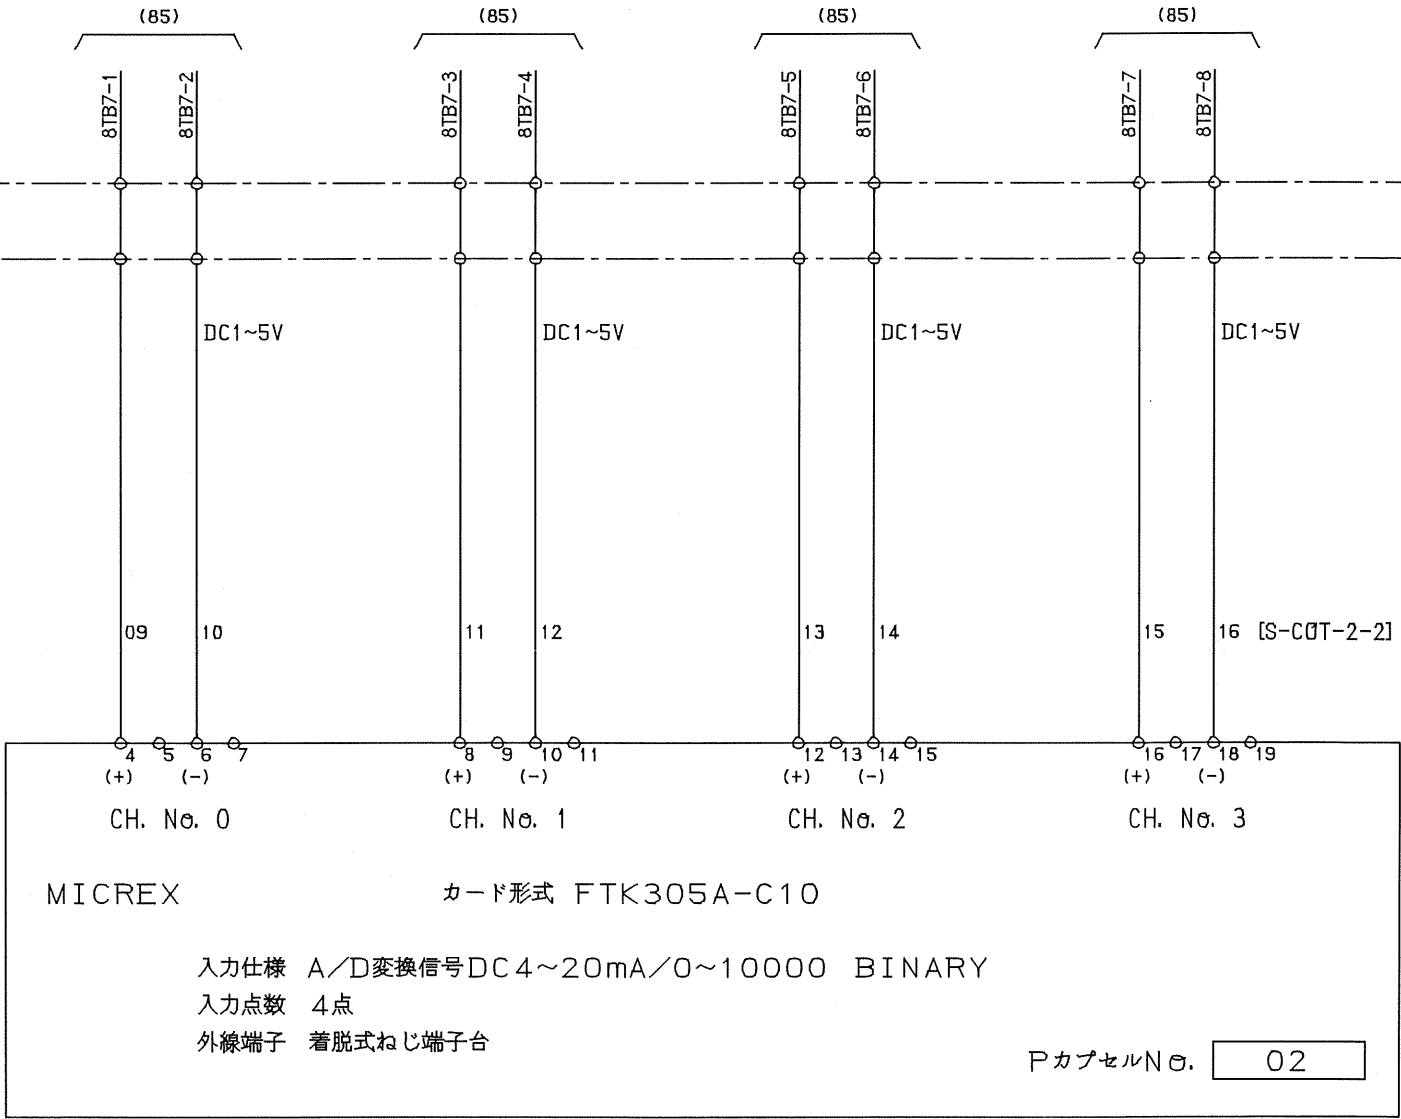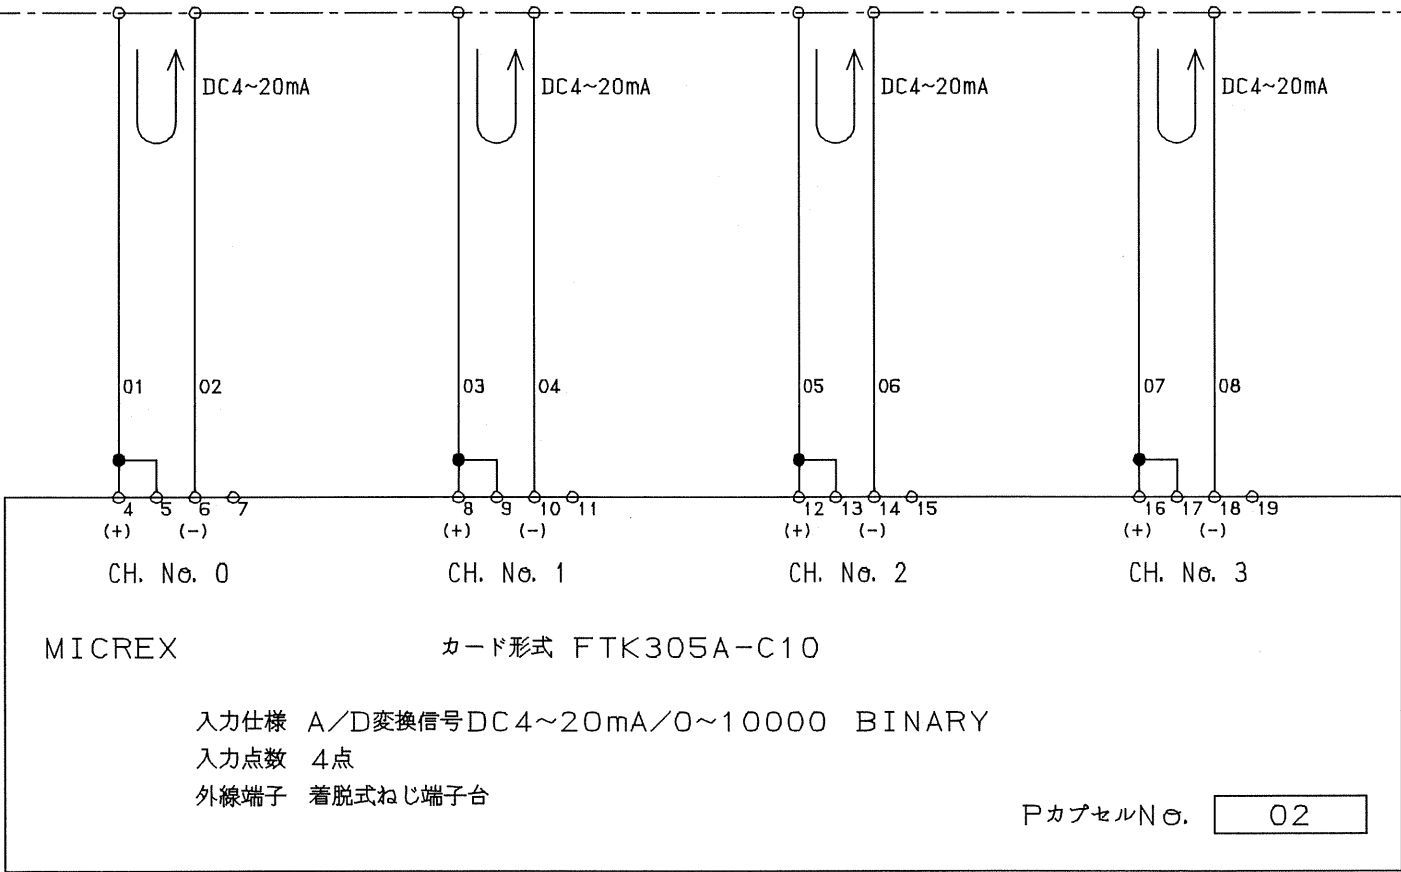

Revisions	○			Date	Name	Fuji Electric Co., Ltd.	Title	管理管轄入出力制御装置 インターフェース回路	Ref. Dwg. No.	W426297	594	f i p			
	②	現地試験フォロー	' 01-06-15	折茂	Drawn								2000-04-24	森竹	
	①	信号削除、取合いフォロー	' 00-08-21	野崎	Checked										
	③	本頁追加 (P.535を書換え)	' 00-04-24	森竹											
A		B		C		D		E		F		G		H	

データロガー室VCF盤(1)
[S-D-1]
AC100V 60Hz
(152E)

a	AL	a1
b	c1	AL
		b1

a	AX	a1	621E
b	c1	AX	b1
		a1	
		c1	
		a1	
		b1	

a	AL	a1	G
b	c1	AL	b1
		a1	
		c1	
		a1	
		b1	

a	AL	a1	G
b	c1	AL	b1
		a1	
		c1	
		a1	
		b1	

a	11	G
b	12	

R7D2S11
T7D2S11

52SC031
<13013>
SA32B/10K

RSC031
TSC031


52SC032
<13015B>
SA32B/5K

RSC032
TSC032

F-150S用電源
約 180VA

52SC033
<13015>
SA32B/5K

RSC033
TSC033

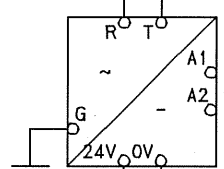


APSSC031
<13051>
APSN-A-200
200W 出力

32SC031
<13016>
CP32FM/5K


PSC031
NSC031

制御用電源

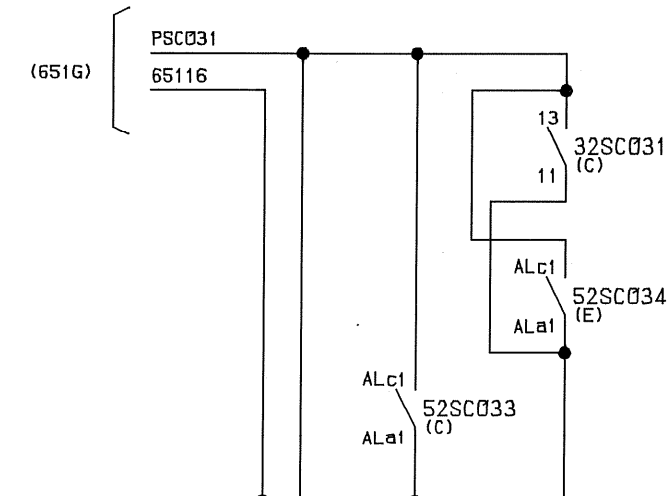

52SC034
<13018>
SA32B/10K

RSC034
TSC034

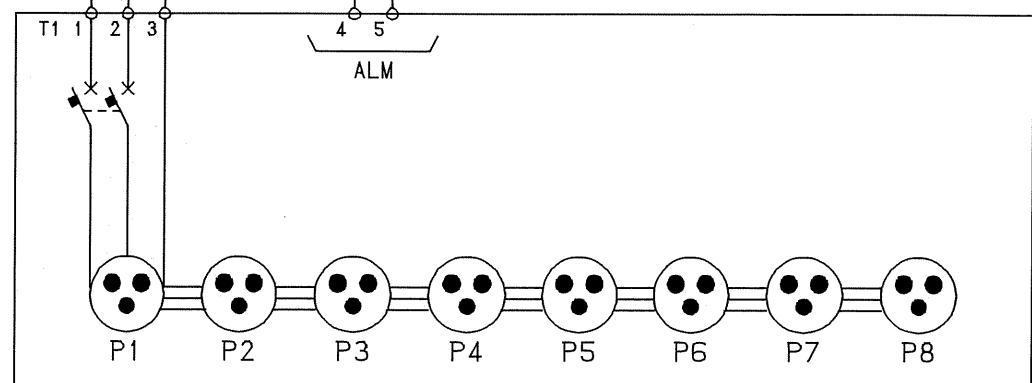

PDUSC031
<13020>
PDU-6

ルータ用電源 約 400W
リピータハブ (1) 用電源
リピータハブ (2) 用電源
ACS用電源
FICアダプタ用電源
予備
予備
予備

[S-C0T-3]


Revisions		Date	Name
◎	取合い追加	01-05-09	折茂
①	ACS用電源取り出し	01-03-21	折茂
①	取合いフォロー	00-08-21	野崎
◎	ブレーカトリップ値変更、一部削除	00-06-08	河野

Fuji Electric Co., Ltd.

浄水場間入出力制御装置
電源回路


W426297
601
g
i
n
o

(596~600欠)

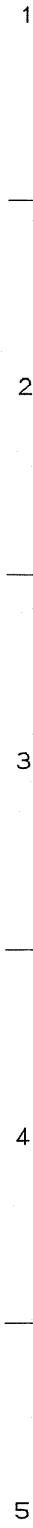


(617~620欠)


P) 現地試験フォロー ' 01-06-15 折茂

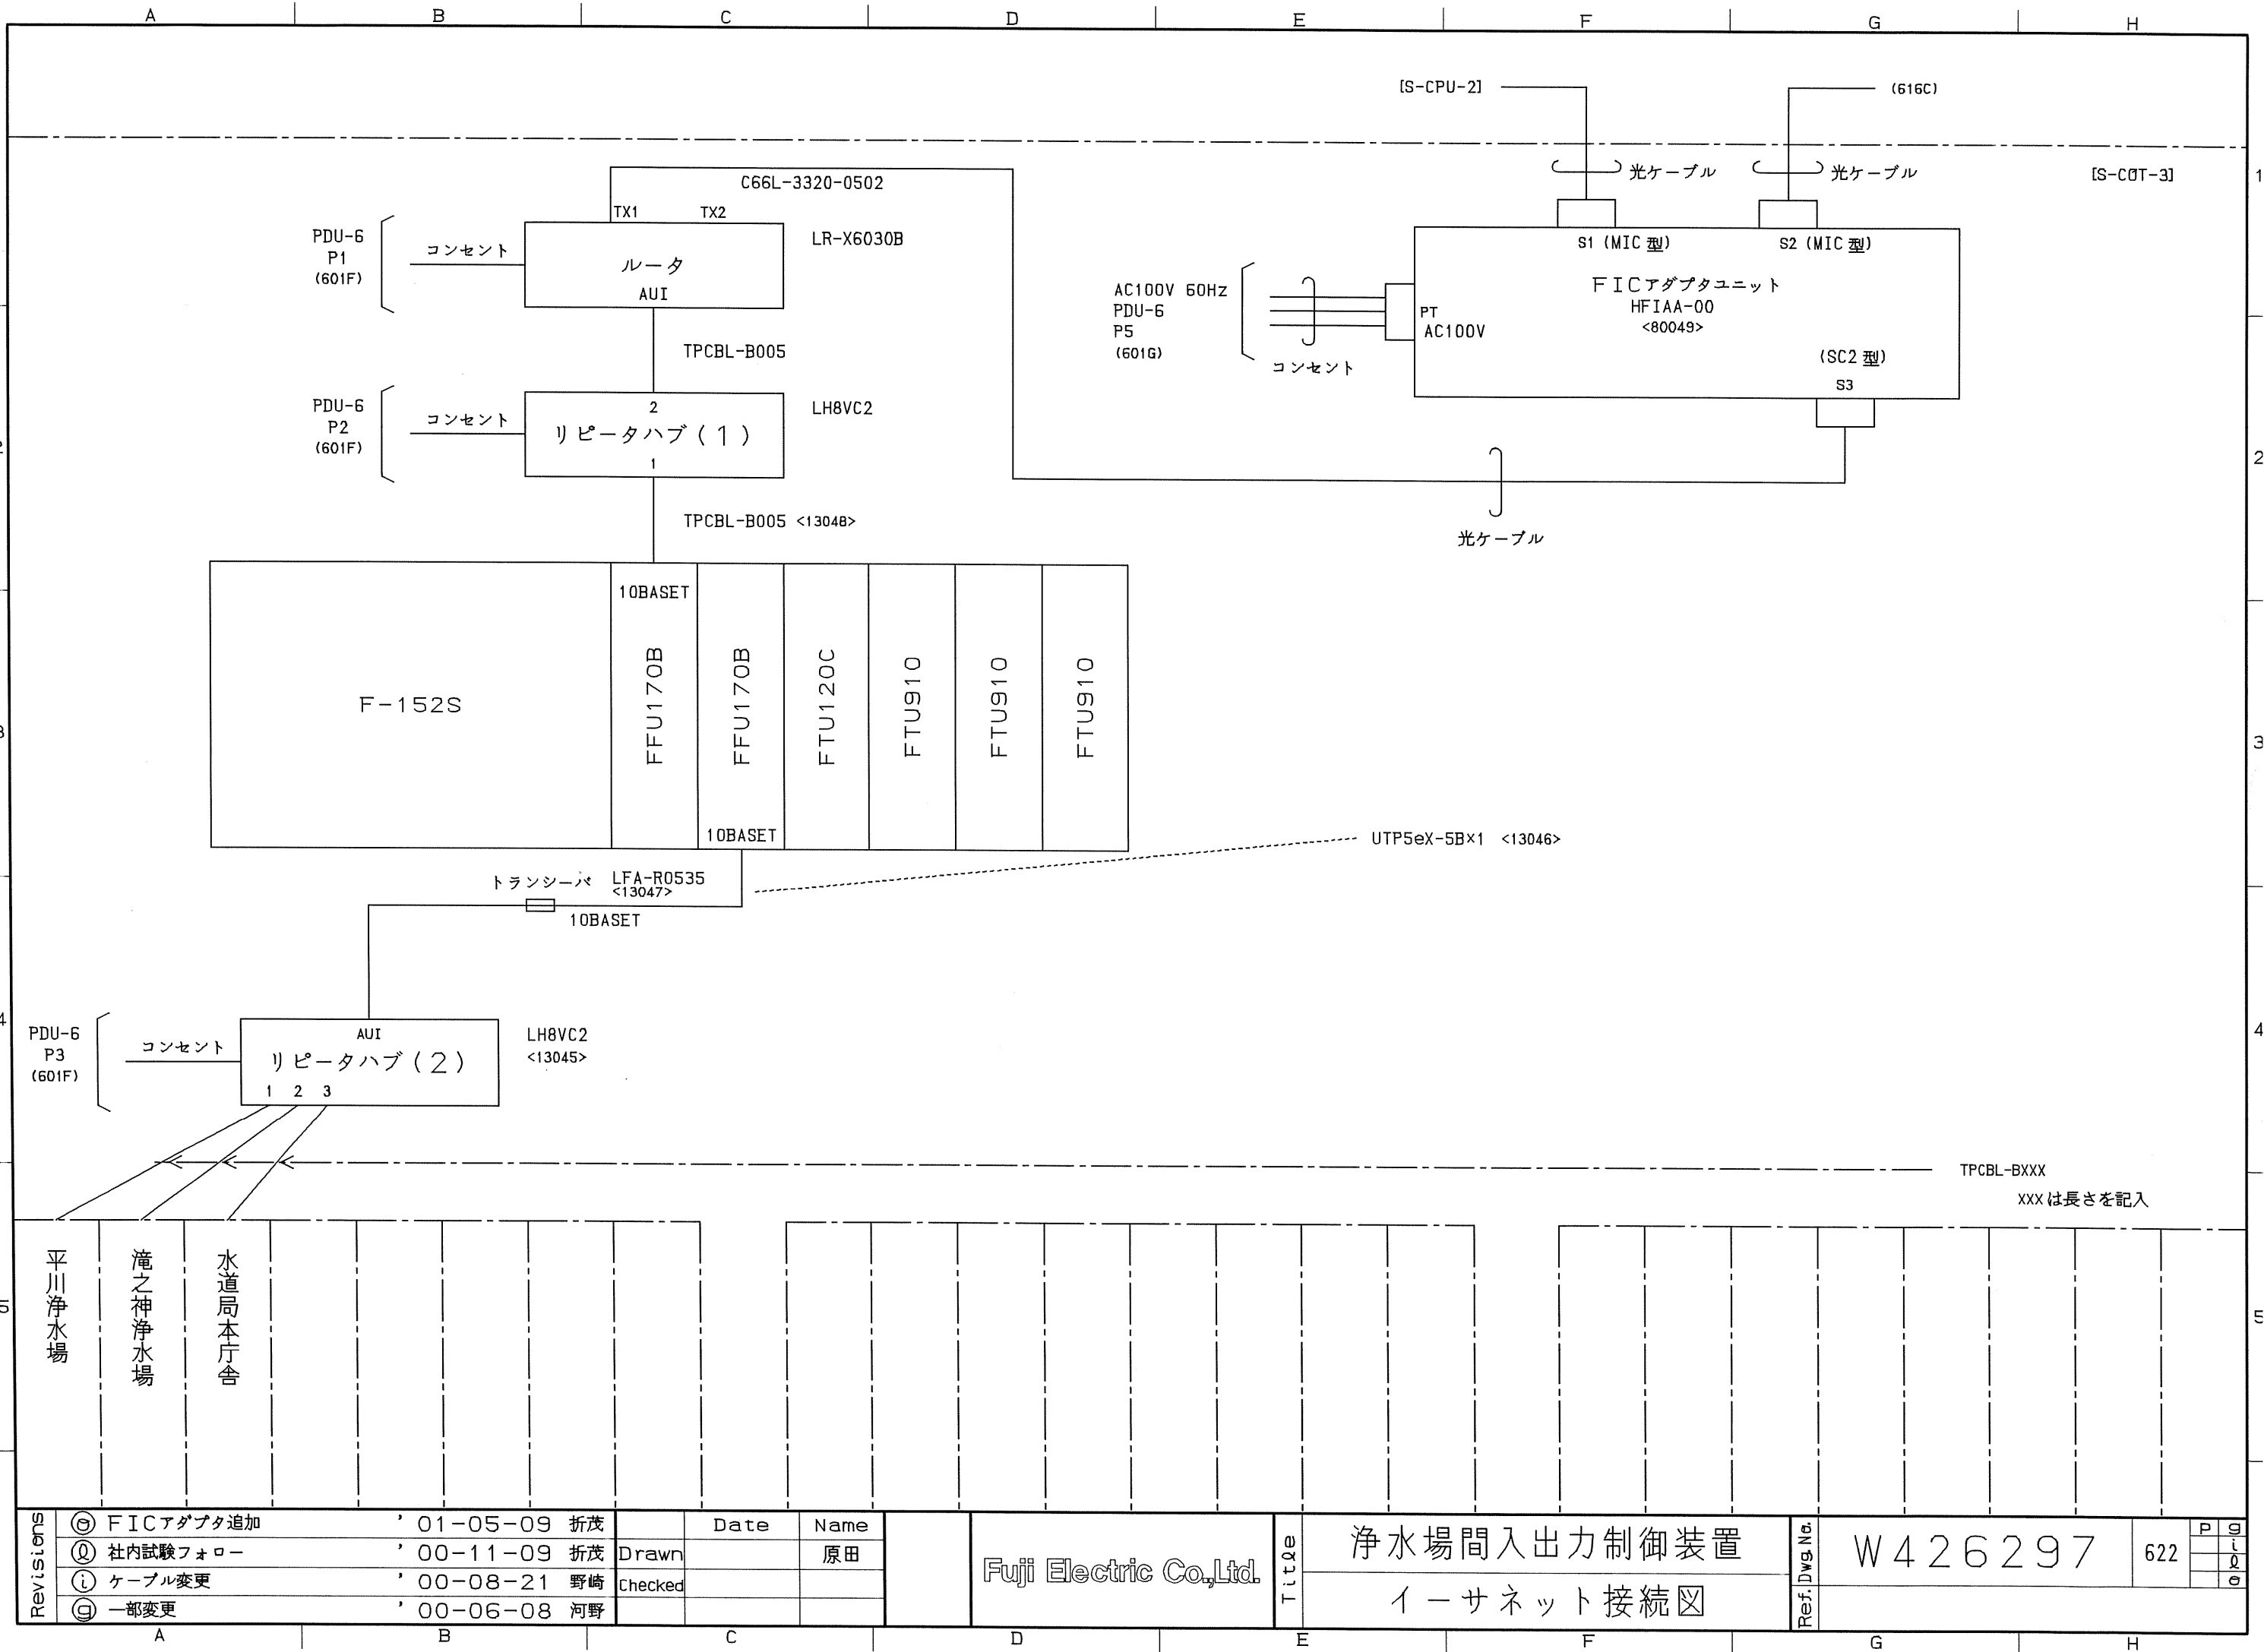

イーサネットモジュールFFU170B (F120Sシリーズ)

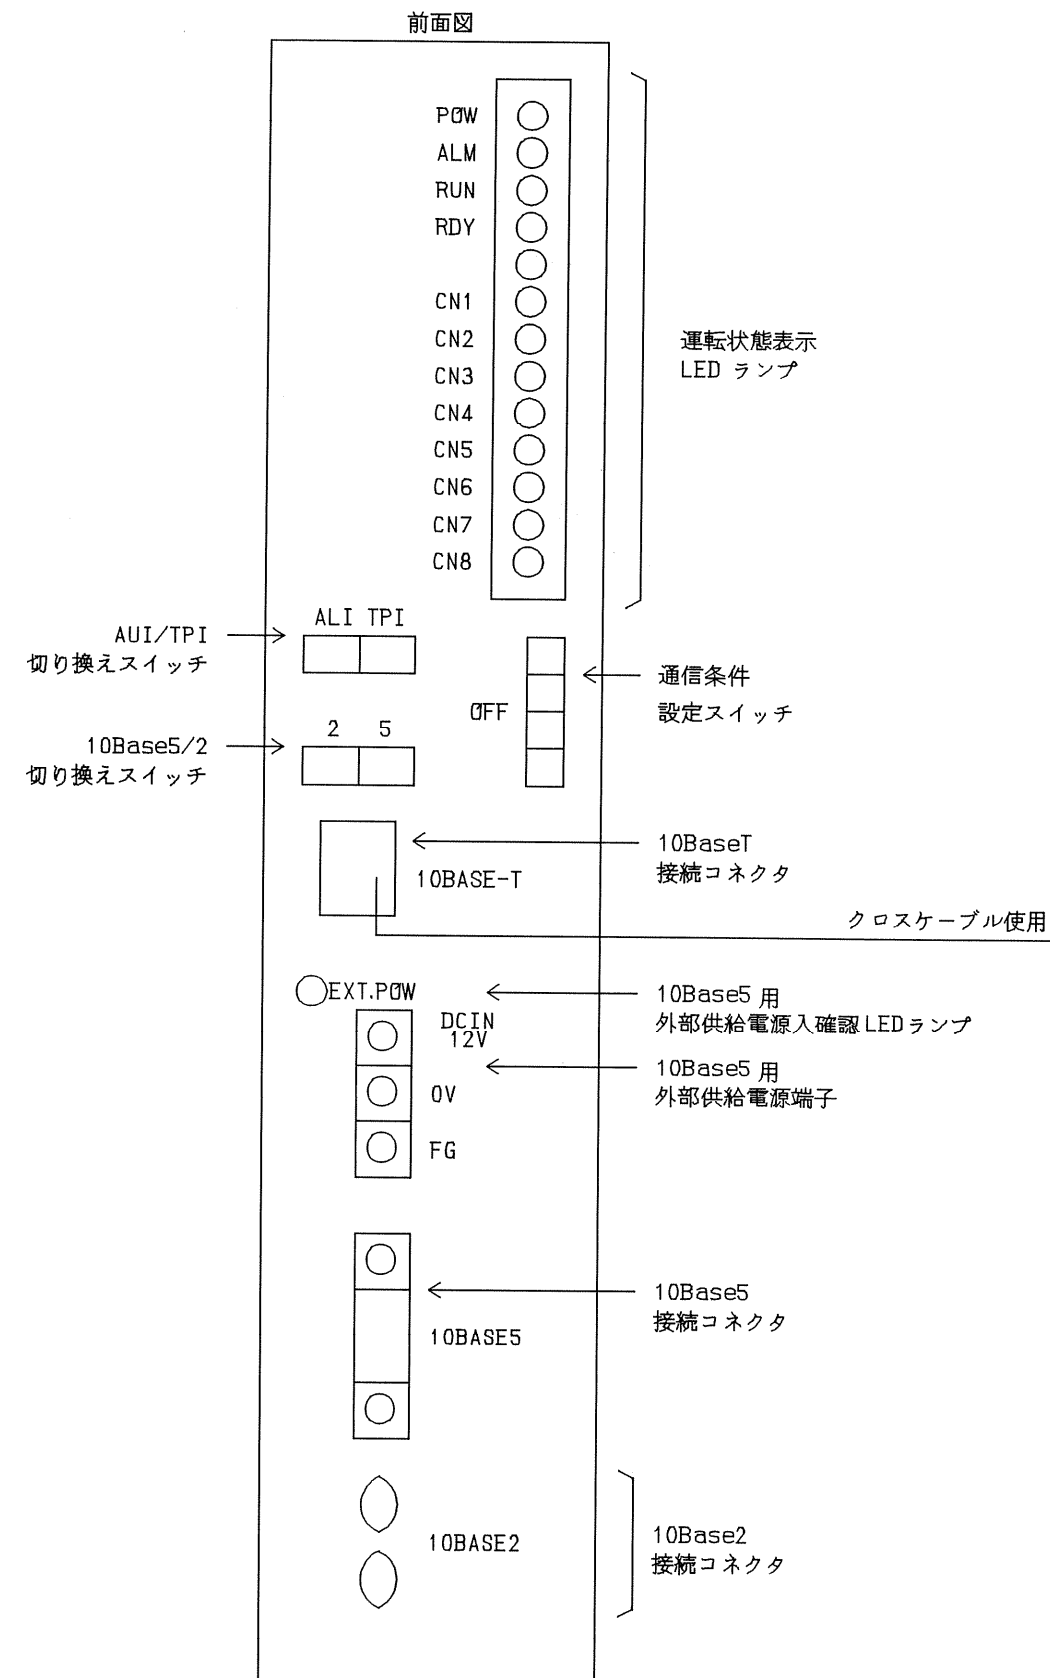

※ 裏面にあるIPアドレス設定S・WをC8に設定




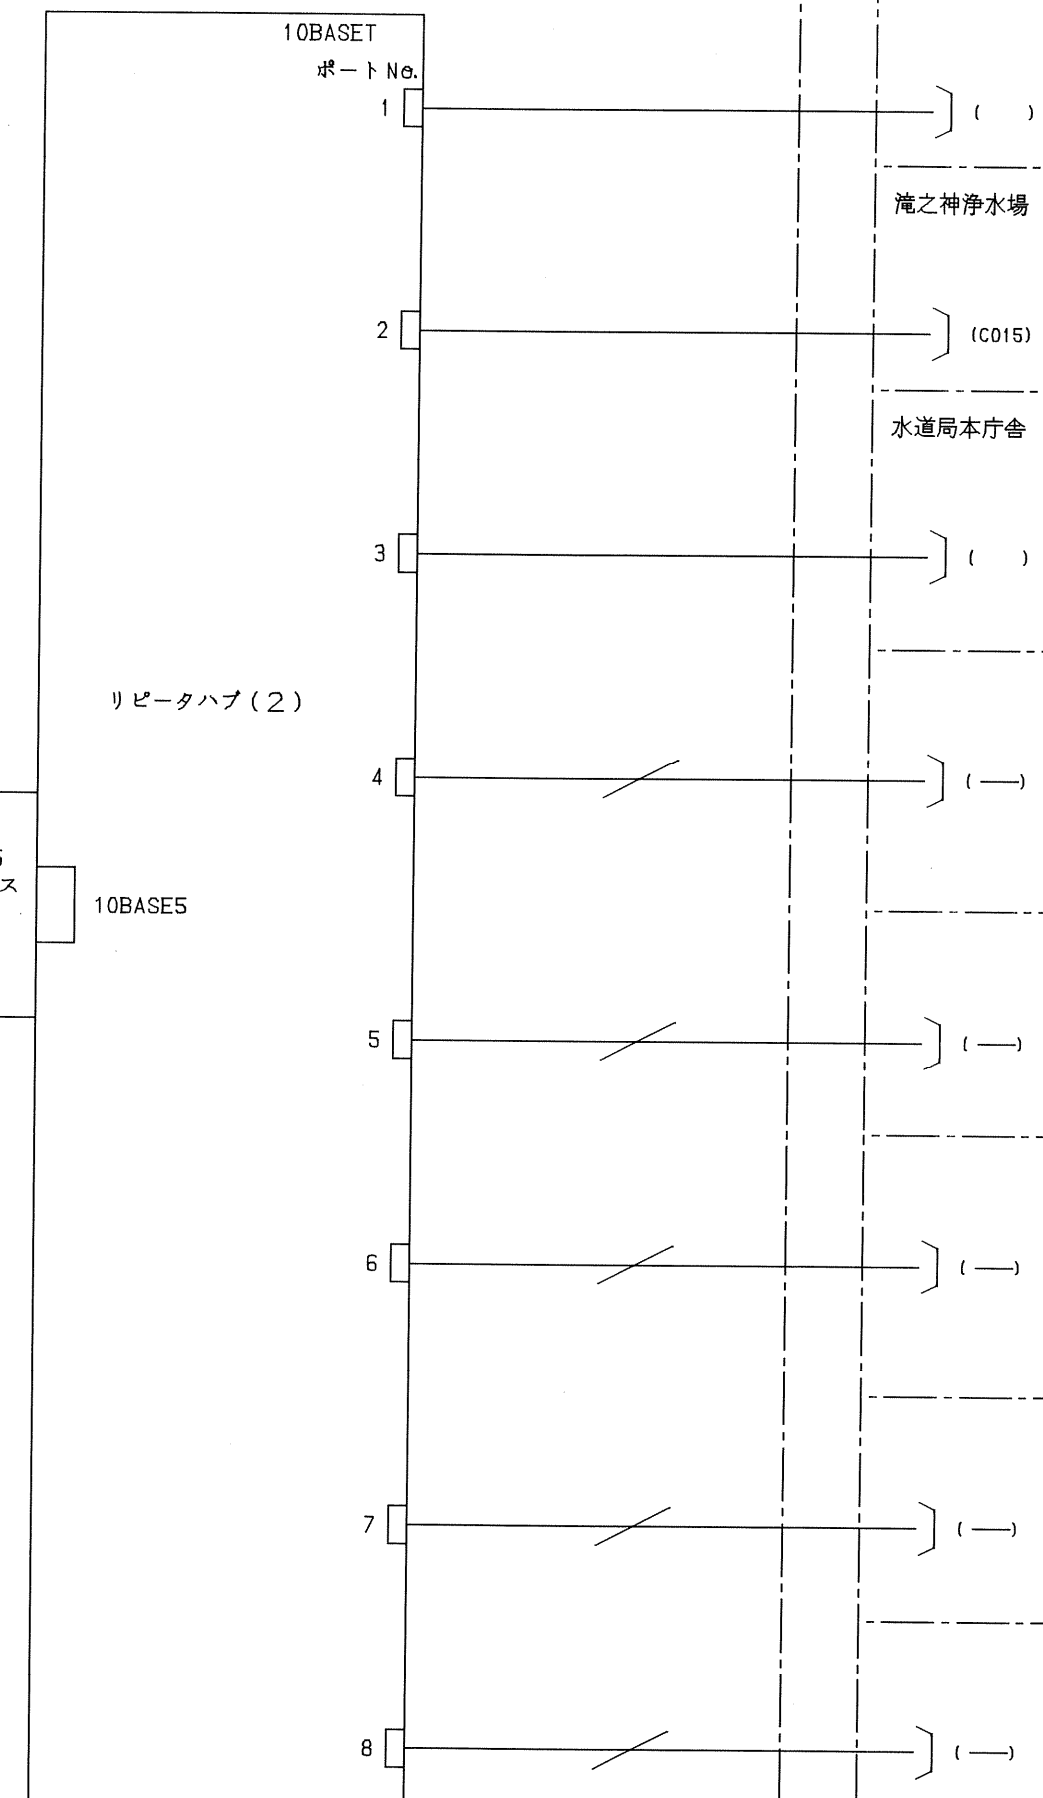


Revisions	○			Date	Name
	○			Drawn	2000-04-24 森竹
	①	IPアドレス変更	' 00-08-21 野崎	Checked	
	②	本頁追加	' 00-04-24 森竹		



Fuji Electric Co., Ltd.

浄水場間入出力制御装置
イーサネット接続図


Ref. Dwg. No.	W 4 2 6 2 9 7	623	f
			i

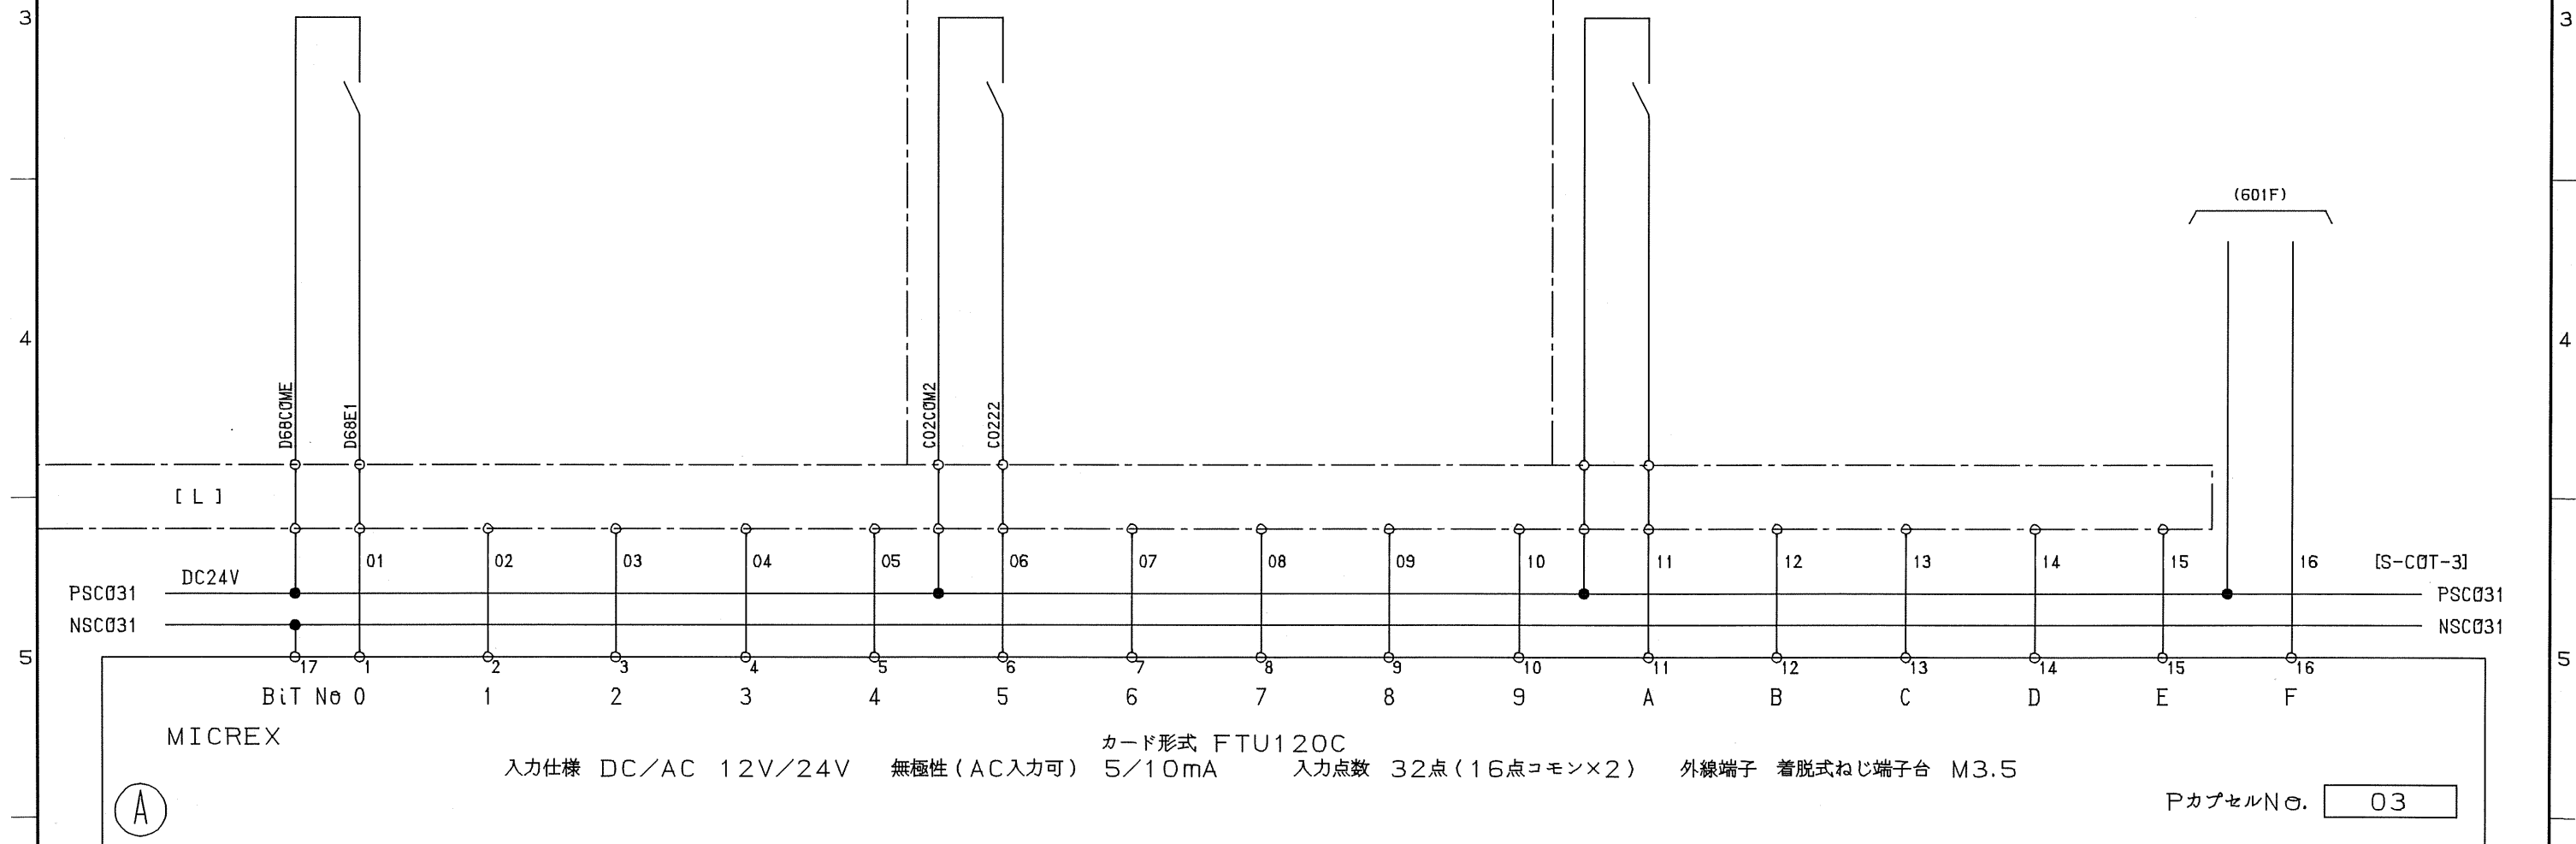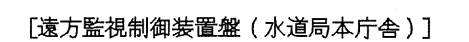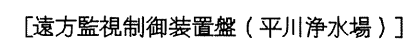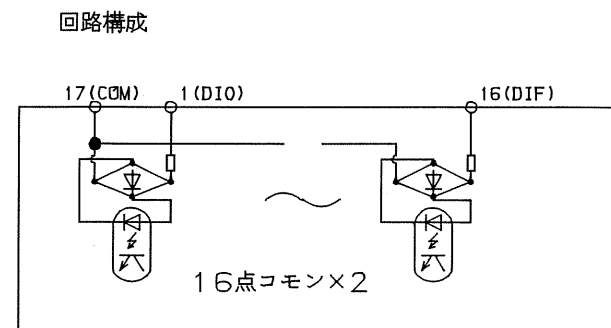

Revisions	○			Date	Name	Fuji Electric Co., Ltd.	Title	浄水場間入出力制御装置 インターフェース回路	Ref. Dwg. No.	W 4 2 6 2 9 7		651	P I P
	⑤	現地試験フォロー	' 01-06-15	折茂	Drawn					2000-04-24	森竹	M/F DI (ユニット・端子) 1/2 CIFDICUA	
	④	信号削除、追加 (1点)	' 00-08-21	野崎	Checked								
	③	本頁追加	' 00-04-24	森竹									

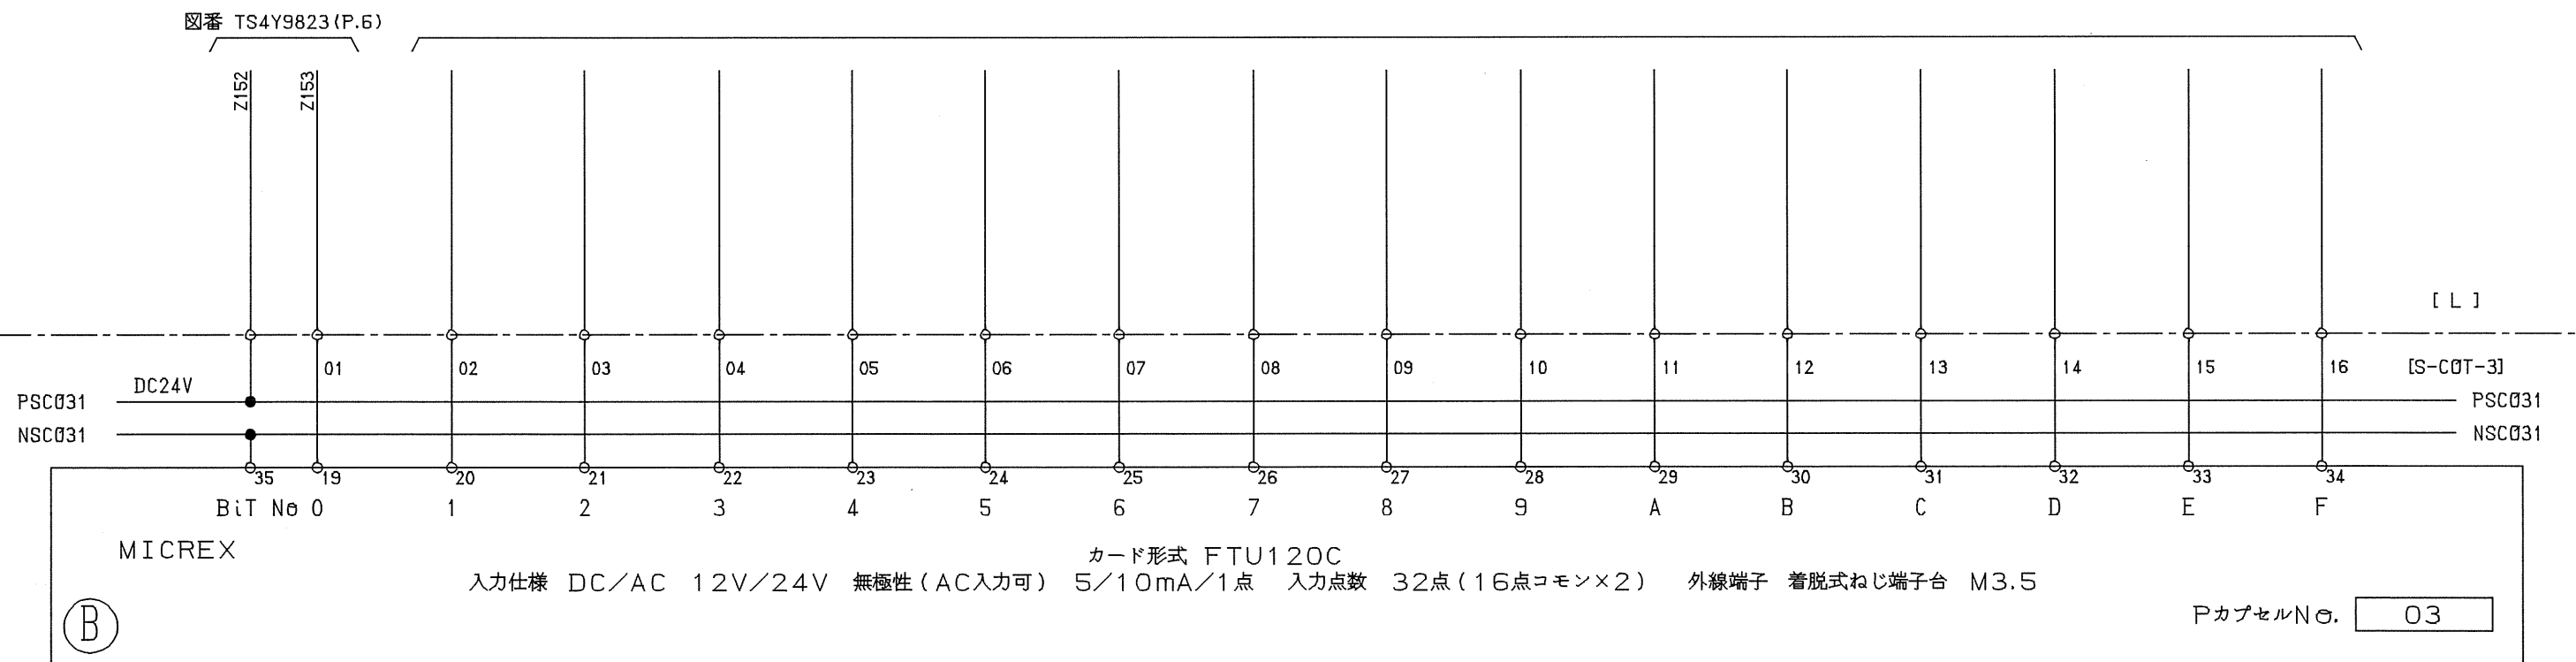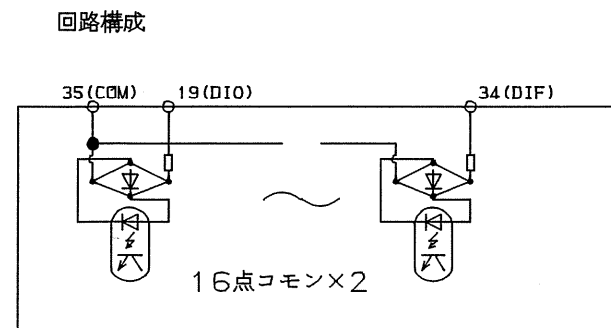

[S-TB-1]
[場外系中継端子盤]

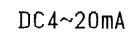

[L]


Revisions	○			Date	Name
	Ⓐ	現地試験フォロー	' 01-06-15 折茂	Drawn	2000-04-24 森竹
	Ⓑ	I/F修正	' 00-09-20 折茂	Checked	
	Ⓒ	行先変更	' 00-06-08 河野		

Title

Ref.	Dwg.No.
------	---------

21

[illegible]

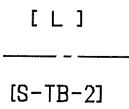

Revisions	○			Date	Name	Fuji Electric Co.,Ltd.	Title	甲系ろ過池操作室中継端子盤 雑電源回路	Ref. Dwg. No.	(722~760x)					
	○		Drawn		河野					W 4 2 6 2 9 7	761	a i			
	① 取合いフォロー		00-08-21	野崎	Checked										
	② 本頁追加		00-01-13	河野											
	A		B		C								D		E

