[L]

[S-D-2]

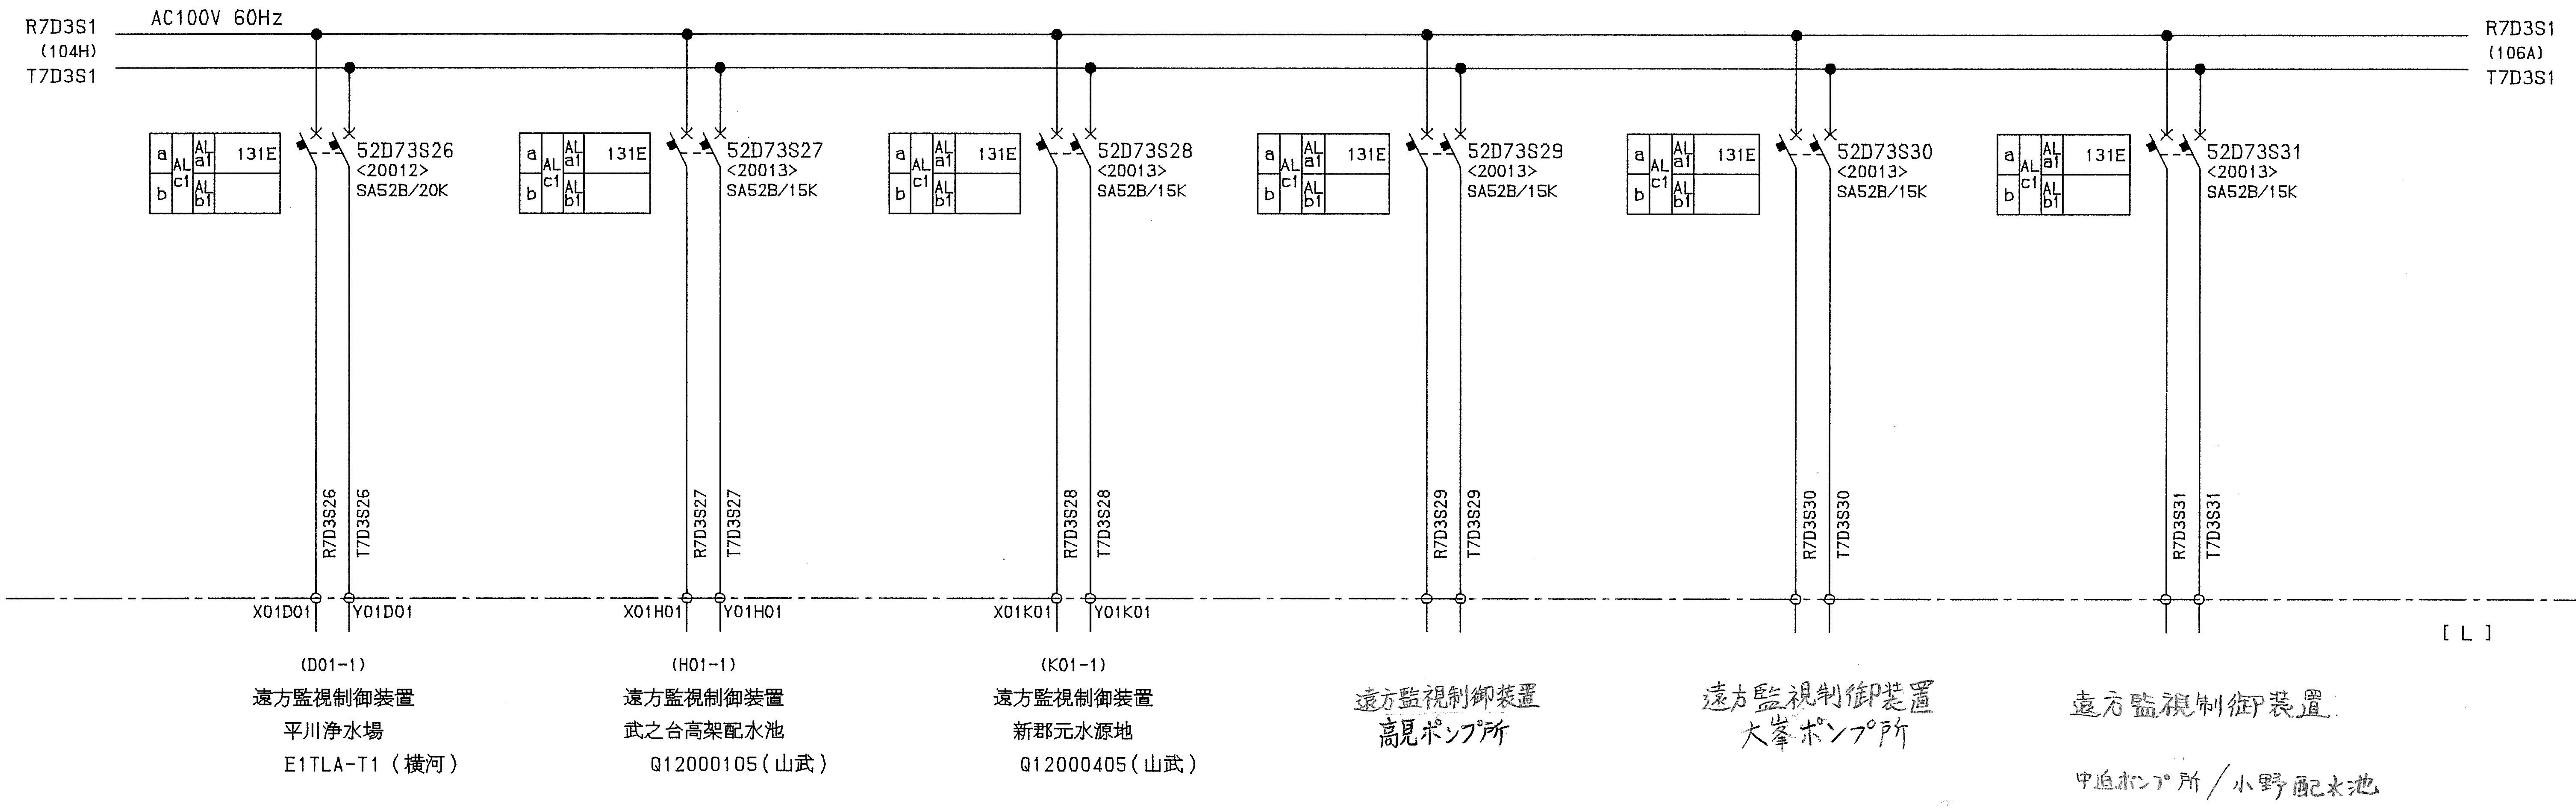
R7D3S1
(104H)
T7D3S1
AC100V 60Hz
R7D3S1
(106A)
T7D3S1
a
b
AL c1
AL a1
AL b1
131E
52D73S26
<20012>
SA52B/20K
52D73S27
<20013>
SA52B/15K
52D73S28
<20013>
SA52B/15K
52D73S29
<20013>
SA52B/15K
52D73S30
<20013>
SA52B/15K
52D73S31
<20013>
SA52B/15K
R7D3S26
T7D3S26
R7D3S27
T7D3S27
R7D3S28
T7D3S28
R7D3S29
T7D3S29
R7D3S30
T7D3S30
R7D3S31
T7D3S31
X01D01
Y01D01
X01H01
Y01H01
X01K01
Y01K01
[L]
(D01-1)
遠方監視制御装置
平川浄水場
E1TLA-T1（横河）
(H01-1)
遠方監視制御装置
武之台高架配水池
Q12000105(山武)
(K01-1)
遠方監視制御装置
新郡元水源地
Q12000405(山武)
遠方監視制御装置
高見ポンプ所
遠方監視制御装置
大峯ポンプ所
遠方監視制御装置
中追ポンプ所／小野配水池

Revisions			
ⓨ C18905による改造	'04-12-03	森竹
ⓟ 現地試験フォロー	'01-06-15	折茂
ⓒ TM追加	'10-02-22	河野
ろ 取合い追加	'05-11-07	大城

	Date	Name
Drawn	2000-06-08	河野
Checked		

Fuji Electric Co.,Ltd.

Title: データロガー室CVCF分電盤(2)
電源回路

Dwg.No. W426297 105
Ref.

ろ d
c o
p
y

[L]
[S-D-2]
R7D3S1
AC100V 60Hz
(105H)
T7D3S1
R7D3S1
(107A)
T7D3S1
a
b
AL c1
AL a1
AL b1
131E
52D73S32
<20013>
SA52B/15K
52D73S33
<20013>
SA52B/15K
52D73S34
<20013>
SA52B/15K
52D73S35
<20013>
SA52B/15K
52D73S36
<20013>
SA52B/15K
52D73S37
<20013>
SA52B/15K
R7D3S32
T7D3S32
R7D3S33
T7D3S33
R7D3S34
T7D3S34
R7D3S35
T7D3S35
R7D3S36
T7D3S36
R7D3S37
T7D3S37
[L]
遠方監視制御装置
中山ポンプ所
遠方監視制御装置
鷹ヶ峯第二配水池
遠方監視制御装置
皇徳寺ポンプ所
予備
予備
予備

Revisions			
○			
Ⓔ	TM追加	'11-07-29	河野
Ⓓ	現地調査結果フォロー	'10-03-30	河野
ⓓ	盤名称変更	'00-02-18	河野

	Date	Name
Drawn		河野
Checked		

Fuji Electric Co.,Ltd.

Title: データロガー室CVCF分電盤(2)

電源回路

Dwg.No. W426297 106

d Ⓓ E

Ref.