回路構成

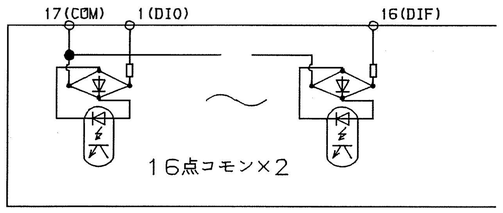

アドレス	項目名称		備考
I.0420	田上ポンプ所田上水源地	停電	
I.0421	田上ポンプ所田上水源地	TM故障	
I.0422	田上ポンプ所田上水源地	一括故障	
I.0423	田上ポンプ所柴ケ原第3配水池	停電	
I.0424	田上ポンプ所柴ケ原第3配水池	故障	
I.0425	田上ポンプ所武田ケ瀬戸ポンプ所	停電	
I.0426	田上ポンプ所武田ケ瀬戸ポンプ所	故障	
I.0427	田上ポンプ所武之台高架配水池	水位低	
I.0428	田上ポンプ所武之台高架配水池	水位高	
I.0429	田上ポンプ所	シーケンサ故障	
I.042A	田上ポンプ所柴原第三配水池	計装故障	
I.042B	田上ポンプ所柴原第三配水池	扉開	
I.042C	田上ポンプ所		
I.042D	田上ポンプ所		
I.042E	田上ポンプ所		
I.042F	田上ポンプ所	TM故障	

[遠方監視制御装置（田上ポンプ所）] より　(65~6)FTE439913

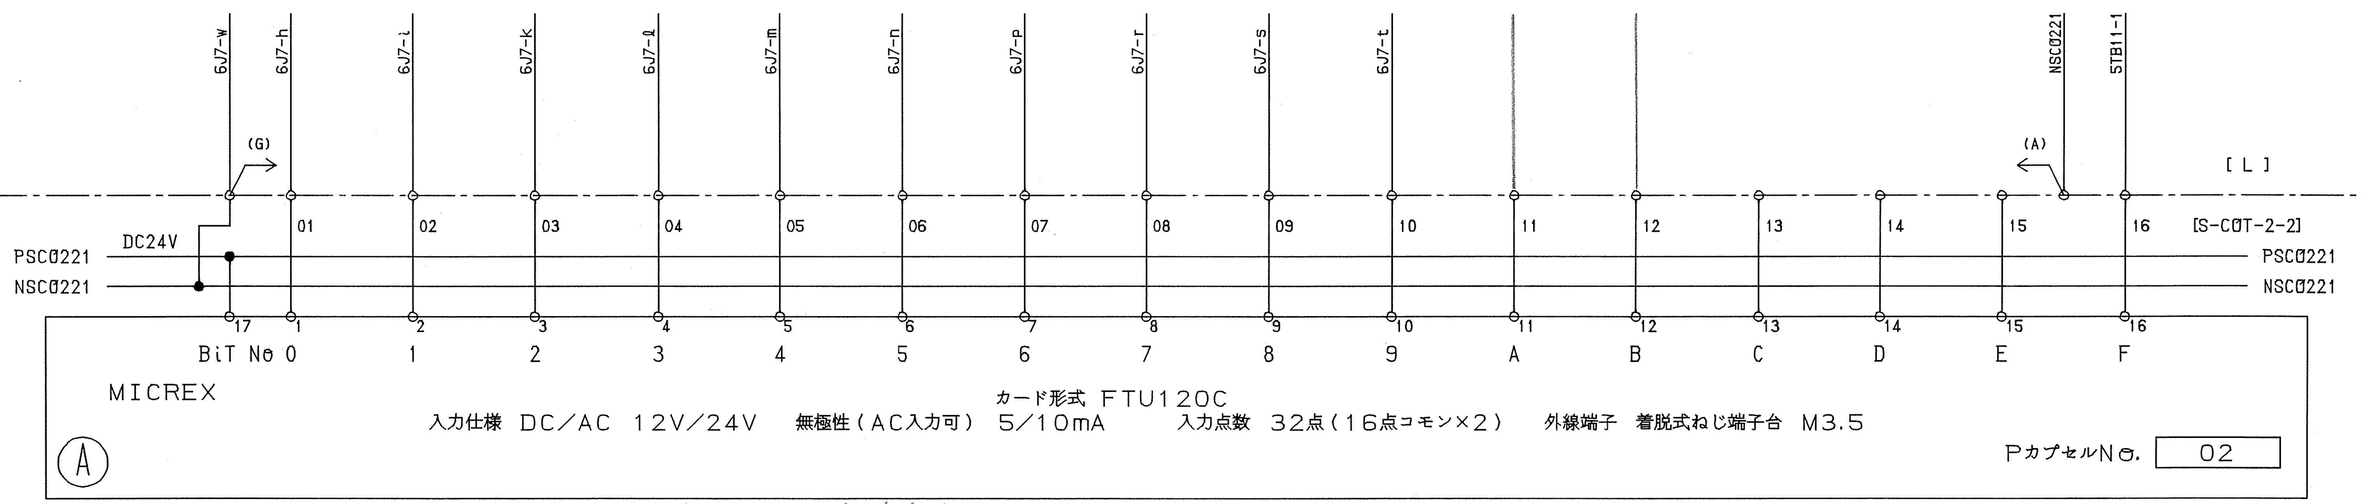

Revisions					
ⓟ	現地試験フォロー	'01-06-15	折茂	G) 清泉寺水源地計装設備等に伴う変更 2013-02-15 黒沼	
ⓜ	コモン変更	'00-11-09	折茂		
ⓚ	信号追加	'00-09-20	折茂		
ⓘ	アドレス変更、取合いフォロー	'00-08-21	野崎		
ⓕ	本頁追加（P.508を書換え）	'00-04-24	森竹		

	Date	Name
Drawn	2000-04-24	森竹
Checked		

Fuji Electric Co.,Ltd.

Title: 管理管轄入出力制御装置 インターフェース回路

Ref. Dwg No. W426297　567

M/F DI（ユニット・端子）1/2
CIFDICUA

P f
G i
k
m

アドレス	CH. NO.	項目名称	備考
WB0164	00	田上ポンプ所紫原第3配水池送水圧力	
WB0165	01	田上ポンプ所送水元弁開度	
WB0166	02	田上ポンプ所紫原第3配水池向送水流量	（田上ポンプ所送水流量）
WB0167	03	田上ポンプ所武岡第2配水池向送水流量	（田上水源地送水流量）
WB0168			CH.00 ステータス情報
WB0169			CH.01 ステータス情報
WB0170			CH.02 ステータス情報
WB0171			CH.03 ステータス情報

アドレス	CH. NO.	項目名称	備考
WB0172	00	田上ポンプ所紫原第3配水池水位	
WB0173	01	垂上ポンプ所 武之台高架配水池/低区配水池水位	
WB0174	02	田上ポンプ所紫原第三配水池 残留塩素	
WB0175	03	田上ポンプ所 予備	
WB0176			CH.00 ステータス情報
WB0177			CH.01 ステータス情報
WB0178			CH.02 ステータス情報
WB0179			CH.03 ステータス情報

[遠方監視制御装置盤（田上ポンプ所）] FTE439913

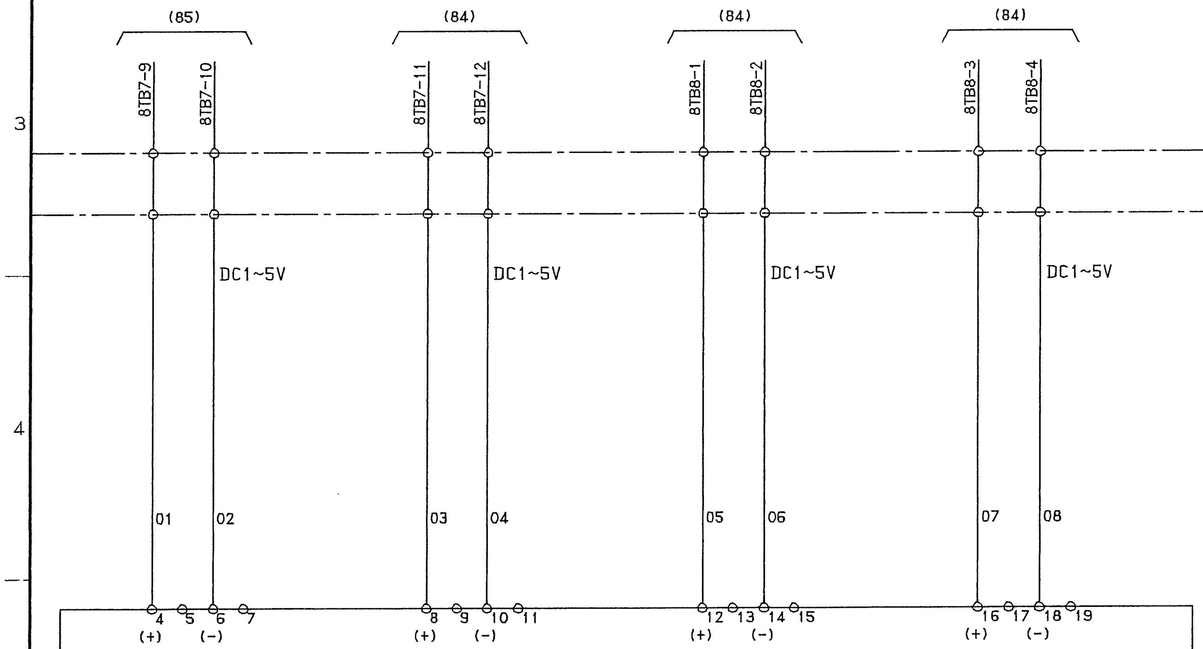

MICREX カード形式 FTK305A-C10

入力仕様 A／D変換信号DC4～20mA／0～10000 BINARY
入力点数 4点
外線端子 着脱式ねじ端子台

Pカプセル No. 02

[遠方監視制御装置盤（田上ポンプ所）]
FTE439913

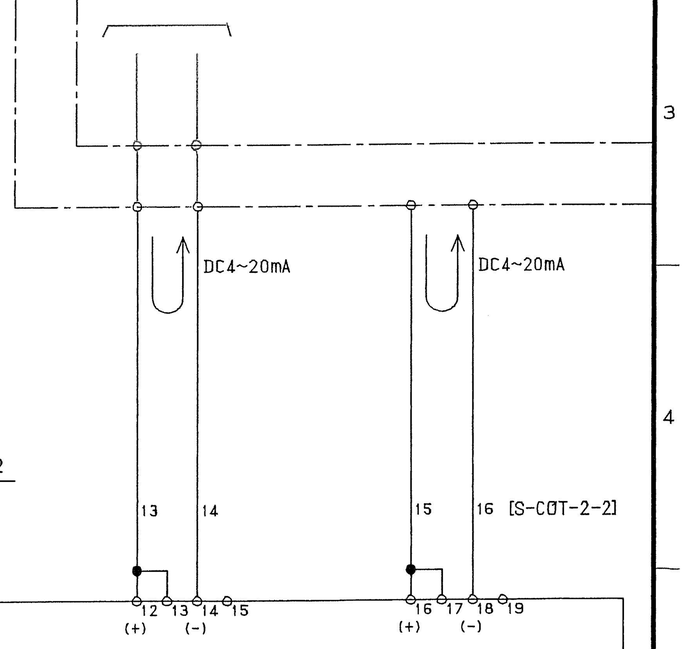

MICREX カード形式 FTK305A-C10

入力仕様 A／D変換信号DC4～20mA／0～10000 BINARY
入力点数 4点
外線端子 着脱式ねじ端子台

Pカプセル No. 02

(G) 清泉寺水源地電気計装設備工事に伴う変更 2013－02－15 黒沼

Revisions				Date	Name
(P)	現地試験フォロー	'01-06-15	折茂		
(m)	コメント変更	'00-11-09	折茂	Drawn 2000-04-24	森竹
(i)	信号名称変更、取合いフォロー	'00-08-21	野崎	Checked	
(f)	本頁追加	'00-04-24	森竹		

Fuji Electric Co.,Ltd.

Title 管理管轄入出力制御装置 インターフェース回路

Ref. Dwg. No. W426297 595

M/F AI（電流）2／1
CIFAIIKA

G f i m P