回路構成

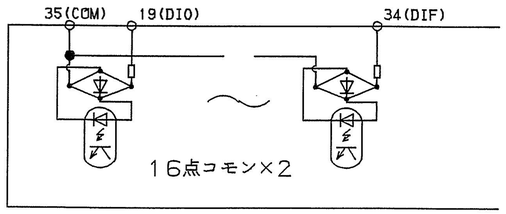

アドレス	項目名称	備考
I.0390	星ケ峯第1配水池テレメータ異常	一括故障
I.0391	予備	
I.0392	予備	
I.0393	予備	
I.0394	予備	
I.0395	大峯ポンプ所テレメータ異常	一括故障
I.0396	予備	
I.0397	予備	
I.0398	予備	
I.0399	予備	
I.039A	星ケ峯第2配水池テレメータ異常	一括故障
I.039B	予備	
I.039C	予備	
I.039D	予備	
I.039E	予備	
I.039F	予備	

[遠方監視制御装置盤(星ケ峯第1配水池)]　[遠方監視制御装置盤(大峯ポンプ所)]　[遠方監視制御装置盤(星ケ峯第2配水池)]

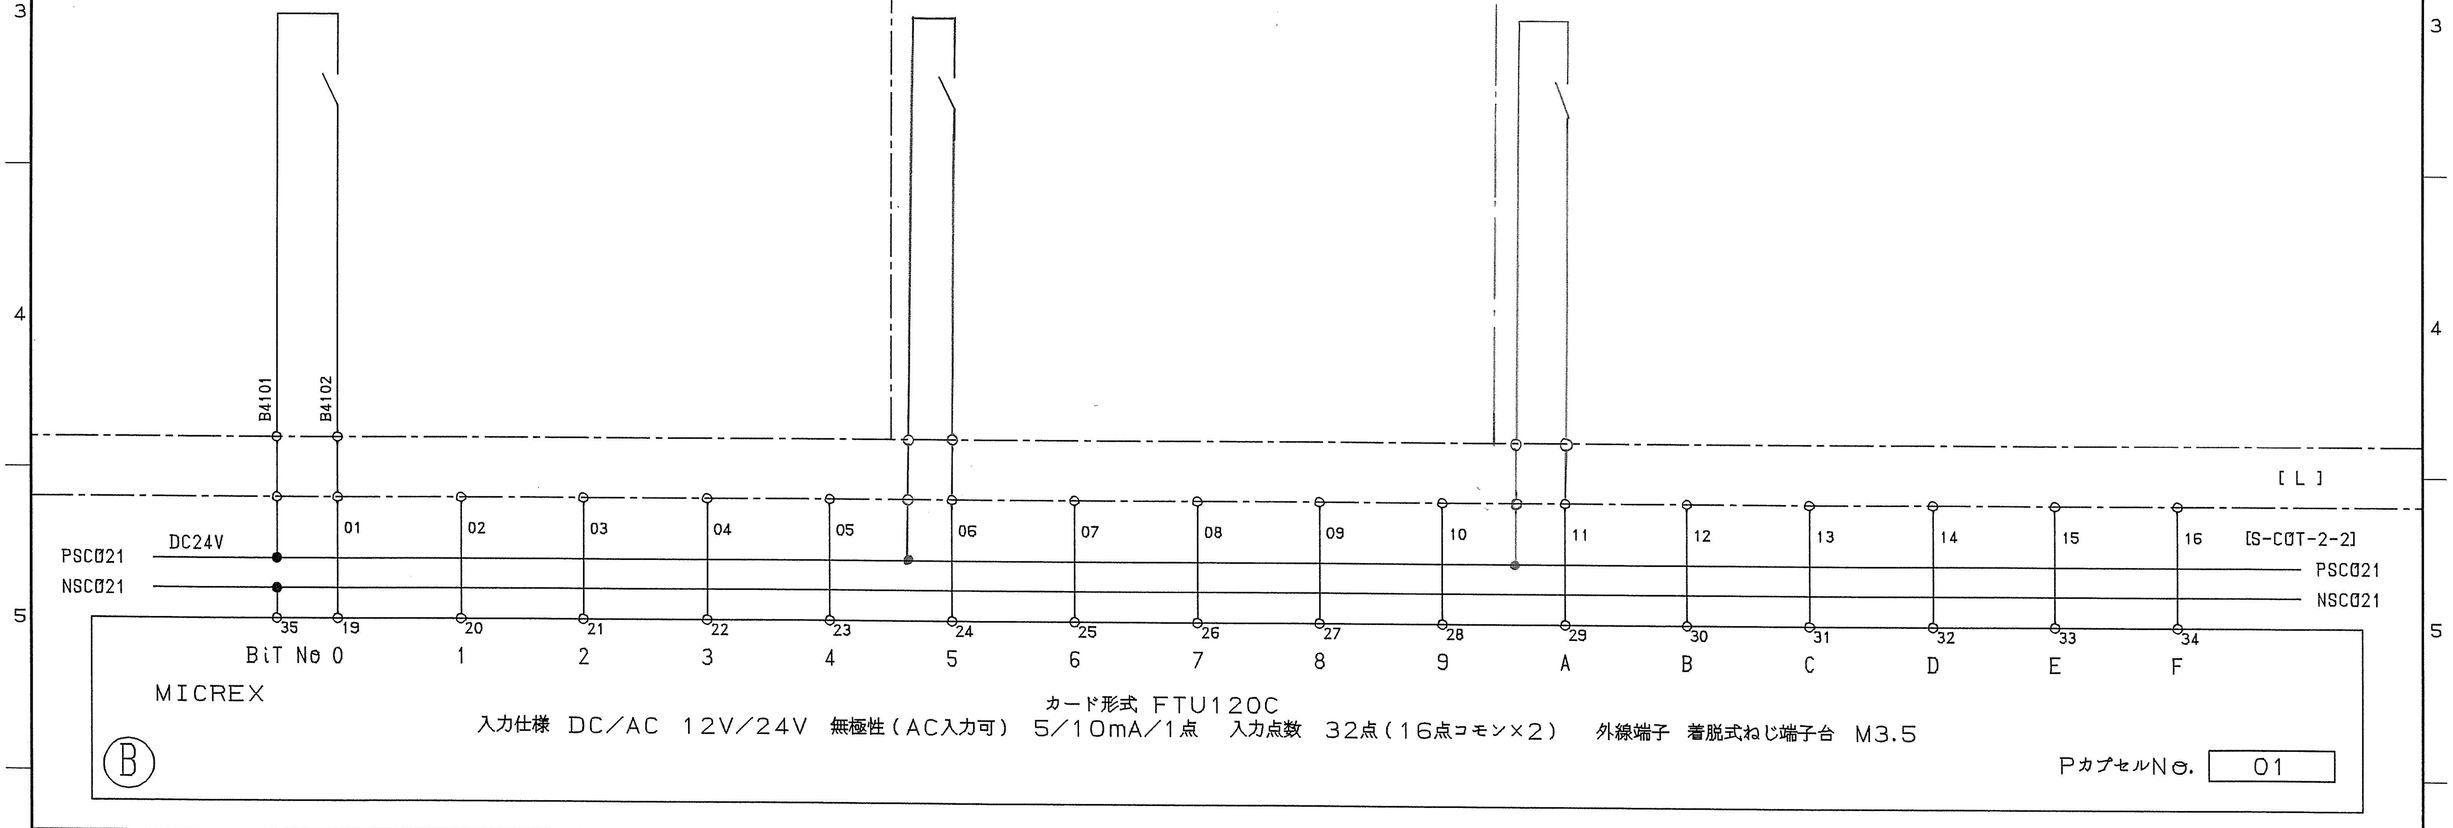

Revisions					
⑤	信号追加	'02-02-08 河野		Date	Name
⑥	信号追加	'10-02-22 河野	Drawn	2000-04-24	森竹
③	信号追加	'05-11-07 大城	Checked		
①	現地試験フォロー	'02-04-03 河野			

Fuji Electric Co.,Ltd.

Title: 管理管轄入出力制御装置 インターフェース回路

Ref. Dwg. No. W426297　514

M/F DI(ユニット・端子)2/2
CIFDICUB

t f
B i
C P
S

管理管轄入出力制御装置

FDDI

ルータ

HUB

MICREX-F(F150S)

MPU | Ethernet | Ethernet | Ethernet | | I/O

MICREX-F(F150S)

MPU | Ethernet | Ethernet | Ethernet | | I/O

HUB HUB HUB HUB

MICREX-F (F120S)

Pリンク

TM/TC TM/TC TM/TC TM TM/TC TM TM/TC TM TM TM TM/TC TM/TC TM/TC TM TM/TC TM TM/TC TM/TC

TM/TC TM/TC TM/TC TM TM/TC TM TM/TC TM TM TM TM/TC TM/TC TM/TC TM TM/TC TM TM/TC TM/TC

山田ポンプ所

自由ケ丘ポンプ所

五ケ別府水源地

星ケ峯第二配水池

星ケ峯第一配水池

大峯ポンプ所

宇宿ポンプ所

中山ポンプ所

亀ケ原高架配水池

皇徳寺ポンプ所

鍋ケ宇都配水池

脇田水源地

新郡元水源地

武之橋下電動弁室

武之台高架配水池

田上水源地

田上台配水池

高見ポンプ所

田上ポンプ所

中央

現場

は現状設備

は今回改造

Revisions				Date	Name
Ⓐ	TM追加	'05-11-07 大城			
Ⓥ	C18905による改造	'04-12-03 森竹			
Ⓒ	TM追加	'10-02-22 河野	Drawn	200-06-08	河野
Ⓔ	皇徳寺ポンプ所追加	'11-07-29 河野	Checked		
Ⓑ	TM追加	'09-01-30 河野			

Fuji Electric Co.,Ltd.

Title 場外系集中監視制御設備 システム構成（3／4）

Ref. Dwg.No. W426297 023

t Ⓐ V Ⓑ X Ⓒ Y Ⓔ

[L]

[S-D-2]

R7D3S1 (105H) T7D3S1

AC100V 60Hz

R7D3S1 (107A) T7D3S1

52D73S32 <20013> SA52B/15K	R7D3S32	T7D3S32	遠方監視制御装置 中山ポンプ所
52D73S33 <20013> SA52B/15K	R7D3S33	T7D3S33	遠方監視制御装置 星ケ峯第二配水池
52D73S34 <20013> SA52B/15K	R7D3S34	T7D3S34	遠方監視制御装置 皇徳寺ポンプ所
52D73S35 <20013> SA52B/15K	R7D3S35	T7D3S35	予備
52D73S36 <20013> SA52B/15K	R7D3S36	T7D3S36	予備
52D73S37 <20013> SA52B/15K	R7D3S37	T7D3S37	予備

131E

[L]

Revisions			Date	Name
ⓔ	TM追加	'11-07-29 河野	Drawn	河野
ⓓ	現地調査結果フォロー	'10-03-30 河野	Checked	
ⓒ	盤名称変更	'00-02-18 河野		

Fuji Electric Co.,Ltd.

Title: データロガー室CVCF分電盤(2)
電源回路

Ref. Dwg.No. W426297 106

[S-COT-2-1]

光ケーブル　光ケーブル

TX1　TX2

PDU-6
P1
(401F)
コンセント
ルータ
10BASET
LR-X6030B

TPCBL-B005

PDU-6
P2
(401F)
コンセント
2
リピータハブ（１）
1　3
LH8VC2

(432C)
TPCBL-B005 <12048>

光ケーブル

S1 (MIC型)　S2 (MIC型)
FICアダプタユニット
HFIAA-00
<80049>
(SC2型)
S3

AC100V 60Hz
PDU-6
P5
(401G)
コンセント
PT
AC100V

F-152S	10BASET FFU170B	FFU170B 10BASET	FFU170B 10BASET	FTU910	FTU910	FTU910

UTP5eX-5Bx2 <12046>

トランシーバ　LFA-R0535 <12047>
AUI　10BASET

PDU-6
P3
(401F)
コンセント
リピータハブ（２）
1 2 3 4 5 7
LH8VC2
<12045>

PDU-6
P4
(401F)
コンセント
AUI
リピータハブ（３）
1 2 6 7 8
LH8VC2
<12045>

TPCBL-BXXX
XXXは長さを記入

山田ポンプ所
自由ヶ丘ポンプ所
五ヶ別府水源地
星ヶ峯第1配水池
星ヶ峯第2配水池
大峯配水池（将来）
大峯ポンプ所
宇宿ポンプ所
鍋ヶ宇都配水池
笠木ポンプ所（将来）
饅頭石ポンプ所（将来）
仏迫ポンプ所（将来）
中山ポンプ所
亀ヶ原高架配水池
皇徳寺ポンプ所

a) TM追加 '05-11-07 大城
b) FICアダプタ追加 '01-05-09 折茂

Revisions			Date	Name
Ⓔ	テレメータ追加による取合変更	'11-07-29 河野		
Ⓒ	テレメータ追加による取合変更	'10-02-22 河野	Drawn	1999-12-29 河野
Ⓑ	テレメータ追加による取合変更	'09-01-30 河野	Checked	
Ⓧ	テレメータ追加による取合変更	'04-01-19 河野		

Fuji Electric Co.,Ltd.

Title: 管理管轄入出力制御装置
イーサネット接続図

Ref. Dwg. No. W426297　422

em 1 / pr 2 / cs 8

イーサネットモジュールFFU170B（F120Sシリーズ）

前面図

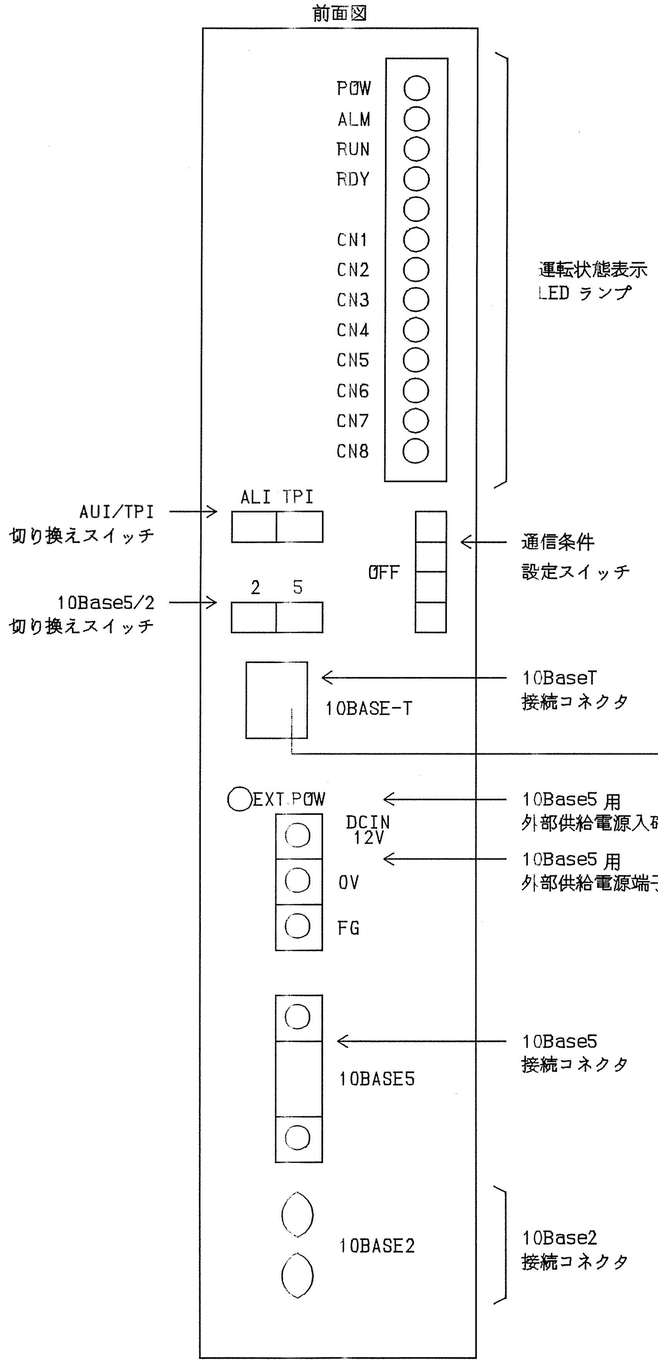

※ 裏面にあるIPアドレス設定S・Wを96に設定

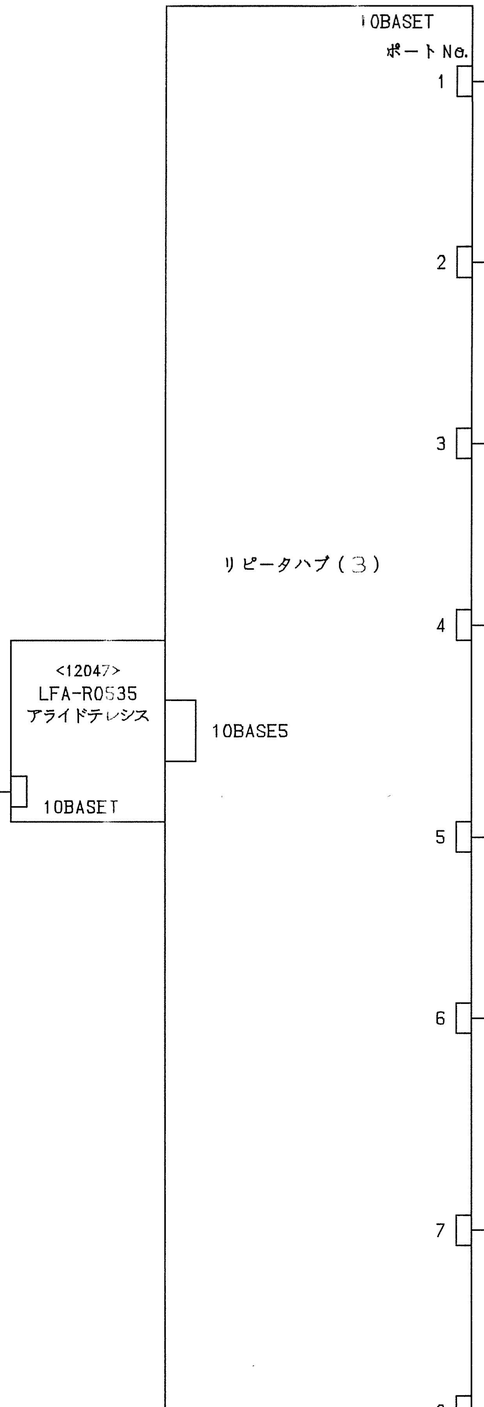

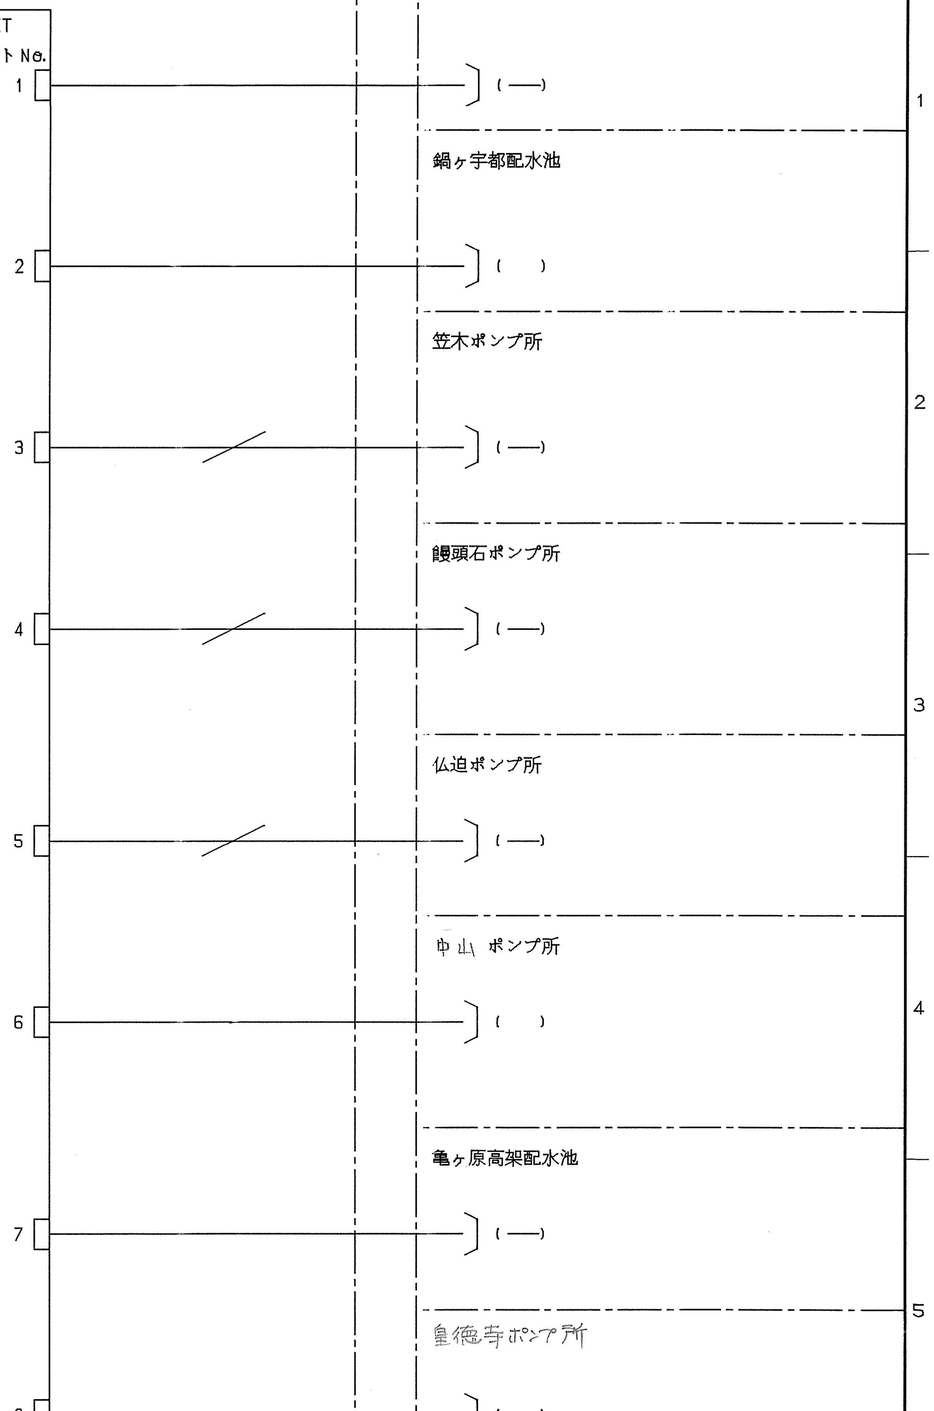

Revisions					
Ⓑ	テレメータ追加による取合変更	'09-01-30	河野		
⊗	テレメータ追加による取合変更	'04-01-19	河野	Drawn	2000-04-24 森竹
ⓣ	現地試験フォロー	'02-04-03	河野	Checked	
Ⓔ	テレメータ追加による取合変更	'11-07-29	河野		

Fuji Electric Co.,Ltd.

Title: 管理管轄入出力制御装置 イーサネット接続図

Ref. Dwg. No.: W426297

424

Sheet: Size B